
NOTES:

- SYED BROTHERS RETAIN COPYRIGHT OF DESIGN, SCHEME & OWNERSHIP OF DRAWINGS.
- DO NOT SCALE DRAWINGS, FOR ALL CRITICAL DIMENSIONS CONSULT WITH GALLERIA DESIGNS.
- DRAWING SHOULD BE READ IN CONJUCTION WITH STRUCTURAL ENGINEER DRAWINGS.
- ANY OMISSION TO BE REPORTED TO AND CLARIFIED WITH CLIENT PRIOR TO COMMENCEMENT OF WORK ON SITE
- VERIFY DIMENSIONS, LEVELS AND EXISTING STRUCTURE, ETC ON SITE PRIOR TO COMMENCEMENT.
- ALL WORKS TO COMPLY WITH SYED BROTHERS, DETAILS & INFORMATION PROVIDED BY OTHER ASSOCIATE CONSULTANTS.
- ANY WORKS COMMENCED ON SITE PRIOR TO OBTAINING PERMISSION FROM LOCAL AUTHORITY WILL BE CARRIED OUT AT CLIENT OWN RISK

revision notes	drawn	checked

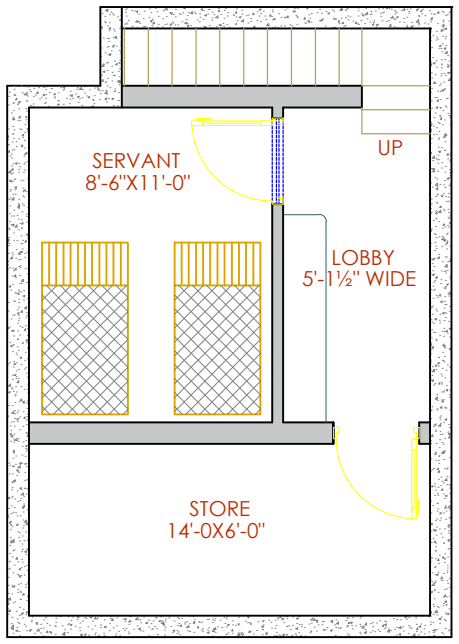

COVERED AREA = 341.SFT

Client
DR. NASIR SHAHEEN

Architect
MUHAMMAD BEHRAM
B. Arch(USA)

Project
PLOT NO115-G DHA

consultants
SYED BROTHERS
Engineers , Architects & Consltants
1st Floor Plaza No.1/1, CCA Commercial Phase 5
DHA Lahore Cantt.

drawing title
BASEMENT PLAN

scale	
N.T.S	
start date: APR:2025	Issue date: 05/05/2025
drawn: NOMAN	checked: RAMEEL RAZA
drawing number	


orientation

Issued for
- Client Approval
- Submission Approval
- On site Construction
- Tenders

NOTES:

- SYED BROTHERS RETAIN COPYRIGHT OF DESIGN, SCHEME & OWNERSHIP OF DRAWINGS.
- DO NOT SCALE DRAWINGS, FOR ALL CRITICAL DIMENSIONS CONSULT WITH GALLERIA DESIGNS.
- DRAWING SHOULD BE READ IN CONJUCTION WITH STRUCTURAL ENGINEER DRAWINGS.
- ANY OMISSION TO BE REPORTED TO AND CLARIFIED WITH CLIENT PRIOR TO COMMENCEMENT OF WORK ON SITE
- VERIFY DIMENSIONS, LEVELS AND EXISTING STRUCTURE, ETC ON SITE PRIOR TO COMMENCEMENT.
- ALL WORKS TO COMPLY WITH SYED BROTHERS, DETAILS & INFORMATION PROVIDED BY OTHER ASSOCIATE CONSULTANTS.
- ANY WORKS COMMENCED ON SITE PRIOR TO OBTAINING PERMISSION FROM LOCAL AUTHORITY WILL BE CARRIED OUT AT CLIENT OWN RISK

revision notes	drawn	checked

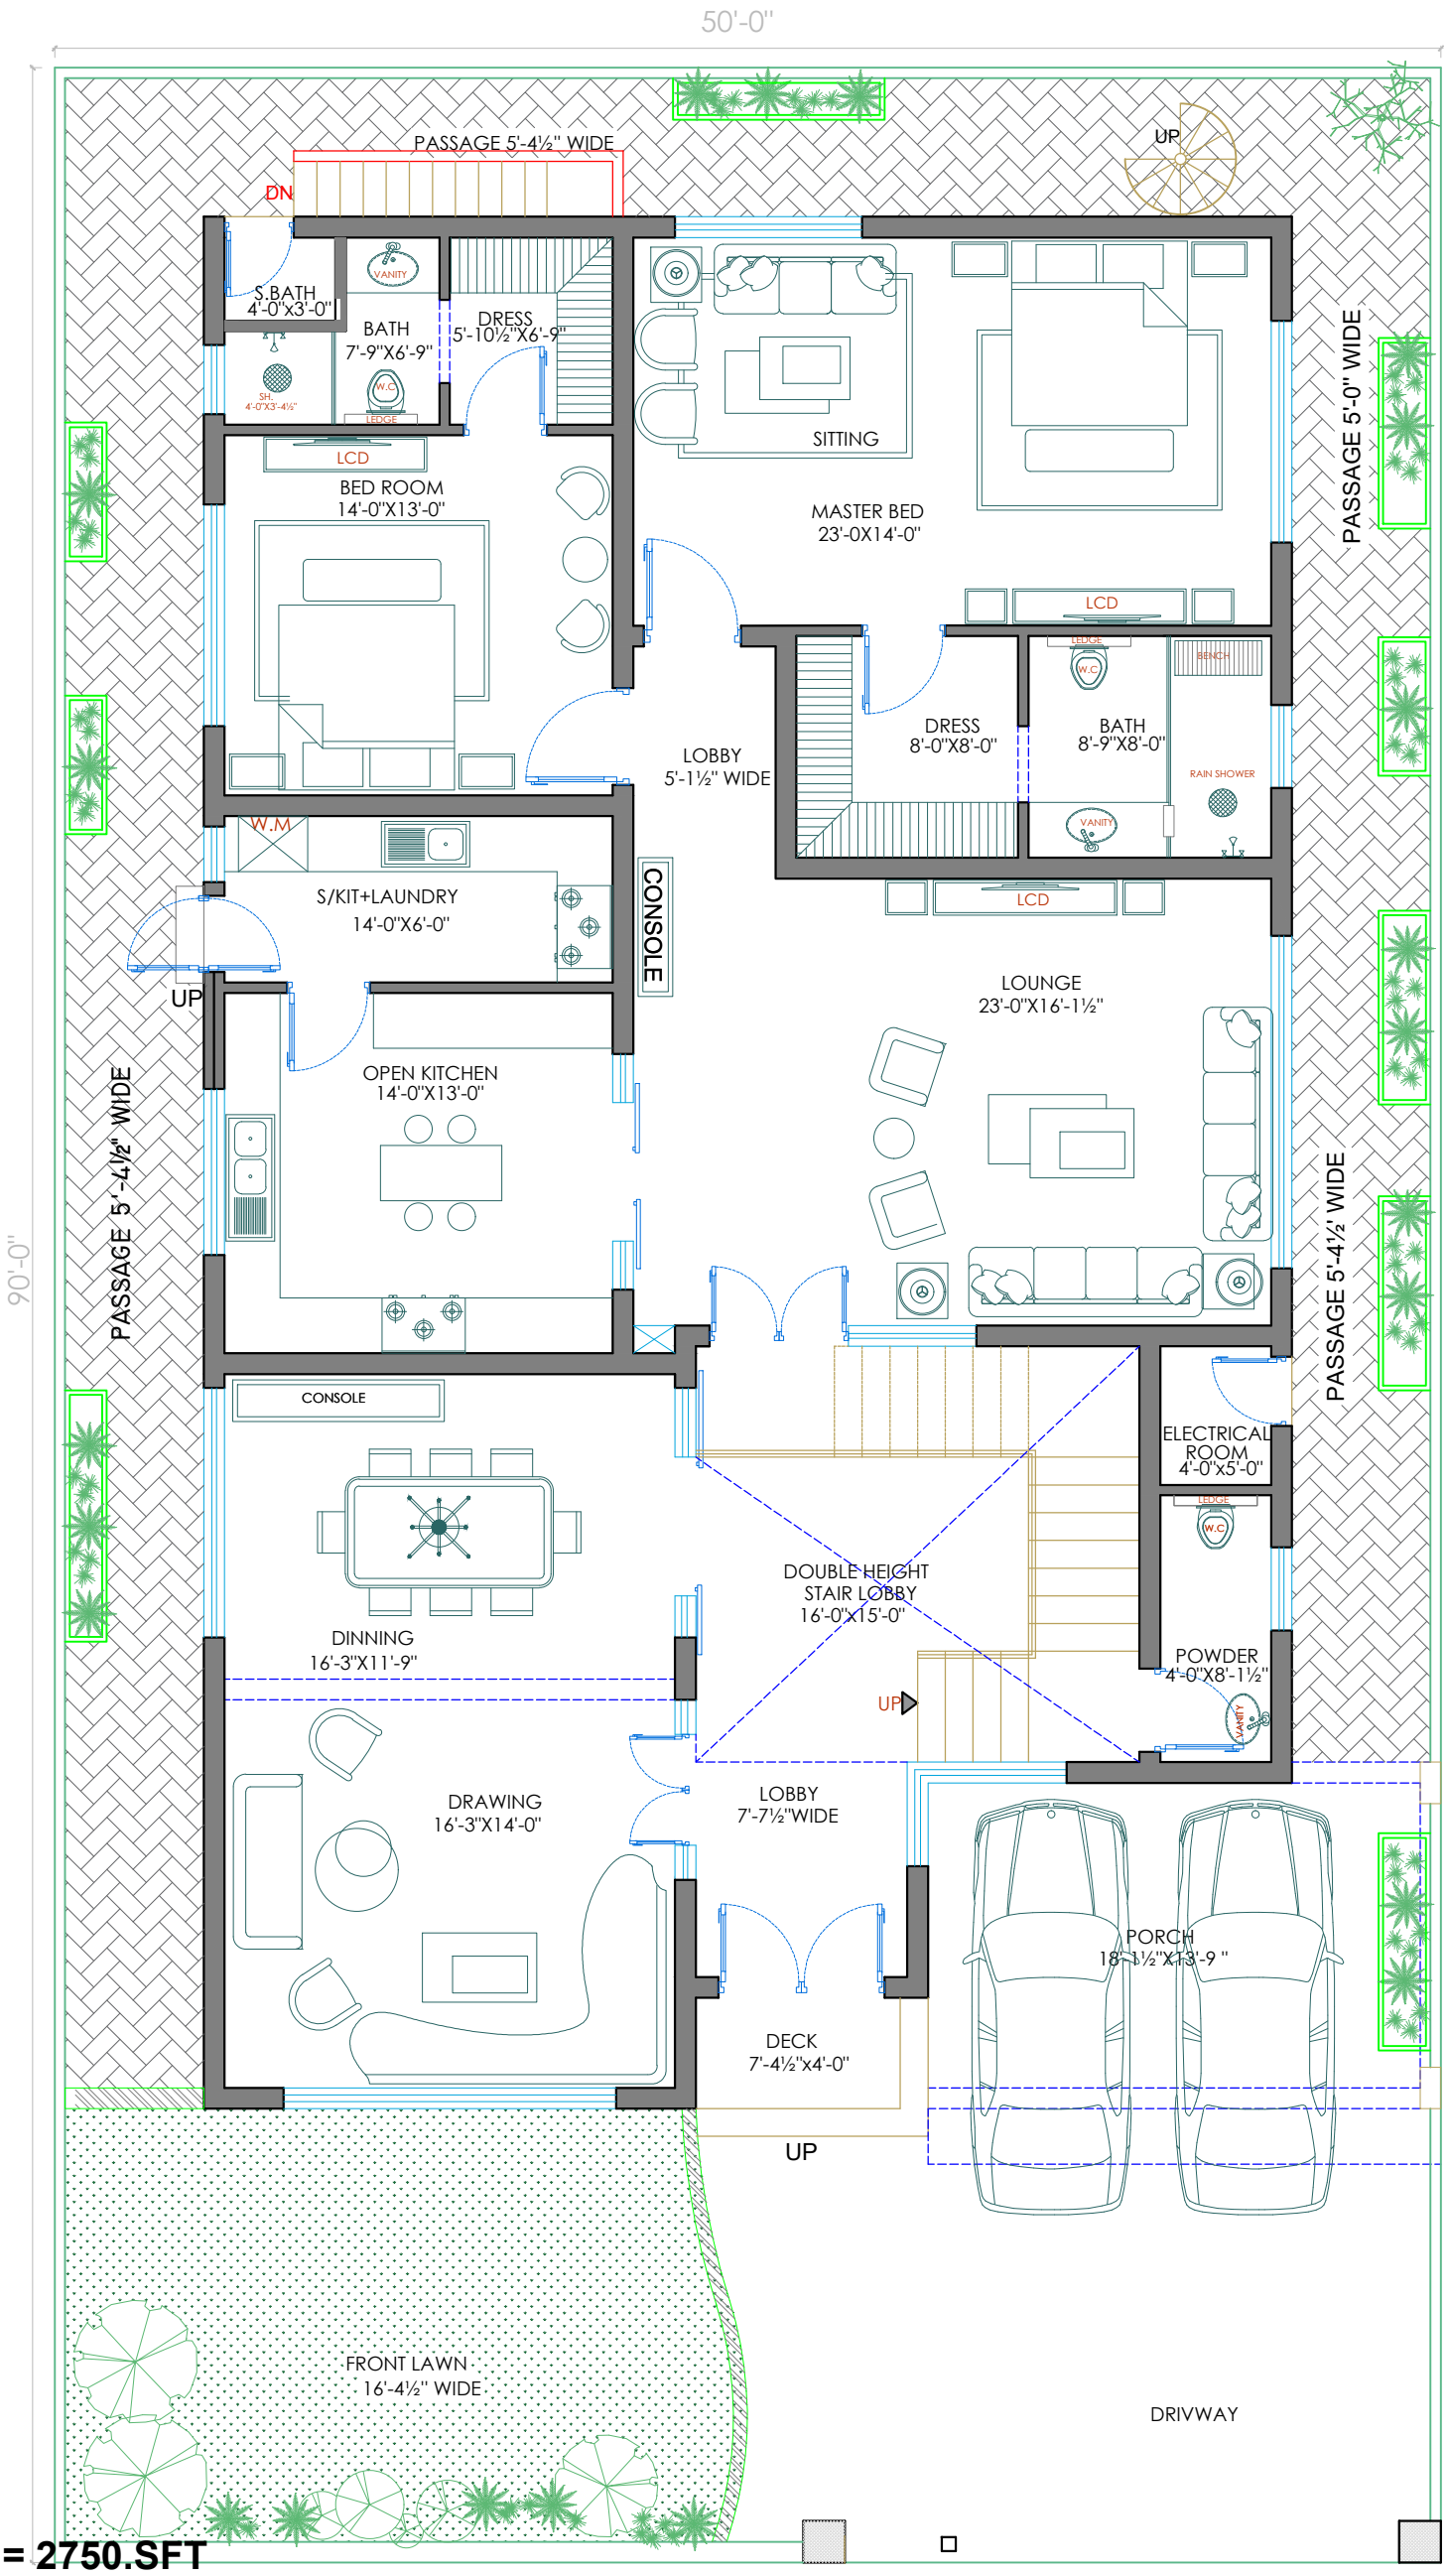

COVERED AREA = 2750.SFT

Client	**DR. NASIR SHAHEEN**
Architect	MUHAMMAD BEHRAM B. Arch(USA)
Project	**PLOT NO115-G DHA**

consultants

SYED BROTHERS
Engineers , Architects & Consltants
1st Floor Plaza No.1/1, CCA Commercial Phase 5
DHA Lahore Cantt.

SB

drawing title	**GROUND FLOOR PLAN**
scale	N.T.S
start date	APR:2025
Issue date	05/05/2025
drawn	NOMAN
checked	RAMEEL RAZA
drawing number	

orientation

S E W N


Issued for

- Client Approval
- Submission Approval
- On site Construction
- Tenders

NOTES:

- SYED BROTHERS RETAIN COPYRIGHT OF DESIGN, SCHEME & OWNERSHIP OF DRAWINGS.
- DO NOT SCALE DRAWINGS, FOR ALL CRITICAL DIMENSIONS CONSULT WITH GALLERIA DESIGNS.
- DRAWING SHOULD BE READ IN CONJUCTION WITH STRUCTURAL ENGINEER DRAWINGS.
- ANY OMISSION TO BE REPORTED TO AND CLARIFIED WITH CLIENT PRIOR TO COMMENCEMENT OF WORK ON SITE
- VERIFY DIMENSIONS, LEVELS AND EXISTING STRUCTURE, ETC ON SITE PRIOR TO COMMENCEMENT.
- ALL WORKS TO COMPLY WITH SYED BROTHERS, DETAILS & INFORMATION PROVIDED BY OTHER ASSOCIATE CONSULTANTS.
- ANY WORKS COMMENCED ON SITE PRIOR TO OBTAINING PERMISSION FROM LOCAL AUTHORITY WILL BE CARRIED OUT AT CLIENT OWN RISK

revision notes	drawn	checked

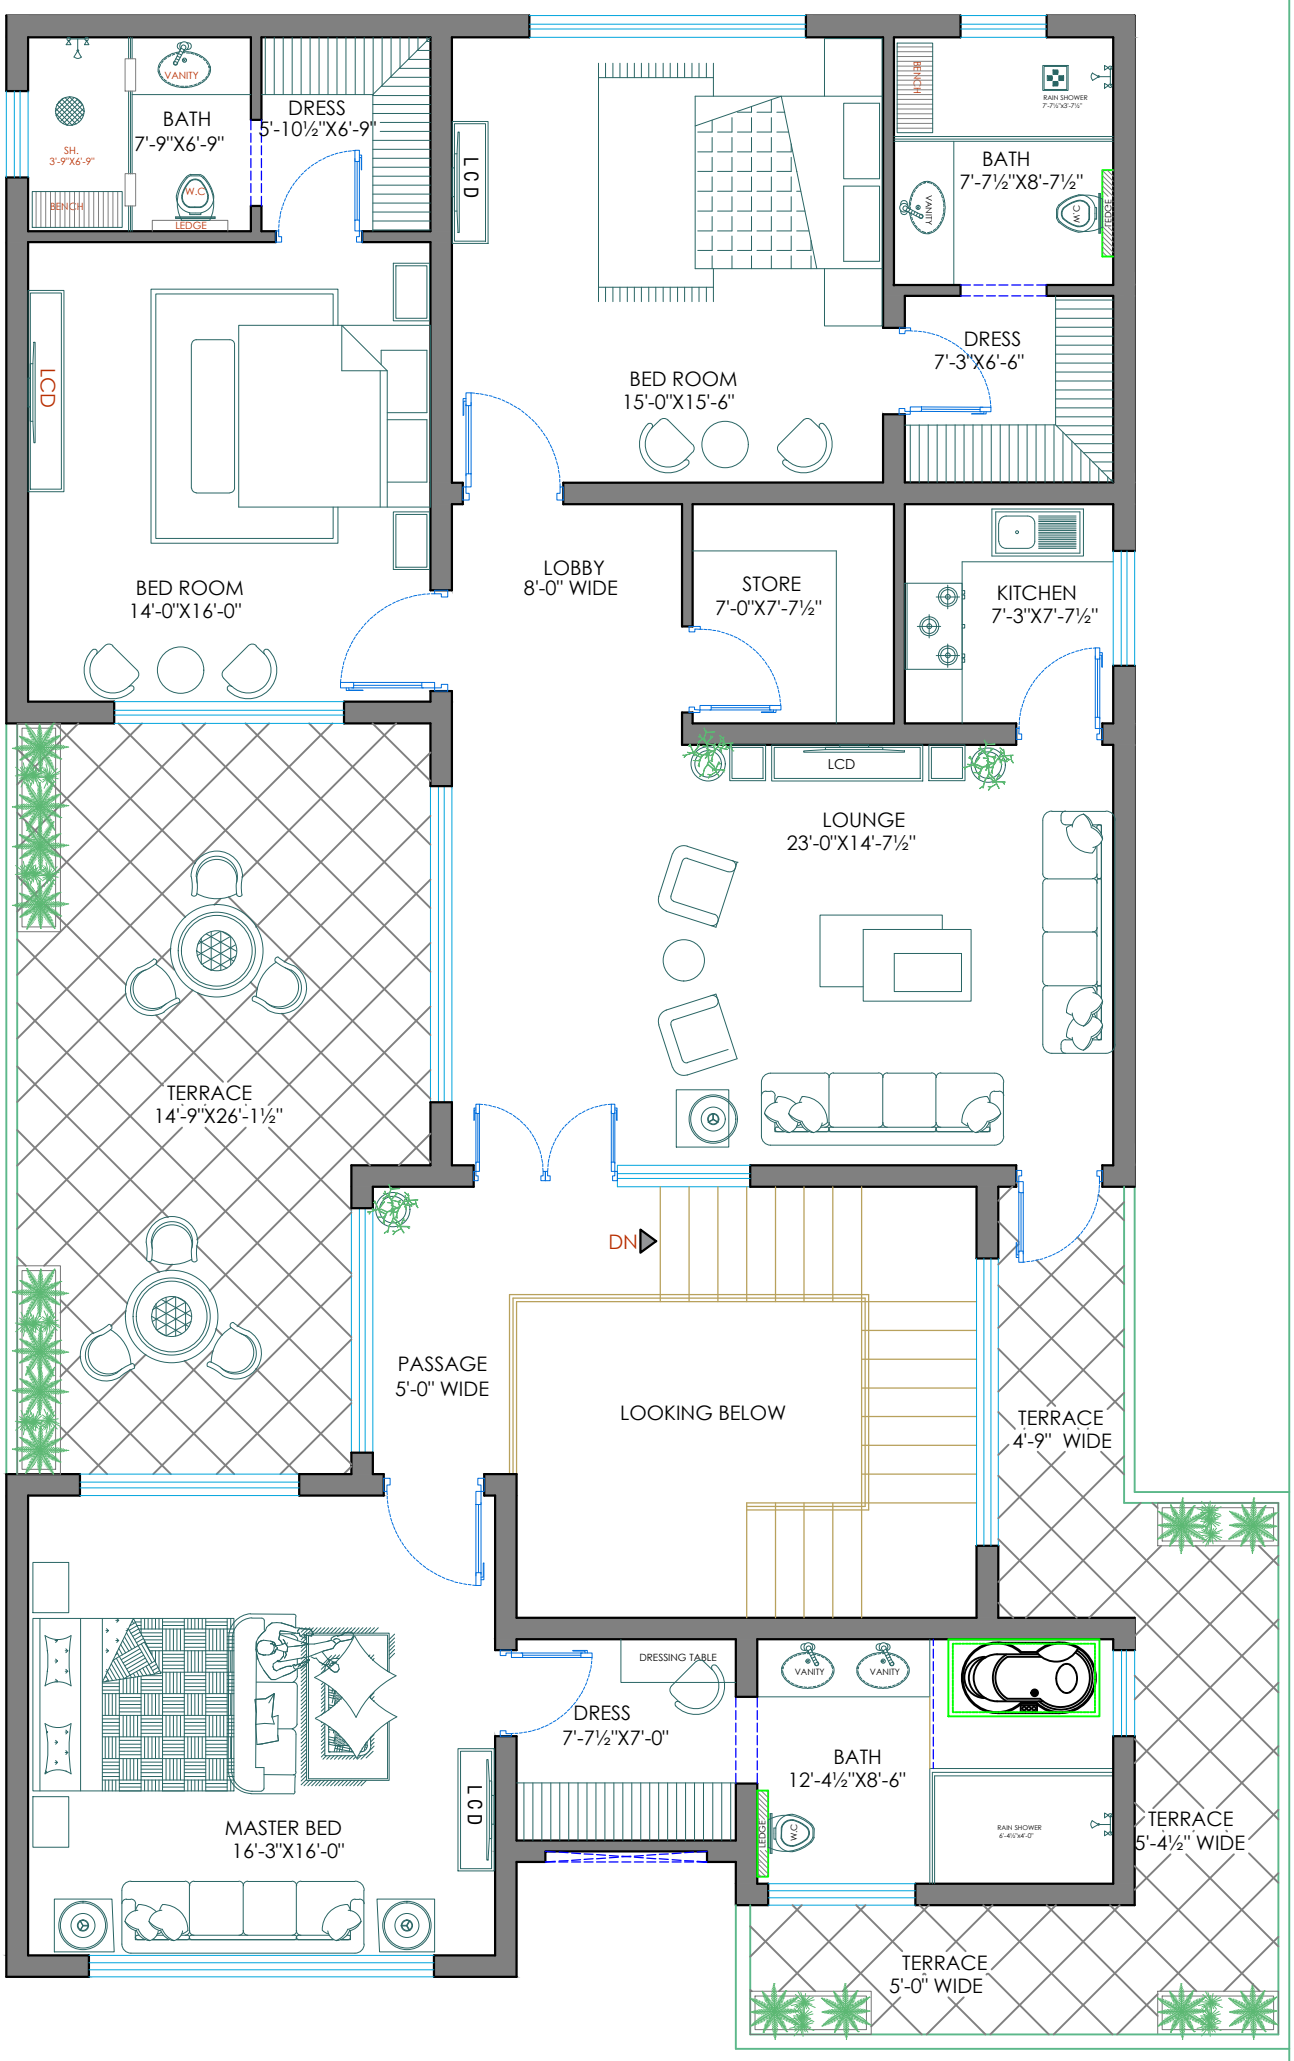

COVERED AREA = 2186.SFT

Client: **DR. NASIR SHAHEEN**	consultants: SYED BROTHERS Engineers , Architects & Consltants 1st Floor Plaza No.1/1, CCA Commercial Phase 5 DHA Lahore Cantt.	drawing title: **FIRST FLOOR PLAN** scale: N.T.S start date: APR:2025 / Issue date: 05/05/2025 drawn: NOMAN / checked: RAMEEL RAZA drawing number:	orientation Issued for: Client Approval; Submission Approval; On site Construction; Tenders
Architect: MUHAMMAD BEHRAM, B. Arch(USA)			
Project: **PLOT NO115-G DHA**			