UNION STEEL ENGINEERING LTD.

UEMS

UNION ENGINEERING AND MANAGEMENT SERVICES

STEEL ENGINEERING EXPERTS

0322-8419451/03000029937

info@uems.com.pk

TABLE OF CONTENTS

DRG NO.	DRAWING TITLE	REV.	DATE:
PR-01	DRAWING INDEX	00	14-07-25
PR-02	COLUMN LAYOUT PLAN	00	14-07-25
PR-03	FOUNDATION LAYOUT PLAN	00	14-07-25
PR-04	FOUNDATION SECTION	00	14-07-25
PR-05	BASE PLATE LAYOUT	00	14-07-25
PR-06	ANCHOR BOLT AND BASE PLATE DETAILS	00	14-07-25
PR-07	ROOF PURLIN LAYOUT AND SECTION	00	14-07-25
PR-08	ROOF SHEETING DETAILS	00	14-07-25
PR-09	LONG CROSSECTION DETAILS	00	14-07-25
PR-10	FRONT AND REAR ELEVATION	00	14-07-25
PR-11	SIDE ELEVATIONS	00	14-07-25

(SCAN FOR PROFILE)

REV.	DATE	DESCRIPTION	DRN	CHK	DSN
00	14-07-25	ISSUED FOR PROPOSAL	YAS	A.A	A.H

PROJECT:
PEB STEEL SHED (86'-6" X 105'-0")


CUSTOMER:
PX97 PADEL COURT, LAHORE

UEMS
Address: 4th Floor, Vouge Towers, MM Alam Road LHR.
Email : info@uems.com.pk
Tell : 0322-8419452 / 0300-0029937


JOB NUMBER		DRAWING NO.
SE-PEB-1211		PR-01
DRAWING TITLE: DRAWING INDEX		

PROPOSAL DRAWING


CLIENT:	PX97 PADEL COURT	JOB NUMBER:	SE-PEB-1219
PROJECT:	(PEB SHED (86'-6" X 105'-0")	LOCATION:	DHA PHASE 5 M BLOCK EXTENSION

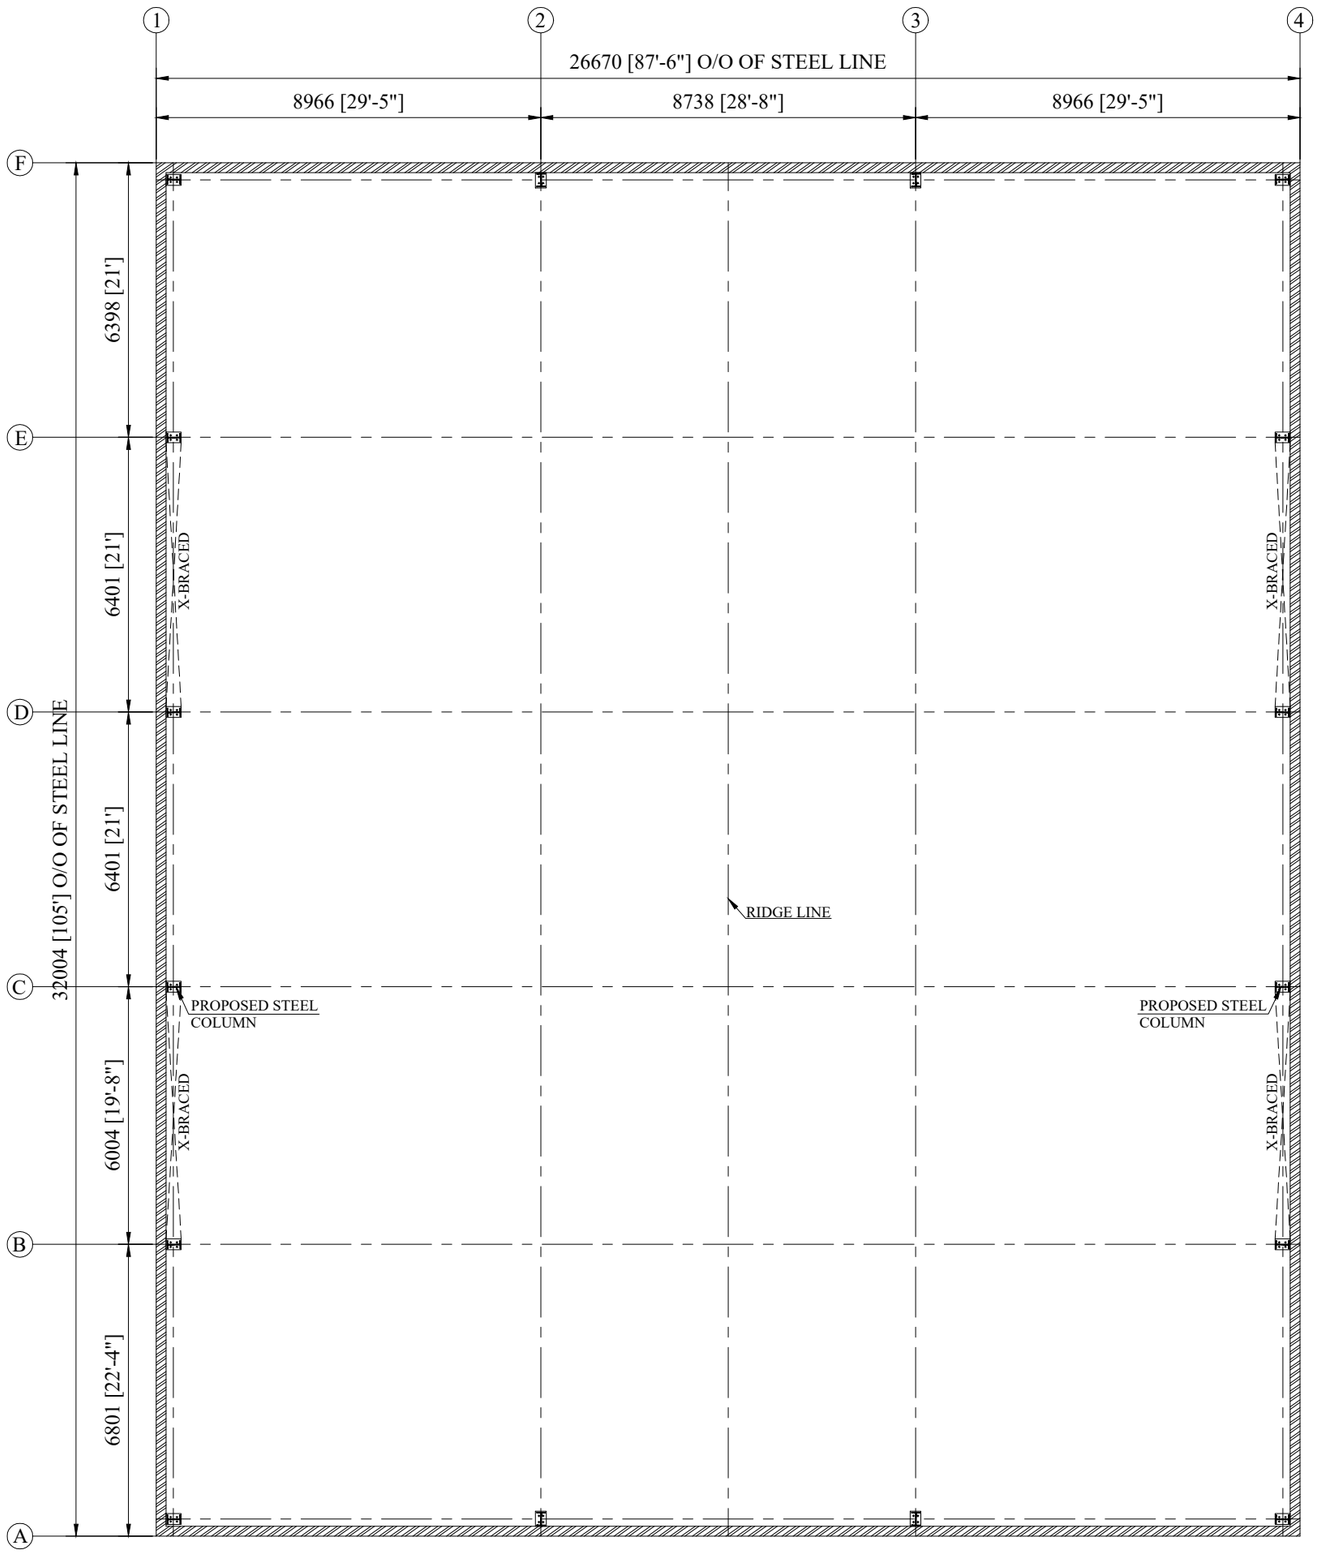

COLUMN LAYOUT PLAN

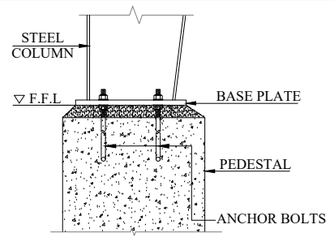

ANCHOR BOLT TYP DETAIL

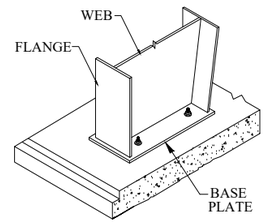

(SCAN FOR PROFILE)

REV.	DATE	DESCRIPTION	DRN	CHK	DSN
00	14-07-25	ISSUED FOR PROPOSAL	YAS	A.A	A.H


PROJECT:
PEB STEEL SHED (86'-6" X 105'-0")

CUSTOMER:
PX97 PADEL COURT, LAHORE


UEMS
Address: 4th Floor, Vouge Towers, MM Alam Road LHR.
Email : info@uems.com.pk
Tell : 0322-8419452 / 0300-0029937

JOB NUMBER		DRAWING NO.
SE-PEB-1211		PR-02


DRAWING TITLE:
COLUMN LAYOUT PLAN

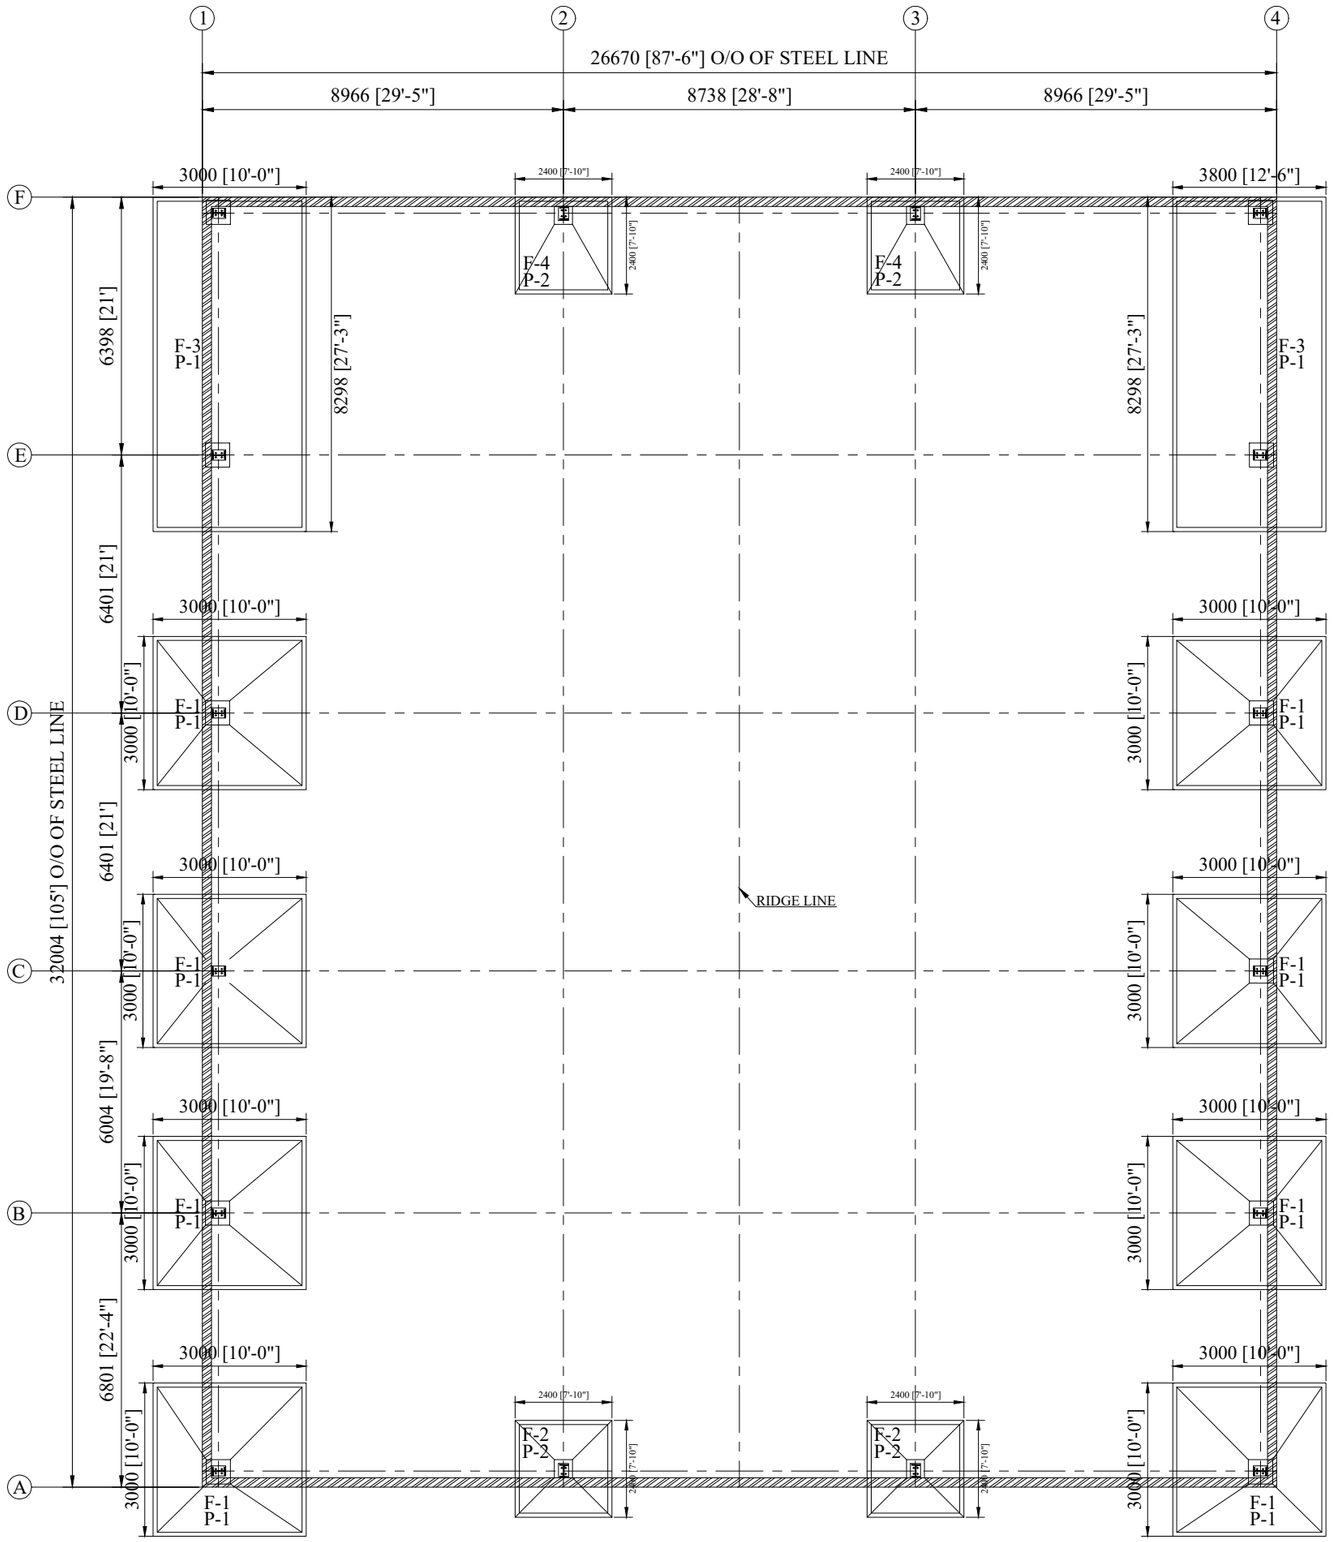

FOUNDATION LAYOUT PLAN

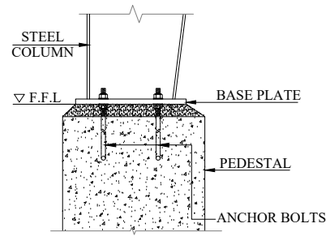

ANCHOR BOLT TYP DETAIL

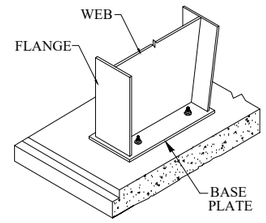

(SCAN FOR PROFILE)

REV.	DATE	DESCRIPTION	DRN	CHK	DSN
00	14-07-25	ISSUED FOR PROPOSAL	YAS	A.A	A.H


PROJECT:
PEB STEEL SHED (86'-6" X 105'-0")

CUSTOMER:
PX97 PADEL COURT, LAHORE


UEMS
Address: 4th Floor, Vouge Towers, MM Alam Road LHR.
Email : info@uems.com.pk
Tell : 0322-8419452 / 0300-0029937

JOB NUMBER		DRAWING NO.
SE-PEB-1211		PR-03


DRAWING TITLE:
FOUNDATION LAYOUT PLAN

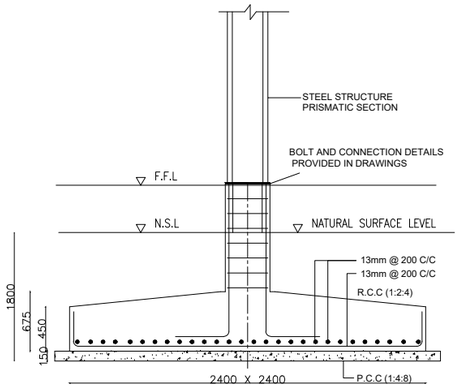


FOOTING F-2 WITH PADESTEL P-2

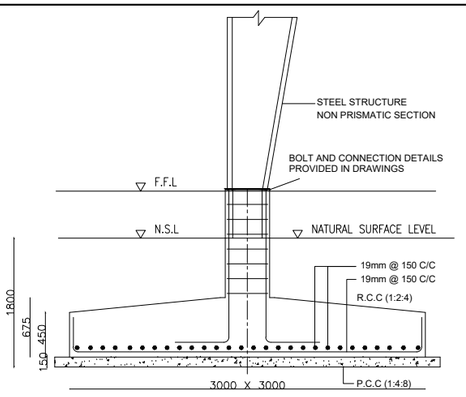


FOOTING F-1 WITH PADESTEL P-1

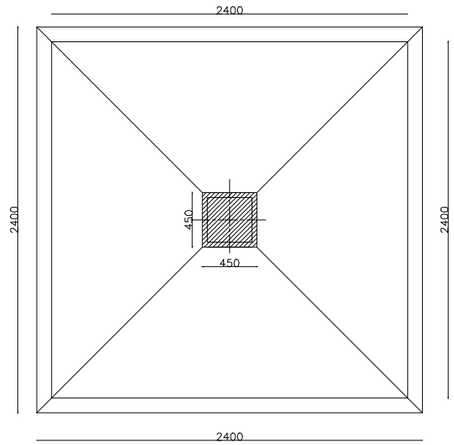


FOOTING F2 AND PADESTEL P-2

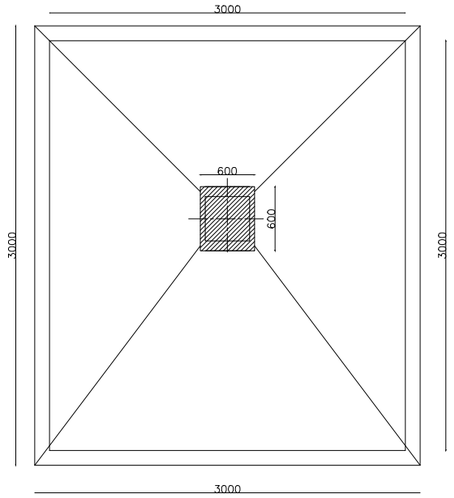


FOOTING F-1 AND PADESTEL P-1

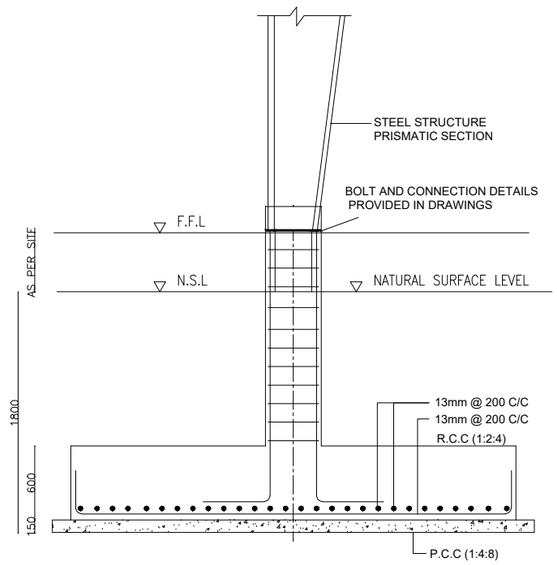

FOOTING F-3 WITH PEDESTAL P-1

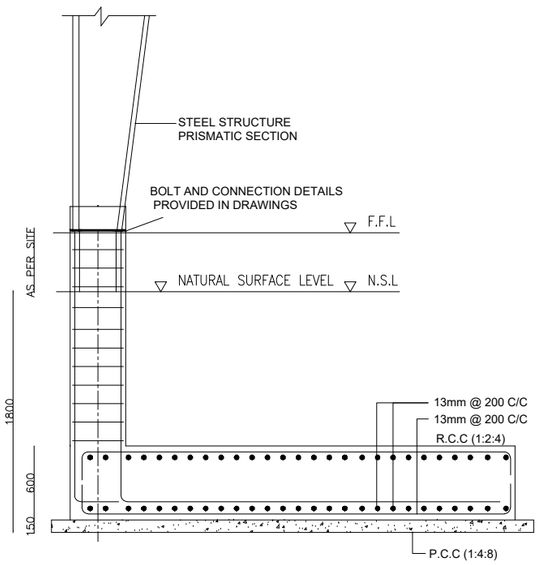


FOOTING F-4 WITH PEDESTAL P-2

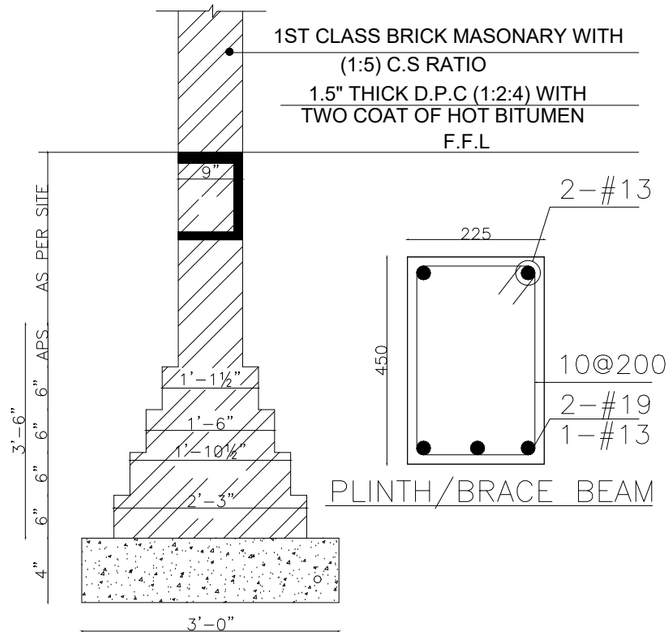


BRICK MASONRY SEC


PLINTH/BRACE BEAM

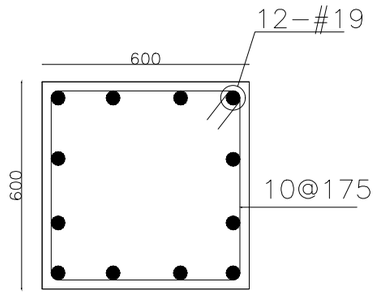


P-1

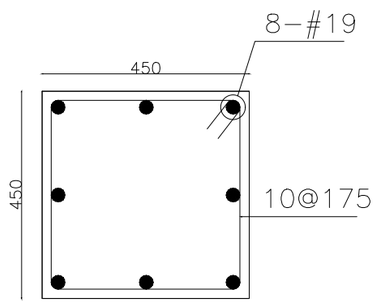

P-2

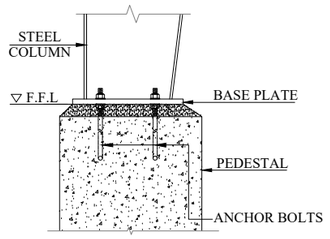

ANCHOR BOLT TYP DETAIL

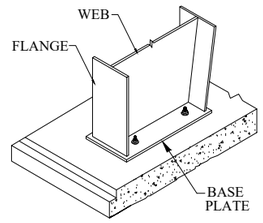

(SCAN FOR PROFILE)

REV.	DATE	DESCRIPTION	DRN	CHK	DSN
00	14-07-25	ISSUED FOR PROPOSAL	YAS	A.A	A.H


PROJECT:
PEB STEEL SHED (86'-6" X 105'-0")

CUSTOMER:
PX97 PADEL COURT, LAHORE


UEMS
Address: 4th Floor, Vouge Towers, MM Alam Road LHR.
Email : info@uems.com.pk
Tell : 0322-8419452 / 0300-0029937

JOB NUMBER		DRAWING NO.
SE-PEB-1211		PR-04


DRAWING TITLE:
FOOTING AND PEDESTAL SECTIONS

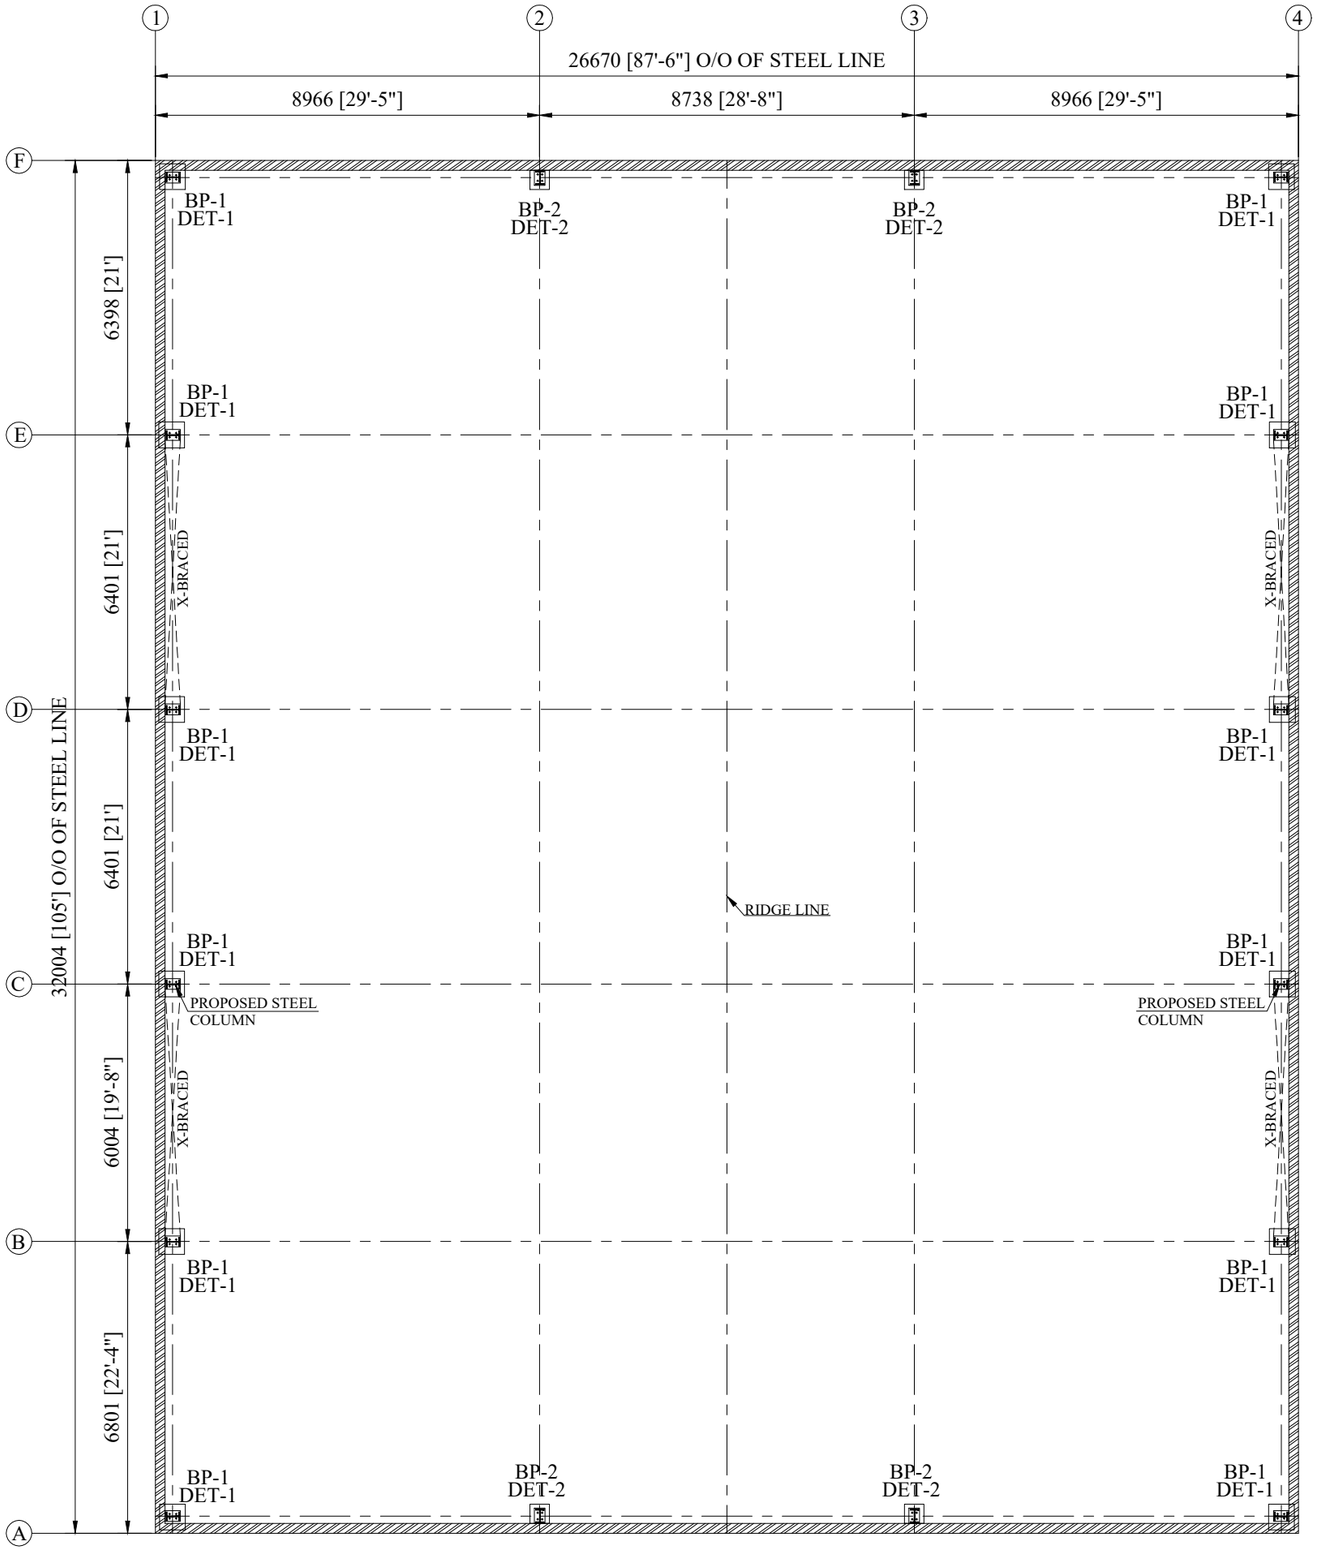

PEDESTAL AND BASE PLATE DETAILS

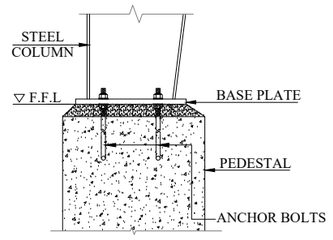

ANCHOR BOLT TYP DETAIL

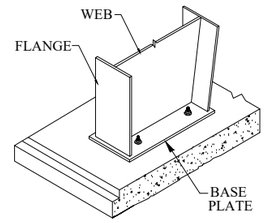

(SCAN FOR PROFILE)

REV.	DATE	DESCRIPTION	DRN	CHK	DSN
00	14-07-25	ISSUED FOR PROPOSAL	YAS	A.A	A.H

PROJECT:
PEB STEEL SHED (86'-6" X 105'-0")


CUSTOMER:
PX97 PADEL COURT, LAHORE

UEMS
Address: 4th Floor, Vouge Towers, MM Alam Road LHR.
Email : info@uems.com.pk
Tell : 0322-8419452 / 0300-0029937

JOB NUMBER		DRAWING NO.
SE-PEB-1211		PR-05


DRAWING TITLE:
BASE PLATE AND CONNECTION

ANCHOR BOLTS LAYOUT PLAN

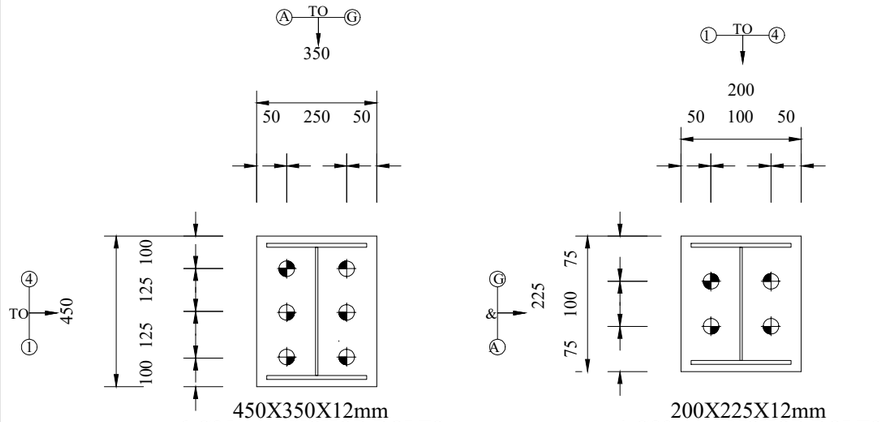


450X350X12mm
6-Ø25mm ANCHOR BOLTS
BP-01


200X225X12mm
4-Ø20mm ANCHOR BOLTS
BP-02

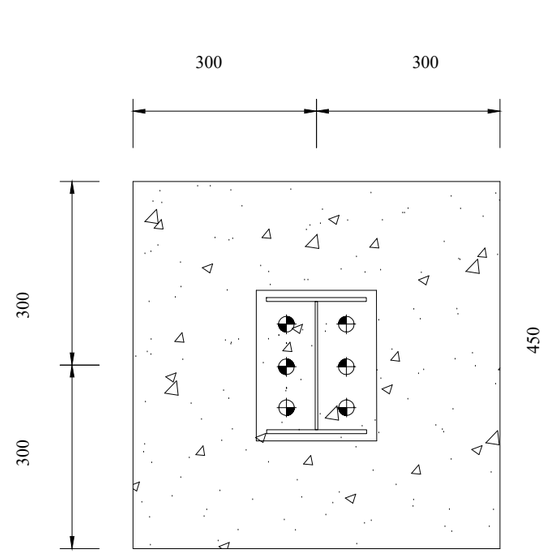

R.C.C PEDESTAL DETAIL-1
(24"X24")

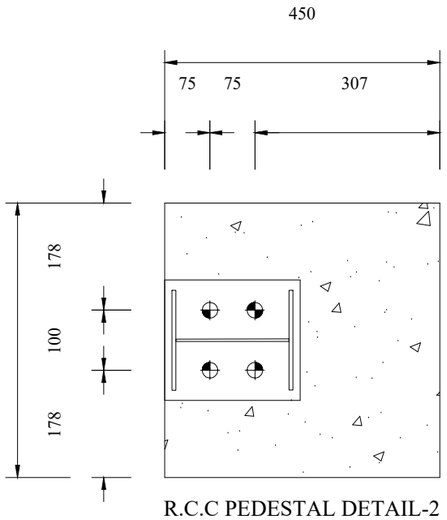

R.C.C PEDESTAL DETAIL-2
(18"X18")

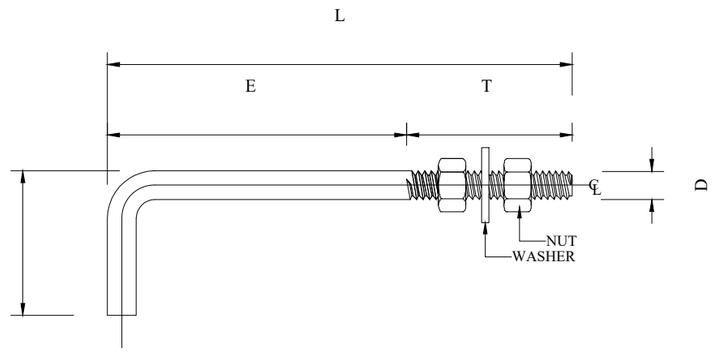


ANCHOR BOLT ASSEMBLY

NOTE:-
EACH SUPPLIED ASSEMBLY CONSISTS OF
1-'L' SHAPED ANCHOR BOLT
2-HEXAGONAL NUTS AND
1-WASHER


LEGEND:-
QTY:-QUANTITY
T:-THREADED BOLT PROJECTION
E:-UNTHREADED STRAIGHT LENGTH
L:-VERTICAL LENGTH
X:-HOOK LENGTH
LO:-OVERALL LENGTH
WT:-WEIGHT
R:-BEND RADIUS
Lc:-CENTERLINE LENGTH

ANCHOR BOLT SCHEDULE

PART MARK	DIAMETER(D)	QTY	T (mm)	E (mm)	L (mm)	X (mm)	Lo (mm)	Wt (mm)	R (mm)	Lc (mm)
SANBO51	20mm	16	100	275	375	120	495	0.828	40	458
SANBO52	25mm	72	150	300	450	175	625	1.599	50	579

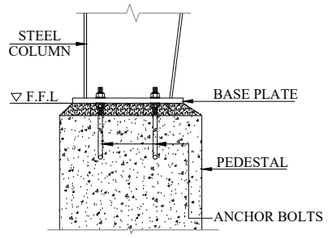

ANCHOR BOLT TYP DETAIL

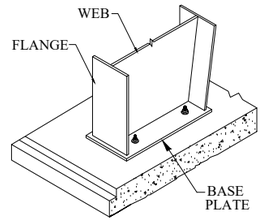

(SCAN FOR PROFILE)

REV.	DATE	DESCRIPTION	DRN	CHK	DSN
00	14-07-25	ISSUED FOR PROPOSAL	YAS	A.A	A.H


PROJECT:
PEB STEEL SHED (86'-6" X 105'-0")

CUSTOMER:
PX97 PADEL COURT, LAHORE


UEMS
Address: 4th Floor, Vouge Towers, MM Alam Road LHR.
Email : info@uems.com.pk
Tell : 0322-8419452 / 0300-0029937


JOB NUMBER		DRAWING NO.
SE-PEB-1211		PR-06

DRAWING TITLE:
BASE PLATE AND BOLT DETAILS

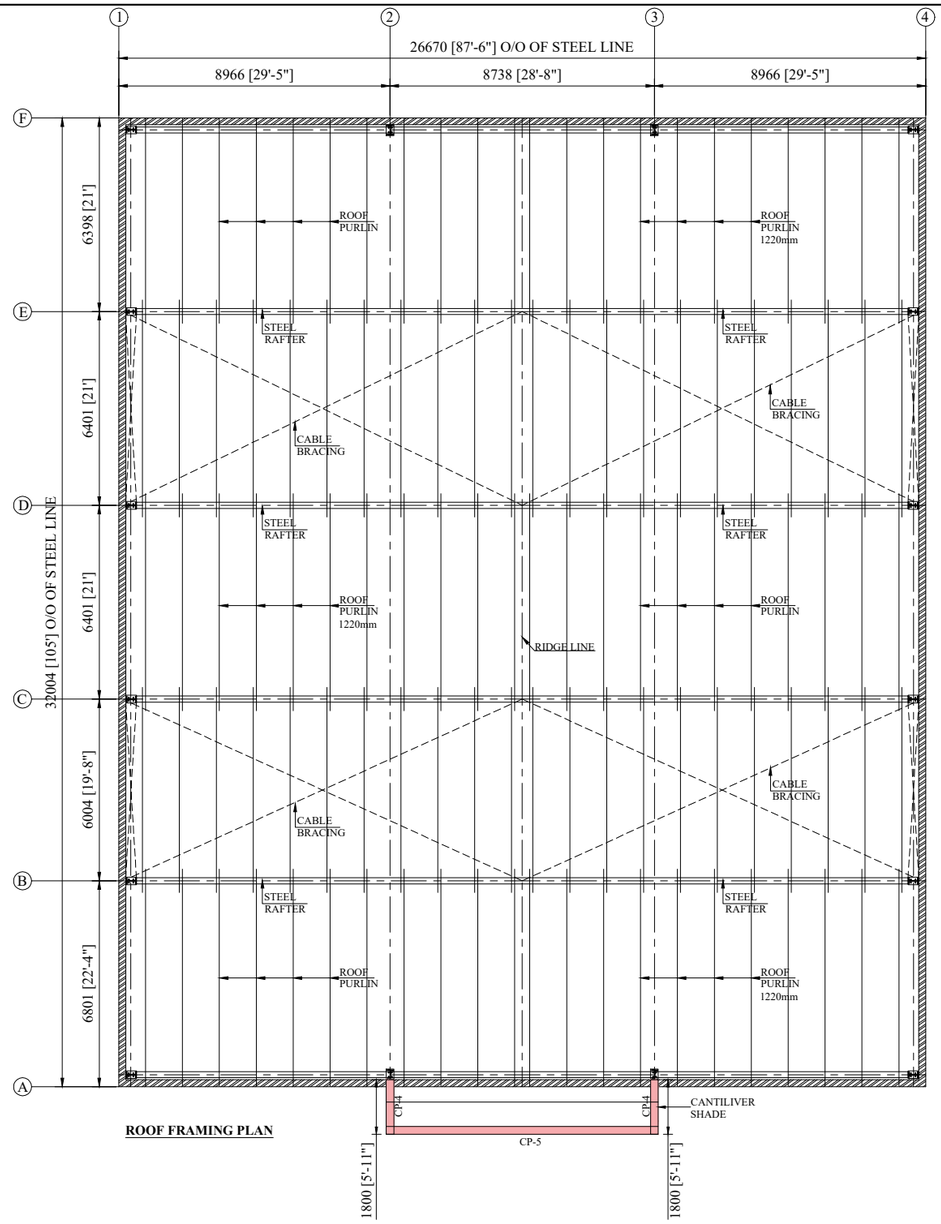


ROOF FRAMING PLAN

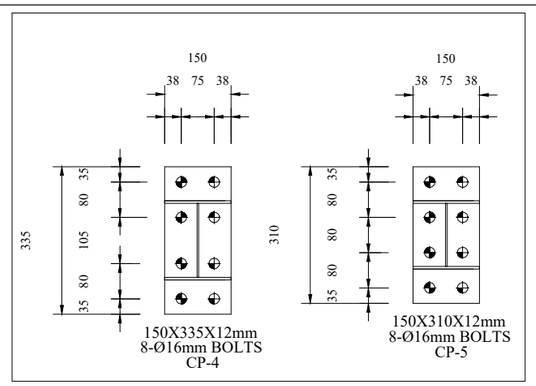


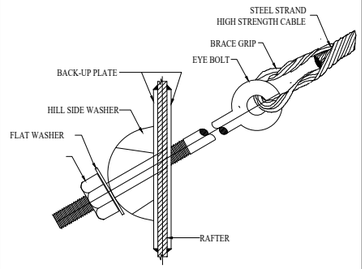

CABLE BRACE DETAIL

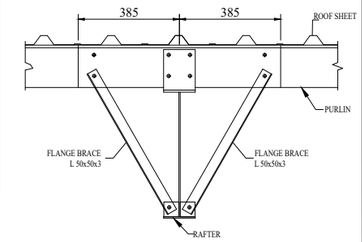

FLANGE BRACE & LAP DETAIL

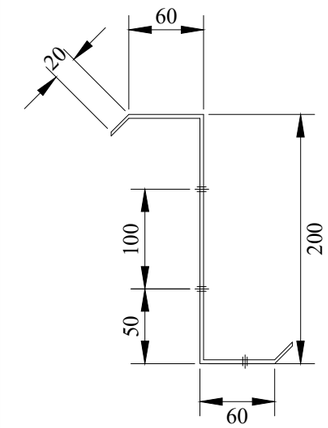

DETAILS AND DIMENSIONS
0F Z PURLIN

REV.	DATE	DESCRIPTION	DRN	CHK	DSN
00	14-07-25	ISSUED FOR PROPOSAL	YAS	A.A	A.H


PROJECT:
PEB STEEL SHED (86'-6" X 105'-0")

CUSTOMER:
PX97 PADEL COURT, LAHORE


UEMS
Address: 4th Floor, Vouge Towers, MM Alam Road LHR.
Email : info@uems.com.pk
Tell : 0322-8419452 / 0300-0029937

JOB NUMBER		DRAWING NO.
SE-PEB-1211		PR-07

DRAWING TITLE:
ROOF PURLIN DETAILS

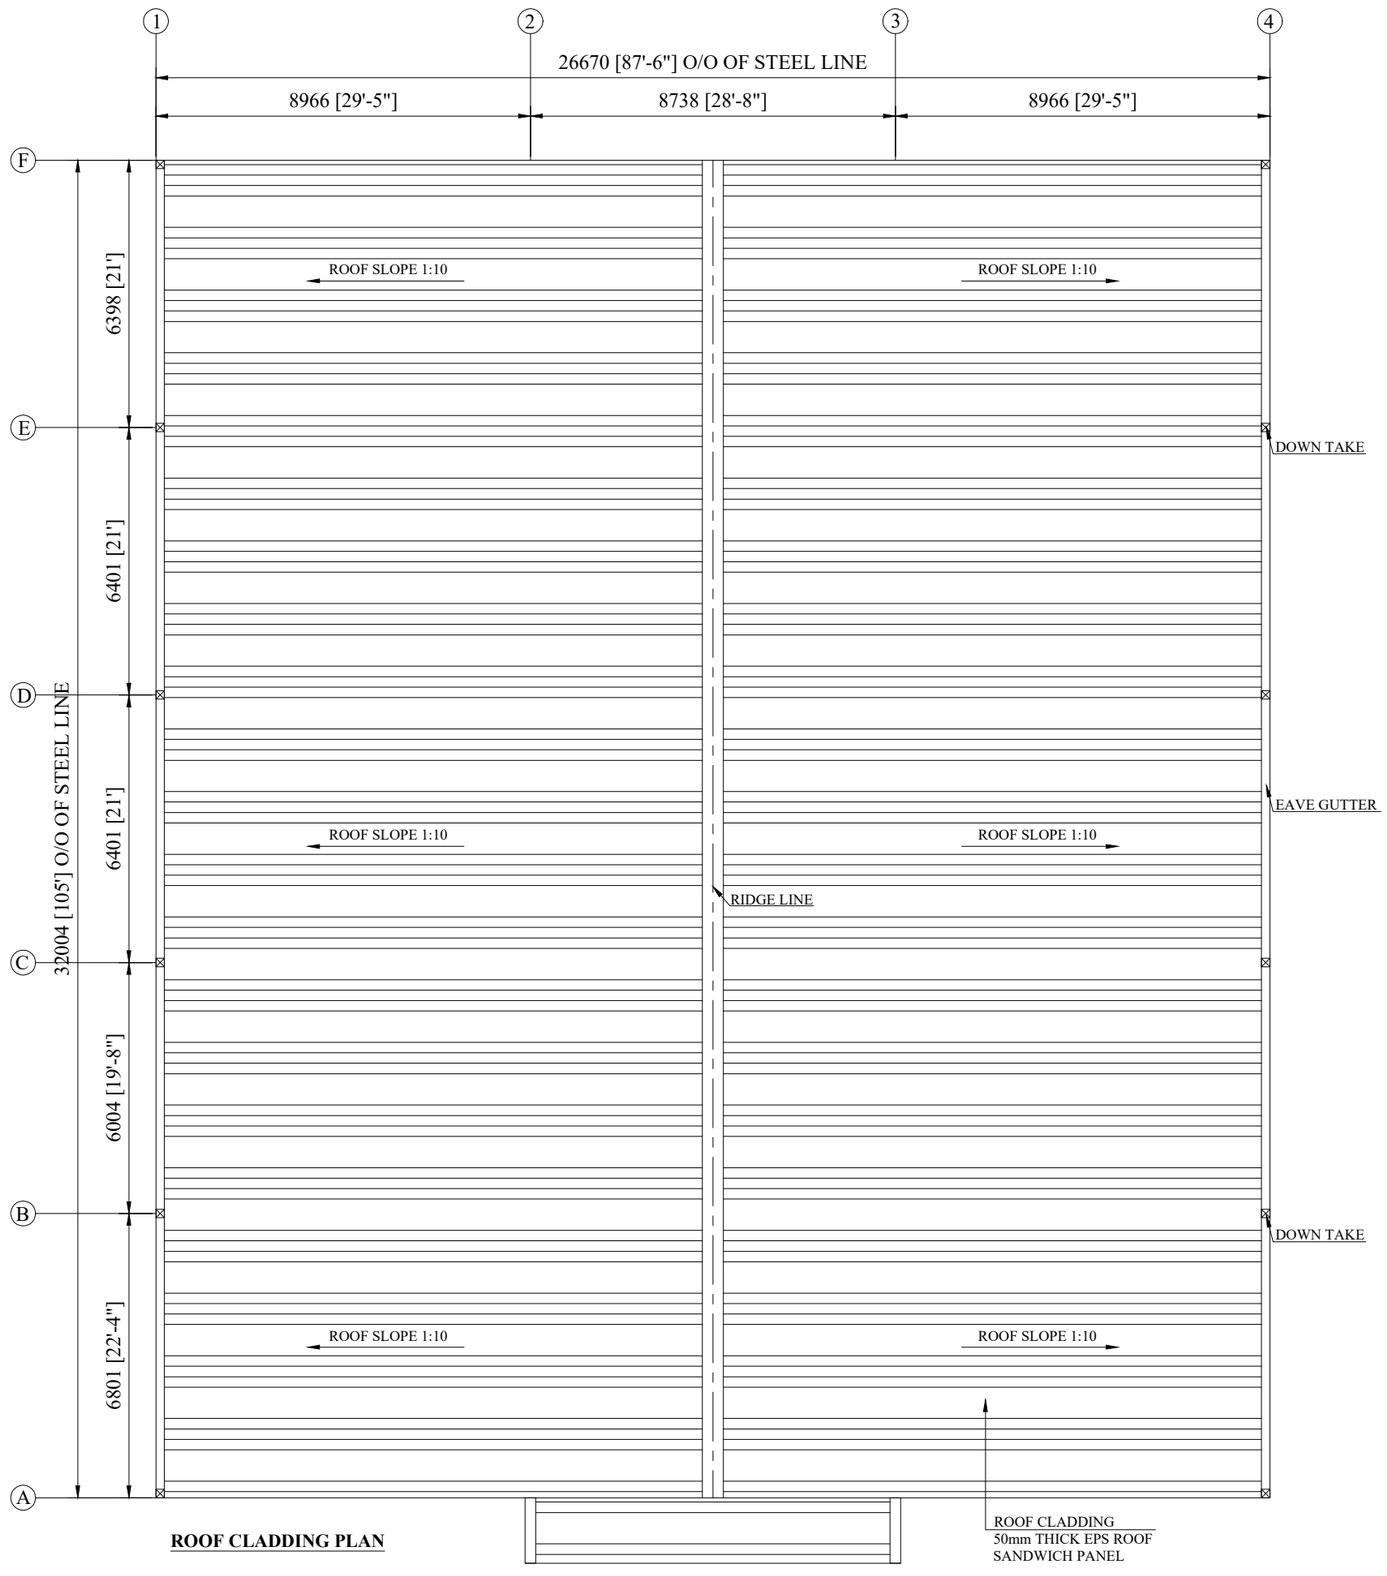

ROOF CLADDING PLAN

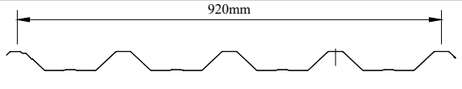

SEEMLOCK SHEET 0.5MM

(SCAN FOR PROFILE)

REV.	DATE	DESCRIPTION	DRN	CHK	DSN
00	14-07-25	ISSUED FOR PROPOSAL	YAS	A.A	A.H


PROJECT:
PEB STEEL SHED (86'-6" X 105'-0")

CUSTOMER:
PX97 PADEL COURT, LAHORE


UEMS
Address: 4th Floor, Vouge Towers, MM Alam Road LHR.
Email : info@uems.com.pk
Tell : 0322-8419452 / 0300-0029937

JOB NUMBER	DRAWING NO.
SE-PEB-1211	PR-08

DRAWING TITLE:
ROOF CLADDING PLAN

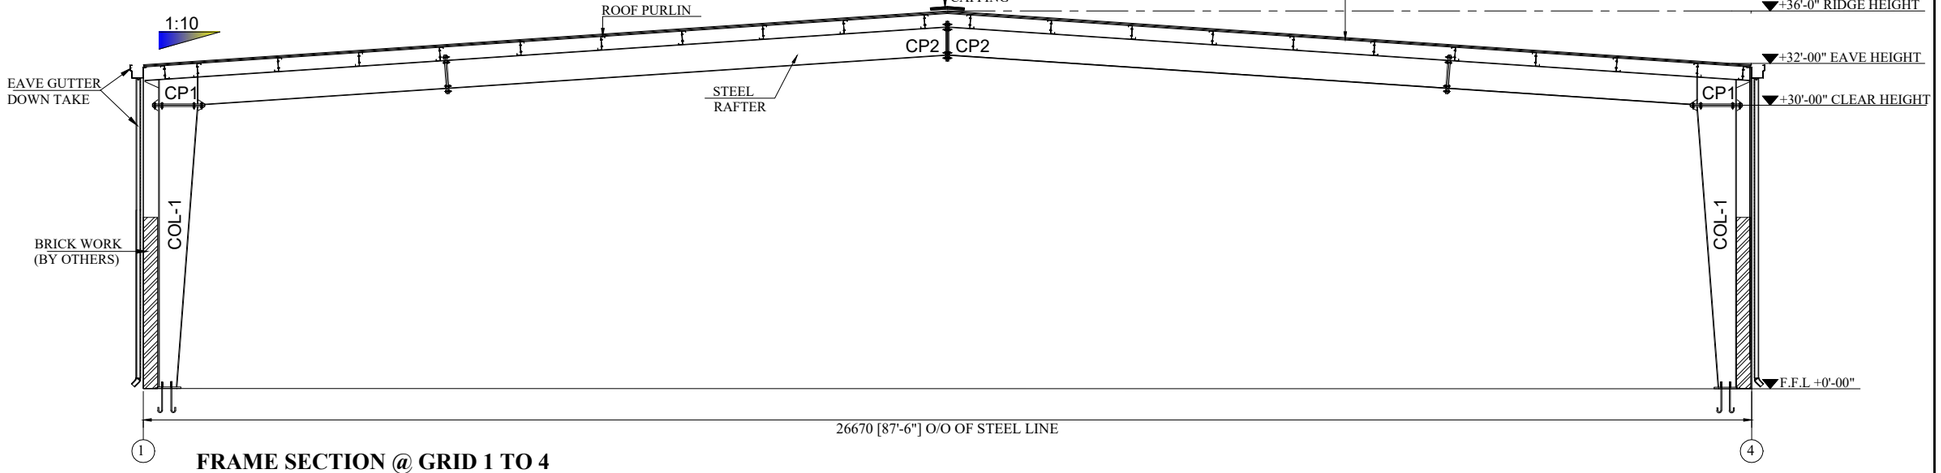


FRAME SECTION @ GRID 1 TO 4

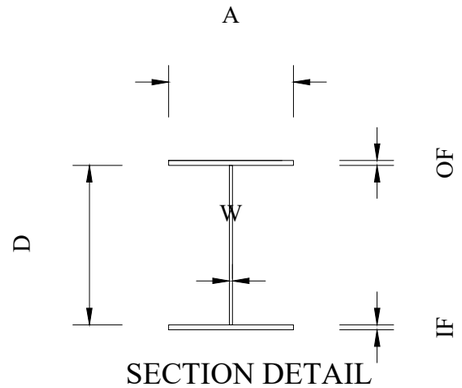


SECTION DETAIL
COLUMN & RAFTER

STEEL COLUMN & RAFTER SCHEDULE					
NUMBER	D (MM)	W (MM)	A (MM)	OF (MM)	IF (MM)
COL-01	350	4	150	5	5
COL-02	200	4	150	6	6
RFT-01	450	4	150	5	5


*OF=OUTER FLANGE
*IF=INNER FLANGE
*W=WEB

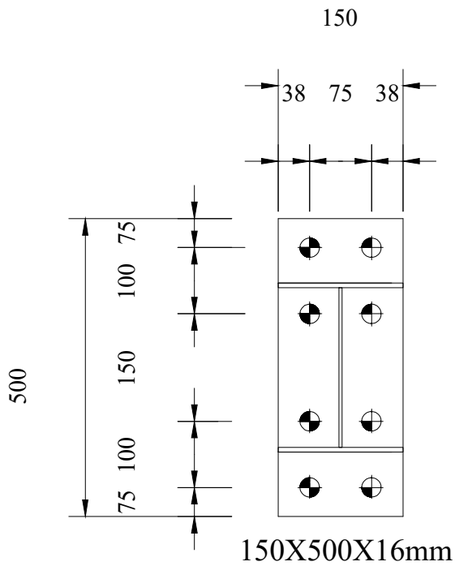


150X500X16mm
8-Ø16mm BOLTS
CP-1

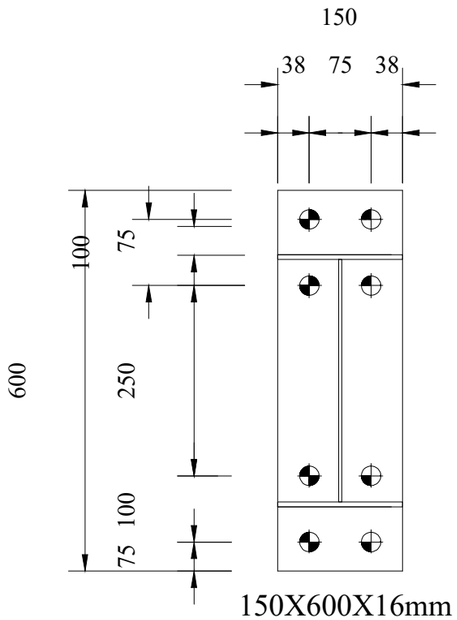


150X600X16mm
8-Ø16mm BOLTS
CP-2

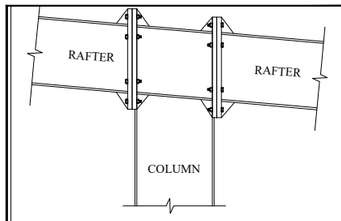


TYP. CONNECTION DETAIL

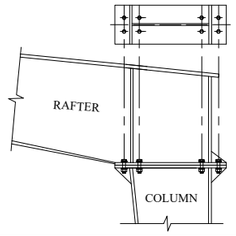

TYP. CONNECTION DETAIL

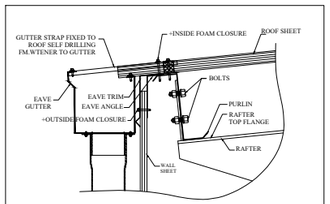

EAVE DETAIL

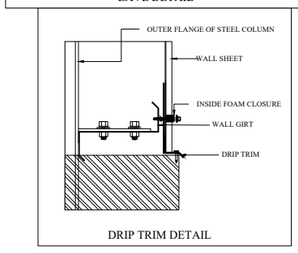

DRIP TRIM DETAIL

REV.	DATE	DESCRIPTION	DRN	CHK	DSN
00	14-07-25	ISSUED FOR PROPOSAL	YAS	A.A	A.H


PROJECT:
PEB STEEL SHED (86'-6" X 105'-0")

CUSTOMER:
PX97 PADEL COURT, LAHORE


UEMS
Address: 4th Floor, Vouge Towers, MM Alam Road LHR.
Email : info@uems.com.pk
Tell : 0322-8419452 / 0300-0029937

JOB NUMBER		DRAWING NO.
SE-PEB-1211		PR-09


DRAWING TITLE:
RAFTER AND COLUMN SECTION

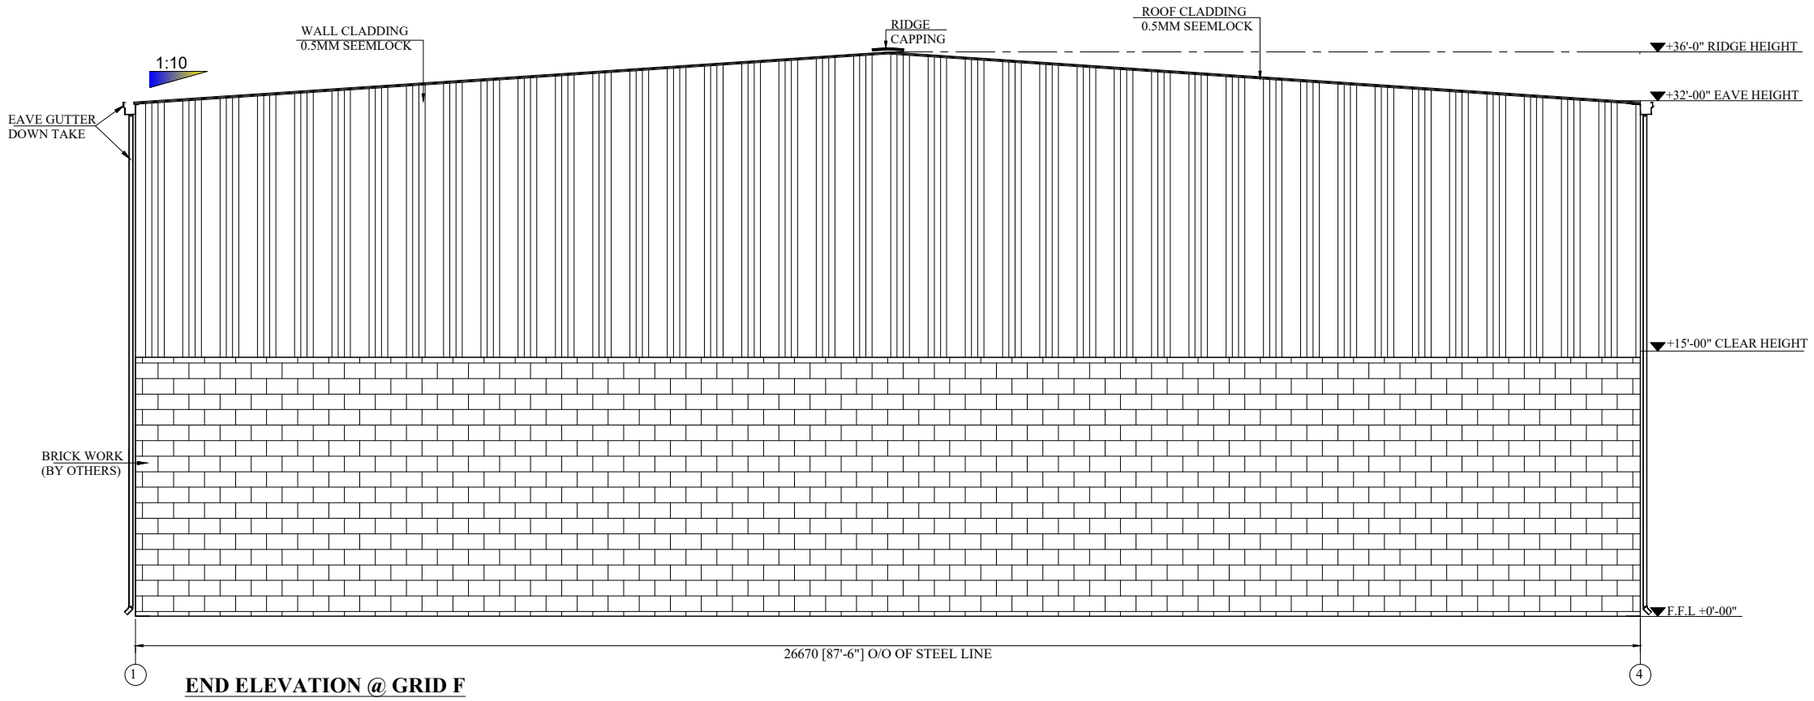


END ELEVATION @ GRID F

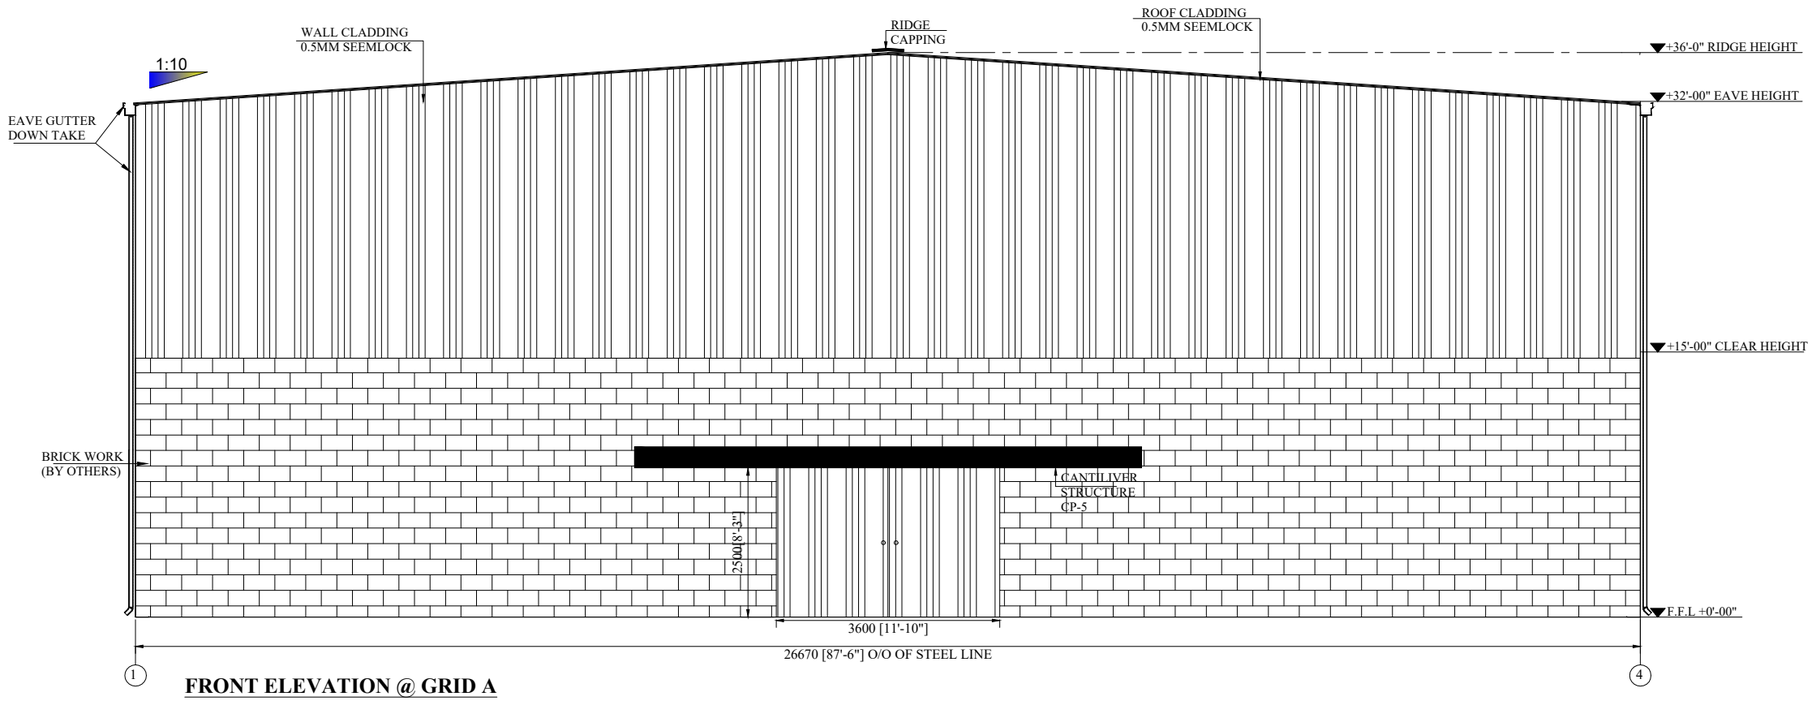


FRONT ELEVATION @ GRID A

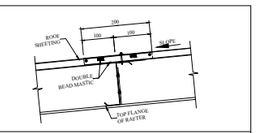

SHEETING LAP DETAIL

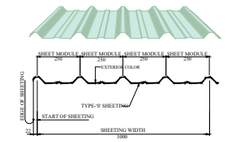

TYPE-'S' SHEETING MODULE

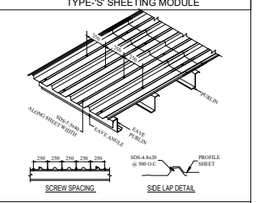

SCREW FIXING DETAIL

(SCAN FOR PROFILE)

REV.	DATE	DESCRIPTION	DRN	CHK	DSN
00	14-07-25	ISSUED FOR PROPOSAL	YAS	A.A	A.H


PROJECT:
PEB STEEL SHED (86'-6" X 105'-0")

CUSTOMER:
PX97 PADEL COURT, LAHORE


UEMS
Address: 4th Floor, Vouge Towers, MM Alam Road LHR.
Email : info@uems.com.pk
Tell : 0322-8419452 / 0300-0029937

JOB NUMBER	DRAWING NO.
SE-PEB-1211	PR-10

DRAWING TITLE:
END ELEVATIONS

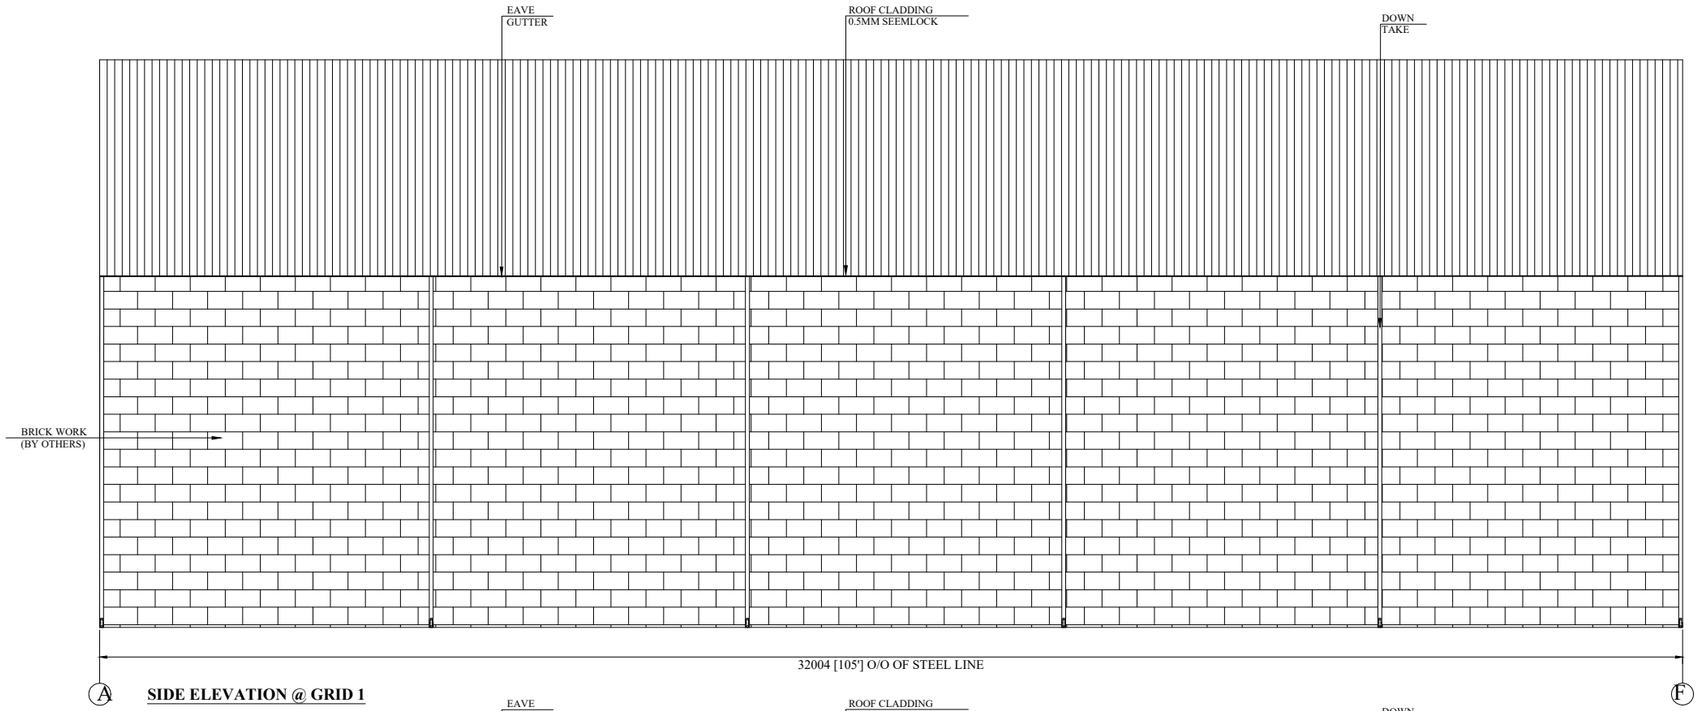

SIDE ELEVATION @ GRID 1

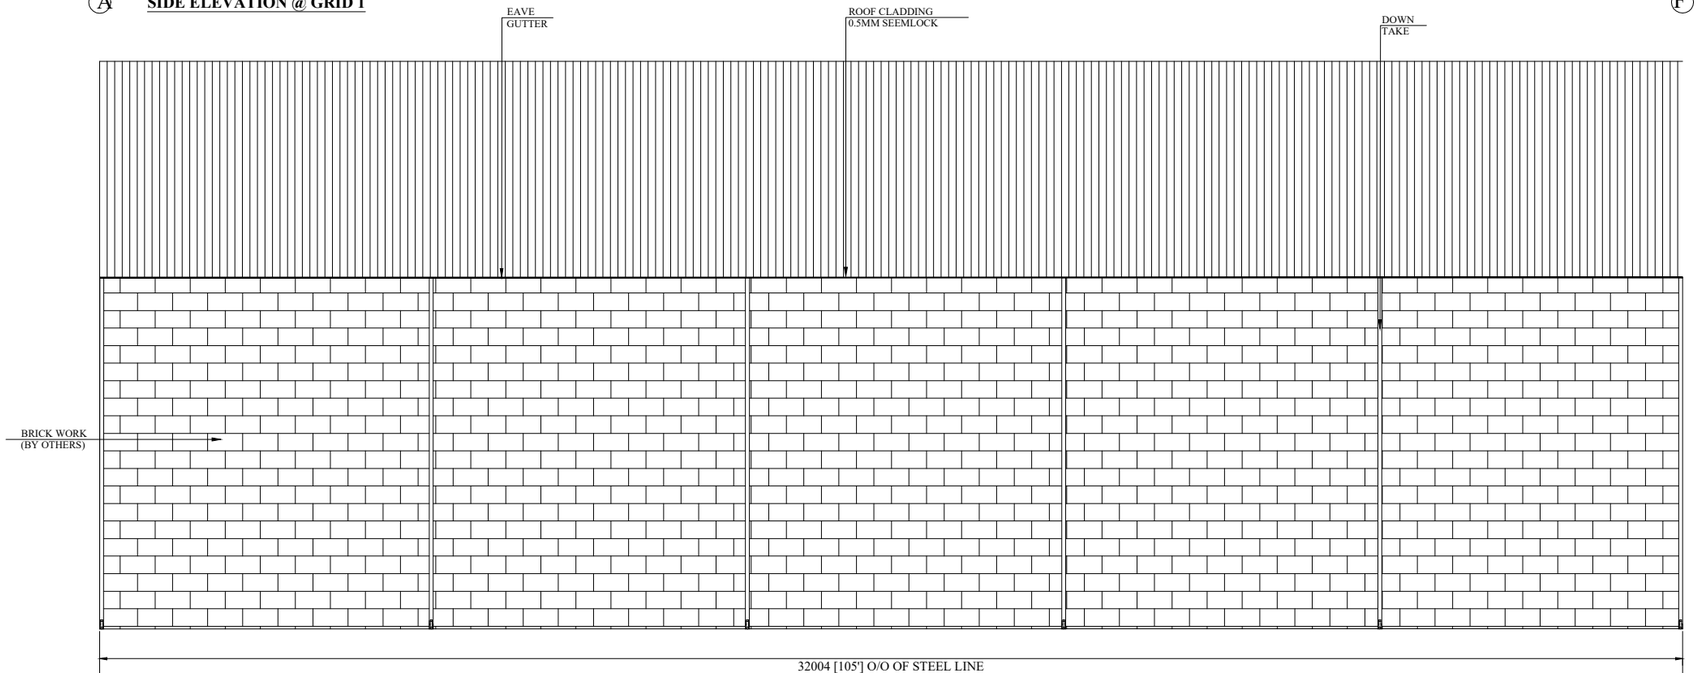

SIDE ELEVATION @ GRID 4

(SCAN FOR PROFILE)

REV.	DATE	DESCRIPTION	DRN	CHK	DSN
00	14-07-25	ISSUED FOR PROPOSAL	YAS	A.A	A.H

PROJECT:
PEB STEEL SHED (86'-6" X 105'-0")

CUSTOMER:
PX97 PADEL COURT, LAHORE

UEMS
Address: 4th Floor, Vouge Towers, MM Alam Road LHR.
Email : info@uems.com.pk
Tell : 0322-8419452 / 0300-0029937

JOB NUMBER	DRAWING NO.
SE-PEB-1211	PR-11

DRAWING TITLE:
SIDE ELEVATIONS