

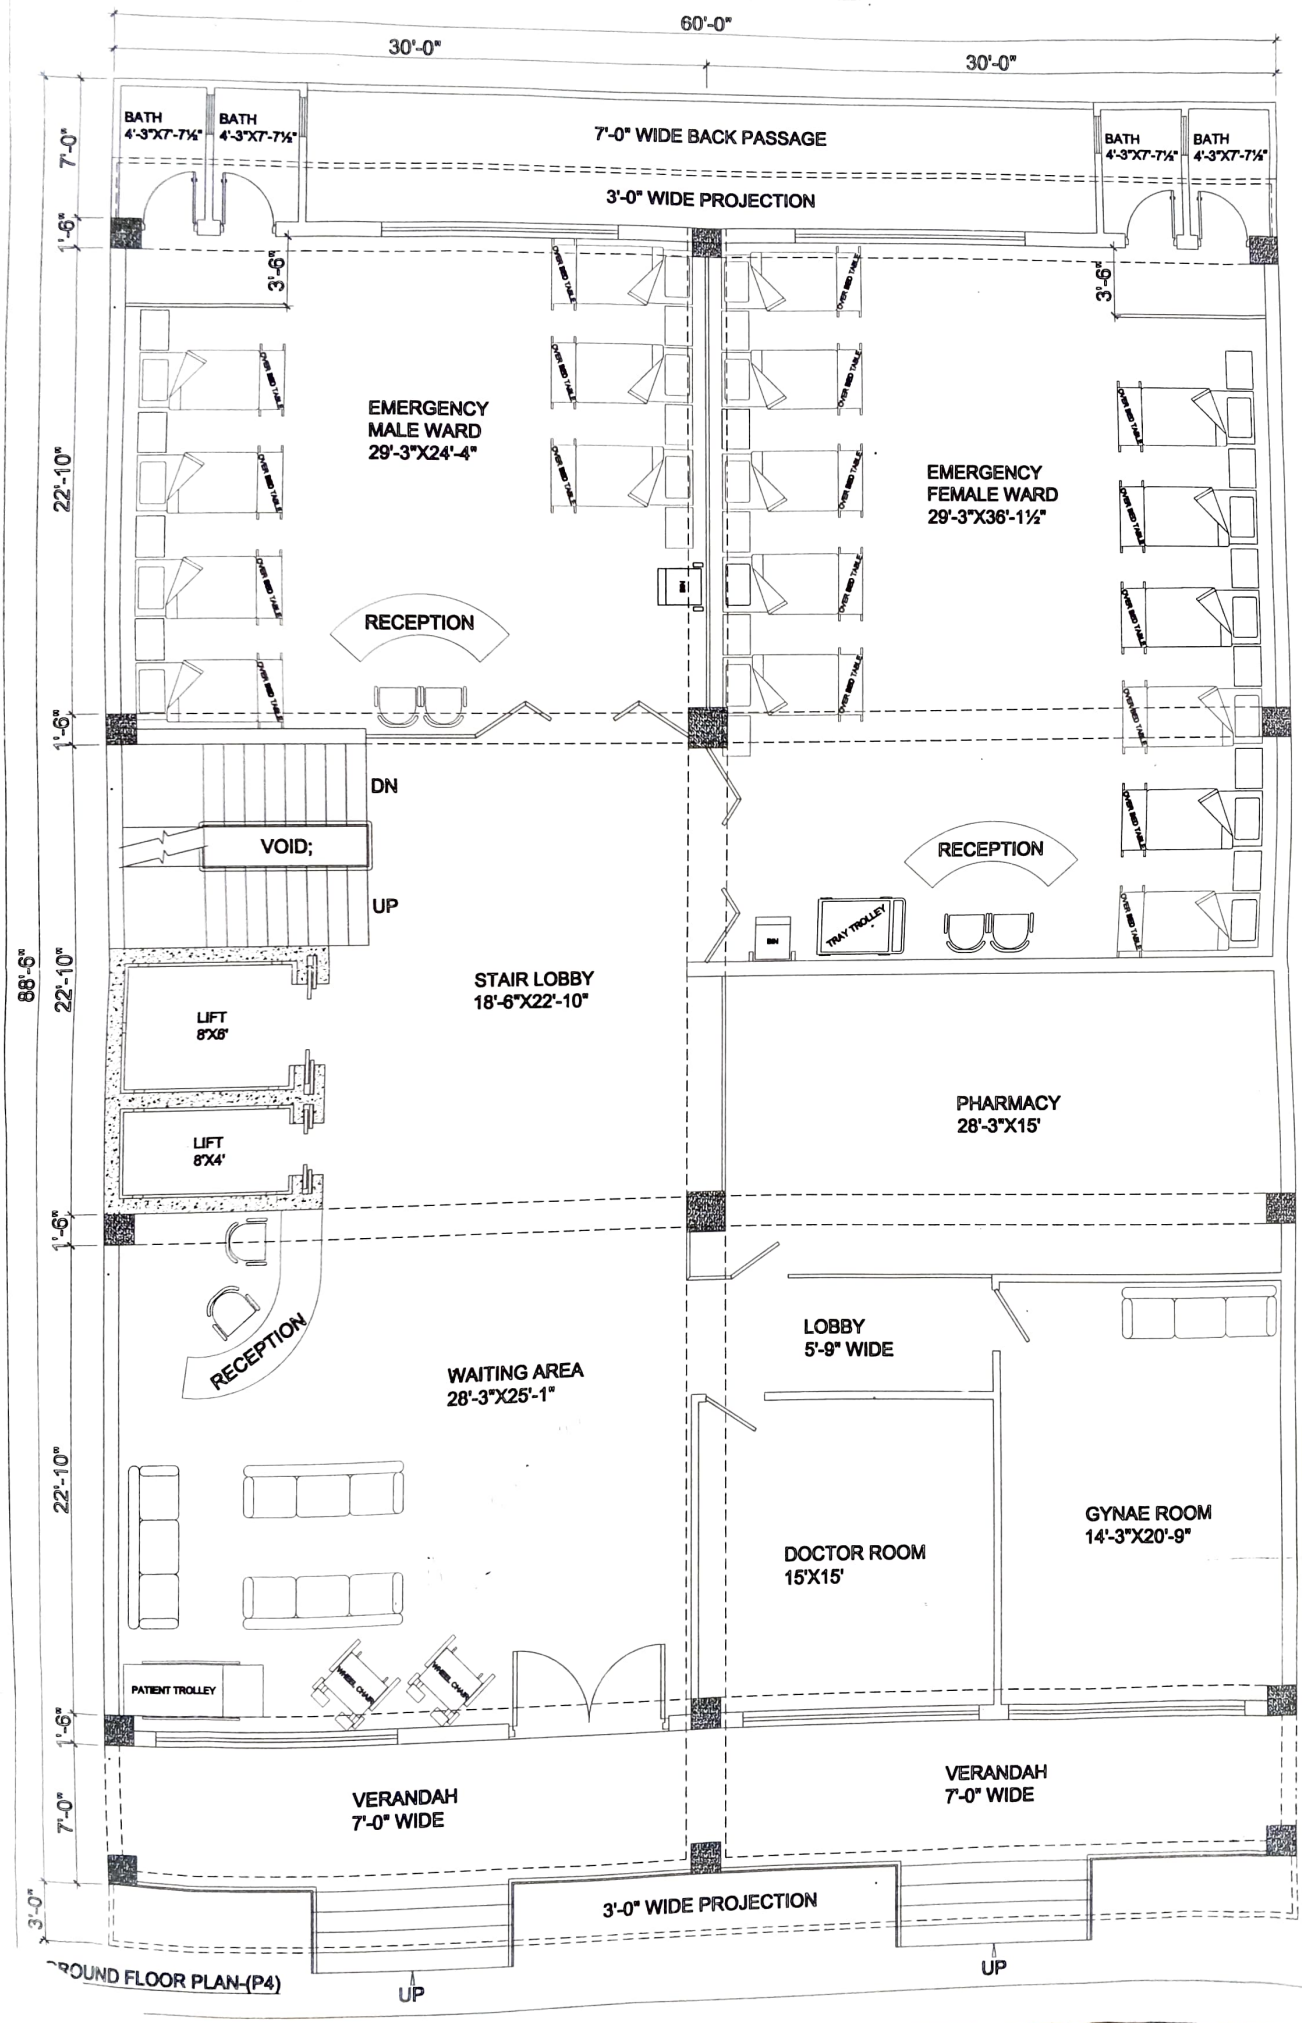



ROUND FLOOR PLAN-(P4)

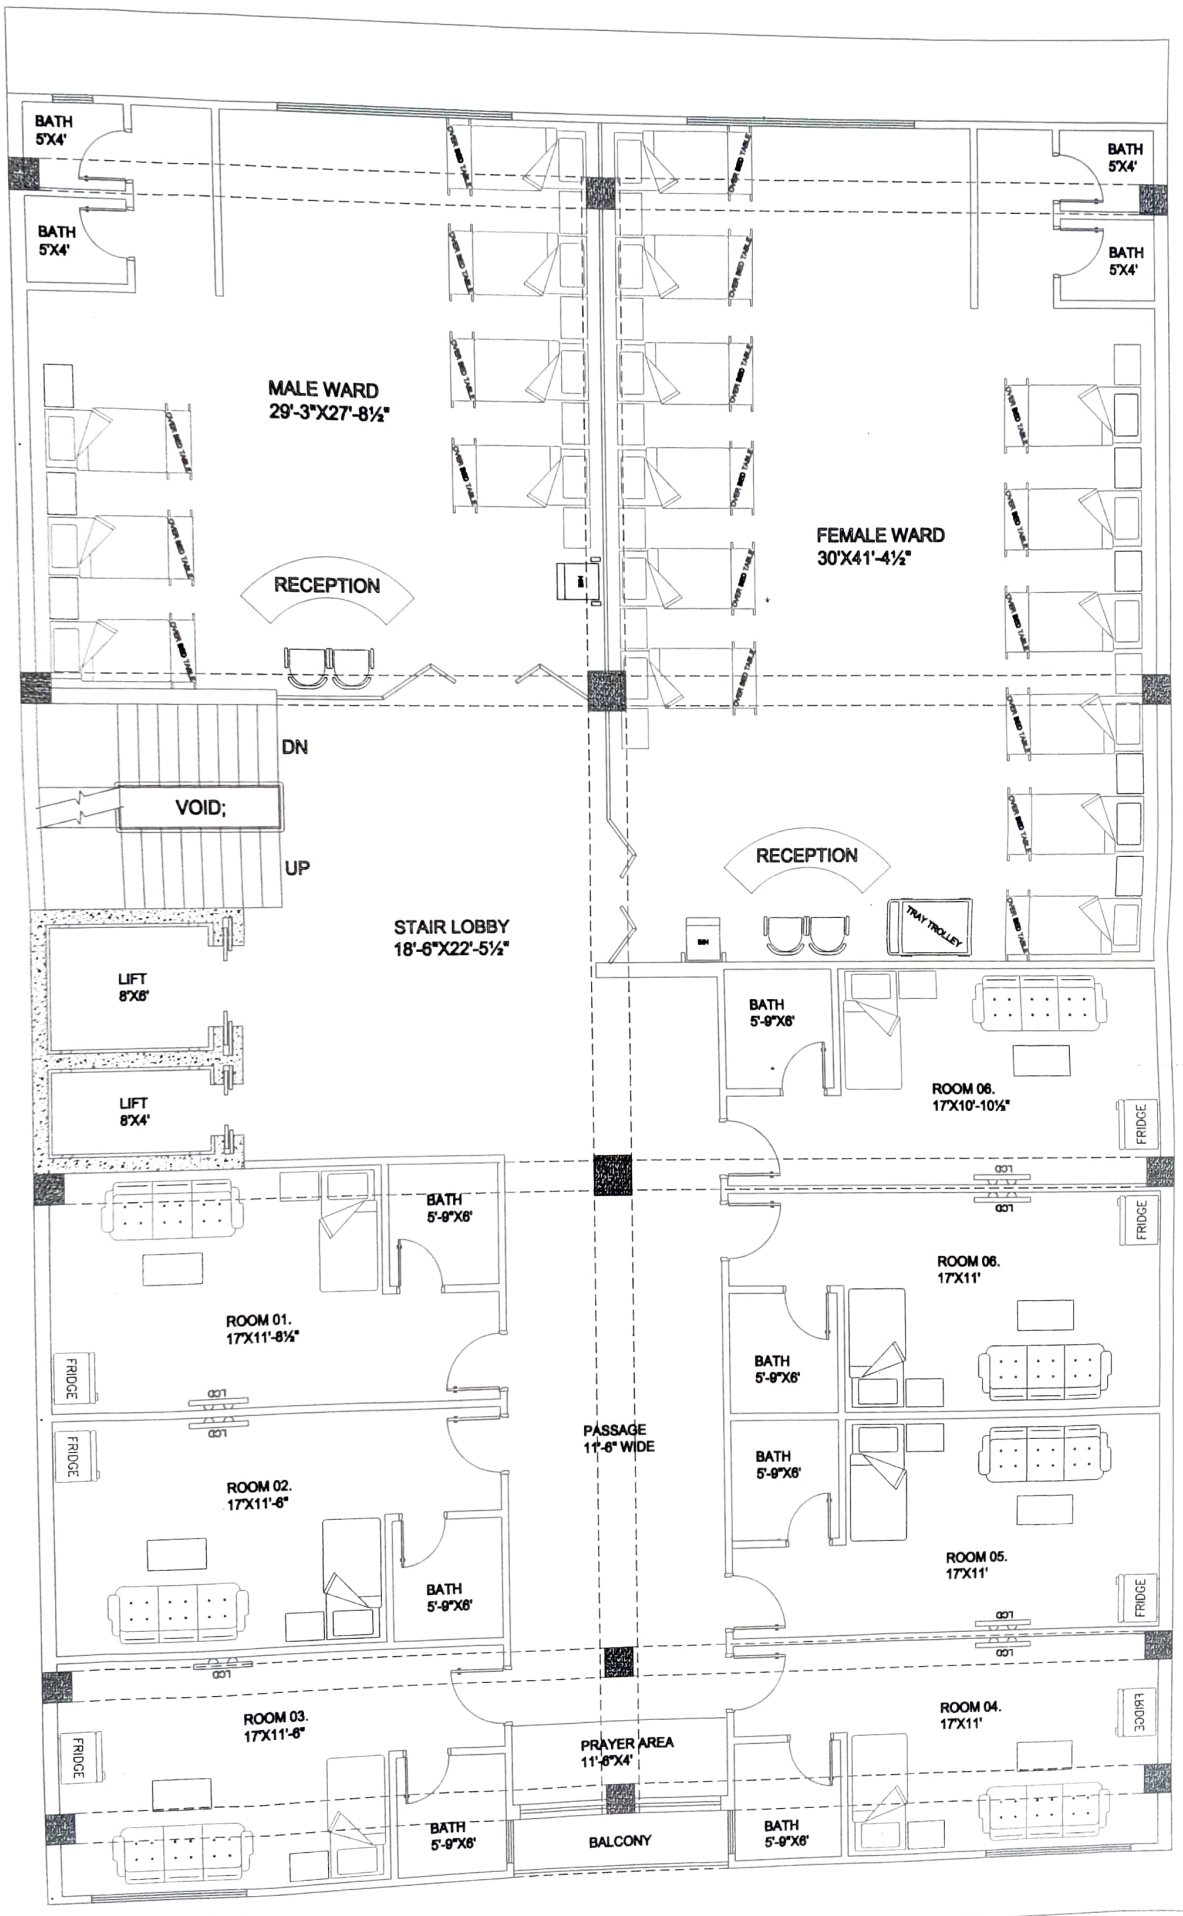


OND FLOOR PLAN-(P4)

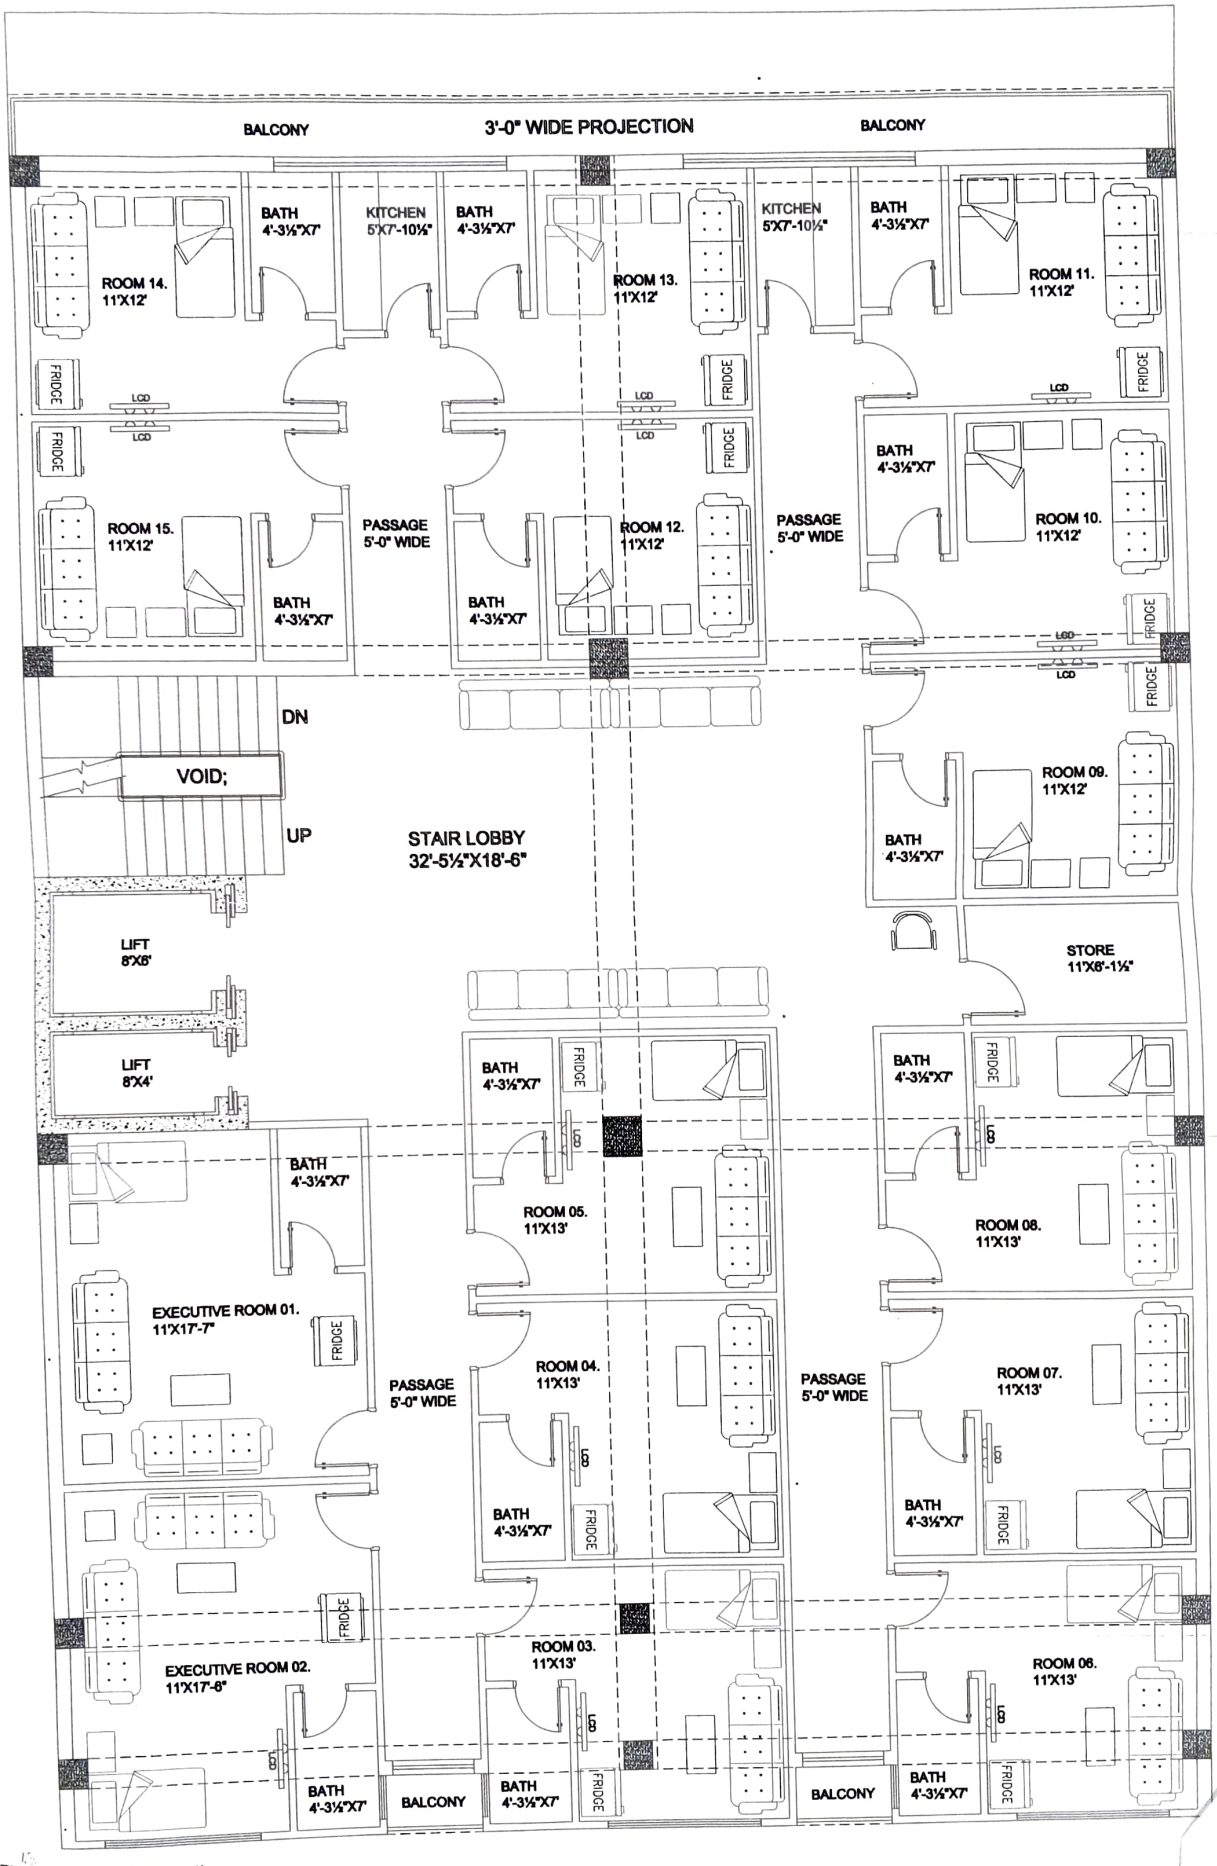


FIRST FLOOR PLAN-(P4)

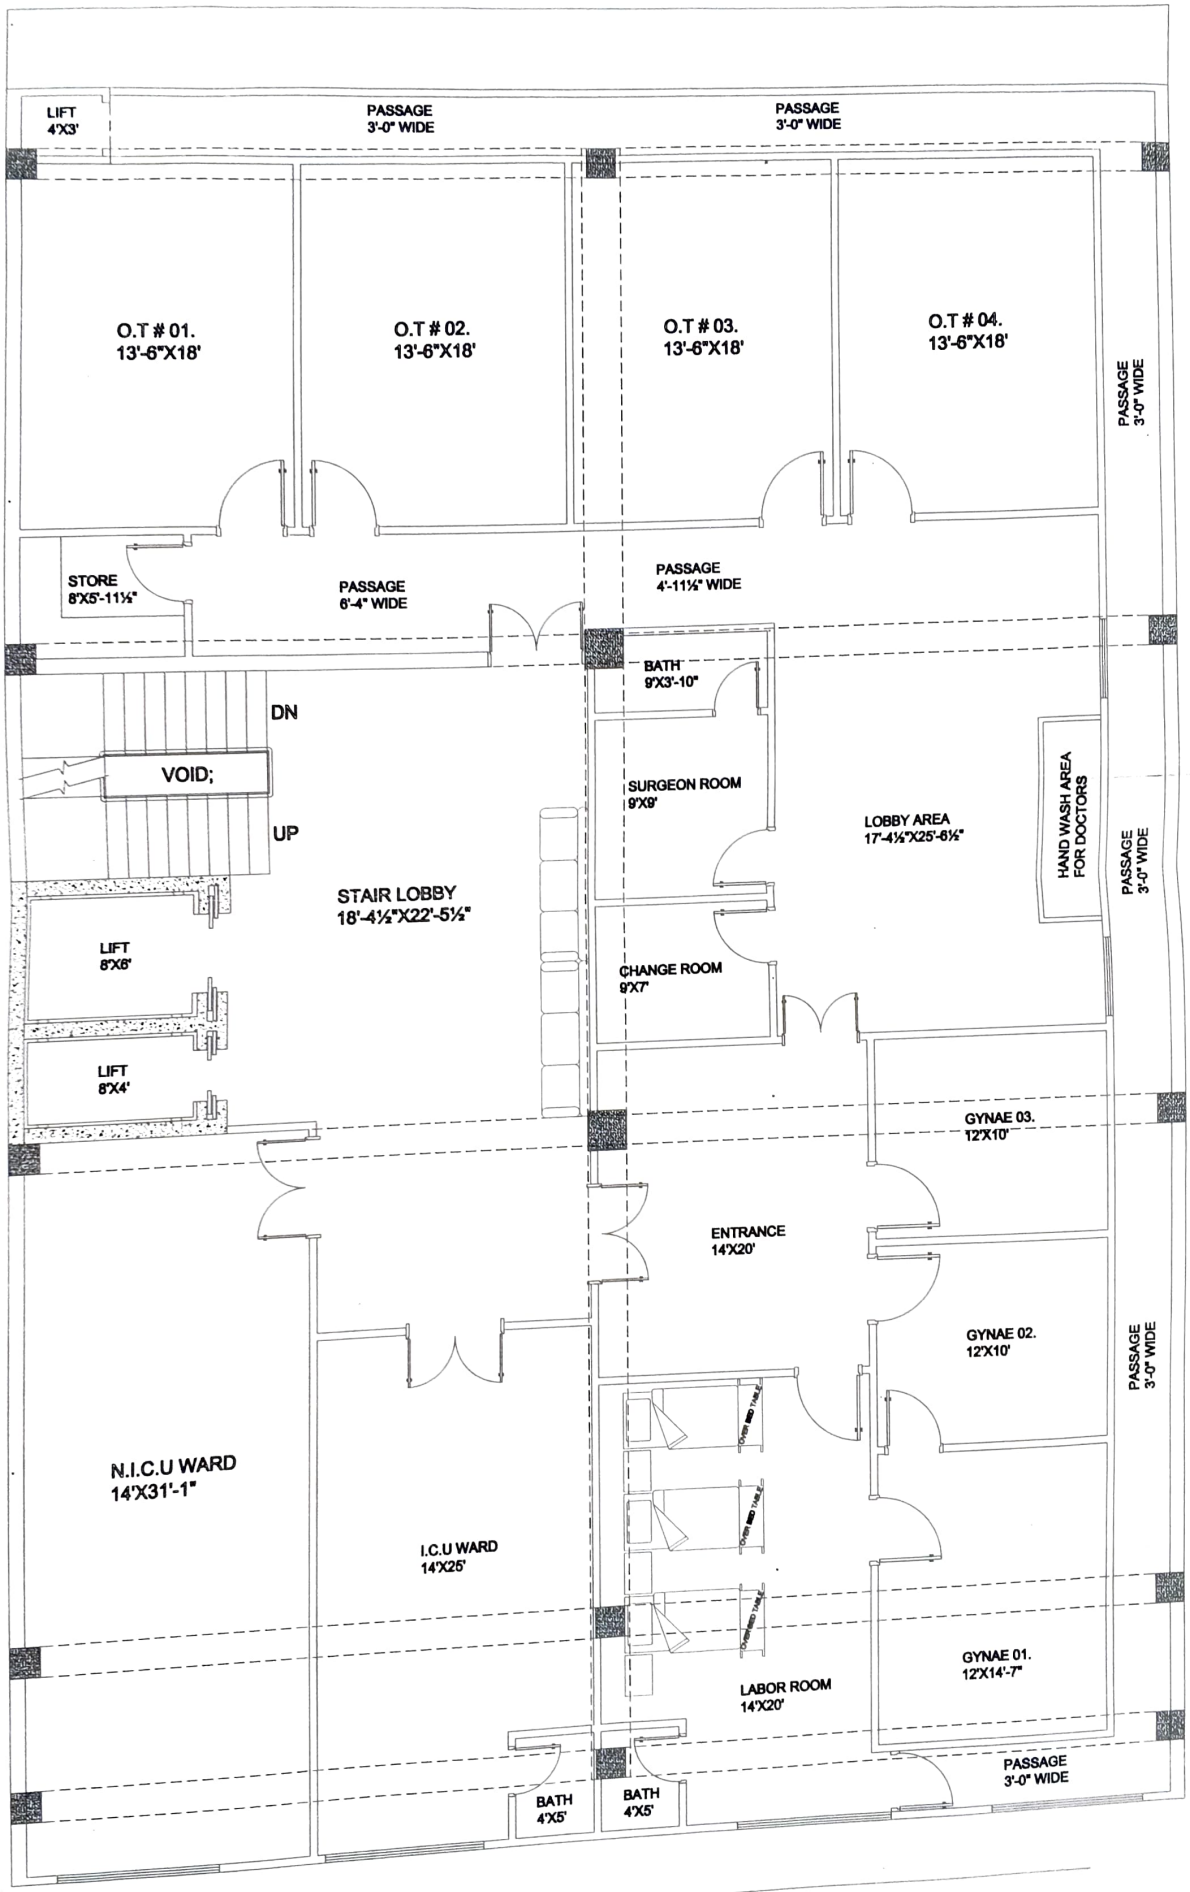
LIFT
4'X3'
PASSAGE
3'-0" WIDE
PASSAGE
3'-0" WIDE
O.T # 01.
13'-6"X18'
O.T # 02.
13'-6"X18'
O.T # 03.
13'-6"X18'
O.T # 04.
13'-6"X18'
PASSAGE
3'-0" WIDE
STORE
8'X5'-11½"
PASSAGE
6'-4" WIDE
PASSAGE
4'-11½" WIDE
BATH
9'X3'-10"
DN
VOID;
UP
SURGEON ROOM
9'X9'
LOBBY AREA
17'-4½"X25'-6½"
HAND WASH AREA
FOR DOCTORS
PASSAGE
3'-0" WIDE
STAIR LOBBY
18'-4½"X22'-5½"
LIFT
8'X6'
CHANGE ROOM
9'X7'
LIFT
8'X4'
GYNAE 03.
12'X10'
ENTRANCE
14'X20'
GYNAE 02.
12'X10'
PASSAGE
3'-0" WIDE
N.I.C.U WARD
14'X31'-1"
I.C.U WARD
14'X25'
GYNAE 01.
12'X14'-7"
LABOR ROOM
14'X20'
PASSAGE
3'-0" WIDE
BATH
4'X5'
BATH
4'X5'

OOR PLAN-(P4)

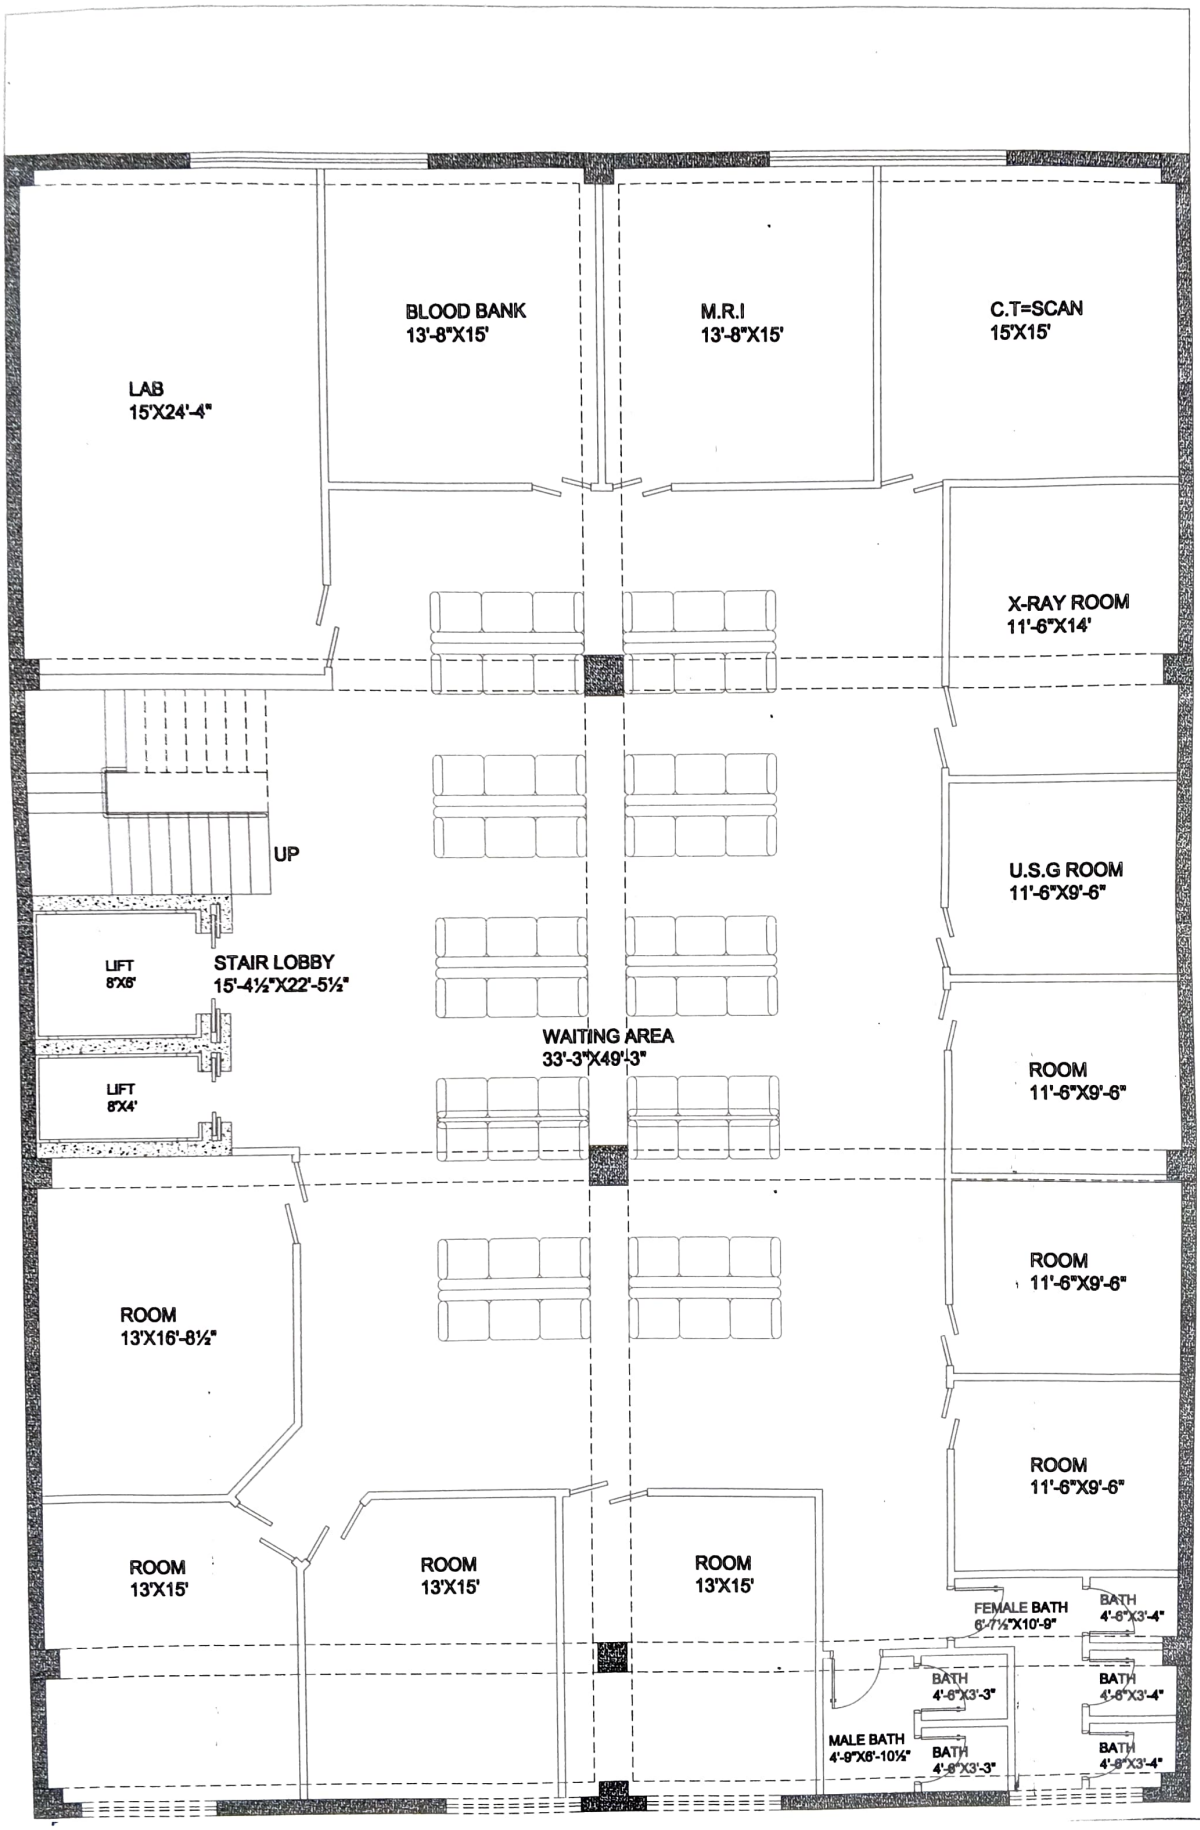

BASEMENT PLAN-(P4)

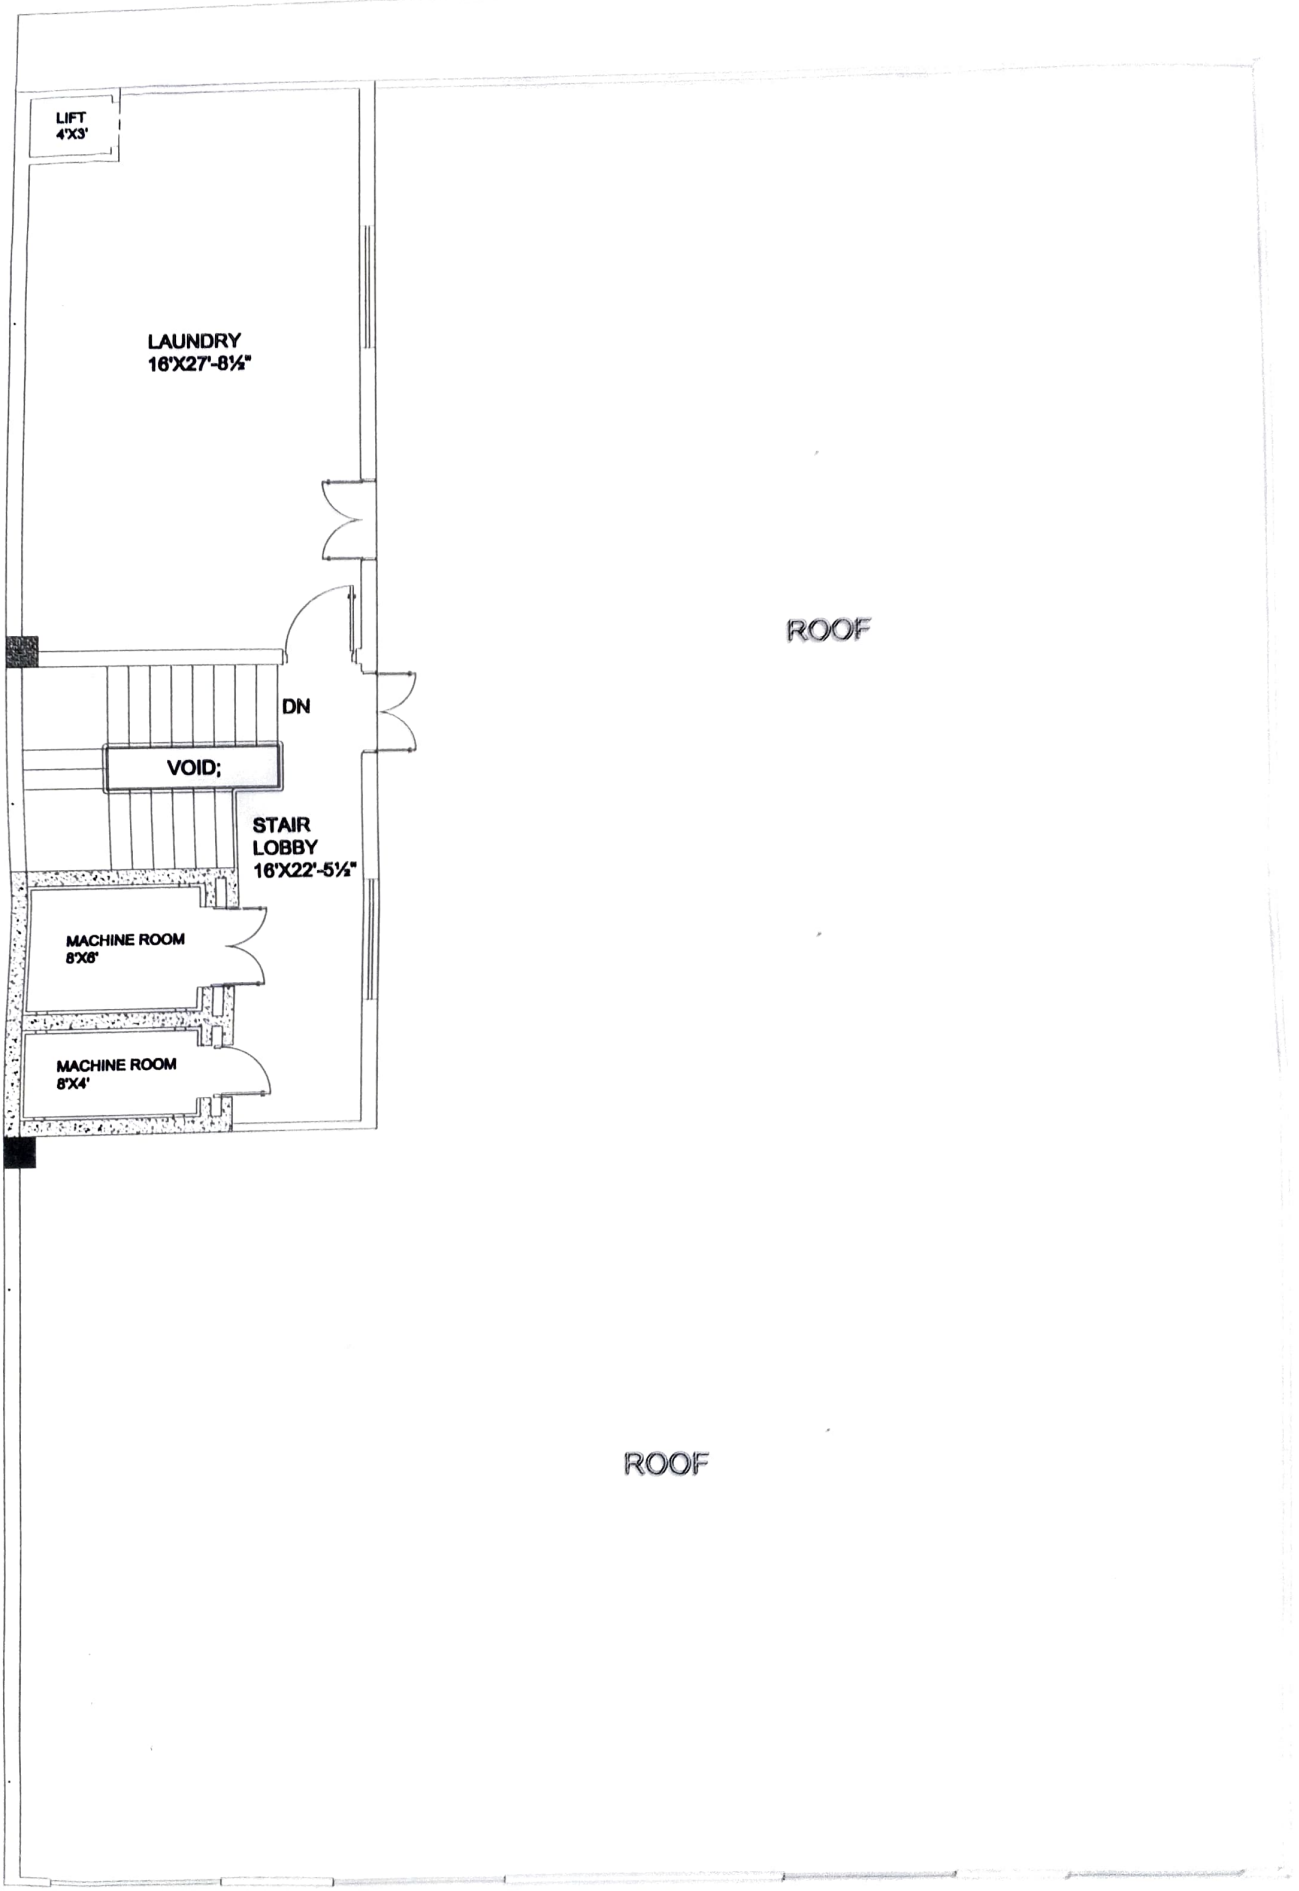
LIFT
4'X3'
LAUNDRY
16'X27'-8½"
ROOF
DN
VOID;
STAIR
LOBBY
16'X22'-5½"
MACHINE ROOM
8'X6'
MACHINE ROOM
8'X4'
ROOF

OOR PLAN-(P4)