

3D FRONT VIEW


DESIGN WING



3D FRONT AND SIDE VIEW



3D SIDE VIEW

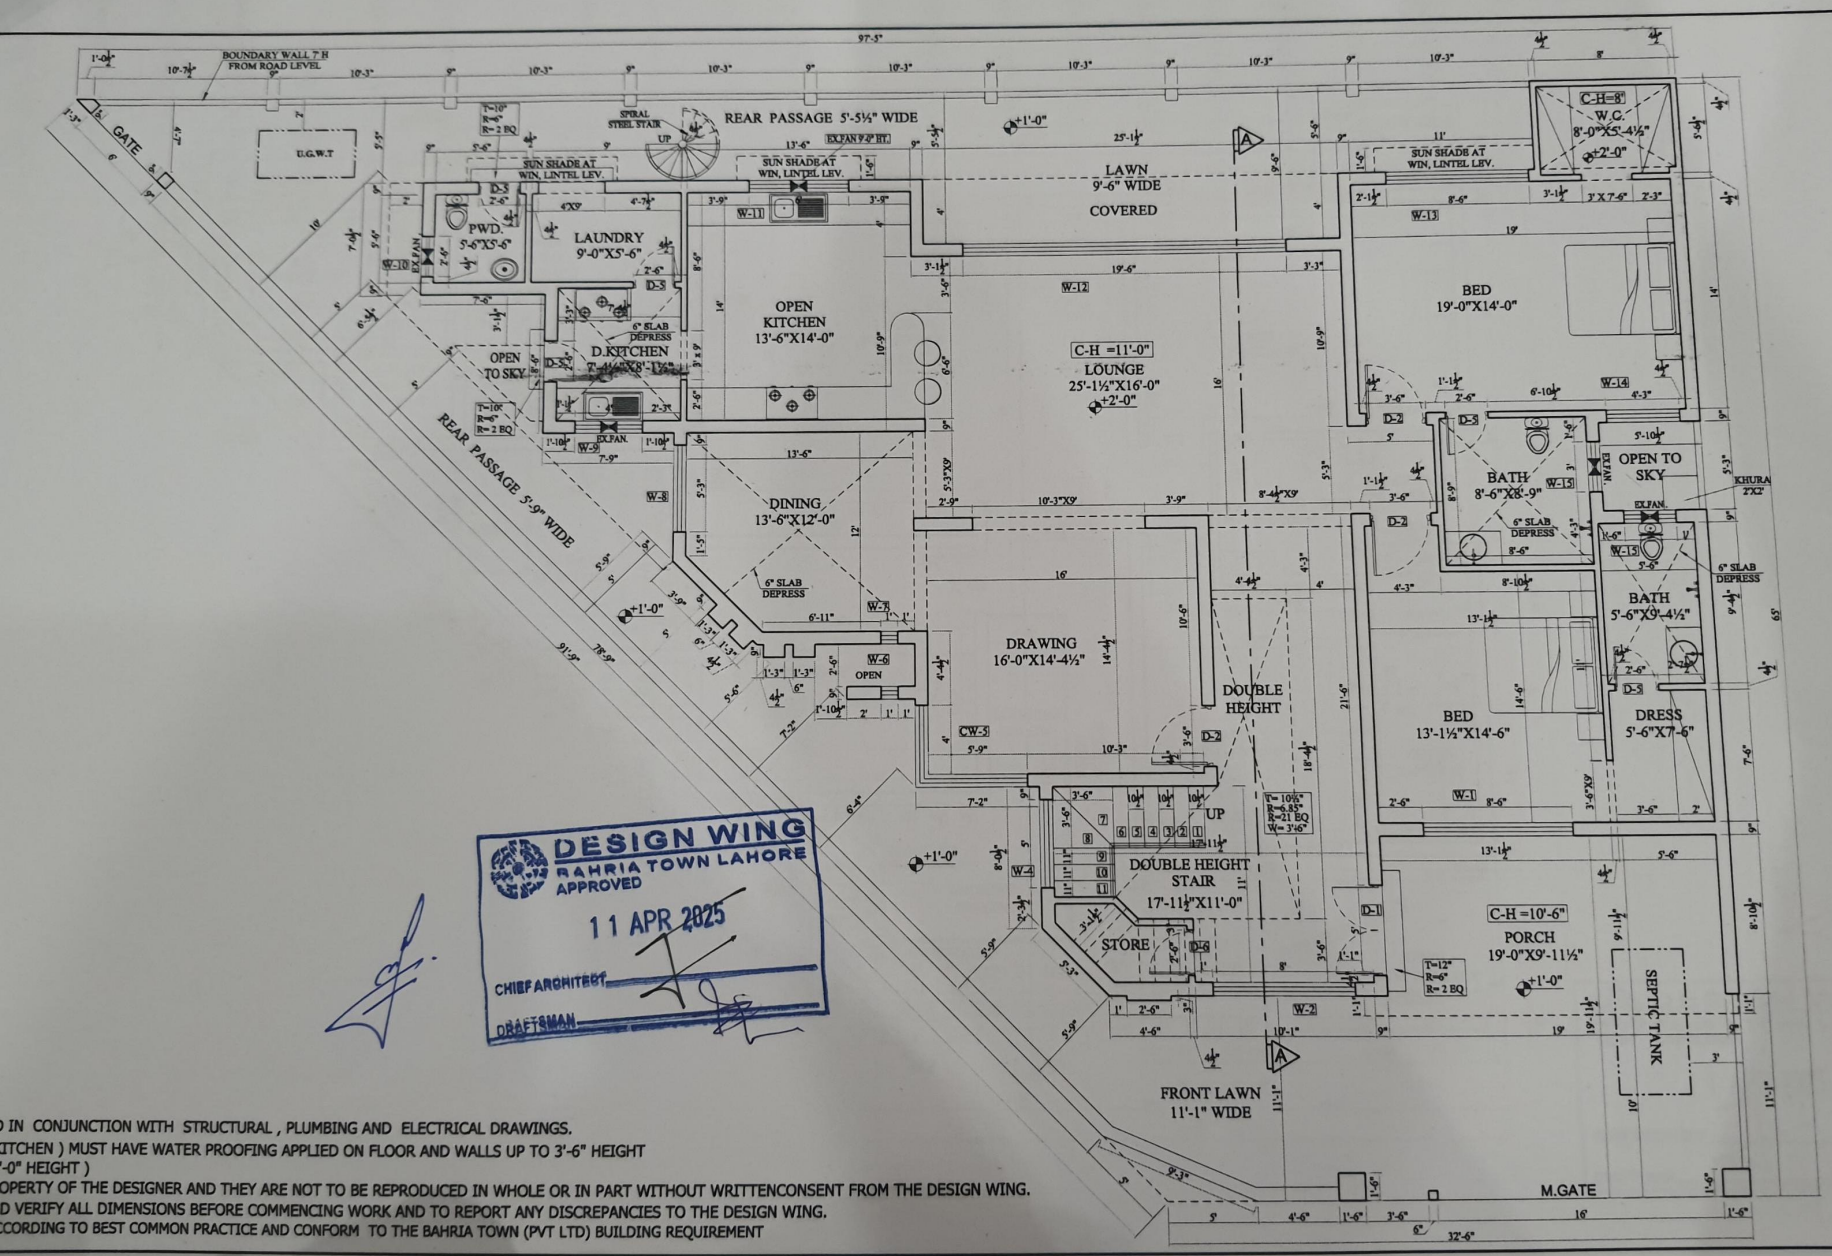

DESIGN WING
BAHRIA TOWN LAHORE
APPROVED
11 APR 2025
CHIEF ARCHITECT
DRAFTSMAN


D IN CONJUNCTION WITH STRUCTURAL , PLUMBING AND ELECTRICAL DRAWINGS.
ITCHEN) MUST HAVE WATER PROOFING APPLIED ON FLOOR AND WALLS UP TO 3'-6" HEIGHT
'-0" HEIGHT)
OPERTY OF THE DESIGNER AND THEY ARE NOT TO BE REPRODUCED IN WHOLE OR IN PART WITHOUT WRITTENCONSENT FROM THE DESIGN WING.
D VERIFY ALL DIMENSIONS BEFORE COMMENCING WORK AND TO REPORT ANY DISCREPANCIES TO THE DESIGN WING.
CCORDING TO BEST COMMON PRACTICE AND CONFORM TO THE BAHRIA TOWN (PVT LTD) BUILDING REQUIREMENT

LL DRAWINGS ARE THE PROPERTY OF THE DESIGNER AND THEY ARE NOT TO BE REPRODUCED IN WHOLE OR IN PART WITHOUT WRITTEN CONSENT FROM THE DESIGN WING (BAHRIA TOWN).

CLIENT

PROJECT
169 , G - 3 BLOCK PHASE - 4

DRAWN
ABDUL QAYUM

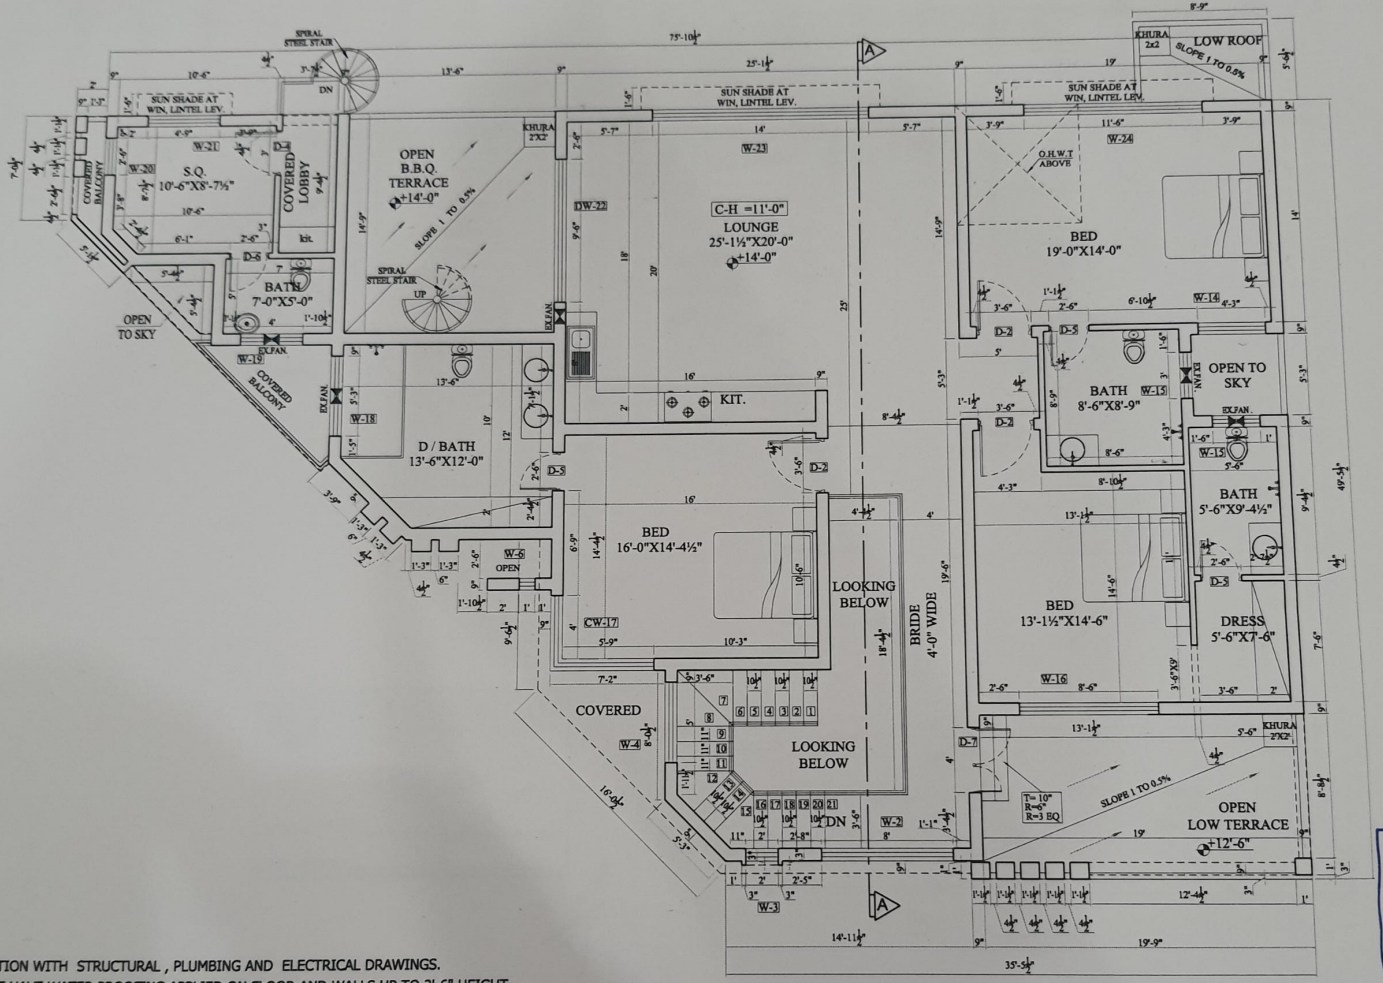

E :
LL DRAWINGS TO BE READ IN CONJUNCTION WITH STRUCTURAL , PLUMBING AND ELECTRICAL DRAWINGS.
LL WET AREAS (BATH & KITCHEN) MUST HAVE WATER PROOFING APPLIED ON FLOOR AND WALLS UP TO 3'-6" HEIGHT
R SHOWER AREA UP TO 7'-0" HEIGHT)
LL DRAWINGS ARE THE PROPERTY OF THE DESIGNER AND THEY ARE NOT TO BE REPRODUCED IN WHOLE OR IN PART WITHOUT WRITTENCONSENT FROM THE DESIGN WING.
ONTRACTOR TO CHECK AND VERIFY ALL DIMENSIONS BEFORE COMMENCING WORK AND TO REPORT ANY DISCREPANCIES TO THE DESIGN WING.
L CONSTRUCTION TO BE ACCORDING TO BEST COMMON PRACTICE AND CONFORM TO THE BAHRIA TOWN (PVT LTD) BUILDING REQUIREMENT

DESIGN WIN
BAHRIA TOWN LAHO
APPROVED
11 APR 2025
CHIEF ARCHITECT
DRAFTSMAN

ALL DRAWINGS ARE THE PROPERTY OF THE DESIGNER AND THEY ARE NOT TO BE REPRODUCED IN WHOLE OR IN PART WITHOUT WRITTEN CONSENT FROM THE DESIGN WING (BAHRIA TOWN).

CONTRACTOR TO CHECK AND VERIFY ALL DIMENSIONS BEFORE COMMENCING WORK AND TO REPORT ANY DISCREPANCIES TO THE DESIGN WING.

DO NOT SCALE DRAWINGS.

ALL CONSTRUCTION TO BE ACCORDING TO BEST COMMON PRACTICE AND CONFORM TO THE BAHRIA TOWN (PVT) BUILDING BY-LAWS.

No.	ISSUED	DATE
1.	ISSUED FOR CONSTRUCTION	----

CLIENT
--

PROJECT
169 , G - 3 BLOCK PHASE - 4
BAHRIA ORCHARD LAHORE

DRAWN
ABDUL QAYUM

DESIGN BY
DESIGN WING


SCALE
1/8"=1'-0"

ARCHITECT
IQRA

CONSULTANT ARCHITECT :
DESIGN WING
BAHRIA TOWN
LAHORE.
Tel.# (042) 35451371-9
Fax # (042) 35451392
bahria.designwing@hotmail.com

DRAWING
FIRST FLOOR WORKING PLAN
COVERED AREA = 2503 SFT

DWG. NO.

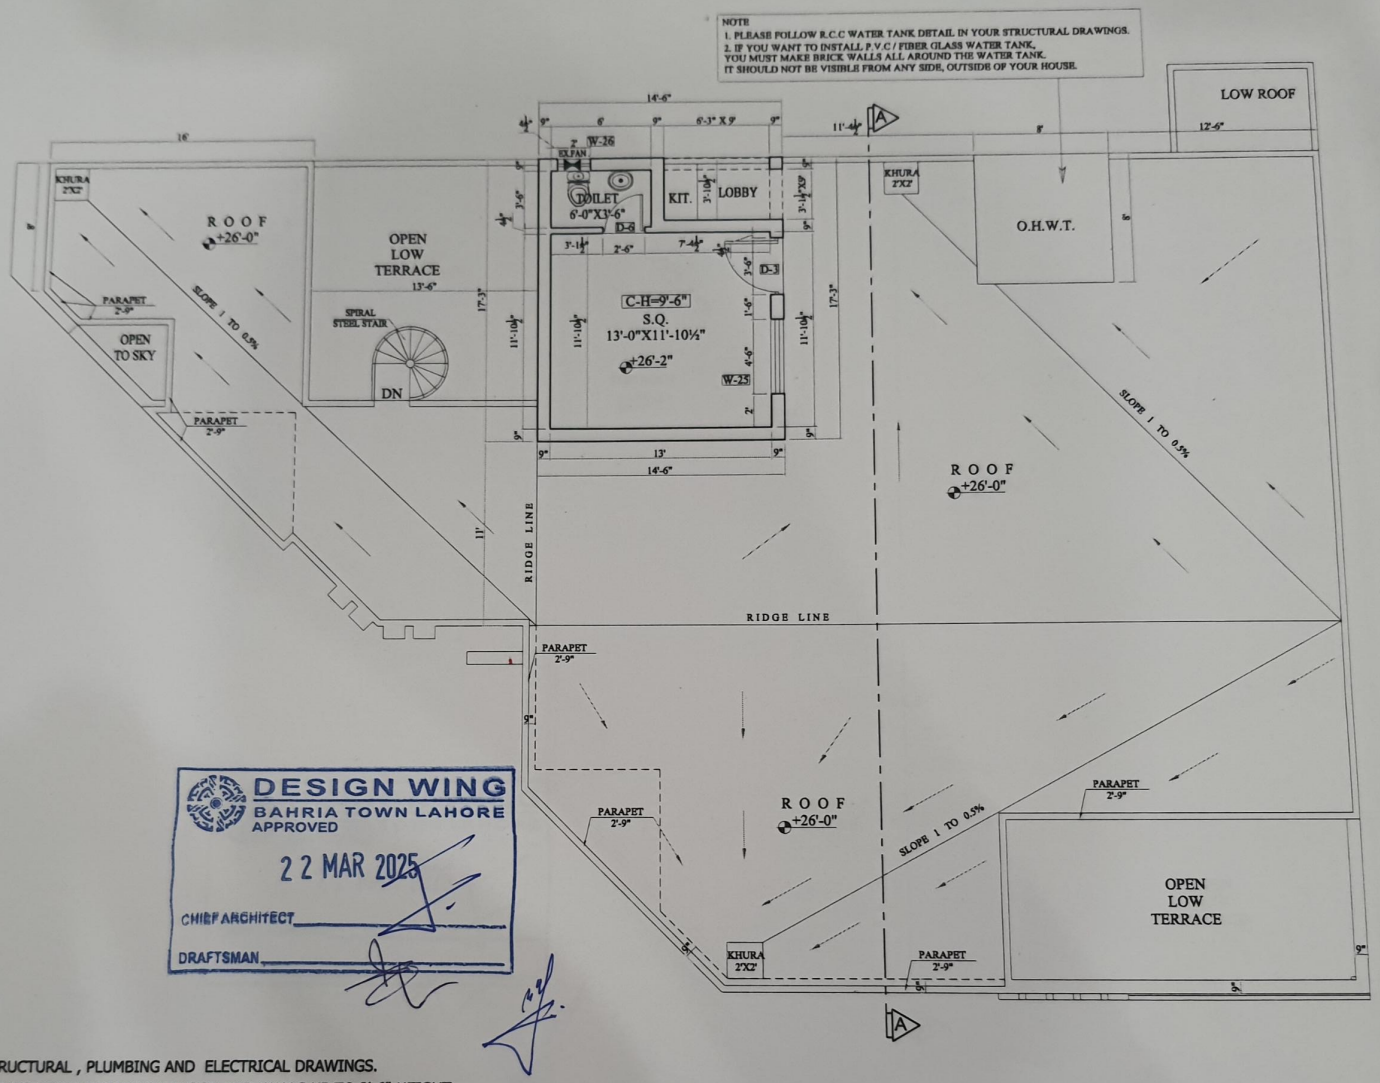

DESIGN WING
BAHRIA TOWN LAHORE
APPROVED
22 MAR 2025
CHIEF ARCHITECT
DRAFTSMAN

NGS TO BE READ IN CONJUNCTION WITH STRUCTURAL , PLUMBING AND ELECTRICAL DRAWINGS.
REAS (BATH & KITCHEN) MUST HAVE WATER PROOFING APPLIED ON FLOOR AND WALLS UP TO 3'-6" HEIGHT
R AREA UP TO 7'-0" HEIGHT)
NGS ARE THE PROPERTY OF THE DESIGNER AND THEY ARE NOT TO BE REPRODUCED IN WHOLE OR IN PART WITHOUT WRITTENCONSENT FROM THE DESIGN WING.
R TO CHECK AND VERIFY ALL DIMENSIONS BEFORE COMMENCING WORK AND TO REPORT ANY DISCREPANCIES TO THE DESIGN WING.
UCTION TO BE ACCORDING TO BEST COMMON PRACTICE AND CONFORM TO THE BAHRIA TOWN (PVT LTD) BUILDING REQUIREMENT

ALL DRAWINGS ARE THE PROPERTY OF THE DESIGNER AND THEY ARE NOT TO BE REPRODUCED IN WHOLE OR IN PART WITHOUT WRITTEN CONSENT FROM THE DESIGN WING (BAHRIA TOWN).

CONTRACTOR TO CHECK AND VERIFY ALL DIMENSIONS BEFORE COMMENCING WORK AND TO REPORT ANY DISCREPANCIES TO THE DESIGN WING.

DO NOT SCALE DRAWINGS.

ALL CONSTRUCTION TO BE ACCORDING TO BEST COMMON PRACTICE AND CONFORM TO THE BAHRIA TOWN (PVT) BUILDING BY-LAWS.

No.	ISSUED	DATE
1.	ISSUED FOR CONSTRUCTION	-----

CLIENT
--

CONSULTANT ARCHITECT :
DESIGN WING
BAHRIA TOWN
LAHORE.
Tel.# (042) 35451371-9
Fax # (042) 35451392
bahria.designwing@hotmail.com

PROJECT
169 , G - 3 BLOCK PHASE - 4
BAHRIA ORCHARD LAHORE

DRAWING
MUMTY FLOOR WORKING PLAN
COVERED AREA = 250 SFT

DRAWN
ABDUL QAYUM

DESIGN BY
DESIGN WING

SCALE
1/8"=1'-0"

ARCHITECT
IQRA