

REVISION DATE	20TH SEPTEMBER 2025
DATE	12TH SEPTEMBER 2025

STRUCTURE DESIGN
WORKING DRAWINGS

FOURTH FLOOR SLAB
(THIRD FLOOR ROOF)

PROJECT

ATA MEDICAL COMPLEX
FAISALABAD

CLIENT

MR. NAVEED HASSAN

CONSULTING ARCHITECT

PARVEZ IQBAL & ASSOCIATES


CONSULTING ARCHITECTS
ENGINEERS, PLANNERS
INTERIOR DESIGNERS

83 - A - 2, GULBERG III,
LAHORE - PAKISTAN

email : piaa@piaa.com.pk
TEL: +92 42 35758026-7
FAX: +92 42 35751838
www.piaa.com.pk

CONSULTING ENGINEER

NIAZI DESIGN SYSTEMS
CONSULTING ENGINEERS & ARCHITECTS
44B/III, GULBERG III, LAHORE.
PHONE: 5757078, 5758465

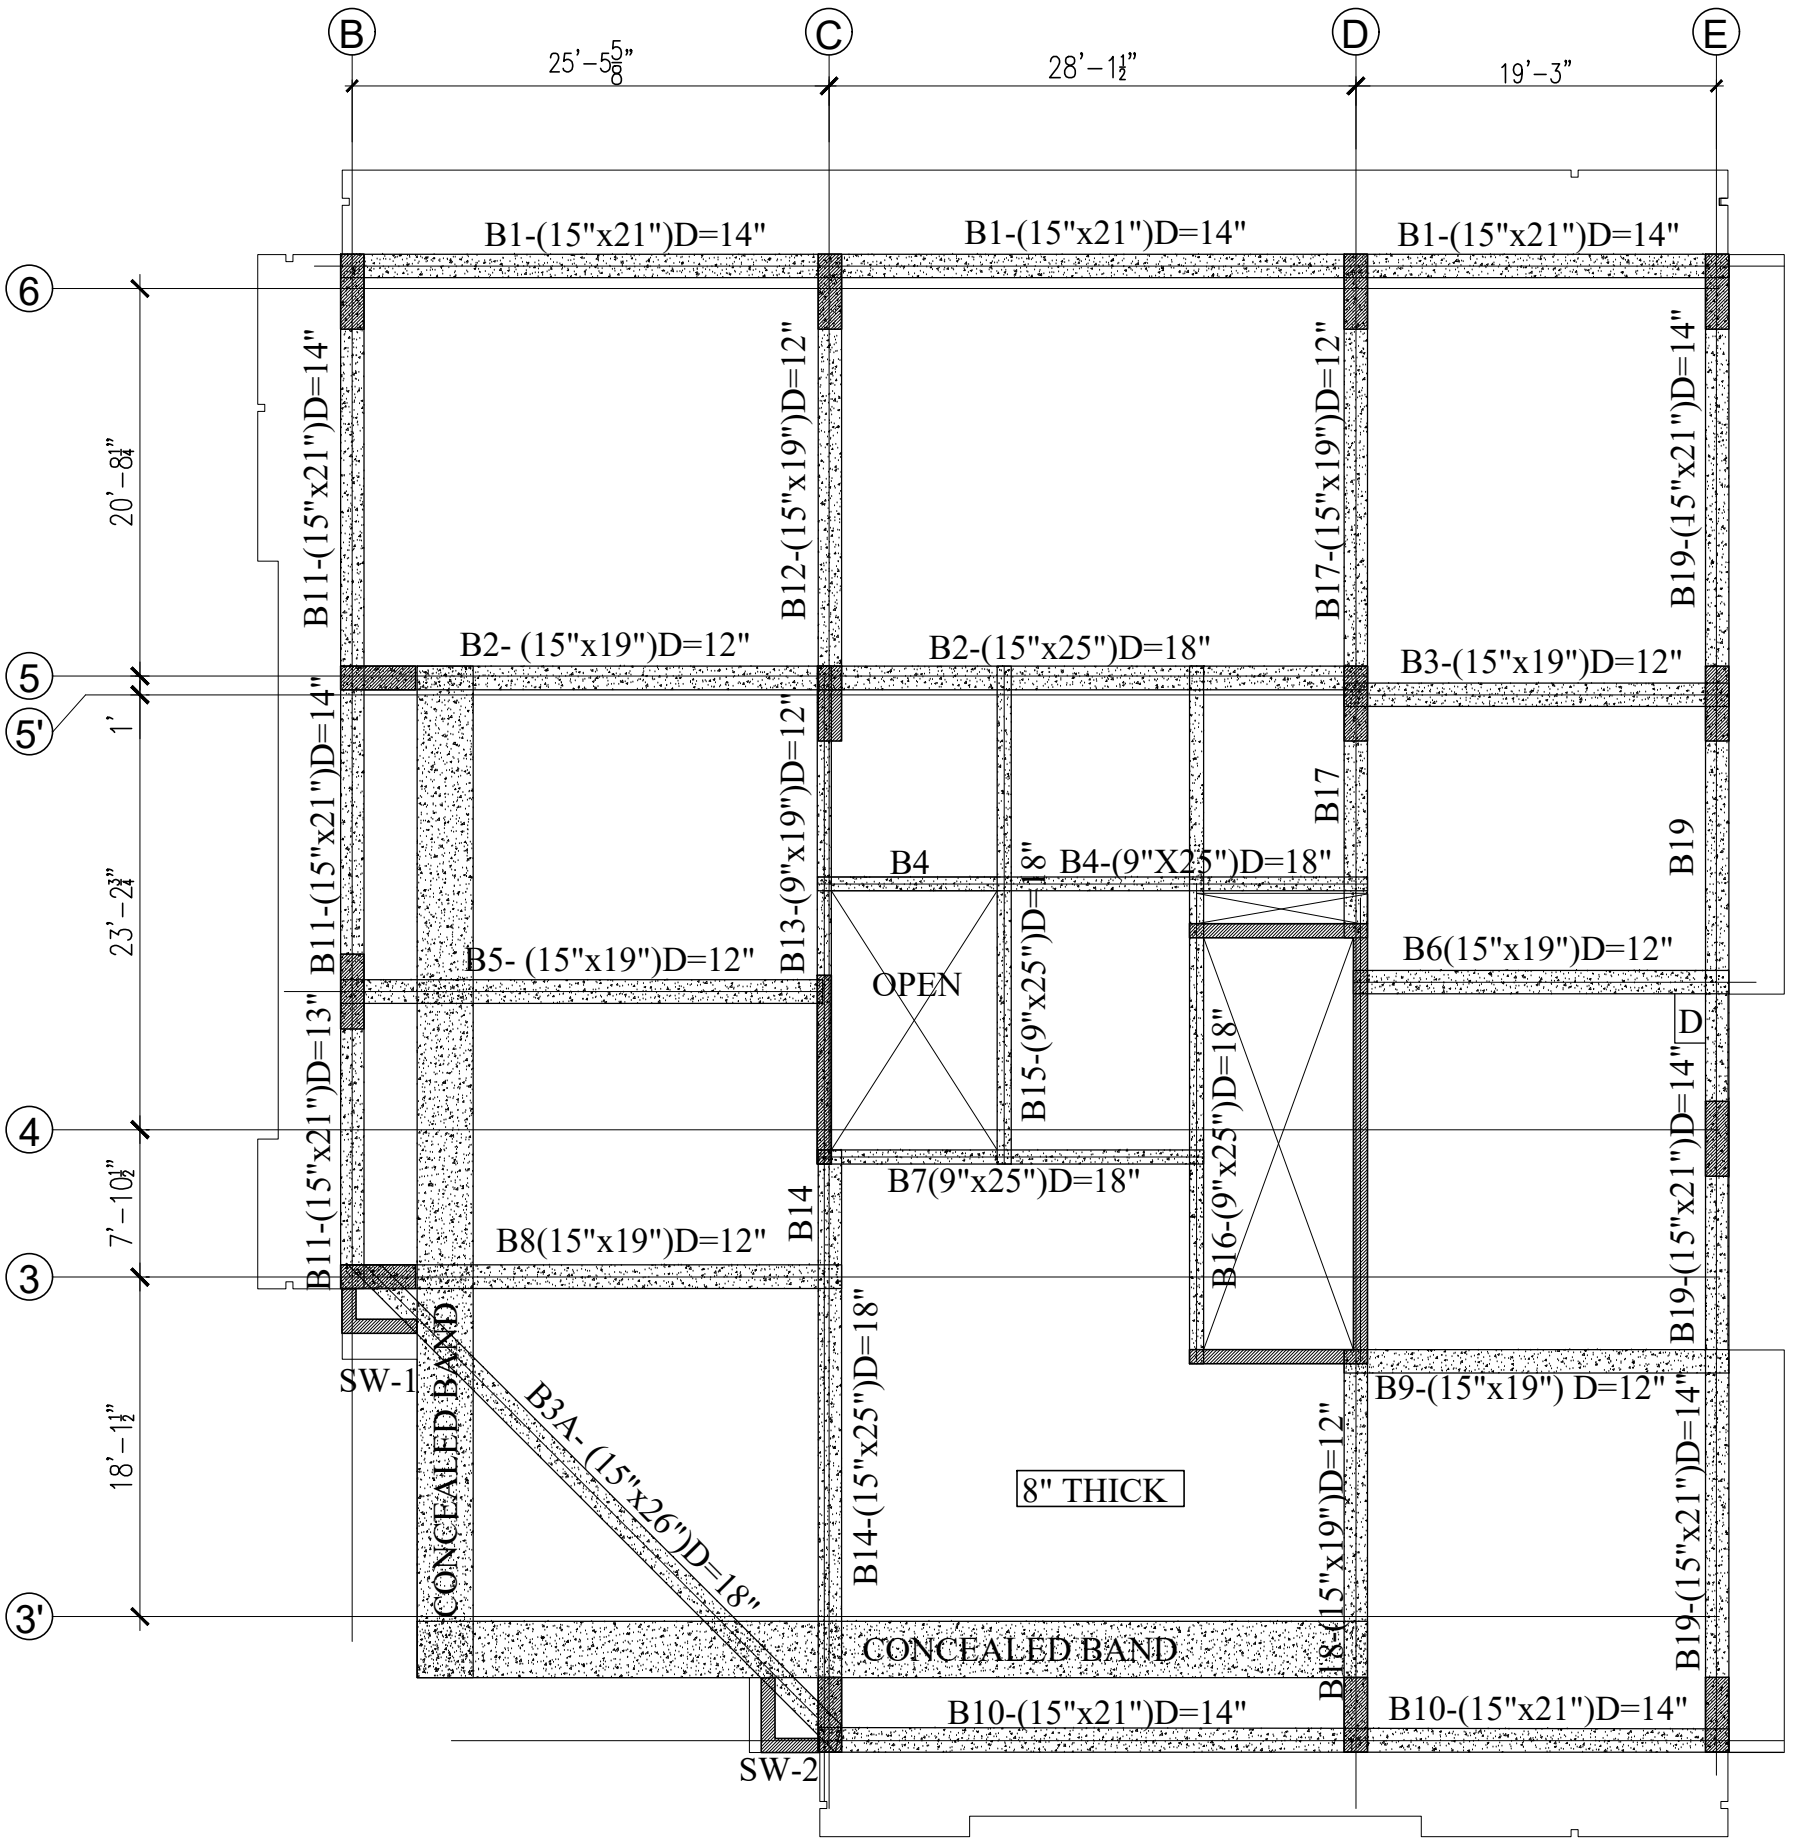


BEAM FRAMING PLAN OF 3rd.FLOOR ROOF SLAB (4th. FLOOR SLAB)(SLAB 7" Th. U.N.O & MESHING BAR #3@10"c/c

FOR CONSTRUCTION

PROJECT. ATA MEDICAL COMPLEX PLOT NO. 672/A PEOPLES COLONY, FAISALABAD	ARCHITECT. PARVEZ IQBAL & ASSOCIATES CONSULTING ARCHITECTS ENGINEERS INTERIOR DESIGNERS & PLANNERS 83-A2,GULBERG III, LAHORE - PAKISTAN TELEPHONE: +92-42 5758026-7 MOB: 0321 8868710	TITLE KEY PLAN OF BEAMS FOR ROOF SLAB OF 3rd.FLOOR (4th. FLOOR SLAB)	REV	DATE	DESCRIPTION	S.S INT.	SIGN	AMJAD INT.	SIGN	NDS INT.	SIGN	CONSULTING ENGINEERS NIAZI DESIGN SYSTEMS CONSULTING ENGINEERS & ARCHITECTS 44-B-III, GULBERG III, LAHORE. PHONE..5757078, 5758465.	DOCUMENT NUMBER ST/011
			1.	20-09-2025	SLAB EDGE REVISED		BY		CHK,D		APP,VD		
		ENGINEER'S SIGNATURE.	REVISION									AMJAD KHAN NIAZI	DRAWN AKHTAR HUSSAIN
		ARCHITECT'S SIGNATURE.	UNAUTHORIZED REPRODUCTION OF ANY KIND IS PROHIBITED, ALL RIGHTS ARE RESERVED BY NIAZI DESIGN SYSTEMS, LAHORE, PAKISTAN									CHECKED BY. AMJAD KHAN NIAZI	SCALE 3/32"=1'-0" DATE 12-09-2025

THIS DOCUMENT HAS BEEN MODIFIED MANUALLY YES NO

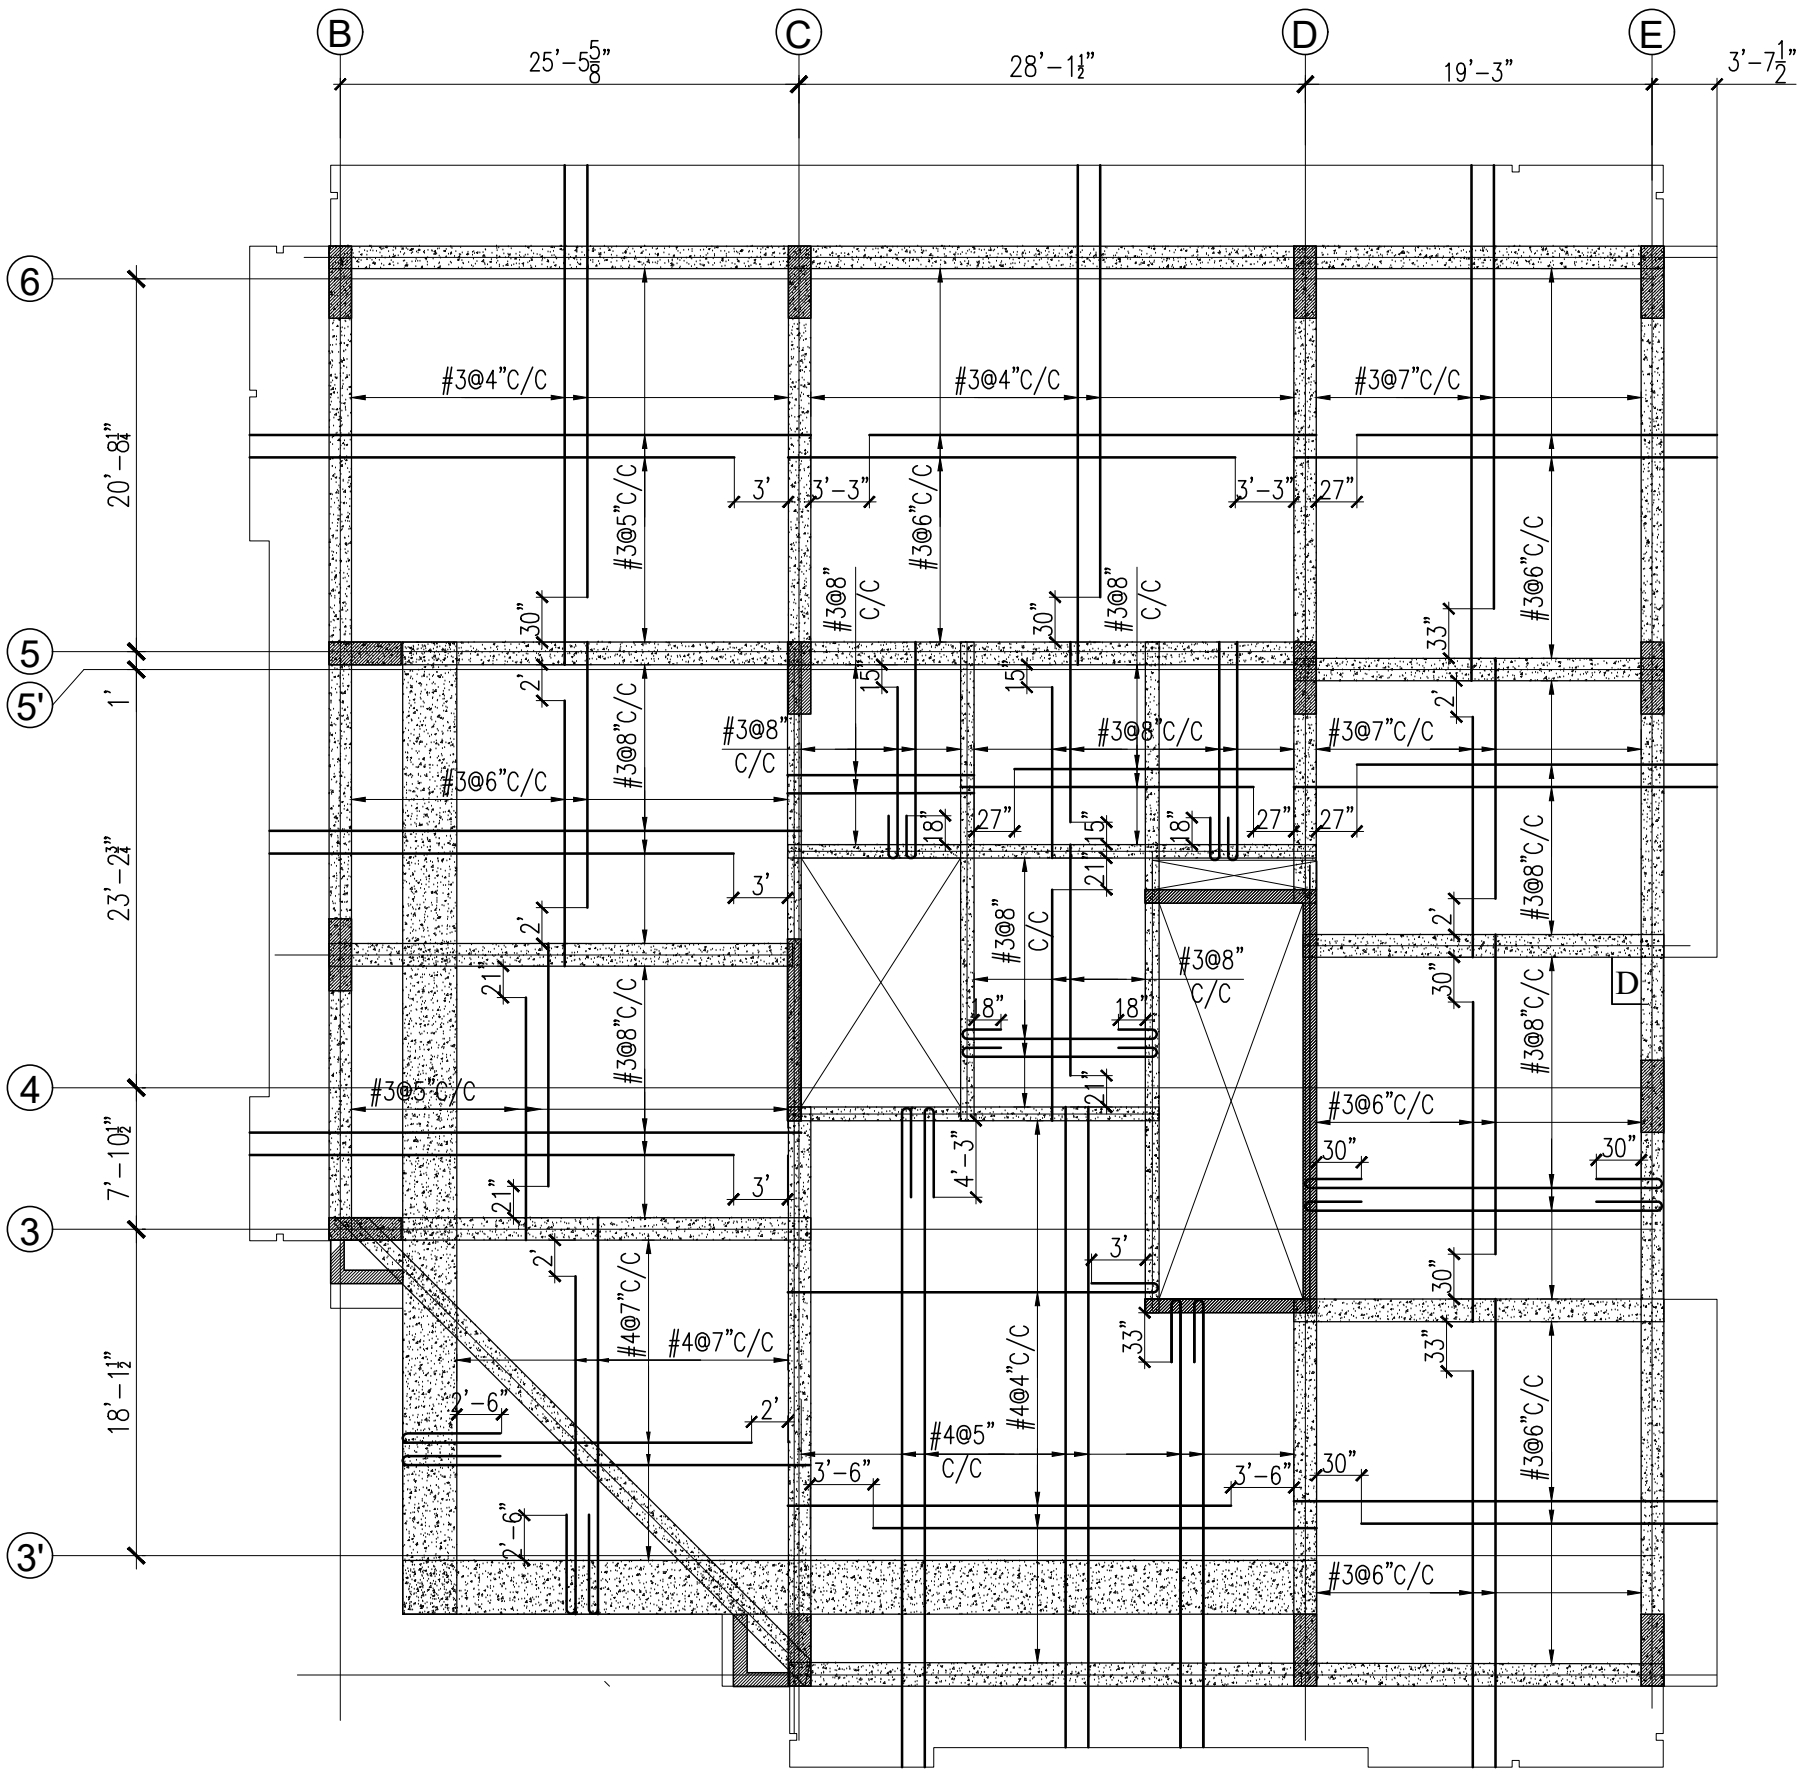

R.C.C ROOF SLAB OF 3rd.FLOOR
(4th. FLOOR SLAB)
BOTTOM STEEL (SLAB 7" Th. U.N.O & MESHING BAR #3@10"c/c

FOR CONSTRUCTION

PROJECT.

ATA MEDICAL COMPLEX
PLOT NO. 672/A PEOPLES COLONY,
FAISALABAD

ARCHITECT.

PARVEZ IQBAL & ASSOCIATES
CONSULTING ARCHITECTS ENGINEERS
INTERIOR DESIGNERS & PLANNERS
83-A2,GULBERG III, LAHORE - PAKISTAN
TELEPHONE: +92-42 5758026-7 MOB: 0321 8868710

TITLE
R.C.C ROOF SLAB OF 3rd.FLOOR
(4th. FLOOR SLAB) BOTTOM STEEL

REV	DATE	DESCRIPTION	S.S INT.	SIGN	AMJAD INT.	SIGN	NDS INT.	SIGN
1.	20-09-2025	SLAB EDGE REVISED						
			BY		CHK,D		APP,VD	

ENGINEER'S SIGNATURE.

ARCHITECT'S SIGNATURE.

REVISION

UNAUTHORIZED REPRODUCTION OF ANY KIND IS PROHIBITED, ALL RIGHTS ARE RESERVED BY NIAZI DESIGN SYSTEMS, LAHORE, PAKISTAN

CONSULTING ENGINEERS
NIAZI DESIGN SYSTEMS
CONSULTING ENGINEERS & ARCHITECTS
44-B-III, GULBERG III, LAHORE.
PHONE..5757078, 5758465.

AMJAD KHAN NIAZI

DRAWN AKHTAR HUSSAIN


CHECKED BY. AMJAD KHAN NIAZI

SCALE 3/32"=1'-0"

DATE 12-09-2025

DOCUMENT NUMBER
ST/012

THIS DOCUMENT HAS BEEN MODIFIED MANUALLY
YES NO

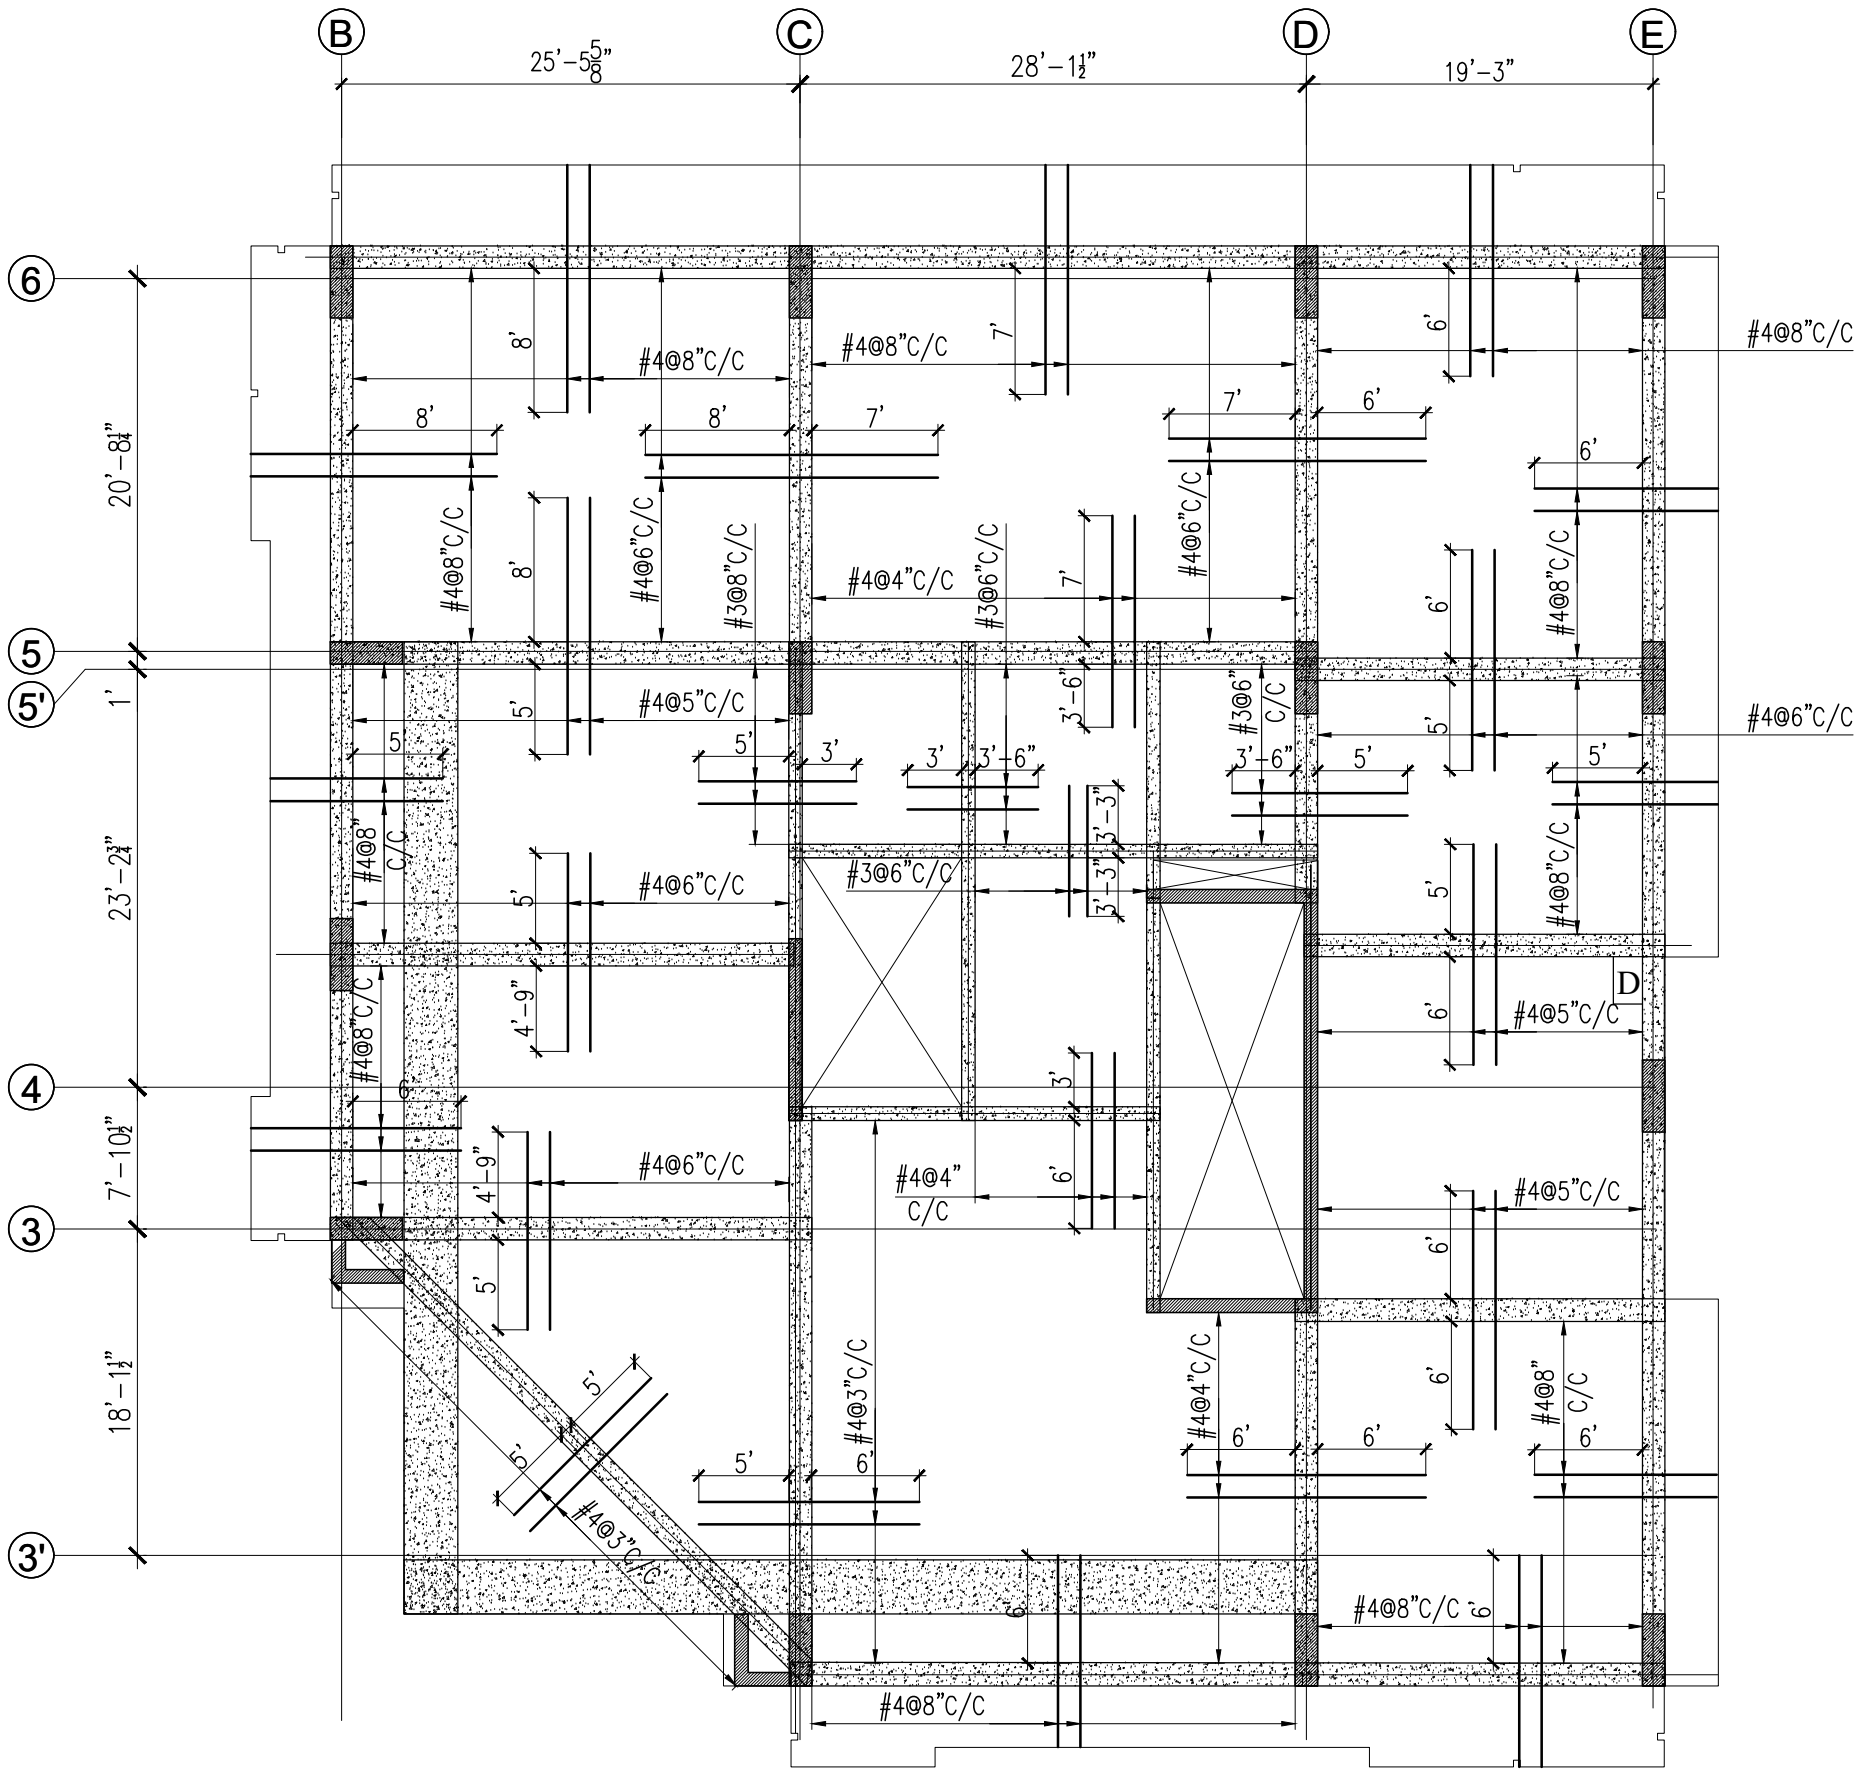


R.C.C ROOF SLAB OF 3rd.FLOOR
(4th. FLOOR SLAB)
TOP STEEL (SLAB 7" Th. U.N.O & MESHING BAR #3@10"c/c


FOR CONSTRUCTION

PROJECT. ATA MEDICAL COMPLEX PLOT NO. 672/A PEOPLES COLONY, FAISALABAD	ARCHITECT. PARVEZ IQBAL & ASSOCIATES CONSULTING ARCHITECTS ENGINEERS INTERIOR DESIGNERS & PLANNERS 83-A2,GULBERG III, LAHORE - PAKISTAN TELEPHONE: +92-42 5758026-7 MOB: 0321 8868710	TITLE R.C.C ROOF SLAB OF 3rd.FLOOR (4th. FLOOR SLAB) TOP STEEL	REV	DATE	DESCRIPTION	S.S INT.	SIGN	AMJAD INT.	SIGN	NDS INT.	SIGN	CONSULTING ENGINEERS NIAZI DESIGN SYSTEMS CONSULTING ENGINEERS & ARCHITECTS 44-B-III, GULBERG III, LAHORE. PHONE..5757078, 5758465.	DOCUMENT NUMBER ST/013
			1.	20-09-2025	SLAB EDGE REVISED		BY		CHK,D		APP,VD		
		ENGINEER'S SIGNATURE.	REVISION									AMJAD KHAN NIAZI	DRAWN AKHTAR HUSSAIN
		ARCHITECT'S SIGNATURE.	UNAUTHORIZED REPRODUCTION OF ANY KIND IS PROHIBITED, ALL RIGHTS ARE RESERVED BY NIAZI DESIGN SYSTEMS, LAHORE, PAKISTAN									CHECKED BY. AMJAD KHAN NIAZI	SCALE 3/32"=1'-0" DATE 12-09-2025


THIS DOCUMENT HAS BEEN MODIFIED MANUALLY YES NO

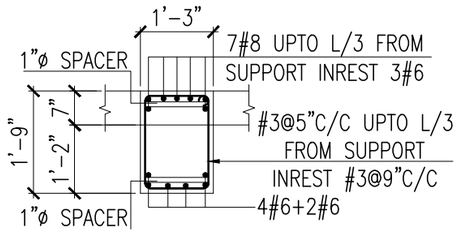


X-SECTION OF BEAM B1

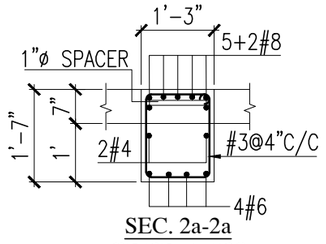


SEC. 2a-2a OF BEAM B2

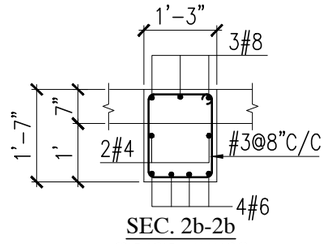


SEC. 2b-2b OF BEAM B2

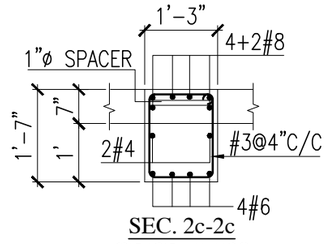


SEC. 2c-2c OF BEAM B2

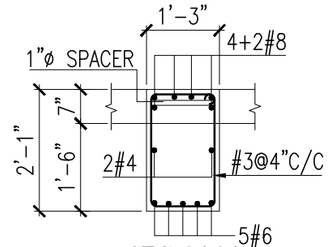


SEC. 2d-2d OF BEAM B2

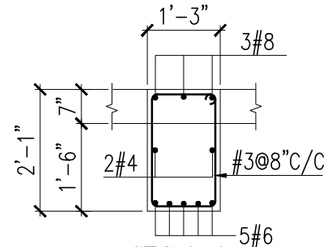


SEC. 2e-2e OF BEAM B2

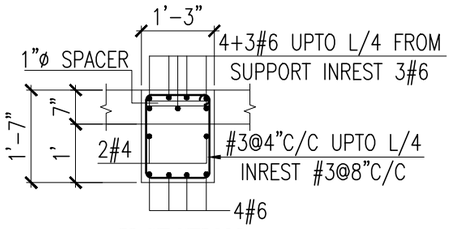


X-SECTION OF BEAM B3

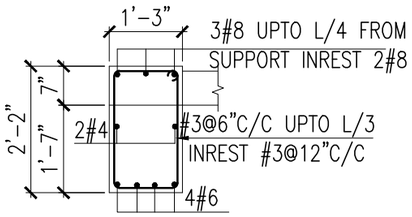


X-SECTION OF BEAM B3A

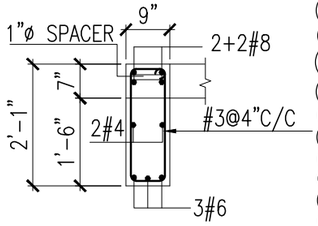


X-SECTION OF BEAM B4

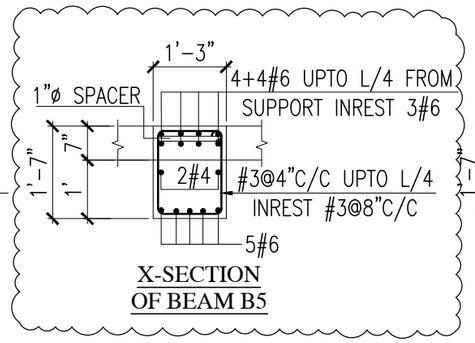


X-SECTION OF BEAM B5

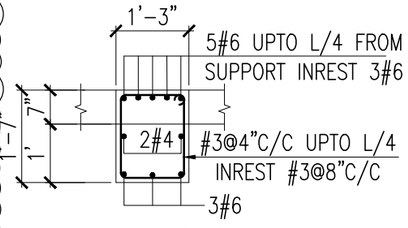


X-SECTION OF BEAM B6

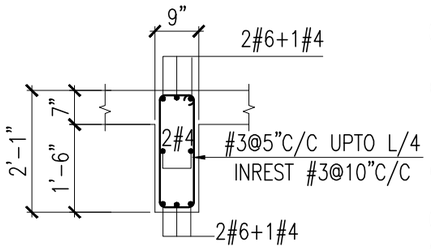


X-SECTION OF BEAM B7

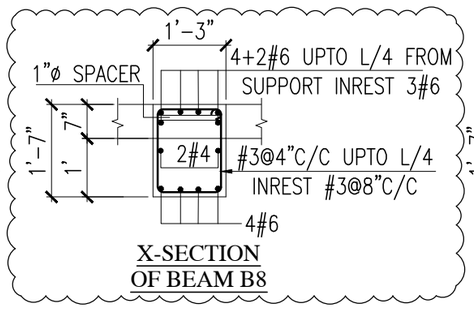


X-SECTION OF BEAM B8

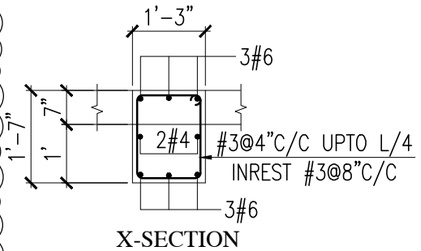


X-SECTION OF BEAM B9

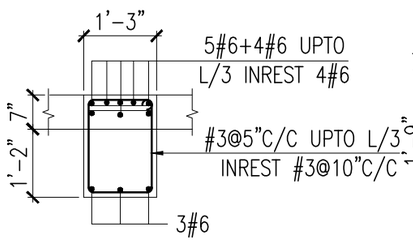


X-SECTION OF BEAM B10

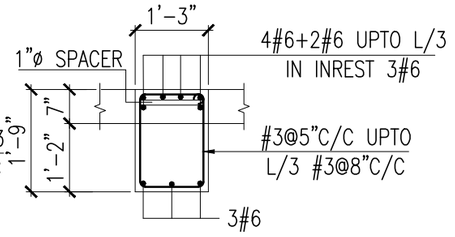


X-SECTION OF BEAM B11

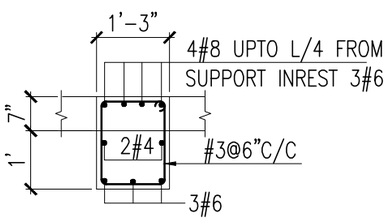


X-SECTION OF BEAM B12

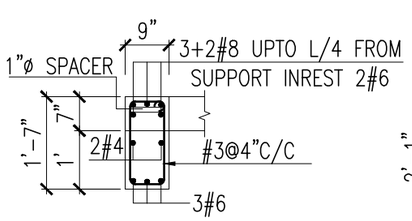


X-SECTION OF BEAM B13

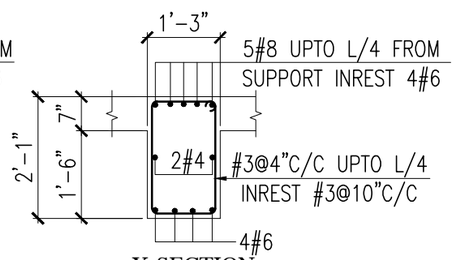

X-SECTION OF BEAM B14

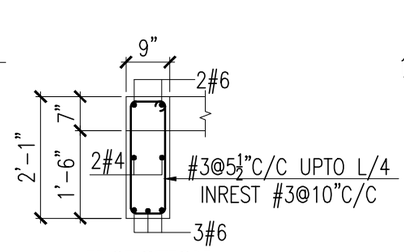

X-SECTION OF BEAM B15

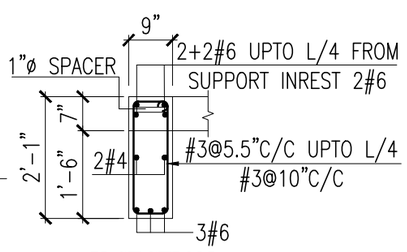

X-SECTION OF BEAM B16

FOR CONSTRUCTION

PROJECT.

ATA MEDICAL COMPLEX
PLOT NO. 672/A PEOPLES COLONY,
FAISALABAD

ARCHITECT.

PARVEZ IQBAL & ASSOCIATES
CONSULTING ARCHITECTS ENGINEERS
INTERIOR DESIGNERS & PLANNERS
83-A2,GULBERG III, LAHORE - PAKISTAN
TELEPHONE: +92-42 5758026-7 MOB: 0321 8868710

TITLE

X-SECTION OF
4th. FLOOR SLAB BEAMS

ENGINEER'S SIGNATURE.

ARCHITECT'S SIGNATURE.

REV	DATE	DESCRIPTION	S.S INT.	SIGN	AMJAD INT.	SIGN	NDS INT.	SIGN
			BY		CHK,D		APP,VD	

REVISION

UNAUTHORIZED REPRODUCTION OF ANY KIND IS PROHIBITED, ALL RIGHTS ARE RESERVED BY NIAZI DESIGN SYSTEMS, LAHORE, PAKISTAN

CONSULTING ENGINEERS

NIAZI DESIGN SYSTEMS
CONSULTING ENGINEERS & ARCHITECTS
44-B-III, GULBERG III, LAHORE.
PHONE..5757078, 5758465.

AMJAD KHAN NIAZI

DRAWN: AKHTAR HUSSAIN

CHECKED BY. AMJAD KHAN NIAZI

SCALE 3/32"=1'-0"


DATE 12-09-2025

DOCUMENT NUMBER


ST/014

THIS DOCUMENT HAS BEEN MODIFIED MANUALLY


YES NO

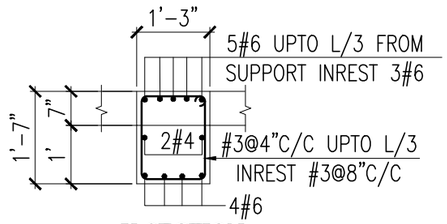


X-SECTION OF BEAM B17

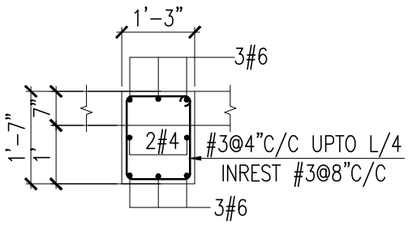


X-SECTION OF BEAM B18

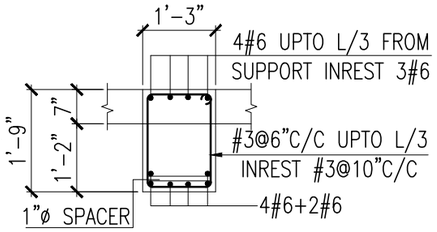


X-SECTION OF BEAM B19

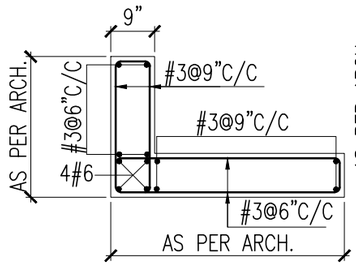

SHEAR WALL-1

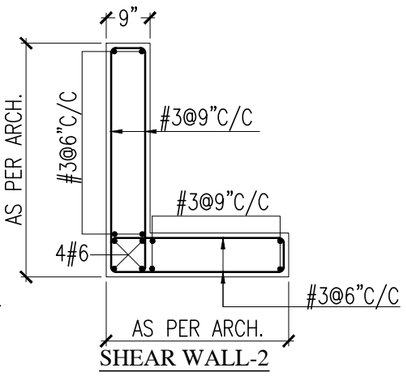


SHEAR WALL-2

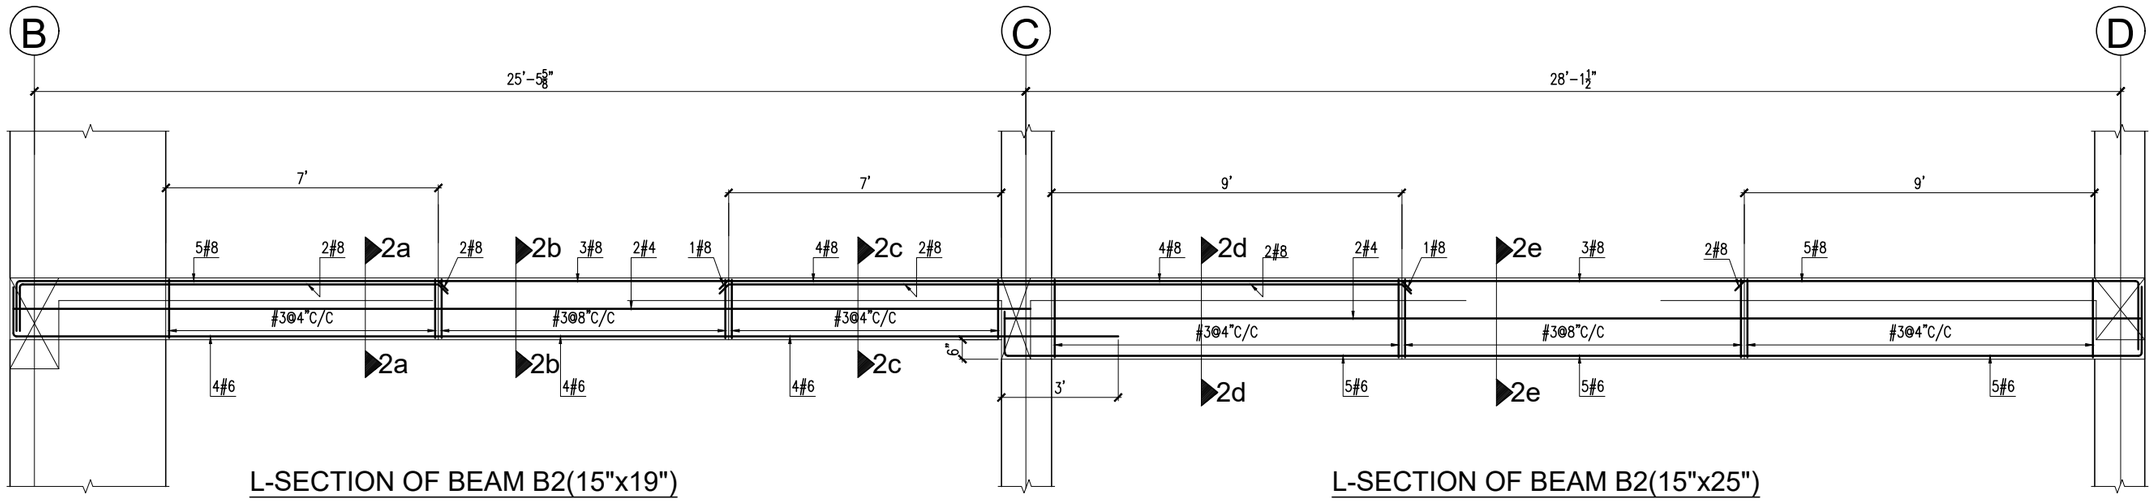


L-SECTION OF BEAM B2(15"x19")


L-SECTION OF BEAM B2(15"x25")

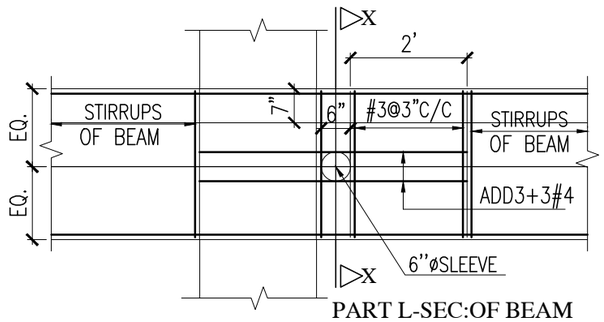


PART L-SEC:OF BEAM SHOWING 6"Ø SLEEVE AT AROUN THE COLUMN

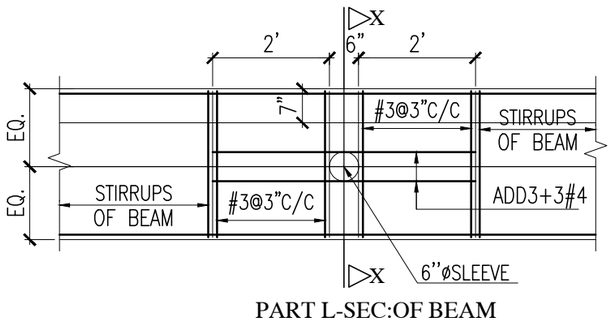


PART L-SEC:OF BEAM SHOWING 6"Ø SLEEVE AT MIDD. OF THE BEAM

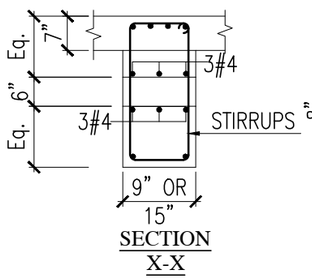

SECTION X-X

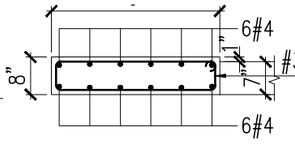

X-SECTION OF CONCEALED BAND

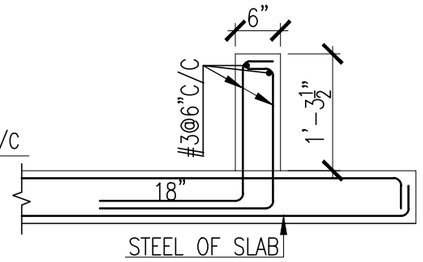

DETAIL OF R.C.C PARAPET

FOR CONSTRUCTION

PROJECT.

ATA MEDICAL COMPLEX
PLOT NO. 672/A PEOPLES COLONY,
FAISALABAD

ARCHITECT.

PARVEZ IQBAL & ASSOCIATES
CONSULTING ARCHITECTS ENGINEERS
INTERIOR DESIGNERS & PLANNERS
83-A2,GULBERG III, LAHORE - PAKISTAN
TELEPHONE: +92-42 5758026-7 MOB: 0321 8868710

TITLE

L & X-SECTION OF
4th. FLOOR SLAB BEAMS

REV	DATE	DESCRIPTION	S.S INT.	SIGN	AMJAD INT.	SIGN	NDS INT.	SIGN
			BY		CHK,D		APP,VD	

ENGINEER'S SIGNATURE.

ARCHITECT'S SIGNATURE.

REVISION

UNAUTHORIZED REPRODUCTION OF ANY KIND IS PROHIBITED, ALL RIGHTS ARE RESERVED BY NIAZI DESIGN SYSTEMS, LAHORE, PAKISTAN

CONSULTING ENGINEERS

NIAZI DESIGN SYSTEMS
CONSULTING ENGINEERS & ARCHITECTS
44-B-III, GULBERG III, LAHORE.
PHONE..5757078, 5758465.

DOCUMENT NUMBER

ST/015

AMJAD KHAN NIAZI

DRAWN AKHTAR HUSSAIN

CHECKED BY. AMJAD KHAN NIAZI

SCALE 3/32"=1'-0"

DATE 12-09-2025

THIS DOCUMENT HAS BEEN MODIFIED MANUALLY

YES NO