


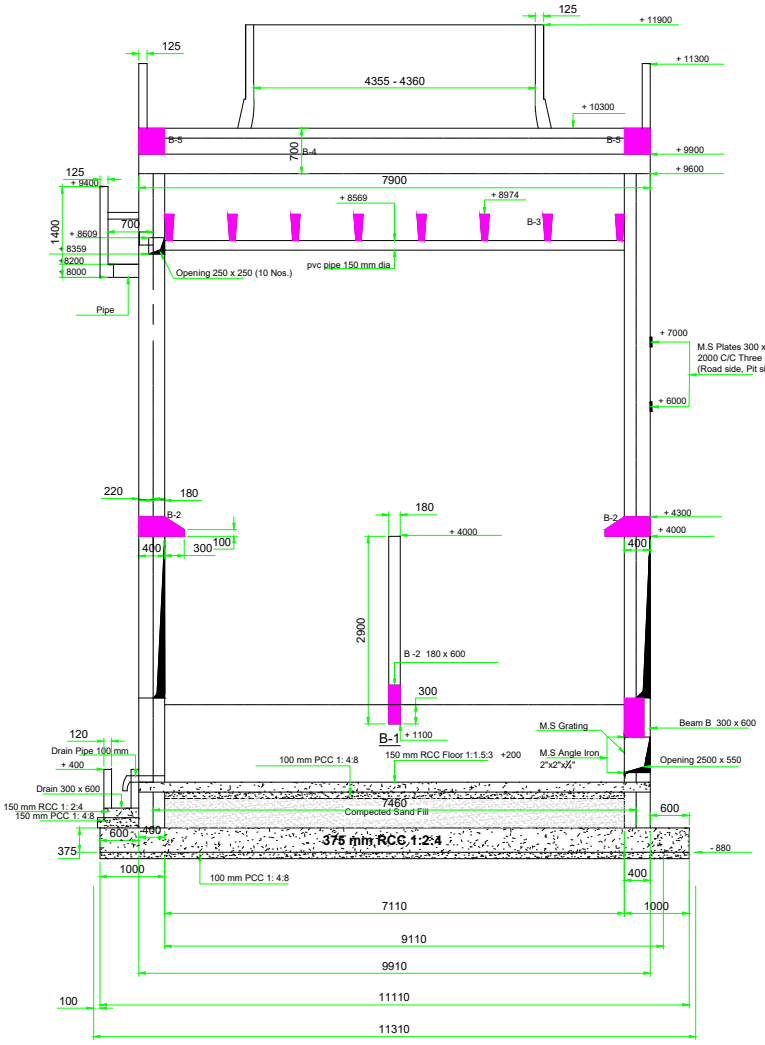


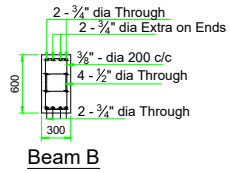


Beam B

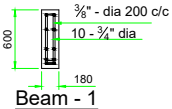


Beam - 1

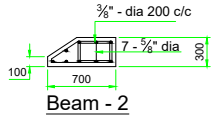


Beam - 2

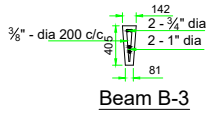

Beam B-3

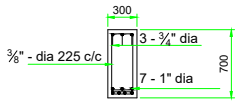


Beam - 4

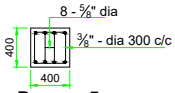

Beam - 5

X - SEC. COOLING TOWER 2 CELL BMR M - II PROJECT

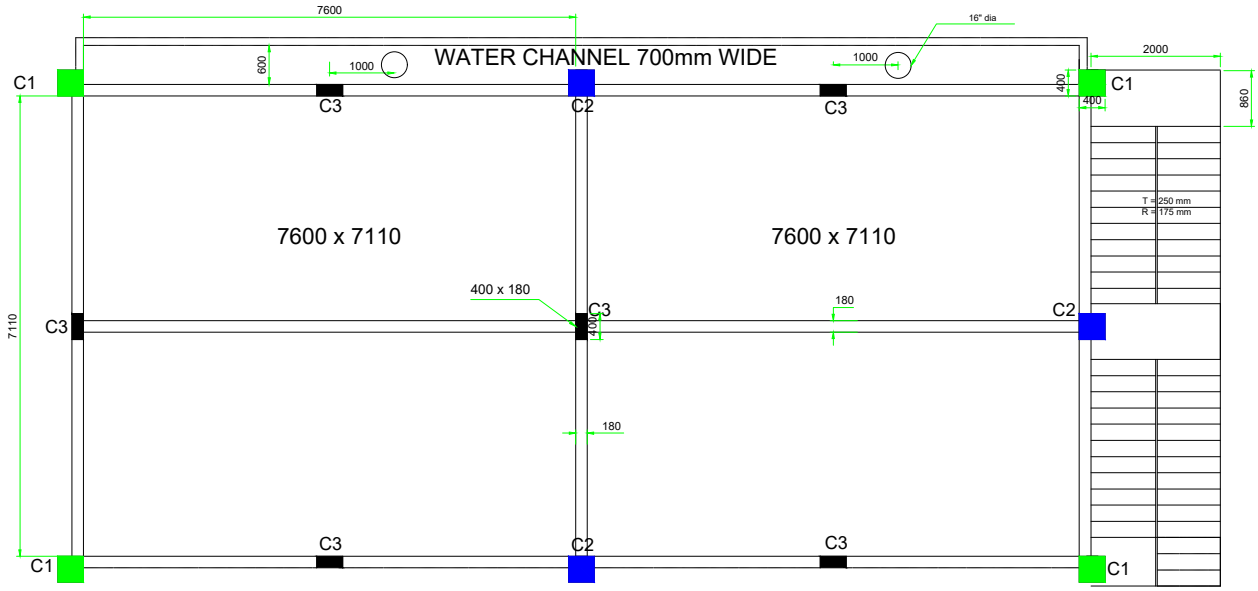


PLAN COOLING TOWER 2 CELL BMR M - II PROJECT

SITARA CHEMICAL INDUSTRIES FAISALABAD

SITARA CHEMICAL INDUSTRIES LTD, FAISALABAD, PAKISTAN

DEPARTMENT	Civil	Sign	DATE:	PROJECT: COOLING TOWER (AREA-1)
DRAWN BY.	Umer Tariq		15-08-2025	TITLE: Proposed Cooling Tower # 2 (1600m3 per hour)
REVIEW BY.			REV. 00	
CHECKED BY.				
VERIFIED BY.			SCALE	DRAWING NO.
APPROVED			N.T.S	SCIL- 00000000

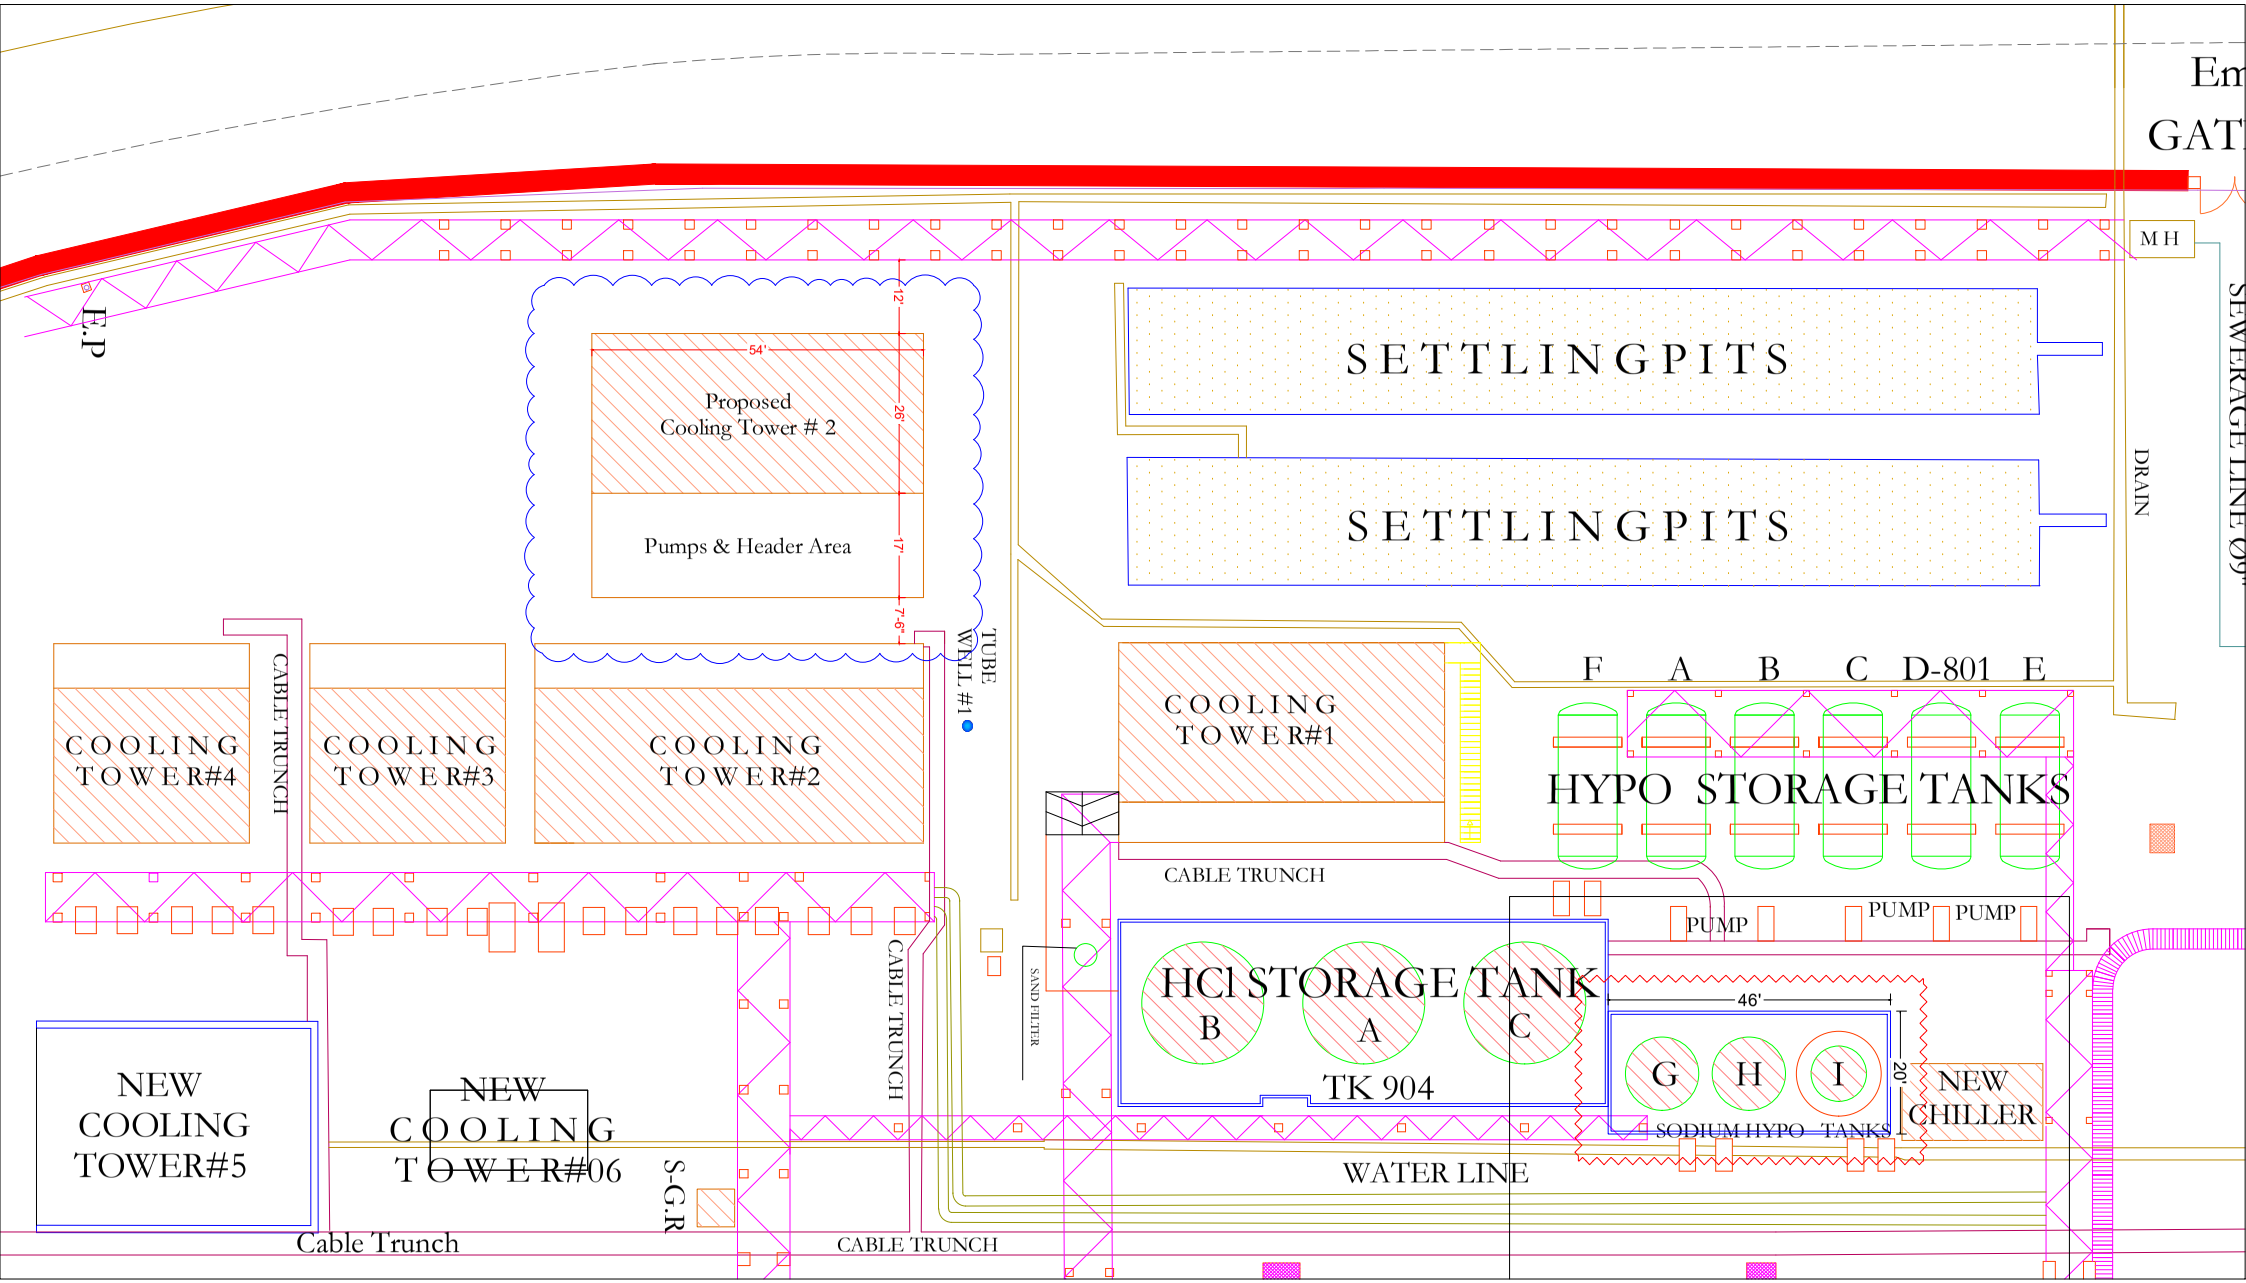
Em
GAT
M H
SEWERAGE LINE Ø9"
DRAIN
E.P
SETTLINGPITS
SETTLINGPITS
54'
12'
26'
17'
7'-6"
Proposed
Cooling Tower # 2
Pumps & Header Area
TUBE
WELL #1
COOLING
TOWER#4
CABLE TRUNCH
COOLING
TOWER#3
COOLING
TOWER#2
COOLING
TOWER#1
F
A
B
C
D-801
E
HYPO STORAGE TANKS
CABLE TRUNCH
PUMP
PUMP
PUMP
HCl STORAGE TANK
B
A
C
TK 904
SAND FILTER
CABLE TRUNCH
46'
20'
G
H
I
SODIUM HYPO TANKS
NEW
CHILLER
NEW
COOLING
TOWER#5
NEW
COOLING
TOWER#06
S-G.R
WATER LINE
Cable Trunch
CABLE TRUNCH