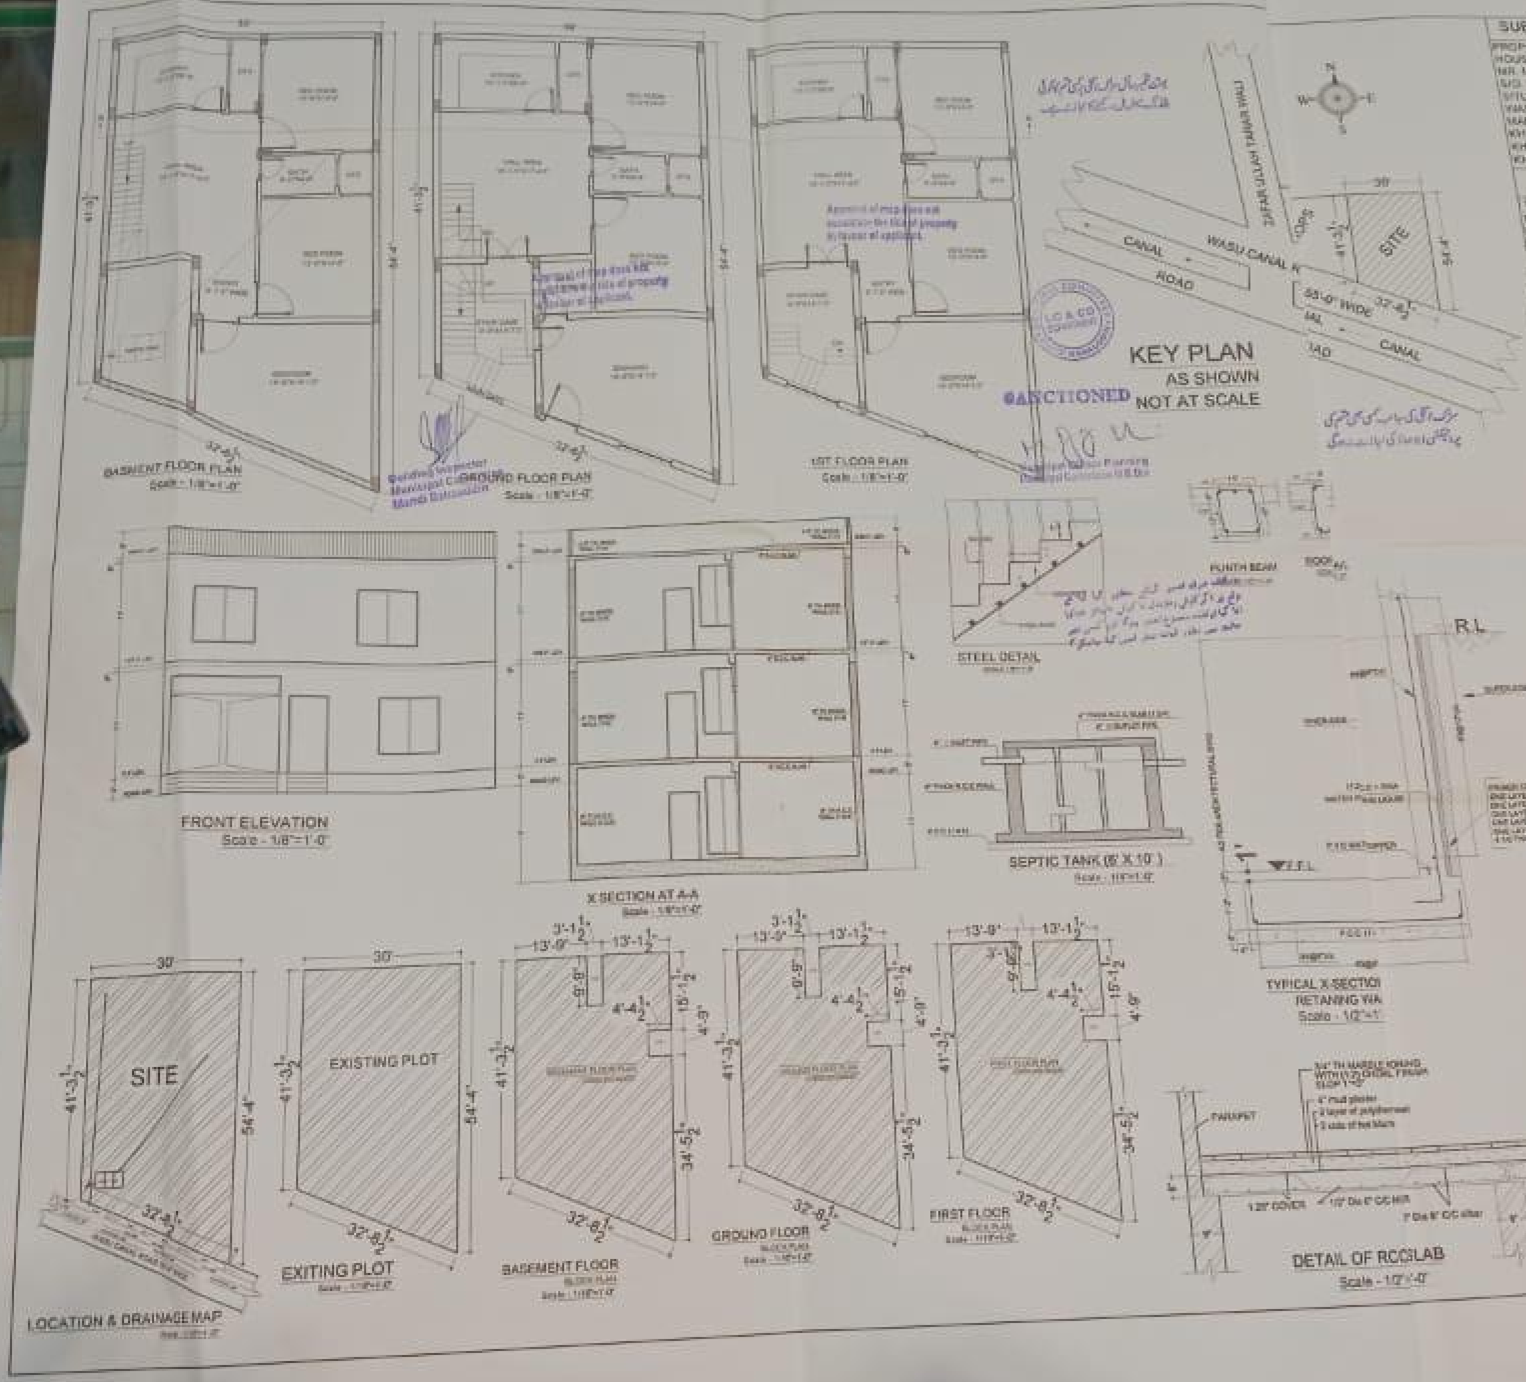

SUBMISSION DRAWING

PROPOSED DESIGN OF
HOUSE FOR
MR. MAZHAR IQBAL NASIR
S/O. SAEE MUHAMMAD
SITUATED AT: MUNSHI MOHALLAH
WASU CANAL ROAD
MANDI BAHAUDDIN
KHEWAT NO. 1556
KHETONI NO. 3423 TO 3429
KHASARA NO. 450/10/5/6

SCHEDULE OF AREA

TOTAL AREA OF PLOT	1634.00 SFT
BASEMENT COVERED AREA	1363.00 SFT
GROUND FLOOR COVERED AREA	1383.00 SFT
FIRST FLOOR COVERED AREA	1383.00 SFT
TOTAL COVERED AREA	4148.00 SFT
OPEN AREA	53.0000 SFT

SCHEDULE OF OPENINGS

D-1	3'-0" x 7'-0"	W-1	6'-0" x 5'-0"
D-2	2'-6" x 7'-0"	W-1	3'-0" x 5'-0"
MD	6'-0" x 5'-0"	DV	2'-0" x 2'-0"

SCHEDULE OF REINFORCEMENT

type	main bars	dist bars
porch	Ø1/2" @6" c/c	Ø1/2" @7" c/c
drawing	Ø1/2" @6" c/c	Ø1/2" @7" c/c
dinning	Ø1/2" @6" c/c	Ø1/2" @7" c/c
lounge	Ø1/2" @6" c/c	Ø1/2" @6" c/c
bed room	Ø1/2" @6" c/c	Ø1/2" @6" c/c
kitchen	Ø1/2" @6" c/c	Ø1/2" @6" c/c
bath	Ø1/2" @6" c/c	Ø1/2" @6" c/c
verandah	Ø1/2" @6" c/c	Ø1/2" @6" c/c

OWNER'S SIGN

DRAWN BY

STAMP & ARCHITECT'S SIGNATURE

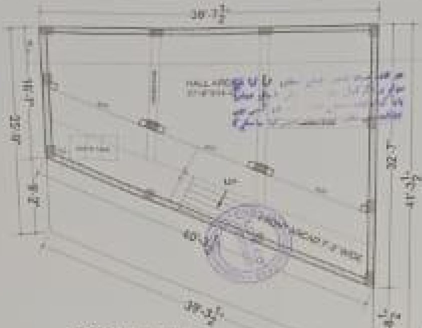

BASMENT FLOOR PLAN
Scale - 1/8"=1'-0"

Building Inspector
Municipal Committee

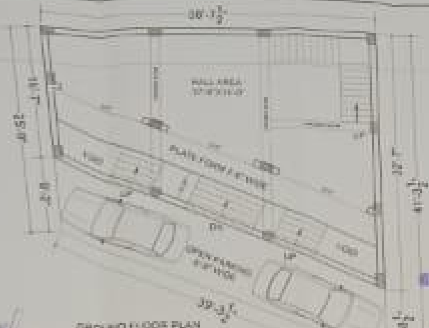

GROUND FLOOR PLAN
Scale - 1/8"=1'-0"

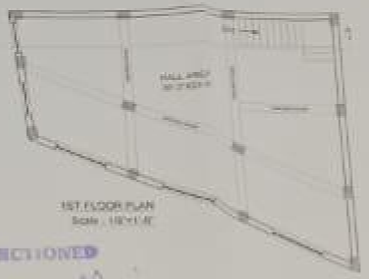

1ST FLOOR PLAN
Scale - 1/8"=1'-0"

SANCTIONED

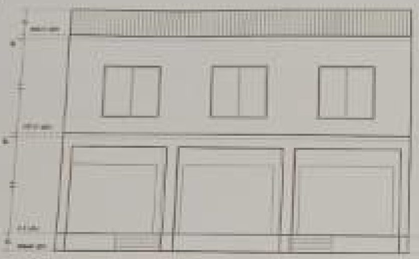

FRONT ELEVATION
Scale - 1/8"=1'-0"

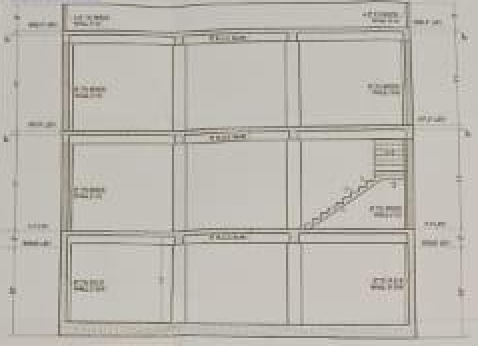

X SECTION AT A-A
Scale - 1/8"=1'-0"

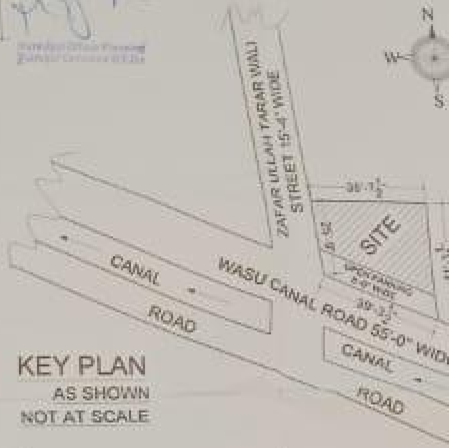
N
W
S
ZAFAR ULLAH TARAR WALI STREET 15'-4" WIDE
38'-7½"
SITE
OPEN PARKING 6'-8" WIDE
39'-3½"
CANAL
ROAD
WASU CANAL ROAD 55'-0" WID
CANAL
ROAD

KEY PLAN
AS SHOWN
NOT AT SCALE

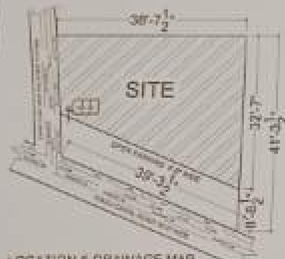

LOCATION & DRAINAGE MAP

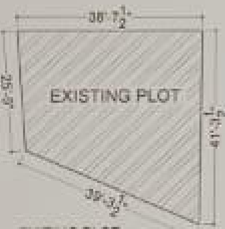

EXITING PLOT

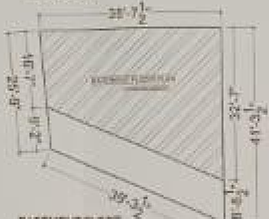

BASEMENT FLOOR

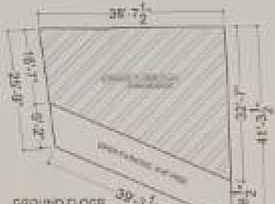

GROUND FLOOR

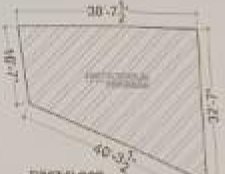

FIRST FLOOR

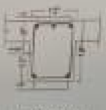

PLINTH BEAM

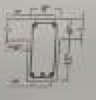

ROOF DETAIL

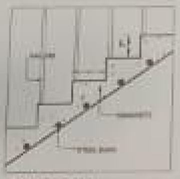

STEEL DETAIL

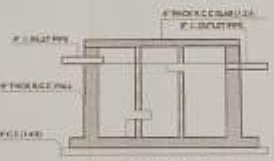

SEPTIC TANK (6' X 10')
Scale - 1/4"=1'-0"

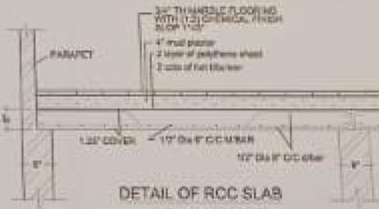

DETAIL OF RCC SLAB
Scale - 1/2"=1'-0"