

NSH

STATEMENT OF REINF.

S.NO.	SHORT SPAN	LONG SPAN
S-1	1/2" ø @ 6" C/C	1/2" ø @ 9" C/C
S-2	1/2" ø @ 7.5"" C/C	1/2" ø @ 7.5" C/C
S-3	3/8" ø @ 7" C/C	3/8"" ø @ 8" C/C
S-4	3/8" ø @ 6" C/C	3/8" ø @ 9" C/C

DOORS SCHEDULE


TYPE	SIZE	DES.
D1	5'-0" x 7'-0"	WOODEN
D2	3'-6" x 7'-0"	=
D3	3'-0" x 7'-0"	=
D4	2'-6" x 7'-0"	=


WINDOWS SCHEDULE

TYPE	SIZE	SILL LEV.,	DES.
W1	10'-0" x 6'-6"	0'-6"	ALUM.
W2	7'-0" x 6'-6"	0'-6"	=
W3	6'-0" x 3'-6"	0'-6"	=
W4	3'-0" x 6'-6"	0'-6"	=
W5	6'-0" x 3'-6"	3'-6"	=
W6	3'-0" x 2'-0"	3'-6"	=

STATEMENT OF AREA


TOTAL AREA OF PLOT	=	4250 SFT
COV. AREA OF G.FLOOR	=	2751 SFT
COV. AREA OF Ist FLOOR	=	2065 SFT
TOTAL COV. AREA	=	4816 SFT
OPEN AREA OF PLOT	=	1499 SFT

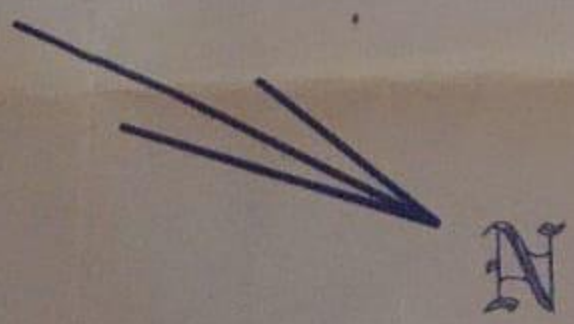


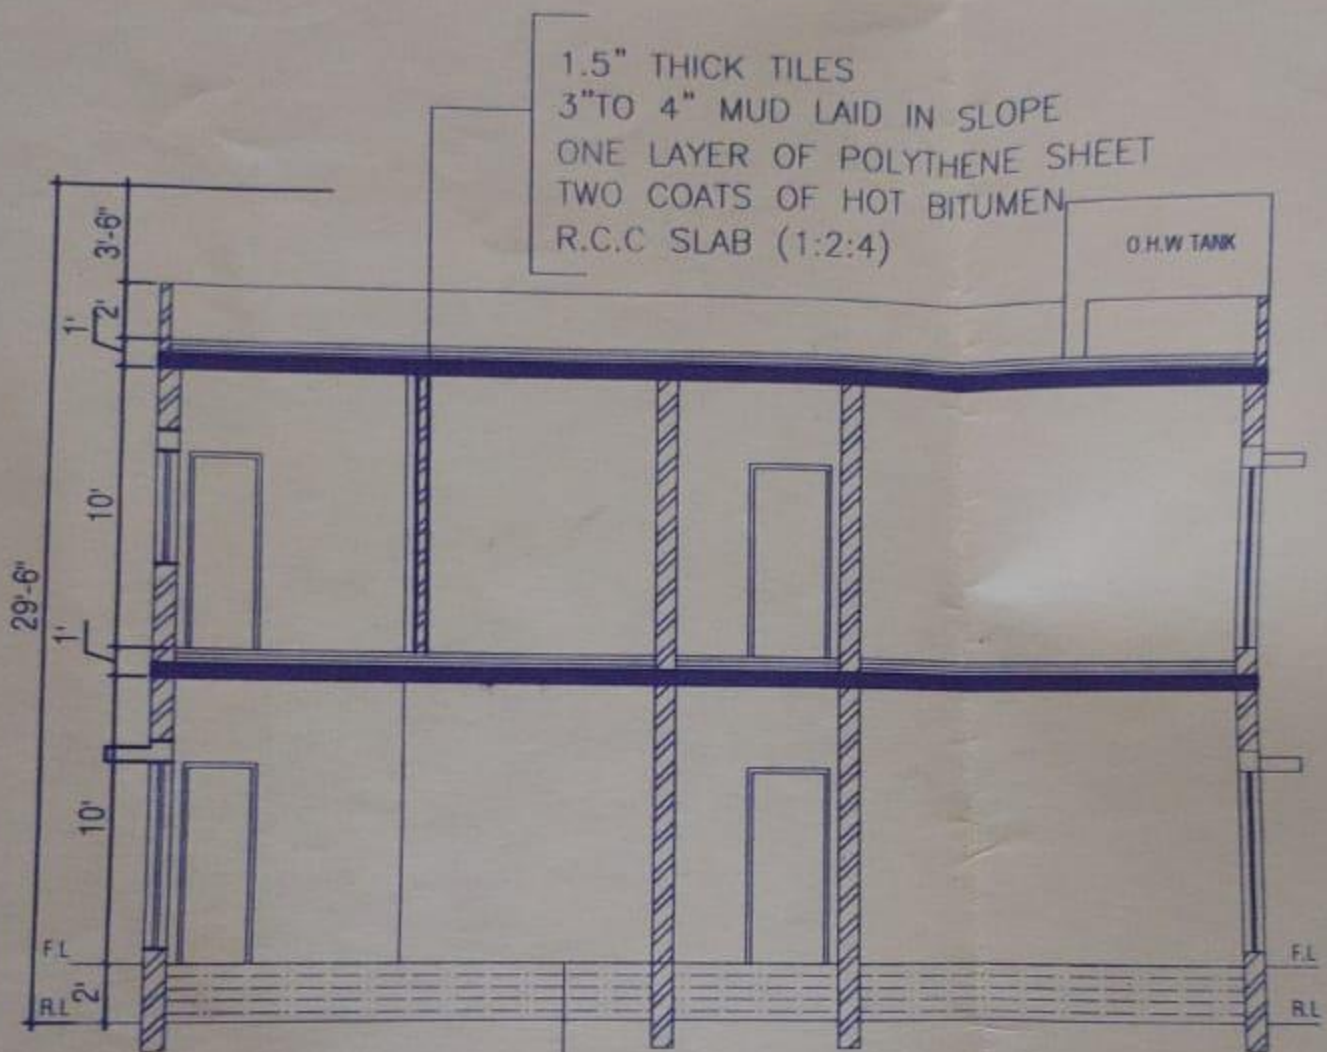


SECTION A-A

3/4" THICK TERRAZO FININSH
1.5" THICK P.C.C (1:2:4)
4" THICK SAND FILLING
COMPACTED EARTH

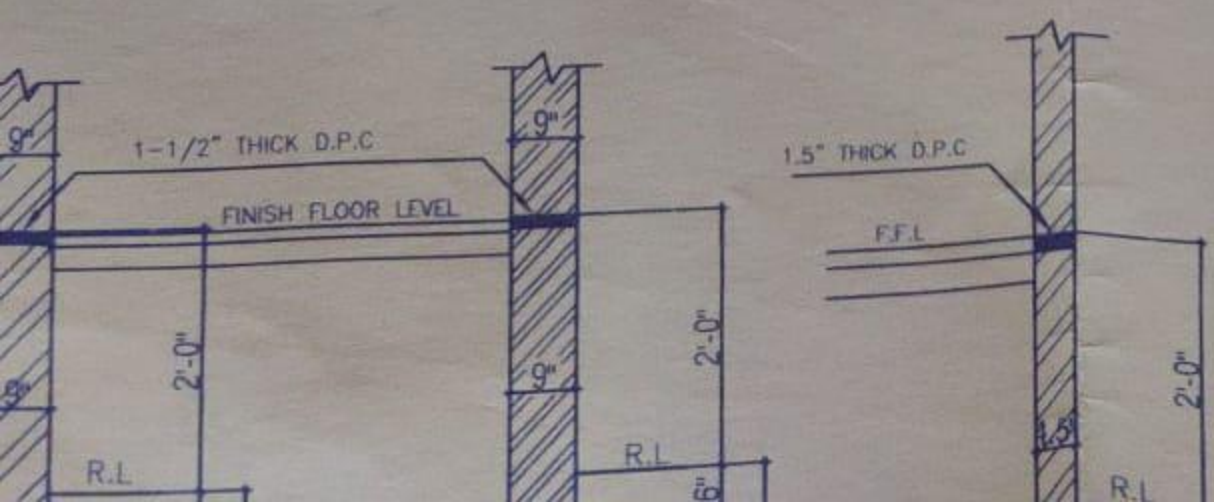


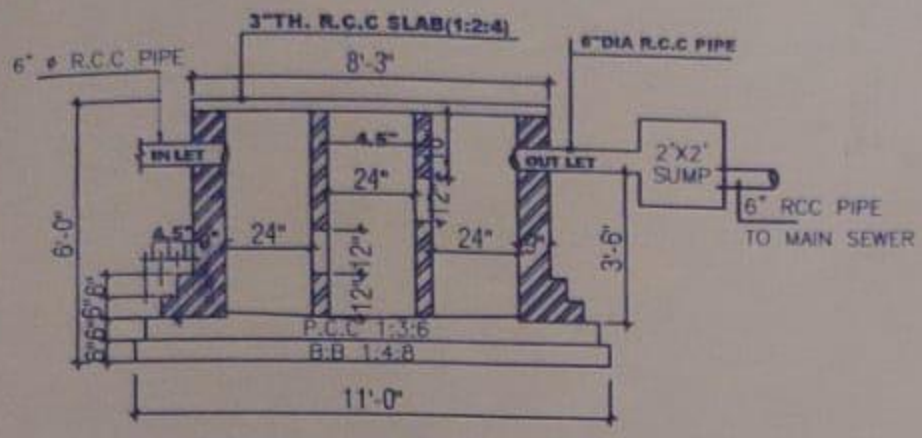


DETAIL OF SEPTIC TANK.

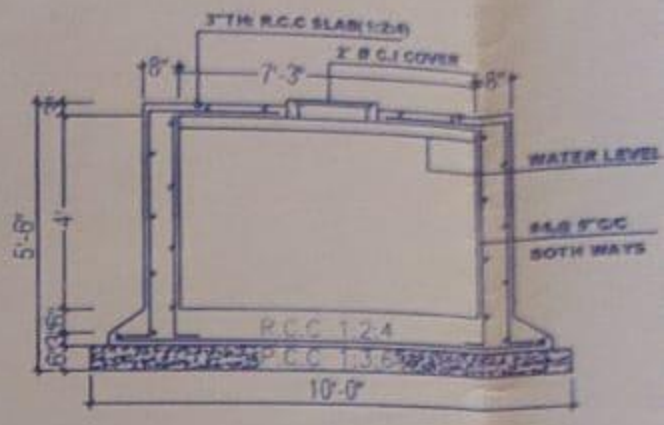


UNDER GROUND WATER TANK

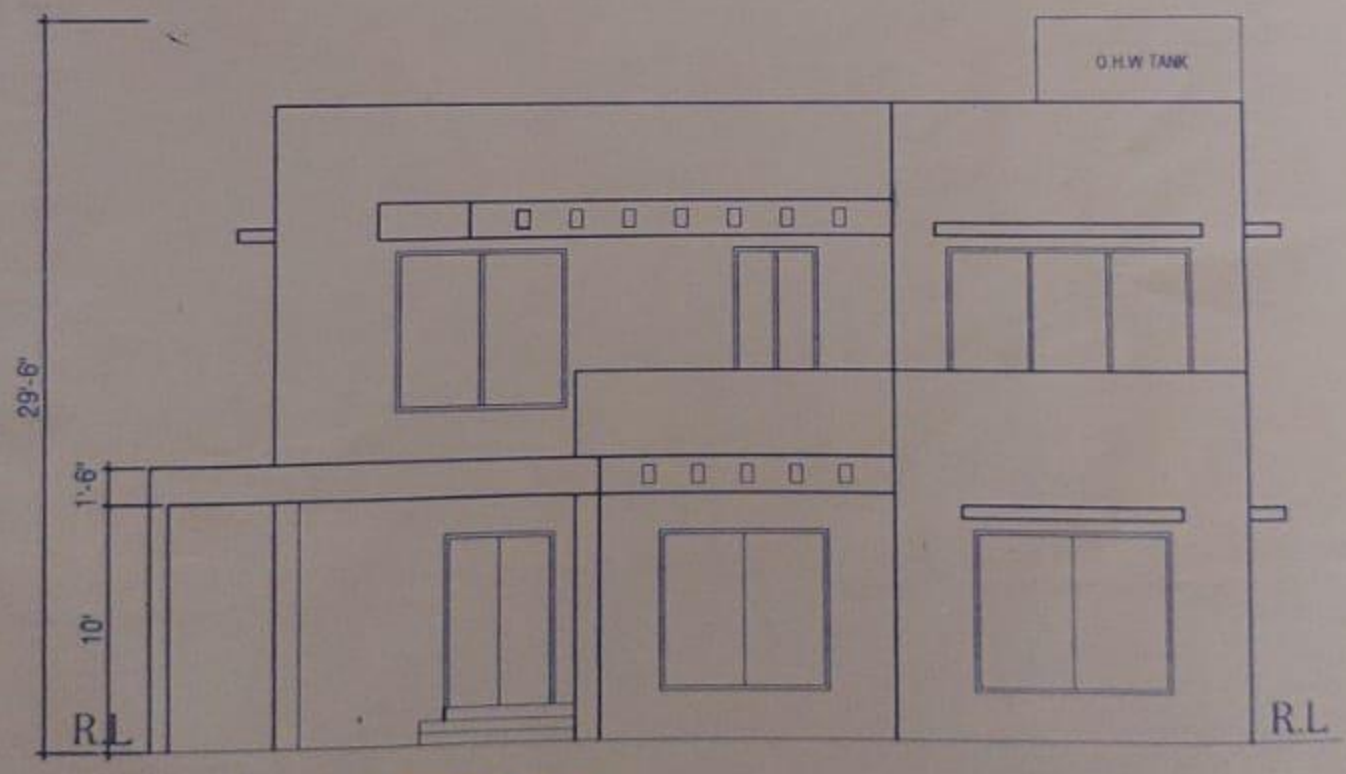


FRONT ELEVATION

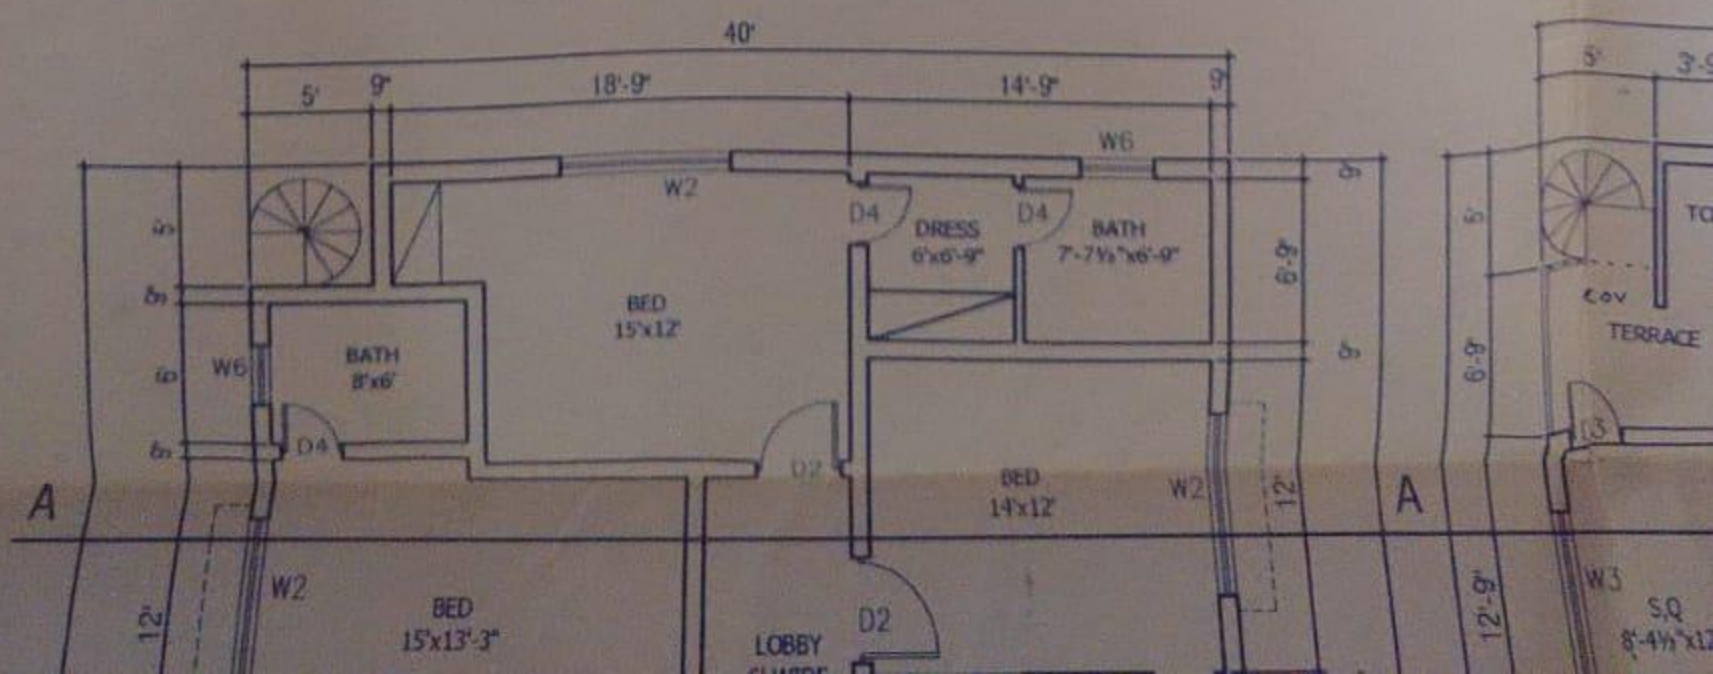

D 307

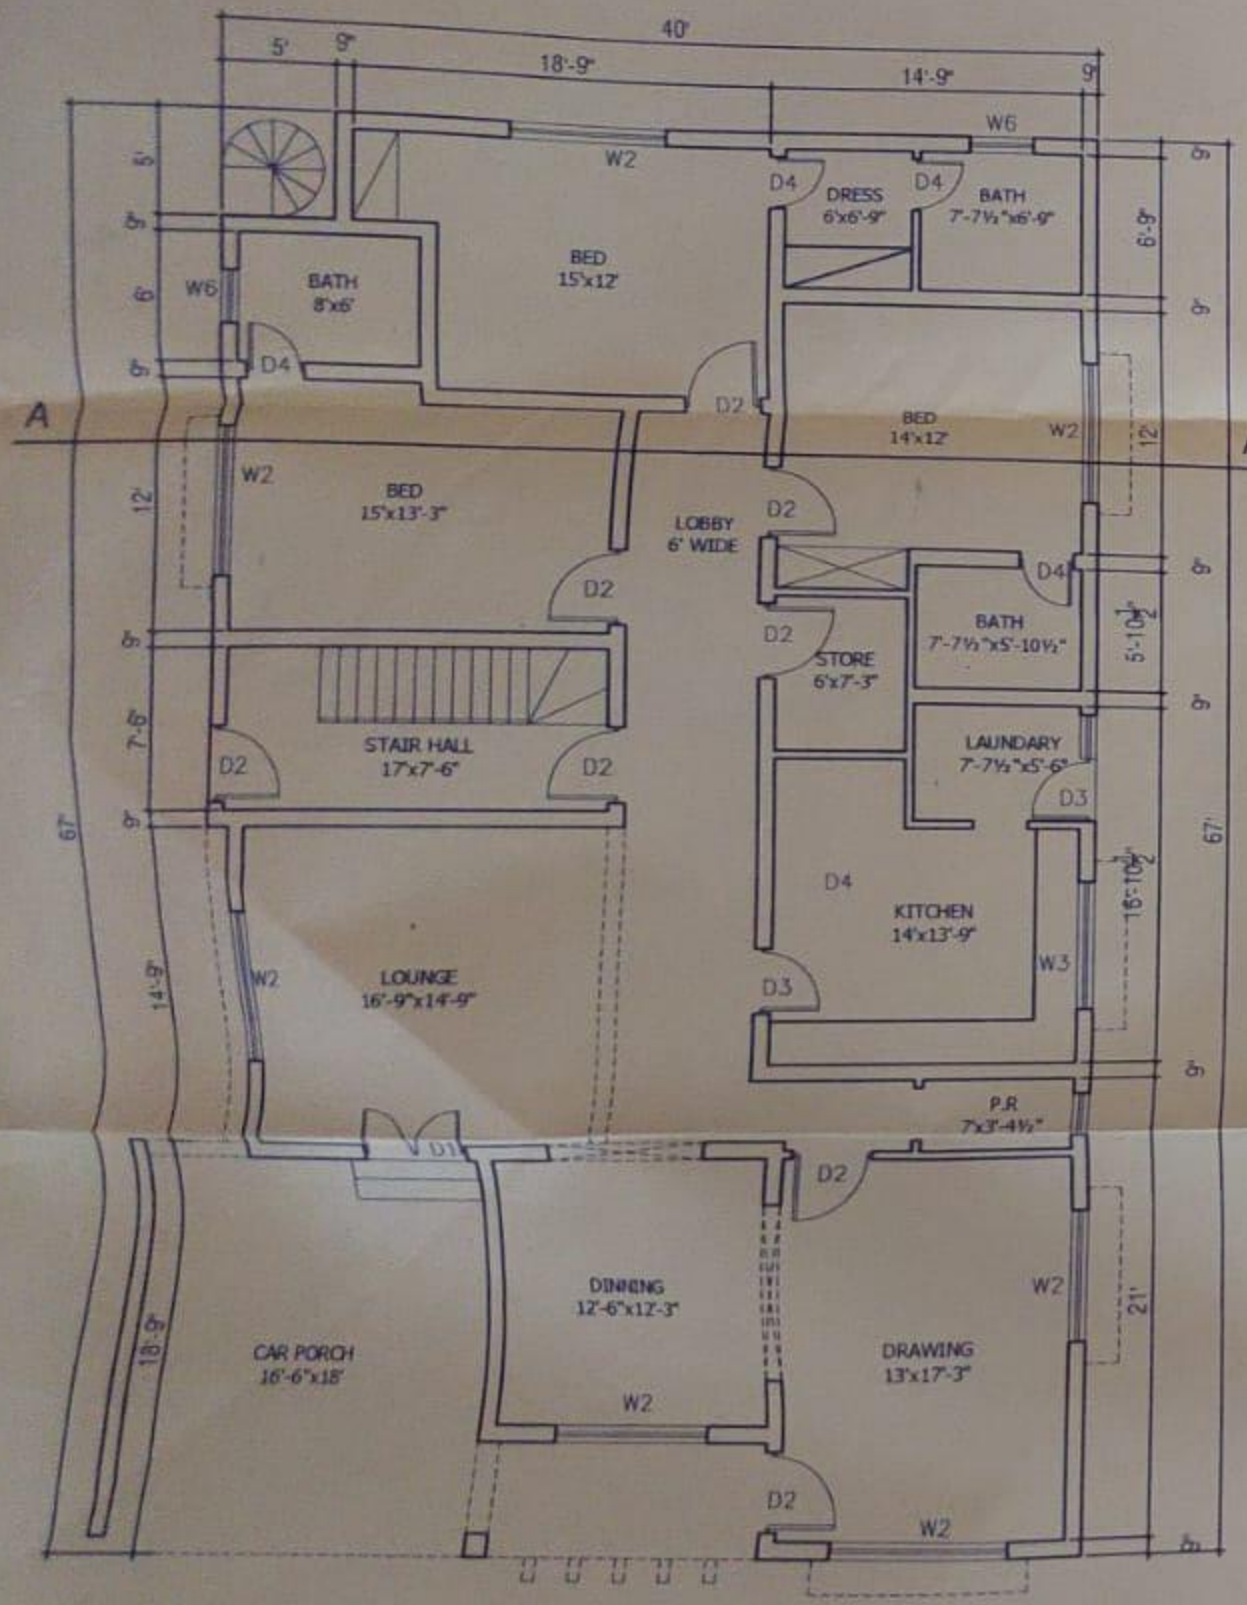


GROUND FLOOR PLAN

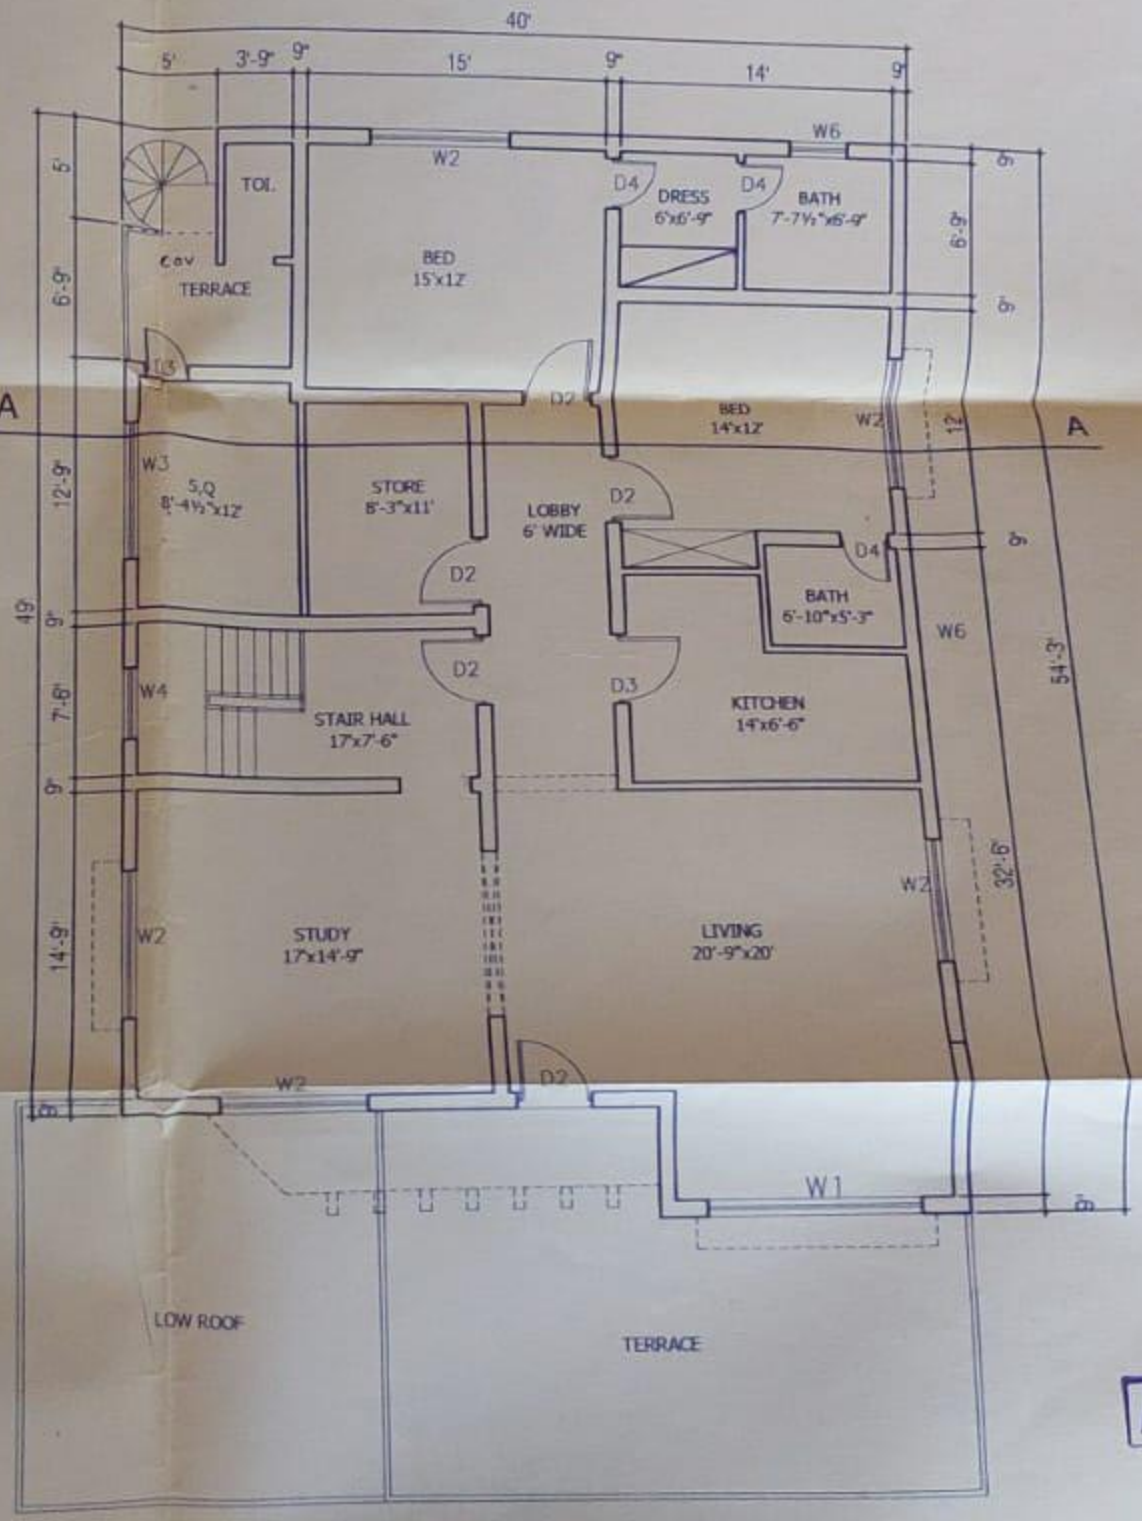


FIRST FLOOR PLAN

APPROVED

Maintenance Engineer (Civil)

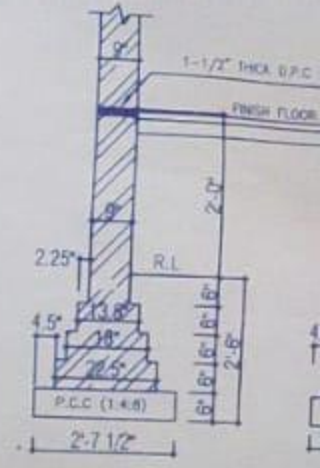

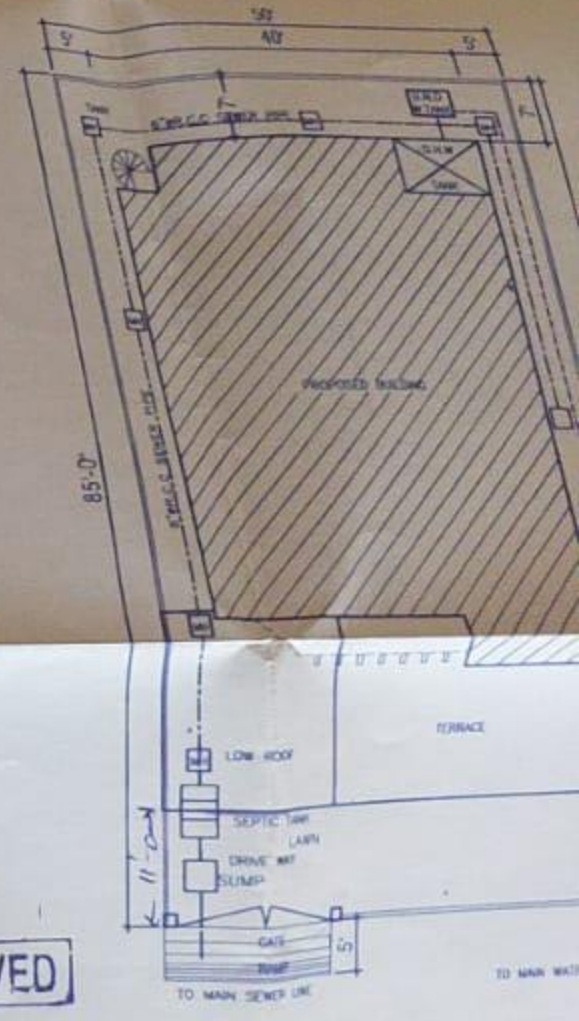

SITE PLAN

SCALE 1/16" = 1'-0"


D 307