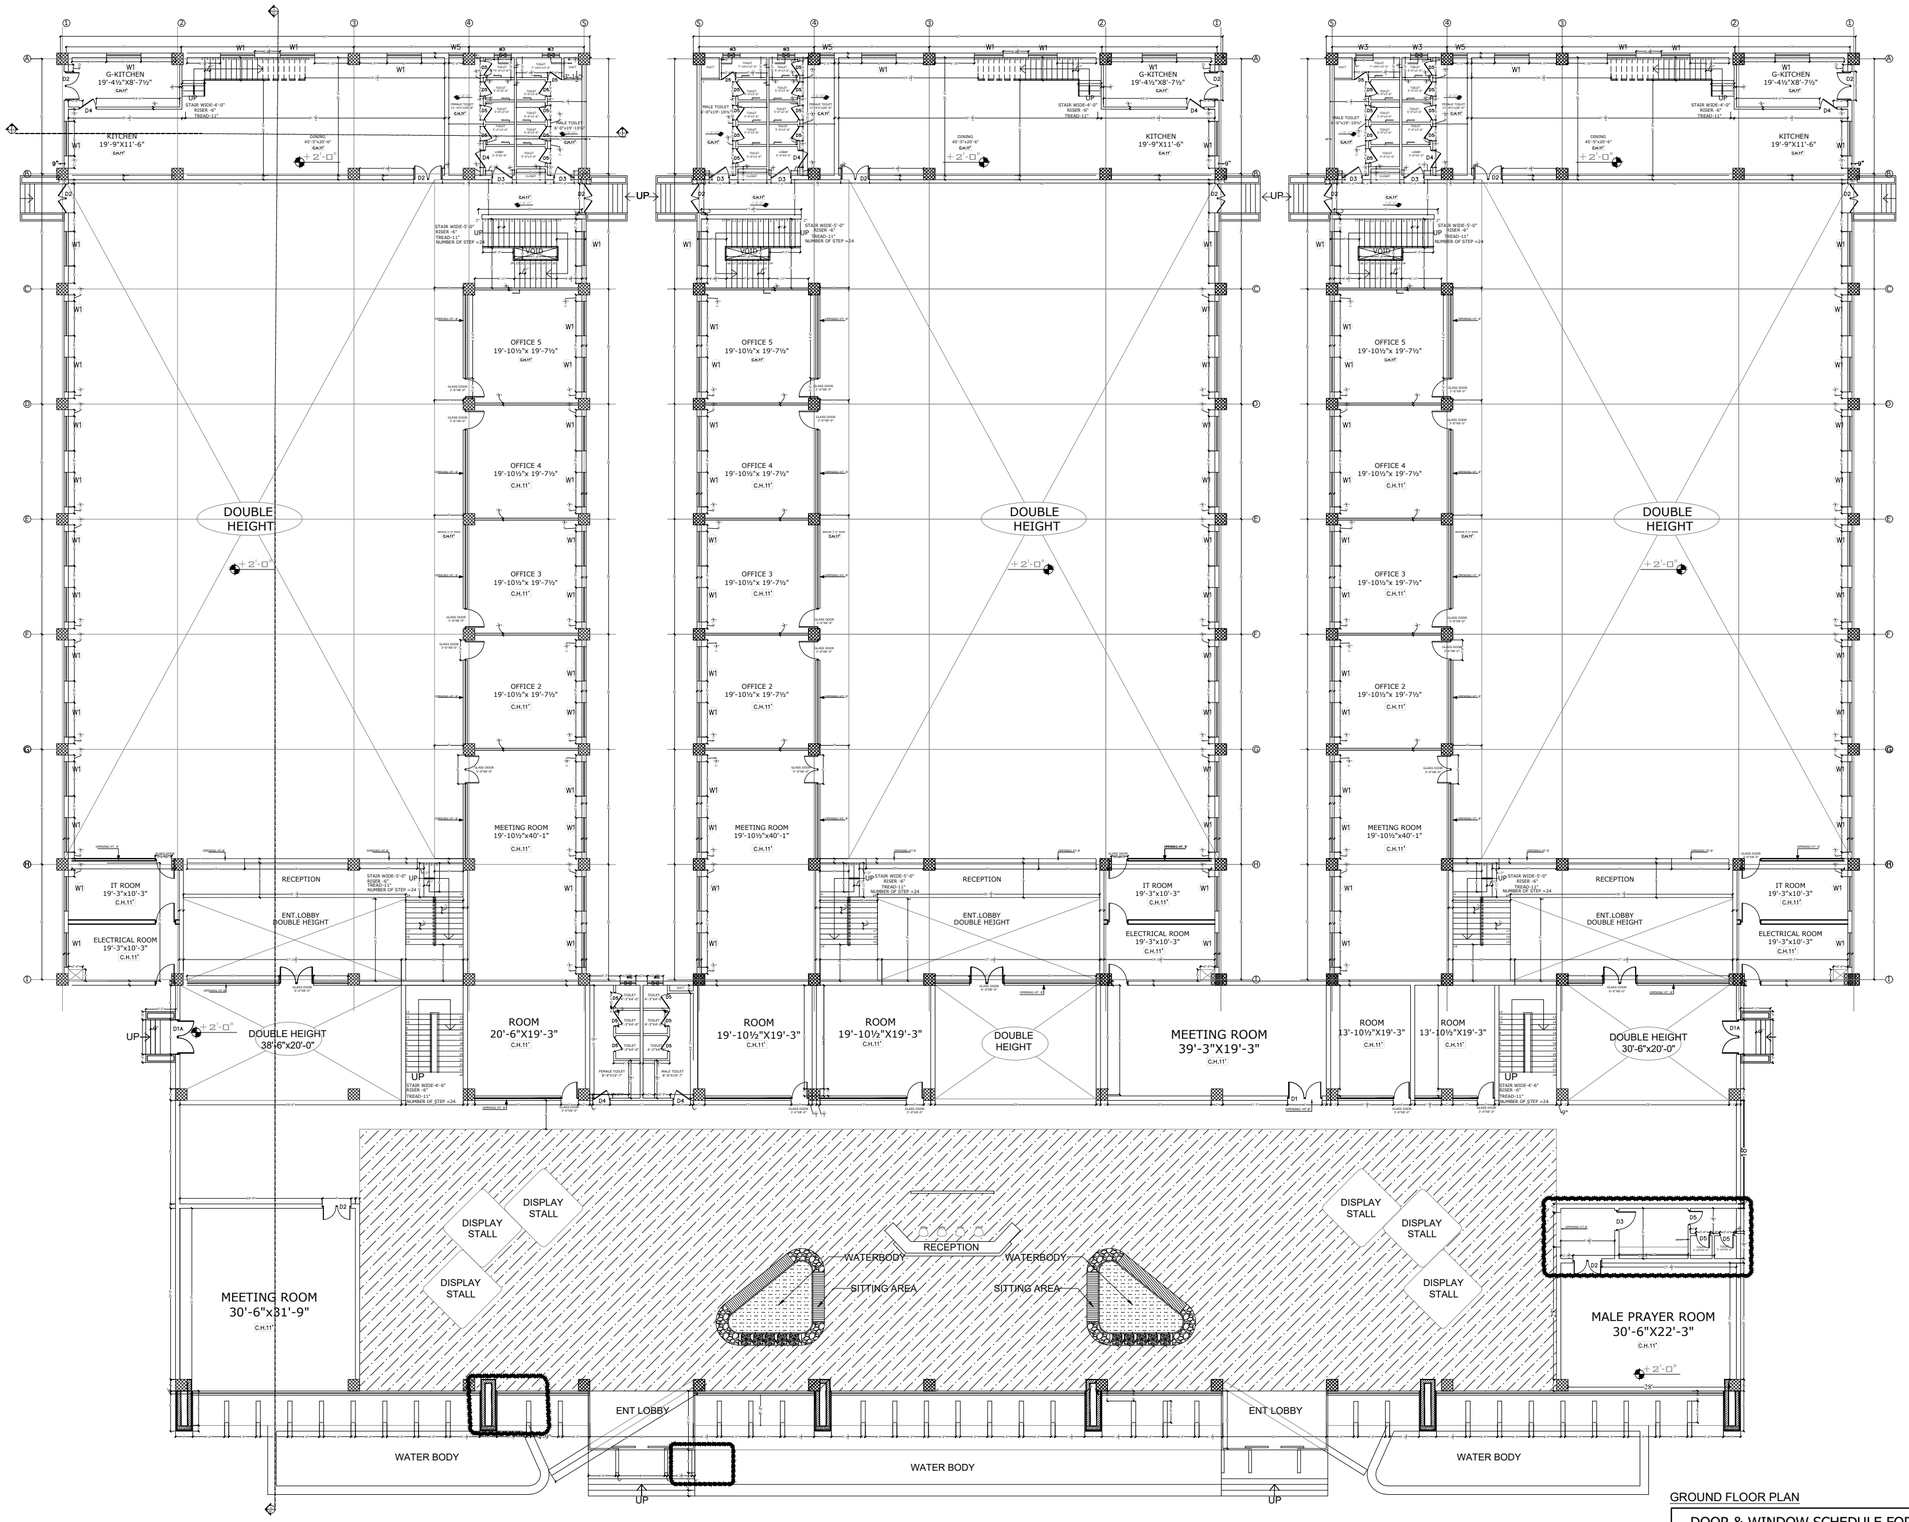


GROUND FLOOR

GROUND FLOOR PLAN

DOOR & WINDOW SCHEDULE FOR FIRST FLOOR

S.NO.	NAME	SIZE	S/LEVEL
1	D1	6'–0"x8–'0"	0'–0"
2	D1A	6'–0"x7–'0"	0'–0"
3	D2	5'–0"X7'–0"	0'–0"
4	D3	3'–6"X7'–0"	0'–0"
5	D4	3'–0"X7'–0"	0'–0"
6	D5	2'–6"X7'–0"	0'–0"
7	W1	6'–0"X4'–0"	3'–0"
8	W2	4'–0"X2'–0"	5'–0"
9	W3	3'–0"X2'–0"	5'–0"
10	W4	2'–9"X2'–0"	5'–0"
10	W5	2'–6"X2'–0"	5'–0"

N

COPYRIGHT :
THIS DRAWING IS COPYRIGHT AND MAY NOT BE ALTERED, REPRODUCED OR USED OTHER THAN FOR THE CONTRACT WORK FOR WHICH IT IS ISSUED WITHOUT THE WRITTEN PERMISSION FOR ***CAPITAL SMART CITY***,

WARNING :
DO NOT SCALE FROM THE DRAWING.
THE CONTRACTOR AND HIS SUB - CONTRACTORS ARE TO VERIFY ALL DIAMENSIONS ON SITE BEFORE PREPARING SHOP DRAWINGS OR COMMENCING MANUFACTURE.
THE CONTRACTOR IS TO BRING TO THE NOTICE OF THE ARCHITECT ANY DISCRIPENCIES CONTAINED IN THIS DRAWING PRIOR TO WORK COMMENCEMENT.

REV. No.	REVISION	DATE
04		
03		
02		
01		

CONSULTANTS :
Infra Tech. Pakistan Pvt.Ltd.

CLIENT :
CAPITAL SMART CITY


PROJECT :
INCUBATION CENTER

TITLE :
GROUND FLOOR WORKING PLAN

SCALE :	A-1	A-3	DATE : 28.09.2023

PROJECT ARCHITECT :	ASSISTANT ARCHITECT :	APPROVED BY :
Urooj Basharat (Sr.Architect)	Noman Khalid (Architect)	Malik Muhammad Aslam (Group C.O.O)
DRAWN BY : Mian Hamza (Draftsman)	CHECKED BY : Ali Imran (Dy.Chief Architect)	

JOB No :	DRG. No :	REV. No :
23-005	A-201	05

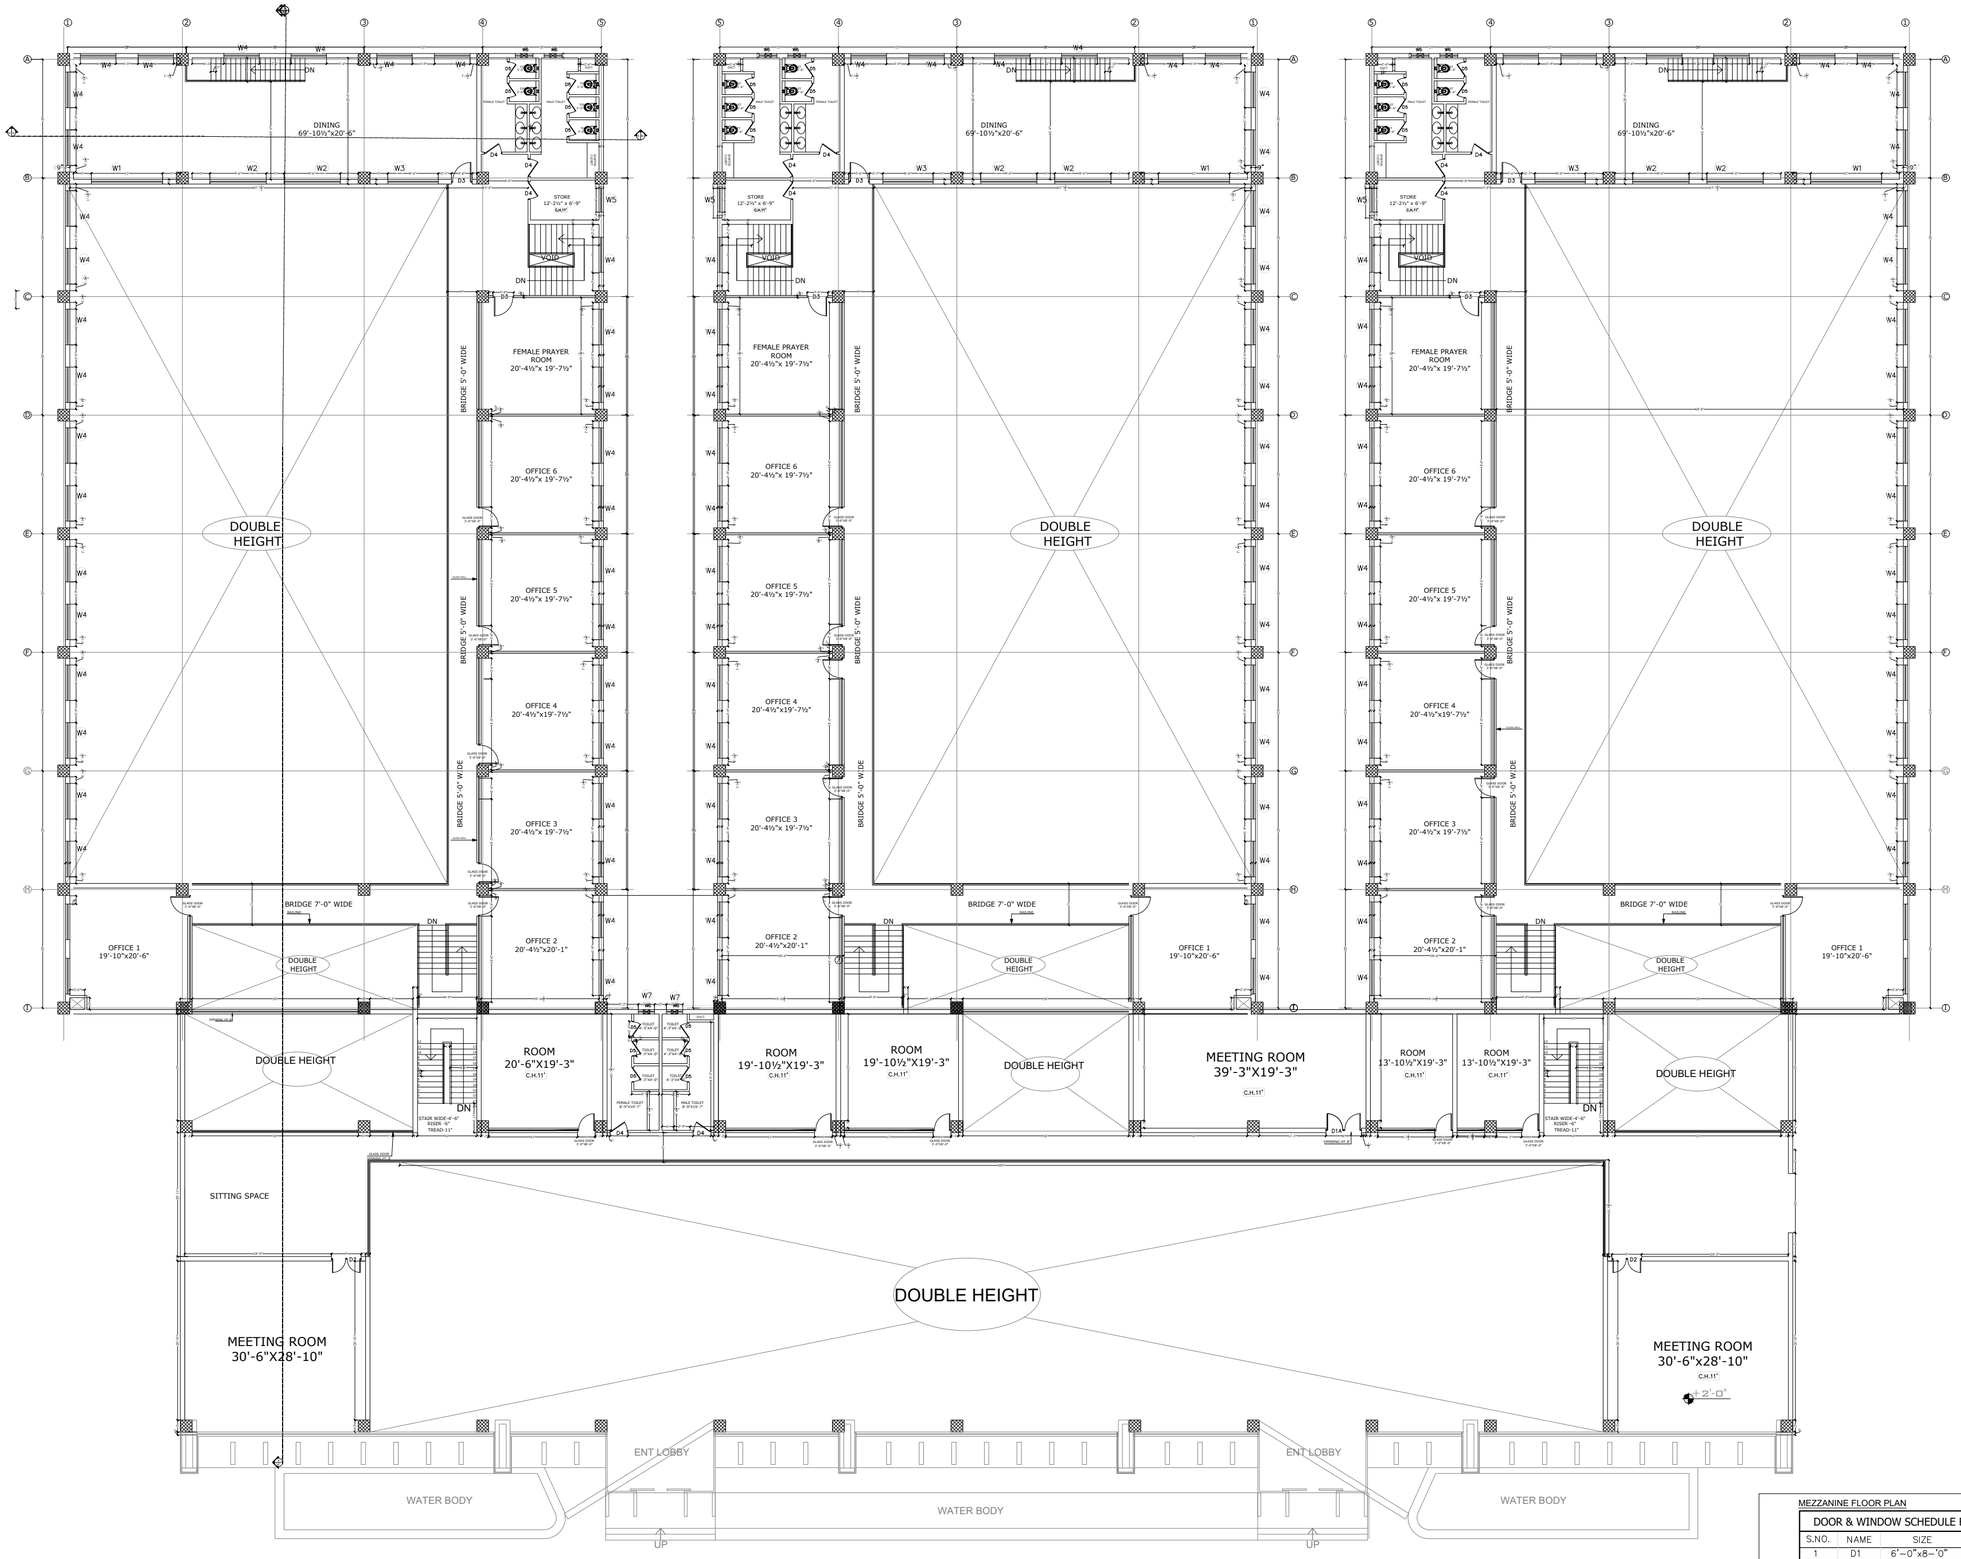

MEZZANINE FLOOR

MEZZANINE FLOOR PLAN

DOOR & WINDOW SCHEDULE FOR FIRST FLOOR

S.NO.	NAME	SIZE	S/LEVEL
1	D1	6'-0"x8-'0"	0'-0"
2	D1A	6'-0"x7-'0"	0'-0"
3	D2	5'-0"X7'-0"	0'-0"
4	D3	3'-6"X7'-0"	0'-0"
5	D4	3'-0"X7'-0"	0'-0"
6	D5	2'-6"x7'-0"	0'-0"
7	W1	12'-0"X4'-0"	3'-0"
8	W2	9'-6"X4'-0"	3'-0"
9	W3	8'-6"X4'-0"	3'-0"
10	W4	6'-0"X4'-0"	3'-0"
11	W5	4'-0"X4'-0"	3'-0"
12	W6	3'-0"X2'-0"	5'-0"
13	W7	2'-9"X2'-0"	5'-0"

COPYRIGHT :

THIS DRAWING IS COPYRIGHT AND MAY NOT BE ALTERED, REPRODUCED OR USED OTHER THAN FOR THE CONTRACT WORK FOR WHICH IT IS ISSUED WITHOUT THE WRITTEN PERMISSION FOR ***CAPITAL SMART CITY***,

WARNING :

DO NOT SCALE FROM THE DRAWING.
THE CONTRACTOR AND HIS SUB - CONTRACTORS ARE TO VERIFY ALL DIAMENSIONS ON SITE BEFORE PREPARING SHOP DRAWINGS OR COMMENCING MANUFACTURE.
THE CONTRACTOR IS TO BRING TO THE NOTICE OF THE ARCHITECT ANY DISCRIPENCIES CONTAINED IN THIS DRAWING PRIOR TO WORK COMMENCEMENT.

REV. No.	REVISION	DATE
04		
03		
02		
01		

CONSULTANTS :

Infra Tech. Pakistan Pvt.Ltd.

CLIENT :

CAPITAL SMART CITY

PROJECT :


INCUBATION CENTER

TITLE :

MEZZANINE FLOOR WORKING PLAN

SCALE :	A - 1	A - 3	DATE : 28.09.2023

PROJECT ARCHITECT : Urooj Basharat (Sr.Architect)	ASSISTANT ARCHITECT : Noman Khalid (Architect)	APPROVED BY : Malik Muhammad Aslam (Group C.O.O)
DRAWN BY : Mian Hamza (Draftsman)	CHECKED BY : Ali Imran (Dy.Chief Architect)	
JOB No : 23-005	DRG. No : A-301	REV. No : 05

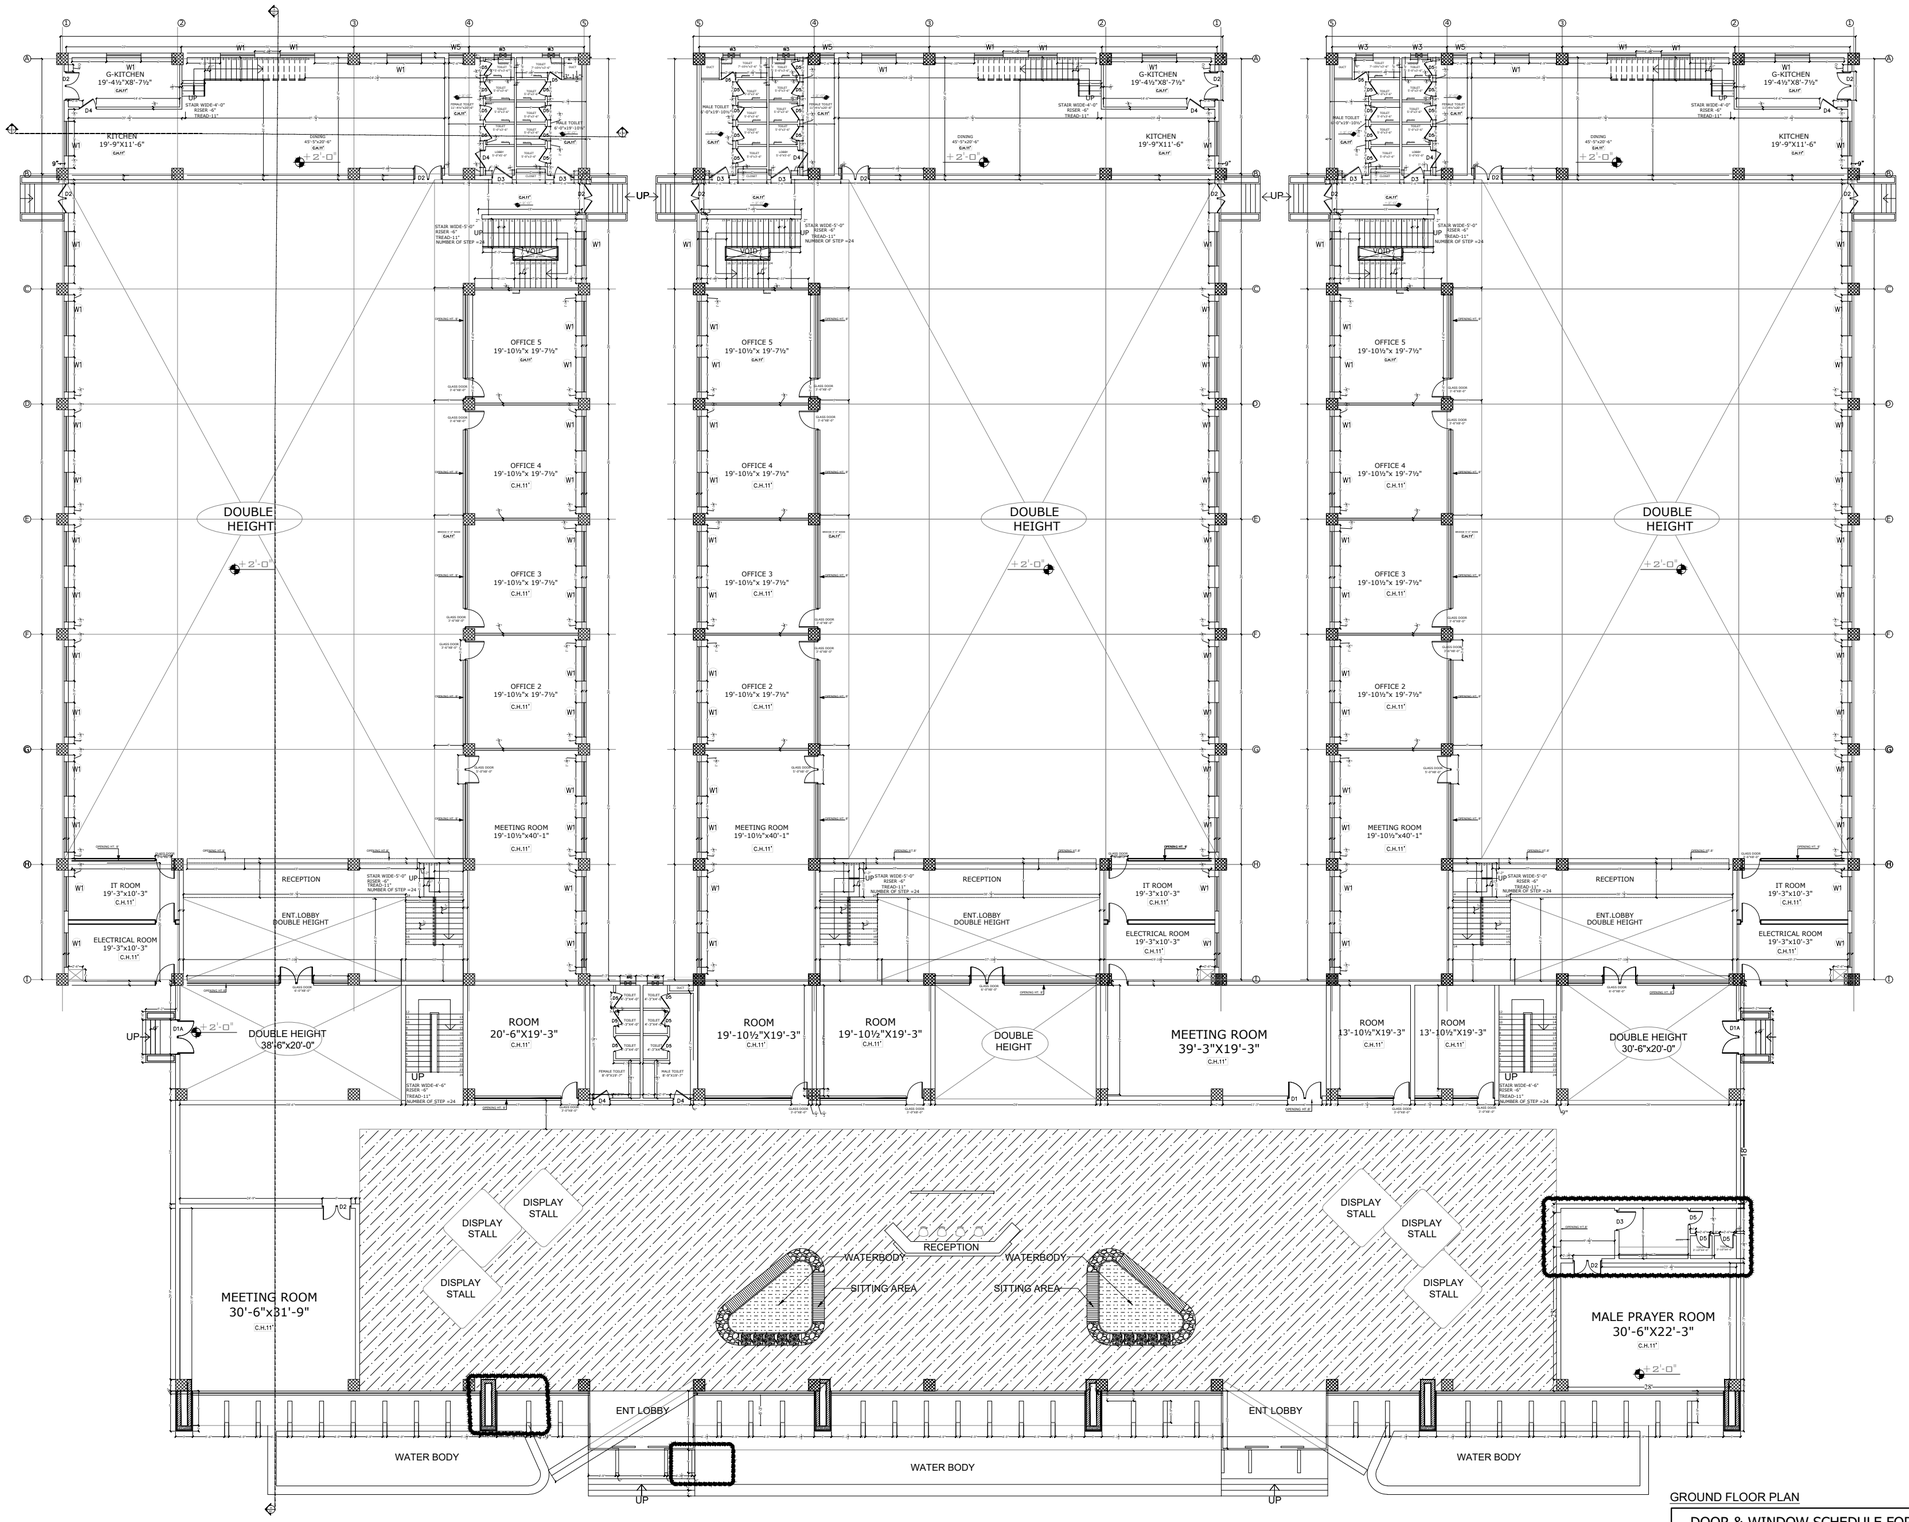

GROUND FLOOR

GROUND FLOOR PLAN

DOOR & WINDOW SCHEDULE FOR FIRST FLOOR

S.NO.	NAME	SIZE	S/LEVEL
1	D1	6'–0"x8–'0"	0'–0"
2	D1A	6'–0"x7–'0"	0'–0"
3	D2	5'–0"X7'–0"	0'–0"
4	D3	3'–6"X7'–0"	0'–0"
5	D4	3'–0"X7'–0"	0'–0"
6	D5	2'–6"X7'–0"	0'–0"
7	W1	6'–0"X4'–0"	3'–0"
8	W2	4'–0"X2'–0"	5'–0"
9	W3	3'–0"X2'–0"	5'–0"
10	W4	2'–9"X2'–0"	5'–0"
10	W5	2'–6"X2'–0"	5'–0"

N

COPYRIGHT :
THIS DRAWING IS COPYRIGHT AND MAY NOT BE ALTERED, REPRODUCED OR USED OTHER THAN FOR THE CONTRACT WORK FOR WHICH IT IS ISSUED WITHOUT THE WRITTEN PERMISSION FOR ***CAPITAL SMART CITY***,

WARNING :
DO NOT SCALE FROM THE DRAWING.
THE CONTRACTOR AND HIS SUB - CONTRACTORS ARE TO VERIFY ALL DIAMENSIONS ON SITE BEFORE PREPARING SHOP DRAWINGS OR COMMENCING MANUFACTURE.
THE CONTRACTOR IS TO BRING TO THE NOTICE OF THE ARCHITECT ANY DISCRIPENCIES CONTAINED IN THIS DRAWING PRIOR TO WORK COMMENCEMENT.

REV. No.	REVISION	DATE
04		
03		
02		
01		

CONSULTANTS :
Infra Tech. Pakistan Pvt.Ltd.

CLIENT :
CAPITAL SMART CITY


PROJECT :
INCUBATION CENTER

TITLE :
GROUND FLOOR WORKING PLAN

SCALE :	A-1	A-3	DATE : 28.09.2023

PROJECT ARCHITECT :	ASSISTANT ARCHITECT :	APPROVED BY :
Urooj Basharat (Sr.Architect)	Noman Khalid (Architect)	Malik Muhammad Aslam (Group C.O.O)
DRAWN BY : Mian Hamza (Draftsman)	CHECKED BY : Ali Imran (Dy.Chief Architect)	

JOB No :	DRG. No :	REV. No :
23-005	A-201	05

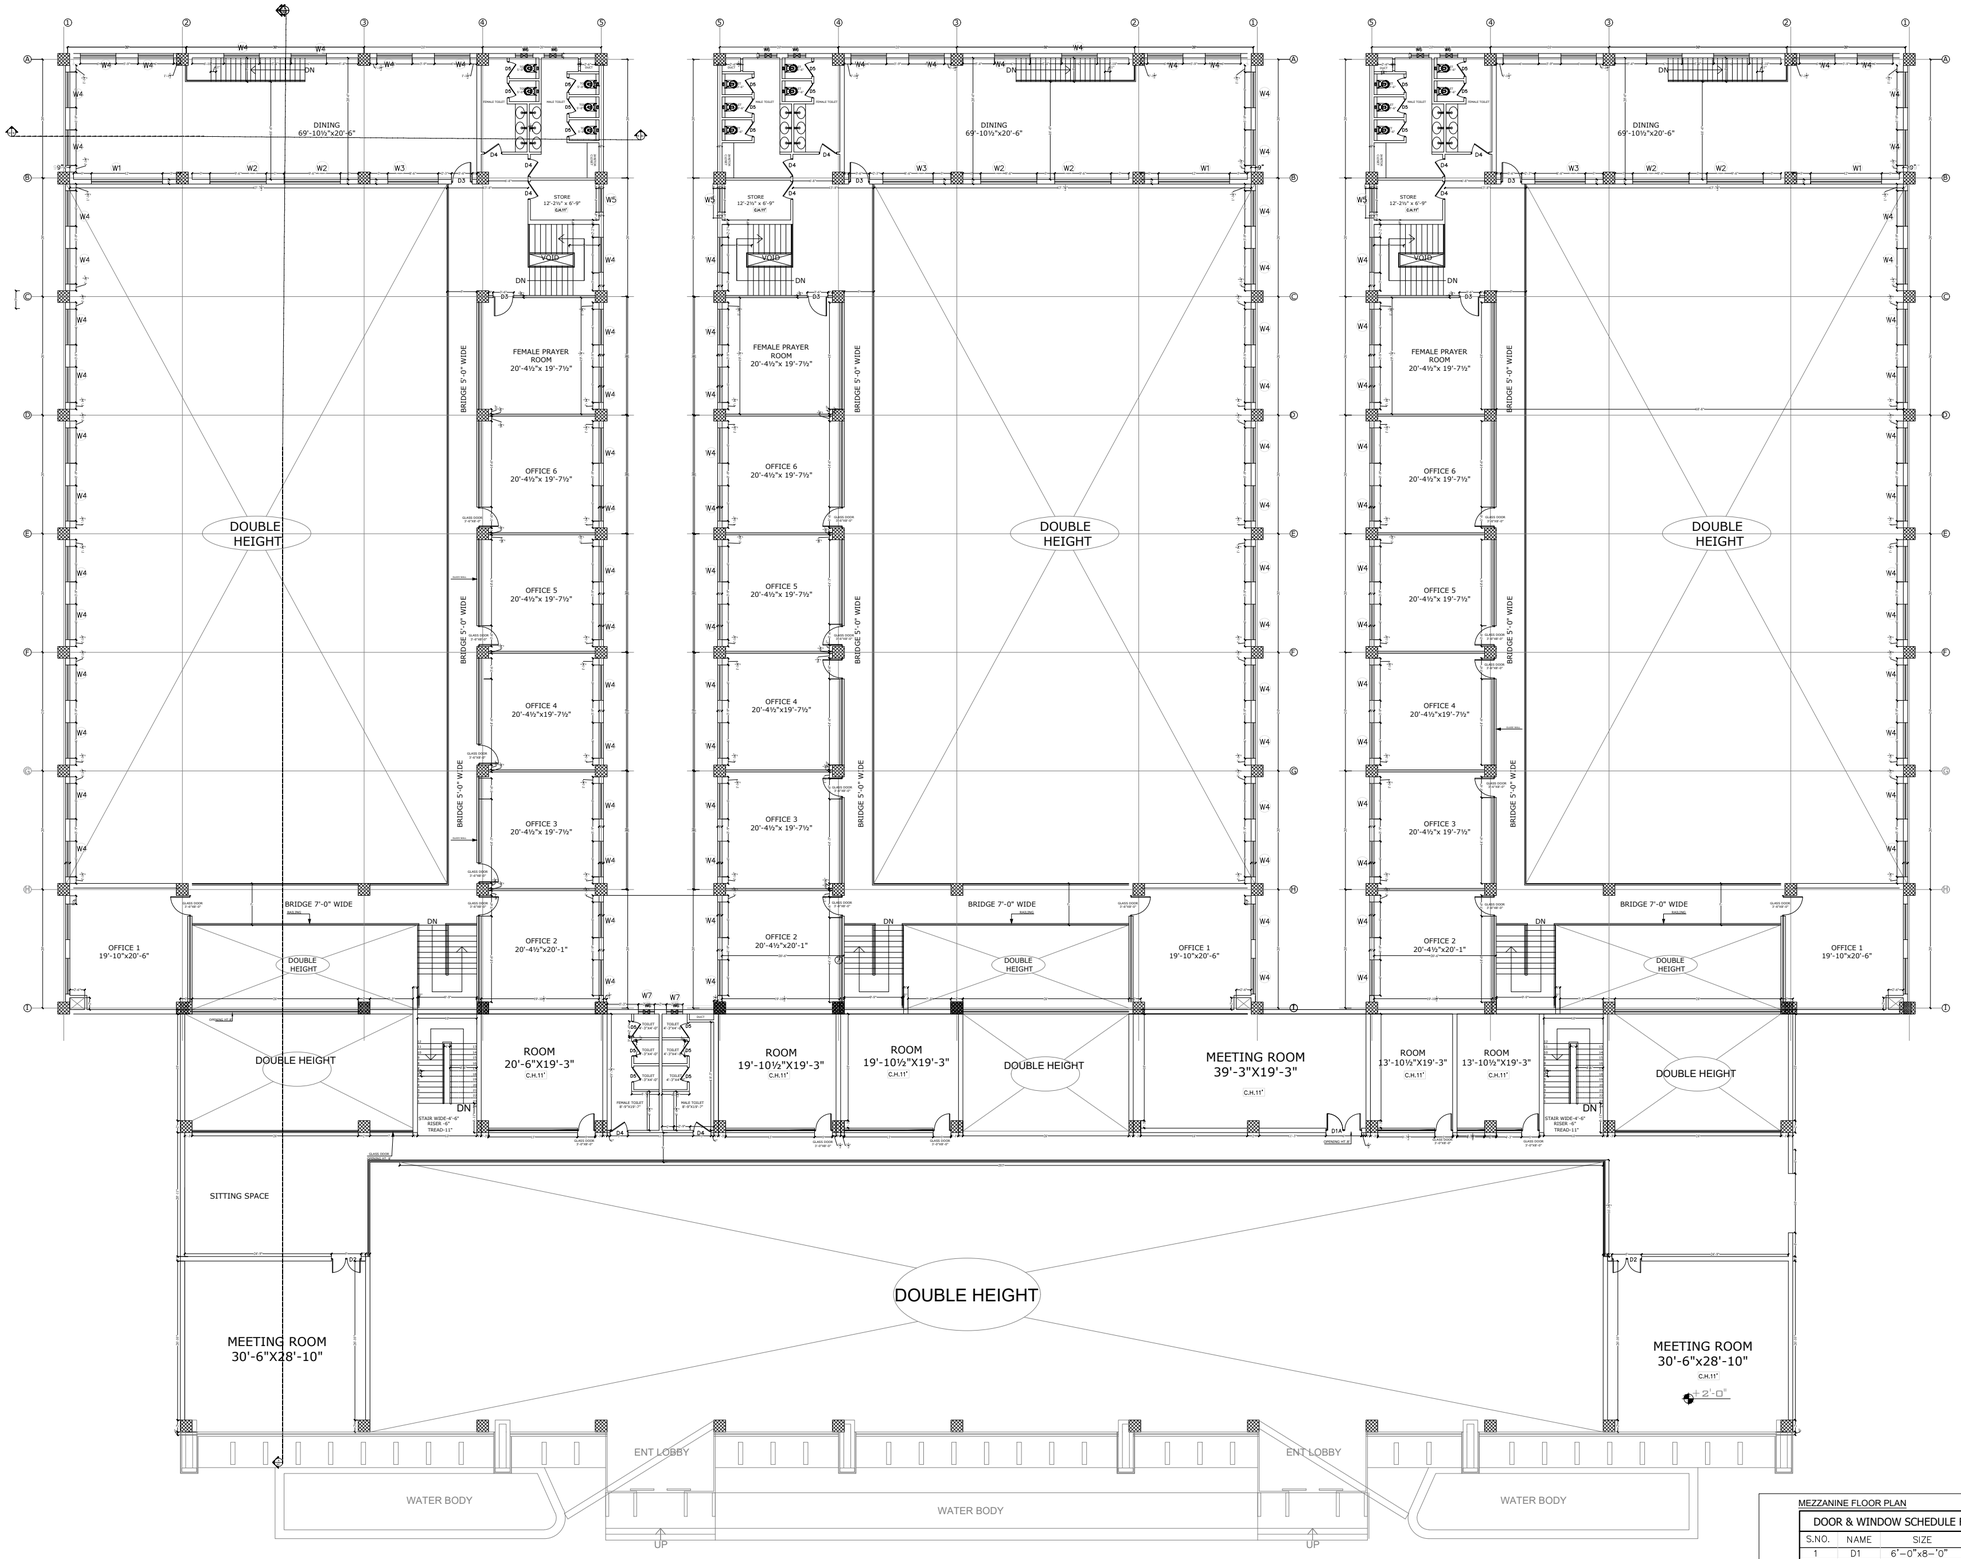

MEZZANINE FLOOR

MEZZANINE FLOOR PLAN

DOOR & WINDOW SCHEDULE FOR FIRST FLOOR

S.NO.	NAME	SIZE	S/LEVEL
1	D1	6'-0"x8-'0"	0'-0"
2	D1A	6'-0"x7-'0"	0'-0"
3	D2	5'-0"X7'-0"	0'-0"
4	D3	3'-6"X7'-0"	0'-0"
5	D4	3'-0"X7'-0"	0'-0"
6	D5	2'-6"x7'-0"	0'-0"
7	W1	12'-0"X4'-0"	3'-0"
8	W2	9'-6"X4'-0"	3'-0"
9	W3	8'-6"X4'-0"	3'-0"
10	W4	6'-0"X4'-0"	3'-0"
11	W5	4'-0"X4'-0"	3'-0"
12	W6	3'-0"X2'-0"	5'-0"
13	W7	2'-9"X2'-0"	5'-0"

COPYRIGHT :

THIS DRAWING IS COPYRIGHT AND MAY NOT BE ALTERED, REPRODUCED OR USED OTHER THAN FOR THE CONTRACT WORK FOR WHICH IT IS ISSUED WITHOUT THE WRITTEN PERMISSION FOR ***CAPITAL SMART CITY***,

WARNING :

DO NOT SCALE FROM THE DRAWING.
THE CONTRACTOR AND HIS SUB - CONTRACTORS ARE TO VERIFY ALL DIAMENSIONS ON SITE BEFORE PREPARING SHOP DRAWINGS OR COMMENCING MANUFACTURE.
THE CONTRACTOR IS TO BRING TO THE NOTICE OF THE ARCHITECT ANY DISCRIPENCIES CONTAINED IN THIS DRAWING PRIOR TO WORK COMMENCEMENT.

REV. No.	REVISION	DATE
04		
03		
02		
01		

CONSULTANTS :

Infra Tech. Pakistan Pvt.Ltd.

CLIENT :

CAPITAL SMART CITY

PROJECT :


INCUBATION CENTER

TITLE :

MEZZANINE FLOOR WORKING PLAN

SCALE :	A - 1	A - 3	DATE : 28.09.2023

PROJECT ARCHITECT : Urooj Basharat (Sr.Architect)	ASSISTANT ARCHITECT : Noman Khalid (Architect)	APPROVED BY : Malik Muhammad Aslam (Group C.O.O)
DRAWN BY : Mian Hamza (Draftsman)	CHECKED BY : Ali Imran (Dy.Chief Architect)	
JOB No : 23-005	DRG. No : A-301	REV. No : 05

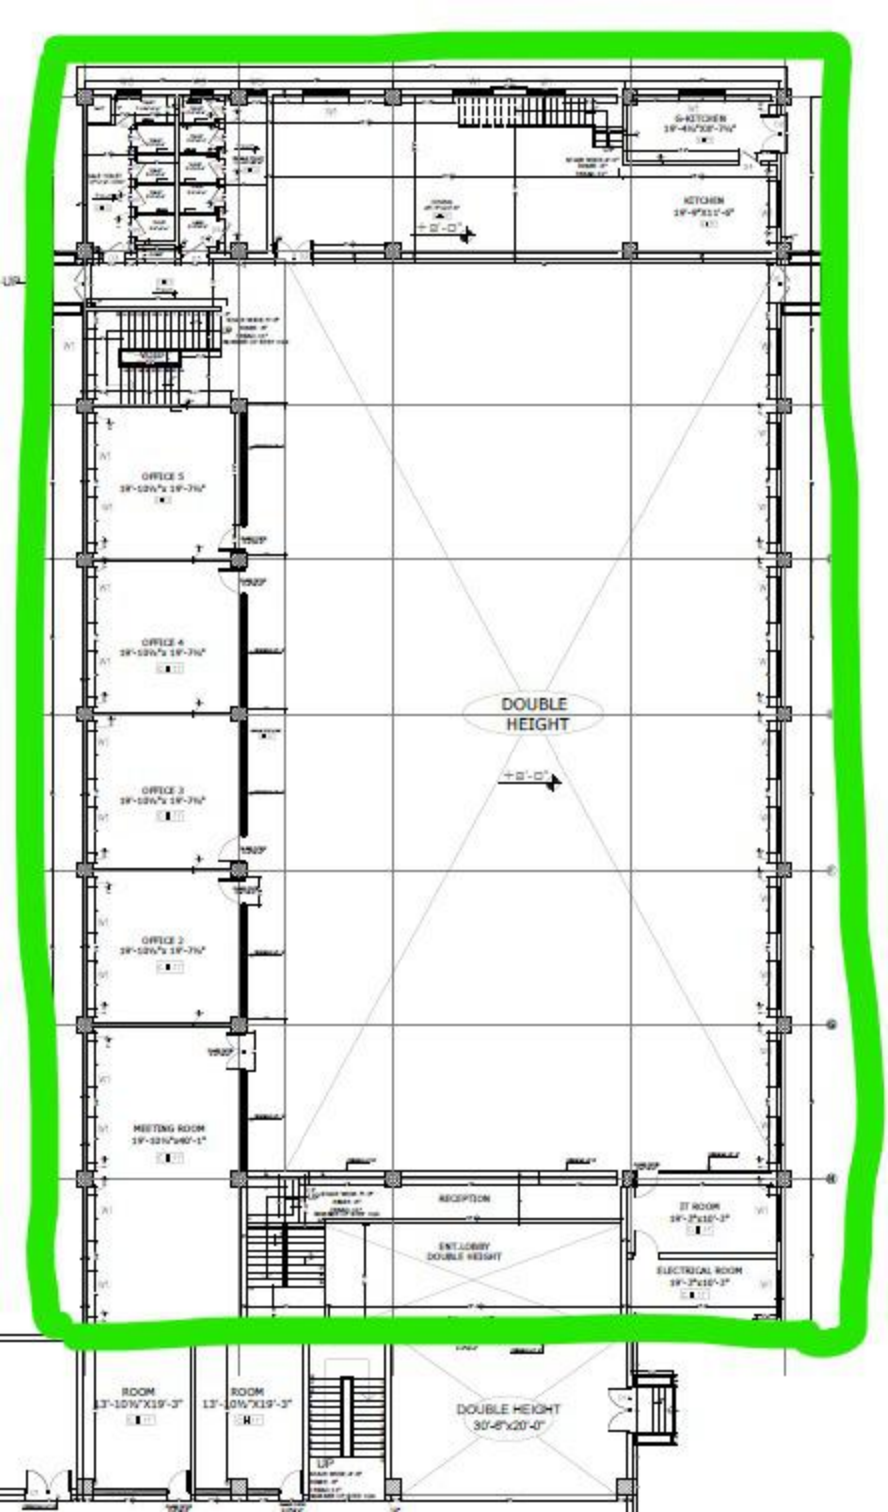
G-KITCHEN
KITCHEN
OFFICE 5
OFFICE 4
OFFICE 3
OFFICE 2
MEETING ROOM
DOUBLE
HEIGHT
RECEPTION
ENT.LOBBY
DOUBLE HEIGHT
IT ROOM
ELECTRICAL ROOM
ROOM
ROOM
UP
DOUBLE HEIGHT