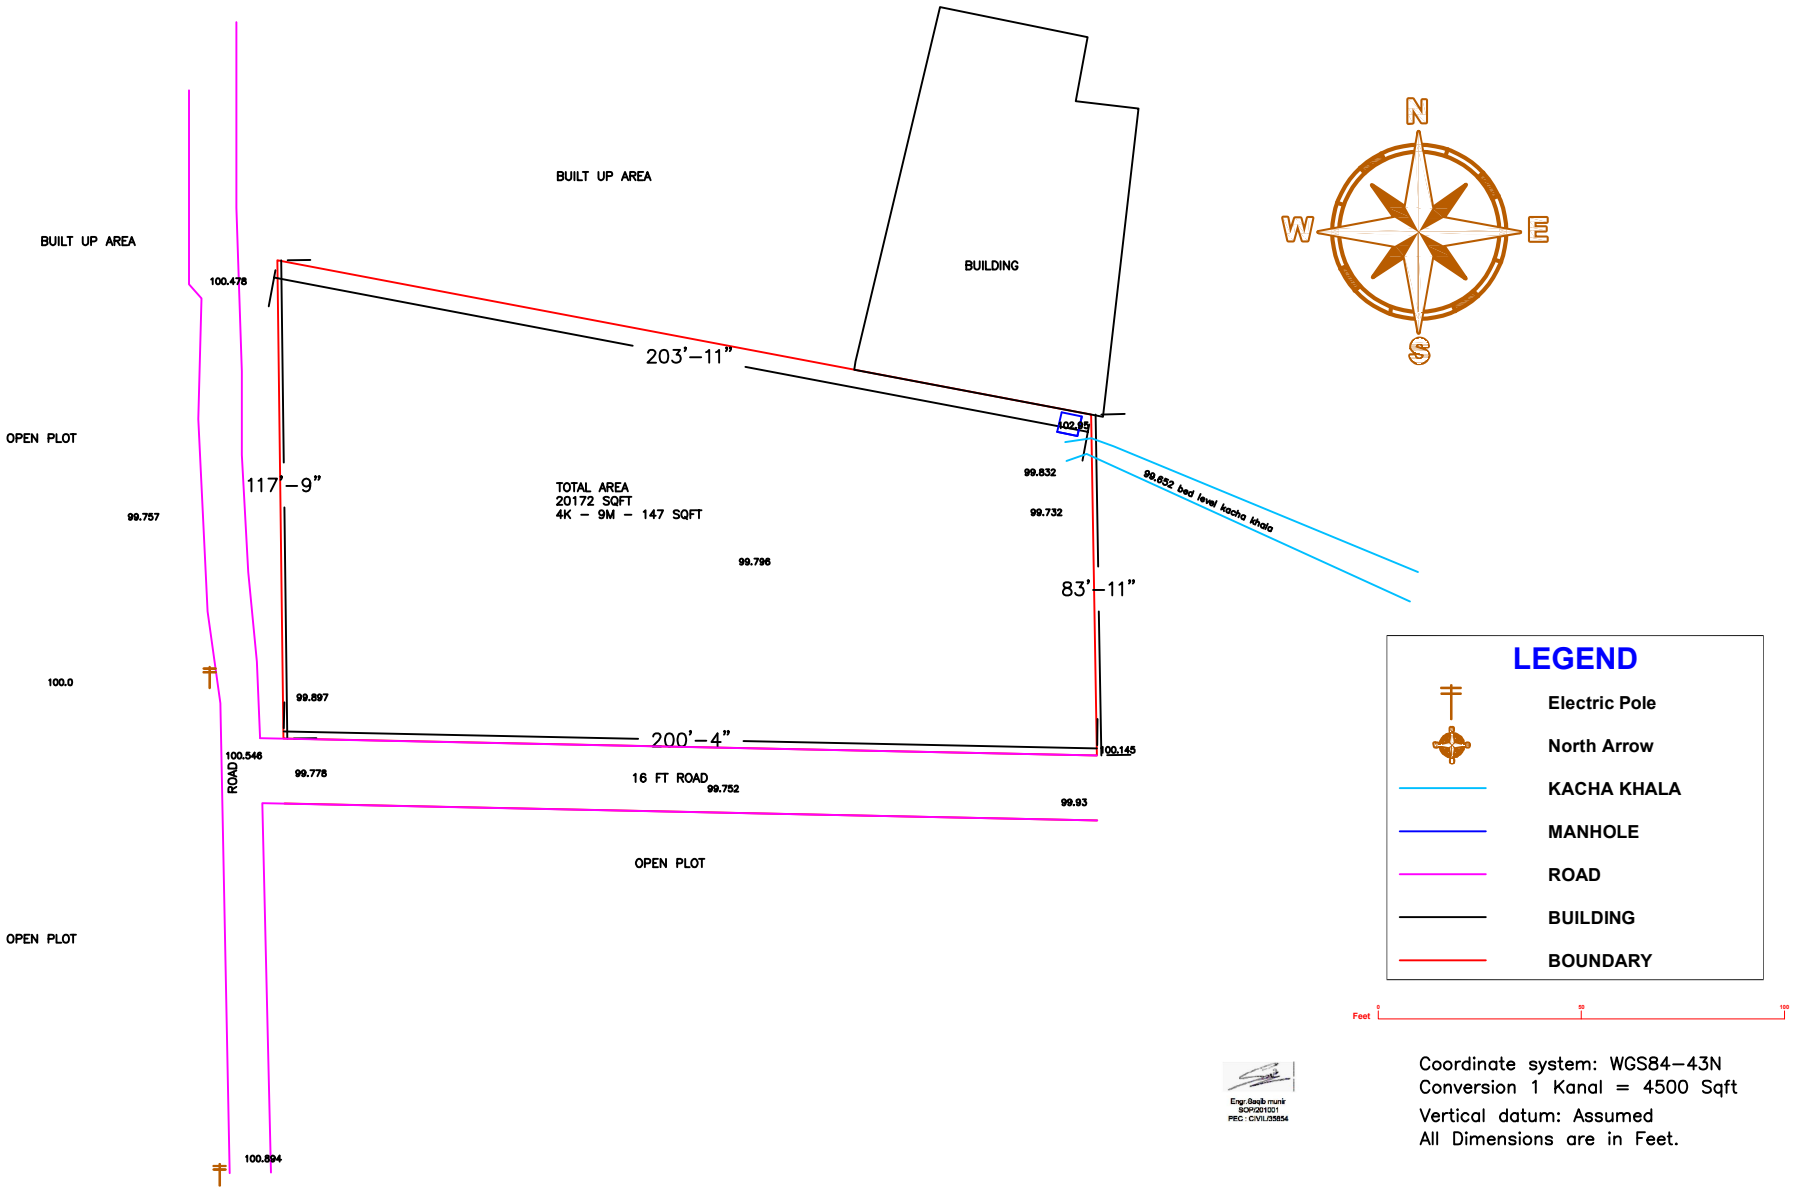


Eng: Beab munir
SOP/201001
PEC : CIVIL/35854

Coordinate system: WGS84–43N
Conversion 1 Kanal = 4500 Sqft
Vertical datum: Assumed
All Dimensions are in Feet.

TITLE:

TOPO SURVEY MAP MCPL Site # 1

SURVEYCONSULT
LAND & ENGINEERING SURVEY CONSULTANTS
769 A Block,
Sabzazar Scheme,
Multan Road Lahore
Phone Number
+92 321 4202202
Send Your Mail
surveyconsultlahore@gmail.com