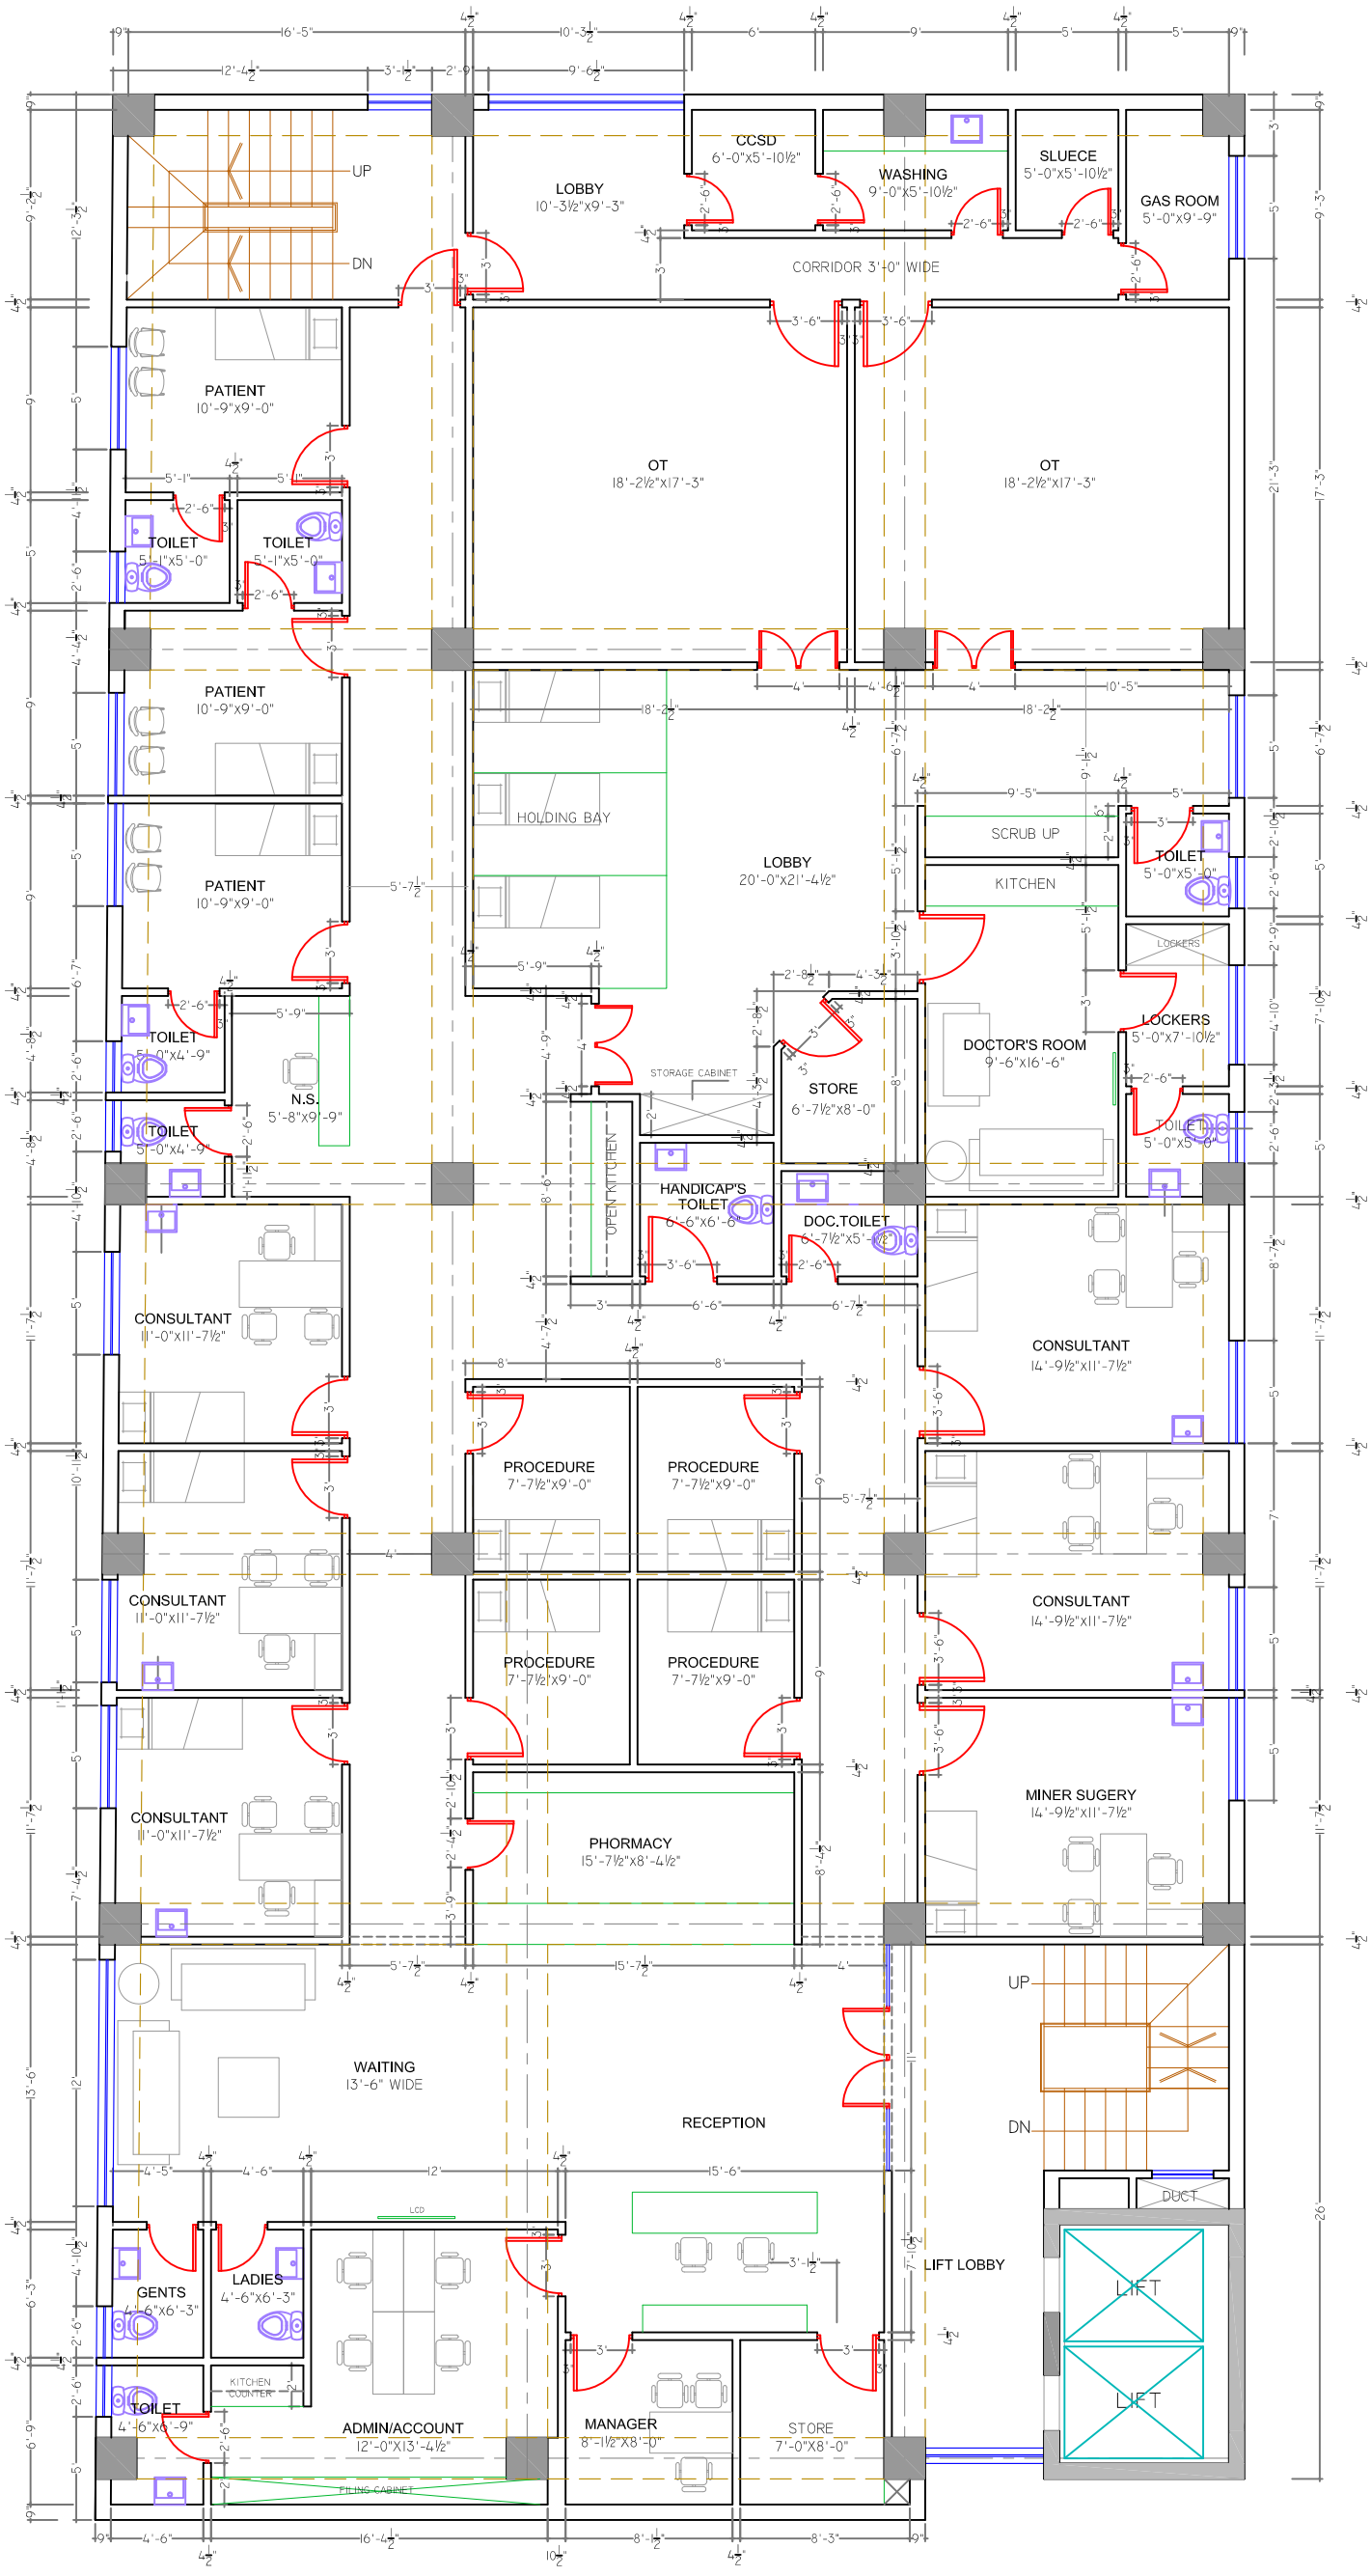


NOTE:-
WINDIW 'S HEIGHT AT 7'-0"
WINDIW 'S SILL AT 3'-0"
WINDIW 'S SILL OF TOILETS AT 4'-0"

PROJECT PROPOSED COMMERCIAL BUILDING FOR Dr. AHMED FARAZ ADDA PLOT, OFF RAIWIND ROAD, LAHORE	TITLE WORKING PLAN DRG. CLINIC	DRAWN: M.NASIR DATED: JANUARY (2024) SACLE: NTS CHECKED:	NORTH	YOUSAF ATHAR ASSOCIATES CONSULTING ARCHITECTS 35-36, 2nd FLOOR, GULBERG CENTRE, GULBERG, LAHORE CELL PHONE. 0333 4258303 email=yousafatharassociates@gmail.com