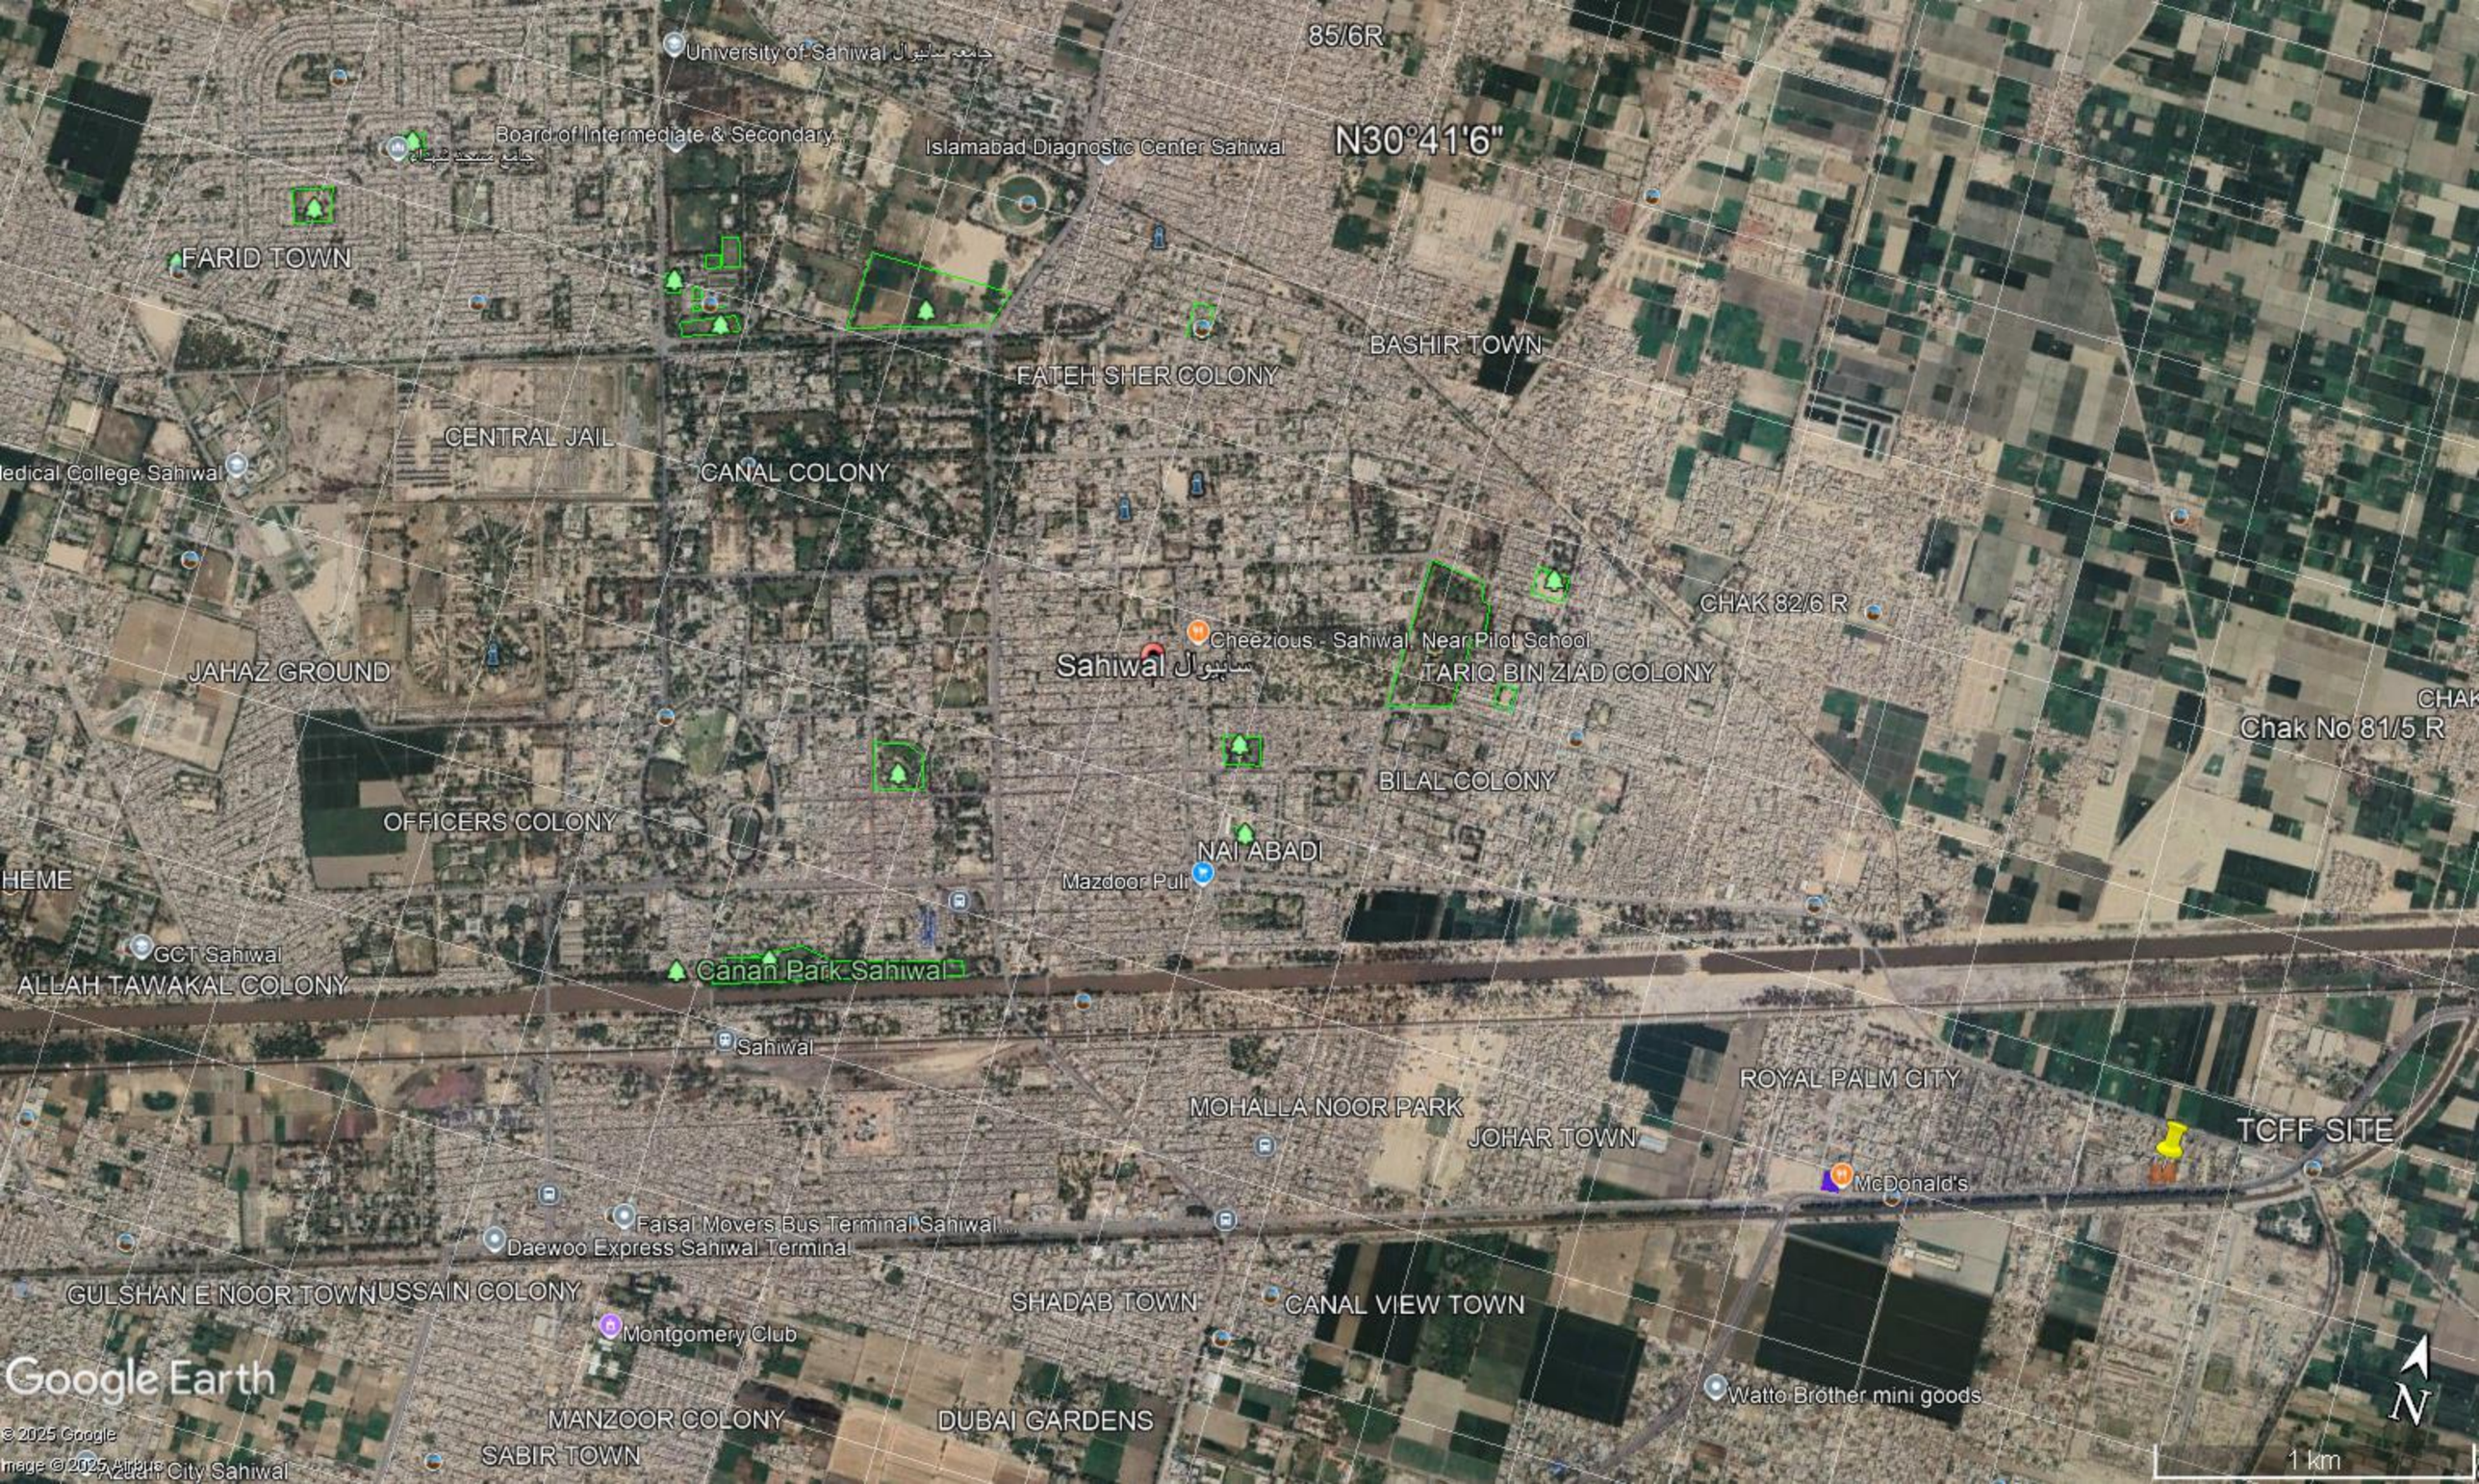
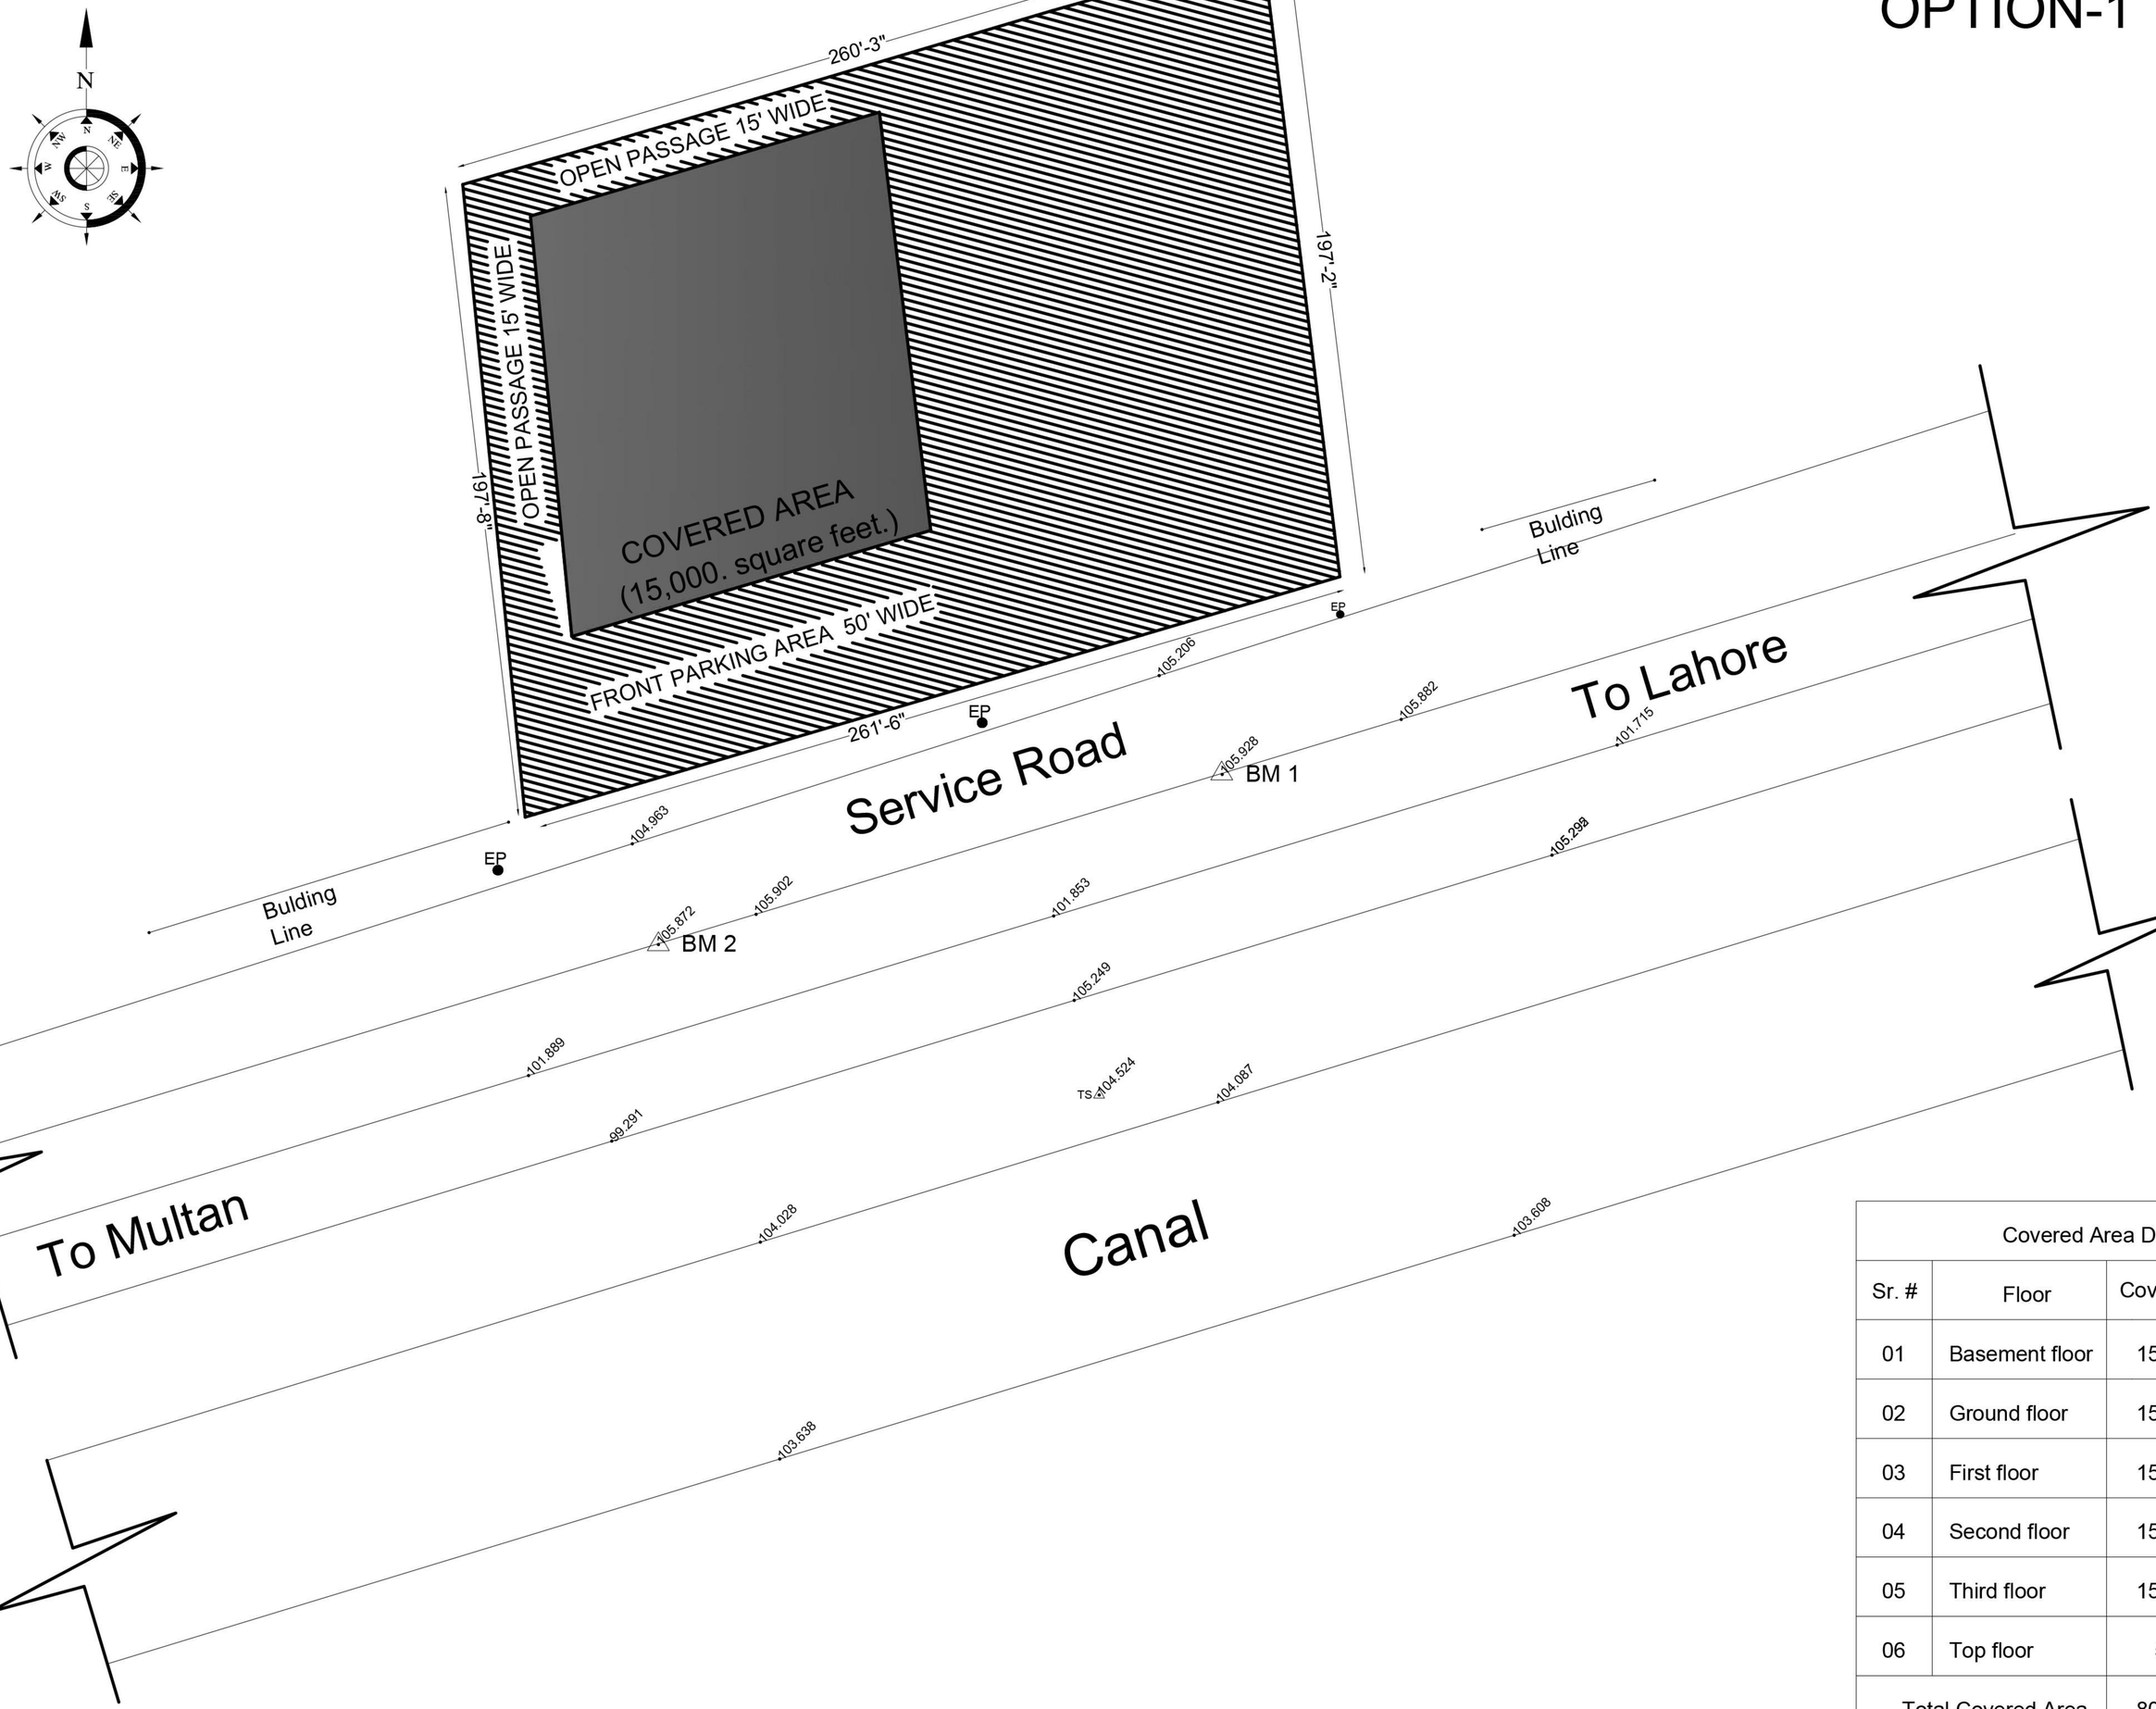

Jamia Masjid Muhammad Musa
Dar'ul Quran Markaz Khatam Un Nabiyyen...
Agrica Chemicals Warehouse Sahiwal
TCFF SITE
E 73°08'54.24"
Parvez Brother Deli-JW Warehouse
Ali Estate and Builders
اتفاق موٹر ورکشاپ
Google Earth
Image © 2025 Airbus
N
60 m

Masood Ahmad Hashmi's House
Desired Technologies
Truck Stand Sahiwal
Royal Palm City Sahiwal
موسی گروپ ٹرانسپورٹ کمپنی
Muller & Phipps PSO Sahiwal
Parvez Brother Deli JW Warehouse
E 73°08'28.32" N30°39'40.32"
Abdul Rehman Tikka Shop عبدالرحمن ٹکہ شاپ
NEW ITTEFAQ CARGO LINES PVT...
McDonald's
Azan Mall
E 73°08'54.24"
Society Office PGS
Google Earth
Image © 2025 Airbus
N
300 m


85/6R
N30°41'6"
University of Sahiwal جامعہ ساہیوال
Board of Intermediate & Secondary
Islamabad Diagnostic Center Sahiwal
FARID TOWN
FATEH SHER COLONY
BASHIR TOWN
CENTRAL JAIL
CANAL COLONY
Medical College Sahiwal
JAHAZ GROUND
Cheezious - Sahiwal, Near Pilot School
Sahiwal ساہیوال
TARIQ BIN ZIAD COLONY
CHAK 82/6 R
Chak No 81/5 R
OFFICERS COLONY
BILAL COLONY
NAI ABADI
Mazdoor Puli
GCT Sahiwal
ALLAH TAWAKAL COLONY
Canan Park Sahiwal
Sahiwal
ROYAL PALM CITY
MOHALLA NOOR PARK
JOHAR TOWN
TCFF SITE
McDonald's
Faisal Movers Bus Terminal Sahiwal
Daewoo Express Sahiwal Terminal
GULSHAN E NOOR TOWN
HUSSAIN COLONY
SHADAB TOWN
CANAL VIEW TOWN
Montgomery Club
Google Earth
© 2025 Google
Image © 2025 Airbus
Watto Brother mini goods
MANZOOR COLONY
DUBAI GARDENS
SABIR TOWN
Azadi City Sahiwal
N
1 km

OPTION-1



Covered Area Detail		
Sr. #	Floor	Covered Area
01	Basement floor	15,000.Sft
02	Ground floor	15,000.Sft
03	First floor	15,000.Sft
04	Second floor	15,000.Sft
05	Third floor	15,000.Sft
06	Top floor	5000.Sft
Total Covered Area		80,000.Sft