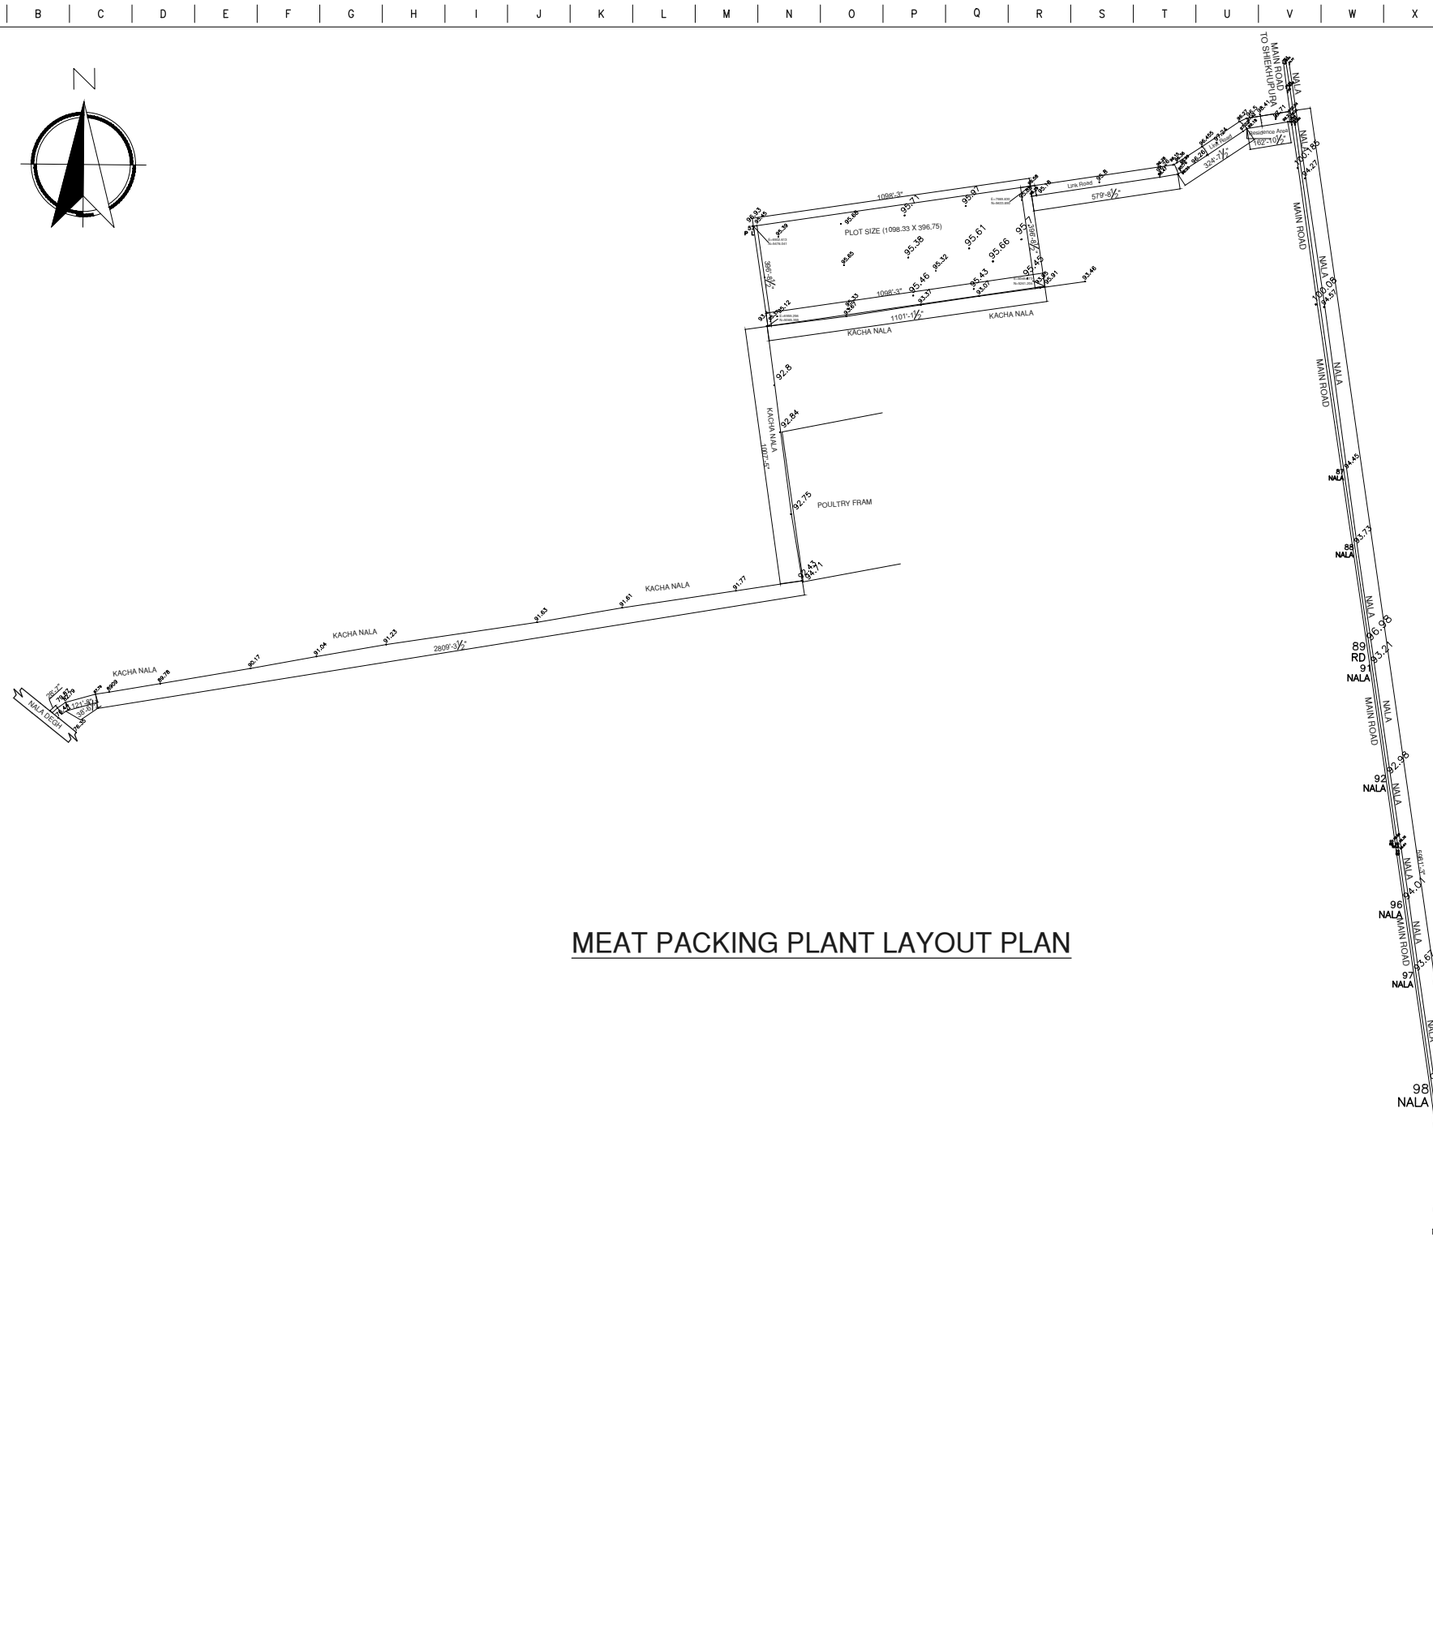


MEAT PACKING PLANT LAYOUT PLAN

NOTE:

1. PLOT SIZE (1098.33 X 396.75)
2. LINK ROAD SIZE IS 40'-0" WIDE & L=1070'-0"
3. FRONT SIDE NALA IS CLOSED AT DIFFERENT POINTS AND NOT PREFERRED FOR DRAIN.
4. BACK SIDE NALA IS TO BE CONNECTED TO NALA DEGH (PREFERRED).
5. PLOT E.G.L LEVEL IS 95.32.
6. LINK ROAD E.G.L LEVEL IS 97.24.
7. MAIN ROAD LEVEL IS 100.02.
8. BACK SIDE NALA E.G.L START FORM (92.8 TO 76.44) L=2998.
9. DIMENSION ARE IN FEET.

REV.	DESCRIPTION	DATE	BY	CHK'D	APP'D
4					
3					
2					
1					


REVISIONS

PROJECT CODE NUMBER: E-10459

ELITE ENGINEERING (Pvt.) LIMITED
113 L1, VALENCIA TOWN, LAHORE.
Engineering, Procurement & Construction

DESIGNED: MK	CLIENT: GO AGRO
DRAWN: MS	PROJECT: MEAT PACKING PLANT SHIEKHUPURA
CHECKED: AS	TITLE: MEAT PACKING PLANT LAYOUT PLAN
APPROVED:	
SCALE: N.T.S.	
SHEET SIZE: A3	DRAWING NO. 10459-MEAT PLANT-A-01
DATE: 17-10-2025	SHEET NO 1 OF 2
	REV. 0

THIS DRAWING IS PRIVATE AND CONFIDENTIAL AND IS PROPERTY OF ELITE ENGINEERING(PVT.)LTD. IT MUST NOT BE COPIED OR LENT WITHOUT THE CONSENT OF ELITE ENGINEERING(PVT.)LTD. AND MUST BE RETURNED WITH THE TENDER AND/OR ON COMPLETION OF THE ORDER TO ELITE ENGINEERING(PVT.)LTD.113-L1 VALANCIA TOWN LAHORE. PAKISTAN

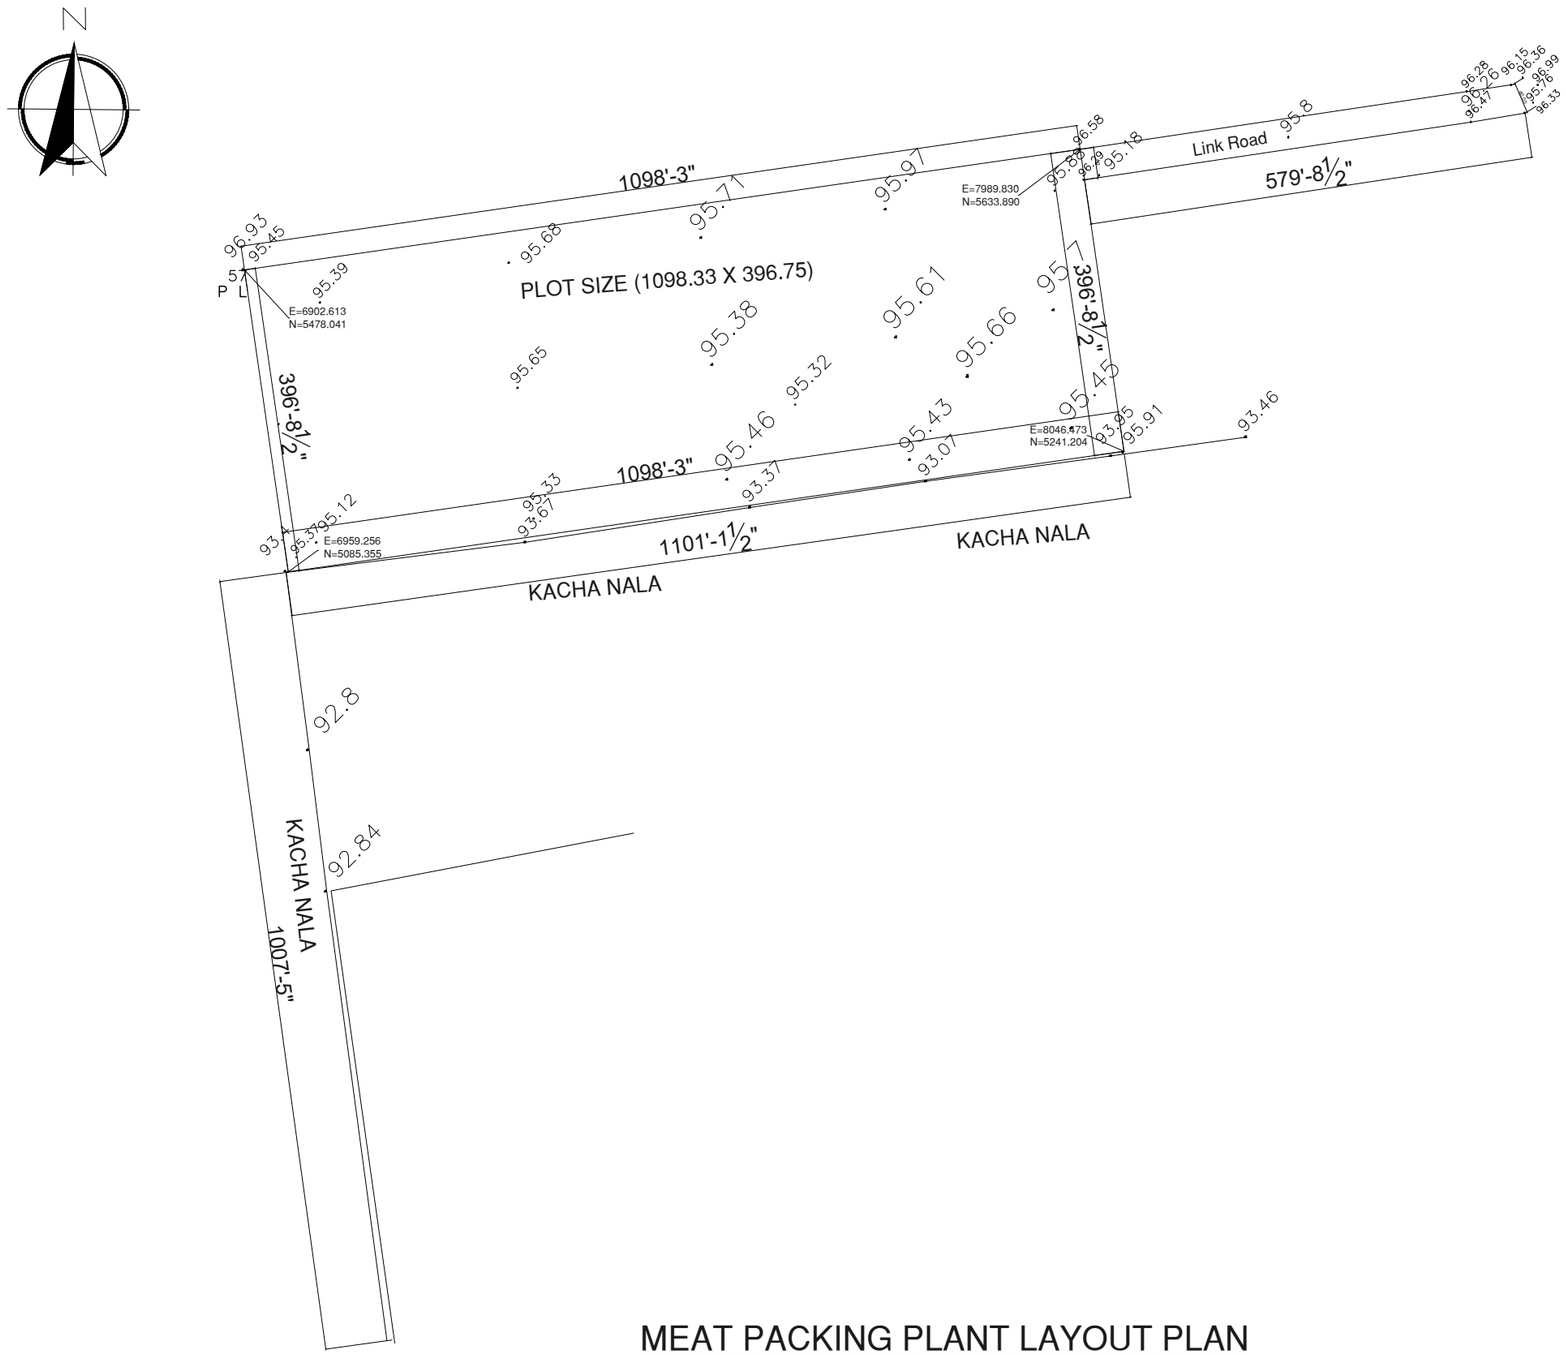

MEAT PACKING PLANT LAYOUT PLAN

NOTE:

1. PLOT SIZE (1098.33 X 396.75)
2. LINK ROAD SIZE IS 40'-0" WIDE & L=1070'-0"
3. FRONT SIDE NALA IS CLOSED AT DIFFERENT POINTS AND NOT PREFERRED FOR DRAIN.
4. BACK SIDE NALA IS TO BE CONNECTED TO NALA DEGH (PREFERRED).
5. PLOT E.G.L LEVEL IS 95.32.
6. LINK ROAD E.G.L LEVEL IS 97.24.
7. MAIN ROAD LEVEL IS 100.02.
8. BACK SIDE NALA E.G.L START FORM (92.8 TO 76.44) L=2998.
9. DIMENSION ARE IN FEET.

REV.	DESCRIPTION	DATE	BY	CHK'D	APP'D
4					
3					
2					
1					


REVISIONS

PROJECT CODE NUMBER: E-10459

ELITE ENGINEERING (Pvt.) LIMITED
113 L1, VALENCIA TOWN, LAHORE.
Engineering, Procurement & Construction

DESIGNED: MK	CLIENT: GO AGRO
DRAWN: MS	PROJECT: MEAT PACKING PLANT SHIEKHUPURA
CHECKED: AS	TITLE: MEAT PACKING PLANT LAYOUT PLAN
APPROVED:	
SCALE: N.T.S.	
SHEET SIZE: A3	DRAWING NO. 10459-MEAT PLANT-A-02 / SHEET NO 2 OF 2 / REV. 0
DATE: 17-10-2025	

THIS DRAWING IS PRIVATE AND CONFIDENTIAL AND IS PROPERTY OF ELITE ENGINEERING(PVT.)LTD. IT MUST NOT BE COPIED OR LENT WITHOUT THE CONSENT OF ELITE ENGINEERING(PVT.)LTD. AND MUST BE RETURNED WITH THE TENDER AND/OR ON COMPLETION OF THE ORDER TO ELITE ENGINEERING(PVT.)LTD.113-L1 VALANCIA TOWN LAHORE. PAKISTAN

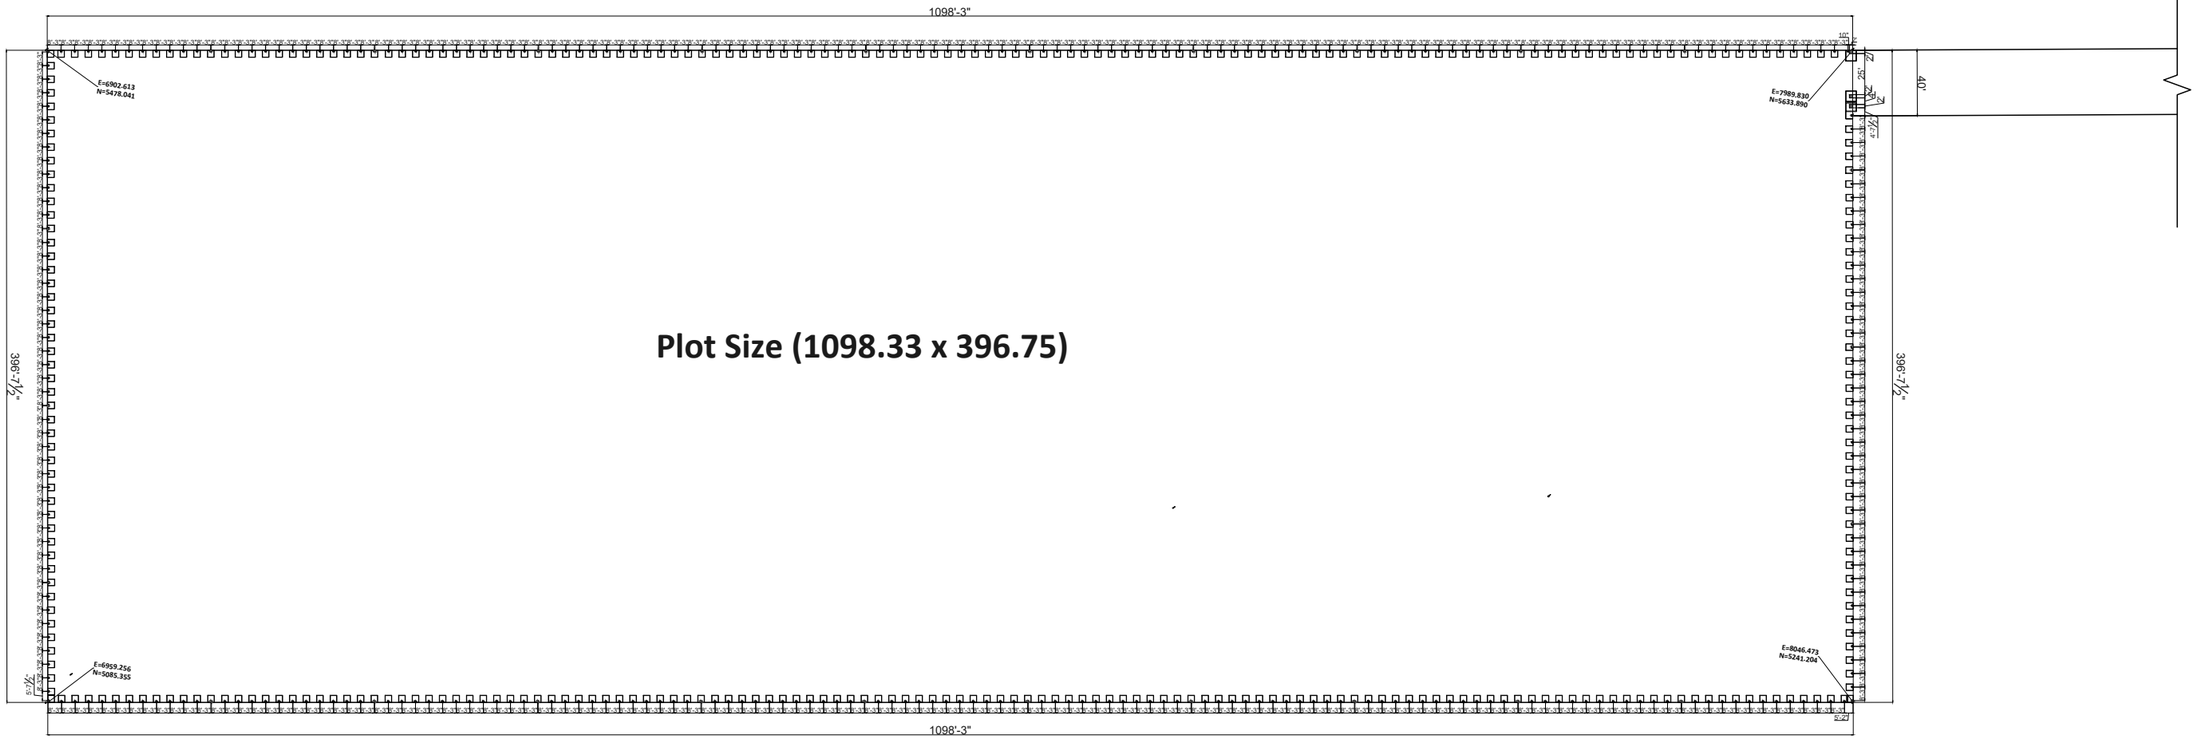

Plot Size (1098.33 x 396.75)

BOUNDARY WALL LAYOUT PLAN

REV.	DESCRIPTION	DATE	BY	CHK'D	APP'D
4					
3					
2					
1					

REVISIONS

PROJECT CODE NUMBER: E-10459


DESIGNED:	AC
DRAWN:	MS
CHECKED:	FM
APPROVED:	
SCALE:	N.T.S.
SHEET SIZE:	A3
DATE:	01-12-2025

CLIENT: GO AGRO


PROJECT: MEAT PACKING PLANT SHIEKHUPURA

TITLE: BOUNDARY WALL LAYOUT PLAN


DRAWING NO.	SHEET NO	REV.
10459-BOUNDARY WALL-L-01	1 OF 3	0

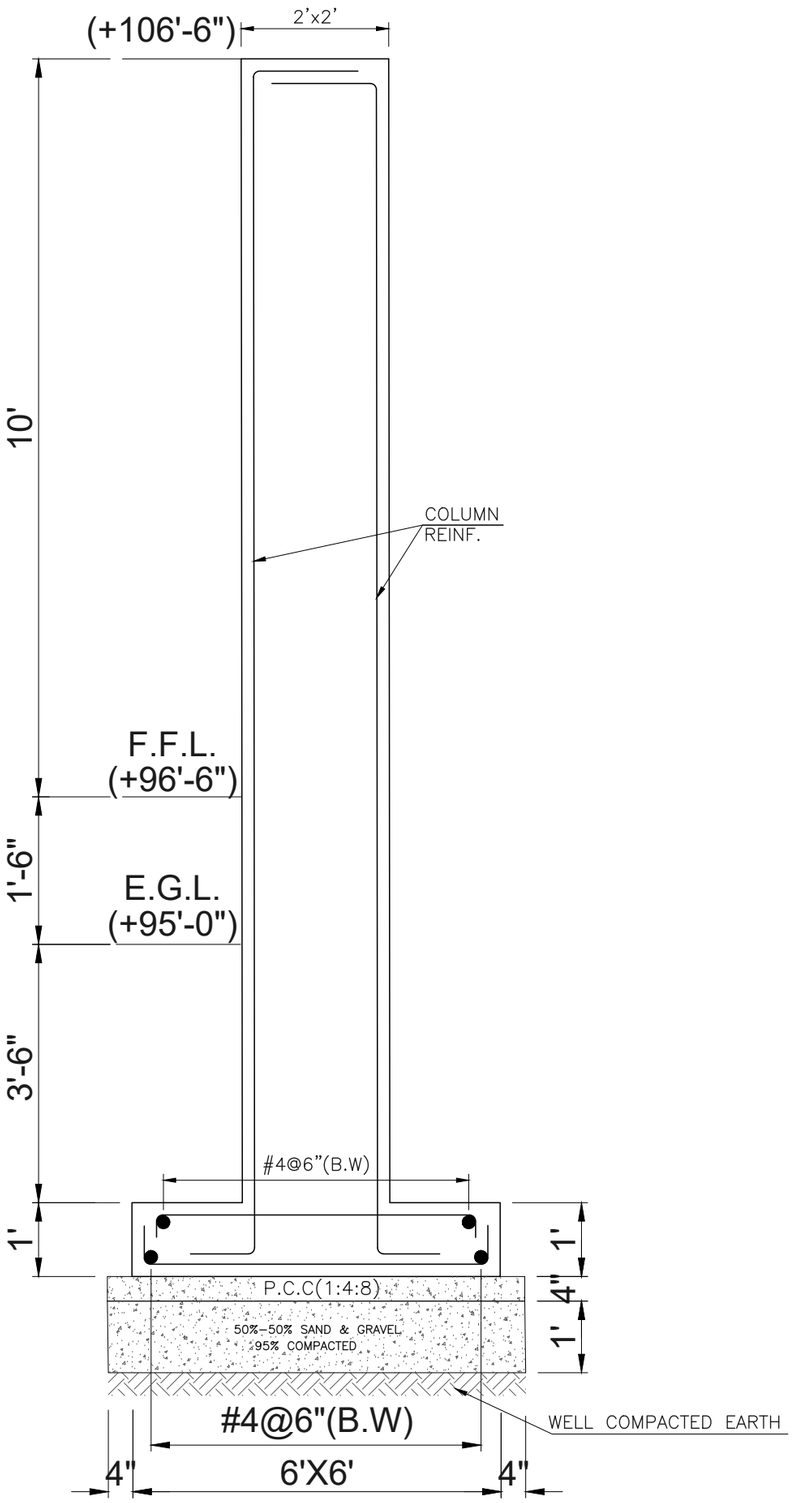


SECTION 1-1

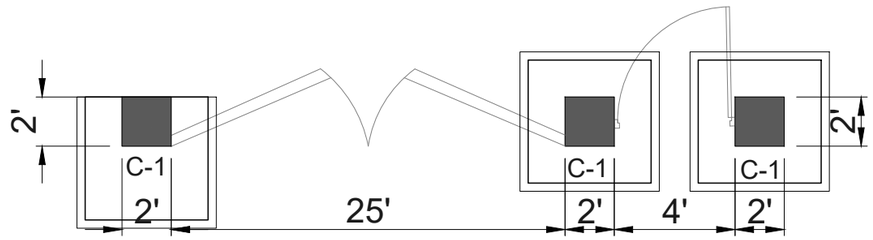

MAIN GATE PLAN

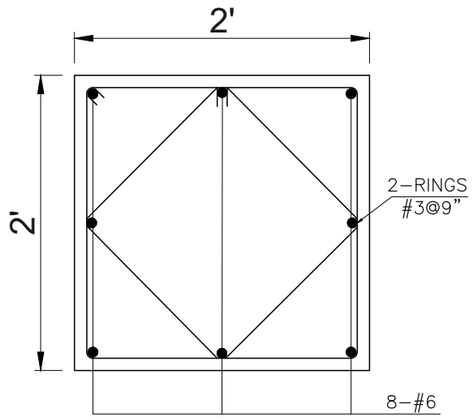

COLUMN C-1

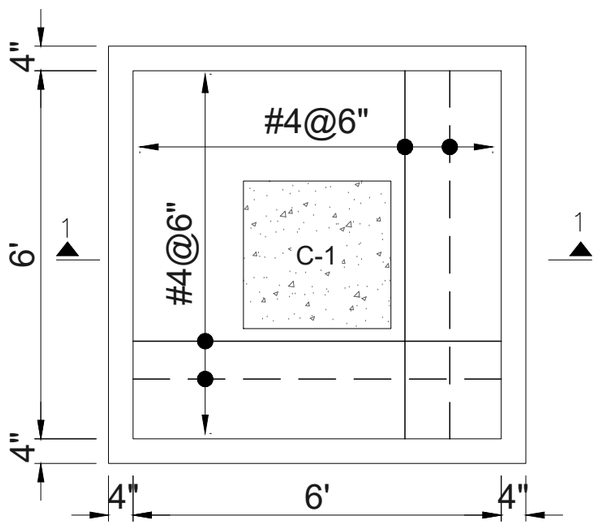

C-1 FOOTING PLAN

REV.	DESCRIPTION	DATE	BY	CHK'D	APP'D
4					
3					
2					
1					

REVISIONS

PROJECT CODE NUMBER: E-10459


DESIGNED:	AC
DRAWN:	MS
CHECKED:	FM
APPROVED:	
SCALE:	N.T.S.
SHEET SIZE:	A3
DATE:	01-12-2025

CLIENT: GO AGRO


PROJECT: MEAT PACKING PLANT SHIEKHUPURA

TITLE: MAIN GATE COLUMNS FOOTING DETAIL


DRAWING NO.	SHEET NO	REV.
10459-MAIN GATE-L-02	2 OF 3	0

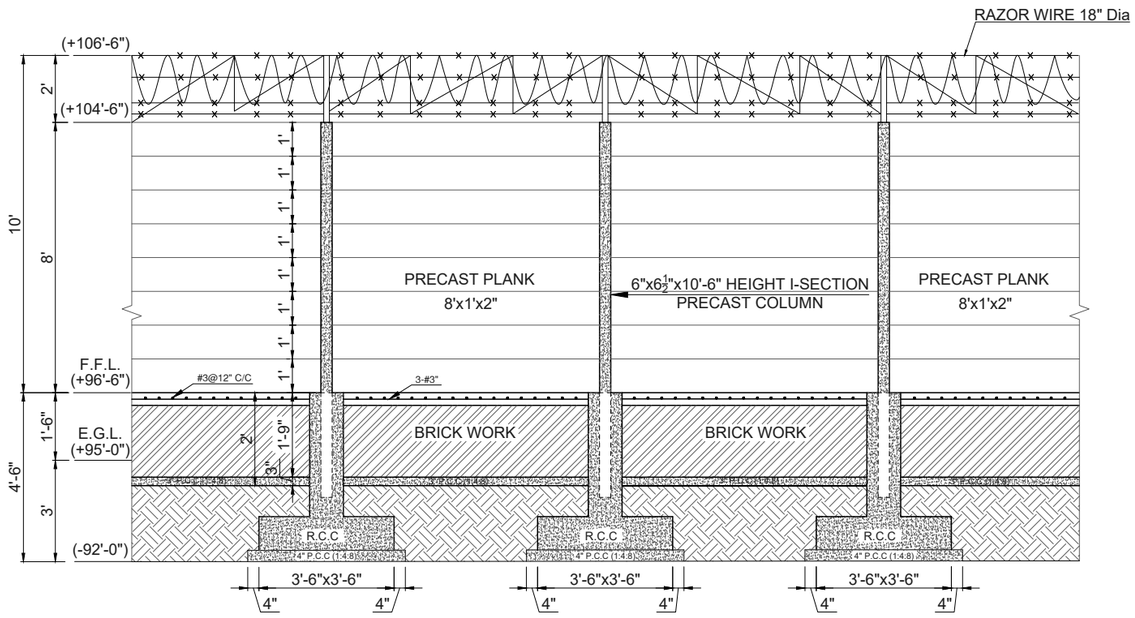

BOUNDARY WALL TYPICAL ELEVATION OF PART PLAN

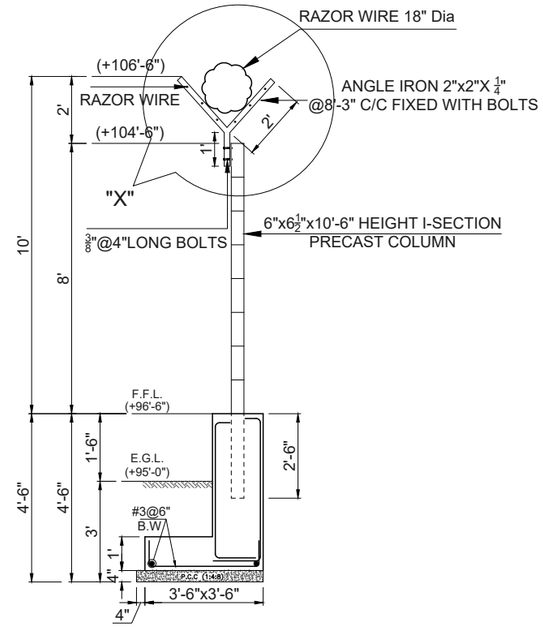


SECTION A'-A'

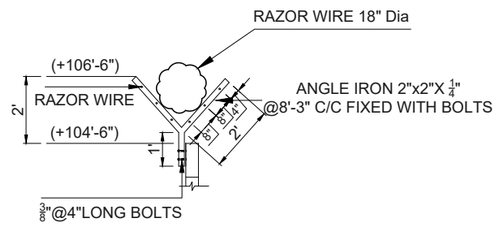


DETAIL "X"

LEGEND:


1. EXPANSION JOINTS AT EVERY 100'-0"
2. FOUNDATION P.C.C 1:4:8 1500 PSI
3. FOUNDATION R.C.C 1:2:4 3750 PSI
4. FOUNDATION STEEL #3@6"
5. 6"x61/2"x10'-6" HEIGHT I-SECTION PRECAST COLUMN 6000 PSI
6. PRECAST PLANK 8'x1'x2" 3800 PSI
7. ANGLE IRON 1½"x1½" SIZE DUALLY PAINTED
8. RAZOR WIRE 18" Dia

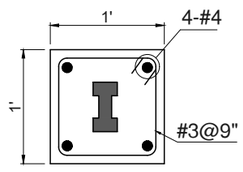


COLUMN C-1

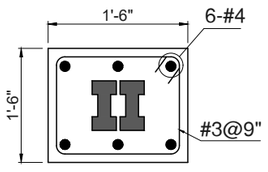


COLUMN C-2

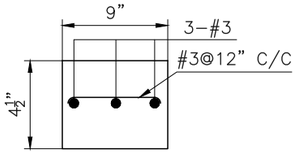


PLINTH BEAM

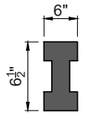


PC.B.W COLUMN

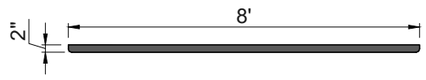

PC.B.W PLANK

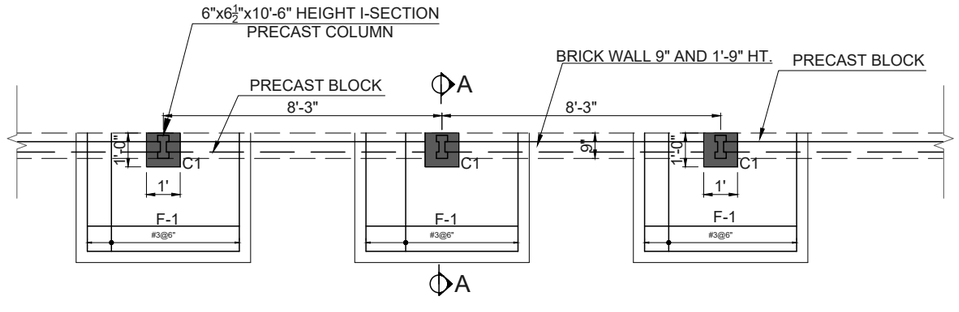

TYPICAL FOUNDATION PART PLAN

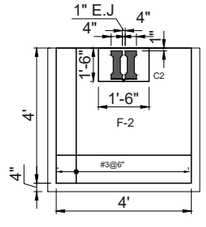

F-2 PLAN

AT EXPANSION JOINTS

REV.	DESCRIPTION	DATE	BY	CHK'D	APP'D
4					
3					
2					
1					

REVISIONS

PROJECT CODE NUMBER: E-10459


AC	
DRAWN: MS	
CHECKED: FM	
APPROVED:	
SCALE: N.T.S.	
SHEET SIZE: A3	
DATE: 01-12-2025	

CLIENT: GO AGRO

PROJECT: MEAT PACKING PLANT SHIEKHUPURA

TITLE: BOUNDARY WALL PLAN AND SECTIONS

DRAWING NO.	SHEET NO	REV.
10459-BOUNDARY WALL-L-03	3 OF 3	0

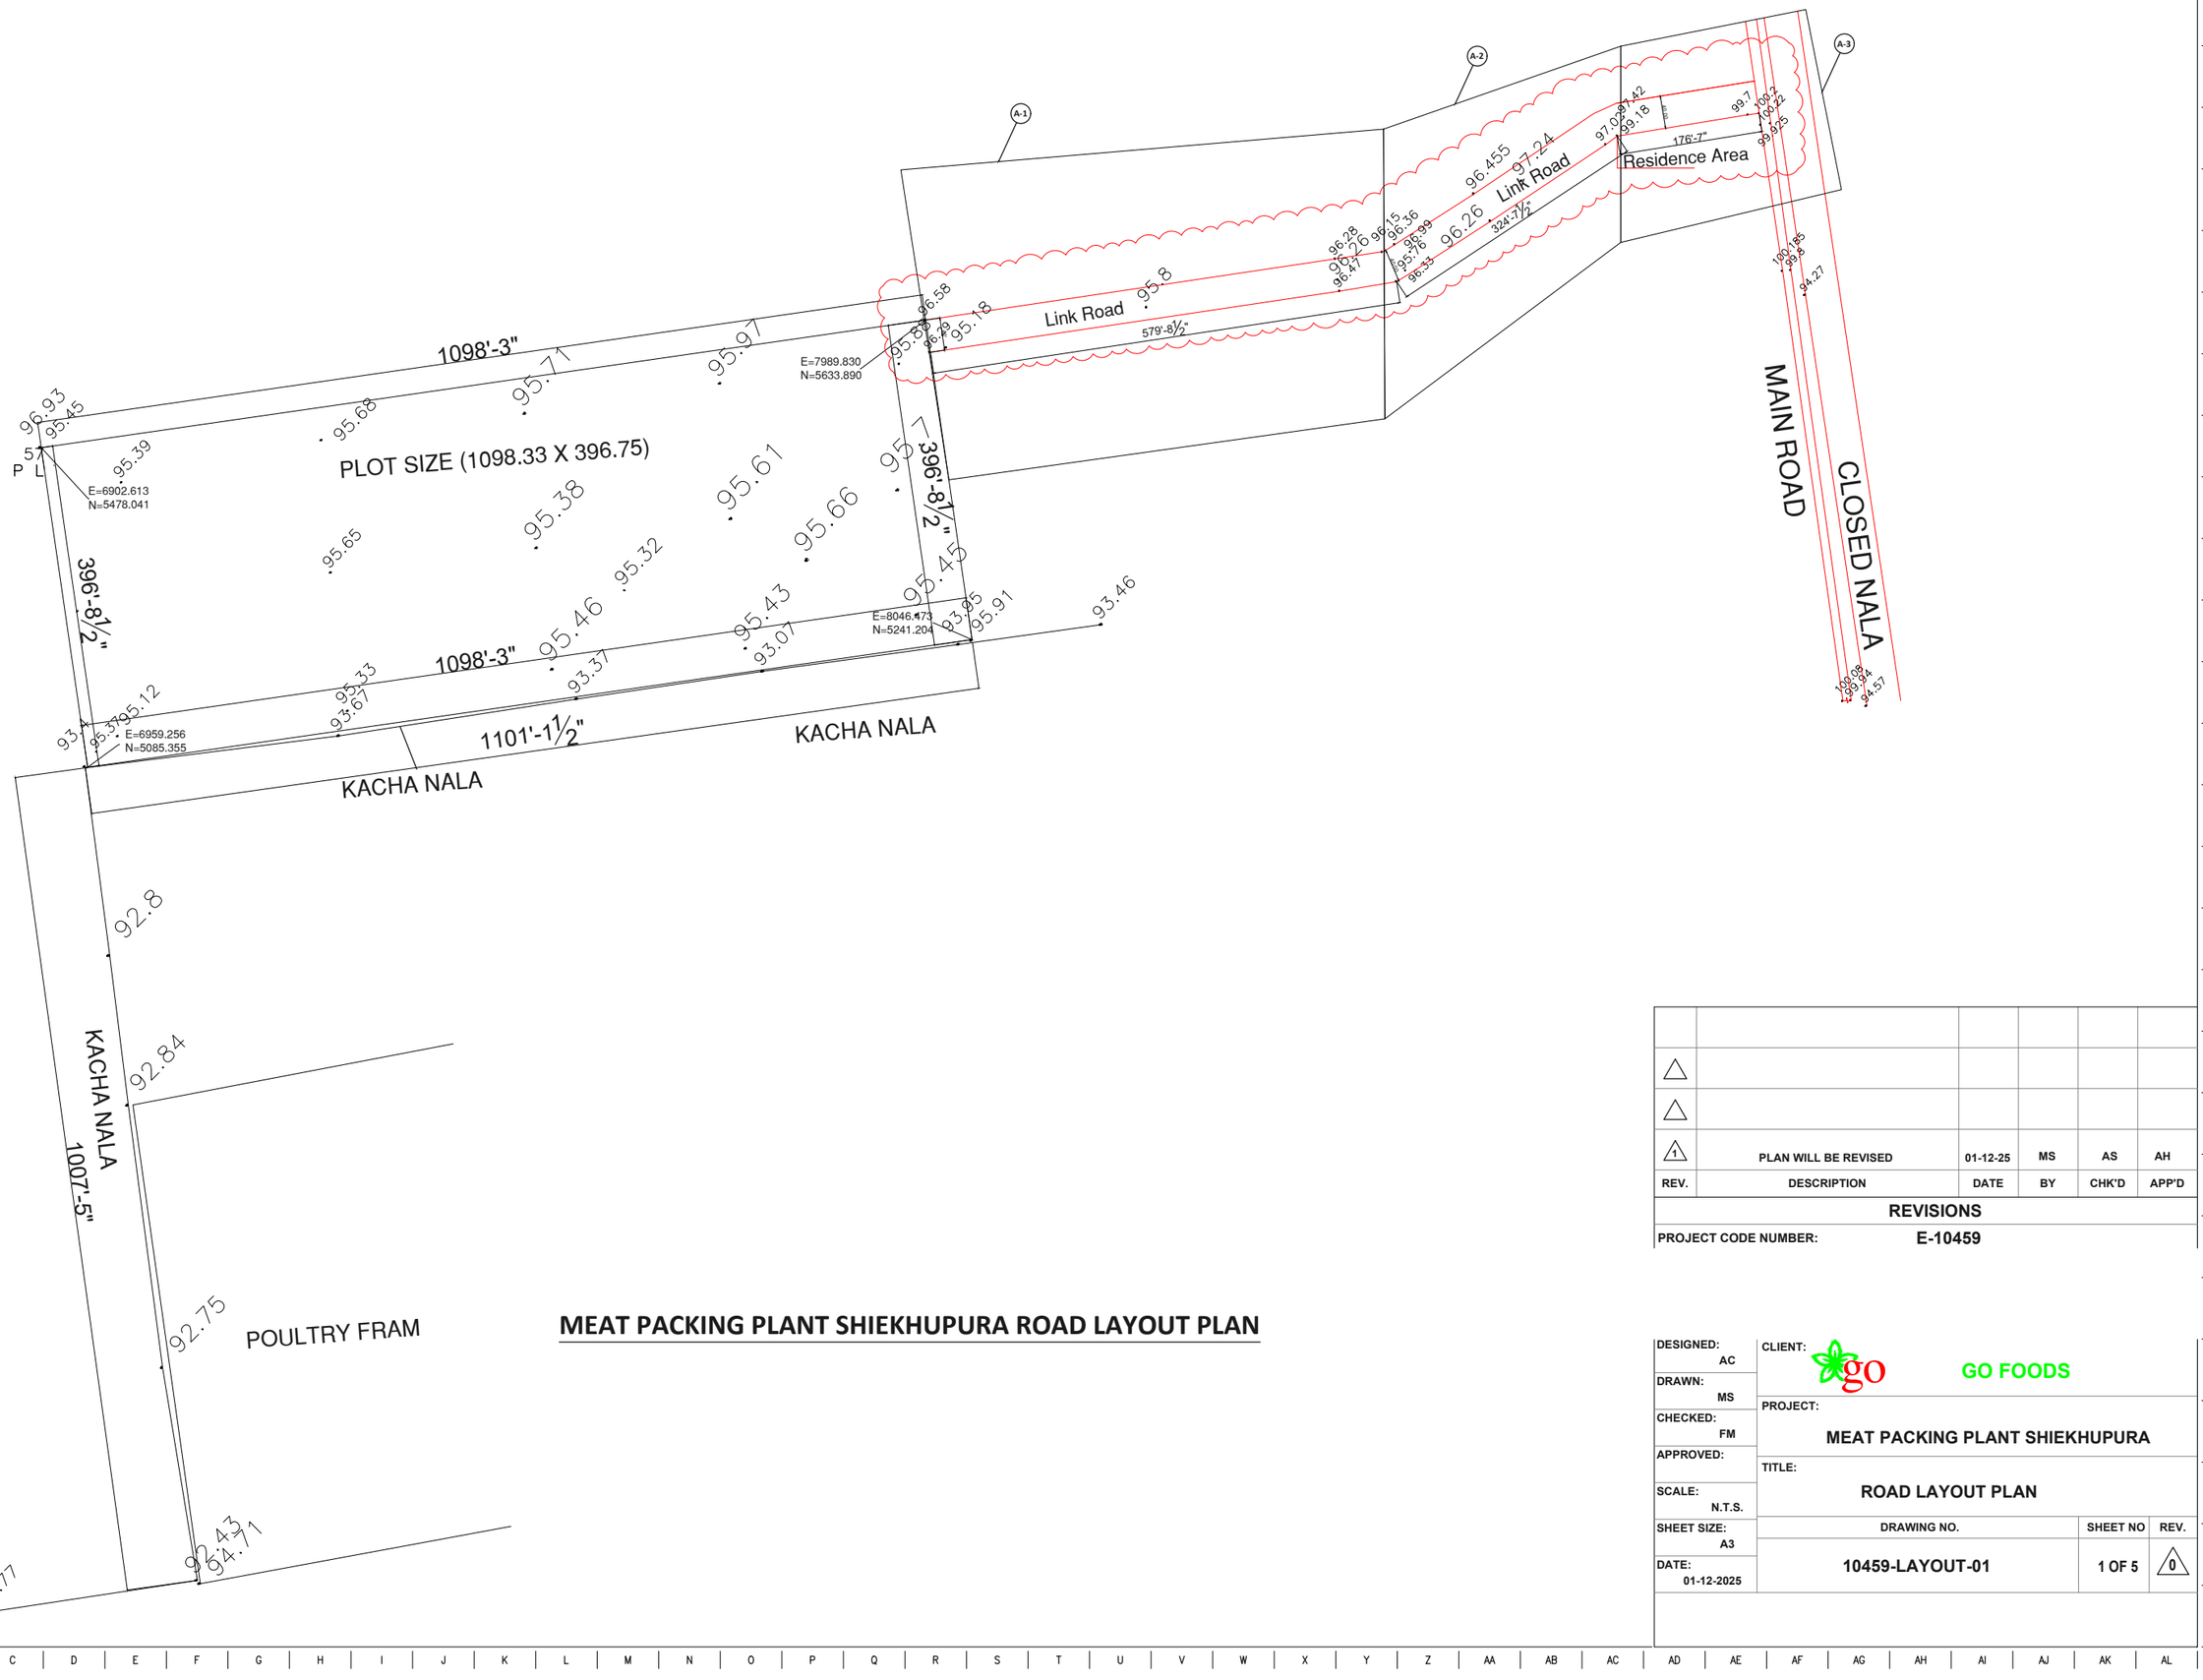

MEAT PACKING PLANT SHIEKHUPURA ROAD LAYOUT PLAN

REV.	DESCRIPTION	DATE	BY	CHK'D	APP'D
△					
△					
1	PLAN WILL BE REVISED	01-12-25	MS	AS	AH

REVISIONS

PROJECT CODE NUMBER: **E-10459**


DESIGNED:	AC
DRAWN:	MS
CHECKED:	FM
APPROVED:	
SCALE:	N.T.S.
SHEET SIZE:	A3
DATE:	01-12-2025

CLIENT: GO FOODS


PROJECT: MEAT PACKING PLANT SHIEKHUPURA

TITLE: ROAD LAYOUT PLAN

DRAWING NO.	SHEET NO	REV.
10459-LAYOUT-01	1 OF 5	0

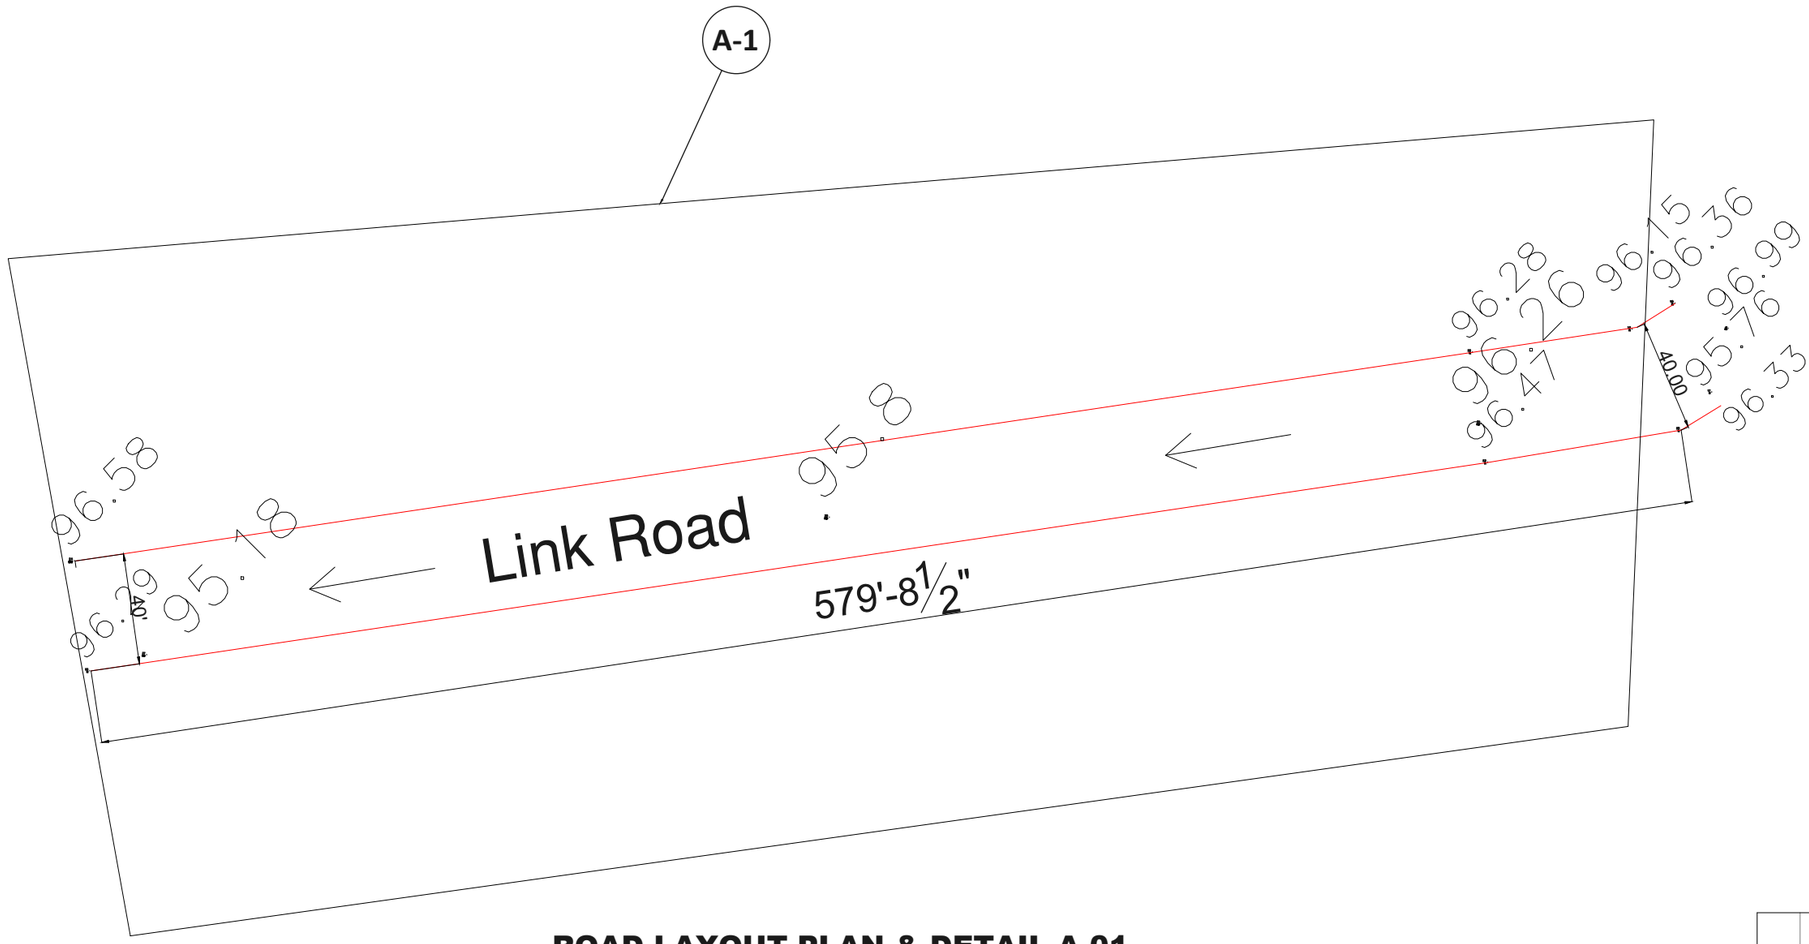

ROAD LAYOUT PLAN & DETAIL A-01

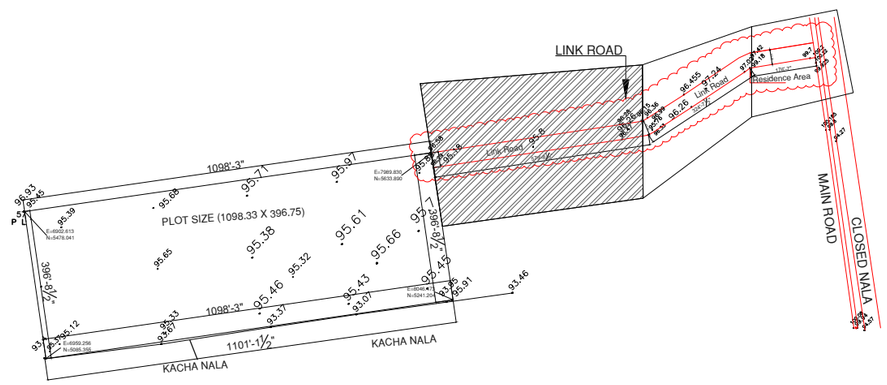

ROAD LAYOUT KEY PLAN

REV.	DESCRIPTION	DATE	BY	CHK'D	APP'D
△					
△					
1	PLAN WILL BE REVISED	01-12-25	MS	AS	AH

REVISIONS

PROJECT CODE NUMBER: E-10477


AC	
DRAWN:	MS
CHECKED:	FM
APPROVED:	
SCALE:	N.T.S.
SHEET SIZE:	A3
DATE:	01-12-2025

CLIENT: GO FOODS


PROJECT: MEAT PACKING PLANT SHIEKHUPURA

TITLE: ROAD LAYOUT PLAN & DETAIL A-01

DRAWING NO.	SHEET NO	REV.
10477-LAYOUT-L-02	2 OF 5	△0

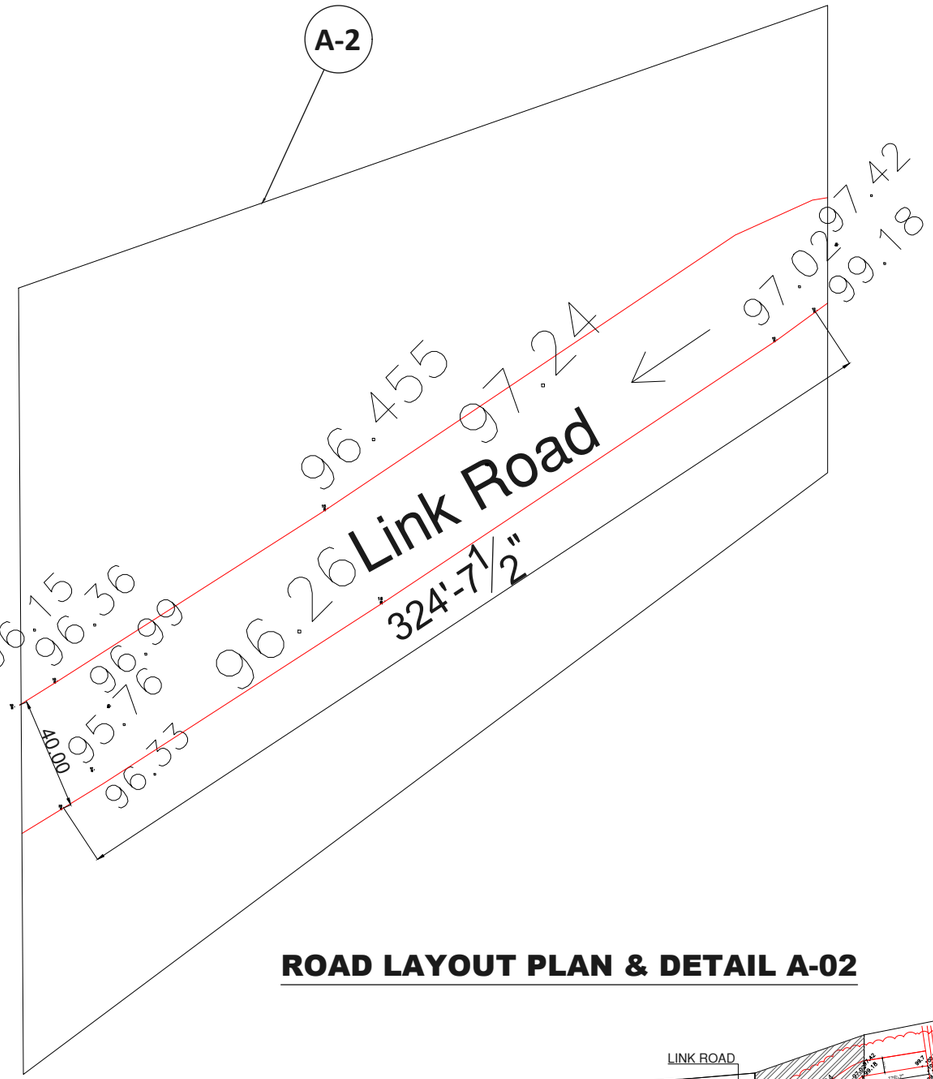

ROAD LAYOUT PLAN & DETAIL A-02

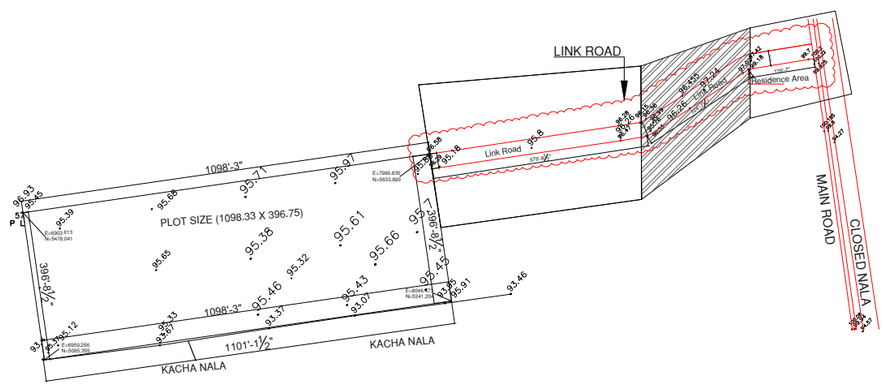

ROAD LAYOUT KEY PLAN

REV.	DESCRIPTION	DATE	BY	CHK'D	APP'D
1	PLAN WILL BE REVISED	01-12-25	MS	AS	AH

REVISIONS

PROJECT CODE NUMBER: **E-10477**


DESIGNED:	AC
DRAWN:	MS
CHECKED:	FM
APPROVED:	
SCALE:	N.T.S.
SHEET SIZE:	A3
DATE:	01-12-2025

CLIENT: GO FOODS


PROJECT: MEAT PACKING PLANT SHIEKHUPURA

TITLE: ROAD LAYOUT PLAN & DETAIL A-02

DRAWING NO.	SHEET NO	REV.
10477-LAYOUT-L-03	3 OF 5	0

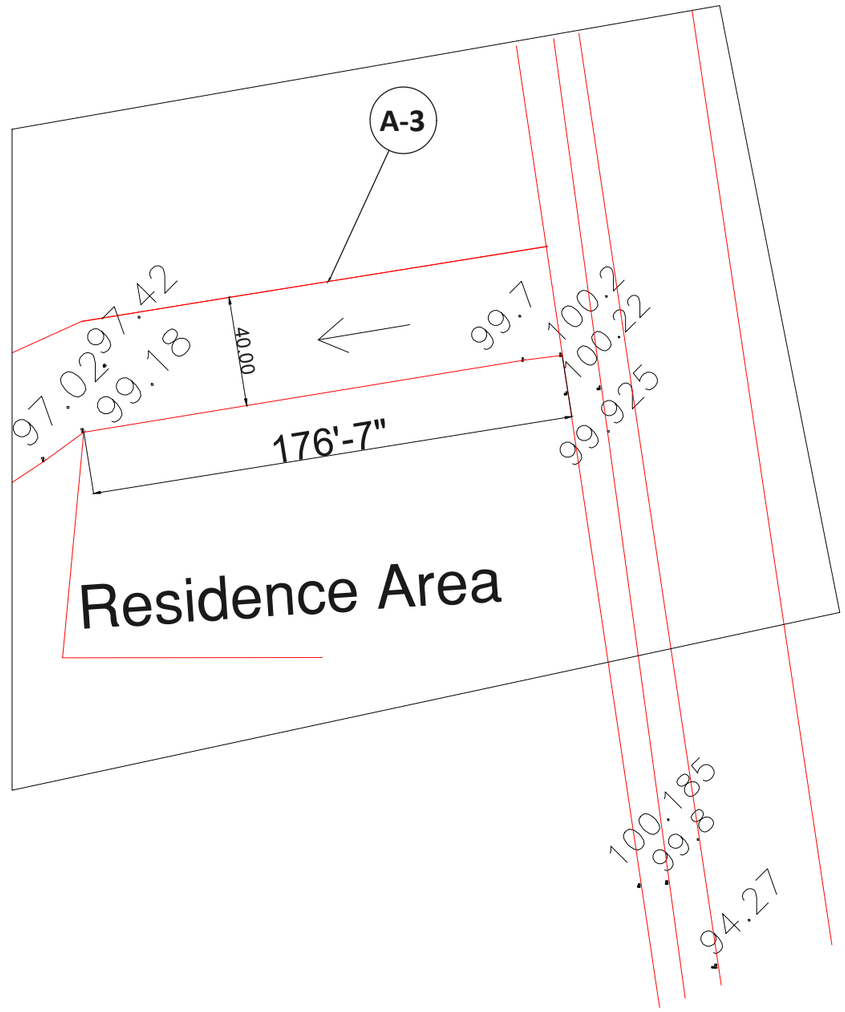

ROAD LAYOUT PLAN & DETAIL A-03

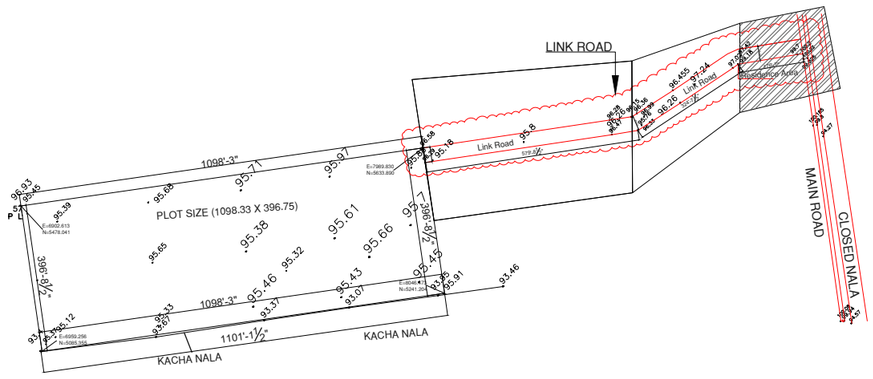

ROAD LAYOUT KEY PLAN

REV.	DESCRIPTION	DATE	BY	CHK'D	APP'D
1	PLAN WILL BE REVISED	01-12-25	MS	AS	AH

REVISIONS

PROJECT CODE NUMBER: **E-10477**


DESIGNED:	AC
DRAWN:	MS
CHECKED:	FM
APPROVED:	
SCALE:	N.T.S.
SHEET SIZE:	A3
DATE:	01-12-2025

CLIENT: GO FOODS

PROJECT: MEAT PACKING PLANT SHIEKHUPURA

TITLE: ROAD LAYOUT PLAN & DETAIL A-03

DRAWING NO.	SHEET NO	REV.
10477-LAYOUT-L-04	4 OF 5	0

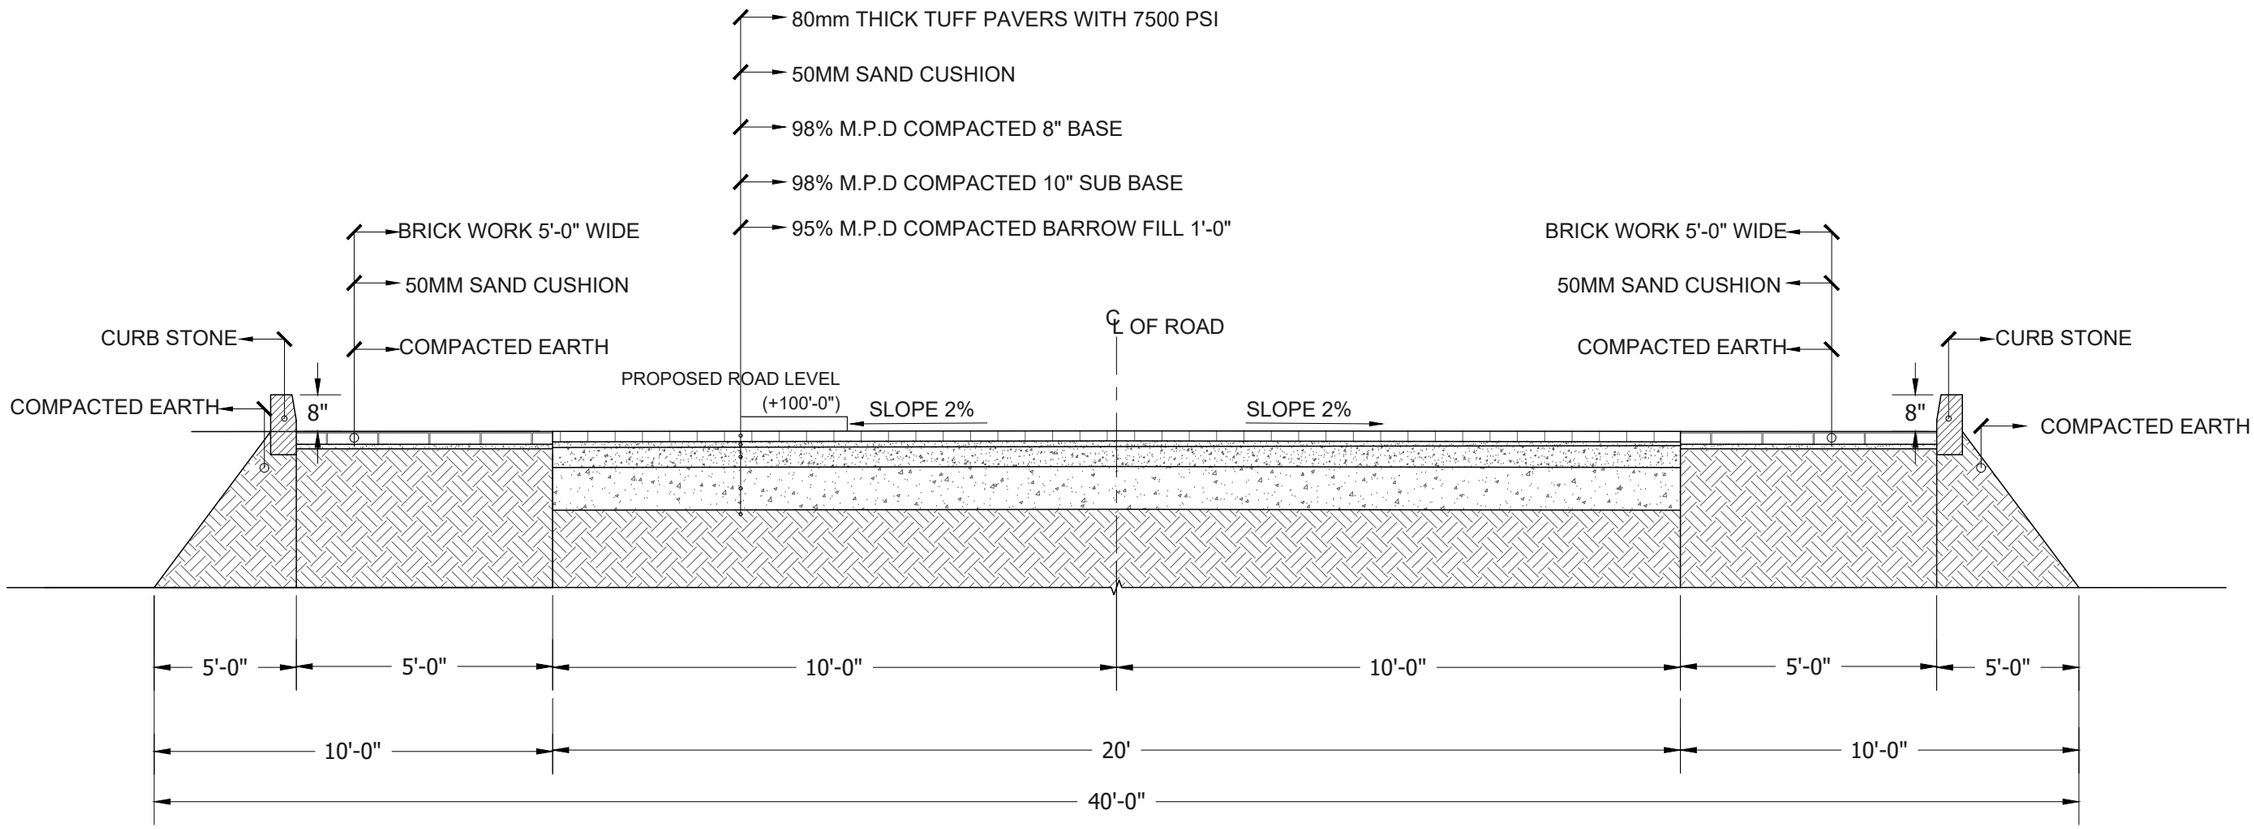

SECTION OF 40'-0" WIDE ROAD

REV.	DESCRIPTION	DATE	BY	CHK'D	APP'D
△					
△					
△1	PLAN WILL BE REVISED	01-12-25	MS	AS	AH

REVISIONS

PROJECT CODE NUMBER: **E-10459**


	AC
DRAWN:	MS
CHECKED:	FM
APPROVED:	
SCALE:	N.T.S.
SHEET SIZE:	A3
DATE:	01-12-2025

CLIENT: GO FOODS

PROJECT: **MEAT PACKING PLANT SHIEKHUPURA**

TITLE: **TYPICAL ROAD SECTION & DETAILS**

DRAWING NO.	SHEET NO	REV.
10459-LAYOUT-05	5 OF 5	△1

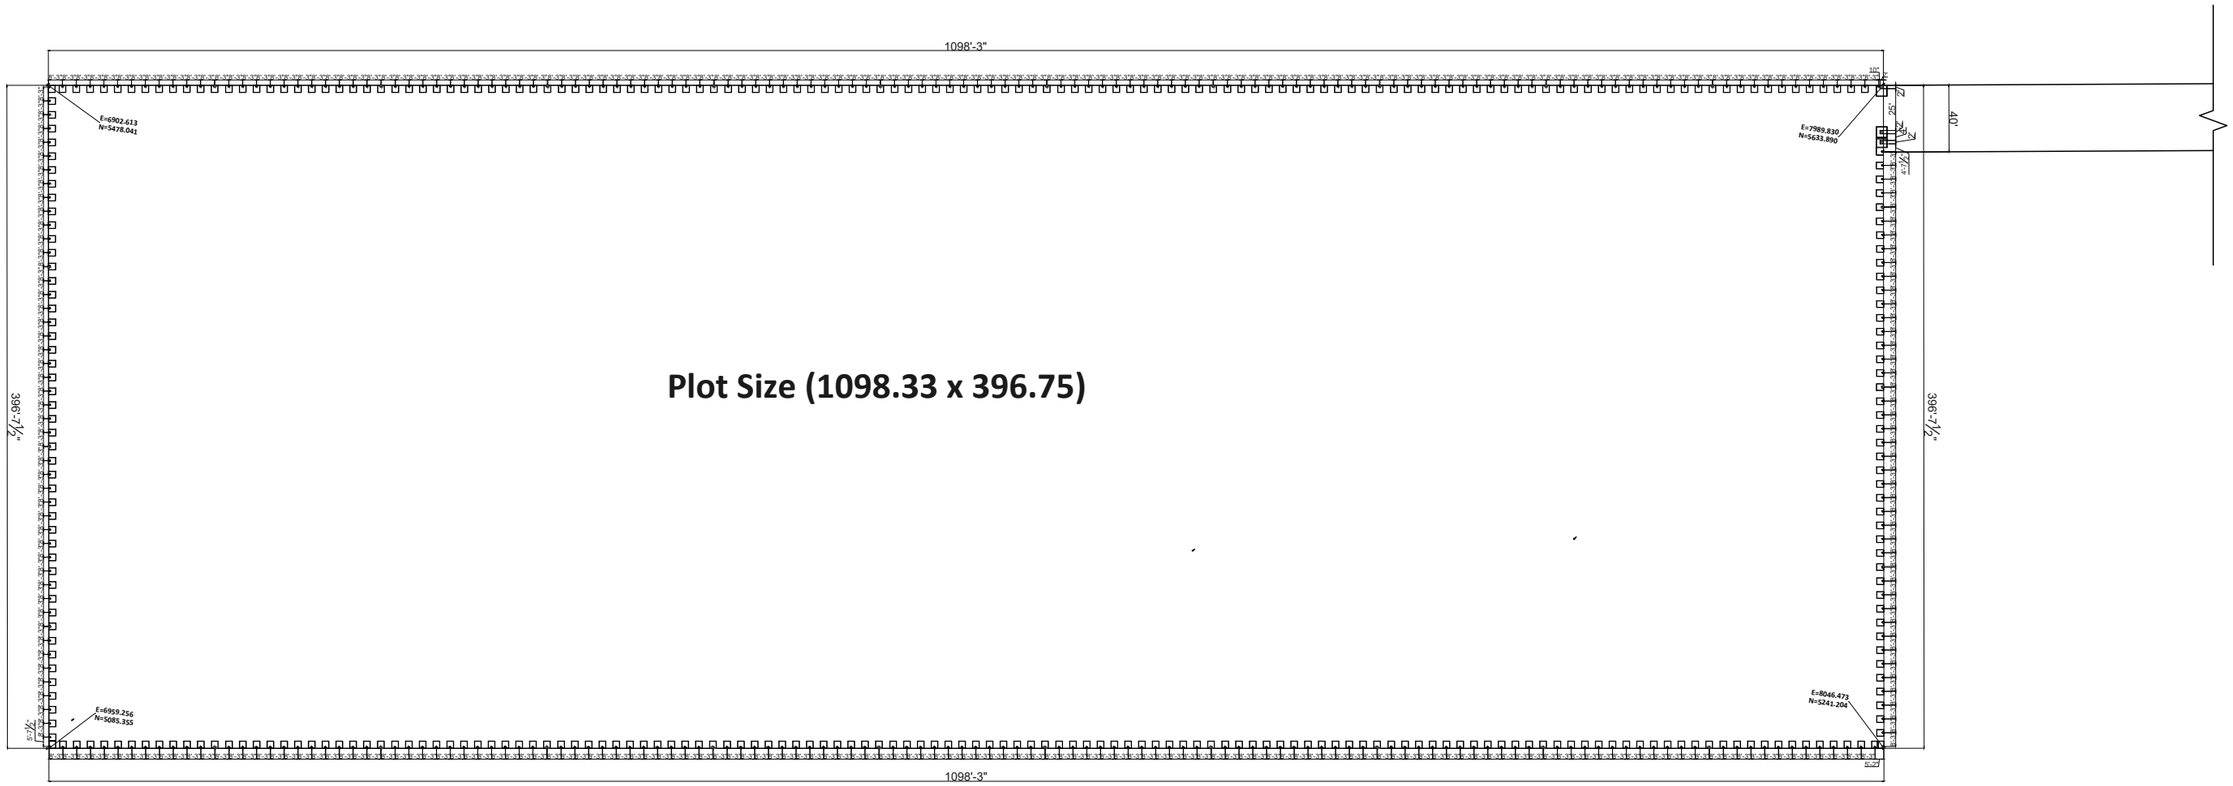

BOUNDARY WALL LAYOUT PLAN


REV.	DESCRIPTION	DATE	BY	CHK'D	APP'D
4					
3					
2					
1					

REVISIONS


PROJECT CODE NUMBER:

DESIGNED: AC	**CLIENT:** GO AGRO
DRAWN: MS	**PROJECT:** MEAT PACKING PLANT SHIEKHUPURA
CHECKED: FM	**TITLE:** BOUNDARY WALL LAYOUT PLAN
APPROVED:	
SCALE: N.T.S.	
SHEET SIZE: A3	
DATE: 01-12-2025	


DRAWING NO.	SHEET NO	REV.
10459-BOUNDARY WALL-L-01	1 OF 3	0

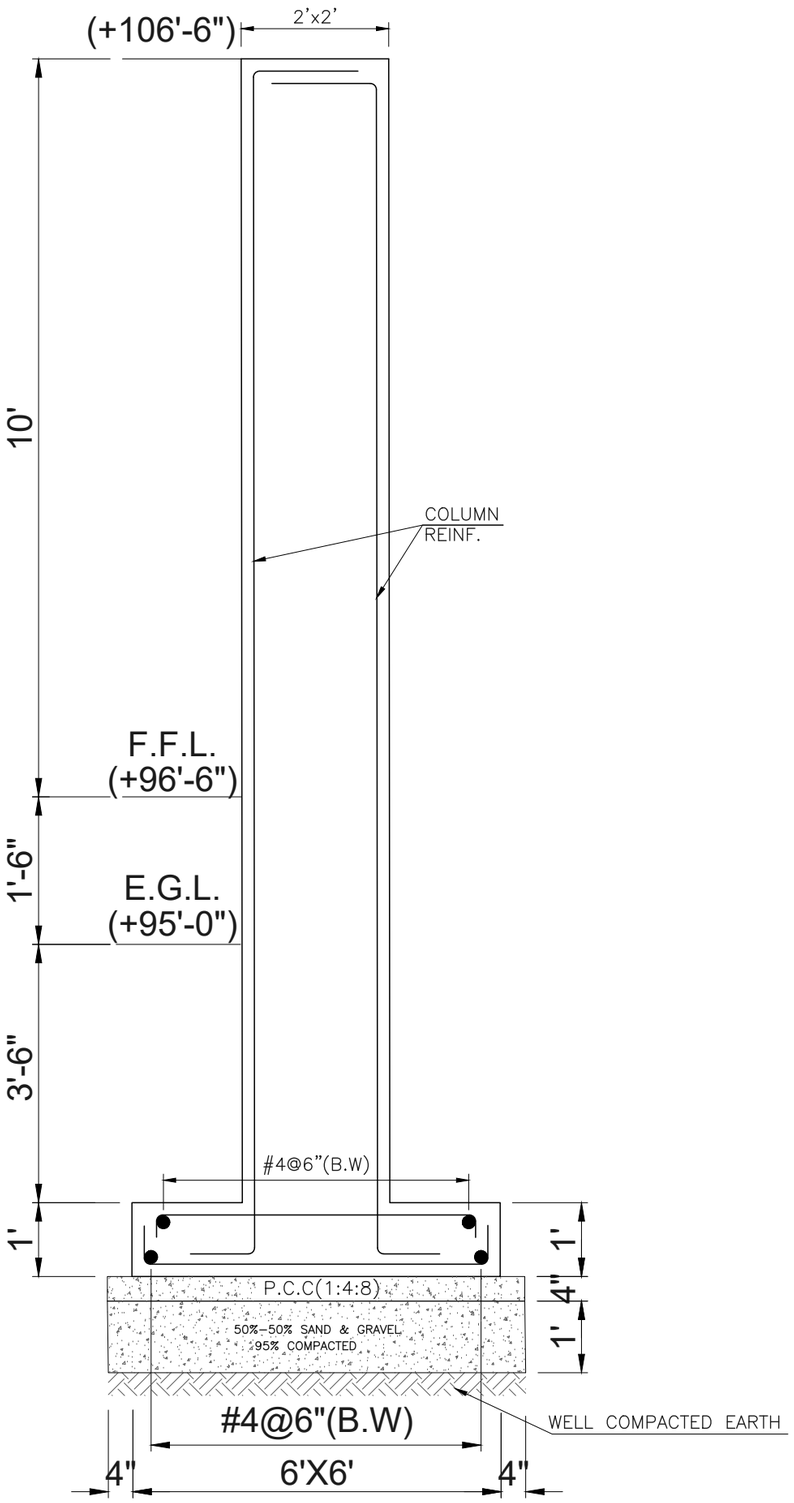


SECTION 1-1

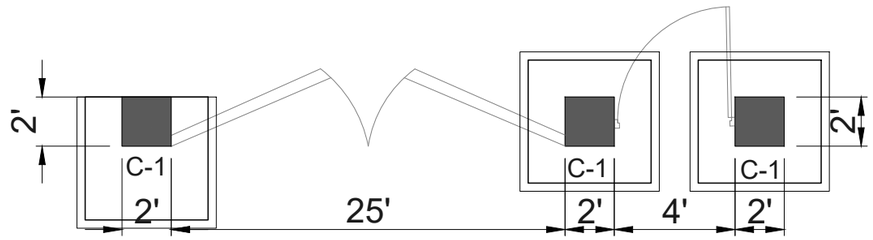

MAIN GATE PLAN

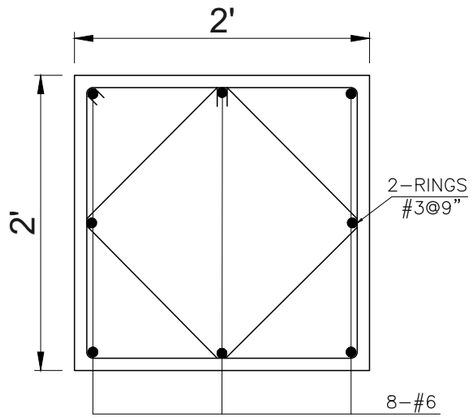

COLUMN C-1

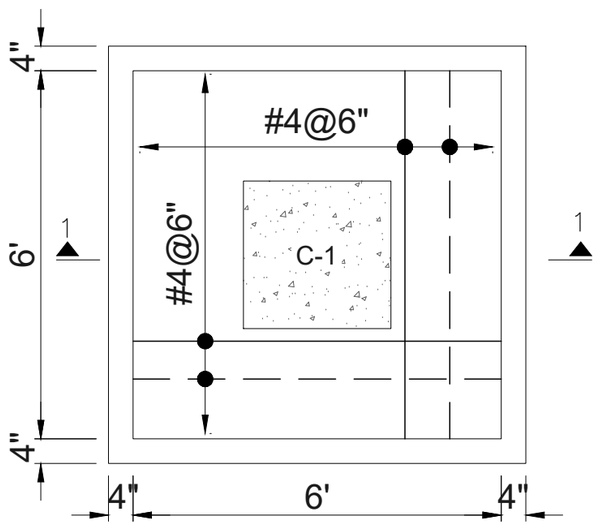


C-1 FOOTING PLAN

REV.	DESCRIPTION	DATE	BY	CHK'D	APP'D
4					
3					
2					
1					


REVISIONS

PROJECT CODE NUMBER:


DESIGNED: AC	CLIENT: GO AGRO
DRAWN: MS	PROJECT: MEAT PACKING PLANT SHIEKHUPURA
CHECKED: FM	TITLE: MAIN GATE COLUMNS FOOTING DETAIL
APPROVED:	
SCALE: N.T.S.	
SHEET SIZE: A3	DRAWING NO. 10459-MAIN GATE-L-02
DATE: 01-12-2025	SHEET NO 2 OF 3
	REV. 0

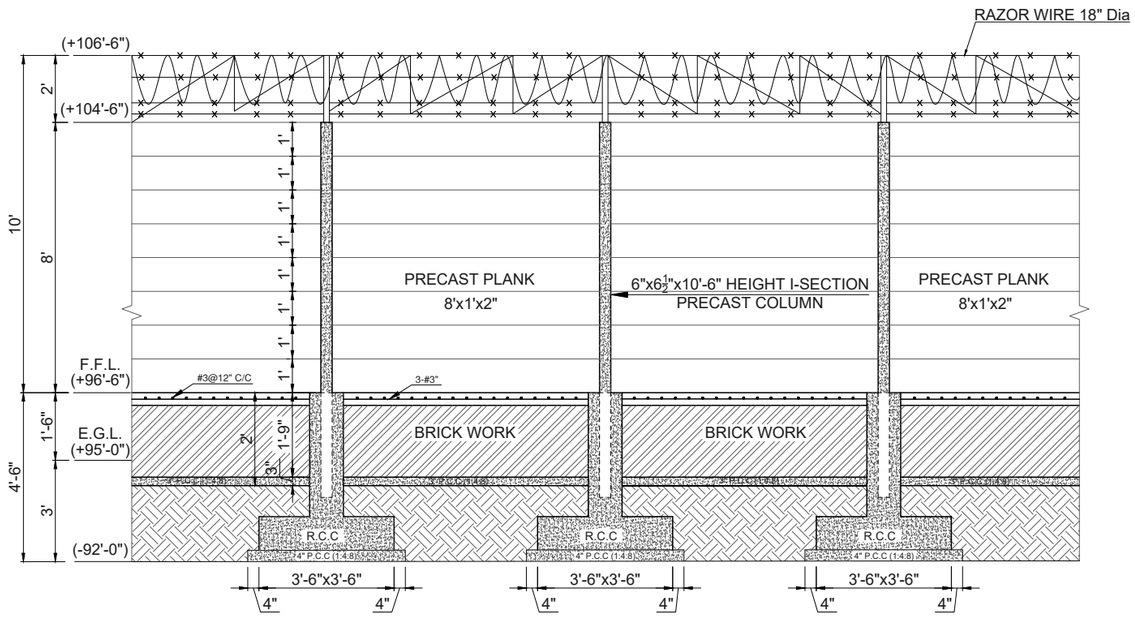

BOUNDARY WALL TYPICAL ELEVATION OF PART PLAN

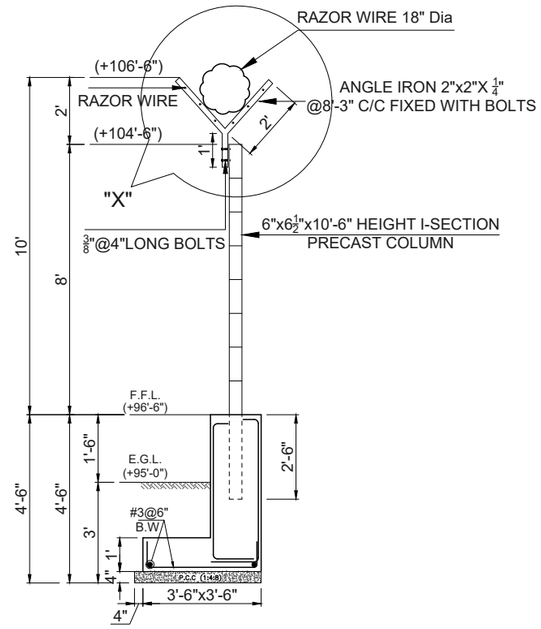


SECTION A'-A'

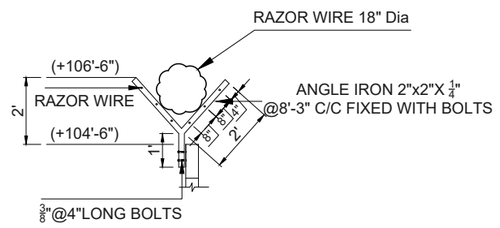


DETAIL "X"

LEGEND:


1. EXPANSION JOINTS AT EVERY 100'-0"
2. FOUNDATION P.C.C 1:4:8 1500 PSI
3. FOUNDATION R.C.C 1:2:4 3750 PSI
4. FOUNDATION STEEL #3@6"
5. 6"x61/2"x10'-6" HEIGHT I-SECTION PRECAST COLUMN 6000 PSI
6. PRECAST PLANK 8'x1'x2" 3800 PSI
7. ANGLE IRON 1½"x1½" SIZE DUALLY PAINTED
8. RAZOR WIRE 18" Dia

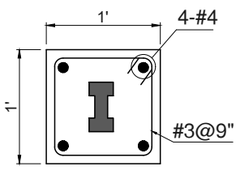


COLUMN C-1

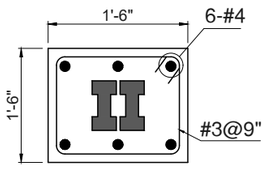


COLUMN C-2

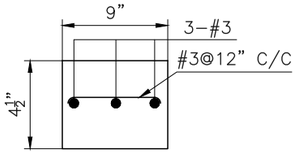


PLINTH BEAM

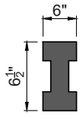


PC.B.W COLUMN

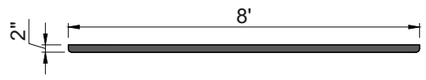

PC.B.W PLANK

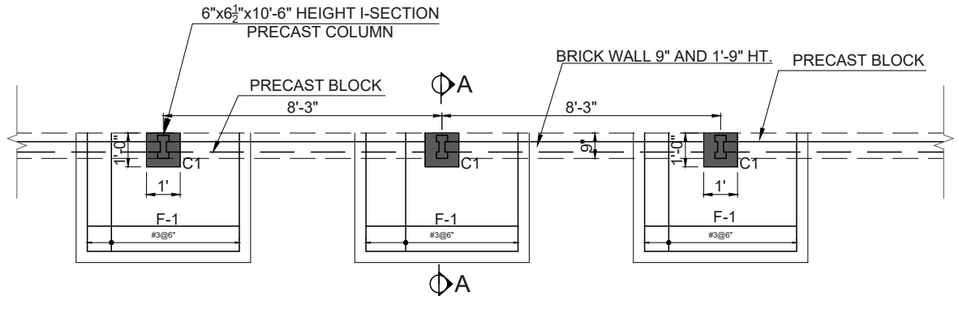

TYPICAL FOUNDATION PART PLAN

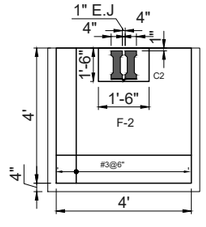

F-2 PLAN

AT EXPANSION JOINTS

REV.	DESCRIPTION	DATE	BY	CHK'D	APP'D
4					
3					
2					
1					

REVISIONS

PROJECT CODE NUMBER:

DESIGNED: AC	**CLIENT:** GO AGRO
DRAWN: MS	**PROJECT:** MEAT PACKING PLANT SHIEKHUPURA
CHECKED: FM	**TITLE:** BOUNDARY WALL PLAN AND SECTIONS
APPROVED:	
SCALE: N.T.S.	
SHEET SIZE: A3	**DRAWING NO.** 10459-BOUNDARY WALL-L-03
DATE: 01-12-2025	**SHEET NO** 3 OF 3
	REV. 0