# SAYYADENA AMEER HAMZA HOSPITAL
# FAISALABAD
## | New Site |


## REVISED 003 LAYOUT

## FINAL LAYOUT PLAN


Architect:

ARCUS
| Exterior & Interior |

4th Floor, 52-MB,
Main Boulevard, DHA Phase-6,
Lahore.
Contact: 0302-844-2276
E-mail: ar.talhamasood@arcus.com.pk

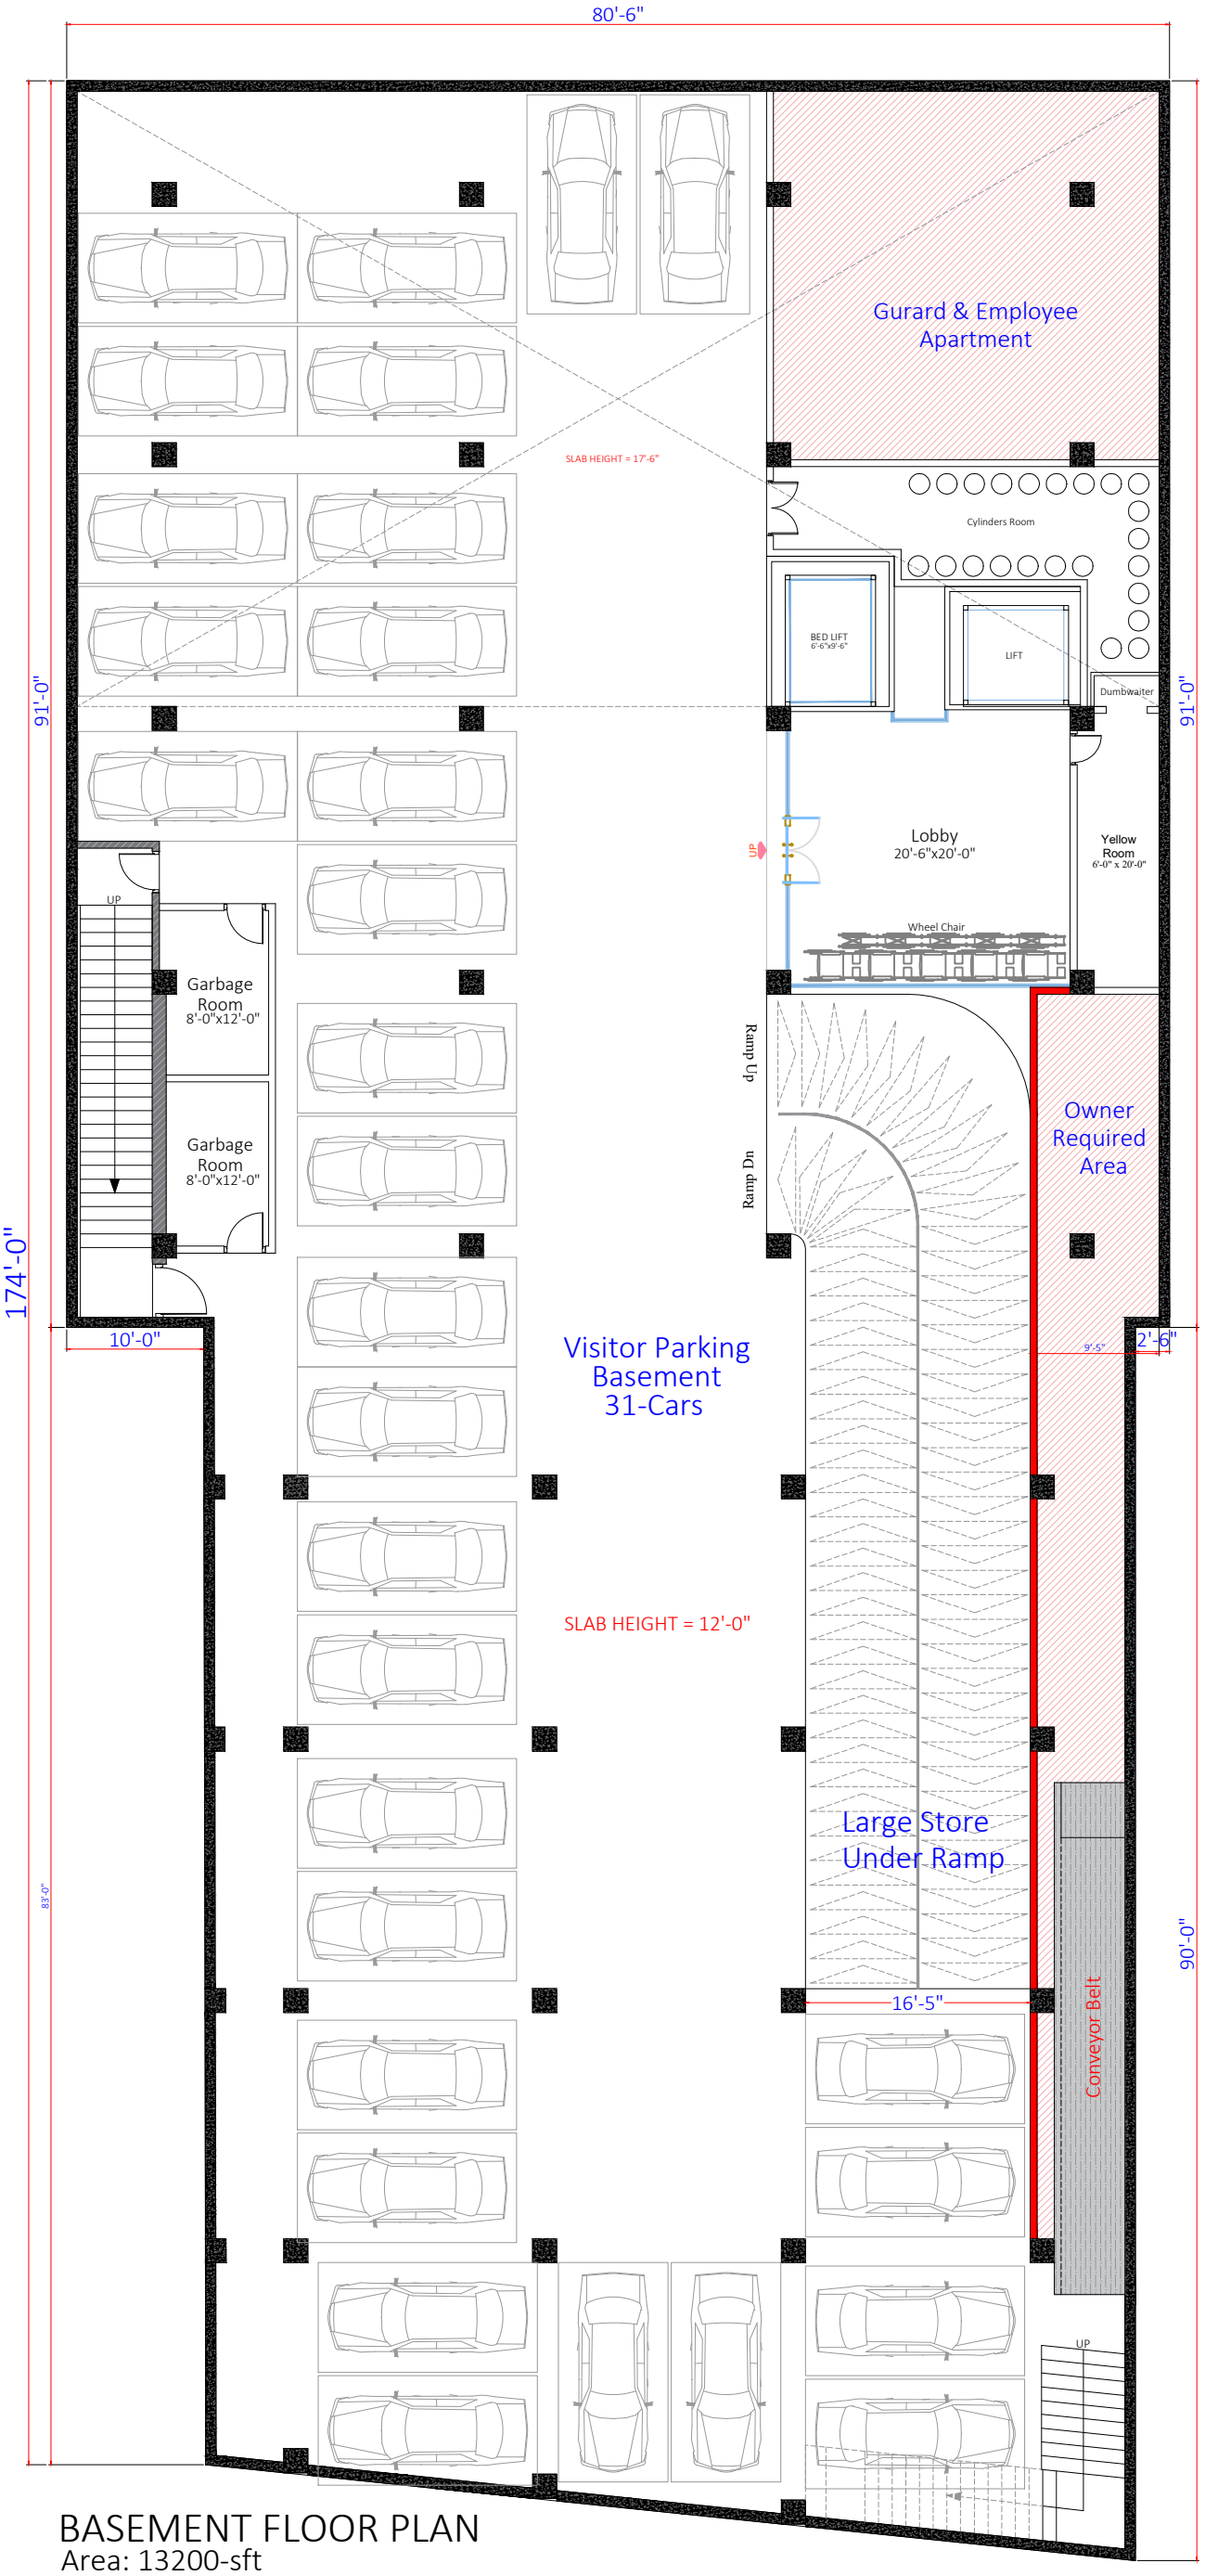


# BASEMENT FLOOR PLAN

Area: 13200-sft

| | | | |
|---|---|---|---|
| PROJECT: NEW SITE **SAYYADENA AMEER HAMZA HOSPITAL** Faisalabad | NO | DATE | REVISION |
| | 001 | 11-21-2025 | Guard Residence Addition |
| | 001 | 11-27-2025 | Yellow room Addtition |
| TOTAL PLOT AREA: 00000 SFT. | | | |
| TOTAL COVERED AREA : G.F + F.F 00000 SFT. | | | |
| TOTAL COVERED AREA G.F: 00000 SFT. / TOTAL COVERED AREA F.F: 00000 SFT. | | | |

ARCHITECT: ARCUS | Exterior & Interior | Talha Masood 0302-844-2276

CONSULTANTS:


TITLE: DRAWINGS REVISED LAYOUT 002

| | |
|---|---|
| PROJ. ARCH. TALHA MASOOD | DWG NO. 001 |
| DRAWN : M.FARHAN | SCALE: N.T.S. @ A-3 |
| CHECKED : TALHA MASOOD | DATE: 11-21-2025 |
| JOB NO: D:\Talha Data\ARCUS Karachi Office\Ameer Hamza,Hospital, Fsd\SAH - New Site (Abu Muhsin Plaza).dwg | |

orientation

Issued for

- Client Approval
- Submission Approval
- On site Construction
- Tenders

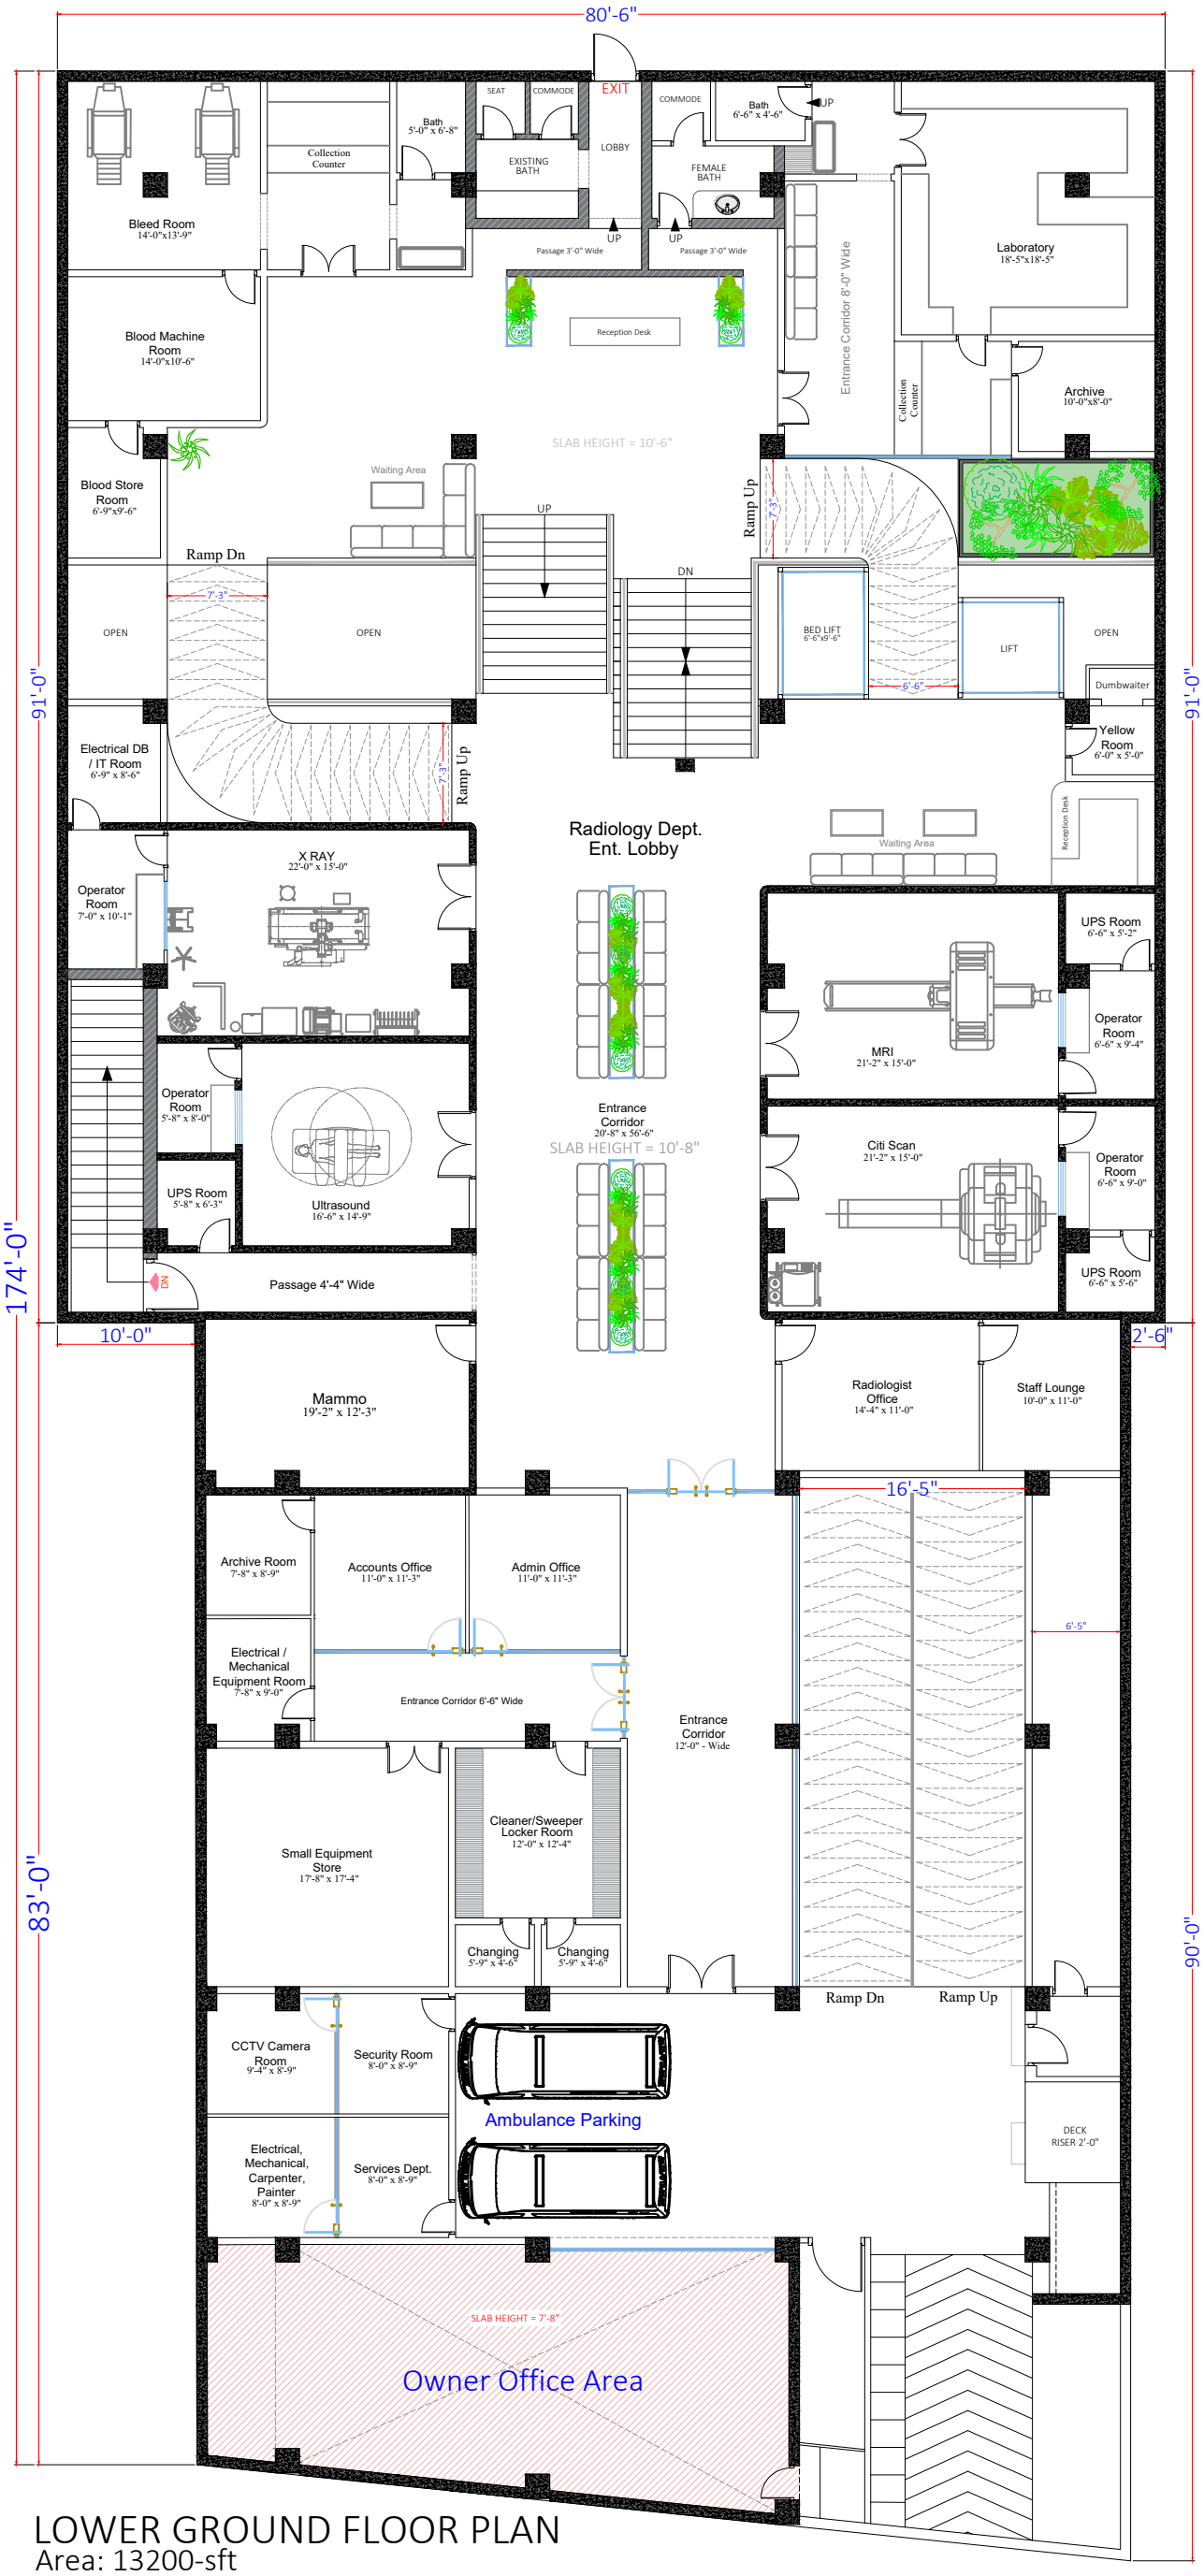


# LOWER GROUND FLOOR PLAN

Area: 13200-sft

| | | | |
|---|---|---|---|
| PROJECT: NEW SITE **SAYYADENA AMEER HAMZA HOSPITAL** Faisalabad | | | |
| TOTAL PLOT AREA: 00000 SFT. | | | |
| TOTAL COVERED AREA : G.F + F.F 00000 SFT. | | | |
| TOTAL COVERED AREA G.F: 00000 SFT. | TOTAL COVERED AREA F.F: 00000 SFT. | | |

| NO | DATE | REVISION |
|---|---|---|
| 001 | 11-21-2025 | Department Addition |
| 002 | 11-22-2025 | Laboratory Extension |
| 003 | 11-27-2025 | Reception Addition |

ARCHITECT: ARCUS | Exterior & Interior | Talha Masood 0302-844-2276


CONSULTANTS:

TITLE: DRAWINGS
REVISED LAYOUT 003

| | |
|---|---|
| PROJ. ARCH. TALHA MASOOD | DWG NO. 002 |
| DRAWN : M.FARHAN | SCALE: N.T.S. @ A-3 |
| CHECKED : TALHA MASOOD | DATE: 11-21-2025 |
| JOB NO: D:\Talha Data\ARCUS Karachi Office\Ameer Hamza,Hospital, Fsd\SAH - New Site (Abu Muhsin Plaza).dwg | |

orientation

Issued for
- Client Approval
- Submission Approval
- On site Construction
- Tenders

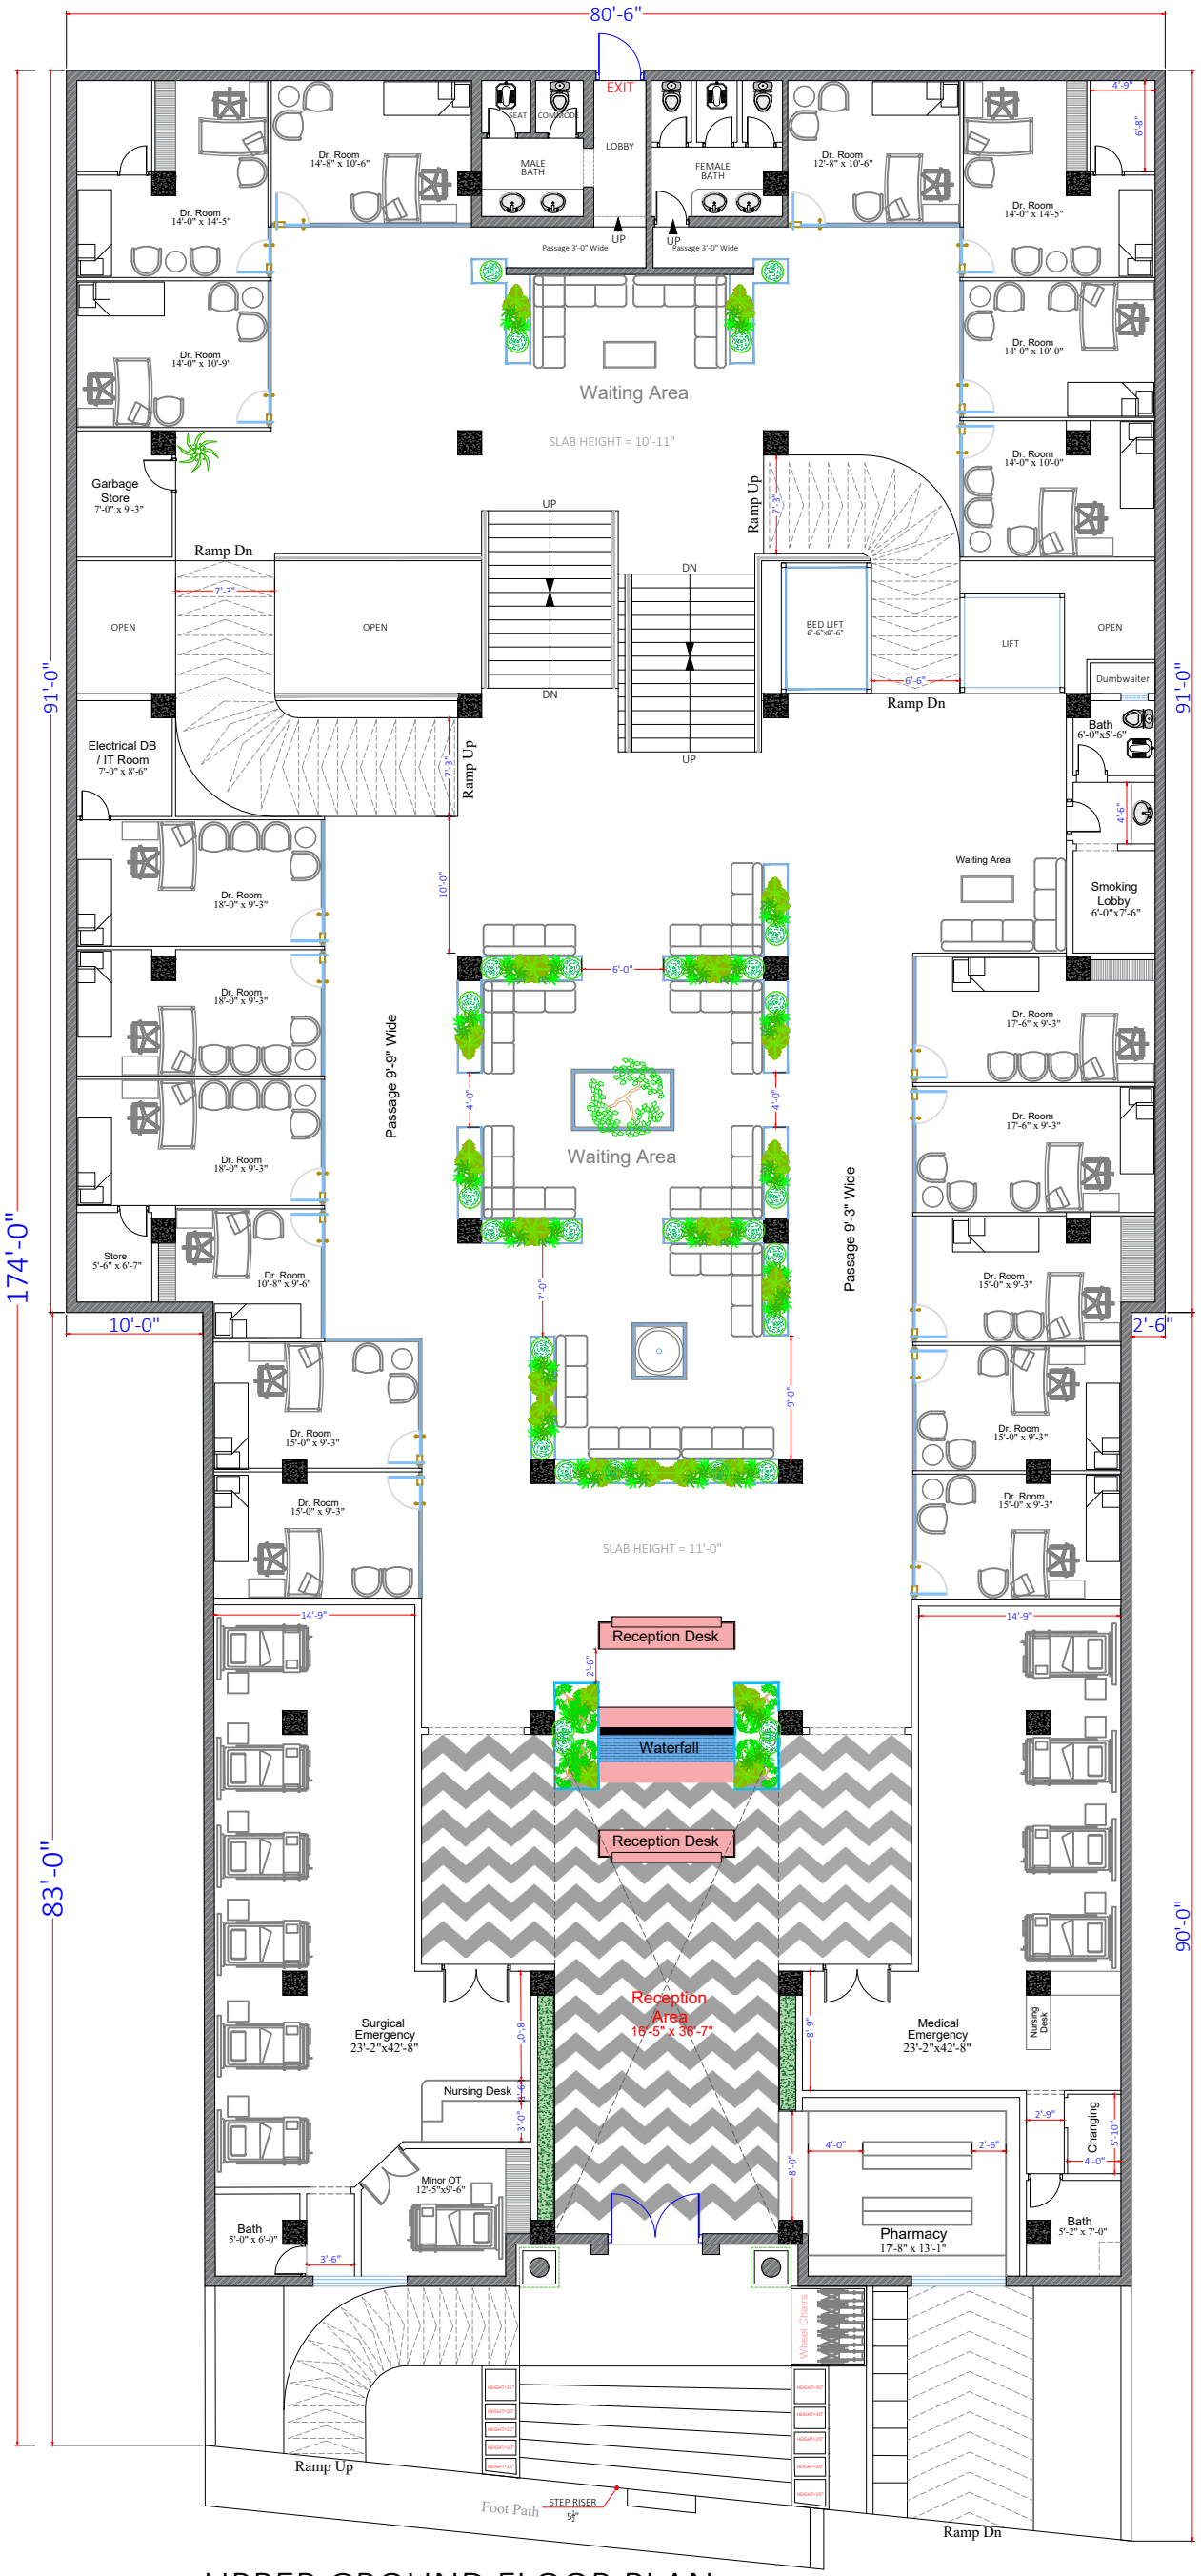


# UPPER GROUND FLOOR PLAN

Area: 12110-sft

| | | | |
|---|---|---|---|
| PROJECT: NEW SITE **SAYYADENA AMEER HAMZA HOSPITAL** Faisalabad | TOTAL PLOT AREA: 00000 SFT. | TOTAL COVERED AREA : G.F + F.F 00000 SFT. | TOTAL COVERED AREA G.F: 00000 SFT. / TOTAL COVERED AREA F.F: 00000 SFT. |

| NO | DATE | REVISION |
|---|---|---|
| 001 | 11-21-2025 | OPD Extend |

ARCHITECT: ARCUS | Exterior & Interior | Talha Masood 0302-844-2276

CONSULTANTS:


TITLE: DRAWINGS
REVISED LAYOUT 001

| | |
|---|---|
| PROJ. ARCH. TALHA MASOOD | DWG NO. 003 |
| DRAWN : M.FARHAN | SCALE: N.T.S. @ A-3 |
| CHECKED : TALHA MASOOD | DATE: 11-21-2025 |

JOB NO: D:\Talha Data\ARCUS Karachi Office\Ameer Hamza,Hospital, Fsd\SAH - New Site (Abu Muhsin Plaza).dwg

orientation

Issued for
- Client Approval
- Submission Approval
- On site Construction
- Tenders

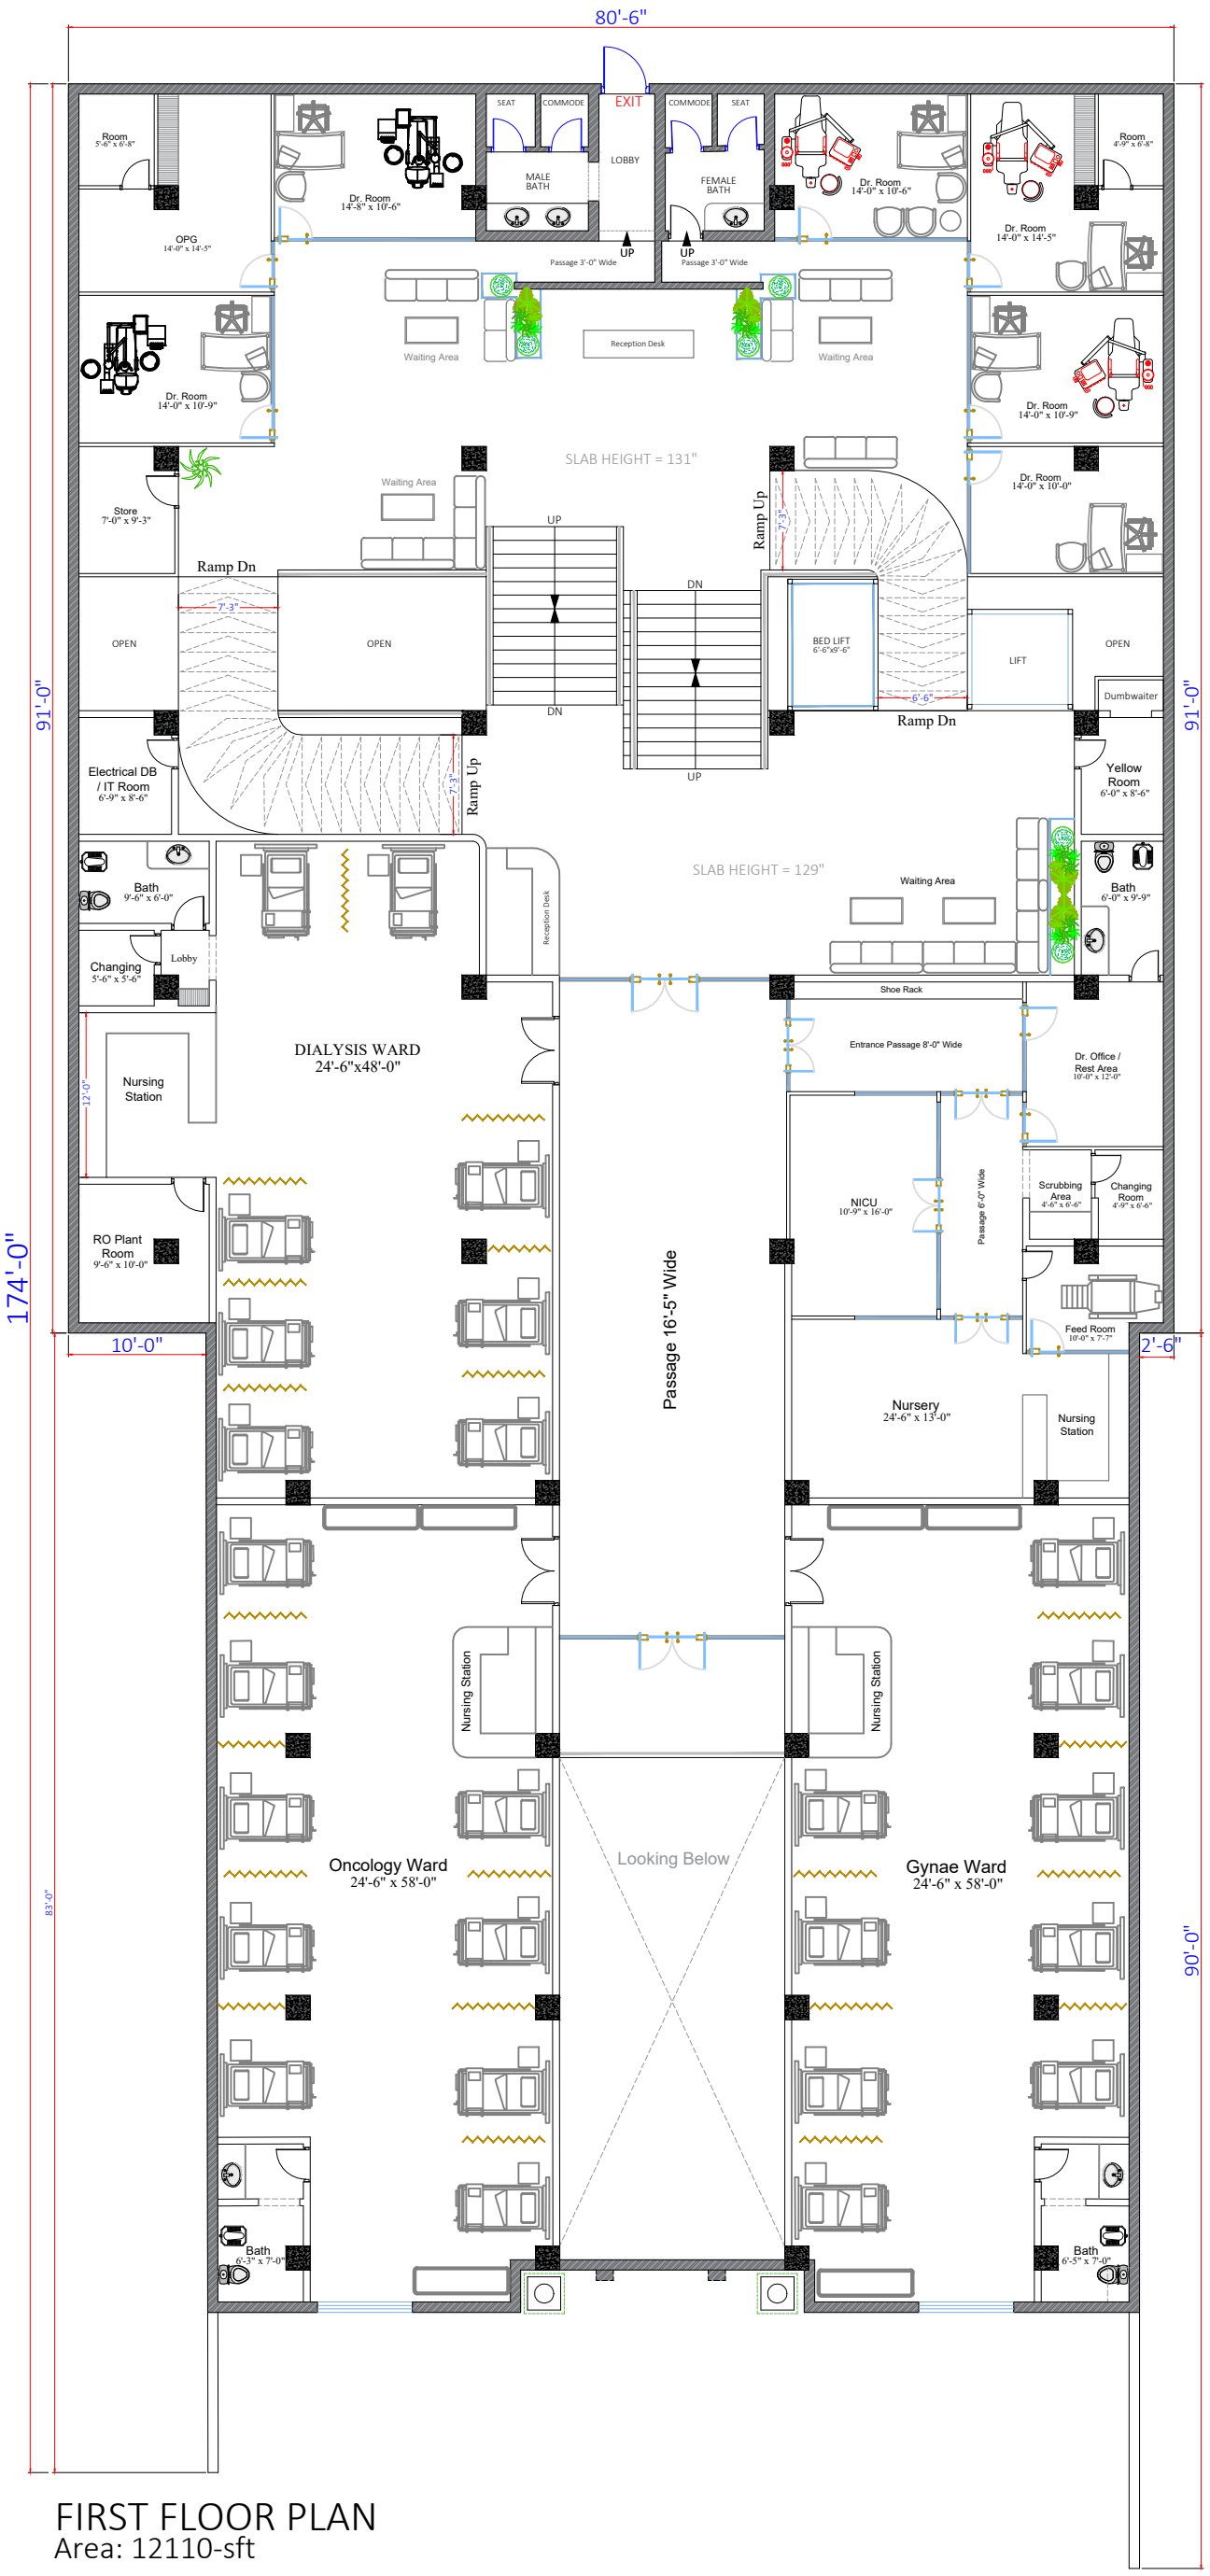


# FIRST FLOOR PLAN

Area: 12110-sft


| | | | |
|---|---|---|---|
| PROJECT: NEW SITE **SAYYADENA AMEER HAMZA HOSPITAL** Faisalabad | ARCHITECT: ARCUS \| Exterior & Interior \| Talha Masood 0302-844-2276 | CONSULTANTS: | TITLE: DRAWINGS REVISED LAYOUT 002 |
| TOTAL PLOT AREA: 00000 SFT. | | | PROJ. ARCH.: TALHA MASOOD; DWG NO.: 004 |
| TOTAL COVERED AREA : G.F + F.F: 00000 SFT. | | | DRAWN : M.FARHAN; SCALE: N.T.S. @ A-3 |
| TOTAL COVERED AREA G.F: 00000 SFT. / TOTAL COVERED AREA F.F: 00000 SFT. | | | CHECKED : TALHA MASOOD; DATE: 11-21-2025 |
| | | | JOB NO: D:\Talha Data\ARCUS Karachi Office\Ameer Hamza,Hospital, Fsd\SAH - New Site (Abu Muhsin Plaza).dwg |

| NO | DATE | REVISION |
|---|---|---|
| 001 | 11-27-2025 | NICU Area Revised |
| 002 | 11-28-2025 | NICU Area Revised |

orientation

Issued for

- Client Approval
- Submission Approval
- On site Construction
- Tenders

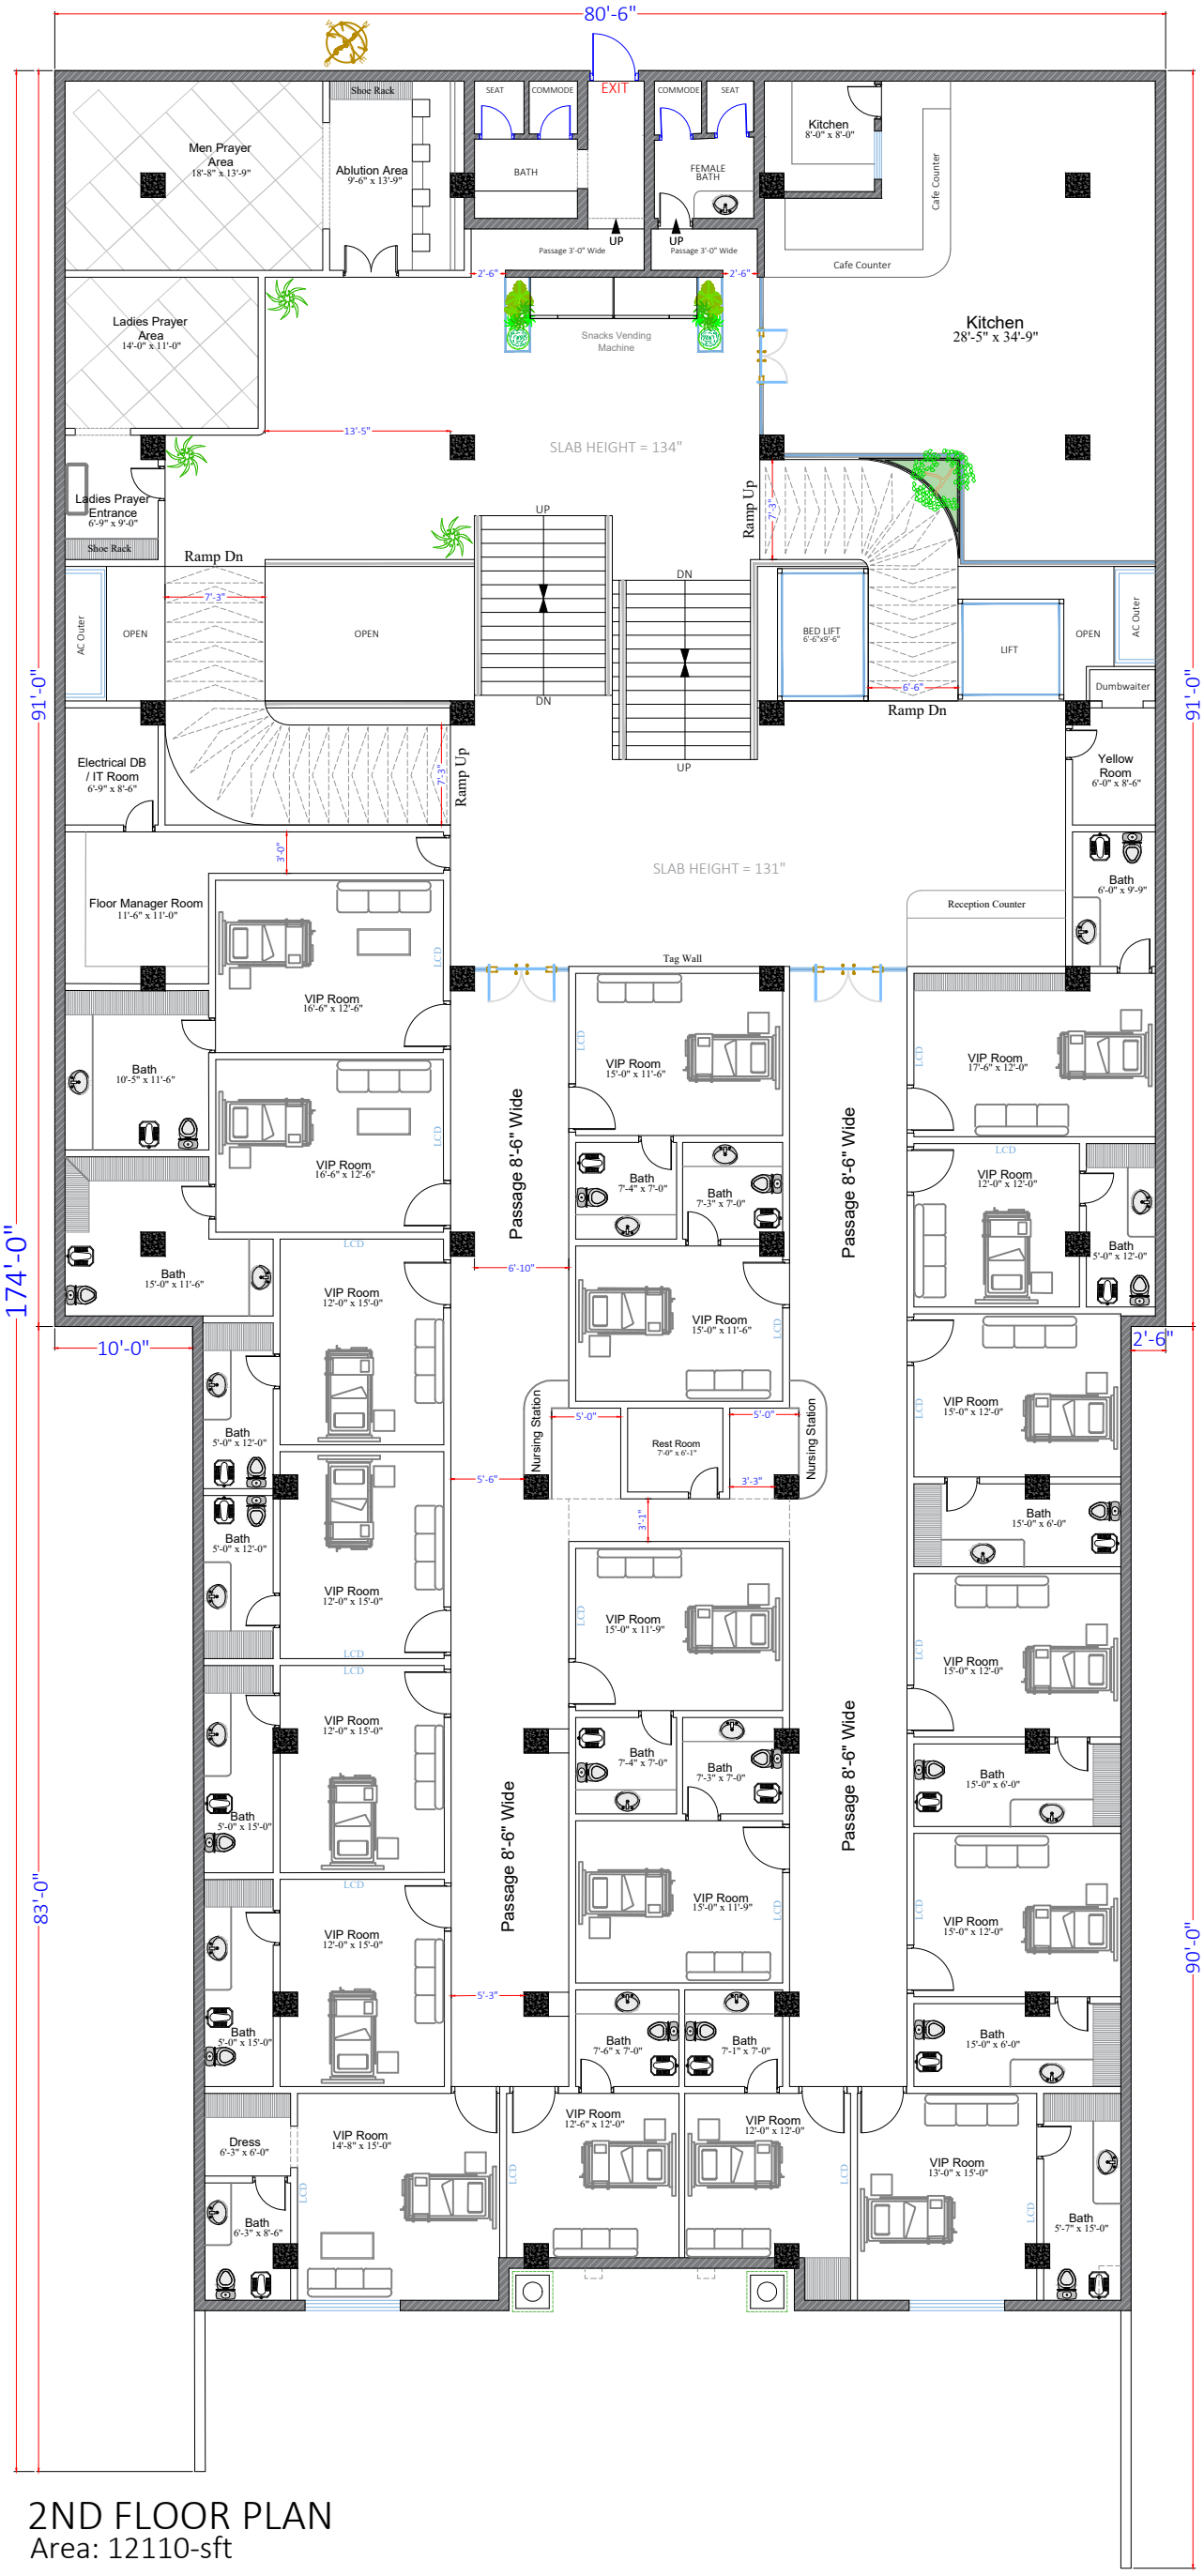


# 2ND FLOOR PLAN

Area: 12110-sft


| | | | | | |
|---|---|---|---|---|---|
| PROJECT: NEW SITE **SAYYADENA AMEER HAMZA HOSPITAL** Faisalabad | NO | DATE | REVISION | ARCHITECT: ARCUS \| Exterior & Interior \| Talha Masood 0302-844-2276 | CONSULTANTS: |
| | 001 | 11-27-2025 | Yellow Room Addition | | |
| TOTAL PLOT AREA: 00000 SFT. | | | | | |
| TOTAL COVERED AREA : G.F + F.F 00000 SFT. | | | | | |
| TOTAL COVERED AREA G.F: 00000 SFT. / TOTAL COVERED AREA F.F: 00000 SFT. | | | | | |

TITLE: DRAWINGS
REVISED LAYOUT 001

| | |
|---|---|
| PROJ. ARCH.: TALHA MASOOD | DWG NO.: 005 |
| DRAWN : M.FARHAN | SCALE: N.T.S. @ A-3 |
| CHECKED : TALHA MASOOD | DATE: 11-25-2025 |
| JOB NO: D:\Talha Data\ARCUS Karachi Office\Ameer Hamza,Hospital, Fsd\SAH - New Site (Abu Muhsin Plaza).dwg | |

orientation

Issued for
- Client Approval
- Submission Approval
- On site Construction
- Tenders

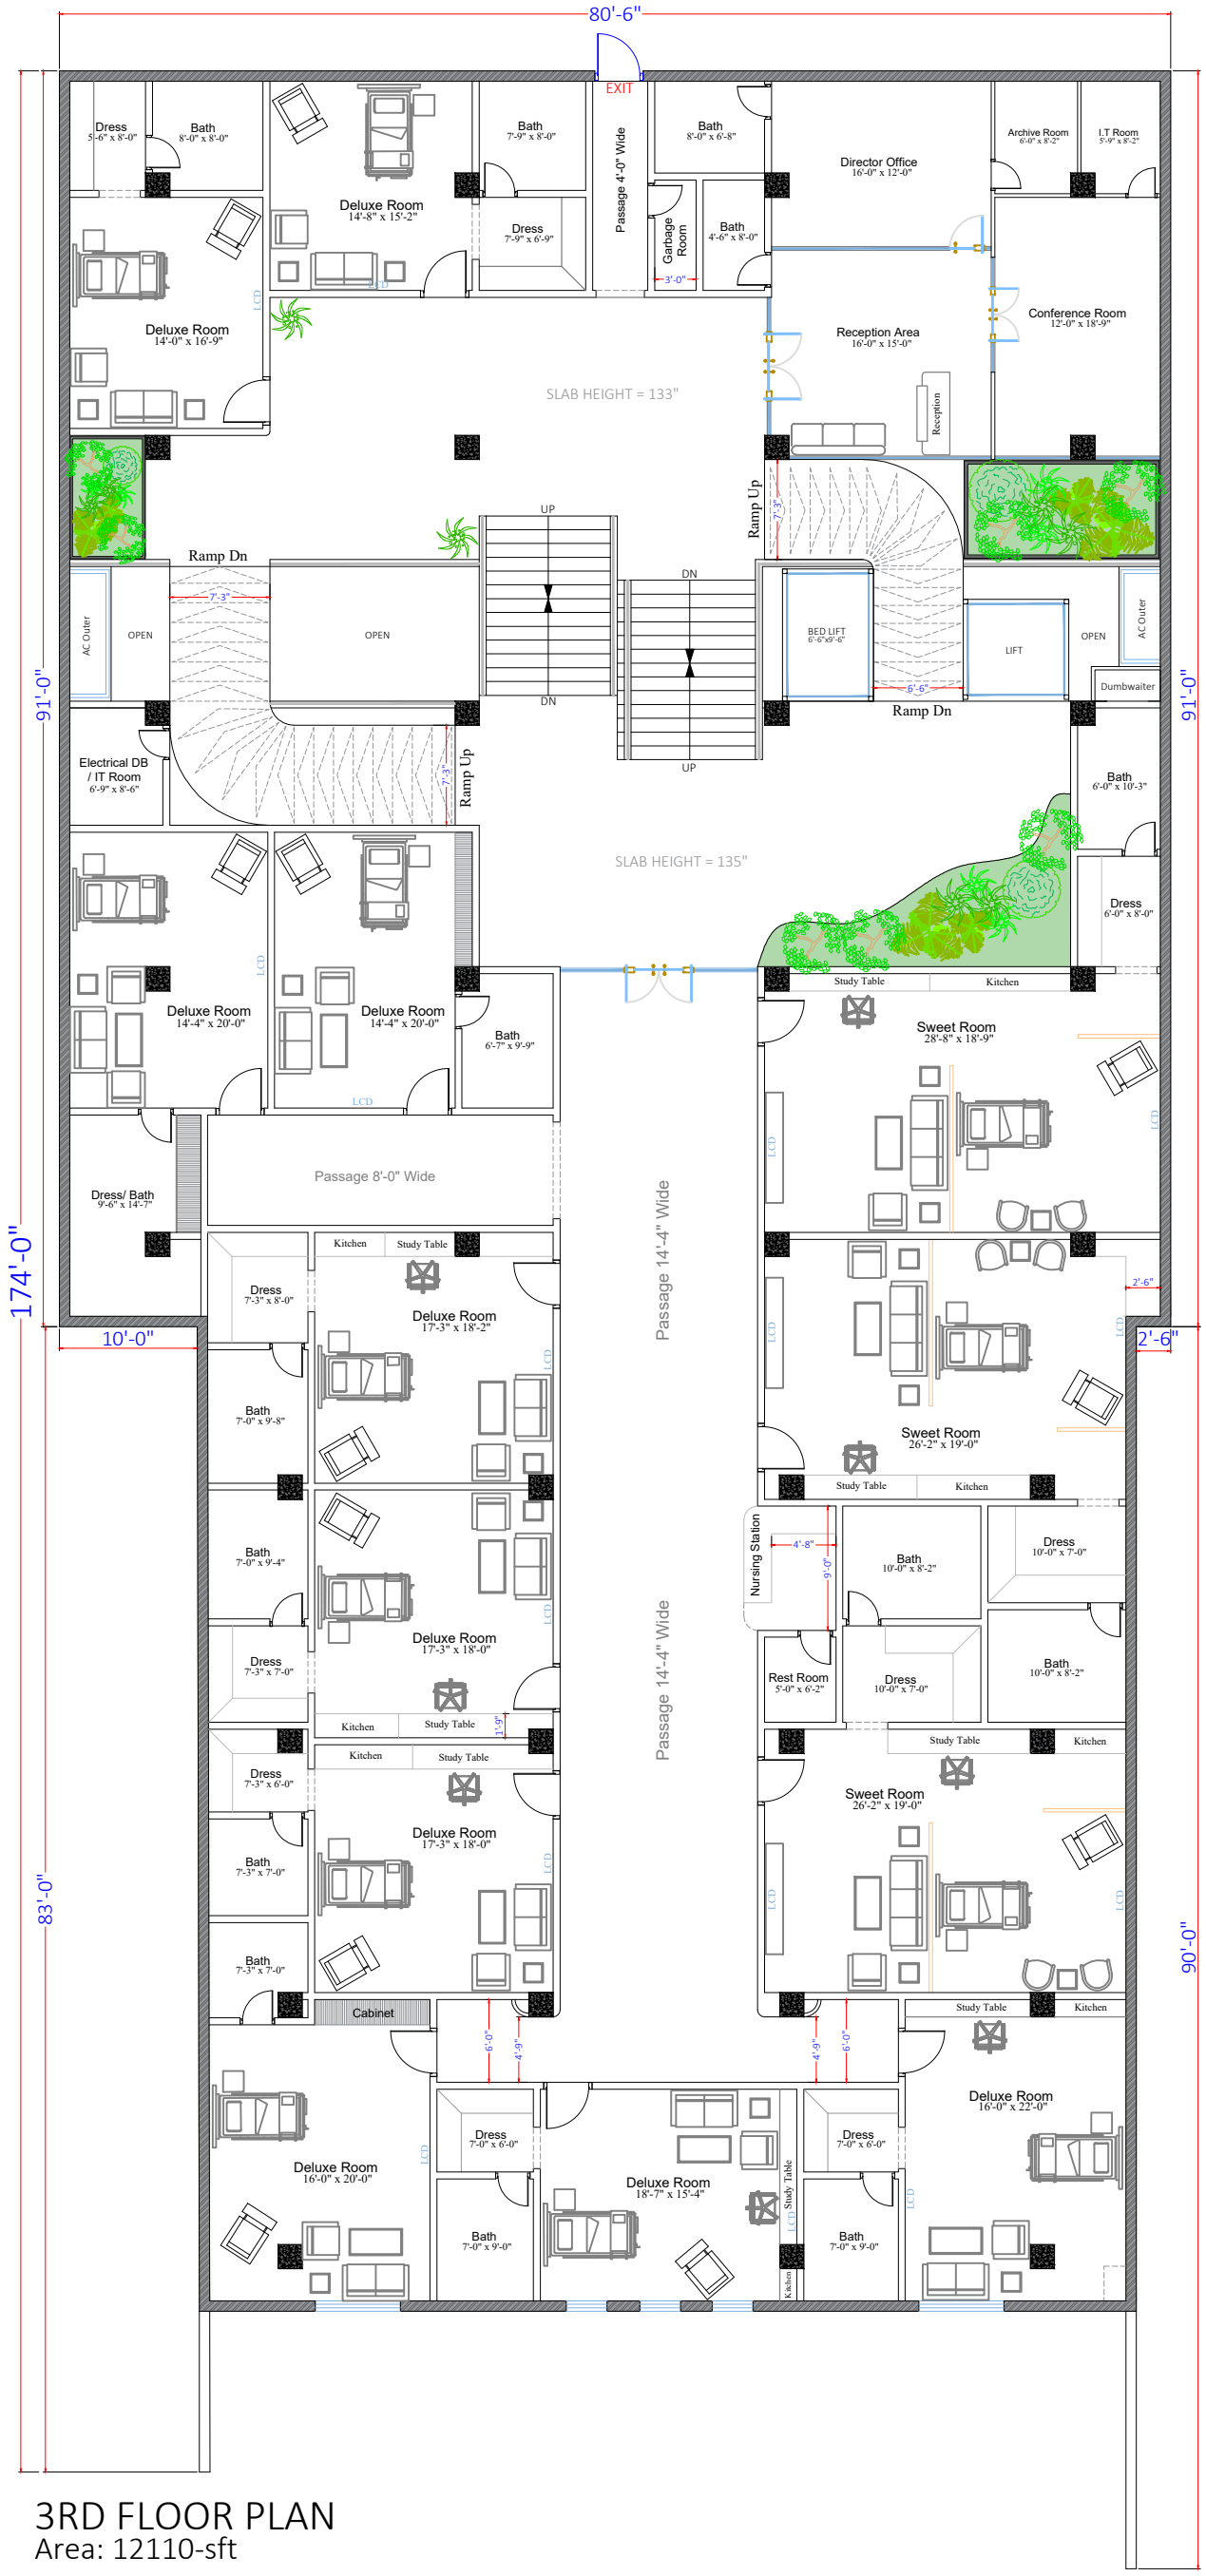


# 3RD FLOOR PLAN

Area: 12110-sft


| | | | | | |
|---|---|---|---|---|---|
| PROJECT: NEW SITE **SAYYADENA AMEER HAMZA HOSPITAL** Faisalabad | NO | DATE | REVISION | ARCHITECT: ARCUS \| Exterior & Interior \| Talha Masood 0302-844-2276 | CONSULTANTS: |
| | 001 | 11-27-2025 | Sweet Room Reduce | | |
| TOTAL PLOT AREA: 00000 SFT. | | | | | |
| TOTAL COVERED AREA : G.F + F.F 00000 SFT. | | | | | |
| TOTAL COVERED AREA G.F: 00000 SFT. / TOTAL COVERED AREA F.F: 00000 SFT. | | | | | |

| | |
|---|---|
| TITLE: | DRAWINGS<br>REVISED LAYOUT 001 |
| PROJ. ARCH. | TALHA MASOOD |
| DWG NO. | 006 |
| DRAWN : | M.FARHAN |
| SCALE: | N.T.S. @ A-3 |
| CHECKED : | TALHA MASOOD |
| DATE: | 11-25-2025 |
| JOB NO: | D:\Talha Data\ARCUS Karachi Office\Ameer Hamza,Hospital, Fsd\SAH - New Site (Abu Muhsin Plaza).dwg |

orientation

Issued for

- Client Approval
- Submission Approval
- On site Construction
- Tenders

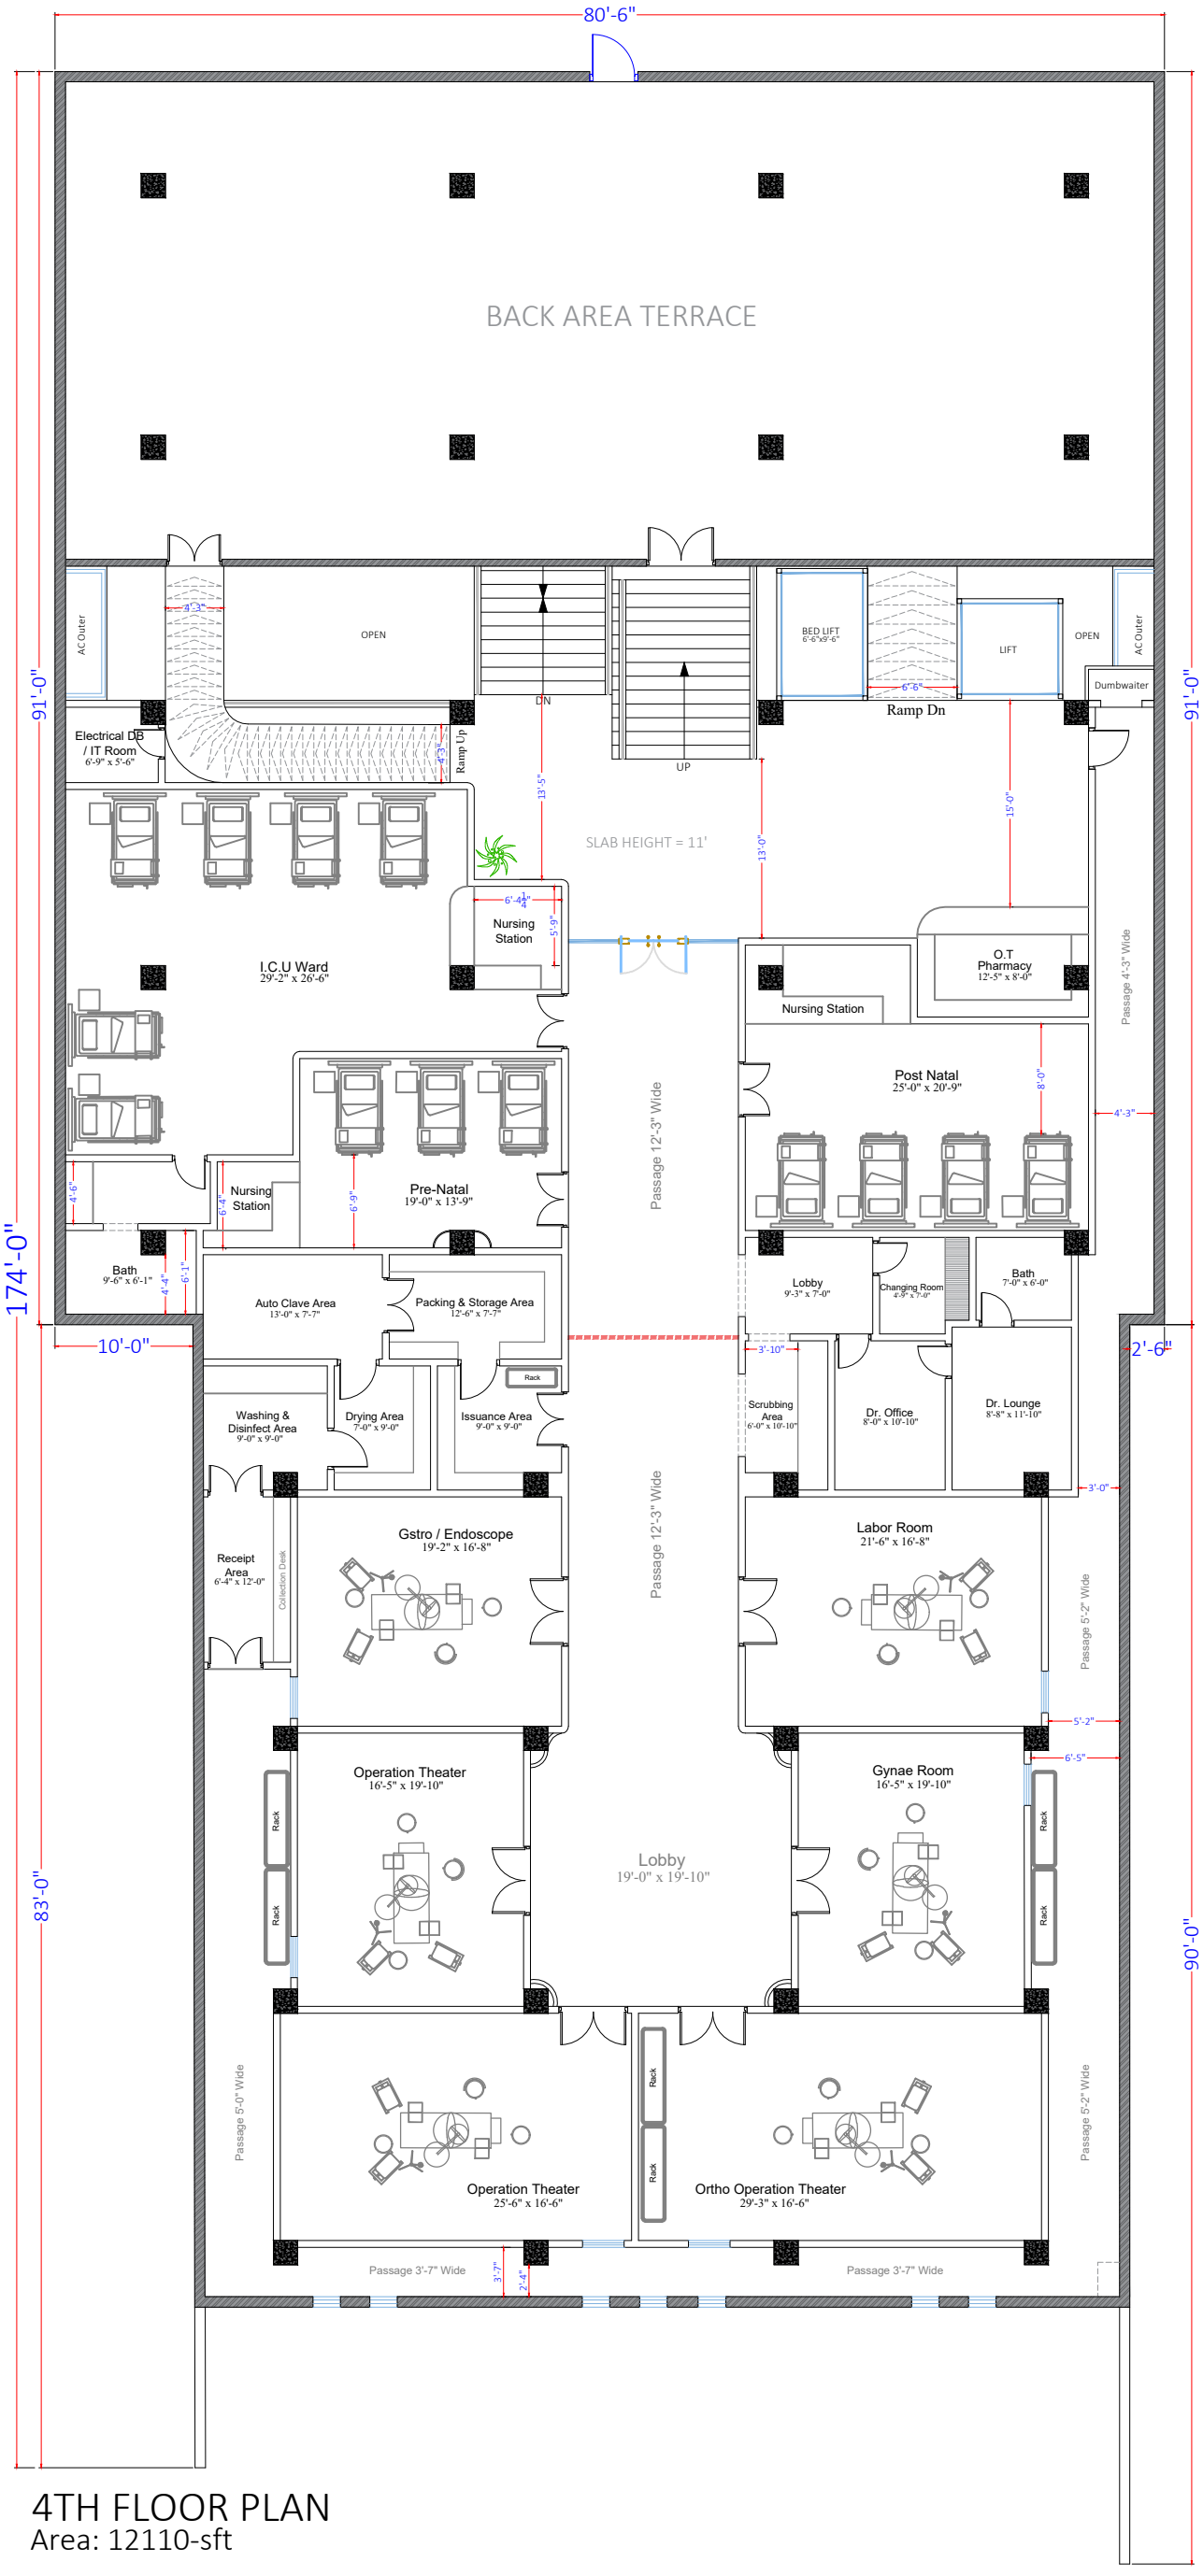


# 4TH FLOOR PLAN

Area: 12110-sft

| | | | |
|---|---|---|---|
| PROJECT: NEW SITE **SAYYADENA AMEER HAMZA HOSPITAL** Faisalabad | NO | DATE | REVISION |
| | 001 | 11-27-2025 | Complete Layout |
| | 002 | 11-28-2025 | ICU Revision |
| | 003 | 11-29-2025 | OT Pharmacy Shift |
| TOTAL PLOT AREA: 00000 SFT. | | | |
| TOTAL COVERED AREA : G.F + F.F 00000 SFT. | | | |
| TOTAL COVERED AREA G.F: 00000 SFT. / TOTAL COVERED AREA F.F: 00000 SFT. | | | |

ARCHITECT: ARCUS | Exterior & Interior | Talha Masood 0302-844-2276

CONSULTANTS:

TITLE: DRAWINGS REVISED LAYOUT 003

| | |
|---|---|
| PROJ. ARCH. TALHA MASOOD | DWG NO. 007 |
| DRAWN : M.FARHAN | SCALE: N.T.S. @ A-3 |
| CHECKED : TALHA MASOOD | DATE: 11-25-2025 |
| JOB NO: D:\Talha Data\ARCUS Karachi Office\Ameer Hamza,Hospital, Fsd\SAH - New Site (Abu Muhsin Plaza).dwg | |

orientation

Issued for

- Client Approval
- Submission Approval
- On site Construction
- Tenders