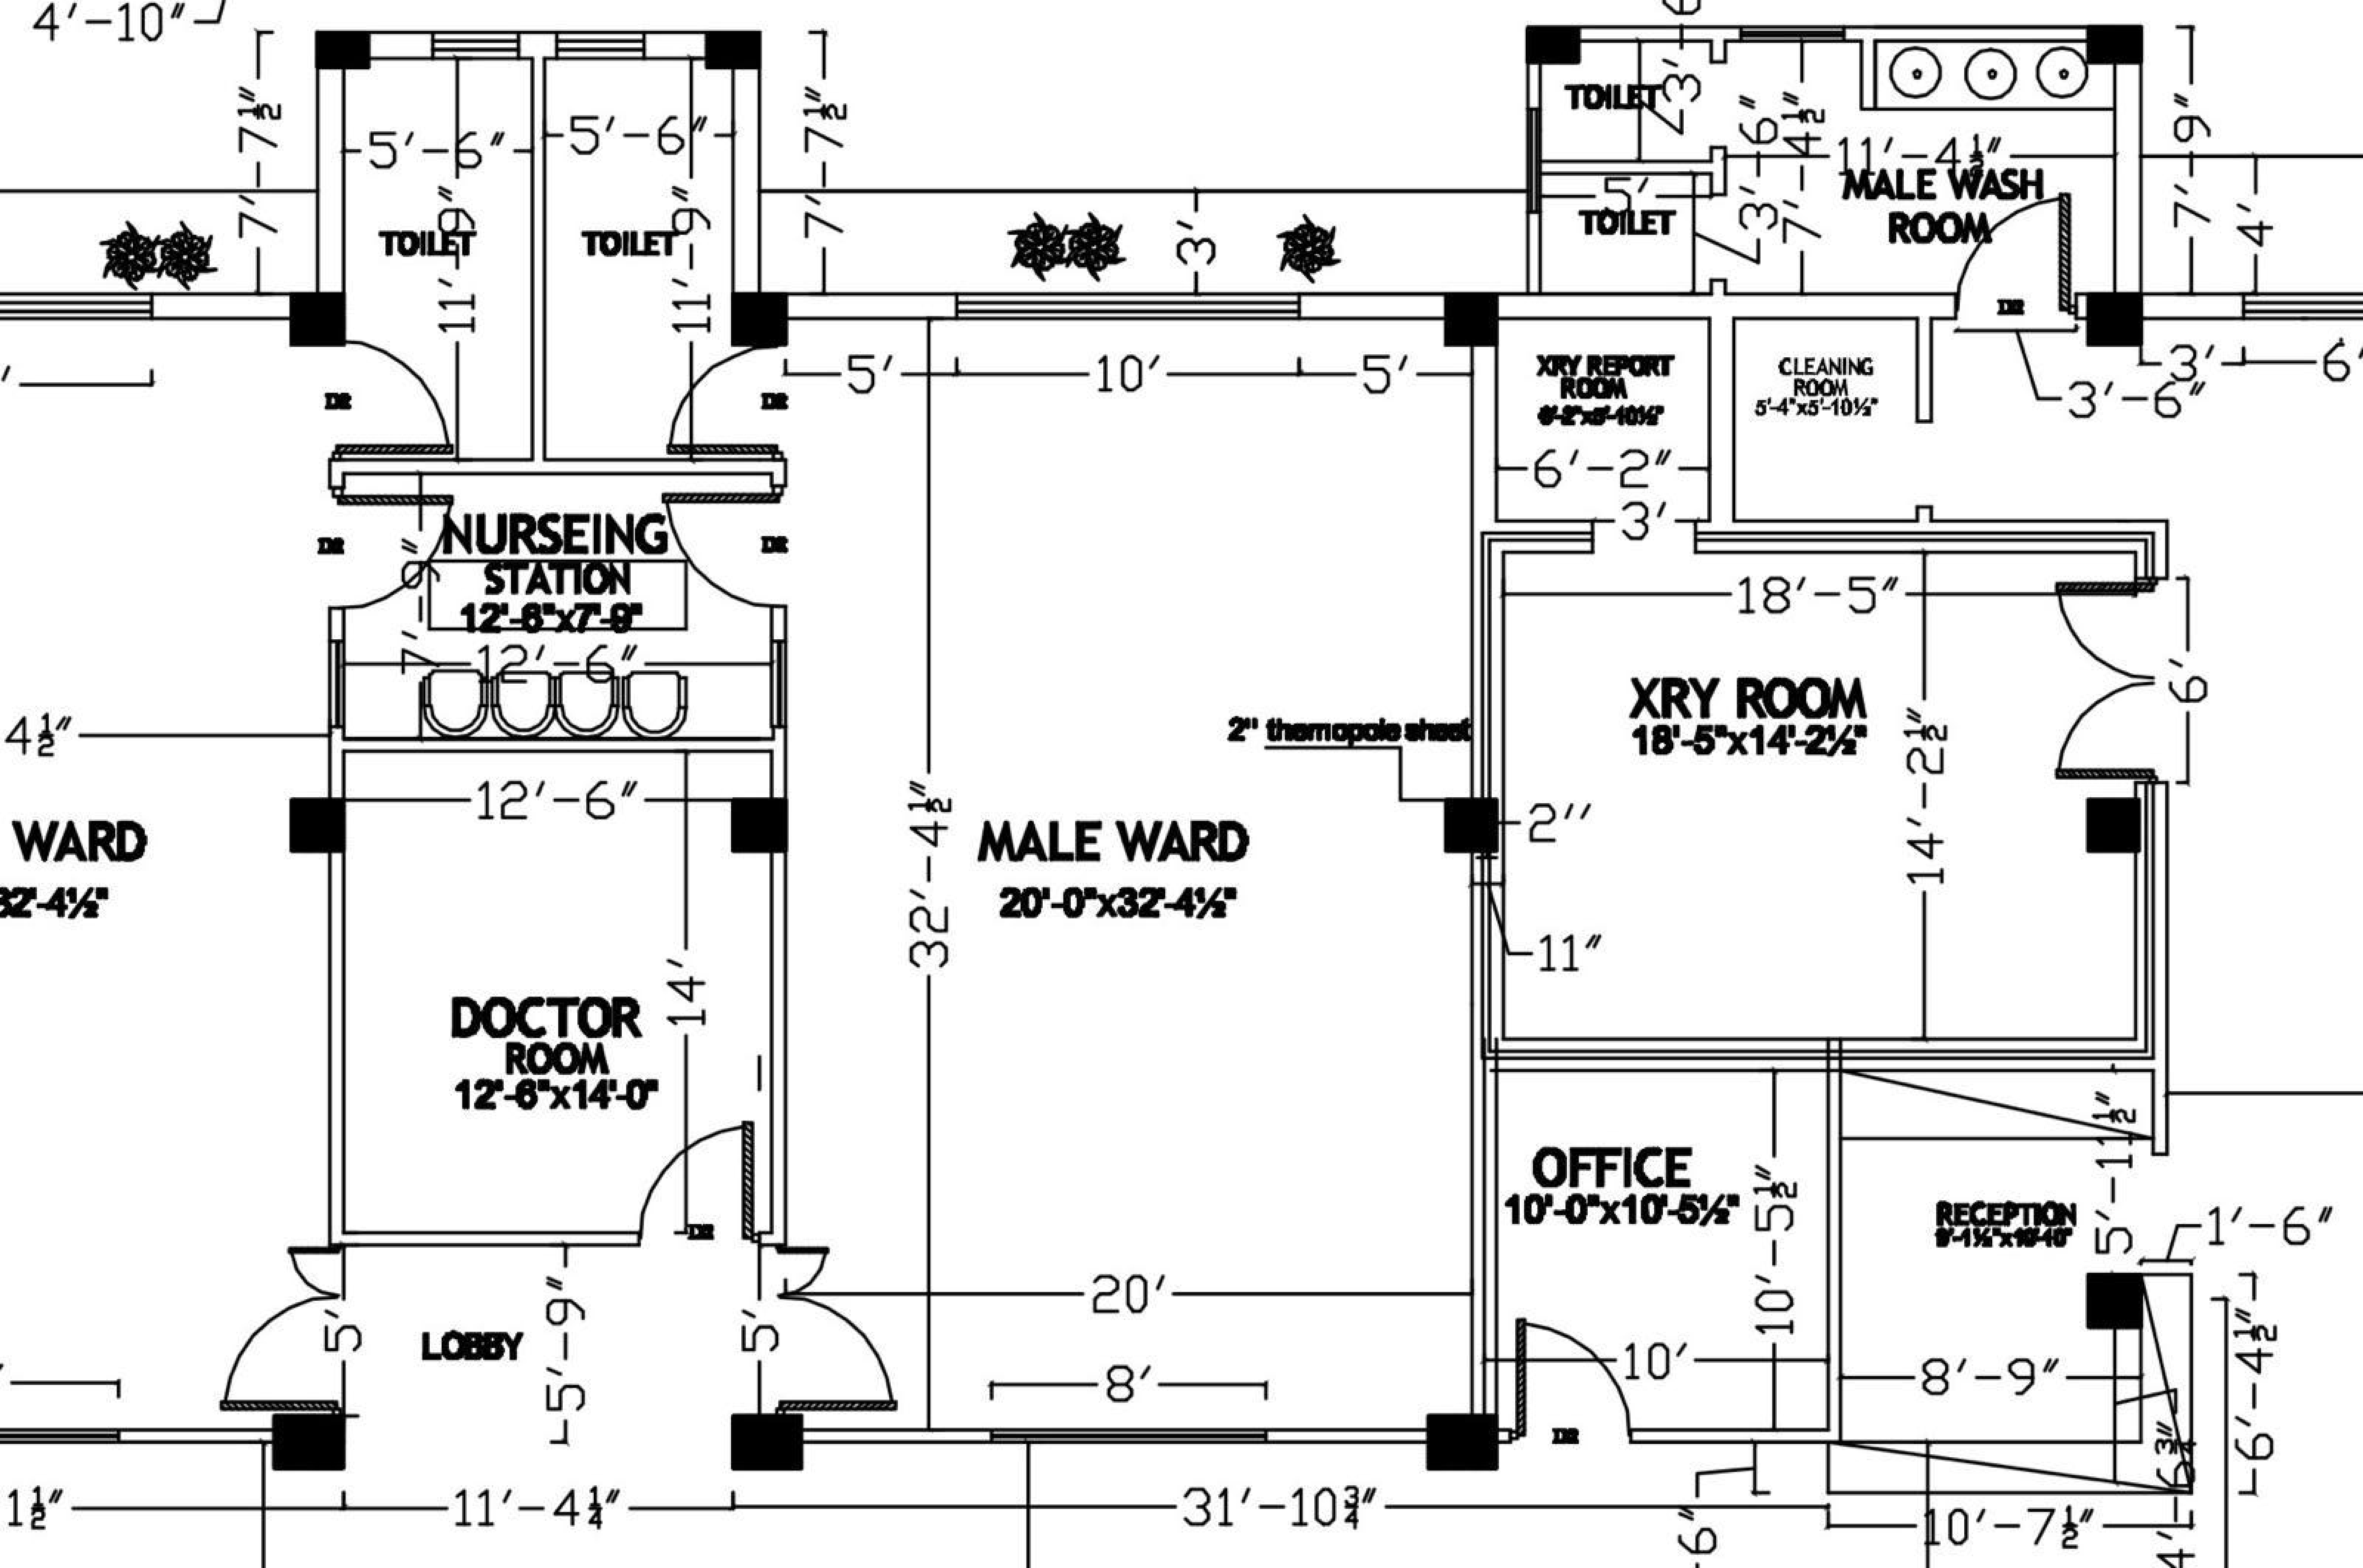
4'-10"
7'-7½"
5'-6"
5'-6"
7'-7½"
TOILET
TOILET
11'-9"
11'-9"
7'
7'
3'
TOILET
TOILET
5'
3'-6"
7'-4½"
11'-4½"
MALE WASH
ROOM
7'-9"
4'
3'
6'
3'-6"
DR
DR
DR
DR
DR
DR
DR
5'
10'
5'
XRY REPORT
ROOM
6'-2"x5'-10½"
CLEANING
ROOM
5'-4"x5'-10½"
6'-2"
3'
NURSEING
STATION
12'-6"x7'-9"
7'-9"
12'-6"
4½"
18'-5"
XRY ROOM
18'-5"x14'-2½"
6'
2" thermopole sheet
14'-2½"
2"
12'-6"
WARD
32'-4½"
32'-4½"
MALE WARD
20'-0"x32'-4½"
11"
DOCTOR
ROOM
12'-6"x14'-0"
14'
OFFICE
10'-0"x10'-5½"
10'-5½"
RECEPTION
9'-1½"x10'-10"
5'-11½"
1'-6"
20'
5'
5'-9"
LOBBY
5'
8'
10'
8'-9"
6'-4½"
6¾"
1½"
11'-4¼"
31'-10¾"
6"
10'-7½"
4'

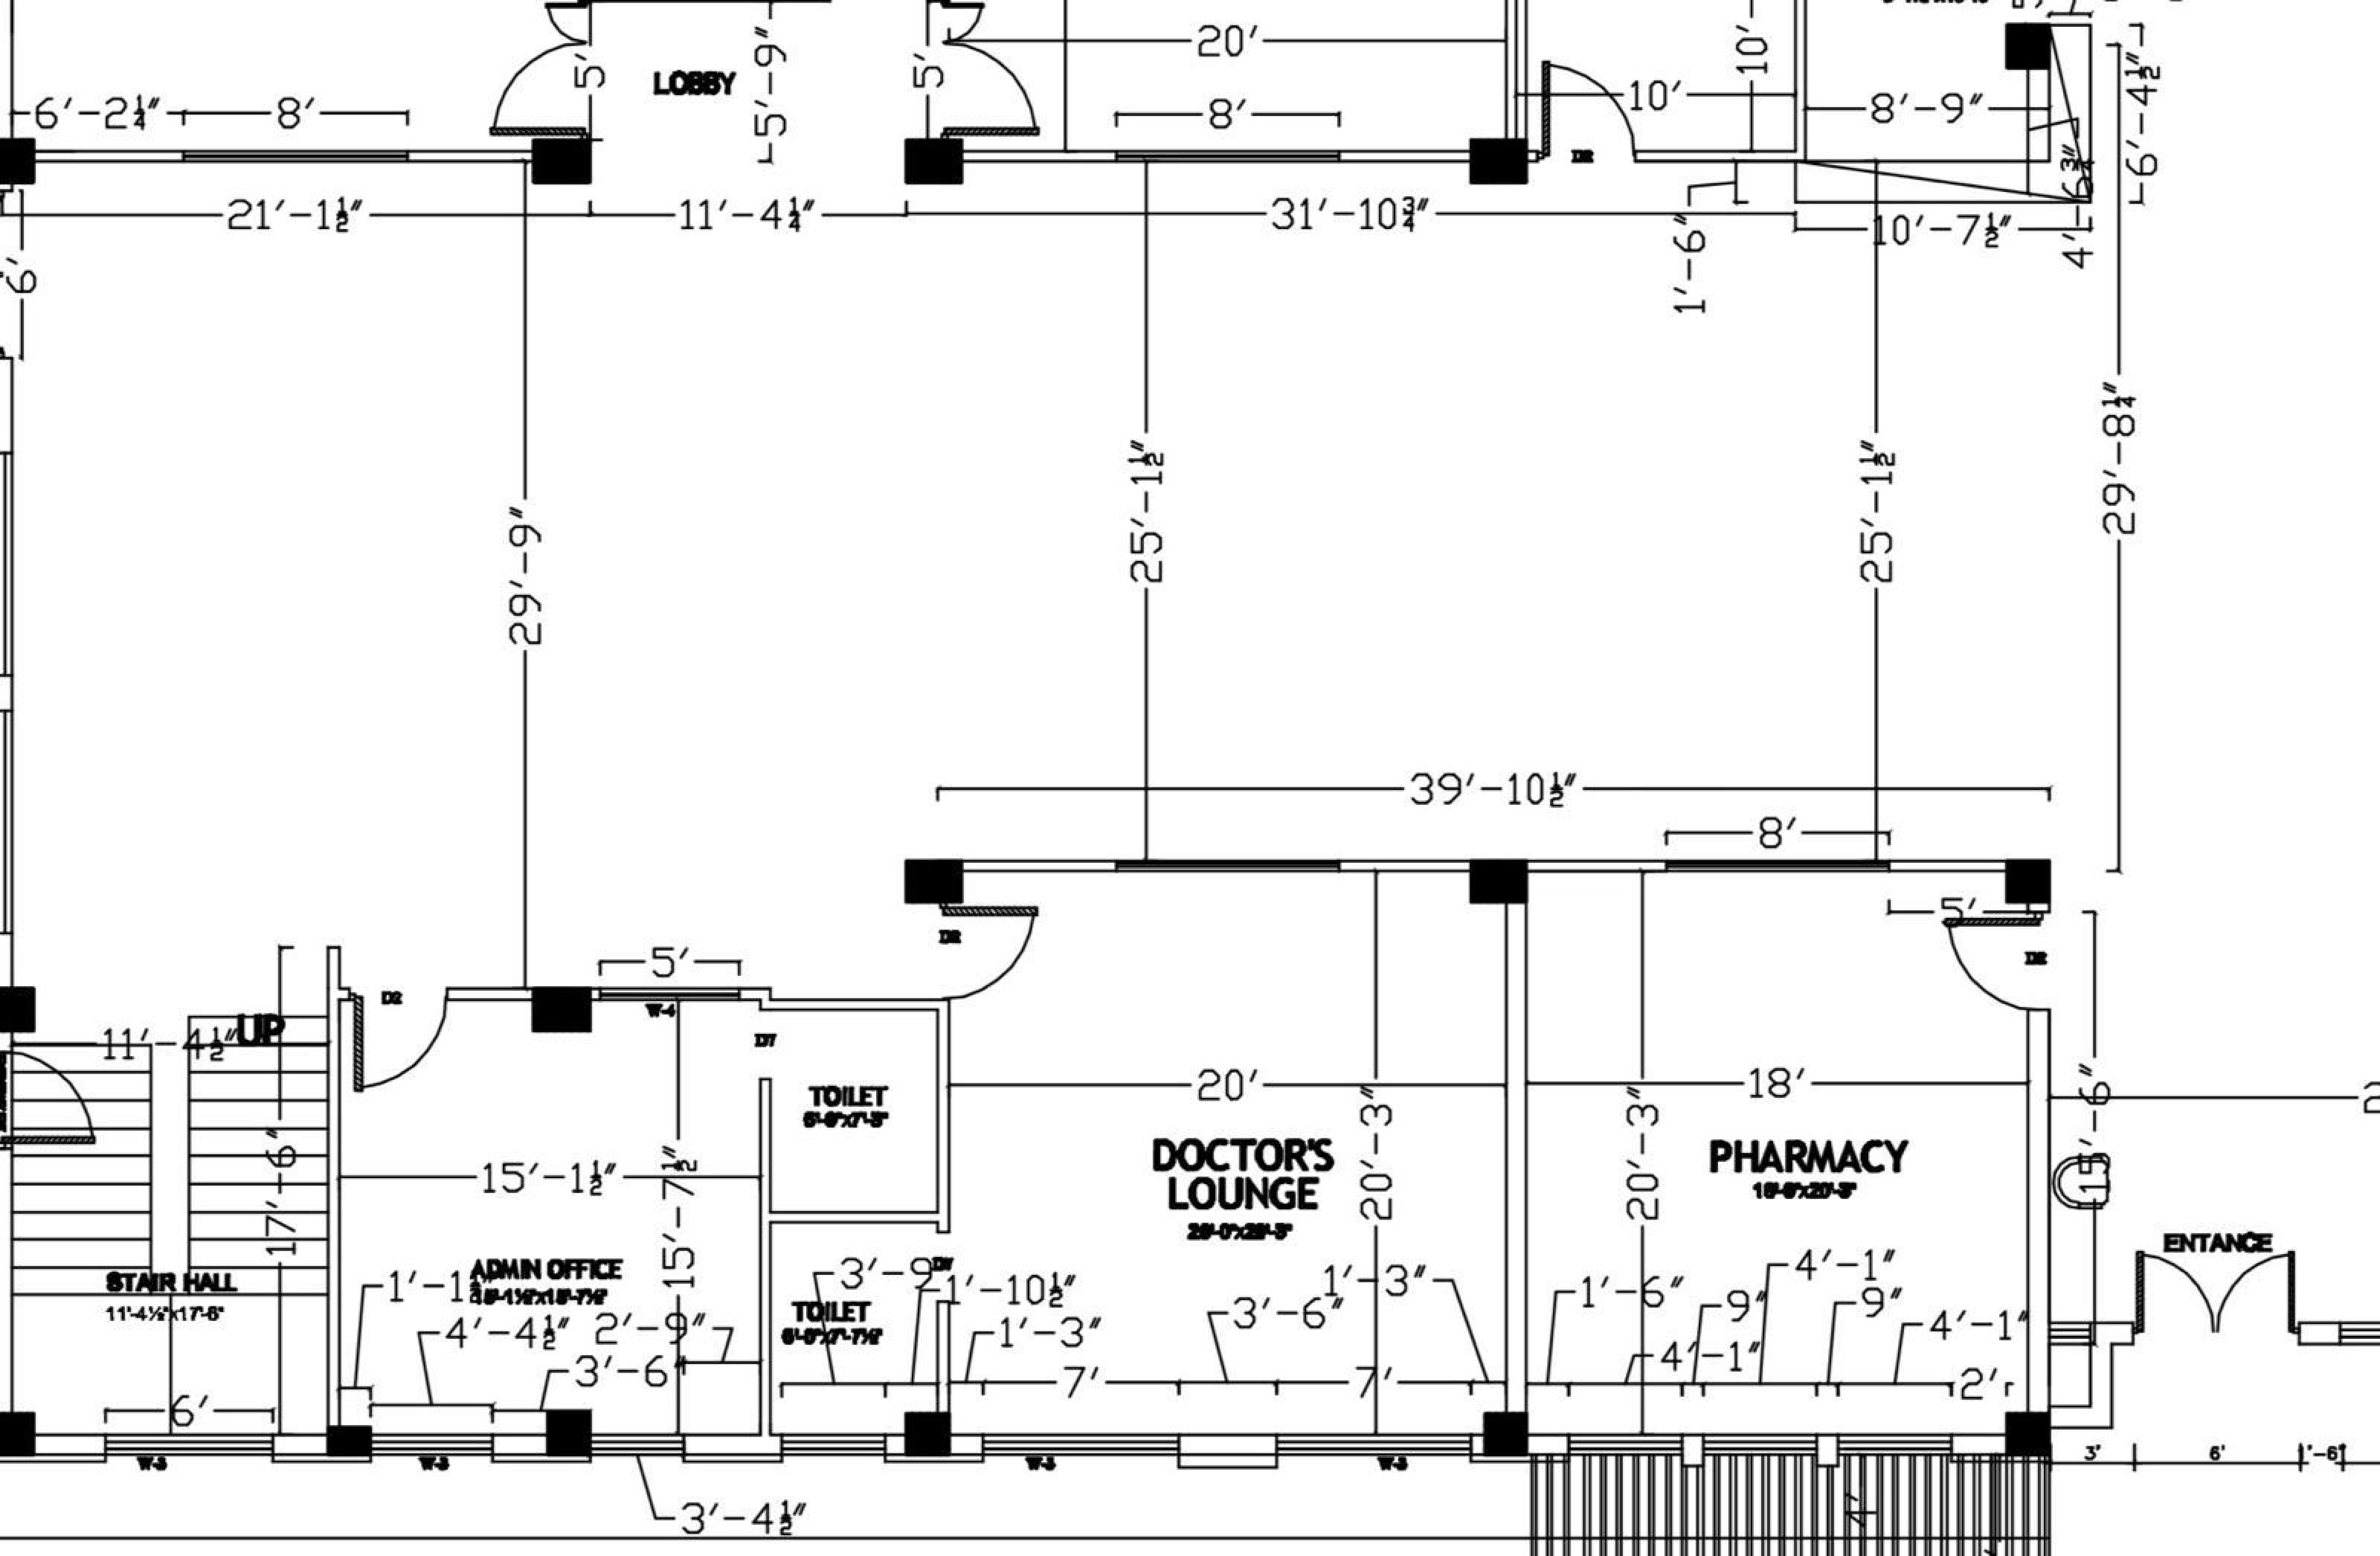
LOBBY
5'
5'-9"
5'
20'
8'
10'
10'
8'-9"
6'-4½"
6'-2¼"
8'
6'
21'-1½"
11'-4¼"
31'-10¾"
1'-6"
10'-7½"
4'
6¾"
DR
29'-9"
25'-1½"
25'-1½"
29'-8¼"
39'-10½"
8'
5'
DR
DR
5'
D2
D7
W-4
11'-4½"
UP
17'-6"
15'-1½"
15'-7½"
TOILET
6'-6"x7'-5"
DOCTOR'S
LOUNGE
20'-0"x20'-3"
20'
20'-3"
PHARMACY
18'-6"x20'-3"
18'
20'-3"
15'-6"
ENTANCE
STAIR HALL
11'-4½"x17'-6"
ADMIN OFFICE
15'-1½"x15'-7½"
1'-1"
4'-4½"
2'-9"
3'-6"
TOILET
6'-6"x7'-7½"
3'-9"
D7
1'-10½"
1'-3"
7'
3'-6"
1'-3"
7'
1'-6"
9"
4'-1"
4'-1"
9"
4'-1"
2'
6'
W-3
W-3
W-3
W-3
3'-4½"
3'
6'
1'-6"
4'

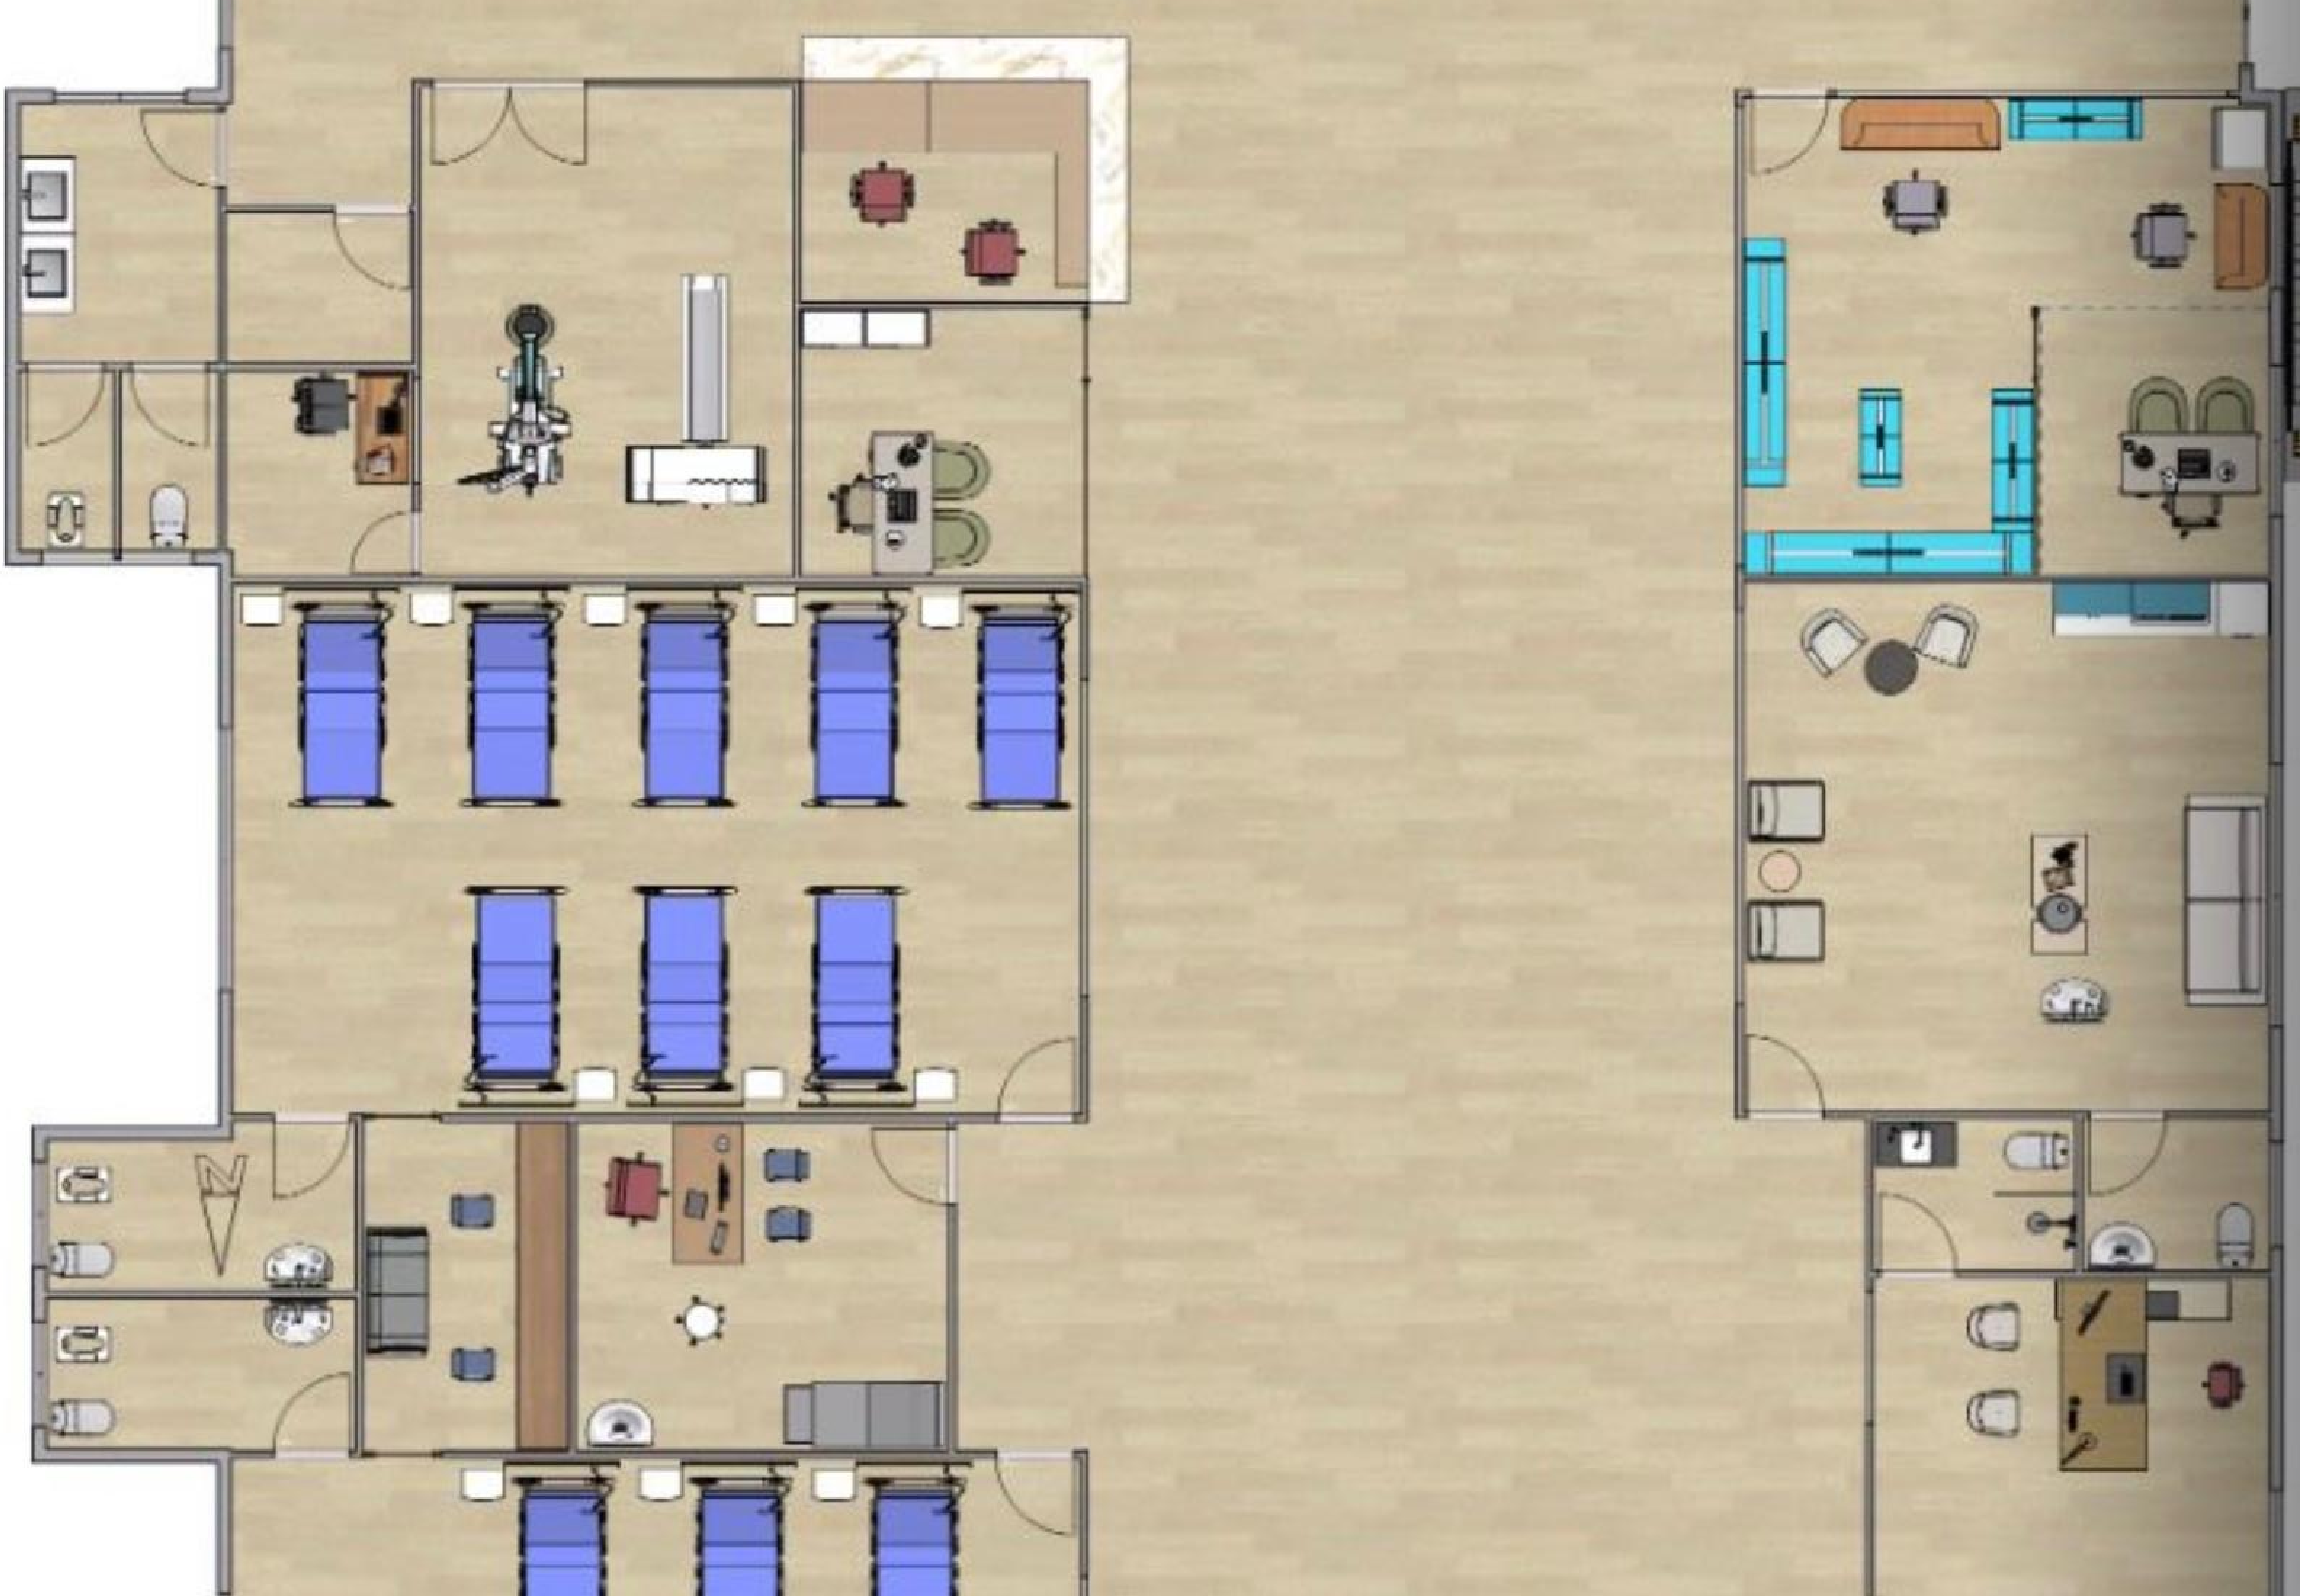
N

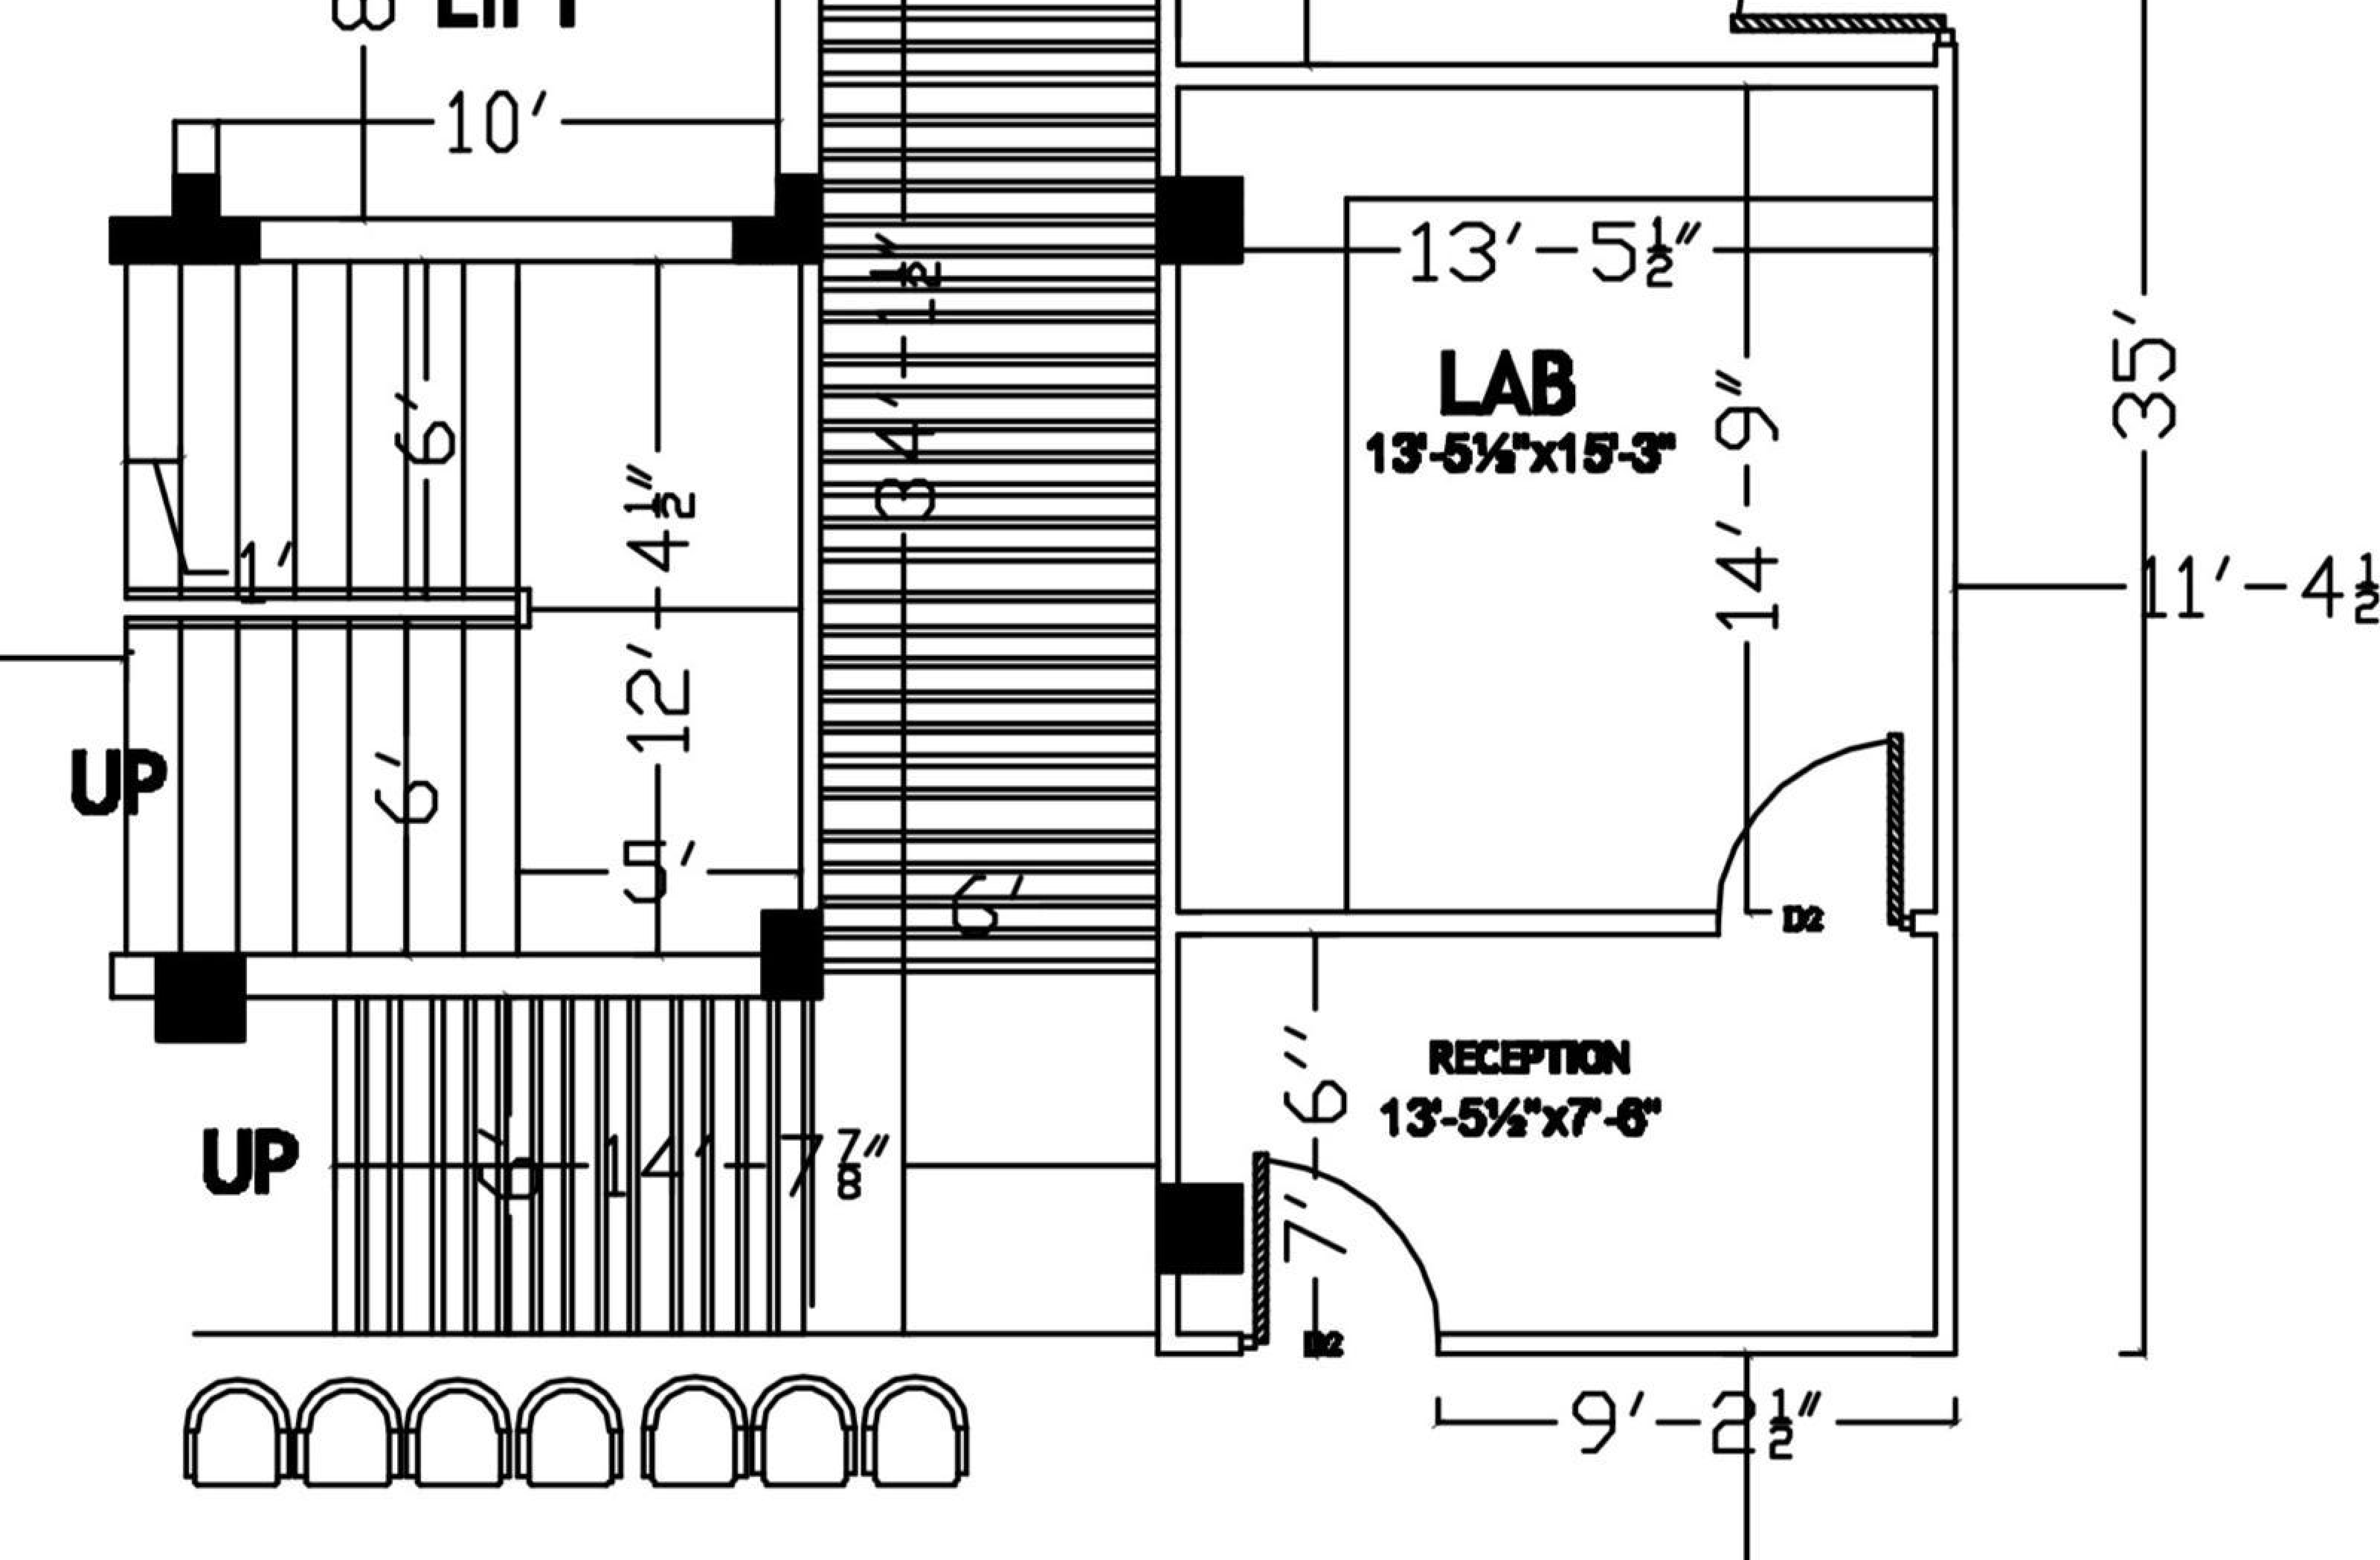
10′
UP
6′
1′
6′
12′-4½″
5′
34′-1½″
6′
UP
14′-7⅞″
LAB
13′-5½″x15′-3″
13′-5½″
14′-9″
35′
11′-4½
D2
RECEPTION
13′-5½″x7′-6″
7′-6″
D2
9′-2½″