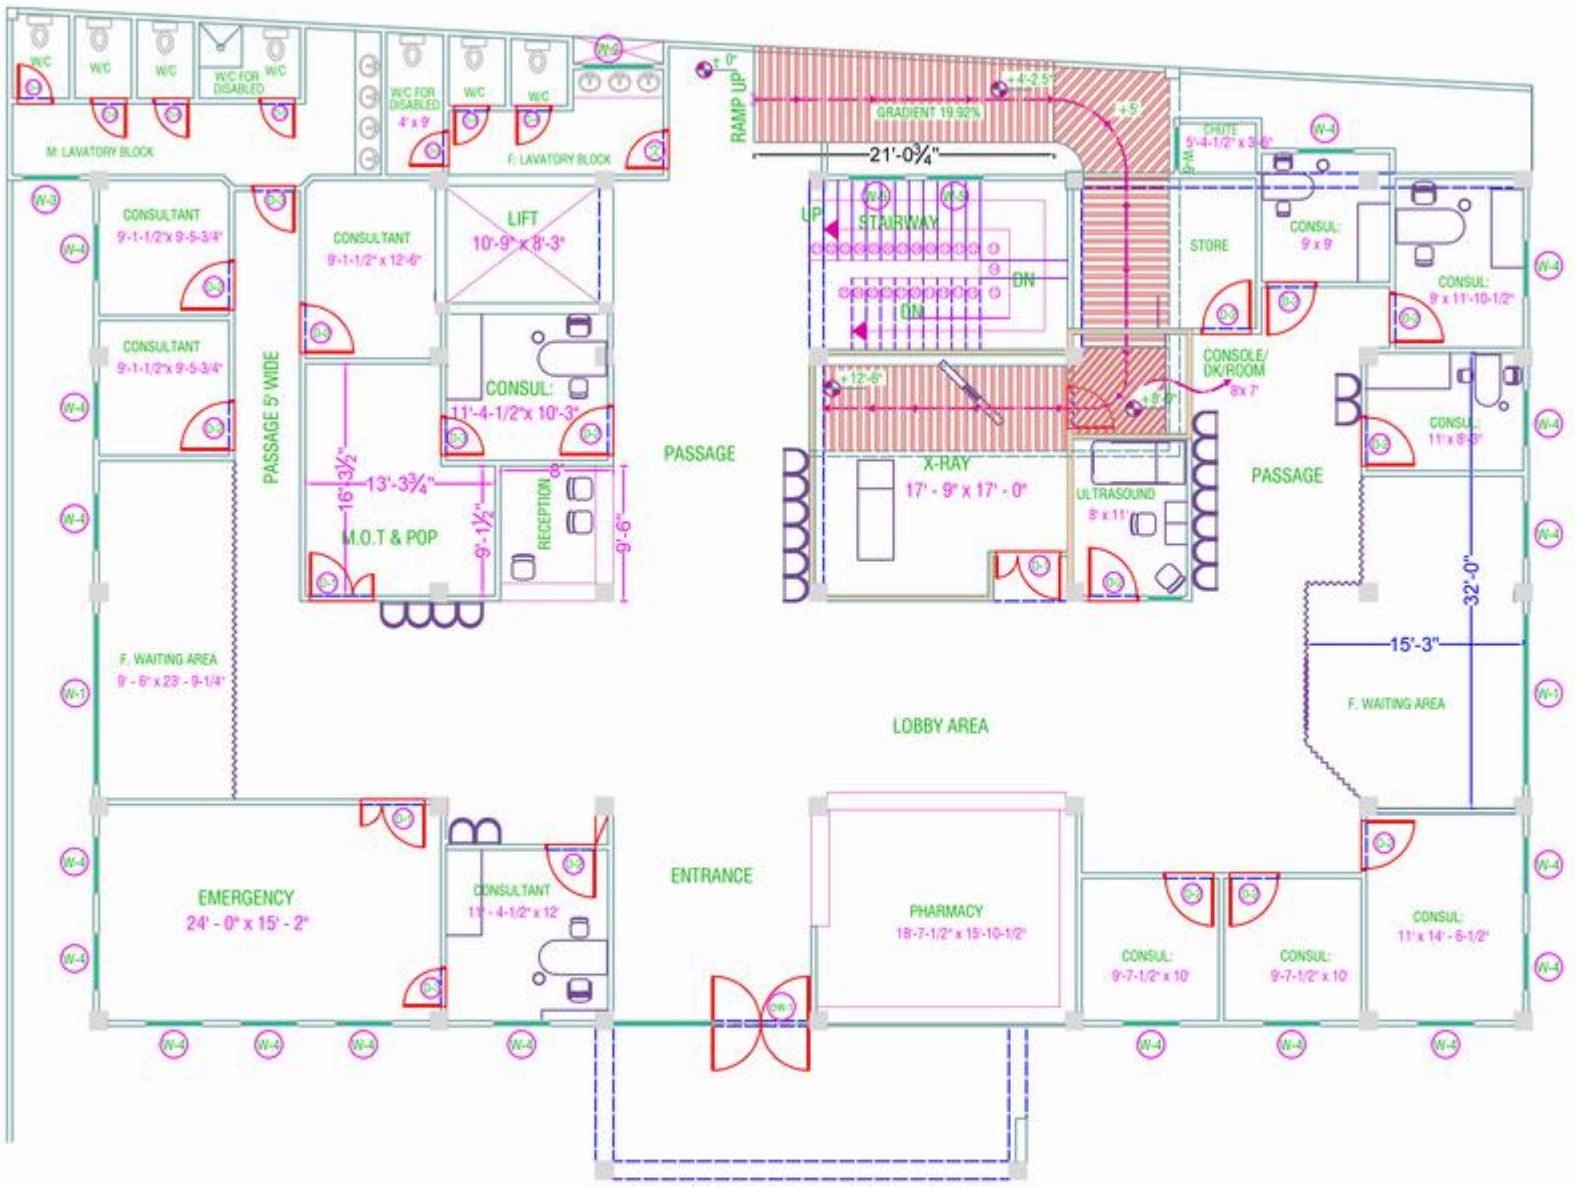


SCHEDULE OF OPENING

GROUND FLOOR PLAN

S/#	TYPE	SIZE	MATERIAL	S/LEVEL	QTY
01	DW-1	6'-10"/6'-11" x 8'-6"/8'	UPVC	± 0'-0"	01
02	D-1	4'-6" x 7'-0"	WOODEN	± 0'-0"	03
03	D-2	3'-6" x 7'-0"	WOODEN	± 0'-0"	13
04	D-3	3'-0" x 7'-0"	WOODEN	± 0'-0"	05
05	D-4	2'-6" x 7'-0"	UPVC	± 0'-0"	05
06	D-4	2'-6" x 7'-0"	UPVC	± 0'-0"	05
07	D-5	2'-9" x 7'-0"	UPVC	± 0'-0"	02
08	W-1	11'-0" x 7'-0"	UPVC	± 0'-6"	02
09	W-2	5'-0" x 5'-0"	UPVC (F. LEV. BLOCK)	± 0'-6"	01
10	W-3	4'-0" x 5'-6"	UPVC	± 3'-6"	02
11	W-4	4'-0" x 6'-0"	UPVC	± 2'-6"	20
12	W-5	4'-0" x A.P.S	UPVC (STAIR W.)	± A.P.S	02
13	W-6	3'-0" x A.P.S	UPVC (CHUTE W.)	± A.P.S	01

SCALE: NOT TO SCALE

All rights reserved. No part of this drawing may be circulated, reproduced, stored in retrieval system or transmitted in any form by means, mechanical, Photocopying, recording, or otherwise without the prior permission of SWAT ENGINEERING CONSULTANCY(SEC) SOFT COPY(CAD & PDF) OF THIS DRAWING IS NOT ALLOWED TO CLIENT. THIS DRAWING FILE/MAP IS NOT VALID FOR COURT.

THIS DRAWING IS THE PROPERTY OF SWAT ENGINEERING CONSULTANCY (SEC)

REV. NO.	DATE	DRWN	CHKD	REMARKS
5				
4	MAY 11TH,2025			
3	FEB 04TH,2025	ENGR. KAMRAN KHAN		
2	APR 14TH,2024	ARCH. RIAZ AHMAD		
1	APR. 8TH, 2024	WAQAR KHAN	ENGRT. LAL ZARIN	

DESIGNED BY: SWAT ENGINEERING CONSULTANCY TEAM
DRAWN BY: ENGR. KAMRAN KHAN, ARCH. RIAZ AHMAD & WAQAR KHAN
SURVEYED BY:
C.CHK'D BY: ENGRT. LAL ZARIN
DATE: JANUARY 13 -2024

SWAT ENGINEERING CONSULTANCY
DESIGNERS (ARCHITECTURAL, STRUCTURAL,) TOWN PLANNERS, SURVEYORS, BUILDERS, MEP DESIGNERS & INTERIOR.
Sheraz Gemstones Center 2nd Floor Block B-106 Watkay Mingora Swat K.P.K Pakistan.
E-Mail: swatengr.consultancy@gmail.com
Tel: No. 811704
Cell No: 0335-910-2424, 0300-910-2424 & 0310-910-2424.

PROJECT: COMMERCIAL

OWNERSHIP: BR. BAHADAR ALI

TITLE : GROUND FLOOR PLAN (LEVEL 02)

LOCATION : TETABAT KHWAZAKHEELA SWAT

PROJECT NO. H-11885 - 23

SHEET NO : A - 040

www.secswat.com
Email.
swatengr.consultancy@gmail.com