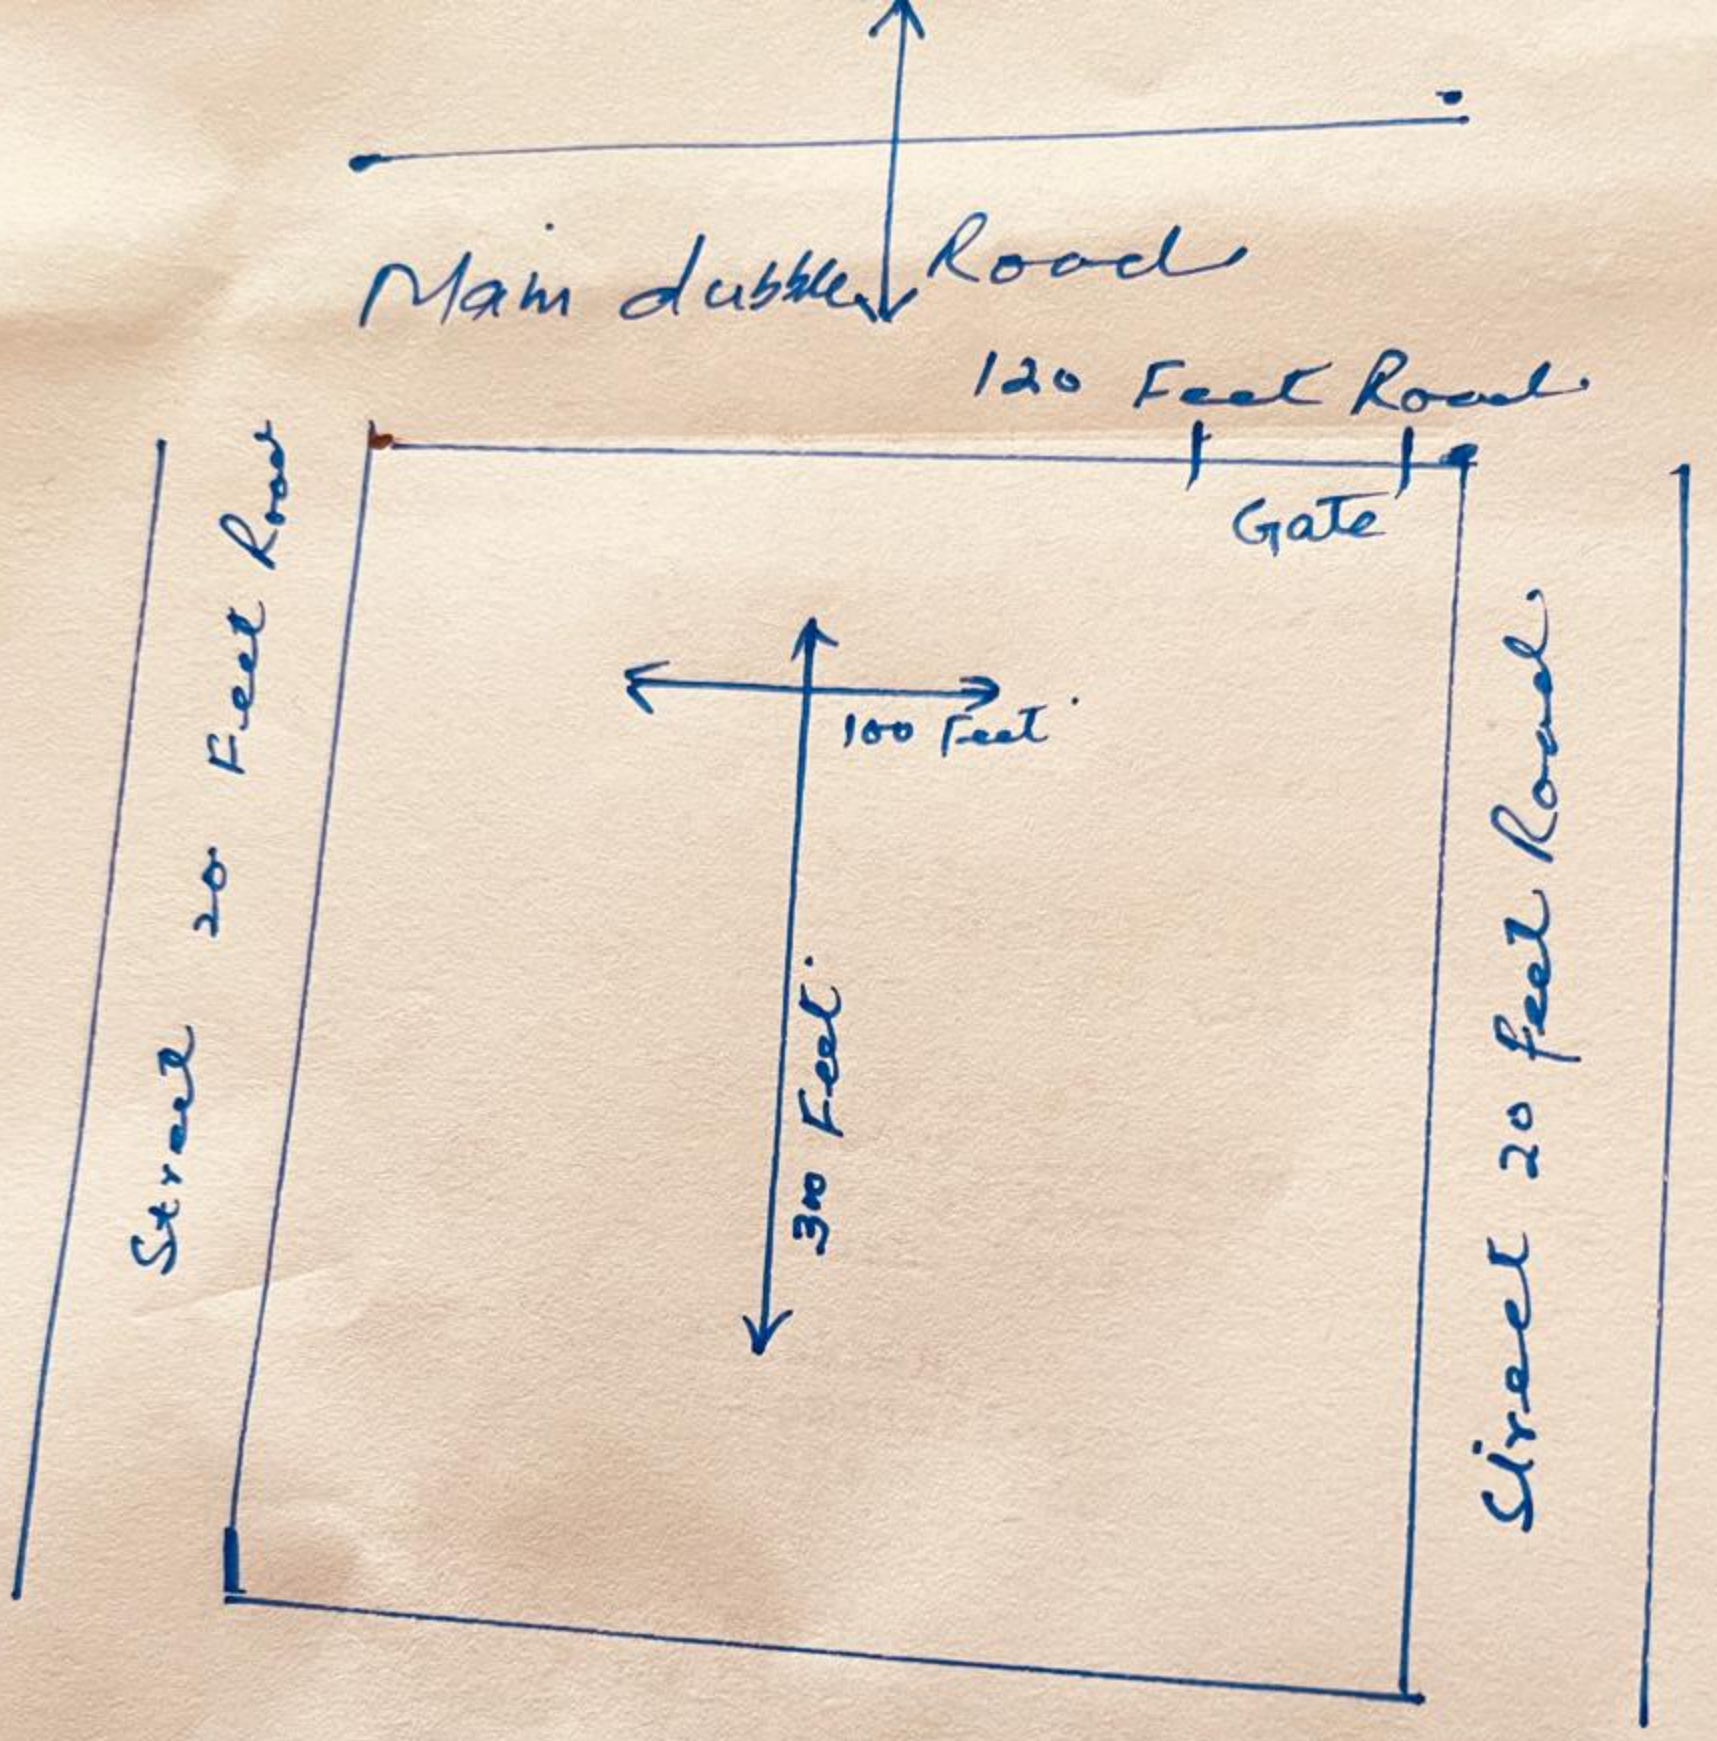
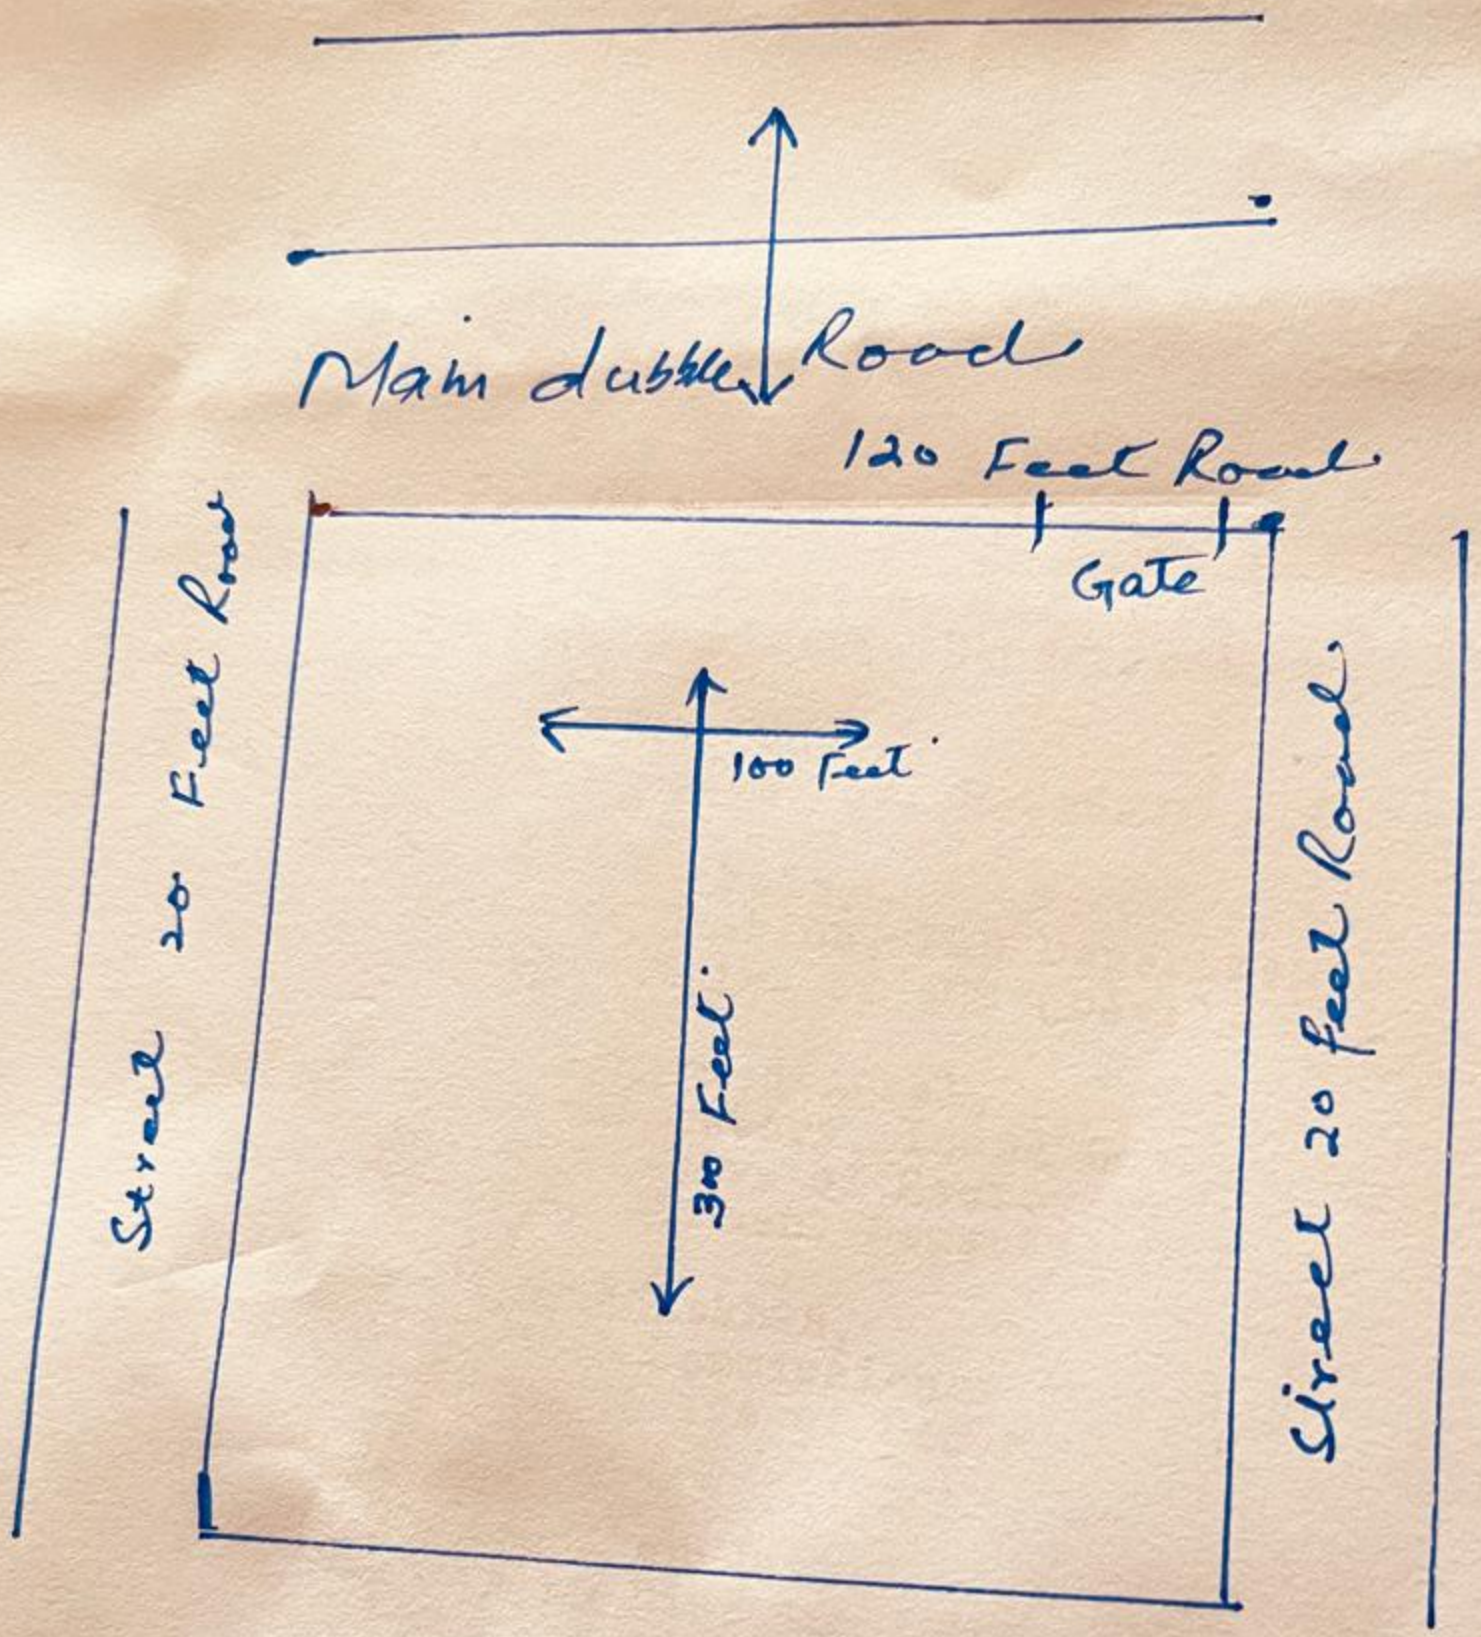

Main dubble Roode
120 Feet Roode
Gate
Street 20 Feet Roode
100 Feet
30 Feet
Street 20 Feet Roode


Main dubble Road
120 Feet Road
Gate
100 Feet
30 Feet
Street 20 Feet Road
Street 20 Feet Road