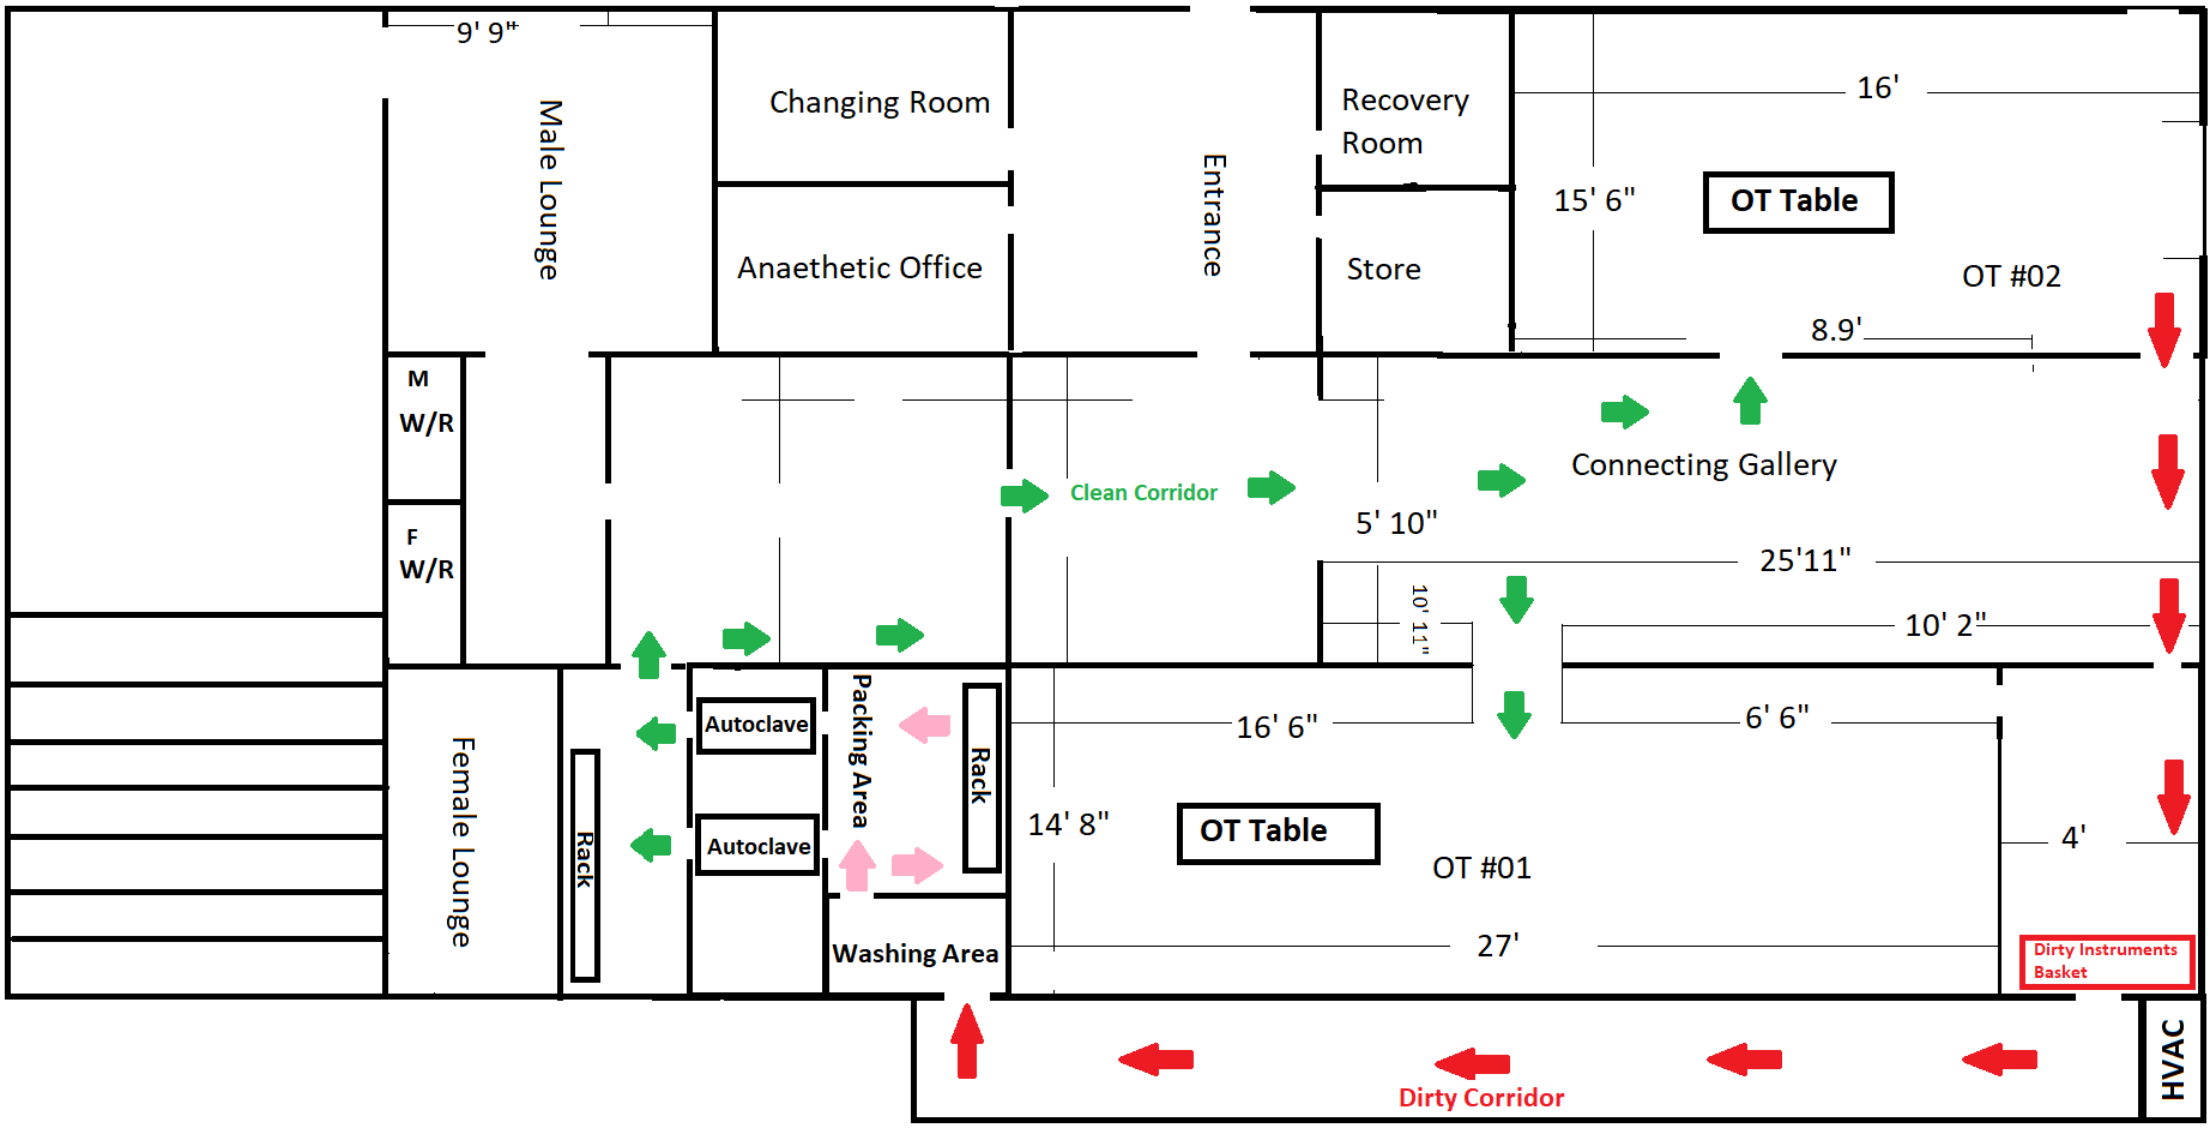
9' 9"
Male Lounge
Changing Room
Anaethetic Office
Entrance
Recovery Room
Store
16'
15' 6"
OT Table
OT #02
8.9'
M W/R
F W/R
Clean Corridor
Connecting Gallery
5' 10"
25'11"
10' 11"
10' 2"
Female Lounge
Rack
Autoclave
Autoclave
Packing Area
Rack
16' 6"
6' 6"
14' 8"
OT Table
OT #01
4'
Washing Area
27'
Dirty Instruments Basket
HVAC
Dirty Corridor