Restoran

SOULed O
3x

Lift To Hotel Room

AED

Lift To Hotel Room

E.D.C.O

ENGINEERING **DESIGNING**

CONSTRUCTION OFFICIAL

Architecture | Engineer | Consultants

Office # 305, D.H.A Phase II ext Bali Business Karachi Consult:-0312-2118445 edco.construction24official@gmail.com

Planning | Interior Design | Exterior Design | Structure Design

DR. ROHAN
DRAWING 321 SQ.YARD
GROUND + THREE & ROOF
PLOT NO....
KARACHI
DESIGN BY
E.D.C.O
ARCHITECTURAL STUDIO

GENERAL NOTES:

1. THE COPYRIGHT OF THIS DRAWING IS VESTED IN YourSpreadsheets AND IT MAY NOT BE REPRODUCED IN WHOLE OR PART OR USED FOR THE MANUFACTURE OF ANY ARTICLE WITHOUT THE EXPRESS PERMISSION OF THE COPYRIGHT HOLDERS.
2. WORK TO FIGURED DIMENSIONS ONLY.
3. THIS DRAWING IS TO BE READ IN CONJUNCTION WITH ALL RELEVANT ARCHITECT'S, SERVICE ENGINEER'S AND YourSpreadsheets DRAWINGS .

ALL DRWAING ARE THE PROPOERTY OF THE DESIGNER & THEY ARE NOT TO BE REPRODUCED IN WHOLE OR IN PART WITHOUT WRITTEN CONSENT FROM THE DESIGN WING

CONTRACTOR TO CHECK &VERIFY ALL DIMENSIONS BEFORE COMMENCING WORK & TO REPORT ANY DISCREPANCIES TO THE DESIGN WING.
DO NOT SCALE DRAWINGS.
ALL CONSTRUCTION TO BE ACCORDING TO BEST COMMON PRACTICE.

REV:	DESCRIPTION:	BY:	DATE:
A	ARCHITECTURE DRAWING	----	25-12-25
B	STRUCTURE DRAWING	----	27-12-25

PROJECT NAME:
300 SQ.YARD HOUSE ARCHITECTURE DRAWING

SIGNATURE BY:

DRAWING TITLE:
ARCHITECTURAL DRAWING

DRAWN BY: MUDASSIR
CHECKED BY: M.SHEHERYAR
APPROVED BY: M.SHEHERYAR
DATE: 27-DEC-2025

CLIENT
MR. ROHAN
KARACHI...

DESIGNED BY:-

E.D.C.O
ENGINEERING **DESIGNING**
CONSTRUCTION OFFICIAL

ARCHITECT| PLANNERS| ENGINEERS| INTERIOR| B.O.Q| EXTERIOR| CONSULT| STRUCTURE DESIGN| PLANNING| LAND SURVEY| CONSTRUCTION| 3D ANIMATION VIDEO| RENOVATION|
MUHAMMAD SHEHERYAR
CONTACT- 0312-2118445|D.H.A PHASE VII

PROJECT NO: AR-7590
SCALE: 1/8"=1'-0"
SHEET SIZE: A3
DRAWING NO: ARC
SHEET NO ----------
REVISION: YES
UNIT: INCHES&FEET

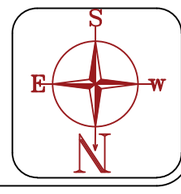

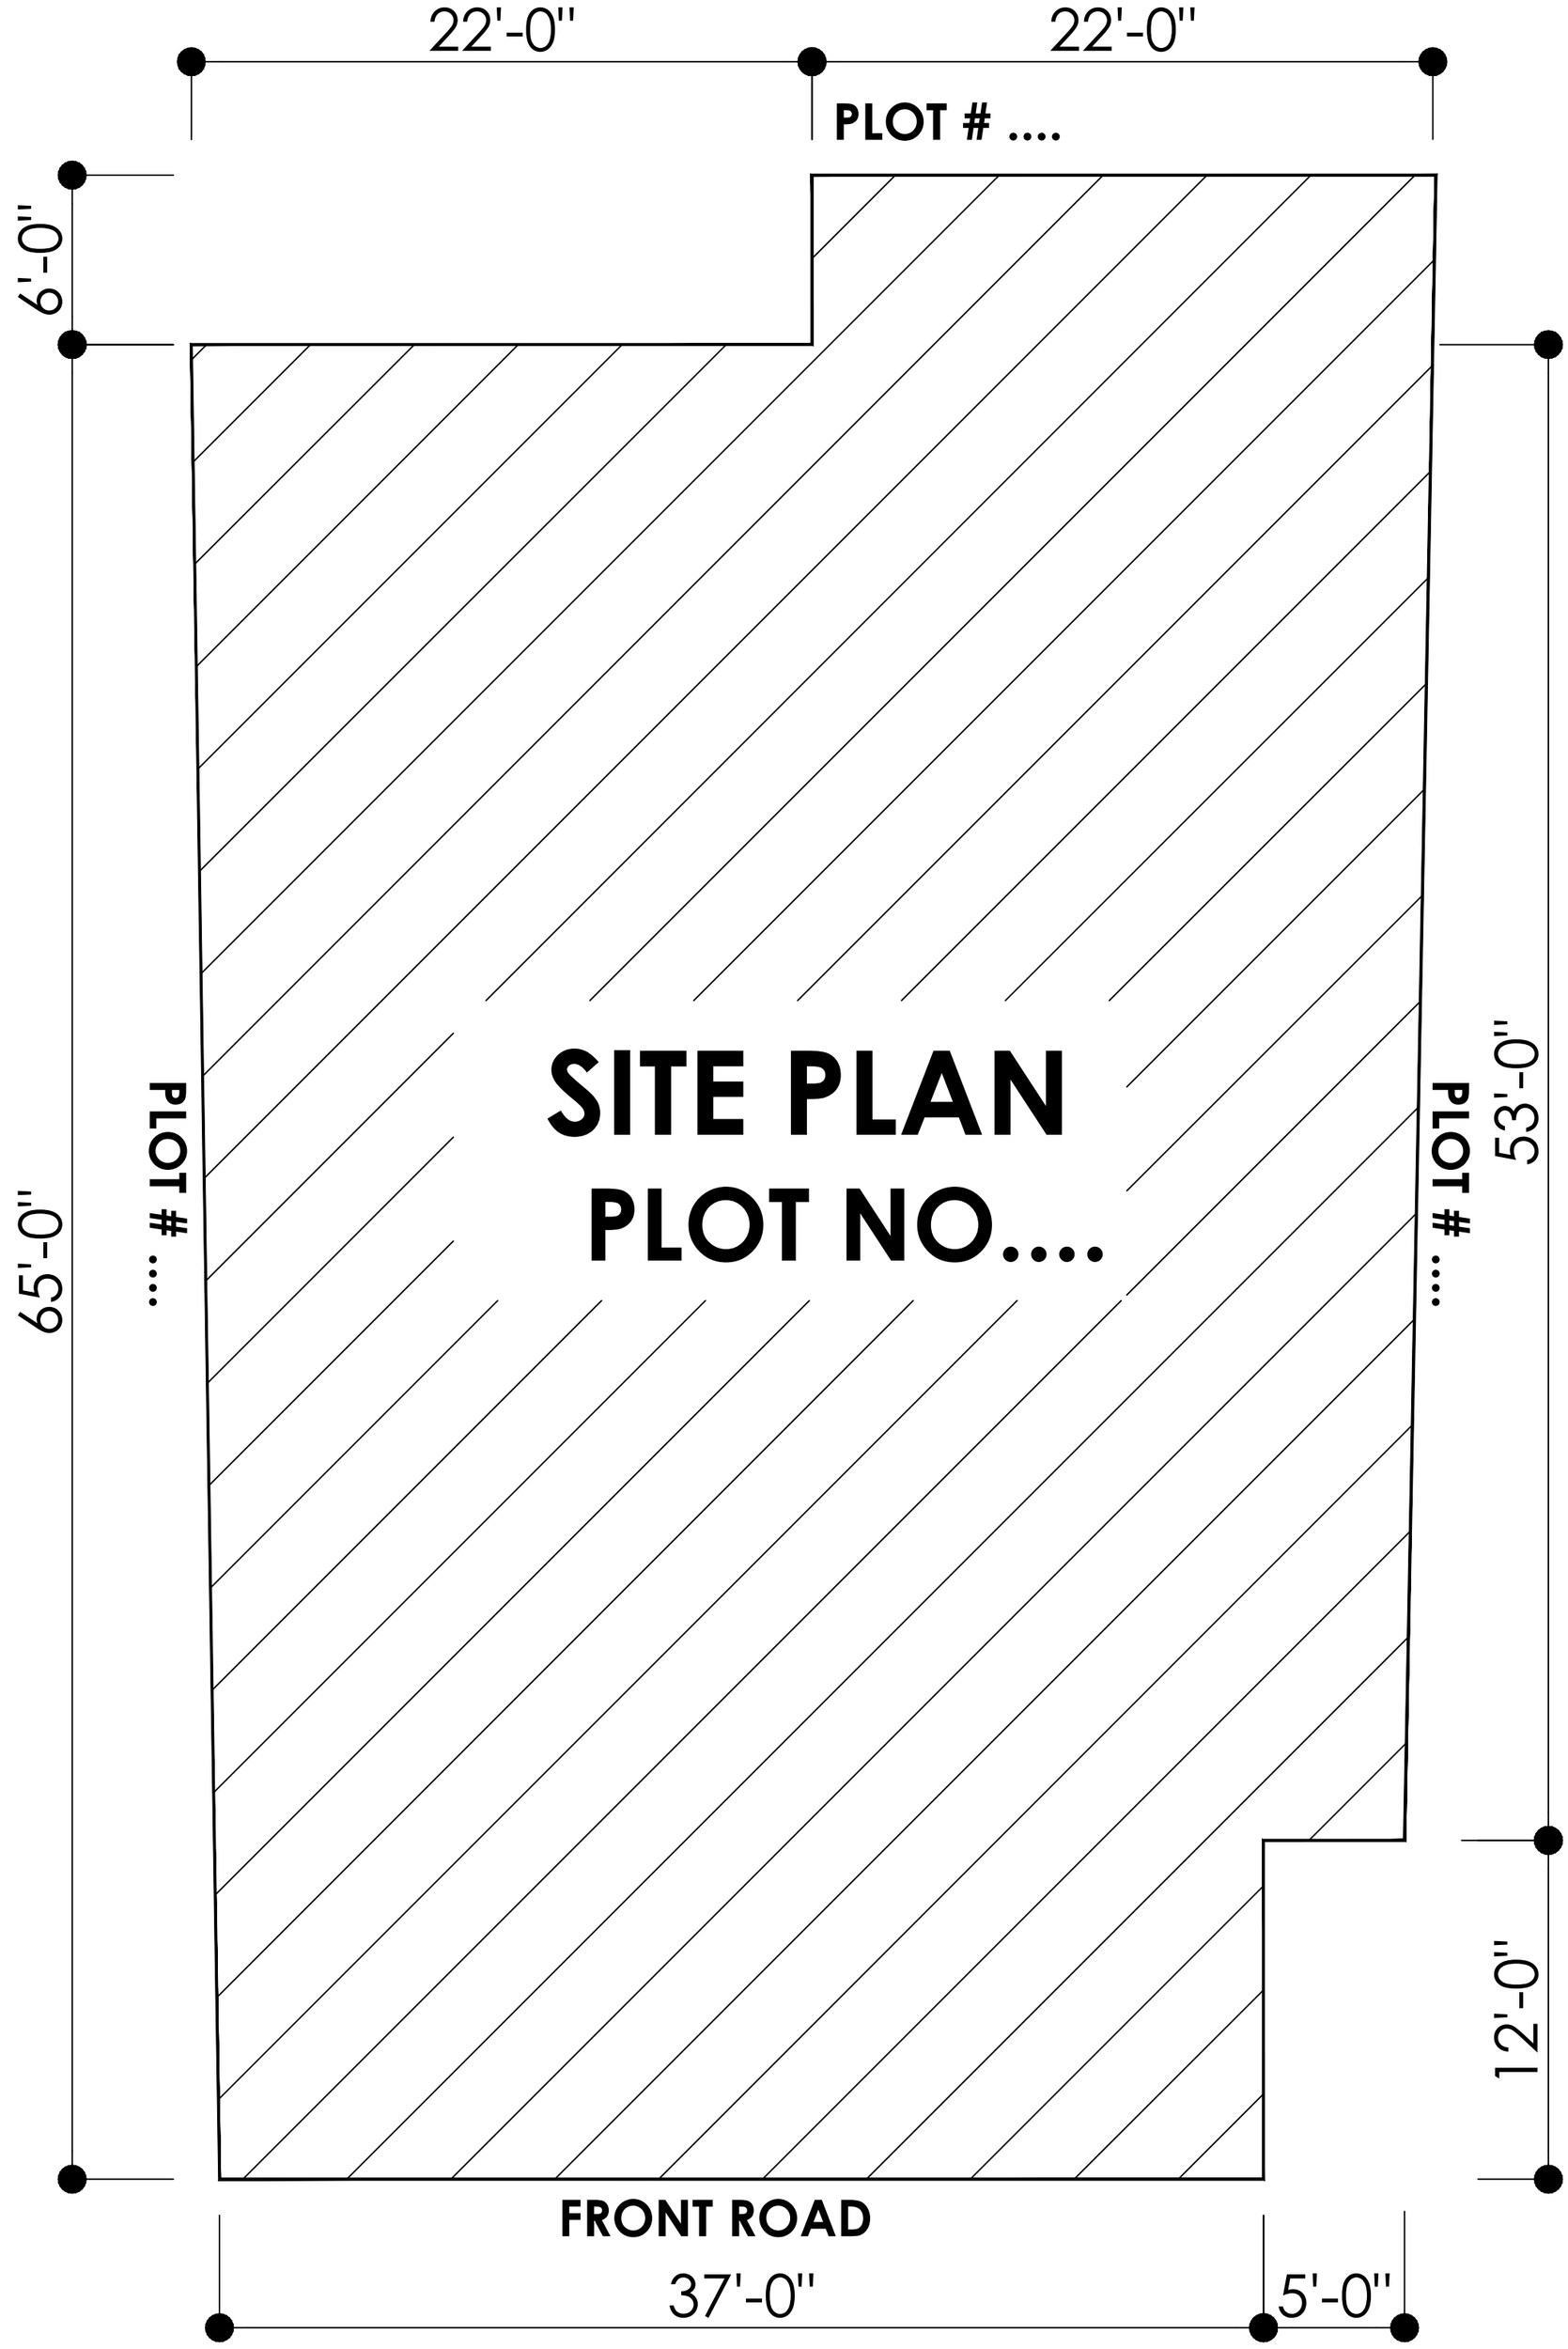

GENERAL NOTES:

1. THE COPYRIGHT OF THIS DRAWING IS VESTED IN YourSpreadsheets AND IT MAY NOT BE REPRODUCED IN WHOLE OR PART OR USED FOR THE MANUFACTURE OF ANY ARTICLE WITHOUT THE EXPRESS PERMISSION OF THE COPYRIGHT HOLDERS.
2. WORK TO FIGURED DIMENSIONS ONLY.
3. THIS DRAWING IS TO BE READ IN CONJUNCTION WITH ALL RELEVANT ARCHITECT'S, SERVICE ENGINEER'S AND YourSpreadsheets DRAWINGS .

ALL DRWAING ARE THE PROPOERTY OF THE DESIGNER & THEY ARE NOT TO BE REPRODUCED IN WHOLE OR IN PART WITHOUT WRITTEN CONSENT FROM THE DESIGN WING

CONTRACTOR TO CHECK &VERIFY ALL DIMENSIONS BEFORE COMMENCING WORK & TO REPORT ANY DISCREPANCIES TO THE DESIGN WING.

DO NOT SCALE DRAWINGS.

ALL CONSTRUCTION TO BE ACCORDING TO BEST COMMON PRACTICE.

REV:	DESCRIPTION:	BY:	DATE:
A	ARCHITECTURE DRAWING	----	25-12-25
B	STRUCTURE DRAWING	----	27-12-25

PROJECT NAME:
300 SQ.YARD HOUSE
ARCHITECTURE DRAWING

SIGNATURE BY:

DRAWING TITLE:
ARCHITECTURAL DRAWING

DRAWN BY: MUDASSIR

CHECKED BY: M.SHEHERYAR

APPROVED BY: M.SHEHERYAR

DATE: 27-DEC-2025

CLIENT
MR. ROHAN
KARACHI...

DESIGNED BY:-

E.D.C.O
ENGINEERING DESIGNING CONSTRUCTION OFFICIAL
ARCHITECT| PLANNERS| ENGINEERS| INTERIOR| B.O.Q| EXTERIOR| CONSULT| STRUCTURE DESIGN| PLANNING| LAND SURVEY| CONSTRUCTION| 3D ANIMATION VIDEO| RENOVATION|
MUHAMMAD SHEHERYAR
CONTACT- 0312-2118445|D.H.A PHASE VII

PROJECT NO: AR-7590

SCALE: 1/8"=1'-0"

SHEET SIZE: A3

DRAWING NO: ARC

SHEET NO ----------

REVISION: YES

UNIT: INCHES&FEET

S E W N

ARCHITECTURE

DRAWING

GENERAL NOTES:

1. THE COPYRIGHT OF THIS DRAWING IS VESTED IN YourSpreadsheets AND IT MAY NOT BE REPRODUCED IN WHOLE OR PART OR USED FOR THE MANUFACTURE OF ANY ARTICLE WITHOUT THE EXPRESS PERMISSION OF THE COPYRIGHT HOLDERS.
2. WORK TO FIGURED DIMENSIONS ONLY.
3. THIS DRAWING IS TO BE READ IN CONJUNCTION WITH ALL RELEVANT ARCHITECT'S, SERVICE ENGINEER'S AND YourSpreadsheets DRAWINGS .

ALL DRWAING ARE THE PROPOERTY OF THE DESIGNER & THEY ARE NOT TO BE REPRODUCED IN WHOLE OR IN PART WITHOUT WRITTEN CONSENT FROM THE DESIGN WING

CONTRACTOR TO CHECK &VERIFY ALL DIMENSIONS BEFORE COMMENCING WORK & TO REPORT ANY DISCREPANCIES TO THE DESIGN WING.

DO NOT SCALE DRAWINGS.

ALL CONSTRUCTION TO BE ACCORDING TO BEST COMMON PRACTICE.

REV:	DESCRIPTION:	BY:	DATE:
A	ARCHITECTURE DRAWING	----	25-12-25
B	STRUCTURE DRAWING	----	27-12-25

PROJECT NAME:
300 SQ.YARD HOUSE ARCHITECTURE DRAWING

SIGNATURE BY:

DRAWING TITLE:
ARCHITECTURAL DRAWING

DRAWN BY: MUDASSIR

CHECKED BY: M.SHEHERYAR

APPROVED BY: M.SHEHERYAR

DATE: 27-DEC-2025

CLIENT
MR. ROHAN
KARACHI...

DESIGNED BY:-

E.D.C.O
ENGINEERING DESIGNING CONSTRUCTION OFFICIAL
ARCHITECT| PLANNERS| ENGINEERS| INTERIOR| B.O.Q| EXTERIOR| CONSULT| STRUCTURE DESIGN| PLANNING| LAND SURVEY| CONSTRUCTION| 3D ANIMATION VIDEO| RENOVATION|
MUHAMMAD SHEHERYAR
CONTACT- 0312-2118445|D.H.A PHASE VII

PROJECT NO: AR-7590

SCALE: 1/8"=1'-0"

SHEET SIZE: A3

DRAWING NO: ARC

SHEET NO ----------

REVISION: YES

UNIT: INCHES&FEET

S E W N

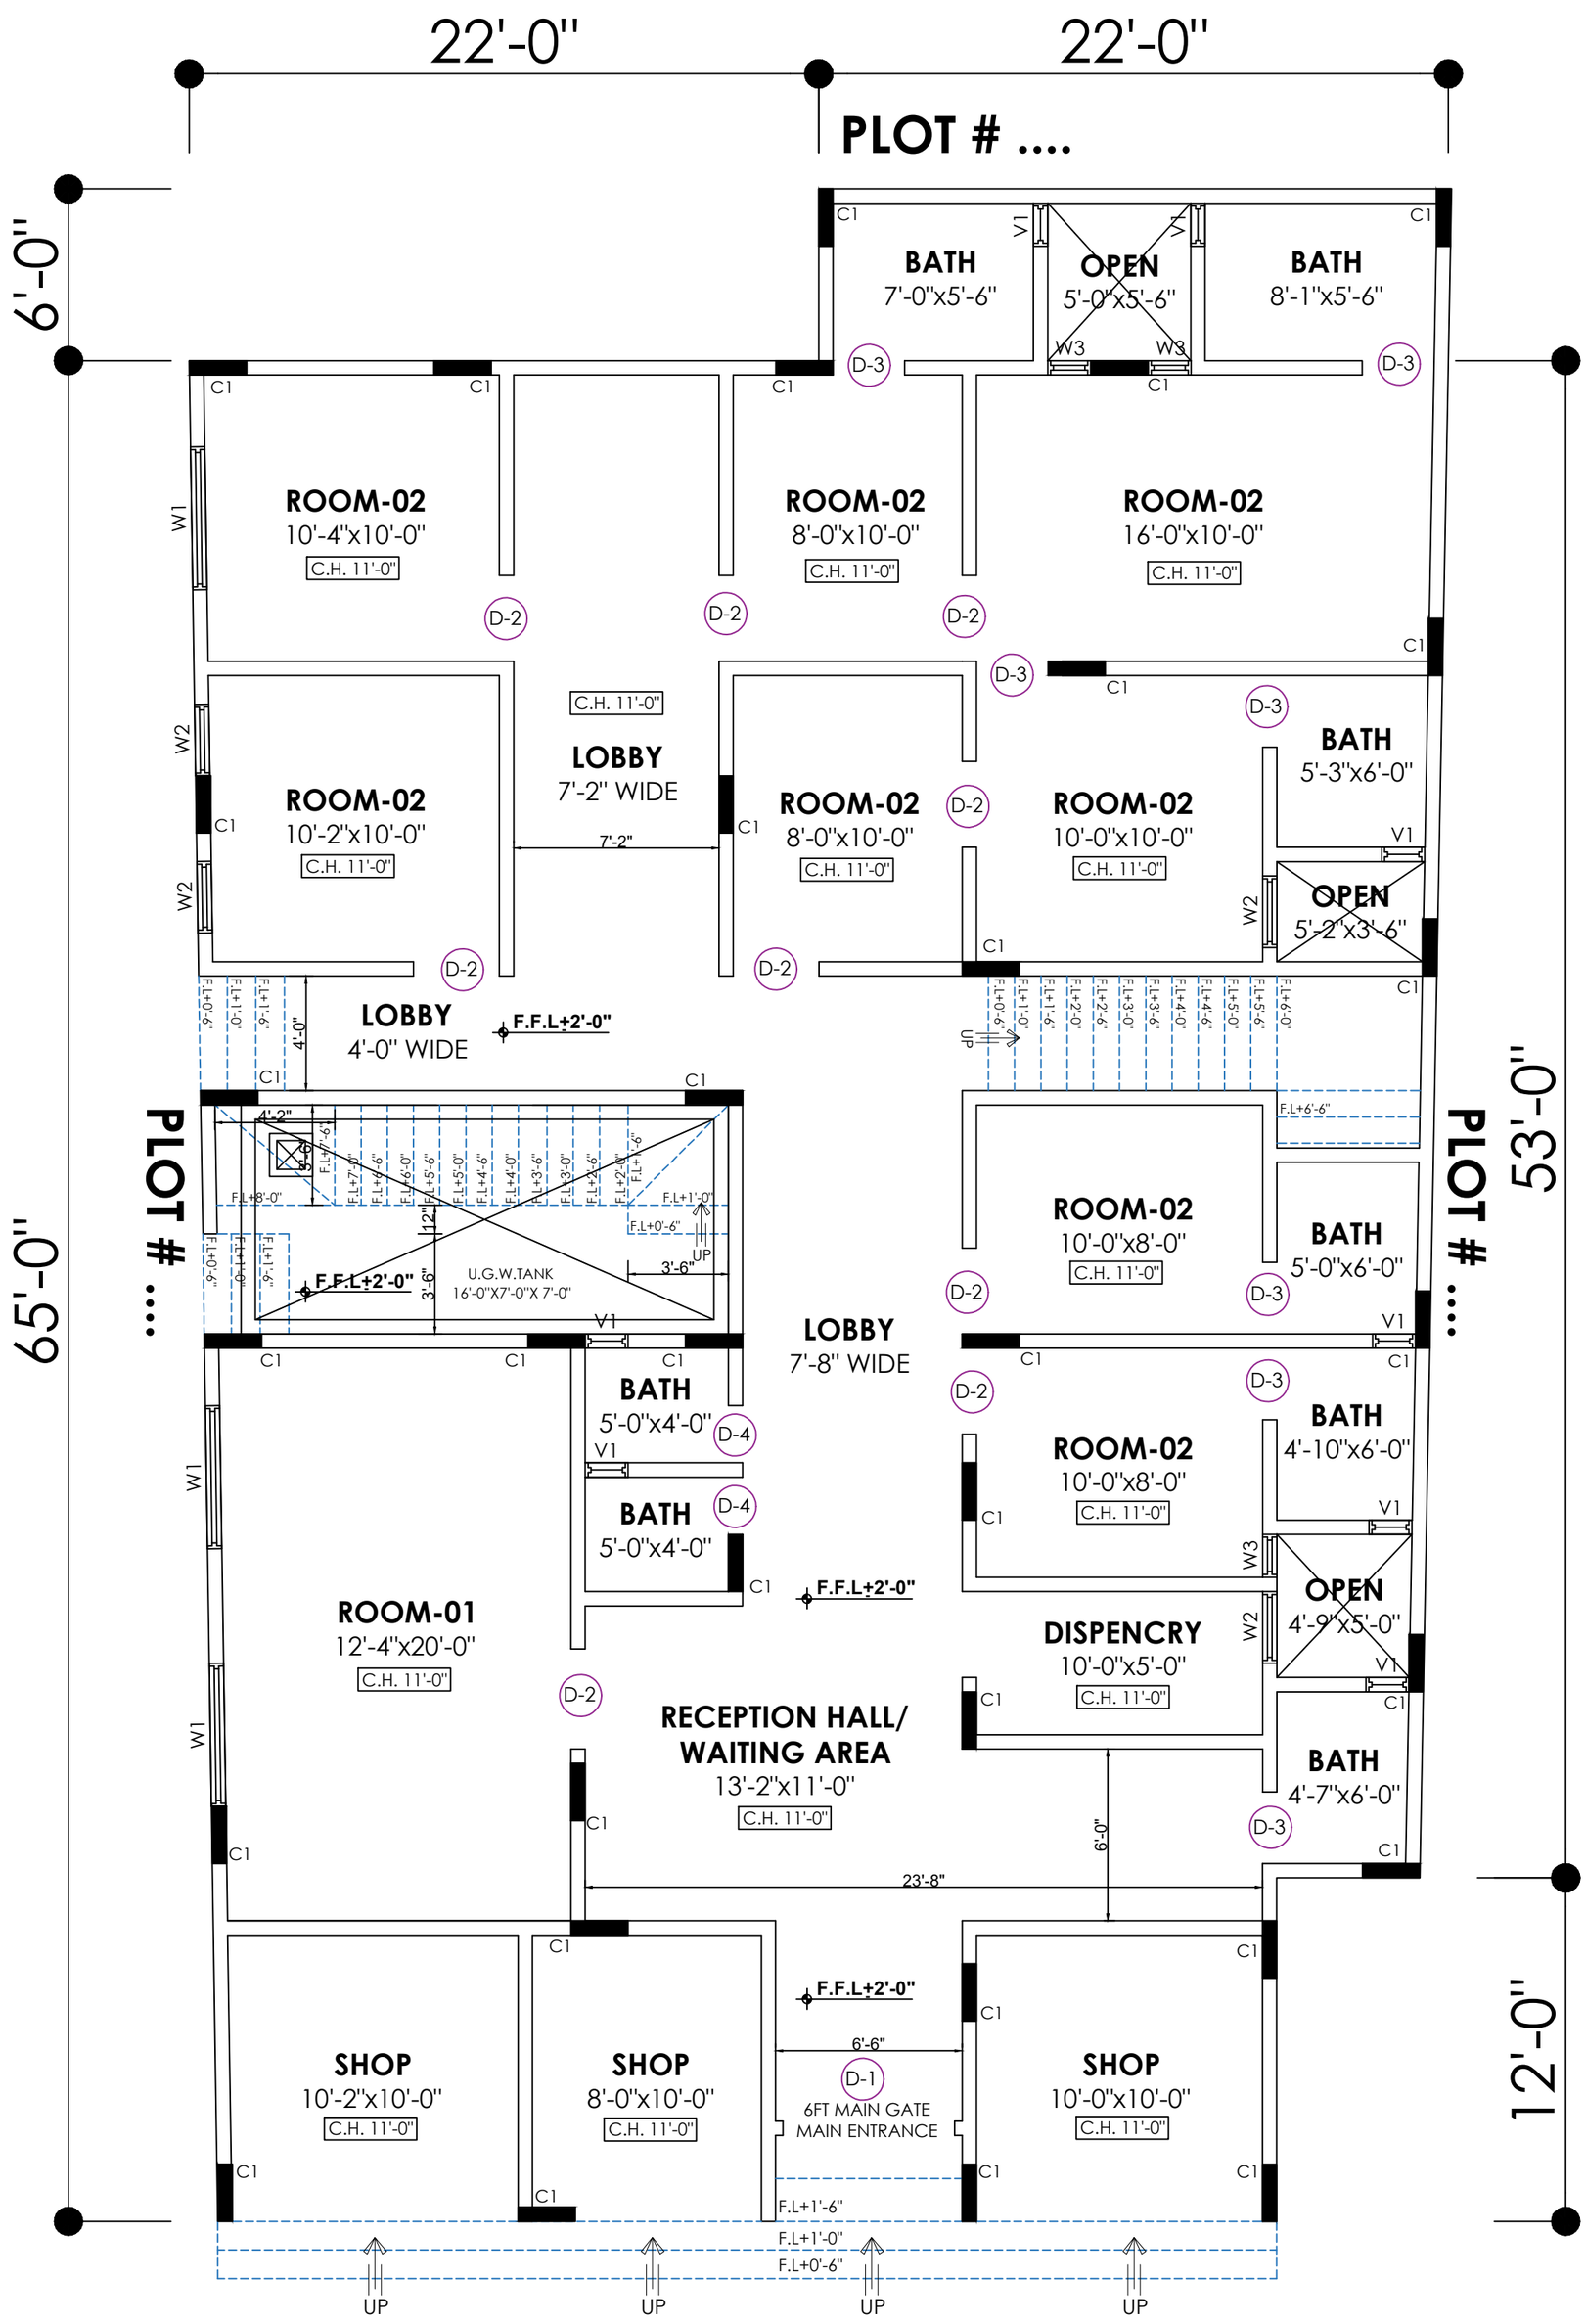

1 GROUND FLOOR PLAN

AR-01

GENERAL NOTES:

1. THE COPYRIGHT OF THIS DRAWING IS VESTED IN YourSpreadsheets AND IT MAY NOT BE REPRODUCED IN WHOLE OR PART OR USED FOR THE MANUFACTURE OF ANY ARTICLE WITHOUT THE EXPRESS PERMISSION OF THE COPYRIGHT HOLDERS.
2. WORK TO FIGURED DIMENSIONS ONLY.
3. THIS DRAWING IS TO BE READ IN CONJUNCTION WITH ALL RELEVANT ARCHITECT'S, SERVICE ENGINEER'S AND YourSpreadsheets DRAWINGS .

ALL DRWAING ARE THE PROPOERTY OF THE DESIGNER & THEY ARE NOT TO BE REPRODUCED IN WHOLE OR IN PART WITHOUT WRITTEN CONSENT FROM THE DESIGN WING
CONTRACTOR TO CHECK &VERIFY ALL DIMENSIONS BEFORE COMMENCING WORK & TO REPORT ANY DISCREPANCIES TO THE DESIGN WING.
DO NOT SCALE DRAWINGS.
ALL CONSTRUCTION TO BE ACCORDING TO BEST COMMON PRACTICE.

REV:	DESCRIPTION:	BY:	DATE:
A	ARCHITECTURE DRAWING	----	25-12-25
B	STRUCTURE DRAWING	----	27-12-25

PROJECT NAME:
300 SQ.YARD HOUSE ARCHITECTURE DRAWING

SIGNATURE BY:

DRAWING TITLE:
ARCHITECTURAL DRAWING

DRAWN BY: MUDASSIR
CHECKED BY: M.SHEHERYAR
APPROVED BY: M.SHEHERYAR
DATE: 27-DEC-2025

CLIENT
MR. ROHAN
KARACHI...

DESIGNED BY:-

E.D.C.O
ENGINEERING DESIGNING CONSTRUCTION OFFICIAL
ARCHITECT| PLANNERS| ENGINEERS| INTERIOR| B.O.Q| EXTERIOR| CONSULT| STRUCTURE DESIGN| PLANNING| LAND SURVEY| CONSTRUCTION| 3D ANIMATION VIDEO| RENOVATION|
MUHAMMAD SHEHERYAR
CONTACT- 0312-2118445|D.H.A PHASE VII

PROJECT NO: AR-7590
SCALE: 1/8"=1'-0"
SHEET SIZE: A3
DRAWING NO: ARC
SHEET NO ----------
REVISION: YES
UNIT: INCHES&FEET

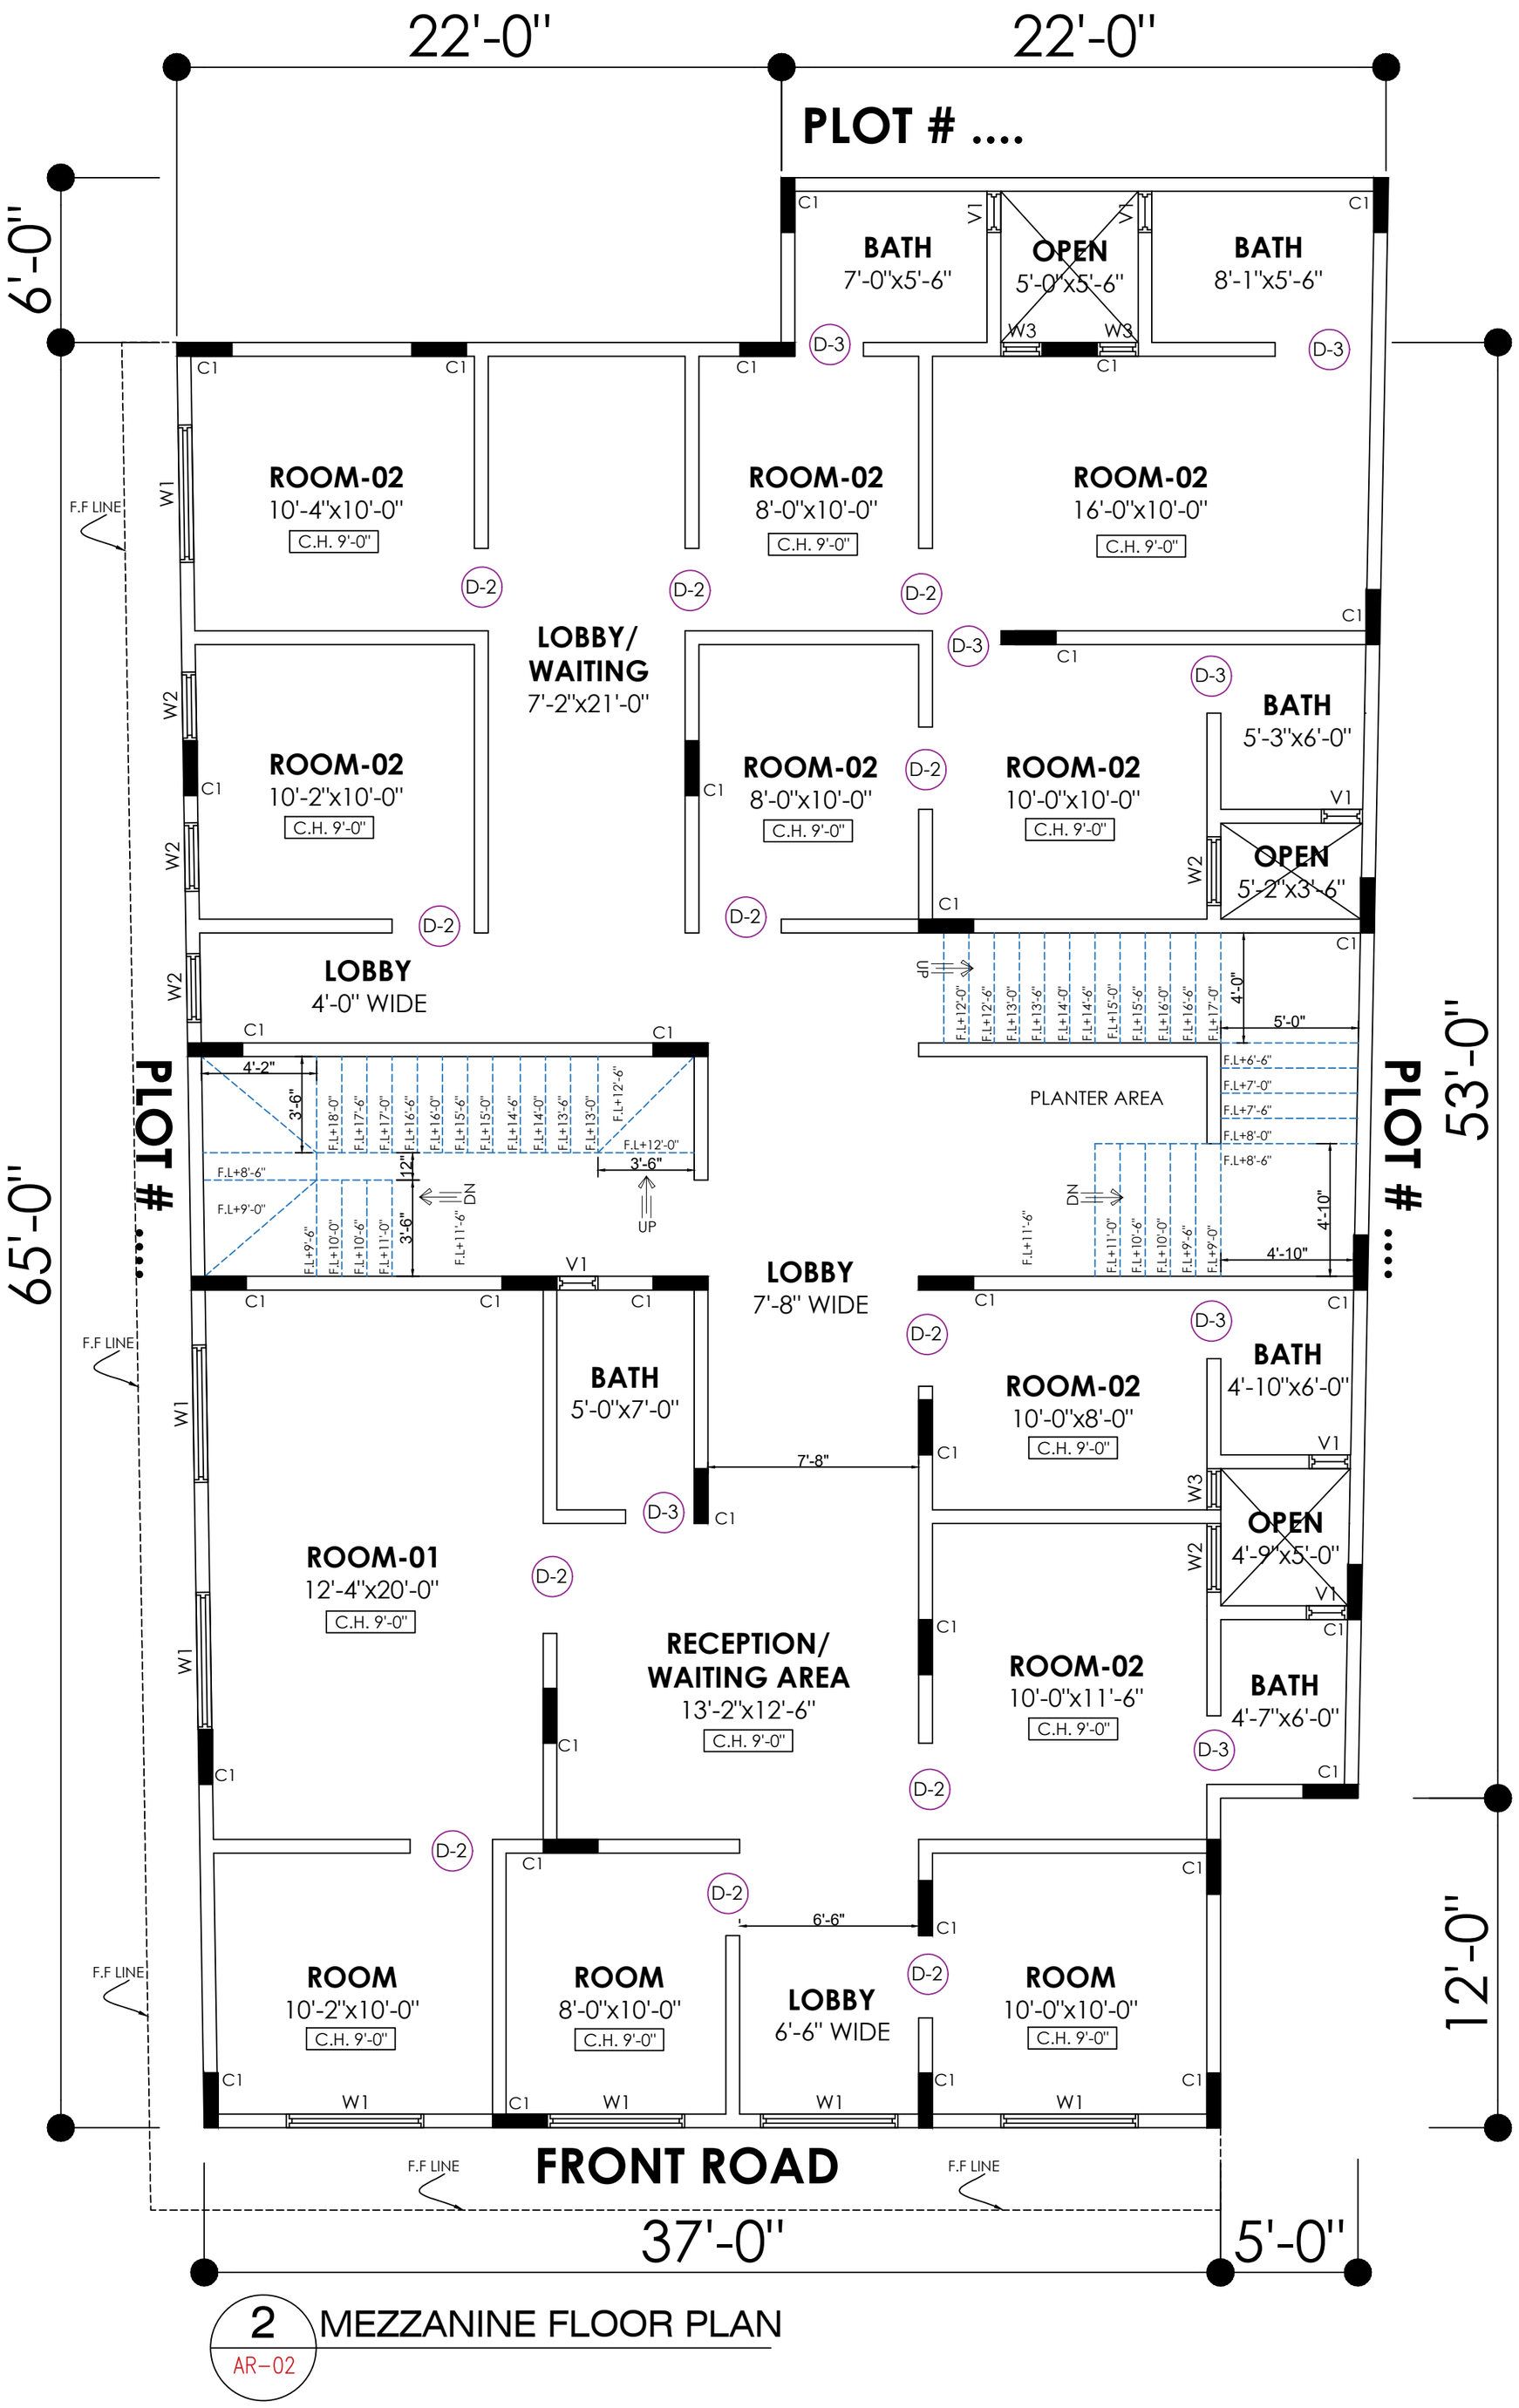

2 MEZZANINE FLOOR PLAN

AR-02

GENERAL NOTES:

1. THE COPYRIGHT OF THIS DRAWING IS VESTED IN YourSpreadsheets AND IT MAY NOT BE REPRODUCED IN WHOLE OR PART OR USED FOR THE MANUFACTURE OF ANY ARTICLE WITHOUT THE EXPRESS PERMISSION OF THE COPYRIGHT HOLDERS.
2. WORK TO FIGURED DIMENSIONS ONLY.
3. THIS DRAWING IS TO BE READ IN CONJUNCTION WITH ALL RELEVANT ARCHITECT'S, SERVICE ENGINEER'S AND YourSpreadsheets DRAWINGS .

ALL DRWAING ARE THE PROPOERTY OF THE DESIGNER & THEY ARE NOT TO BE REPRODUCED IN WHOLE OR IN PART WITHOUT WRITTEN CONSENT FROM THE DESIGN WING
CONTRACTOR TO CHECK &VERIFY ALL DIMENSIONS BEFORE COMMENCING WORK & TO REPORT ANY DISCREPANCIES TO THE DESIGN WING.
DO NOT SCALE DRAWINGS.
ALL CONSTRUCTION TO BE ACCORDING TO BEST COMMON PRACTICE.

REV:	DESCRIPTION:	BY:	DATE:
A	ARCHITECTURE DRAWING	----	25-12-25
B	STRUCTURE DRAWING	----	27-12-25

PROJECT NAME:
300 SQ.YARD HOUSE ARCHITECTURE DRAWING

SIGNATURE BY:

DRAWING TITLE:
ARCHITECTURAL DRAWING

DRAWN BY: MUDASSIR
CHECKED BY: M.SHEHERYAR
APPROVED BY: M.SHEHERYAR
DATE: 27-DEC-2025

CLIENT
MR. ROHAN
KARACHI...

DESIGNED BY:-

E.D.C.O
ENGINEERING DESIGNING CONSTRUCTION OFFICIAL
ARCHITECT| PLANNERS| ENGINEERS| INTERIOR| B.O.Q| EXTERIOR| CONSULT| STRUCTURE DESIGN| PLANNING| LAND SURVEY| CONSTRUCTION| 3D ANIMATION VIDEO| RENOVATION|
MUHAMMAD SHEHERYAR
CONTACT- 0312-2118445|D.H.A PHASE VII

PROJECT NO: AR-7590
SCALE: 1/8"=1'-0"
SHEET SIZE: A3
DRAWING NO: ARC
SHEET NO ----------
REVISION: YES
UNIT: INCHES&FEET

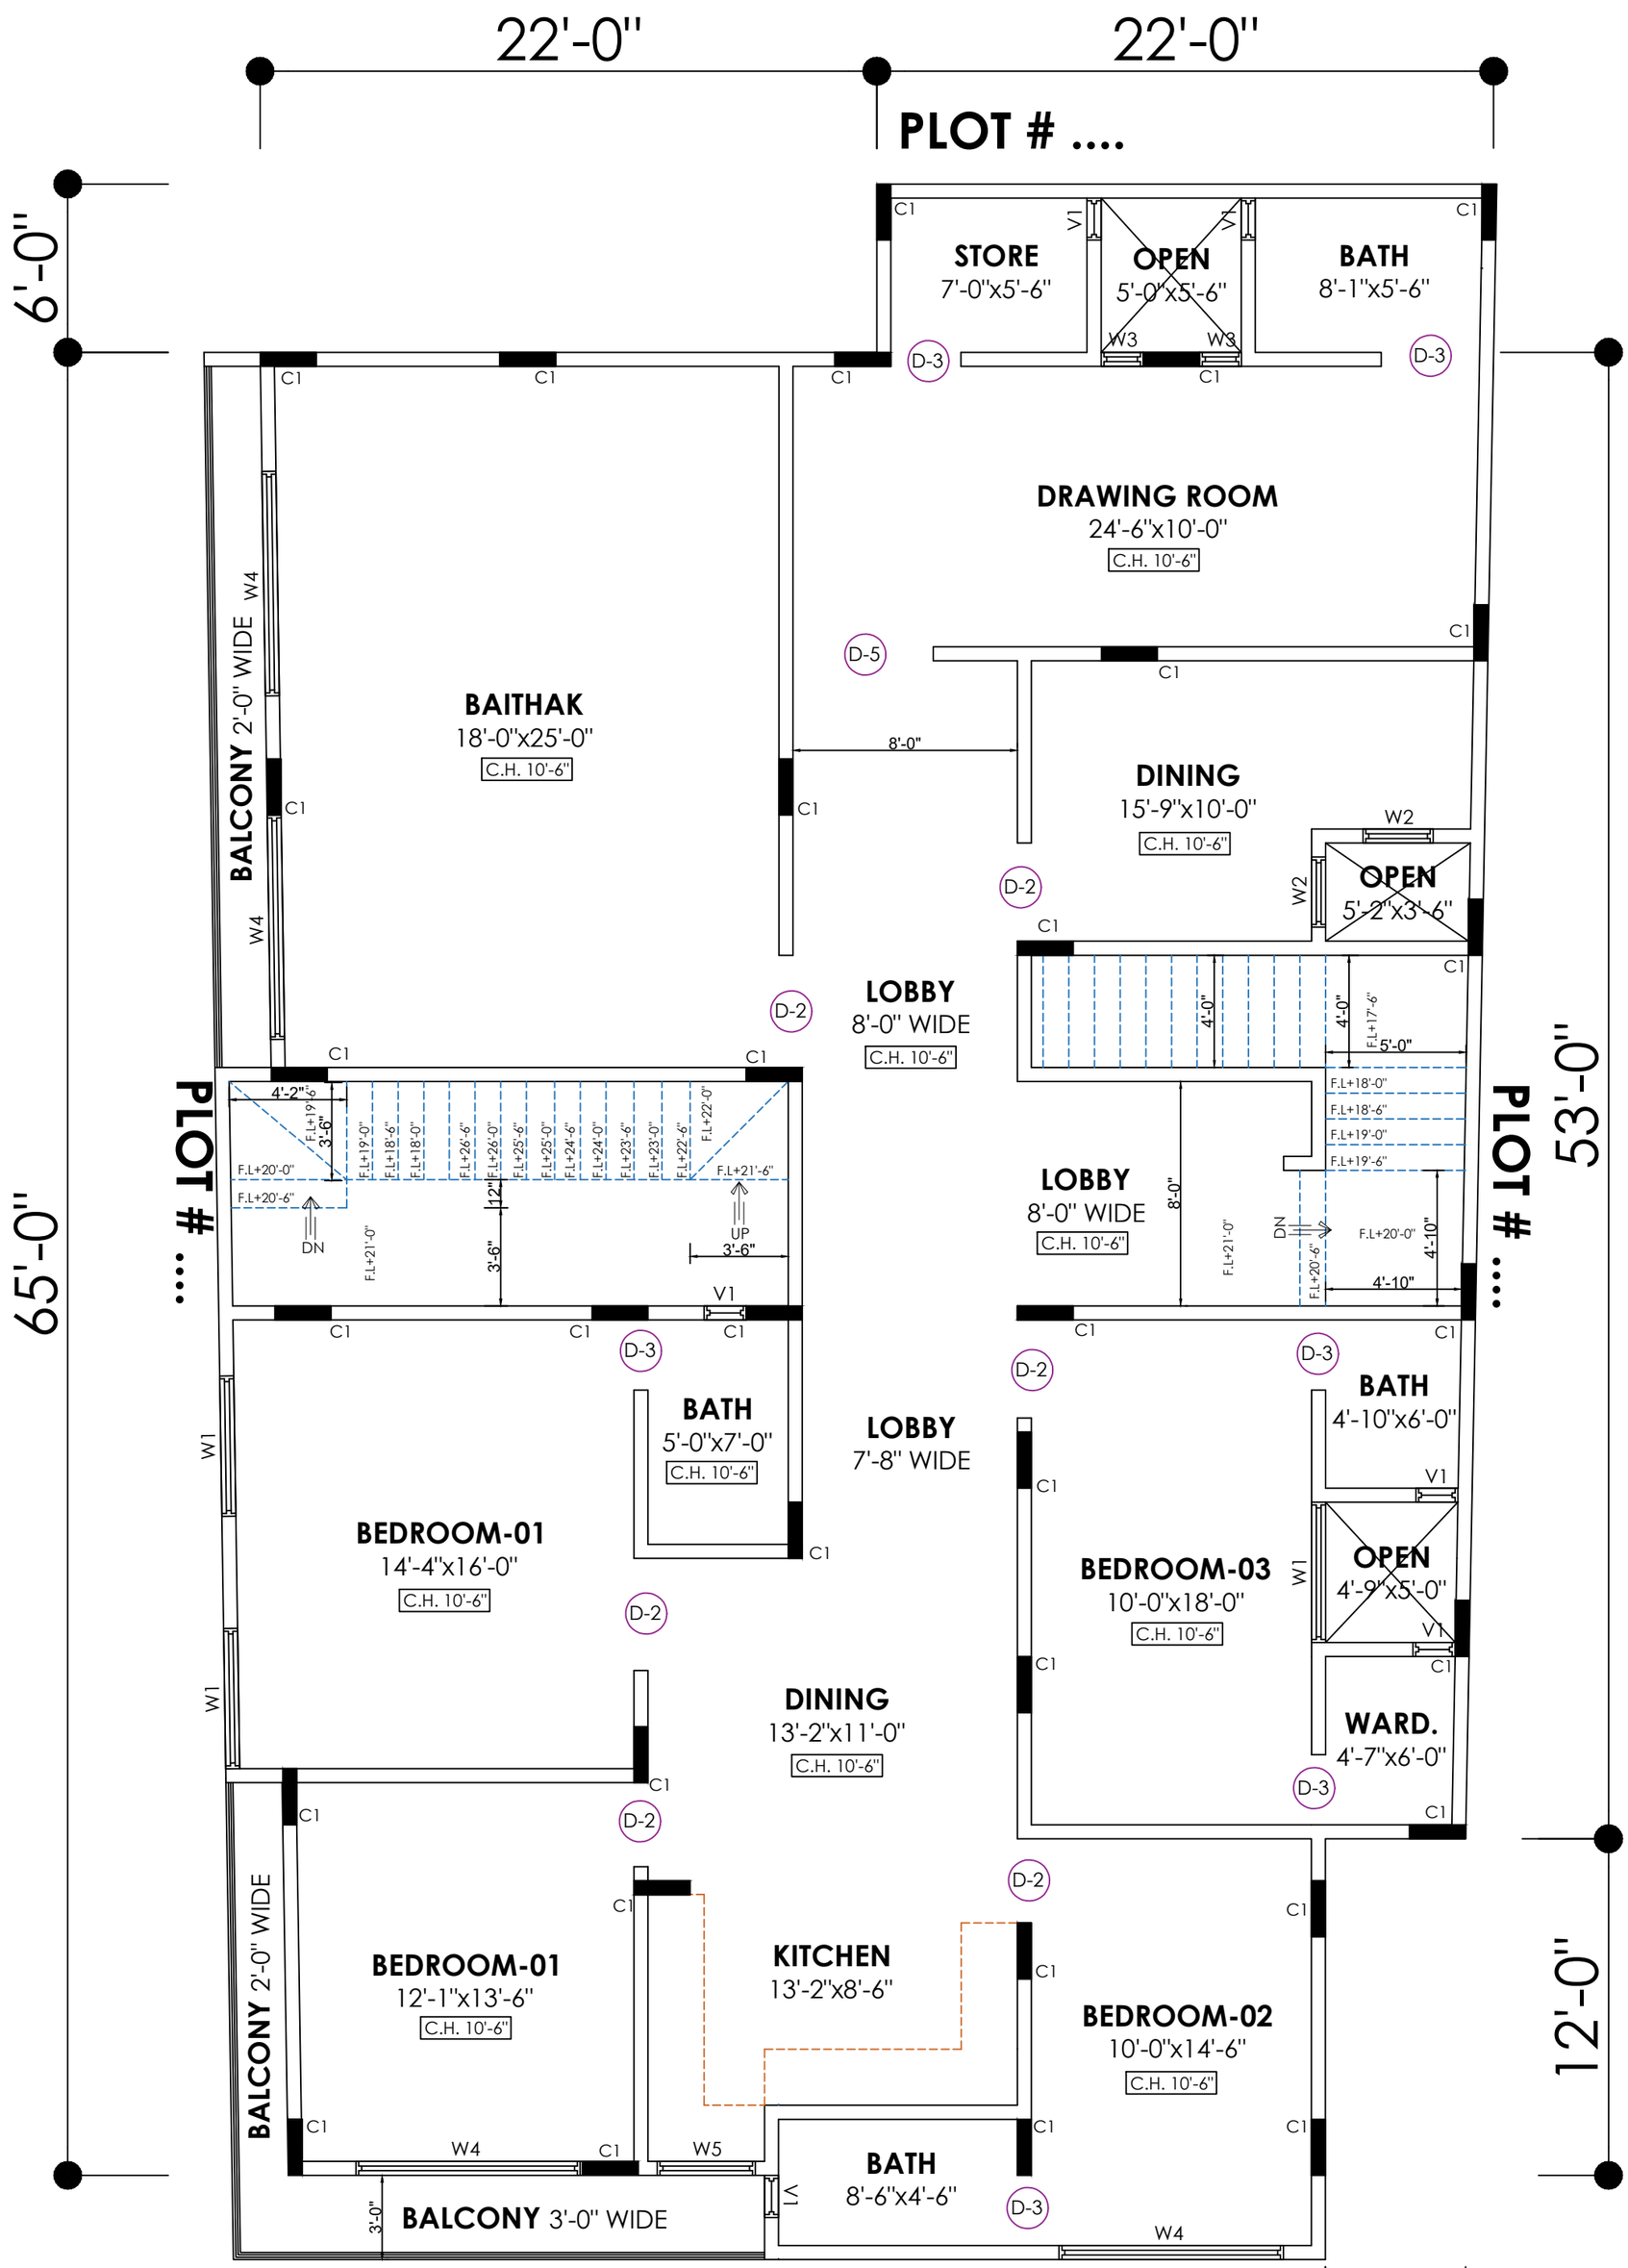

3 FIRST FLOOR PLAN

AR-03

GENERAL NOTES:

1. THE COPYRIGHT OF THIS DRAWING IS VESTED IN YourSpreadsheets AND IT MAY NOT BE REPRODUCED IN WHOLE OR PART OR USED FOR THE MANUFACTURE OF ANY ARTICLE WITHOUT THE EXPRESS PERMISSION OF THE COPYRIGHT HOLDERS.
2. WORK TO FIGURED DIMENSIONS ONLY.
3. THIS DRAWING IS TO BE READ IN CONJUNCTION WITH ALL RELEVANT ARCHITECT'S, SERVICE ENGINEER'S AND YourSpreadsheets DRAWINGS .
ALL DRWAING ARE THE PROPOERTY OF THE DESIGNER & THEY ARE NOT TO BE REPRODUCED IN WHOLE OR IN PART WITHOUT WRITTEN CONSENT FROM THE DESIGN WING
CONTRACTOR TO CHECK &VERIFY ALL DIMENSIONS BEFORE COMMENCING WORK & TO REPORT ANY DISCREPANCIES TO THE DESIGN WING.
DO NOT SCALE DRAWINGS.
ALL CONSTRUCTION TO BE ACCORDING TO BEST COMMON PRACTICE.

REV:	DESCRIPTION:	BY:	DATE:
A	ARCHITECTURE DRAWING	----	25-12-25
B	STRUCTURE DRAWING	----	27-12-25

PROJECT NAME:
300 SQ.YARD HOUSE ARCHITECTURE DRAWING

SIGNATURE BY:

DRAWING TITLE:
ARCHITECTURAL DRAWING

DRAWN BY: MUDASSIR
CHECKED BY: M.SHEHERYAR
APPROVED BY: M.SHEHERYAR
DATE: 27-DEC-2025

CLIENT
MR. ROHAN
KARACHI...

DESIGNED BY:-

E.D.C.O
ENGINEERING DESIGNING CONSTRUCTION OFFICIAL
ARCHITECT| PLANNERS| ENGINEERS| INTERIOR| B.O.Q| EXTERIOR| CONSULT| STRUCTURE DESIGN| PLANNING| LAND SURVEY| CONSTRUCTION| 3D ANIMATION VIDEO| RENOVATION|
MUHAMMAD SHEHERYAR
CONTACT- 0312-2118445|D.H.A PHASE VII

PROJECT NO: AR-7590
SCALE: 1/8"=1'-0"
SHEET SIZE: A3
DRAWING NO: ARC
SHEET NO ----------
REVISION: YES
UNIT: INCHES&FEET

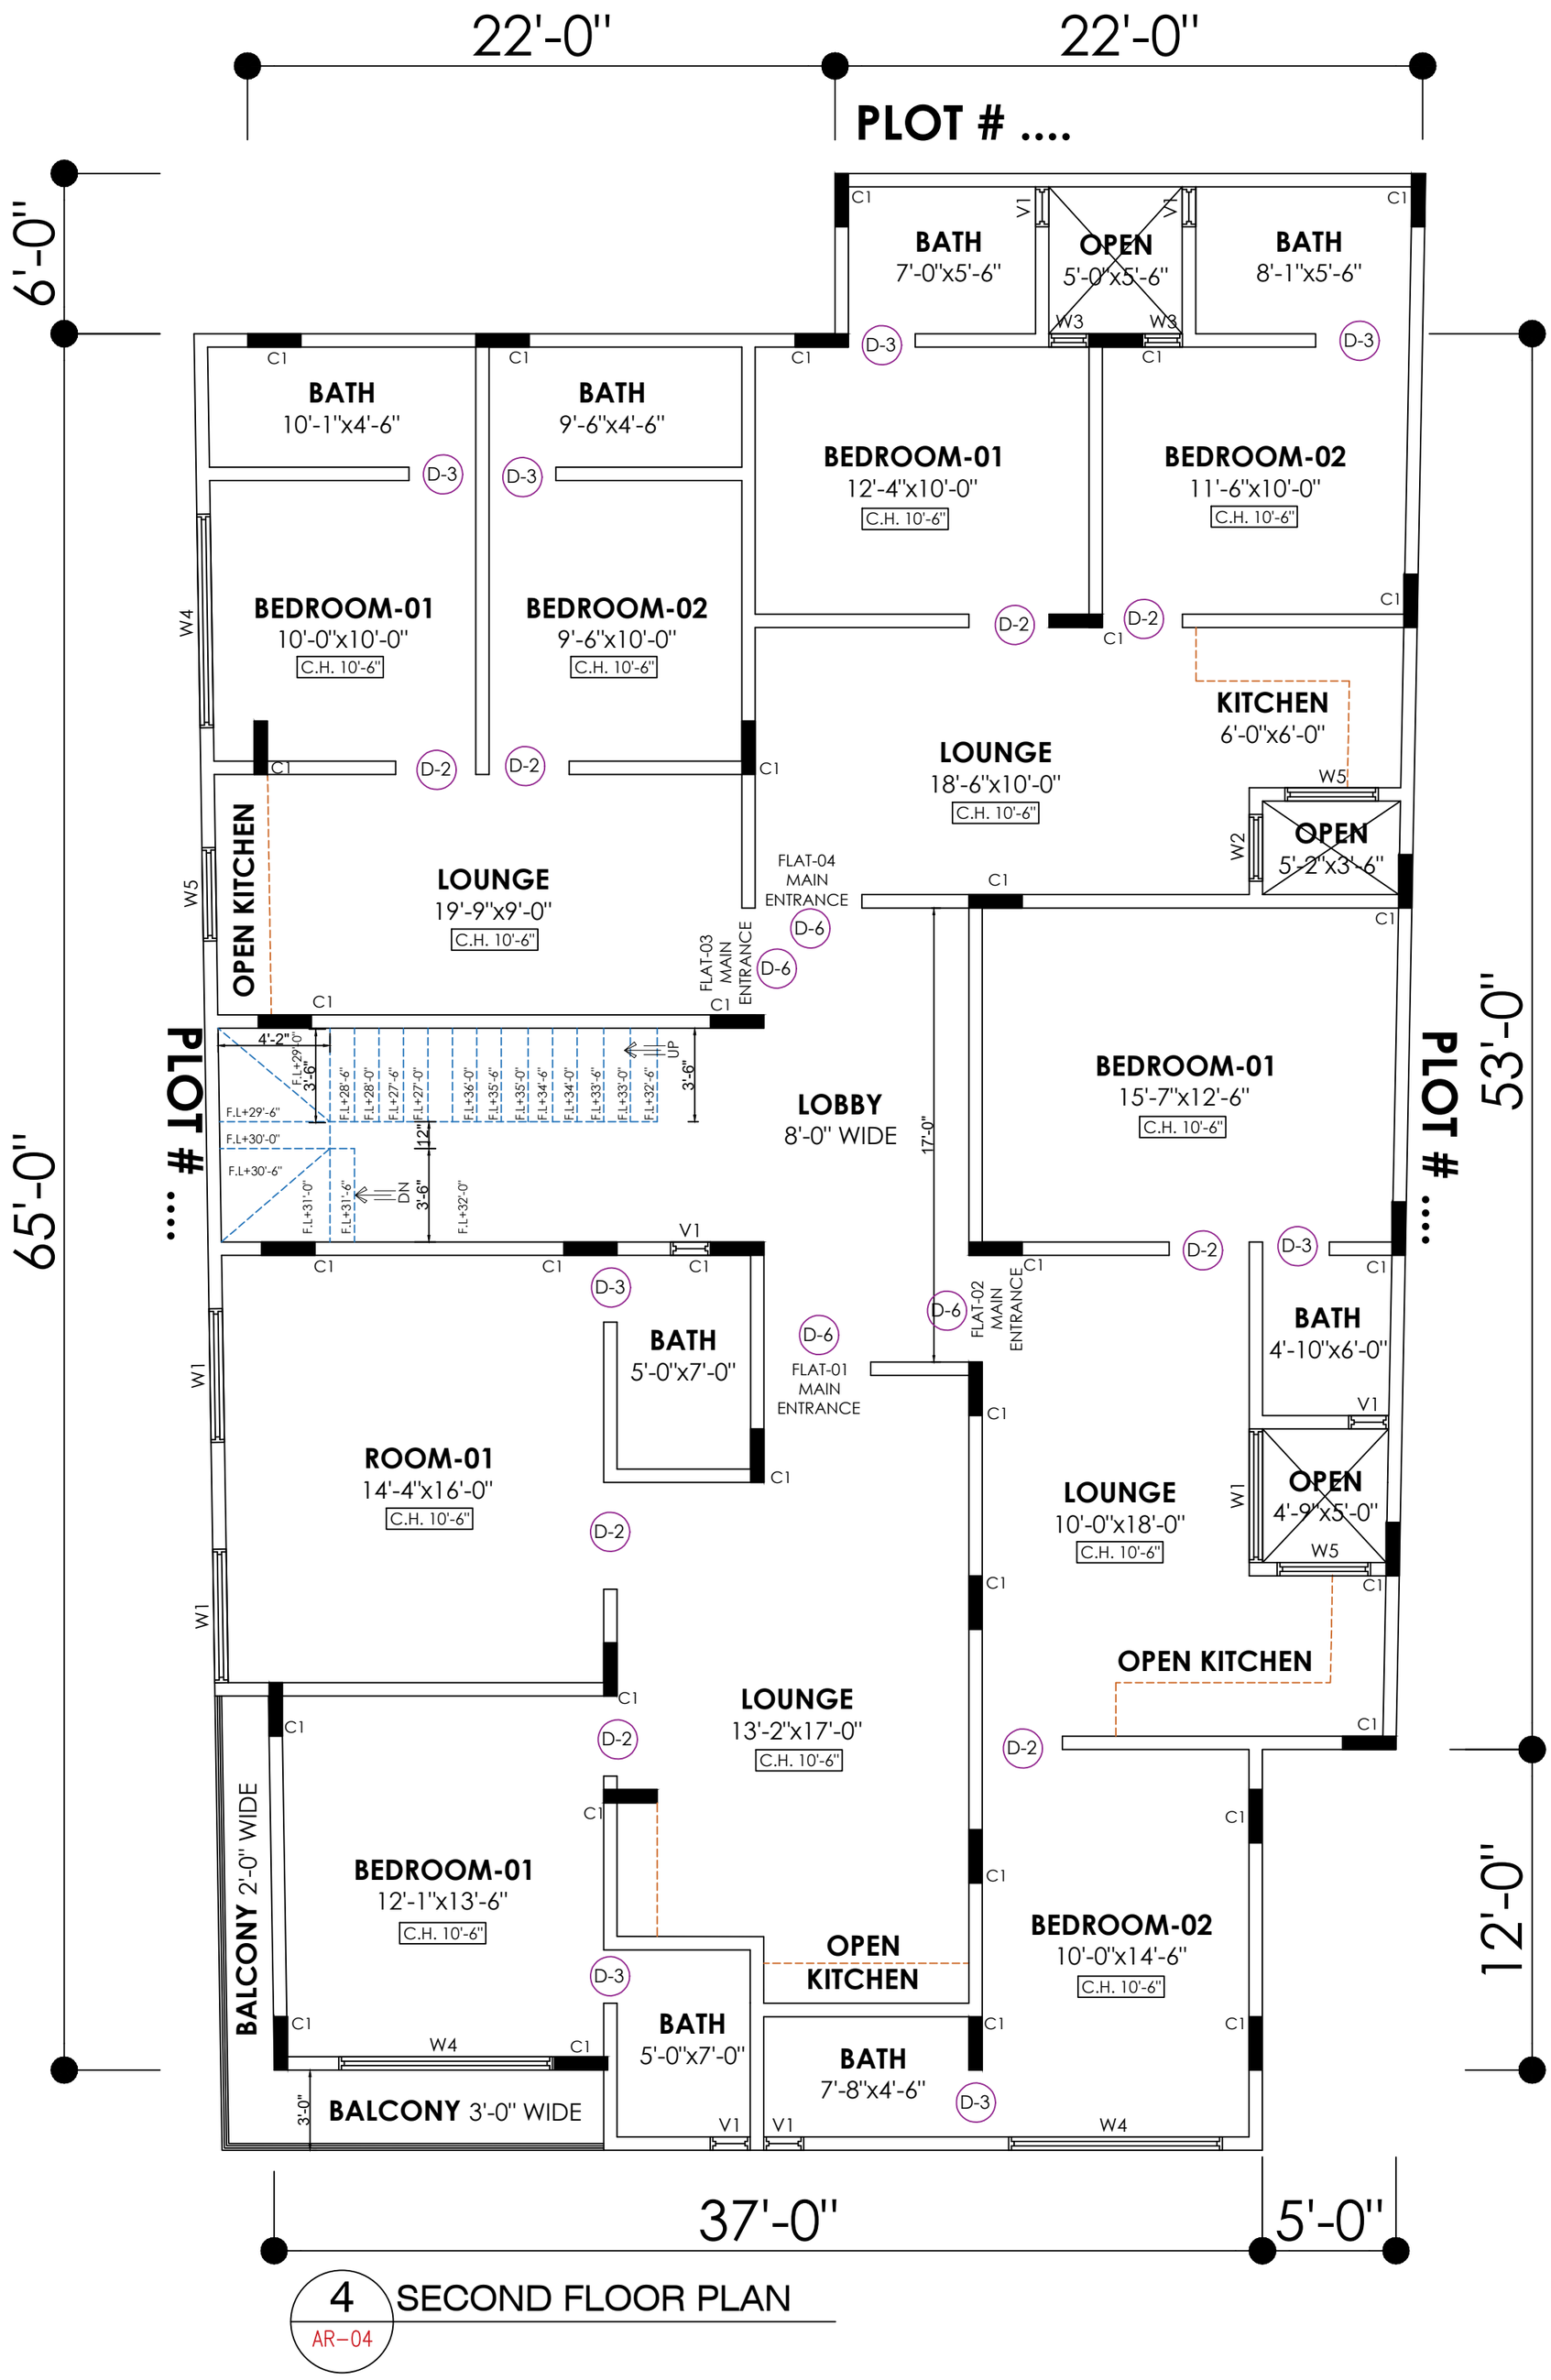

4 SECOND FLOOR PLAN

AR-04

GENERAL NOTES:

1. THE COPYRIGHT OF THIS DRAWING IS VESTED IN YourSpreadsheets AND IT MAY NOT BE REPRODUCED IN WHOLE OR PART OR USED FOR THE MANUFACTURE OF ANY ARTICLE WITHOUT THE EXPRESS PERMISSION OF THE COPYRIGHT HOLDERS.
2. WORK TO FIGURED DIMENSIONS ONLY.
3. THIS DRAWING IS TO BE READ IN CONJUNCTION WITH ALL RELEVANT ARCHITECT'S, SERVICE ENGINEER'S AND YourSpreadsheets DRAWINGS .

ALL DRWAING ARE THE PROPOERTY OF THE DESIGNER & THEY ARE NOT TO BE REPRODUCED IN WHOLE OR IN PART WITHOUT WRITTEN CONSENT FROM THE DESIGN WING

CONTRACTOR TO CHECK &VERIFY ALL DIMENSIONS BEFORE COMMENCING WORK & TO REPORT ANY DISCREPANCIES TO THE DESIGN WING.

DO NOT SCALE DRAWINGS.

ALL CONSTRUCTION TO BE ACCORDING TO BEST COMMON PRACTICE.

REV:	DESCRIPTION:	BY:	DATE:
A	ARCHITECTURE DRAWING	----	25-12-25
B	STRUCTURE DRAWING	----	27-12-25

PROJECT NAME:
300 SQ.YARD HOUSE ARCHITECTURE DRAWING

SIGNATURE BY:

DRAWING TITLE:
ARCHITECTURAL DRAWING

DRAWN BY: MUDASSIR

CHECKED BY: M.SHEHERYAR

APPROVED BY: M.SHEHERYAR

DATE: 27-DEC-2025

CLIENT
MR. ROHAN
KARACHI...

DESIGNED BY:-

E.D.C.O
ENGINEERING DESIGNING CONSTRUCTION OFFICIAL
ARCHITECT| PLANNERS| ENGINEERS| INTERIOR| B.O.Q| EXTERIOR| CONSULT| STRUCTURE DESIGN| PLANNING| LAND SURVEY| CONSTRUCTION| 3D ANIMATION VIDEO| RENOVATION|
MUHAMMAD SHEHERYAR
CONTACT- 0312-2118445|D.H.A PHASE VII

PROJECT NO: AR-7590

SCALE: 1/8"=1'-0"

SHEET SIZE: A3

DRAWING NO: ARC

SHEET NO ----------

REVISION: YES

UNIT: INCHES&FEET

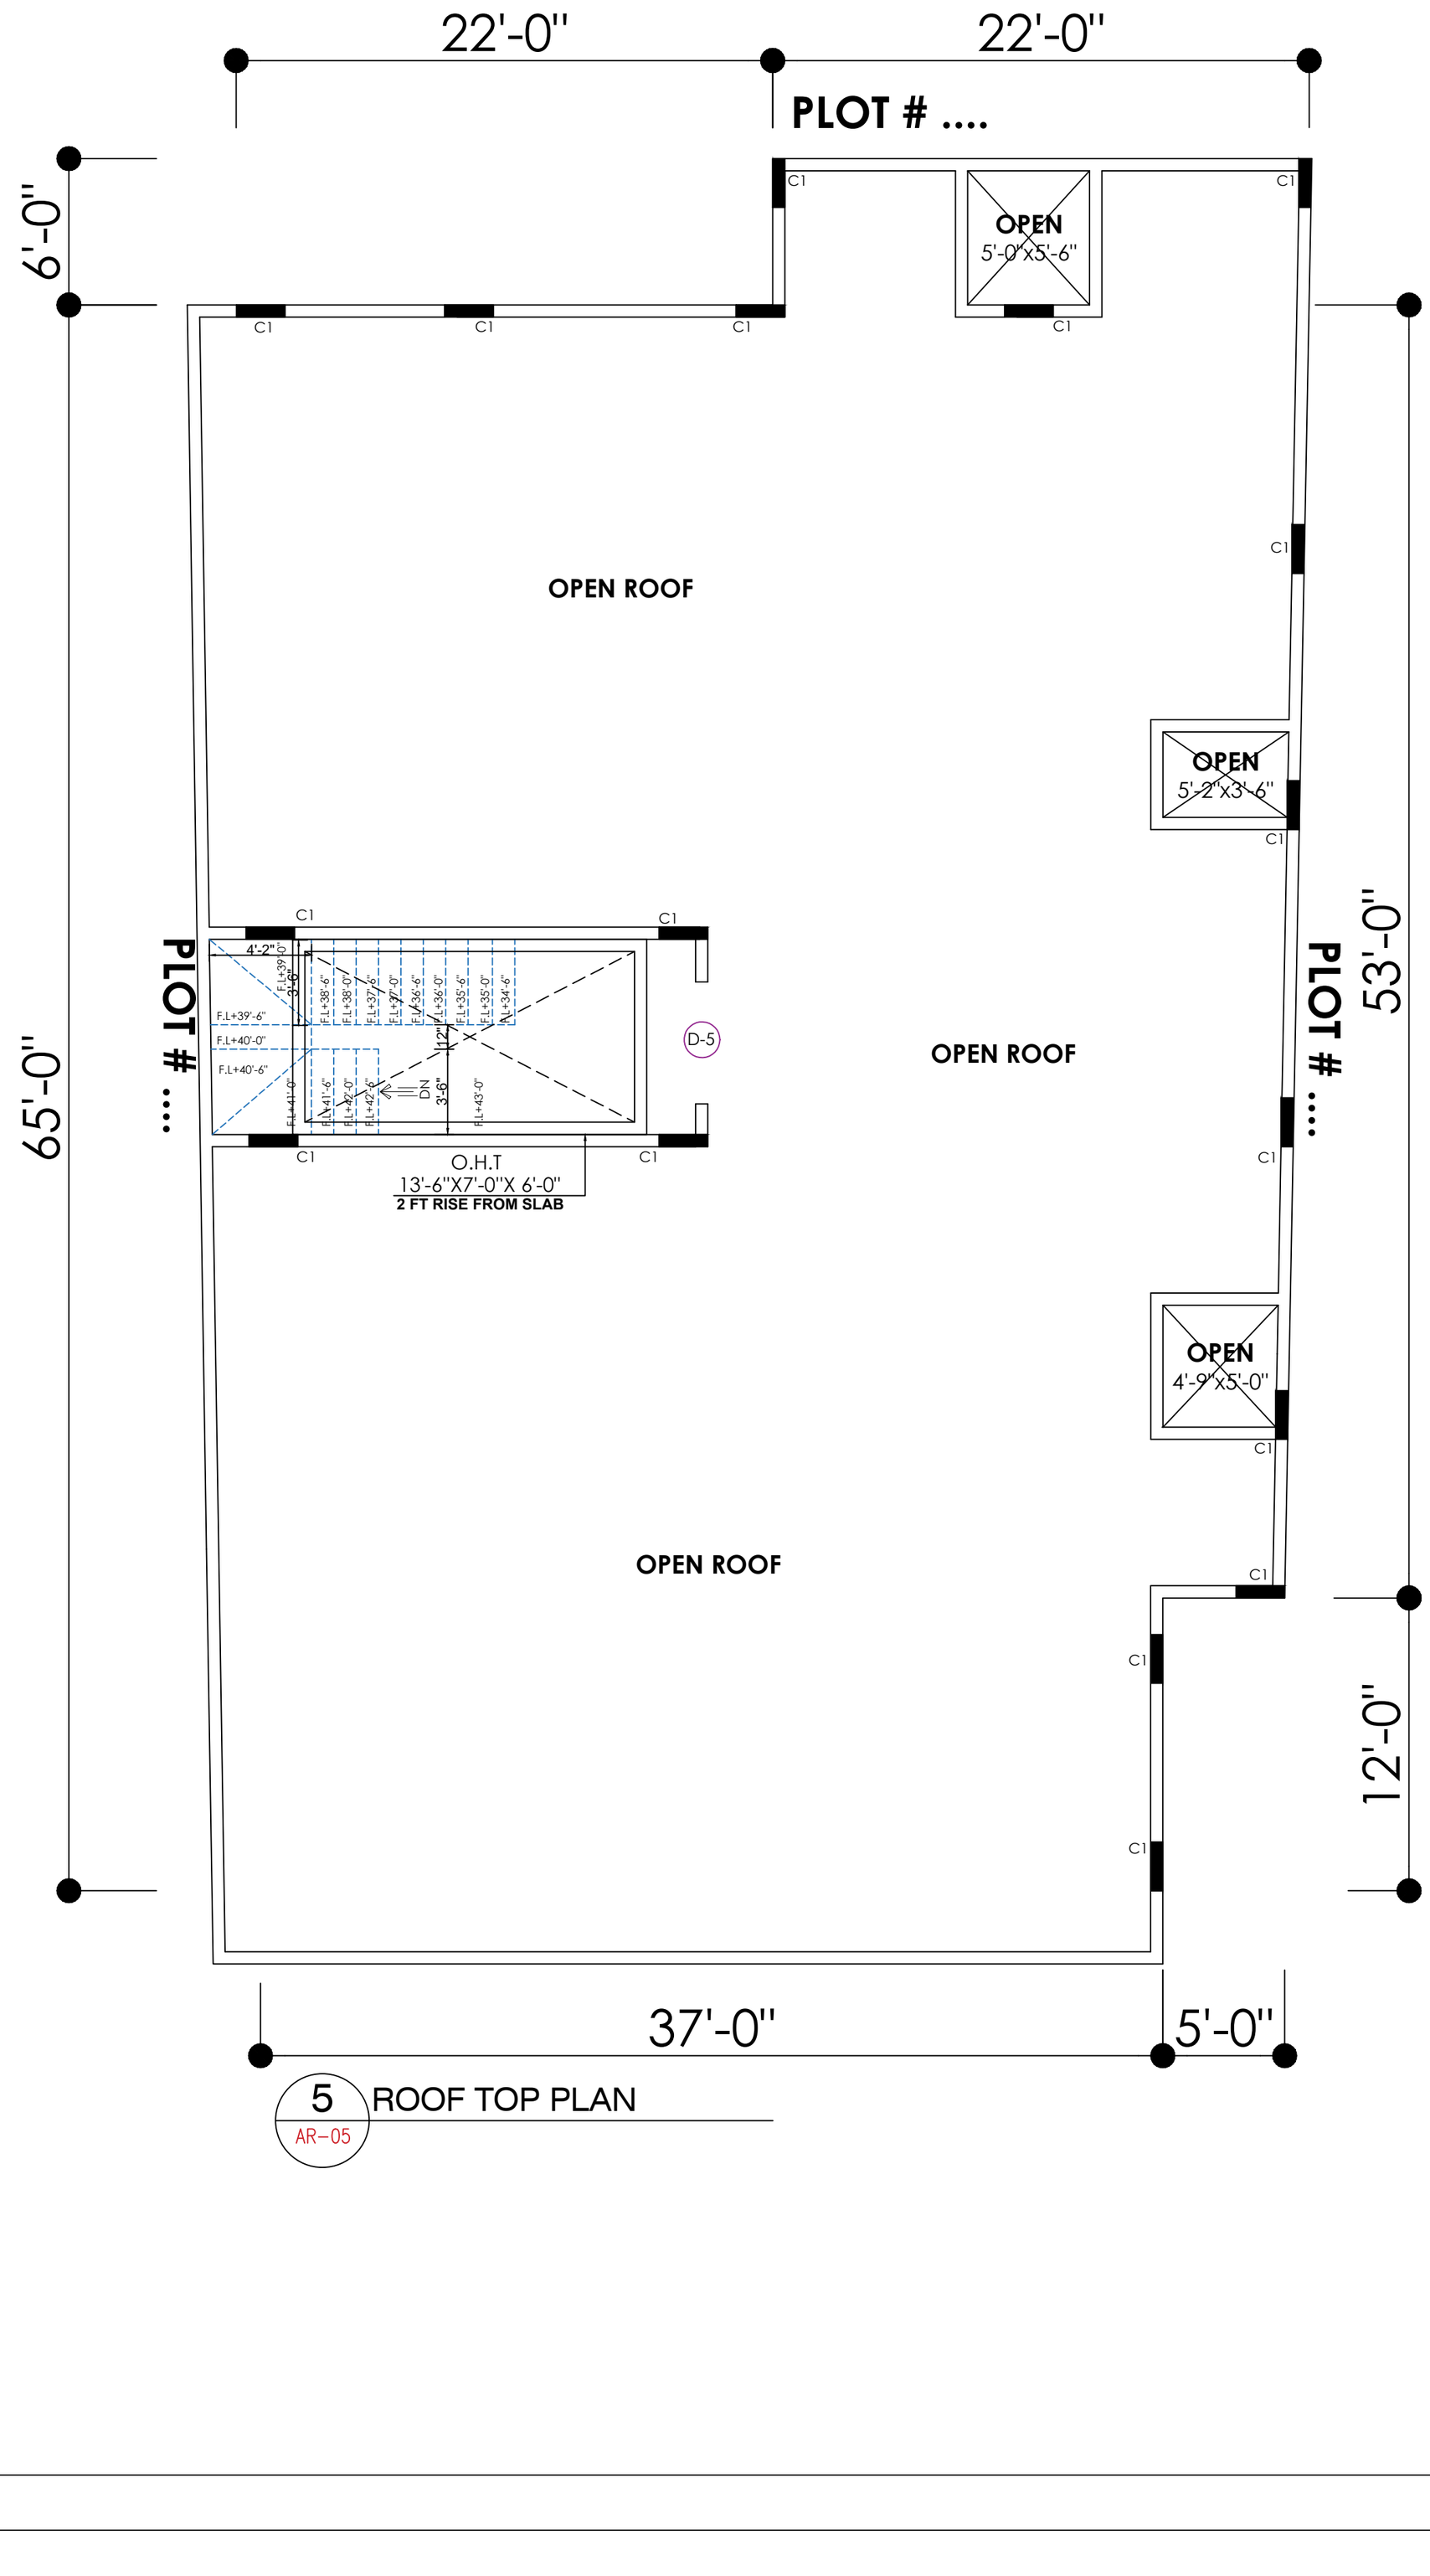

5 ROOF TOP PLAN
AR-05

GENERAL NOTES:

1. THE COPYRIGHT OF THIS DRAWING IS VESTED IN YourSpreadsheets AND IT MAY NOT BE REPRODUCED IN WHOLE OR PART OR USED FOR THE MANUFACTURE OF ANY ARTICLE WITHOUT THE EXPRESS PERMISSION OF THE COPYRIGHT HOLDERS.
2. WORK TO FIGURED DIMENSIONS ONLY.
3. THIS DRAWING IS TO BE READ IN CONJUNCTION WITH ALL RELEVANT ARCHITECT'S, SERVICE ENGINEER'S AND YourSpreadsheets DRAWINGS .
ALL DRWAING ARE THE PROPOERTY OF THE DESIGNER & THEY ARE NOT TO BE REPRODUCED IN WHOLE OR IN PART WITHOUT WRITTEN CONSENT FROM THE DESIGN WING
CONTRACTOR TO CHECK &VERIFY ALL DIMENSIONS BEFORE COMMENCING WORK & TO REPORT ANY DISCREPANCIES TO THE DESIGN WING.
DO NOT SCALE DRAWINGS.
ALL CONSTRUCTION TO BE ACCORDING TO BEST COMMON PRACTICE.

REV:	DESCRIPTION:	BY:	DATE:
A	ARCHITECTURE DRAWING	----	25-12-25
B	STRUCTURE DRAWING	----	27-12-25

PROJECT NAME:
300 SQ.YARD HOUSE ARCHITECTURE DRAWING

SIGNATURE BY:

DRAWING TITLE:
ARCHITECTURAL DRAWING

DRAWN BY: MUDASSIR
CHECKED BY: M.SHEHERYAR
APPROVED BY: M.SHEHERYAR
DATE: 27-DEC-2025

CLIENT
MR. ROHAN
KARACHI...

DESIGNED BY:-

E.D.C.O
ENGINEERING DESIGNING CONSTRUCTION OFFICIAL
ARCHITECT| PLANNERS| ENGINEERS| INTERIOR| B.O.Q| EXTERIOR| CONSULT| STRUCTURE DESIGN| PLANNING| LAND SURVEY| CONSTRUCTION| 3D ANIMATION VIDEO| RENOVATION|
MUHAMMAD SHEHERYAR
CONTACT- 0312-2118445|D.H.A PHASE VII

PROJECT NO: AR-7590
SCALE: 1/8"=1'-0"
SHEET SIZE: A3
DRAWING NO: ARC
SHEET NO ----------
REVISION: YES
UNIT: INCHES&FEET

GENERAL NOTES:

1. THE COPYRIGHT OF THIS DRAWING IS VESTED IN YourSpreadsheets AND IT MAY NOT BE REPRODUCED IN WHOLE OR PART OR USED FOR THE MANUFACTURE OF ANY ARTICLE WITHOUT THE EXPRESS PERMISSION OF THE COPYRIGHT HOLDERS.
2. WORK TO FIGURED DIMENSIONS ONLY.
3. THIS DRAWING IS TO BE READ IN CONJUNCTION WITH ALL RELEVANT ARCHITECT'S, SERVICE ENGINEER'S AND YourSpreadsheets DRAWINGS .

ALL DRWAING ARE THE PROPOERTY OF THE DESIGNER & THEY ARE NOT TO BE REPRODUCED IN WHOLE OR IN PART WITHOUT WRITTEN CONSENT FROM THE DESIGN WING

CONTRACTOR TO CHECK &VERIFY ALL DIMENSIONS BEFORE COMMENCING WORK & TO REPORT ANY DISCREPANCIES TO THE DESIGN WING.

DO NOT SCALE DRAWINGS.

ALL CONSTRUCTION TO BE ACCORDING TO BEST COMMON PRACTICE.

REV:	DESCRIPTION:	BY:	DATE:
A	ARCHITECTURE DRAWING	----	25-12-25
B	STRUCTURE DRAWING	----	27-12-25

WORKING

DRAWING

PROJECT NAME:
300 SQ.YARD HOUSE ARCHITECTURE DRAWING

SIGNATURE BY:

DRAWING TITLE:
ARCHITECTURAL DRAWING

DRAWN BY: MUDASSIR

CHECKED BY: M.SHEHERYAR

APPROVED BY: M.SHEHERYAR

DATE: 27-DEC-2025

CLIENT
MR. ROHAN
KARACHI...

DESIGNED BY:-

E.D.C.O
ENGINEERING DESIGNING CONSTRUCTION OFFICIAL
ARCHITECT| PLANNERS| ENGINEERS| INTERIOR| B.O.Q| EXTERIOR| CONSULT| STRUCTURE DESIGN| PLANNING| LAND SURVEY| CONSTRUCTION| 3D ANIMATION VIDEO| RENOVATION|
MUHAMMAD SHEHERYAR
CONTACT- 0312-2118445|D.H.A PHASE VII

PROJECT NO: AR-7590

SCALE: 1/8"=1'-0"

SHEET SIZE: A3

DRAWING NO: ARC

SHEET NO ----------

REVISION: YES

UNIT: INCHES&FEET

S E W N

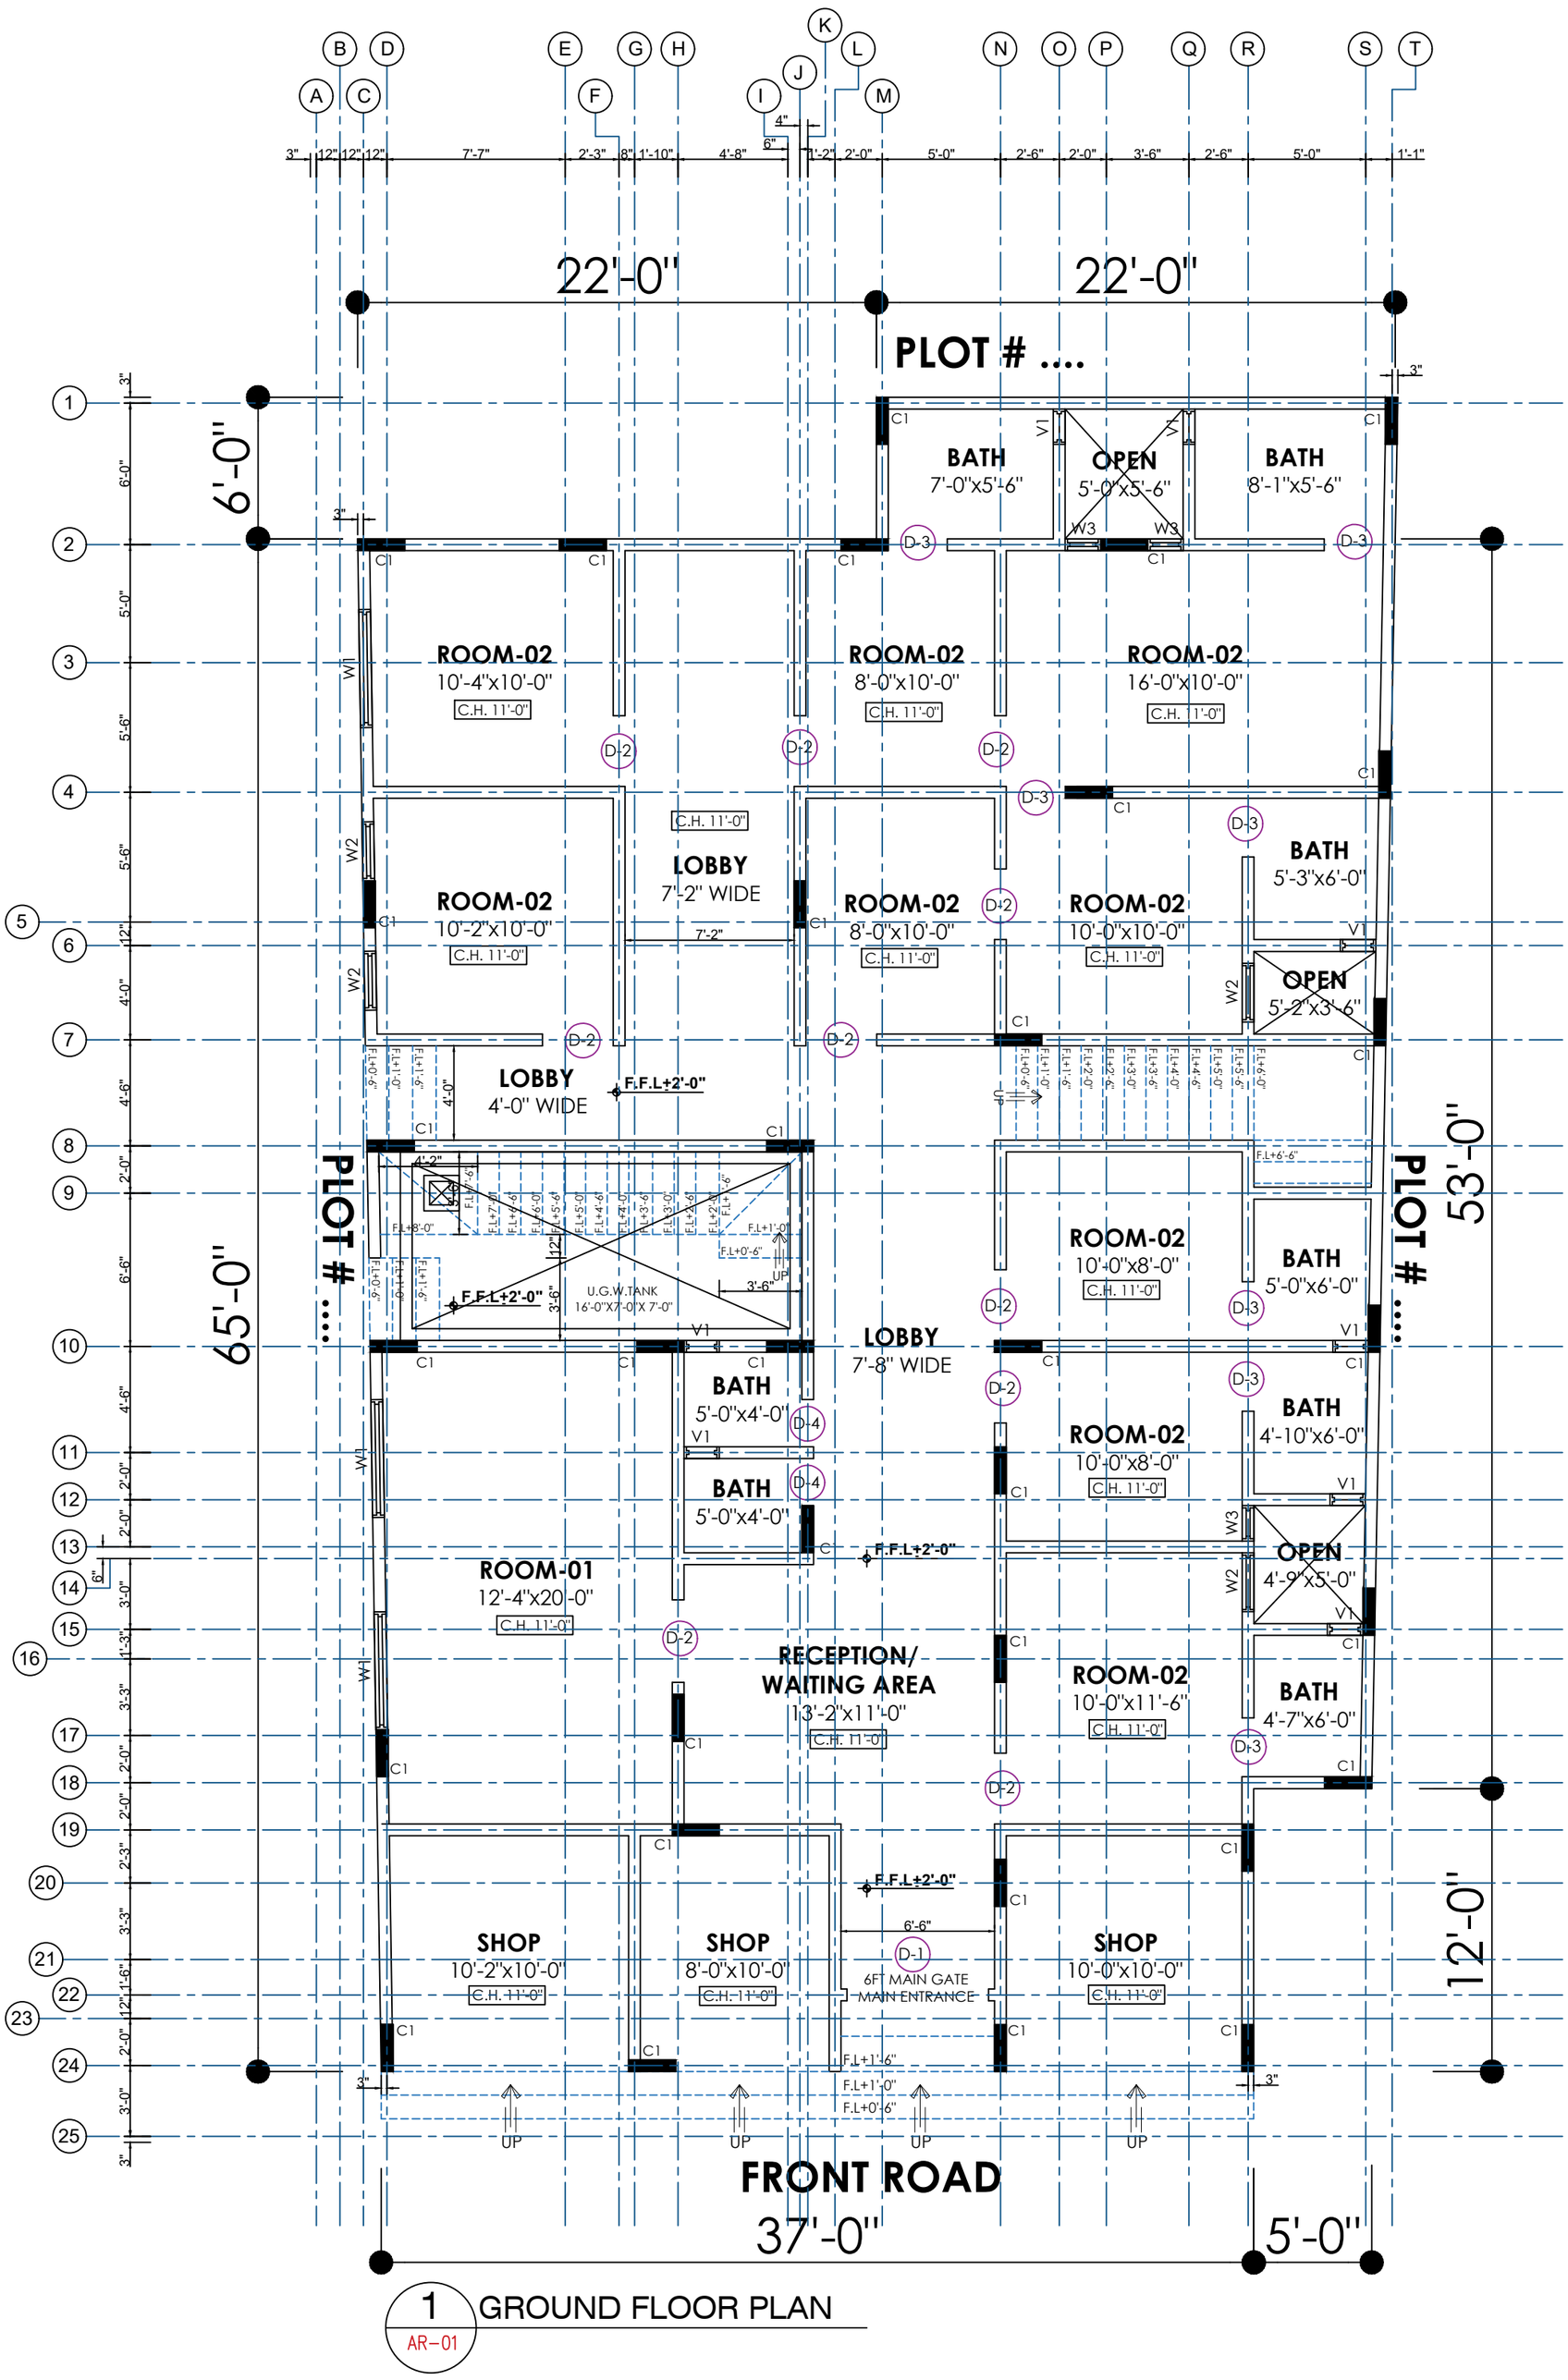

1 GROUND FLOOR PLAN

AR-01

GENERAL NOTES:

1. THE COPYRIGHT OF THIS DRAWING IS VESTED IN YourSpreadsheets AND IT MAY NOT BE REPRODUCED IN WHOLE OR PART OR USED FOR THE MANUFACTURE OF ANY ARTICLE WITHOUT THE EXPRESS PERMISSION OF THE COPYRIGHT HOLDERS.
2. WORK TO FIGURED DIMENSIONS ONLY.
3. THIS DRAWING IS TO BE READ IN CONJUNCTION WITH ALL RELEVANT ARCHITECT'S, SERVICE ENGINEER'S AND YourSpreadsheets DRAWINGS .

ALL DRWAING ARE THE PROPOERTY OF THE DESIGNER & THEY ARE NOT TO BE REPRODUCED IN WHOLE OR IN PART WITHOUT WRITTEN CONSENT FROM THE DESIGN WING

CONTRACTOR TO CHECK &VERIFY ALL DIMENSIONS BEFORE COMMENCING WORK & TO REPORT ANY DISCREPANCIES TO THE DESIGN WING.

DO NOT SCALE DRAWINGS.

ALL CONSTRUCTION TO BE ACCORDING TO BEST COMMON PRACTICE.

REV:	DESCRIPTION:	BY:	DATE:
A	ARCHITECTURE DRAWING	----	25-12-25
B	STRUCTURE DRAWING	----	27-12-25

PROJECT NAME:
300 SQ.YARD HOUSE ARCHITECTURE DRAWING

SIGNATURE BY:

DRAWING TITLE:
ARCHITECTURAL DRAWING

DRAWN BY: MUDASSIR

CHECKED BY: M.SHEHERYAR

APPROVED BY: M.SHEHERYAR

DATE: 27-DEC-2025

CLIENT
MR. ROHAN
KARACHI...

DESIGNED BY:-

E.D.C.O
ENGINEERING DESIGNING CONSTRUCTION OFFICIAL

ARCHITECT| PLANNERS| ENGINEERS| INTERIOR| B.O.Q| EXTERIOR| CONSULT| STRUCTURE DESIGN| PLANNING| LAND SURVEY| CONSTRUCTION| 3D ANIMATION VIDEO| RENOVATION|
MUHAMMAD SHEHERYAR
CONTACT- 0312-2118445|D.H.A PHASE VII

PROJECT NO: AR-7590

SCALE: 1/8"=1'-0"

SHEET SIZE: A3

DRAWING NO: ARC

SHEET NO ----------

REVISION: YES

UNIT: INCHES&FEET

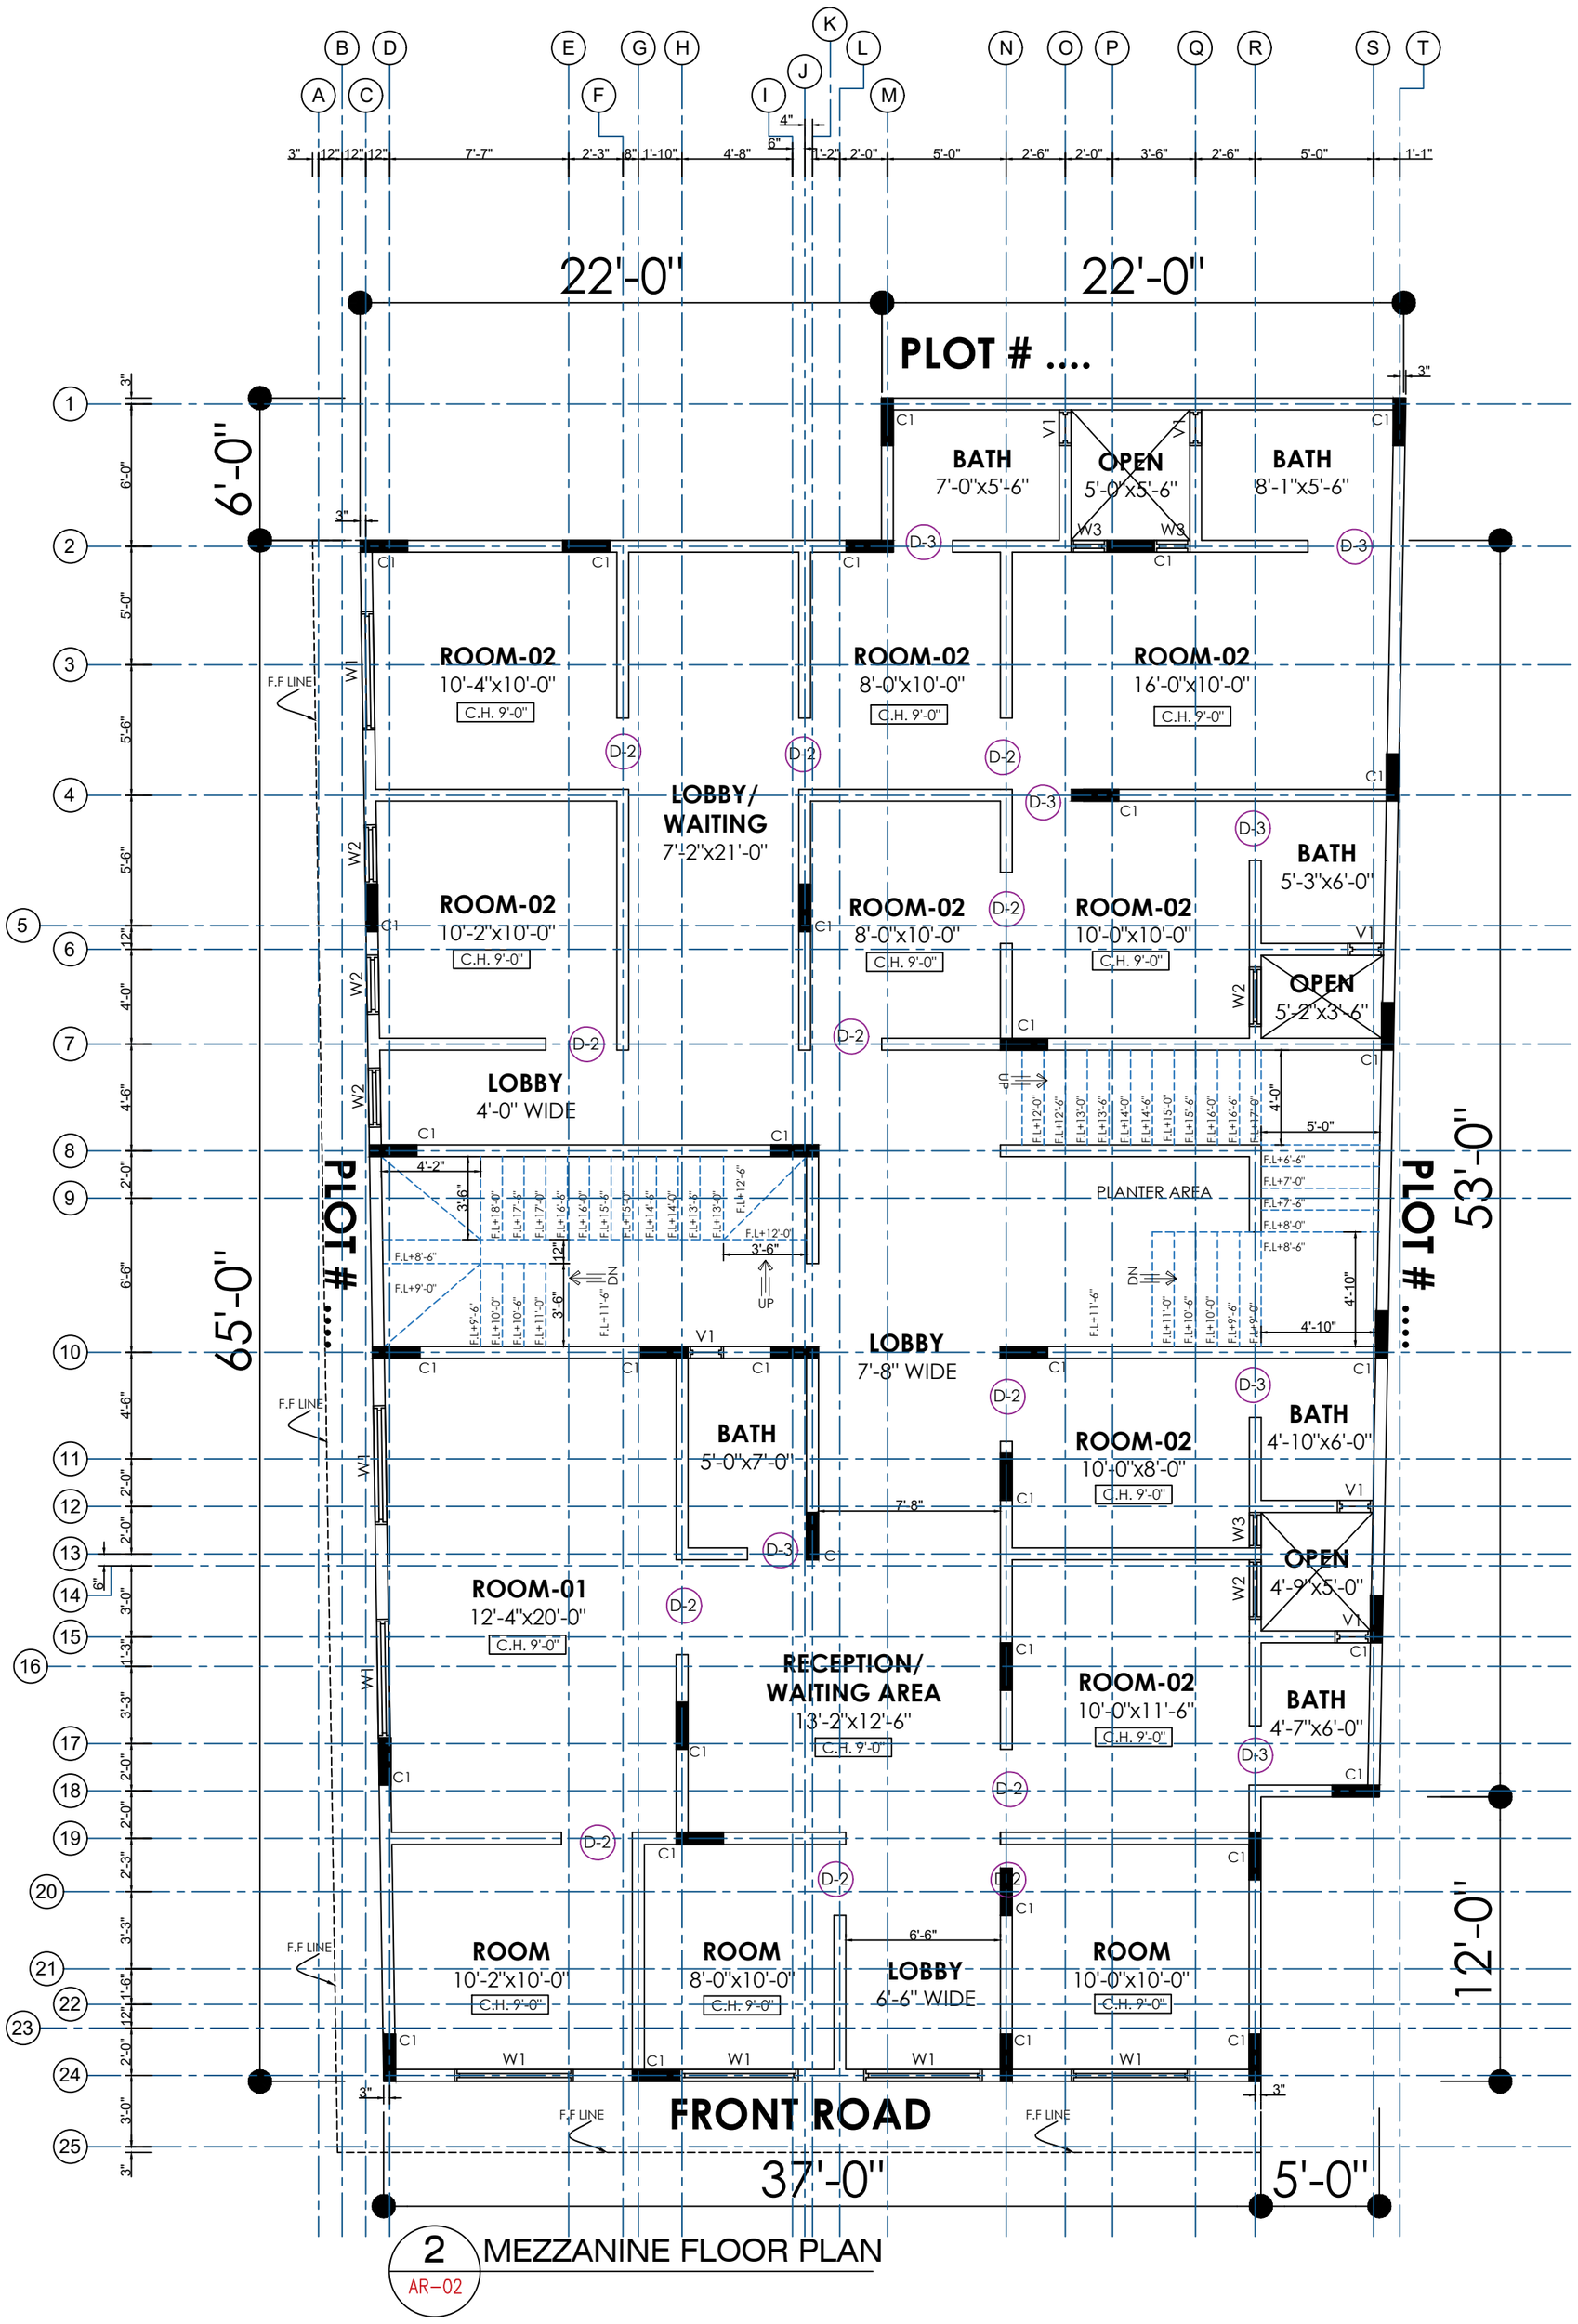

2 MEZZANINE FLOOR PLAN

AR–02

GENERAL NOTES:

1. THE COPYRIGHT OF THIS DRAWING IS VESTED IN YourSpreadsheets AND IT MAY NOT BE REPRODUCED IN WHOLE OR PART OR USED FOR THE MANUFACTURE OF ANY ARTICLE WITHOUT THE EXPRESS PERMISSION OF THE COPYRIGHT HOLDERS.
2. WORK TO FIGURED DIMENSIONS ONLY.
3. THIS DRAWING IS TO BE READ IN CONJUNCTION WITH ALL RELEVANT ARCHITECT'S, SERVICE ENGINEER'S AND YourSpreadsheets DRAWINGS .
ALL DRWAING ARE THE PROPOERTY OF THE DESIGNER & THEY ARE NOT TO BE REPRODUCED IN WHOLE OR IN PART WITHOUT WRITTEN CONSENT FROM THE DESIGN WING
CONTRACTOR TO CHECK &VERIFY ALL DIMENSIONS BEFORE COMMENCING WORK & TO REPORT ANY DISCREPANCIES TO THE DESIGN WING.
DO NOT SCALE DRAWINGS.
ALL CONSTRUCTION TO BE ACCORDING TO BEST COMMON PRACTICE.

REV:	DESCRIPTION:	BY:	DATE:
A	ARCHITECTURE DRAWING	----	25-12-25
B	STRUCTURE DRAWING	----	27-12-25

PROJECT NAME:
300 SQ.YARD HOUSE ARCHITECTURE DRAWING

SIGNATURE BY:

DRAWING TITLE:
ARCHITECTURAL DRAWING

DRAWN BY: MUDASSIR

CHECKED BY: M.SHEHERYAR

APPROVED BY: M.SHEHERYAR

DATE: 27-DEC-2025

CLIENT
MR. ROHAN
KARACHI...

DESIGNED BY:-

E.D.C.O
ENGINEERING DESIGNING CONSTRUCTION OFFICIAL
ARCHITECT| PLANNERS| ENGINEERS| INTERIOR| B.O.Q| EXTERIOR| CONSULT| STRUCTURE DESIGN| PLANNING| LAND SURVEY| CONSTRUCTION| 3D ANIMATION VIDEO| RENOVATION|
MUHAMMAD SHEHERYAR
CONTACT- 0312-2118445|D.H.A PHASE VII

PROJECT NO: AR-7590

SCALE: 1/8"=1'-0"

SHEET SIZE: A3

DRAWING NO: ARC

SHEET NO ----------

REVISION: YES

UNIT: INCHES&FEET

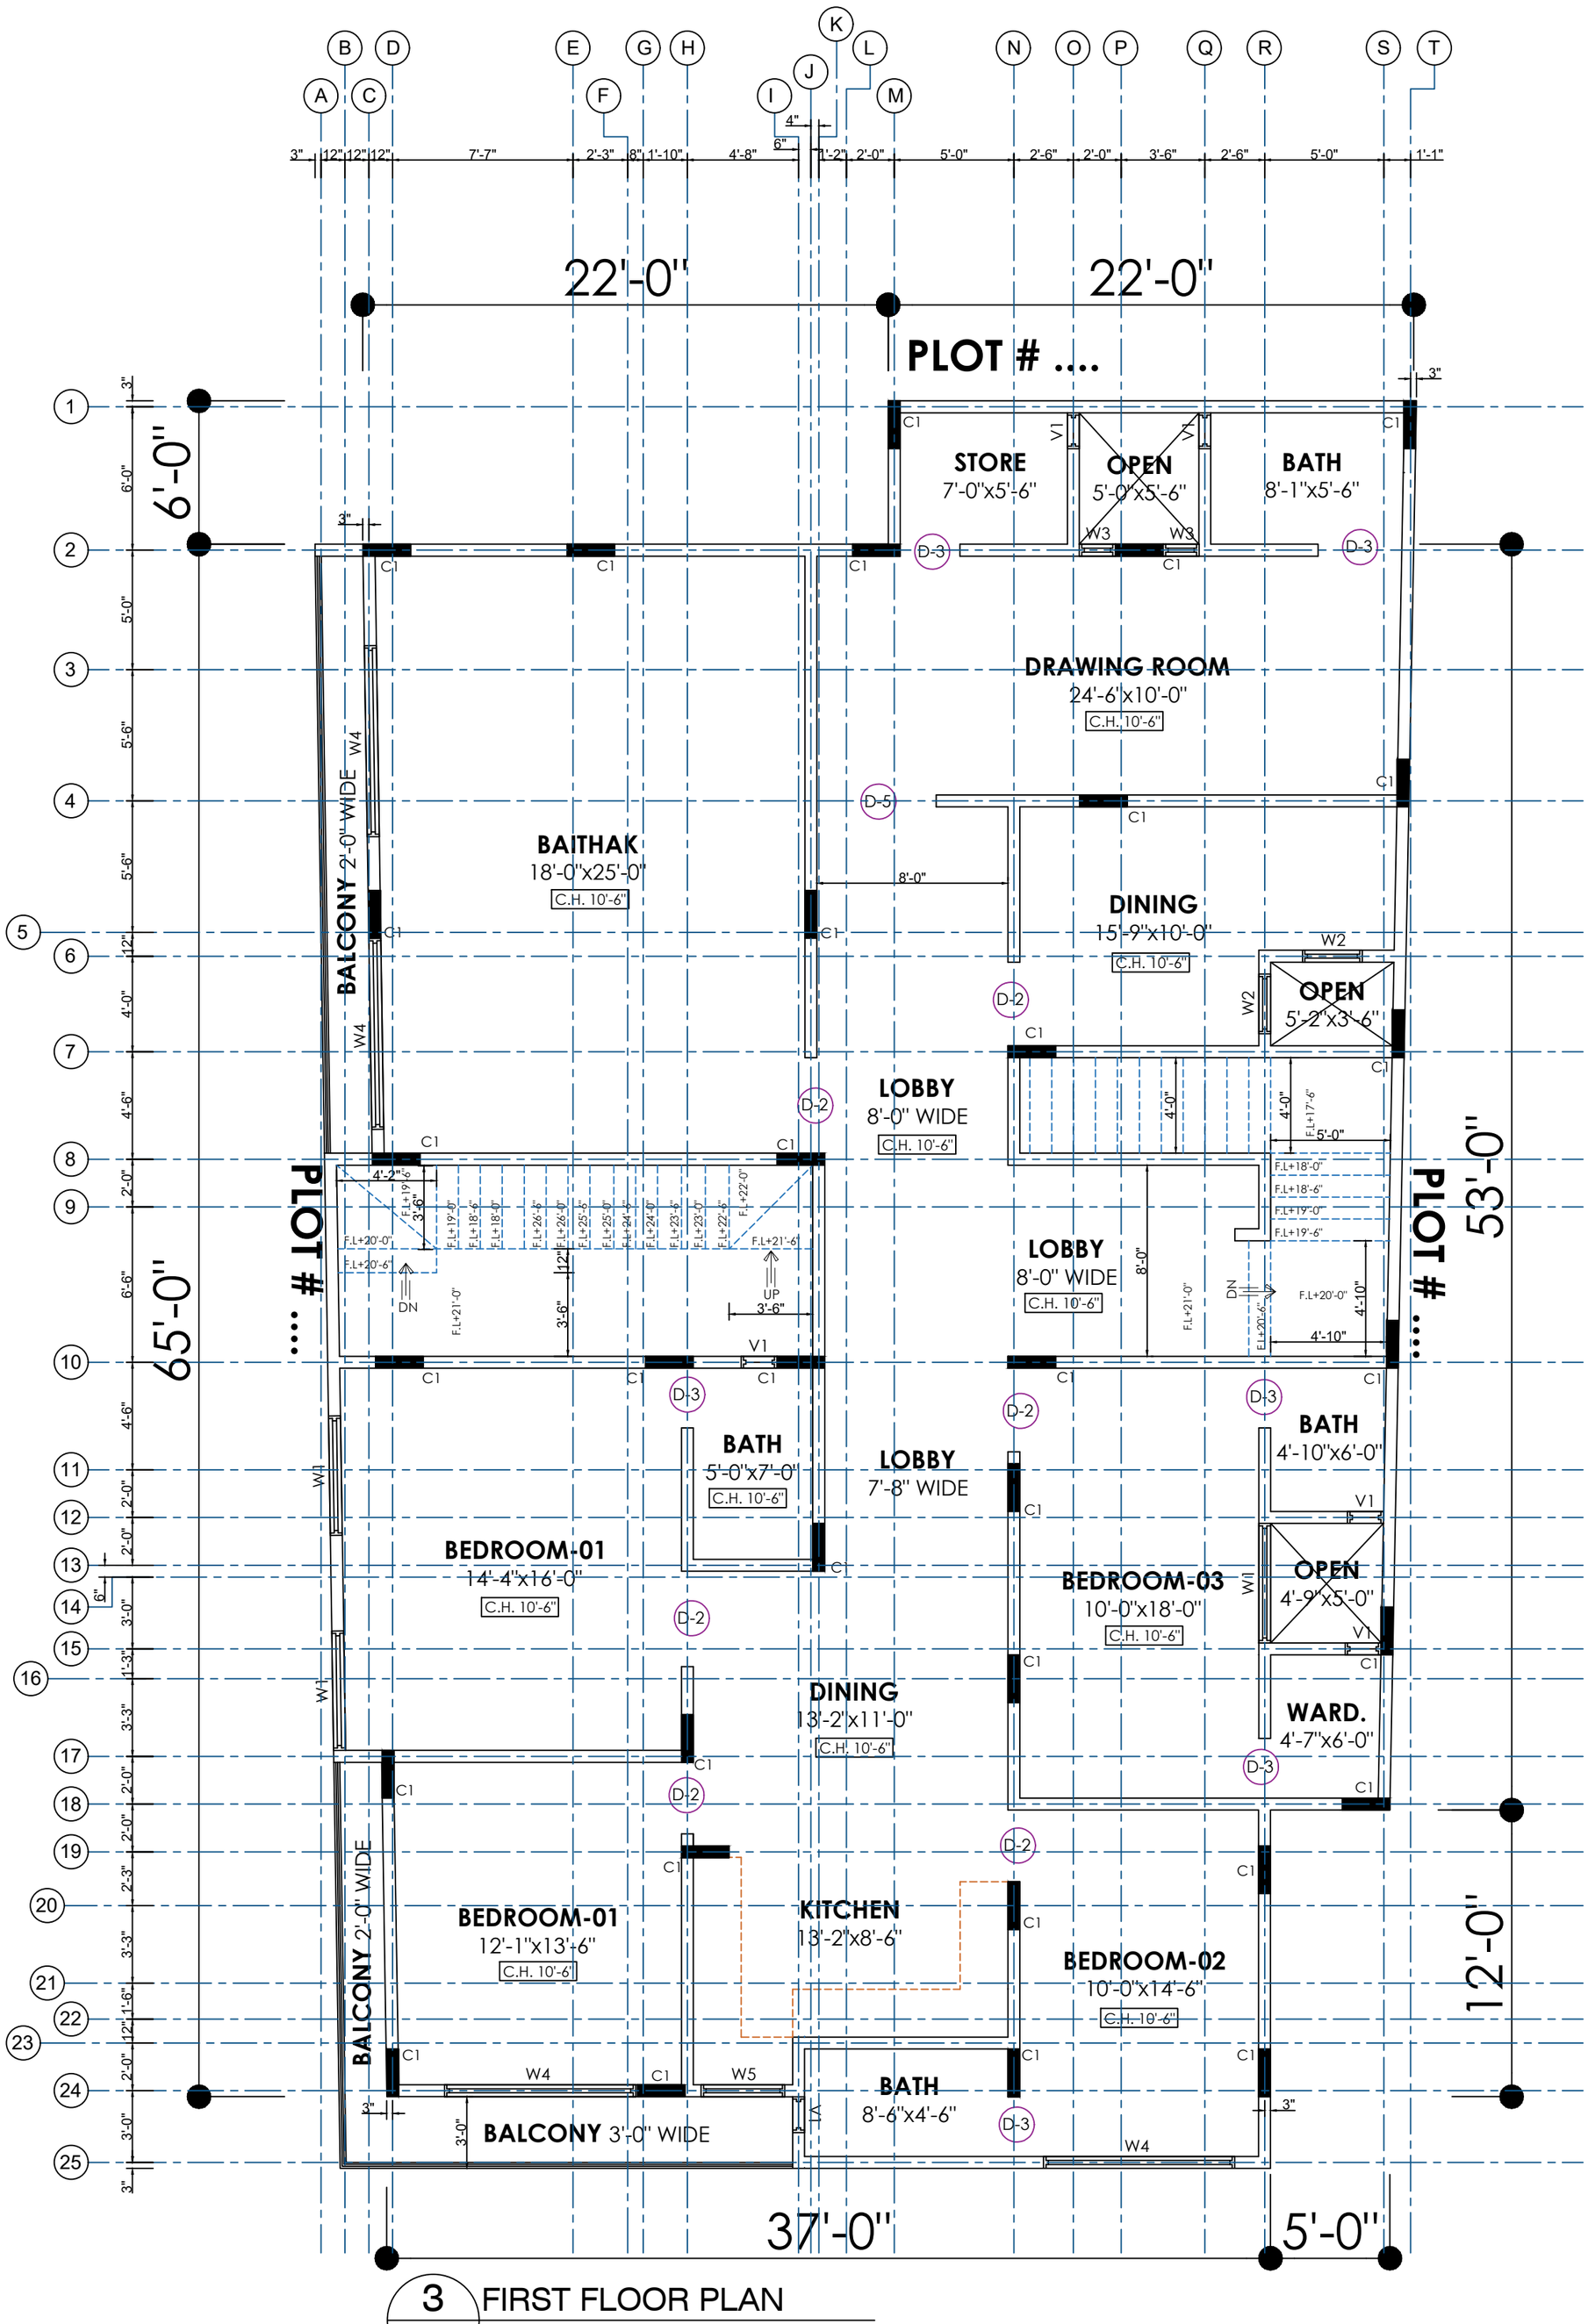

3 FIRST FLOOR PLAN

AR-03

GENERAL NOTES:

1. THE COPYRIGHT OF THIS DRAWING IS VESTED IN YourSpreadsheets AND IT MAY NOT BE REPRODUCED IN WHOLE OR PART OR USED FOR THE MANUFACTURE OF ANY ARTICLE WITHOUT THE EXPRESS PERMISSION OF THE COPYRIGHT HOLDERS.
2. WORK TO FIGURED DIMENSIONS ONLY.
3. THIS DRAWING IS TO BE READ IN CONJUNCTION WITH ALL RELEVANT ARCHITECT'S, SERVICE ENGINEER'S AND YourSpreadsheets DRAWINGS .

ALL DRWAING ARE THE PROPOERTY OF THE DESIGNER & THEY ARE NOT TO BE REPRODUCED IN WHOLE OR IN PART WITHOUT WRITTEN CONSENT FROM THE DESIGN WING
CONTRACTOR TO CHECK &VERIFY ALL DIMENSIONS BEFORE COMMENCING WORK & TO REPORT ANY DISCREPANCIES TO THE DESIGN WING.
DO NOT SCALE DRAWINGS.
ALL CONSTRUCTION TO BE ACCORDING TO BEST COMMON PRACTICE.

REV:	DESCRIPTION:	BY:	DATE:
A	ARCHITECTURE DRAWING	----	25-12-25
B	STRUCTURE DRAWING	----	27-12-25

PROJECT NAME:
300 SQ.YARD HOUSE ARCHITECTURE DRAWING

SIGNATURE BY:

DRAWING TITLE:
ARCHITECTURAL DRAWING

DRAWN BY: MUDASSIR
CHECKED BY: M.SHEHERYAR
APPROVED BY: M.SHEHERYAR
DATE: 27-DEC-2025

CLIENT
MR. ROHAN
KARACHI...

DESIGNED BY:-
E.D.C.O
ENGINEERING DESIGNING CONSTRUCTION OFFICIAL
ARCHITECT| PLANNERS| ENGINEERS| INTERIOR| B.O.Q| EXTERIOR| CONSULT| STRUCTURE DESIGN| PLANNING| LAND SURVEY| CONSTRUCTION| 3D ANIMATION VIDEO| RENOVATION|
MUHAMMAD SHEHERYAR
CONTACT- 0312-2118445|D.H.A PHASE VII

PROJECT NO: AR-7590
SCALE: 1/8"=1'-0"
SHEET SIZE: A3
DRAWING NO: ARC
SHEET NO ----------
REVISION: YES
UNIT: INCHES&FEET

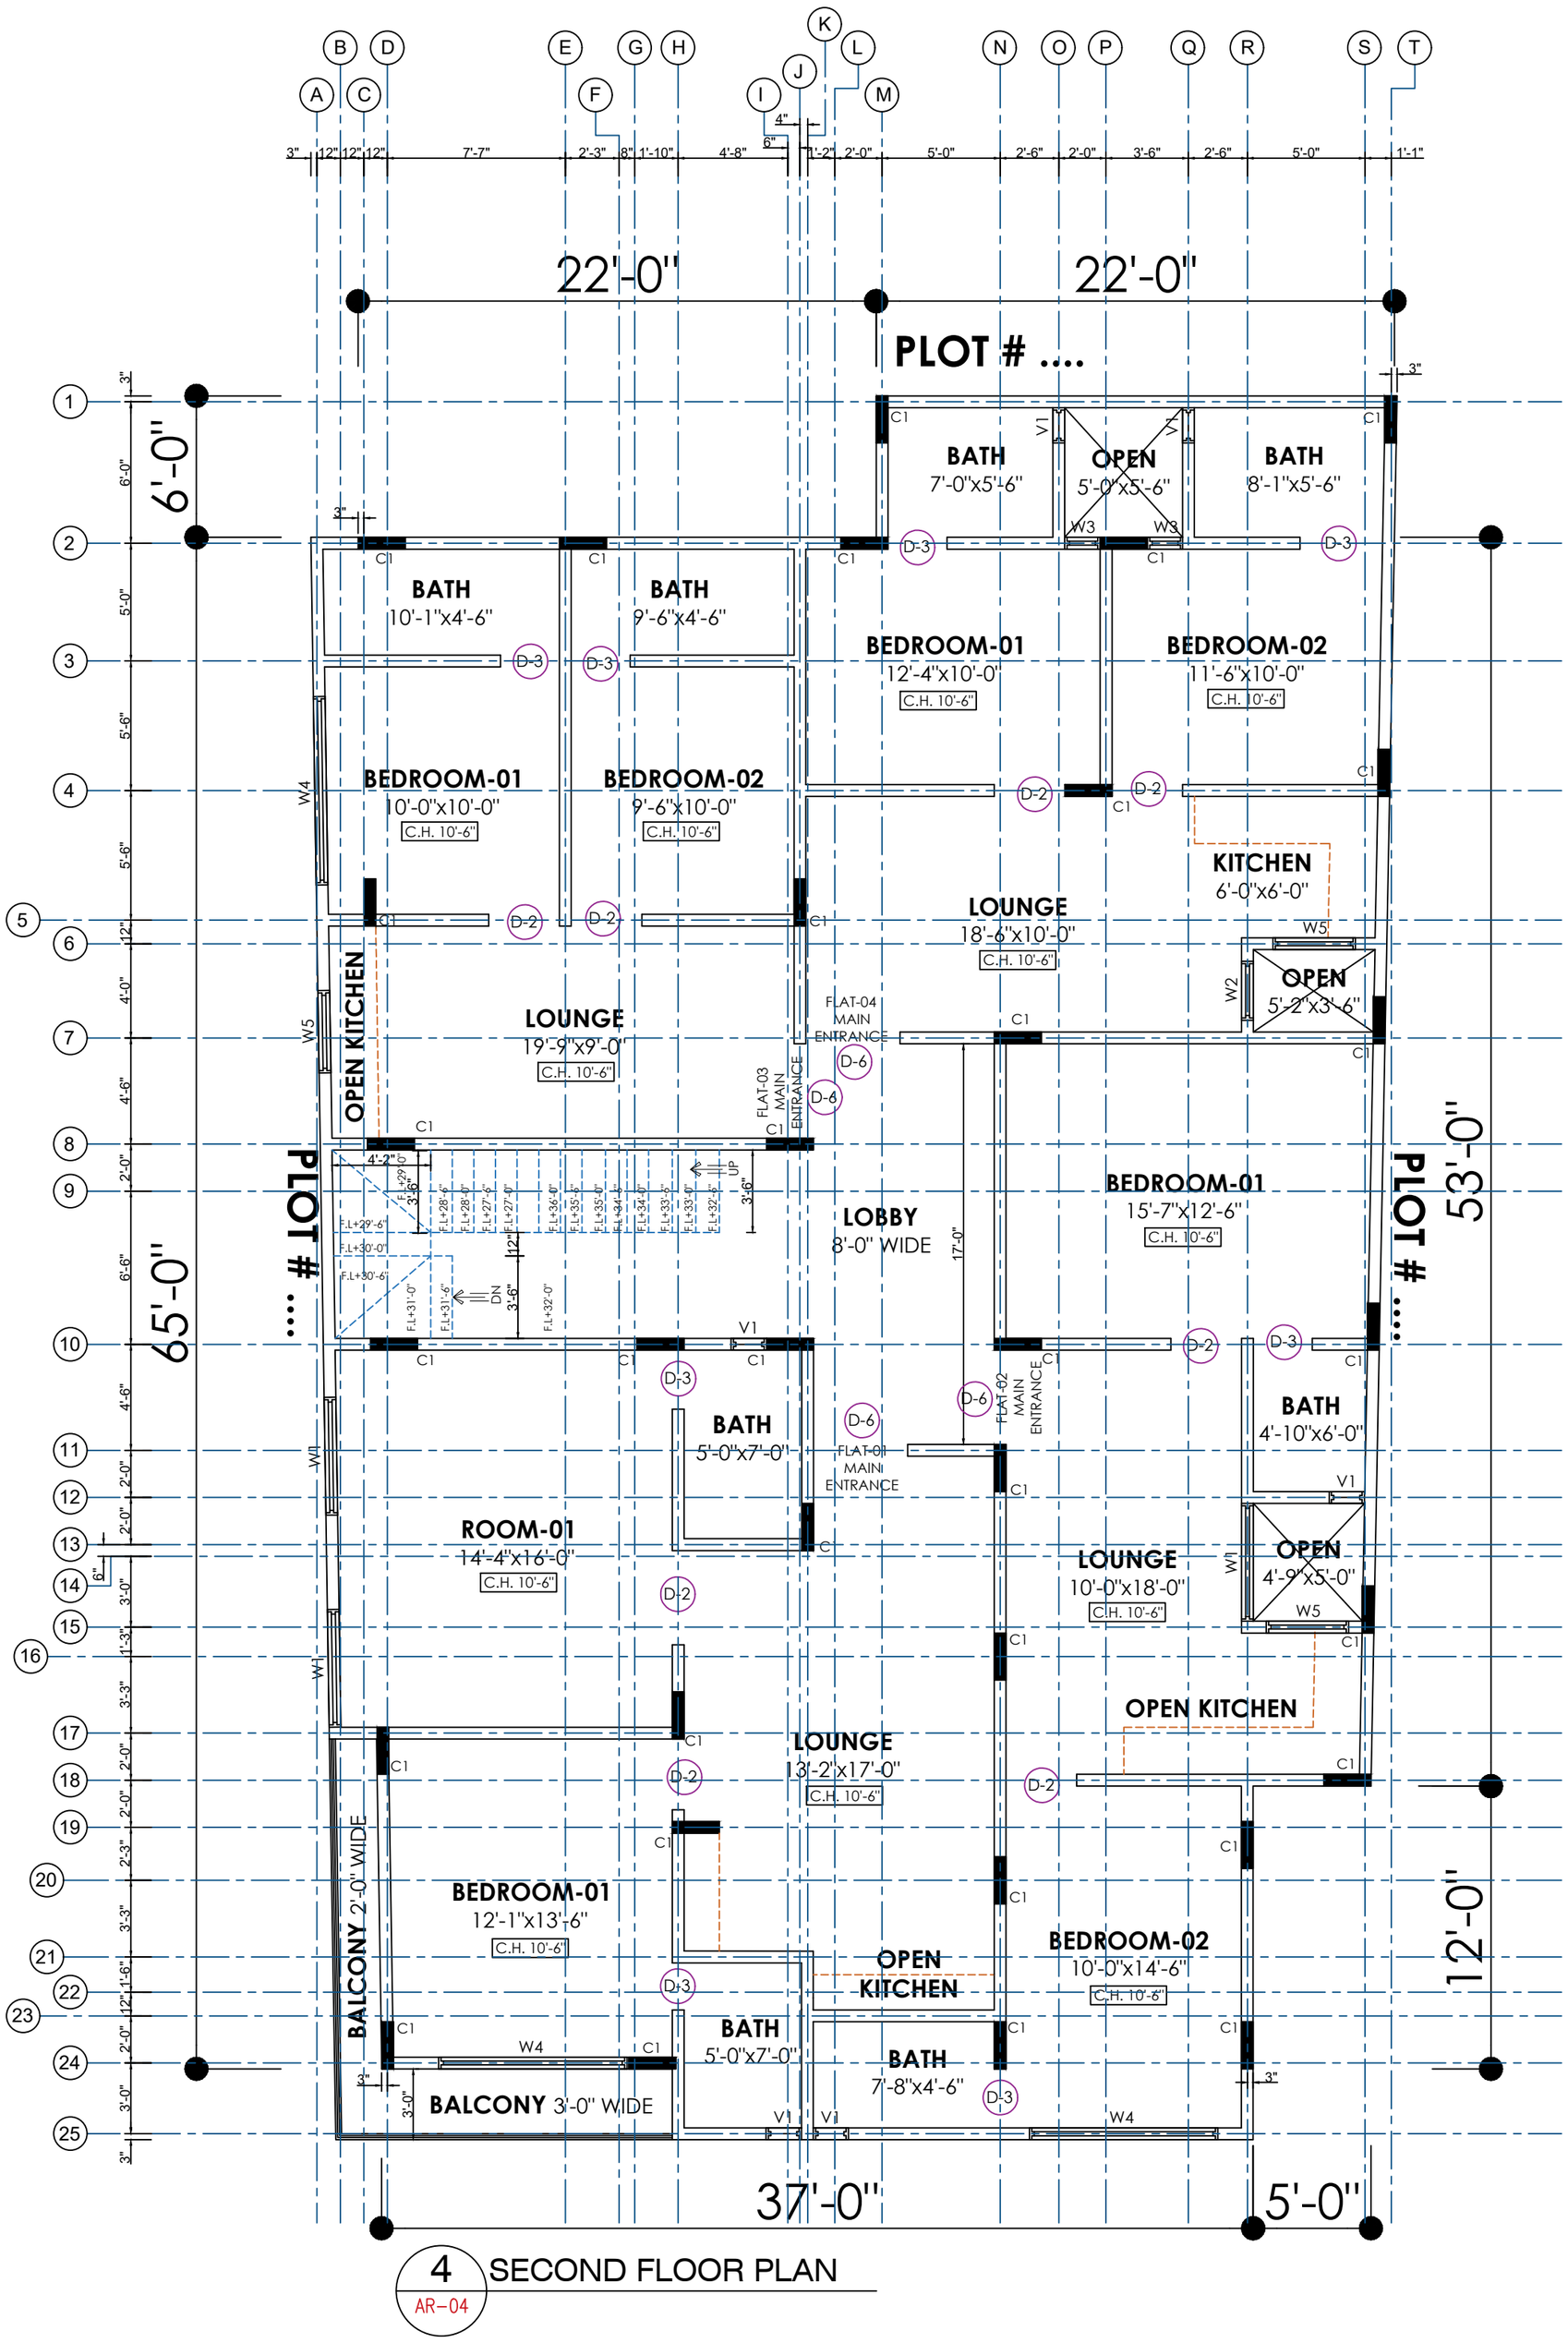

4 SECOND FLOOR PLAN
AR-04

GENERAL NOTES:

1. THE COPYRIGHT OF THIS DRAWING IS VESTED IN YourSpreadsheets AND IT MAY NOT BE REPRODUCED IN WHOLE OR PART OR USED FOR THE MANUFACTURE OF ANY ARTICLE WITHOUT THE EXPRESS PERMISSION OF THE COPYRIGHT HOLDERS.
2. WORK TO FIGURED DIMENSIONS ONLY.
3. THIS DRAWING IS TO BE READ IN CONJUNCTION WITH ALL RELEVANT ARCHITECT'S, SERVICE ENGINEER'S AND YourSpreadsheets DRAWINGS .
ALL DRWAING ARE THE PROPOERTY OF THE DESIGNER & THEY ARE NOT TO BE REPRODUCED IN WHOLE OR IN PART WITHOUT WRITTEN CONSENT FROM THE DESIGN WING
CONTRACTOR TO CHECK &VERIFY ALL DIMENSIONS BEFORE COMMENCING WORK & TO REPORT ANY DISCREPANCIES TO THE DESIGN WING.
DO NOT SCALE DRAWINGS.
ALL CONSTRUCTION TO BE ACCORDING TO BEST COMMON PRACTICE.

REV:	DESCRIPTION:	BY:	DATE:
A	ARCHITECTURE DRAWING	----	25-12-25
B	STRUCTURE DRAWING	----	27-12-25

PROJECT NAME:
300 SQ.YARD HOUSE ARCHITECTURE DRAWING

SIGNATURE BY:

DRAWING TITLE:
ARCHITECTURAL DRAWING

DRAWN BY: MUDASSIR
CHECKED BY: M.SHEHERYAR
APPROVED BY: M.SHEHERYAR
DATE: 27-DEC-2025

CLIENT
MR. ROHAN
KARACHI...

DESIGNED BY:-

E.D.C.O
ENGINEERING DESIGNING CONSTRUCTION OFFICIAL
ARCHITECT| PLANNERS| ENGINEERS| INTERIOR| B.O.Q| EXTERIOR| CONSULT| STRUCTURE DESIGN| PLANNING| LAND SURVEY| CONSTRUCTION| 3D ANIMATION VIDEO| RENOVATION|
MUHAMMAD SHEHERYAR
CONTACT- 0312-2118445|D.H.A PHASE VII

PROJECT NO: AR-7590
SCALE: 1/8"=1'-0"
SHEET SIZE: A3
DRAWING NO: ARC
SHEET NO ----------
REVISION: YES
UNIT: INCHES&FEET

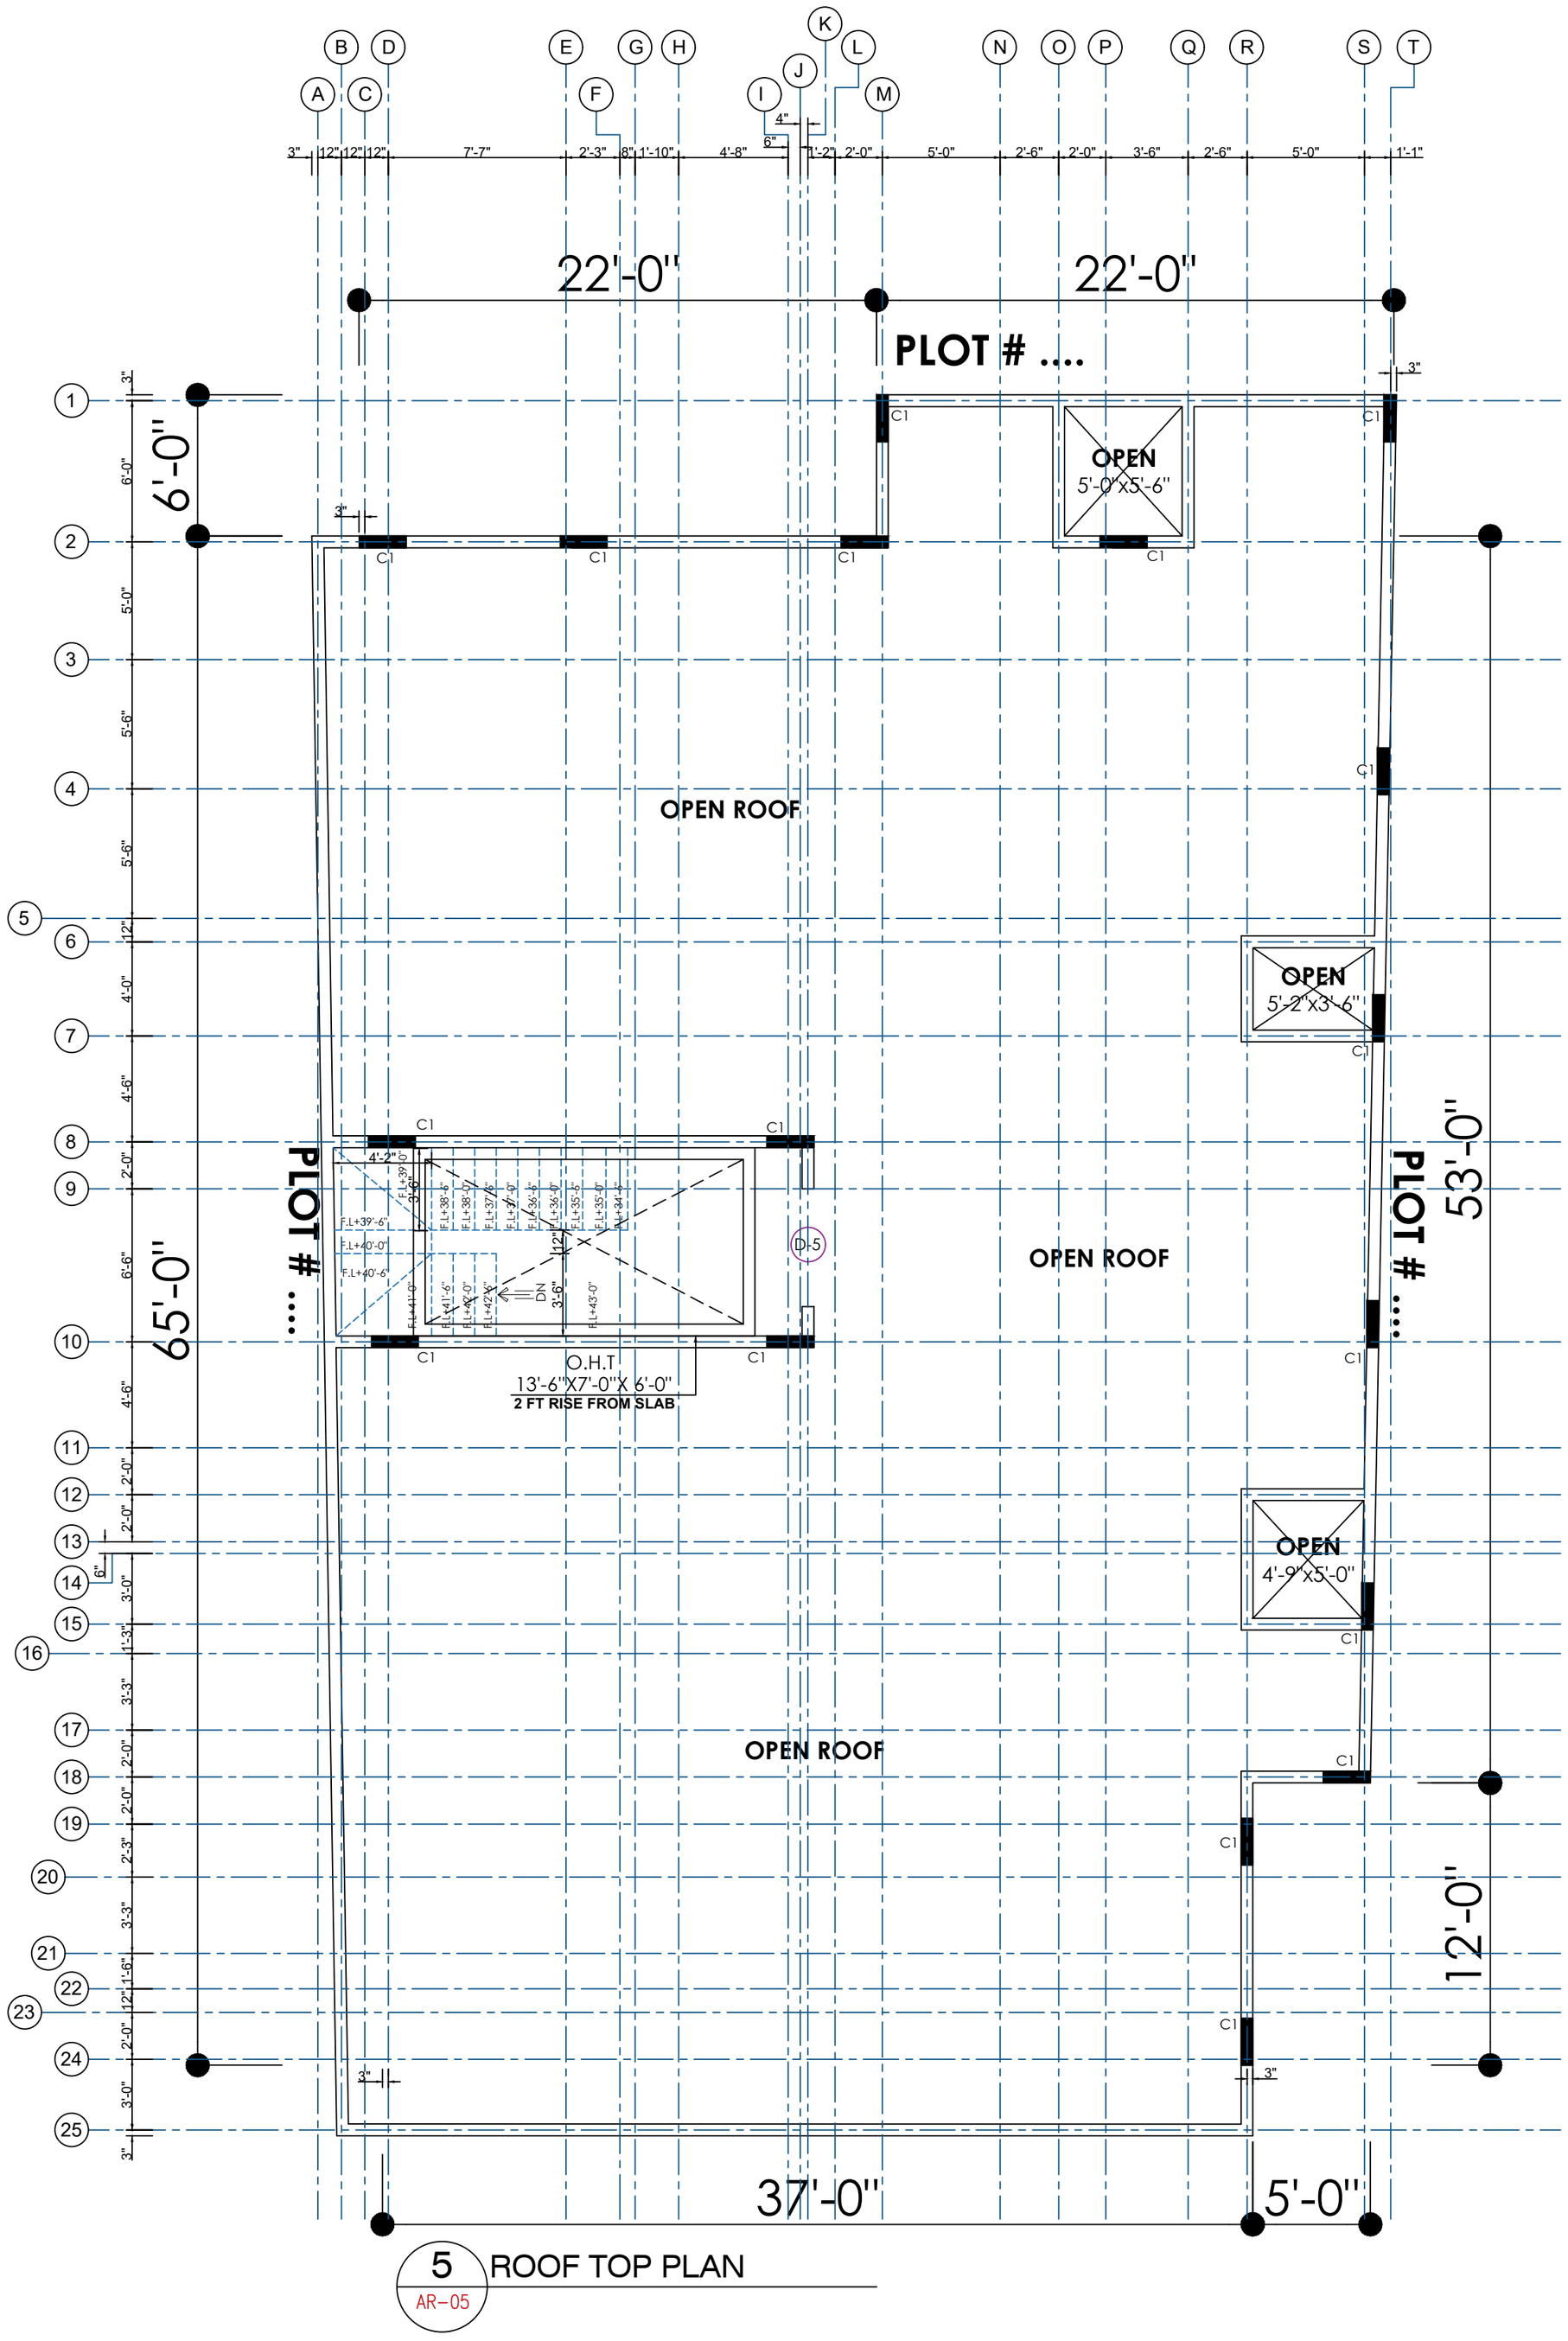

5 ROOF TOP PLAN
AR-05

GENERAL NOTES:

1. THE COPYRIGHT OF THIS DRAWING IS VESTED IN YourSpreadsheets AND IT MAY NOT BE REPRODUCED IN WHOLE OR PART OR USED FOR THE MANUFACTURE OF ANY ARTICLE WITHOUT THE EXPRESS PERMISSION OF THE COPYRIGHT HOLDERS.
2. WORK TO FIGURED DIMENSIONS ONLY.
3. THIS DRAWING IS TO BE READ IN CONJUNCTION WITH ALL RELEVANT ARCHITECT'S, SERVICE ENGINEER'S AND YourSpreadsheets DRAWINGS .

ALL DRWAING ARE THE PROPOERTY OF THE DESIGNER & THEY ARE NOT TO BE REPRODUCED IN WHOLE OR IN PART WITHOUT WRITTEN CONSENT FROM THE DESIGN WING
CONTRACTOR TO CHECK &VERIFY ALL DIMENSIONS BEFORE COMMENCING WORK & TO REPORT ANY DISCREPANCIES TO THE DESIGN WING.
DO NOT SCALE DRAWINGS.
ALL CONSTRUCTION TO BE ACCORDING TO BEST COMMON PRACTICE.

REV:	DESCRIPTION:	BY:	DATE:
A	ARCHITECTURE DRAWING	----	25-12-25
B	STRUCTURE DRAWING	----	27-12-25

PROJECT NAME:
300 SQ.YARD HOUSE ARCHITECTURE DRAWING

SIGNATURE BY:

DRAWING TITLE:
ARCHITECTURAL DRAWING

DRAWN BY: MUDASSIR
CHECKED BY: M.SHEHERYAR
APPROVED BY: M.SHEHERYAR
DATE: 27-DEC-2025

CLIENT
MR. ROHAN
KARACHI...

DESIGNED BY:-

E.D.C.O
ENGINEERING DESIGNING CONSTRUCTION OFFICIAL
ARCHITECT| PLANNERS| ENGINEERS| INTERIOR| B.O.Q| EXTERIOR| CONSULT| STRUCTURE DESIGN| PLANNING| LAND SURVEY| CONSTRUCTION| 3D ANIMATION VIDEO| RENOVATION|
MUHAMMAD SHEHERYAR
CONTACT- 0312-2118445|D.H.A PHASE VII

PROJECT NO: AR-7590
SCALE: 1/8"=1'-0"
SHEET SIZE: A3
DRAWING NO: ARC
SHEET NO ----------
REVISION: YES
UNIT: INCHES&FEET

SCHEDULE OF JOINERY

DOORS

D1	= 6'-0" X 7'-0"
D2	= 3'-0" X 8'-0"
D3	= 2'-6" X 8'-0"
D4	= 2'-0" X 8'-0"
D5	= 5'-0" X 8'-0"

WINDOWS

W1	= 5'-0" X 6'-0"
W2	= 2'-6" X 6'-0"
W3	= 1'-6" X 6'-0"
W4	= 8'-0" X 6'-0"
W5	= 3'-6" X 3'-6"

VENTILATORS:

V1	= 1'-6" X 2'-0"

GENERAL NOTES:

1. THE COPYRIGHT OF THIS DRAWING IS VESTED IN YourSpreadsheets AND IT MAY NOT BE REPRODUCED IN WHOLE OR PART OR USED FOR THE MANUFACTURE OF ANY ARTICLE WITHOUT THE EXPRESS PERMISSION OF THE COPYRIGHT HOLDERS.
2. WORK TO FIGURED DIMENSIONS ONLY.
3. THIS DRAWING IS TO BE READ IN CONJUNCTION WITH ALL RELEVANT ARCHITECT'S, SERVICE ENGINEER'S AND YourSpreadsheets DRAWINGS .
ALL DRWAING ARE THE PROPOERTY OF THE DESIGNER & THEY ARE NOT TO BE REPRODUCED IN WHOLE OR IN PART WITHOUT WRITTEN CONSENT FROM THE DESIGN WING
CONTRACTOR TO CHECK &VERIFY ALL DIMENSIONS BEFORE COMMENCING WORK & TO REPORT ANY DISCREPANCIES TO THE DESIGN WING.
DO NOT SCALE DRAWINGS.
ALL CONSTRUCTION TO BE ACCORDING TO BEST COMMON PRACTICE.

REV:	DESCRIPTION:	BY:	DATE:
A	ARCHITECTURE DRAWING	----	25-12-25
B	STRUCTURE DRAWING	----	27-12-25

PROJECT NAME:
300 SQ.YARD HOUSE ARCHITECTURE DRAWING

SIGNATURE BY:

DRAWING TITLE:
ARCHITECTURAL DRAWING

DRAWN BY: MUDASSIR
CHECKED BY: M.SHEHERYAR
APPROVED BY: M.SHEHERYAR
DATE: 27-DEC-2025

CLIENT
MR. ROHAN
KARACHI...

DESIGNED BY:-
E.D.C.O
ENGINEERING DESIGNING CONSTRUCTION OFFICIAL PVT
ARCHITECT| PLANNERS| ENGINEERS| INTERIOR| B.O.Q| EXTERIOR| CONSULT| STRUCTURE DESIGN| PLANNING| LAND SURVEY| CONSTRUCTION| 3D ANIMATION VIDEO| RENOVATION|
MUHAMMAD SHEHERYAR
CONTACT- 0312-2118445|D.H.A PHASE VII

PROJECT NO: AR-7590
SCALE: 1/8"=1'-0"
SHEET SIZE: A3
DRAWING NO: ARC
SHEET NO ----------
REVISION: YES
UNIT: INCHES&FEET

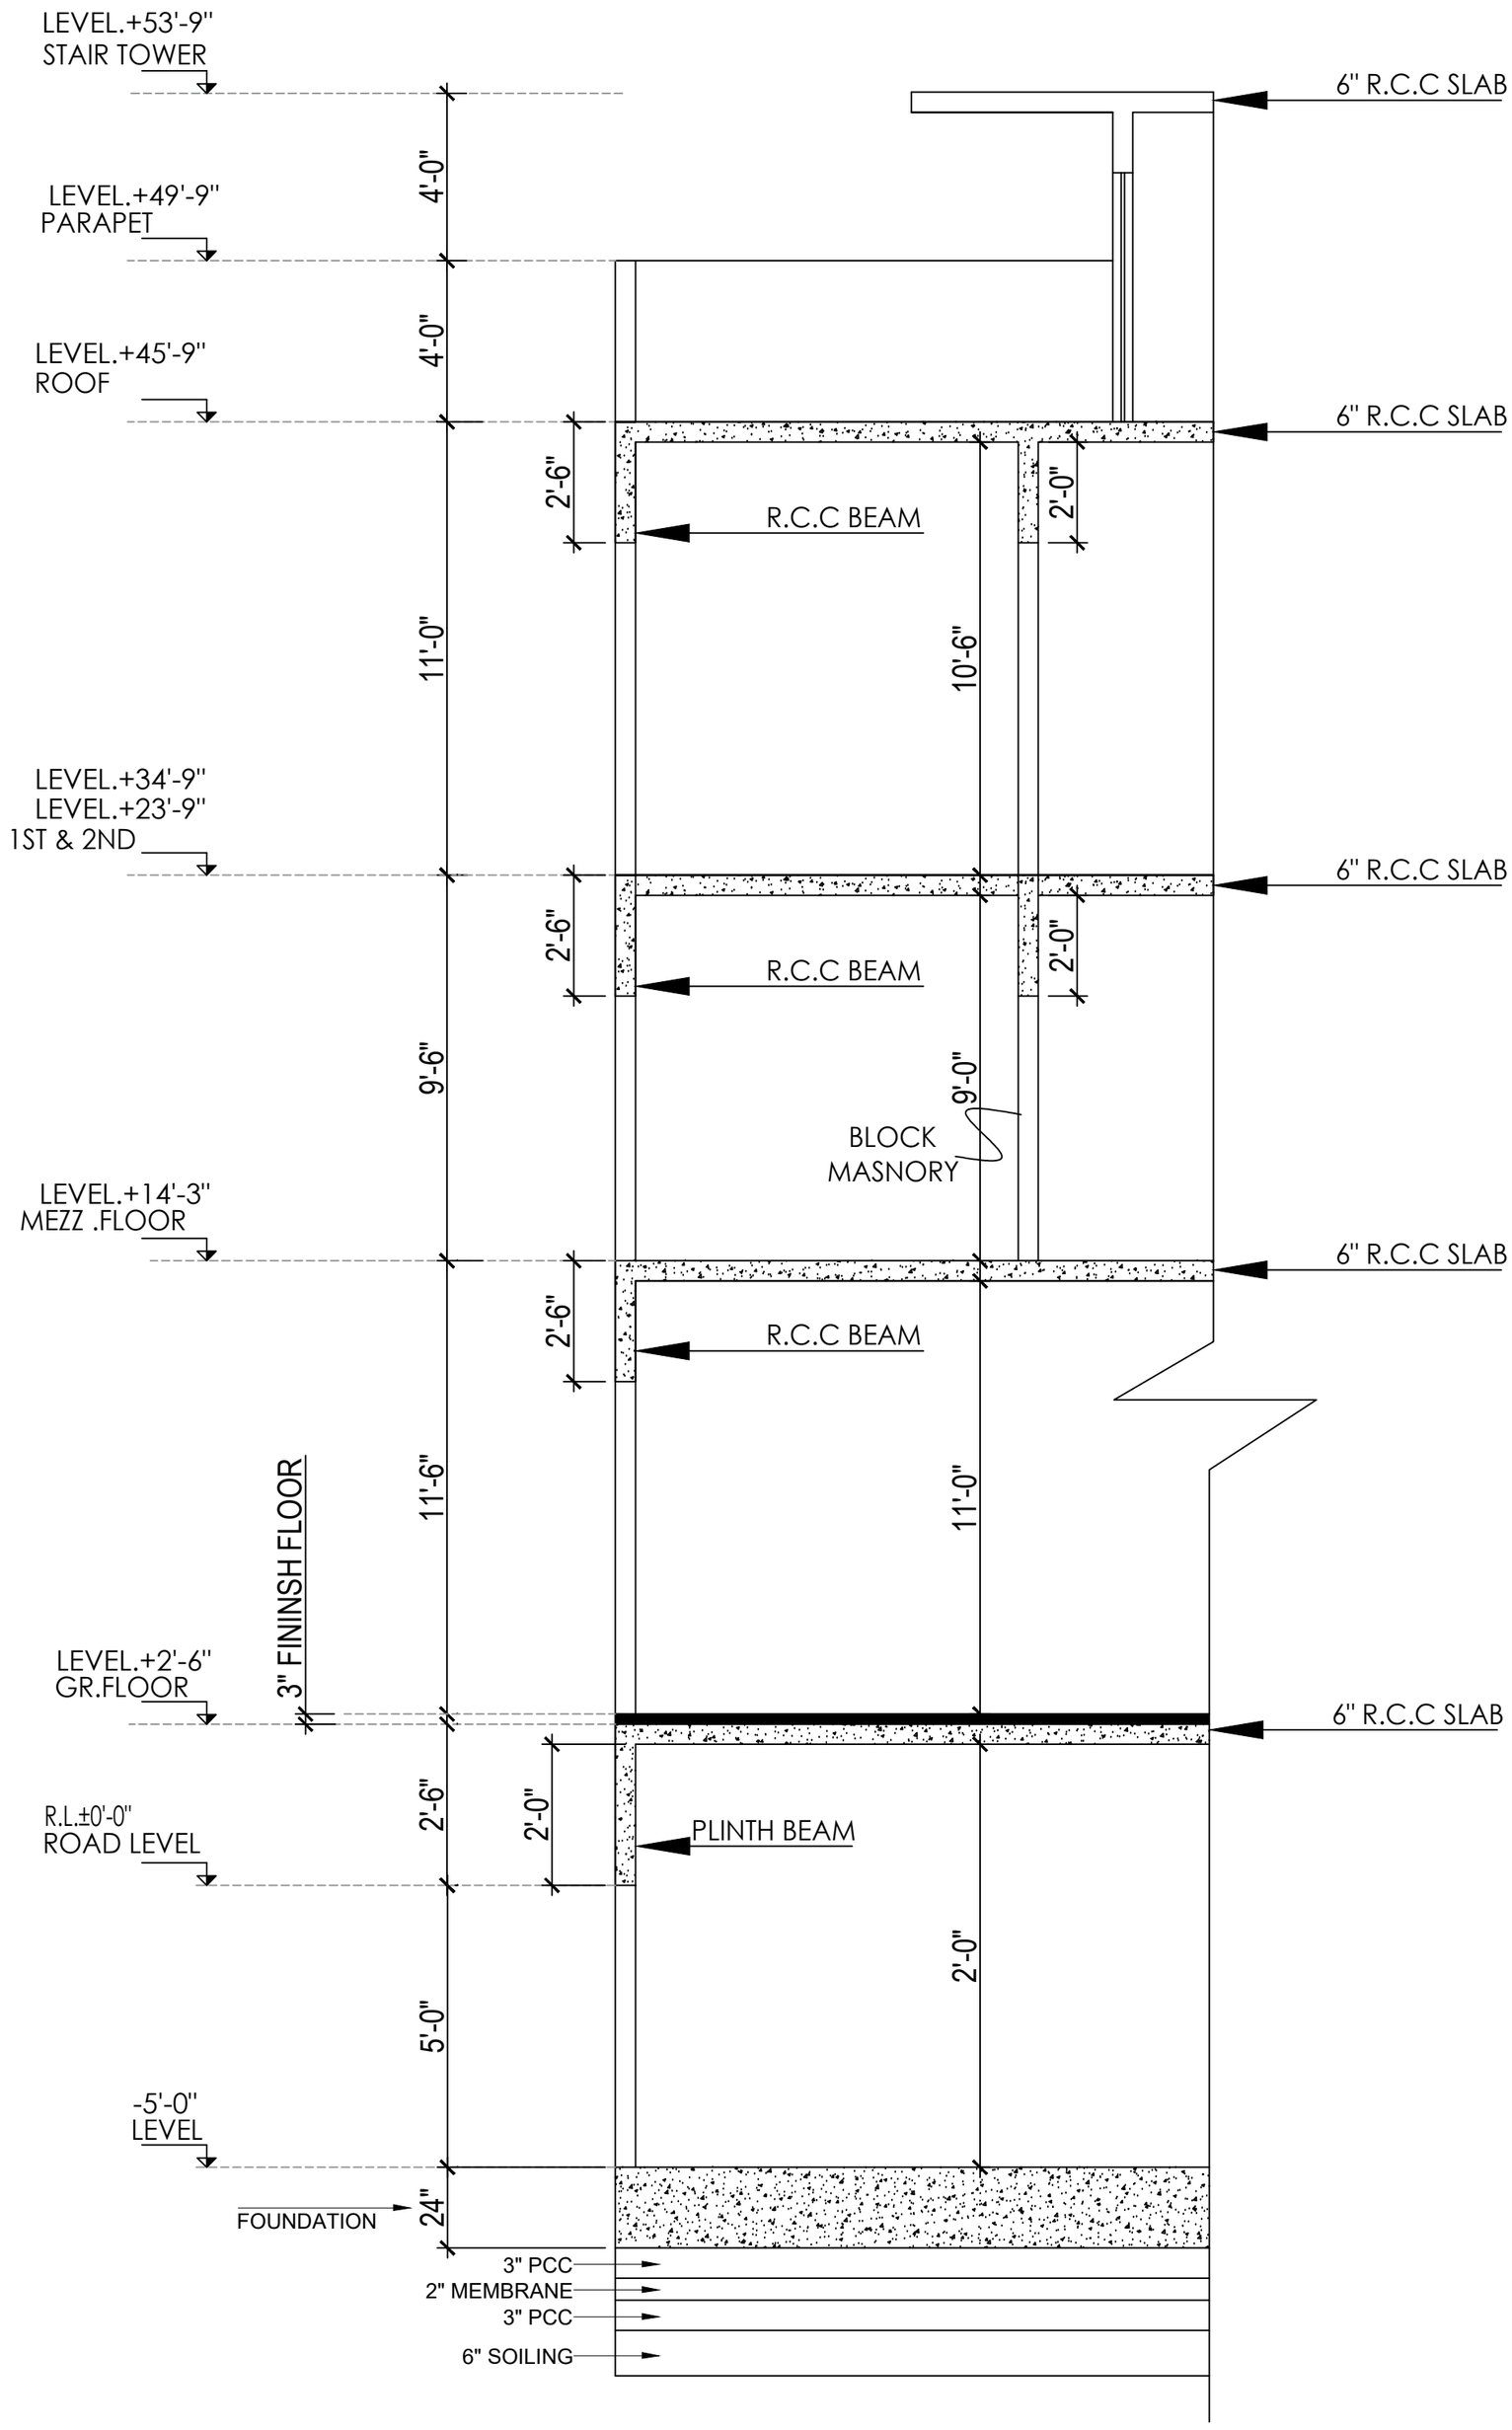

TYPICAL SECTION

GENERAL NOTES:

1. THE COPYRIGHT OF THIS DRAWING IS VESTED IN YourSpreadsheets AND IT MAY NOT BE REPRODUCED IN WHOLE OR PART OR USED FOR THE MANUFACTURE OF ANY ARTICLE WITHOUT THE EXPRESS PERMISSION OF THE COPYRIGHT HOLDERS.
2. WORK TO FIGURED DIMENSIONS ONLY.
3. THIS DRAWING IS TO BE READ IN CONJUNCTION WITH ALL RELEVANT ARCHITECT'S, SERVICE ENGINEER'S AND YourSpreadsheets DRAWINGS .

ALL DRWAING ARE THE PROPOERTY OF THE DESIGNER & THEY ARE NOT TO BE REPRODUCED IN WHOLE OR IN PART WITHOUT WRITTEN CONSENT FROM THE DESIGN WING

CONTRACTOR TO CHECK &VERIFY ALL DIMENSIONS BEFORE COMMENCING WORK & TO REPORT ANY DISCREPANCIES TO THE DESIGN WING.

DO NOT SCALE DRAWINGS.

ALL CONSTRUCTION TO BE ACCORDING TO BEST COMMON PRACTICE.

REV:	DESCRIPTION:	BY:	DATE:
A	ARCHITECTURE DRAWING	----	25-12-25
B	STRUCTURE DRAWING	----	27-12-25

PROJECT NAME:
300 SQ.YARD HOUSE
ARCHITECTURE DRAWING

SIGNATURE BY:

DRAWING TITLE:
ARCHITECTURAL DRAWING

DRAWN BY: MUDASSIR
CHECKED BY: M.SHEHERYAR
APPROVED BY: M.SHEHERYAR
DATE: 27-DEC-2025

CLIENT
MR. ROHAN
KARACHI...

DESIGNED BY:-

E.D.C.O
ENGINEERING DESIGNING CONSTRUCTION OFFICIAL
ARCHITECT| PLANNERS| ENGINEERS| INTERIOR| B.O.Q| EXTERIOR| CONSULT| STRUCTURE DESIGN| PLANNING| LAND SURVEY| CONSTRUCTION| 3D ANIMATION VIDEO| RENOVATION|
MUHAMMAD SHEHERYAR
CONTACT- 0312-2118445|D.H.A PHASE VII

PROJECT NO: AR-7590
SCALE: 1/8"=1'-0"
SHEET SIZE: A3
DRAWING NO: ARC
SHEET NO ----------
REVISION: YES
UNIT: INCHES&FEET

STRUCTURE

DRAWING

GENERAL NOTES:

1. THE COPYRIGHT OF THIS DRAWING IS VESTED IN YourSpreadsheets AND IT MAY NOT BE REPRODUCED IN WHOLE OR PART OR USED FOR THE MANUFACTURE OF ANY ARTICLE WITHOUT THE EXPRESS PERMISSION OF THE COPYRIGHT HOLDERS.
2. WORK TO FIGURED DIMENSIONS ONLY.
3. THIS DRAWING IS TO BE READ IN CONJUNCTION WITH ALL RELEVANT ARCHITECT'S, SERVICE ENGINEER'S AND YourSpreadsheets DRAWINGS .

ALL DRWAING ARE THE PROPOERTY OF THE DESIGNER & THEY ARE NOT TO BE REPRODUCED IN WHOLE OR IN PART WITHOUT WRITTEN CONSENT FROM THE DESIGN WING
CONTRACTOR TO CHECK &VERIFY ALL DIMENSIONS BEFORE COMMENCING WORK & TO REPORT ANY DISCREPANCIES TO THE DESIGN WING.
DO NOT SCALE DRAWINGS.
ALL CONSTRUCTION TO BE ACCORDING TO BEST COMMON PRACTICE.

REV:	DESCRIPTION:	BY:	DATE:
A	ARCHITECTURE DRAWING	----	25-12-25
B	STRUCTURE DRAWING	----	27-12-25

PROJECT NAME:
300 SQ.YARD HOUSE ARCHITECTURE DRAWING

SIGNATURE BY:

DRAWING TITLE:
ARCHITECTURAL DRAWING

DRAWN BY: MUDASSIR

CHECKED BY: M.SHEHERYAR

APPROVED BY: M.SHEHERYAR

DATE: 27-DEC-2025

CLIENT
MR. ROHAN
KARACHI...

DESIGNED BY:-

E.D.C.O
ENGINEERING DESIGNING CONSTRUCTION OFFICIAL

ARCHITECT| PLANNERS| ENGINEERS| INTERIOR| B.O.Q| EXTERIOR| CONSULT| STRUCTURE DESIGN| PLANNING| LAND SURVEY| CONSTRUCTION| 3D ANIMATION VIDEO| RENOVATION|

MUHAMMAD SHEHERYAR
CONTACT- 0312-2118445|D.H.A PHASE VII

PROJECT NO: AR-7590

SCALE: 1/8"=1'-0"

SHEET SIZE: A3

DRAWING NO: ARC

SHEET NO ----------

REVISION: YES

UNIT: INCHES&FEET

S E W N

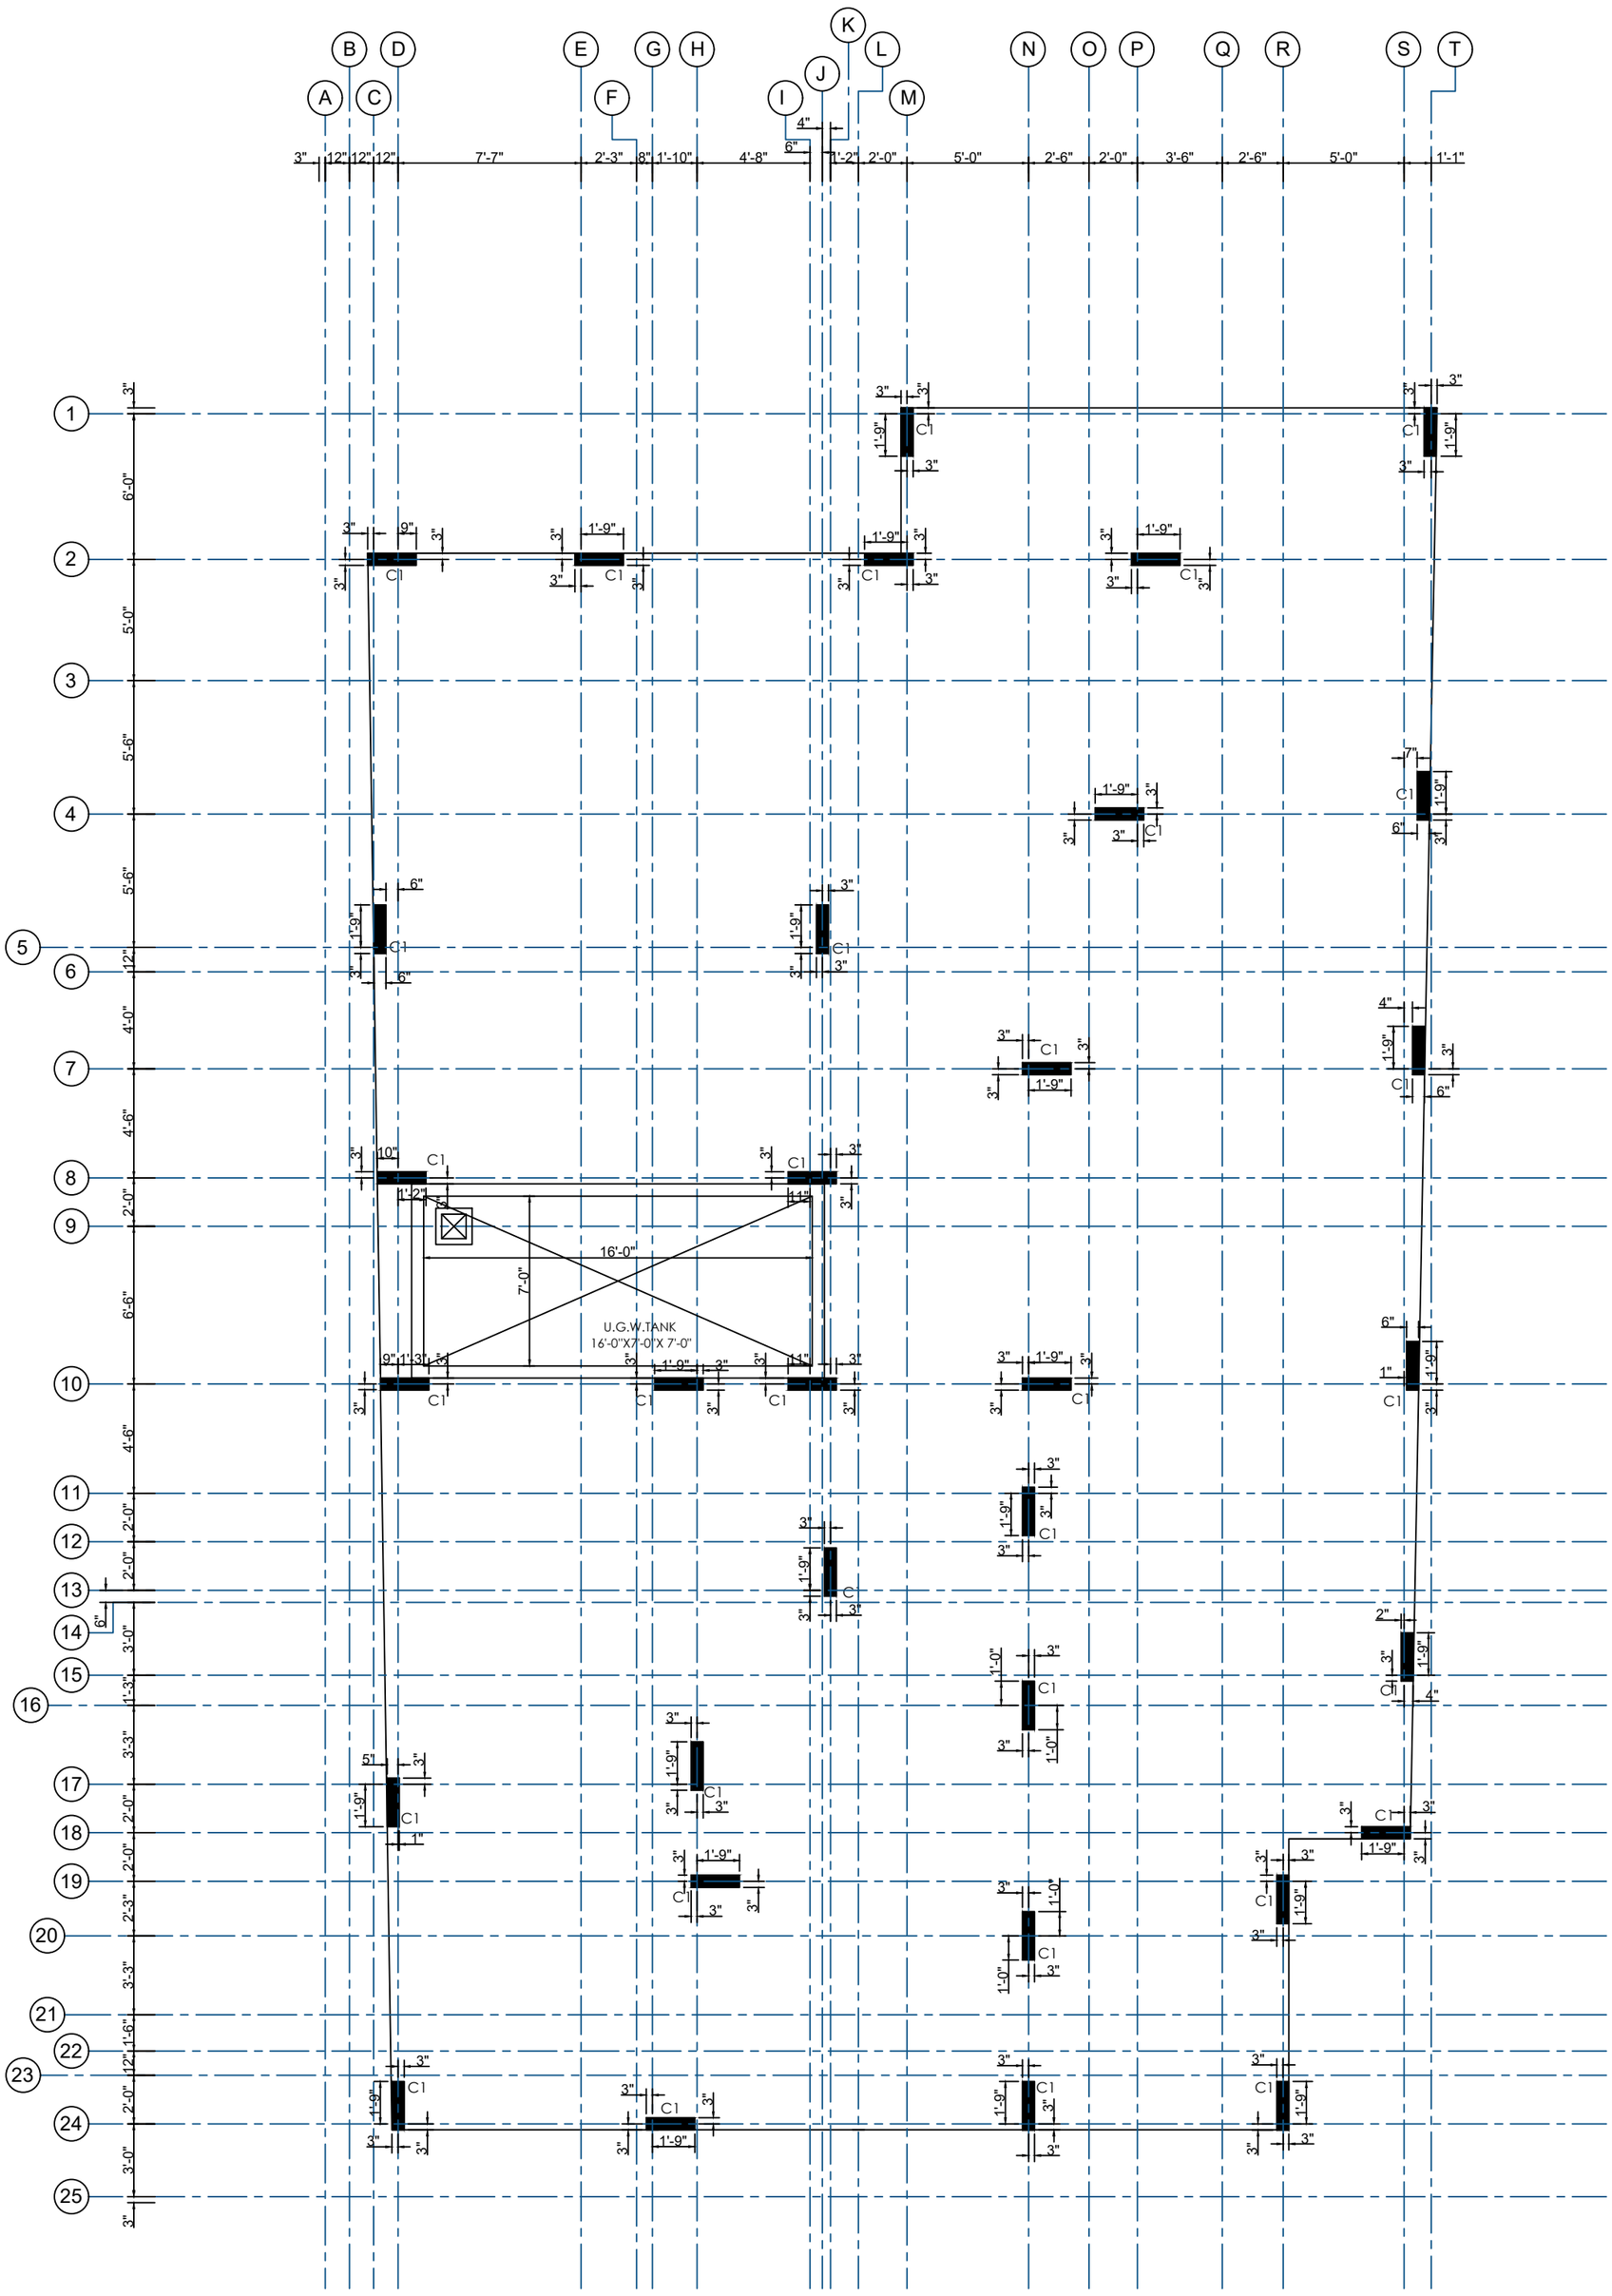

00 COLUMN LAYOUT PLAN

GENERAL NOTES:

1. THE COPYRIGHT OF THIS DRAWING IS VESTED IN YourSpreadsheets AND IT MAY NOT BE REPRODUCED IN WHOLE OR PART OR USED FOR THE MANUFACTURE OF ANY ARTICLE WITHOUT THE EXPRESS PERMISSION OF THE COPYRIGHT HOLDERS.
2. WORK TO FIGURED DIMENSIONS ONLY.
3. THIS DRAWING IS TO BE READ IN CONJUNCTION WITH ALL RELEVANT ARCHITECT'S, SERVICE ENGINEER'S AND YourSpreadsheets DRAWINGS .

ALL DRWAING ARE THE PROPOERTY OF THE DESIGNER & THEY ARE NOT TO BE REPRODUCED IN WHOLE OR IN PART WITHOUT WRITTEN CONSENT FROM THE DESIGN WING
CONTRACTOR TO CHECK &VERIFY ALL DIMENSIONS BEFORE COMMENCING WORK & TO REPORT ANY DISCREPANCIES TO THE DESIGN WING.
DO NOT SCALE DRAWINGS.
ALL CONSTRUCTION TO BE ACCORDING TO BEST COMMON PRACTICE.

REV:	DESCRIPTION:	BY:	DATE:
A	ARCHITECTURE DRAWING	----	25-12-25
B	STRUCTURE DRAWING	----	27-12-25

PROJECT NAME:
300 SQ.YARD HOUSE ARCHITECTURE DRAWING

SIGNATURE BY:

DRAWING TITLE:
ARCHITECTURAL DRAWING

DRAWN BY: MUDASSIR
CHECKED BY: M.SHEHERYAR
APPROVED BY: M.SHEHERYAR
DATE: 27-DEC-2025

CLIENT
MR. ROHAN
KARACHI...

DESIGNED BY:-

E.D.C.O
ENGINEERING DESIGNING CONSTRUCTION OFFICIAL
ARCHITECT| PLANNERS| ENGINEERS| INTERIOR| B.O.Q| EXTERIOR| CONSULT| STRUCTURE DESIGN| PLANNING| LAND SURVEY| CONSTRUCTION| 3D ANIMATION VIDEO| RENOVATION|
MUHAMMAD SHEHERYAR
CONTACT- 0312-2118445|D.H.A PHASE VII

PROJECT NO: AR-7590
SCALE: 1/8"=1'-0"
SHEET SIZE: A3
DRAWING NO: ARC
SHEET NO ----------
REVISION: YES
UNIT: INCHES&FEET

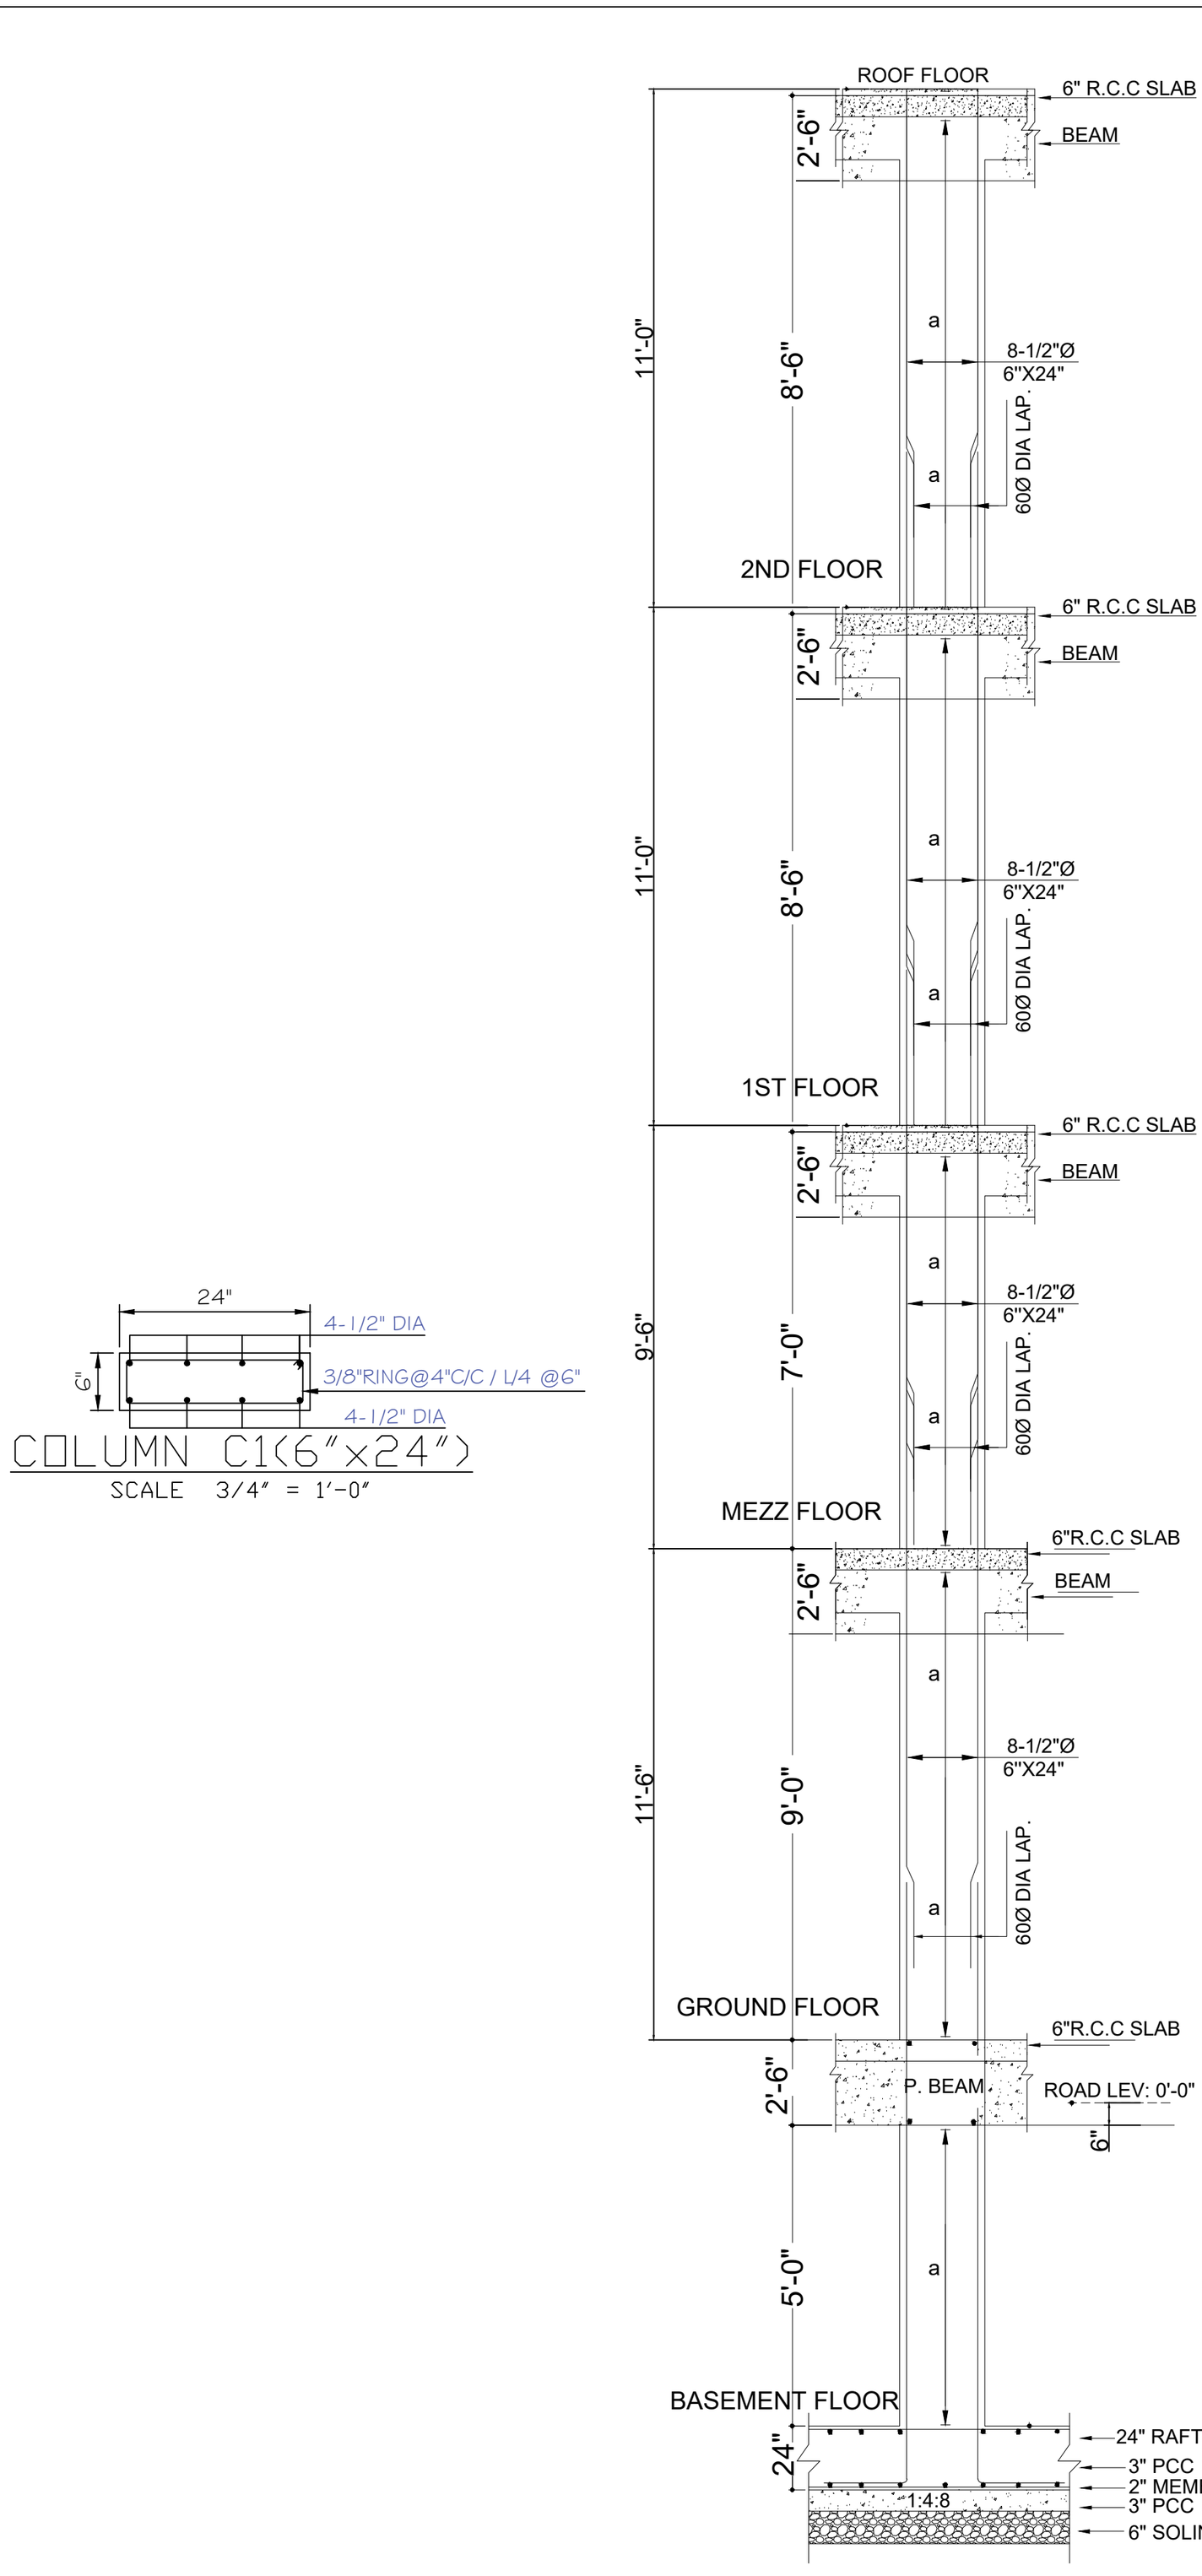

COLUMN C1(6"x24")

SCALE 3/4" = 1'-0"

COLUMN "C1"

TYP. SEC. OF COLUMNS

00 COLUMN DETAIL & SECTION PLAN

GENERAL NOTES:

1. THE COPYRIGHT OF THIS DRAWING IS VESTED IN YourSpreadsheets AND IT MAY NOT BE REPRODUCED IN WHOLE OR PART OR USED FOR THE MANUFACTURE OF ANY ARTICLE WITHOUT THE EXPRESS PERMISSION OF THE COPYRIGHT HOLDERS.
2. WORK TO FIGURED DIMENSIONS ONLY.
3. THIS DRAWING IS TO BE READ IN CONJUNCTION WITH ALL RELEVANT ARCHITECT'S, SERVICE ENGINEER'S AND YourSpreadsheets DRAWINGS .

ALL DRWAING ARE THE PROPOERTY OF THE DESIGNER & THEY ARE NOT TO BE REPRODUCED IN WHOLE OR IN PART WITHOUT WRITTEN CONSENT FROM THE DESIGN WING

CONTRACTOR TO CHECK &VERIFY ALL DIMENSIONS BEFORE COMMENCING WORK & TO REPORT ANY DISCREPANCIES TO THE DESIGN WING.

DO NOT SCALE DRAWINGS.

ALL CONSTRUCTION TO BE ACCORDING TO BEST COMMON PRACTICE.

REV:	DESCRIPTION:	BY:	DATE:
A	ARCHITECTURE DRAWING	----	25-12-25
B	STRUCTURE DRAWING	----	27-12-25

PROJECT NAME:
300 SQ.YARD HOUSE ARCHITECTURE DRAWING

SIGNATURE BY:

DRAWING TITLE:
ARCHITECTURAL DRAWING

DRAWN BY: MUDASSIR

CHECKED BY: M.SHEHERYAR

APPROVED BY: M.SHEHERYAR

DATE: 27-DEC-2025

CLIENT
MR. ROHAN
KARACHI...

DESIGNED BY:-

E.D.C.O
ENGINEERING DESIGNING CONSTRUCTION OFFICIAL
ARCHITECT| PLANNERS| ENGINEERS| INTERIOR| B.O.Q| EXTERIOR| CONSULT| STRUCTURE DESIGN| PLANNING| LAND SURVEY| CONSTRUCTION| 3D ANIMATION VIDEO| RENOVATION|
MUHAMMAD SHEHERYAR
CONTACT- 0312-2118445|D.H.A PHASE VII

PROJECT NO: AR-7590

SCALE: 1/8"=1'-0"

SHEET SIZE: A3

DRAWING NO: ARC

SHEET NO ----------

REVISION: YES

UNIT: INCHES&FEET

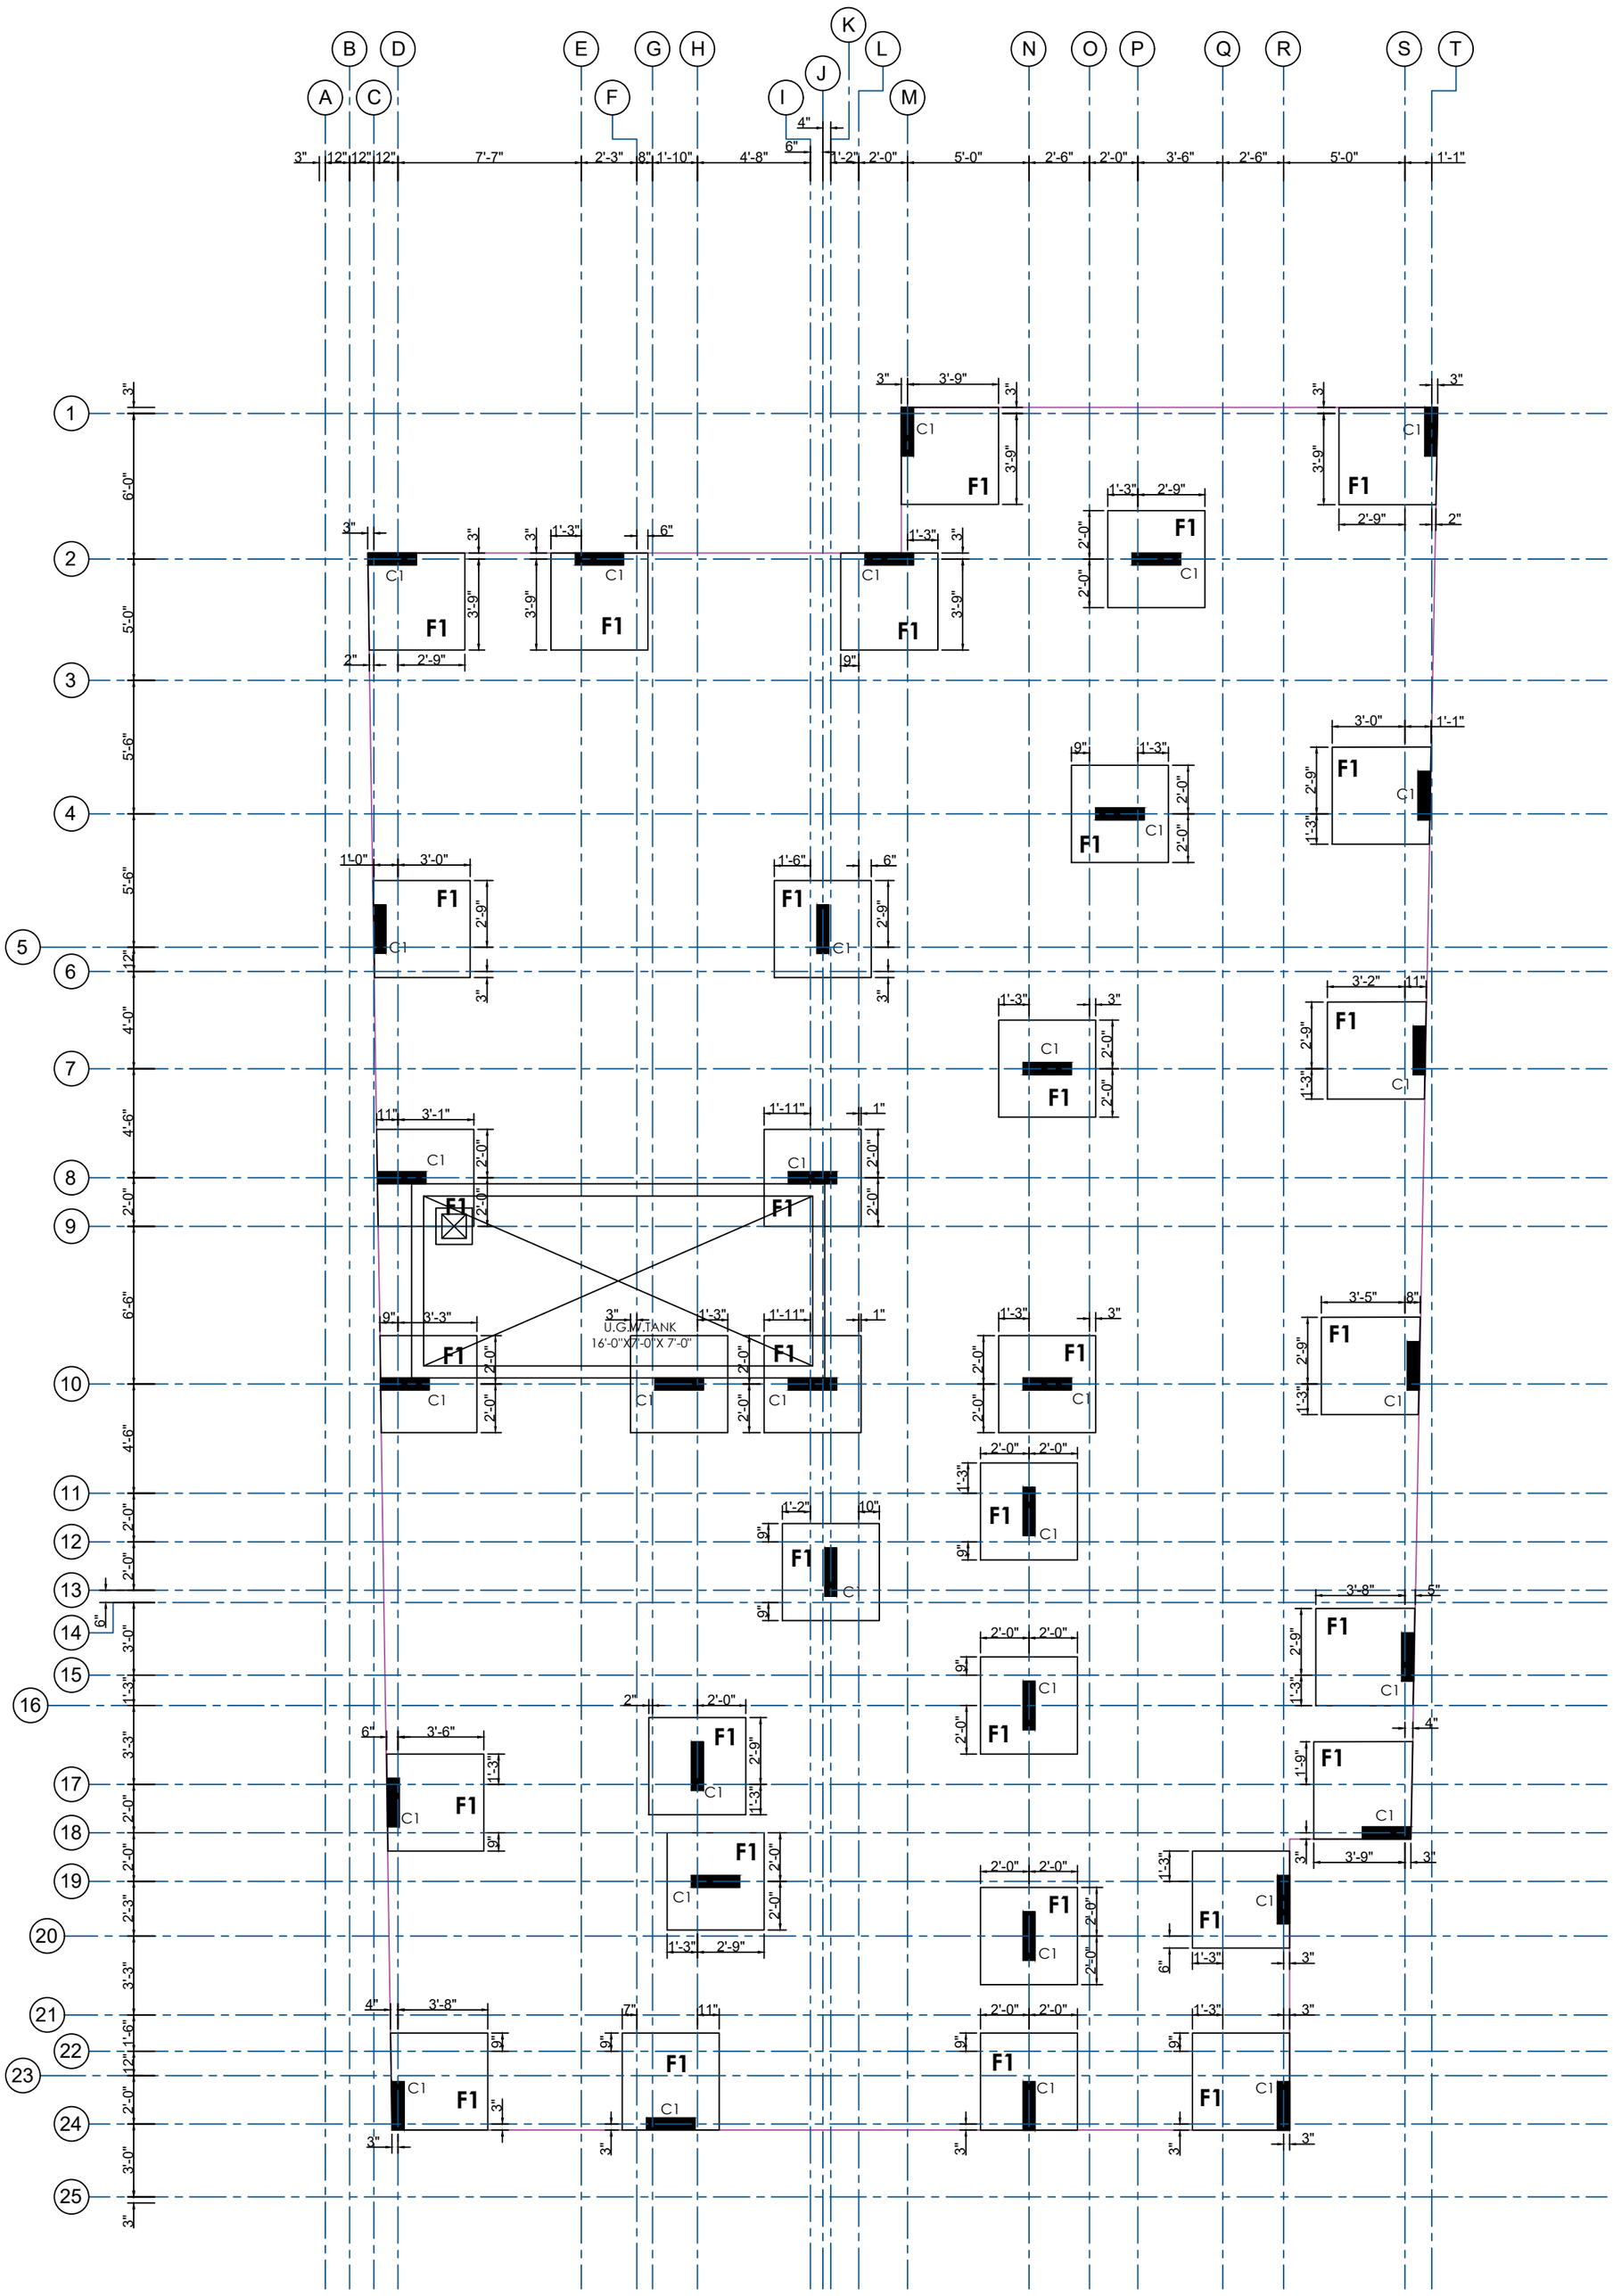

00 FOOTING LAYOUT PLAN

GENERAL NOTES:

1. THE COPYRIGHT OF THIS DRAWING IS VESTED IN YourSpreadsheets AND IT MAY NOT BE REPRODUCED IN WHOLE OR PART OR USED FOR THE MANUFACTURE OF ANY ARTICLE WITHOUT THE EXPRESS PERMISSION OF THE COPYRIGHT HOLDERS.
2. WORK TO FIGURED DIMENSIONS ONLY.
3. THIS DRAWING IS TO BE READ IN CONJUNCTION WITH ALL RELEVANT ARCHITECT'S, SERVICE ENGINEER'S AND YourSpreadsheets DRAWINGS .

ALL DRWAING ARE THE PROPOERTY OF THE DESIGNER & THEY ARE NOT TO BE REPRODUCED IN WHOLE OR IN PART WITHOUT WRITTEN CONSENT FROM THE DESIGN WING
CONTRACTOR TO CHECK &VERIFY ALL DIMENSIONS BEFORE COMMENCING WORK & TO REPORT ANY DISCREPANCIES TO THE DESIGN WING.
DO NOT SCALE DRAWINGS.
ALL CONSTRUCTION TO BE ACCORDING TO BEST COMMON PRACTICE.

REV:	DESCRIPTION:	BY:	DATE:
A	ARCHITECTURE DRAWING	----	25-12-25
B	STRUCTURE DRAWING	----	27-12-25

PROJECT NAME:
300 SQ.YARD HOUSE ARCHITECTURE DRAWING

SIGNATURE BY:

DRAWING TITLE:
ARCHITECTURAL DRAWING

DRAWN BY: MUDASSIR
CHECKED BY: M.SHEHERYAR
APPROVED BY: M.SHEHERYAR
DATE: 27-DEC-2025

CLIENT
MR. ROHAN
KARACHI...

DESIGNED BY:-

E.D.C.O
ENGINEERING DESIGNING CONSTRUCTION OFFICIAL
ARCHITECT| PLANNERS| ENGINEERS| INTERIOR| B.O.Q| EXTERIOR| CONSULT| STRUCTURE DESIGN| PLANNING| LAND SURVEY| CONSTRUCTION| 3D ANIMATION VIDEO| RENOVATION|
MUHAMMAD SHEHERYAR
CONTACT- 0312-2118445|D.H.A PHASE VII

PROJECT NO: AR-7590
SCALE: 1/8"=1'-0"
SHEET SIZE: A3
DRAWING NO: ARC
SHEET NO ----------
REVISION: YES
UNIT: INCHES&FEET

SCHEDULE OF R.C.C. FOOTING

FOOTINGS MARK	EXCAVATION	R.C.C.BASE 1:2:4 (LxB)	DEPTH T	REINFORCEMENT		DOUBLE JAAL STEEL	DEPTH C
				LONG STEEL	SHORT STEEL		
F1	4'-0"x4'-0"	4'-0"x4'-0"	24"	1/2"Ø@6"c/c	1/2"Ø@6"c/c		5'-0"

SCHEDULE OF R.C.C COLUMN

MARK	SIZE	MAIN BARS	BINDERS
C1	6" x 24"	8 # 4	3/8" ø 6" c/c
CB2	24" x 6"	8 # 4	3/8" ø 6" c/c

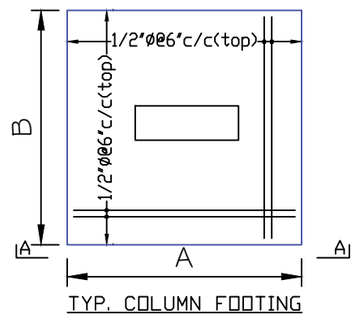

TYP. COLUMN FOOTING

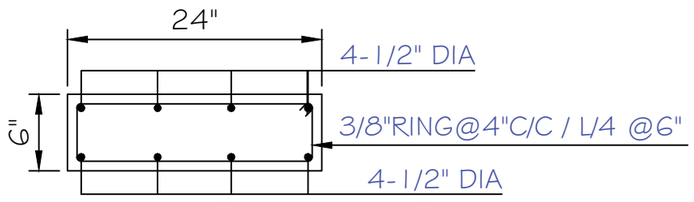

COLUMN C1(6"x24")

SCALE 3/4" = 1'-0"

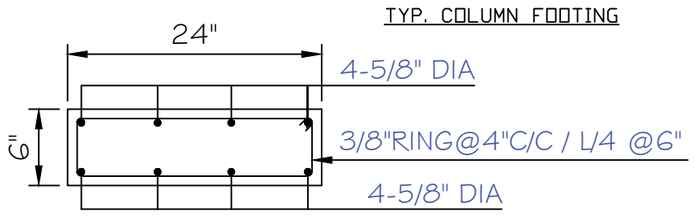

CB2(6"x24")

SCALE 3/4" = 1'-0"

SCHEDULE OF R.C.C SLAB

MARK	DEPTH	S / W STEEL	L / W STEEL	EXTRA TOP	DOUBLE JAAL STEEL
S-1	6"	3/8" ø 6" c/c	1/2" ø 6" c/c	----------	

NOTES:-

1- 4000 PSI FOR RAFT / FOUNDATION.
2- 4000 PSI FOR COLUMN/ BEAM/ SLAB.
3- ALL LEVELS TO BE CO-ORDINATED WITH ARCH. DRAWING.
4- READY MIX CONCRETE TO BE USED.
5- RAFT /FOUNDATION THICKNESS ALSO SHOULD BE DEPEND ON SOIL CONDITION DURING EXCAVATION.

00 R.C.C PLAN

GENERAL NOTES:

1. THE COPYRIGHT OF THIS DRAWING IS VESTED IN YourSpreadsheets AND IT MAY NOT BE REPRODUCED IN WHOLE OR PART OR USED FOR THE MANUFACTURE OF ANY ARTICLE WITHOUT THE EXPRESS PERMISSION OF THE COPYRIGHT HOLDERS.
2. WORK TO FIGURED DIMENSIONS ONLY.
3. THIS DRAWING IS TO BE READ IN CONJUNCTION WITH ALL RELEVANT ARCHITECT'S, SERVICE ENGINEER'S AND YourSpreadsheets DRAWINGS .
ALL DRWAING ARE THE PROPOERTY OF THE DESIGNER & THEY ARE NOT TO BE REPRODUCED IN WHOLE OR IN PART WITHOUT WRITTEN CONSENT FROM THE DESIGN WING
CONTRACTOR TO CHECK &VERIFY ALL DIMENSIONS BEFORE COMMENCING WORK & TO REPORT ANY DISCREPANCIES TO THE DESIGN WING.
DO NOT SCALE DRAWINGS.
ALL CONSTRUCTION TO BE ACCORDING TO BEST COMMON PRACTICE.

REV:	DESCRIPTION:	BY:	DATE:
A	ARCHITECTURE DRAWING	----	25-12-25
B	STRUCTURE DRAWING	----	27-12-25

PROJECT NAME:
300 SQ.YARD HOUSE ARCHITECTURE DRAWING

SIGNATURE BY:

DRAWING TITLE:
ARCHITECTURAL DRAWING

DRAWN BY: MUDASSIR
CHECKED BY: M.SHEHERYAR
APPROVED BY: M.SHEHERYAR
DATE: 27-DEC-2025

CLIENT
MR. ROHAN
KARACHI...

DESIGNED BY:-

E.D.C.O
ENGINEERING DESIGNING CONSTRUCTION OFFICIAL
ARCHITECT| PLANNERS| ENGINEERS| INTERIOR| B.O.Q| EXTERIOR| CONSULT| STRUCTURE DESIGN| PLANNING| LAND SURVEY| CONSTRUCTION| 3D ANIMATION VIDEO| RENOVATION|
MUHAMMAD SHEHERYAR
CONTACT- 0312-2118445|D.H.A PHASE VII

PROJECT NO: AR-7590
SCALE: 1/8"=1'-0"
SHEET SIZE: A3
DRAWING NO: ARC
SHEET NO ----------
REVISION: YES
UNIT: INCHES&FEET

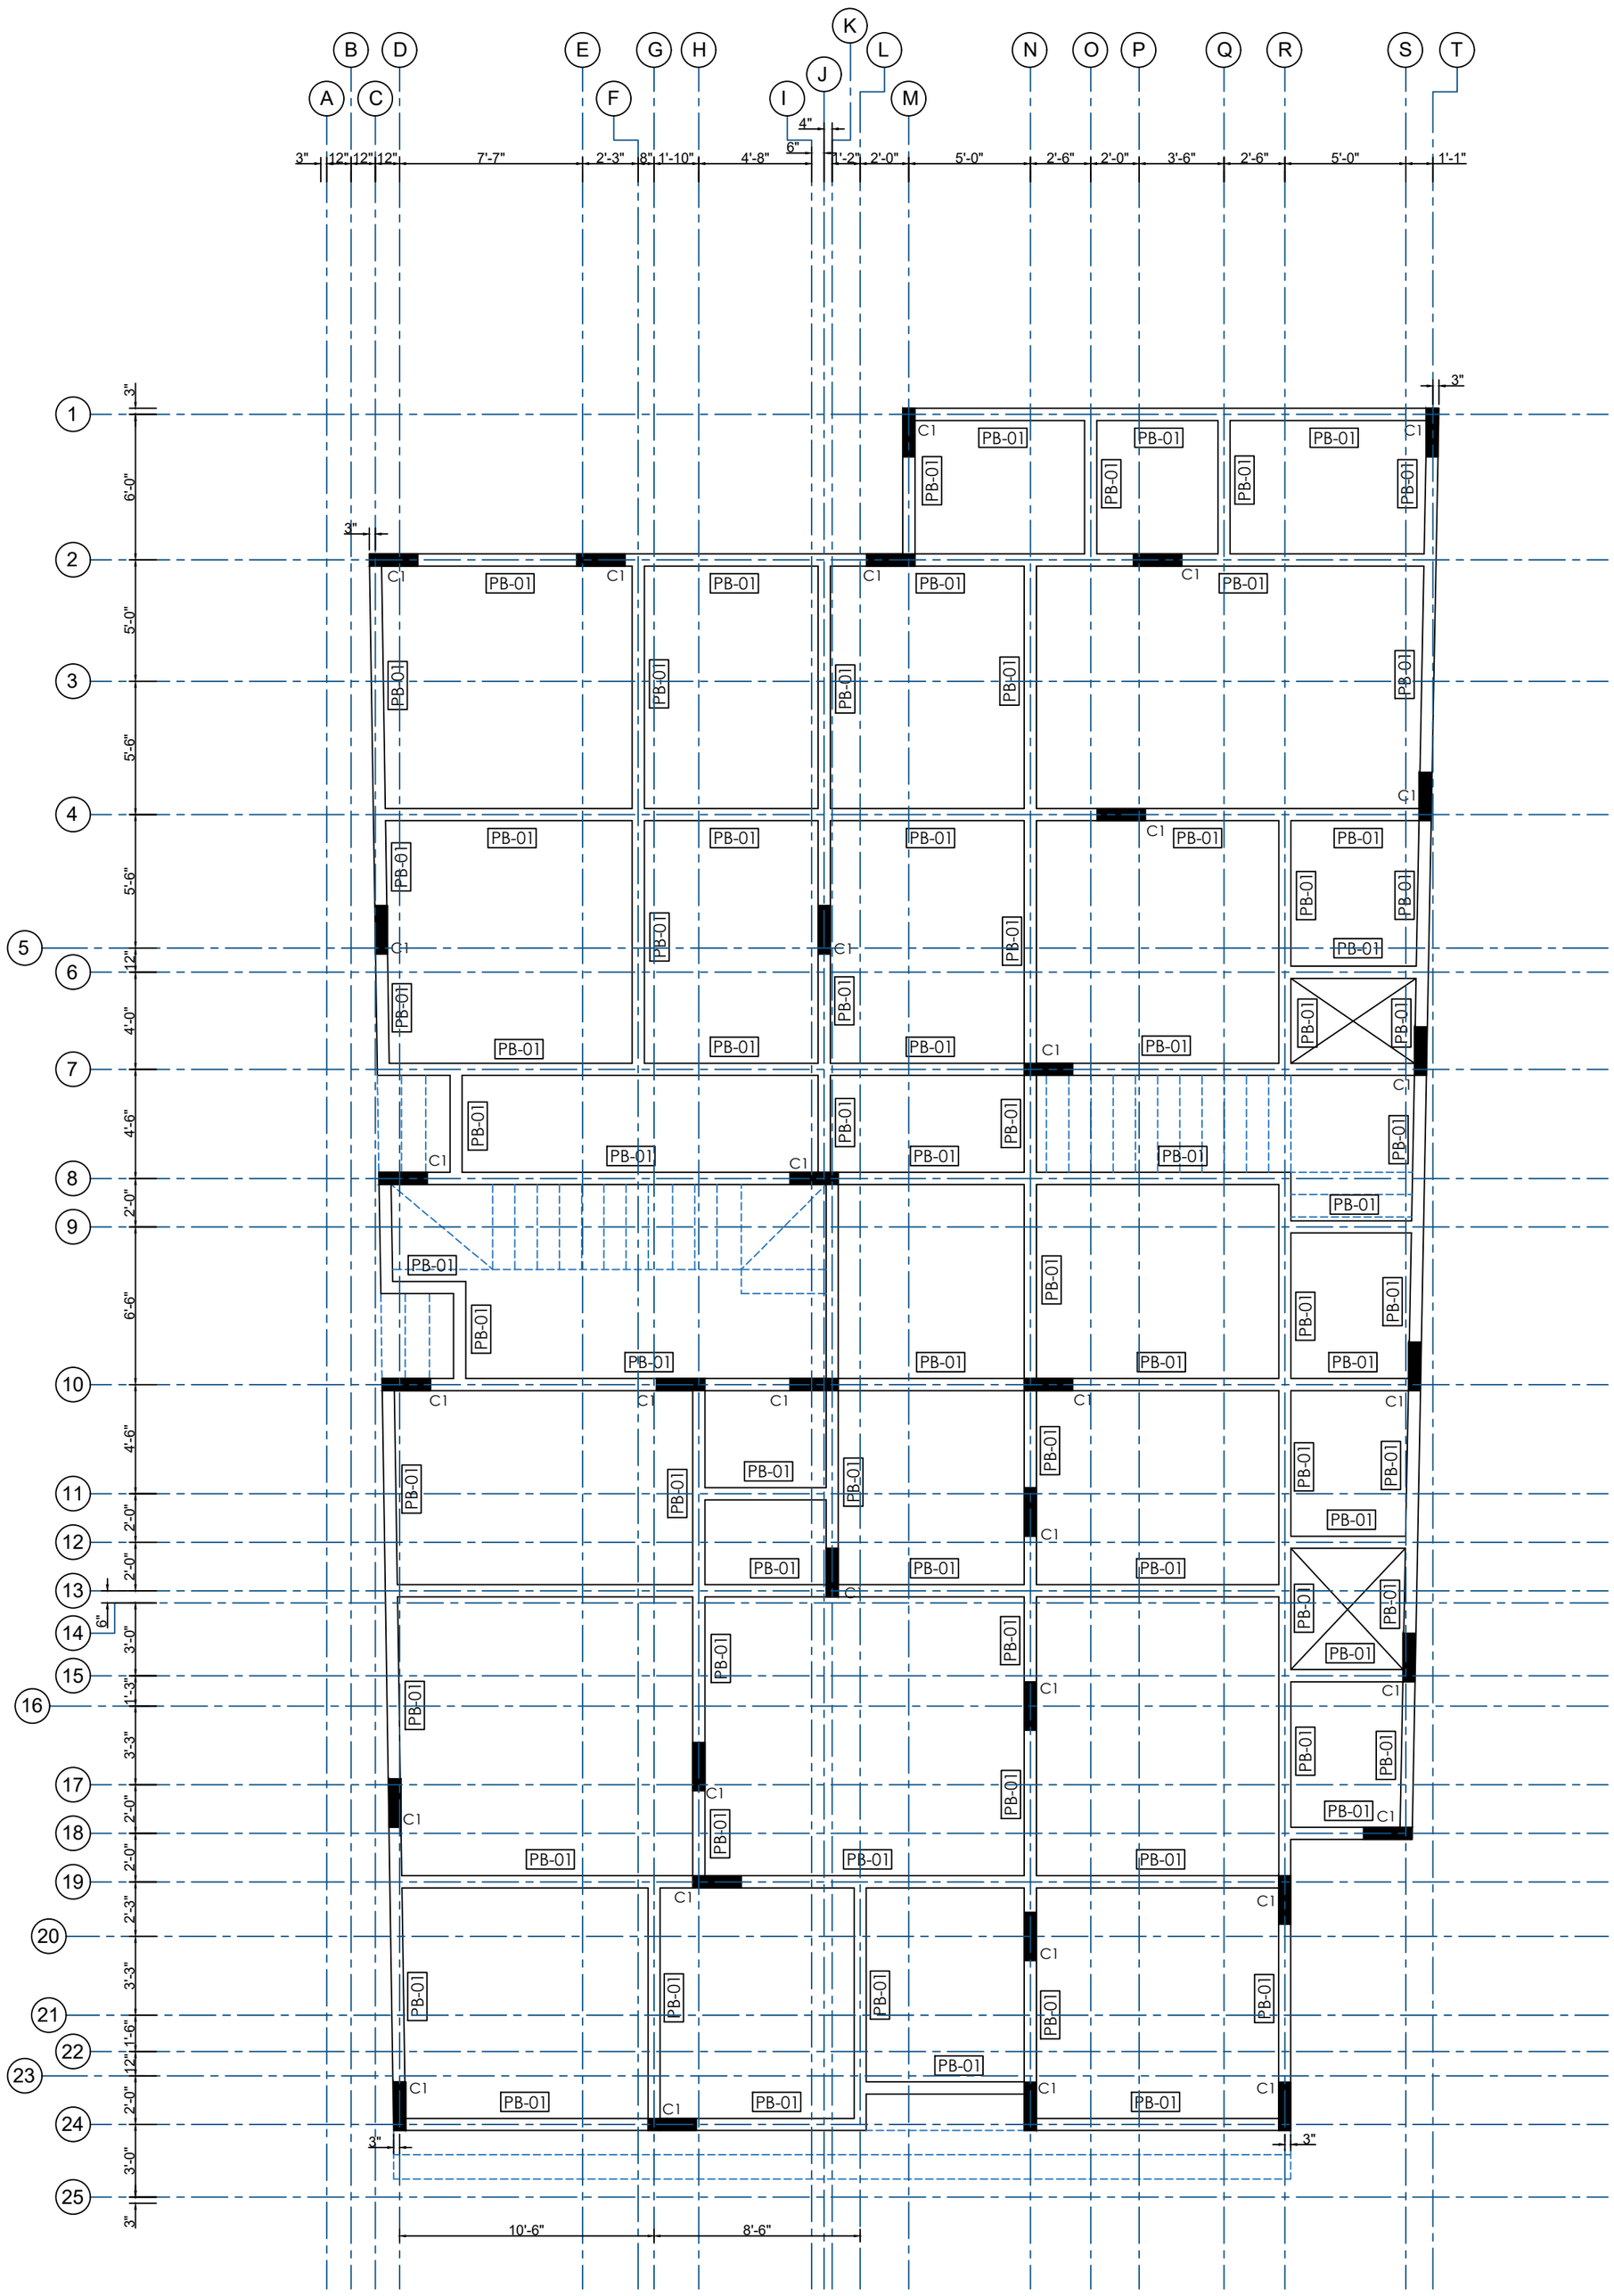

00 PLINTH BEAM LAYOUT PLAN

GENERAL NOTES:

1. THE COPYRIGHT OF THIS DRAWING IS VESTED IN YourSpreadsheets AND IT MAY NOT BE REPRODUCED IN WHOLE OR PART OR USED FOR THE MANUFACTURE OF ANY ARTICLE WITHOUT THE EXPRESS PERMISSION OF THE COPYRIGHT HOLDERS.
2. WORK TO FIGURED DIMENSIONS ONLY.
3. THIS DRAWING IS TO BE READ IN CONJUNCTION WITH ALL RELEVANT ARCHITECT'S, SERVICE ENGINEER'S AND YourSpreadsheets DRAWINGS .

ALL DRWAING ARE THE PROPOERTY OF THE DESIGNER & THEY ARE NOT TO BE REPRODUCED IN WHOLE OR IN PART WITHOUT WRITTEN CONSENT FROM THE DESIGN WING
CONTRACTOR TO CHECK &VERIFY ALL DIMENSIONS BEFORE COMMENCING WORK & TO REPORT ANY DISCREPANCIES TO THE DESIGN WING.
DO NOT SCALE DRAWINGS.
ALL CONSTRUCTION TO BE ACCORDING TO BEST COMMON PRACTICE.

REV:	DESCRIPTION:	BY:	DATE:
A	ARCHITECTURE DRAWING	----	25-12-25
B	STRUCTURE DRAWING	----	27-12-25

PROJECT NAME:
300 SQ.YARD HOUSE ARCHITECTURE DRAWING

SIGNATURE BY:

DRAWING TITLE:
ARCHITECTURAL DRAWING

DRAWN BY: MUDASSIR
CHECKED BY: M.SHEHERYAR
APPROVED BY: M.SHEHERYAR
DATE: 27-DEC-2025

CLIENT
MR. ROHAN
KARACHI...

DESIGNED BY:-

E.D.C.O
ENGINEERING DESIGNING CONSTRUCTION OFFICIAL
ARCHITECT| PLANNERS| ENGINEERS| INTERIOR| B.O.Q| EXTERIOR| CONSULT| STRUCTURE DESIGN| PLANNING| LAND SURVEY| CONSTRUCTION| 3D ANIMATION VIDEO| RENOVATION|
MUHAMMAD SHEHERYAR
CONTACT- 0312-2118445|D.H.A PHASE VII

PROJECT NO: AR-7590
SCALE: 1/8"=1'-0"
SHEET SIZE: A3
DRAWING NO: ARC
SHEET NO ----------
REVISION: YES
UNIT: INCHES&FEET

S E W N

SCHEDULE OF PLINTH BEAMS

MARK	SIZE		BOTTOM BARS		TOP BARS	RINGS		EXTRA STEEL AT CONT. SUPP.
	W	D	FULL	CURTAIL		AT END. SUPPORT	AT MID SPAN	
PB-01	7"	30"	4-1/2"Ø	-	4-1/2"Ø	3/8"Ø@4"C/C	3/8"Ø@6"C/C	2-1/2"Ø PB1 / PB1

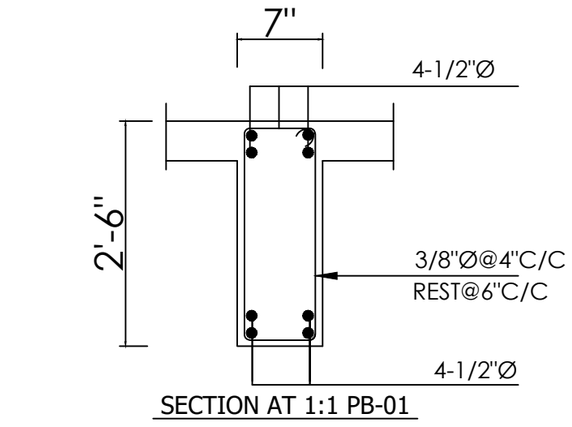

SECTION AT 1:1 PB-01

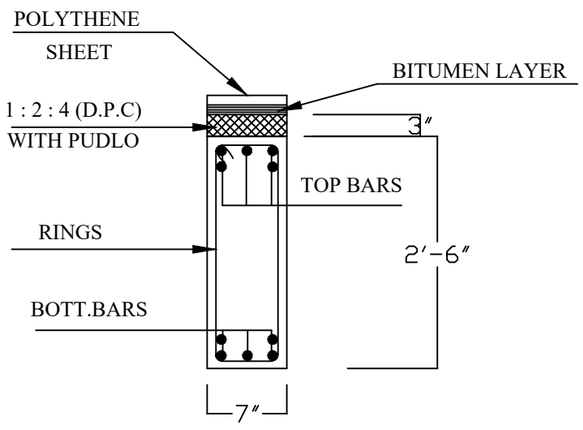

SEC. OF INT. PL. BEAMS
(PB-01)

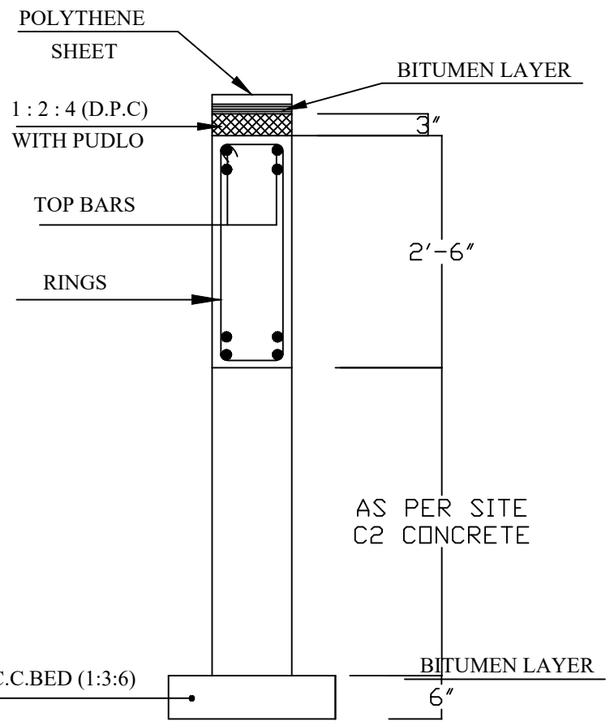

SEC. OF EXT. PL. BEAMS
(PB-01)

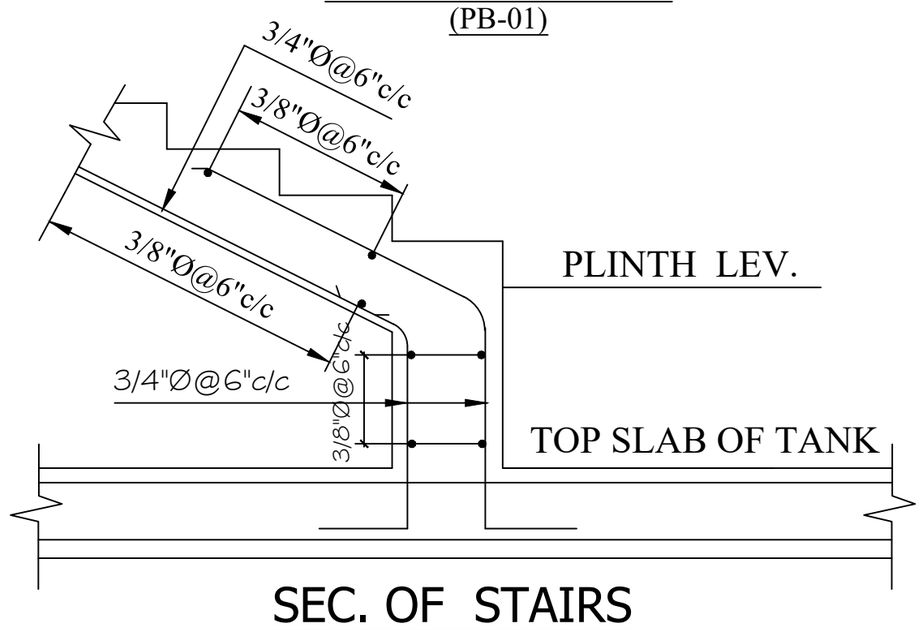

SEC. OF STAIRS

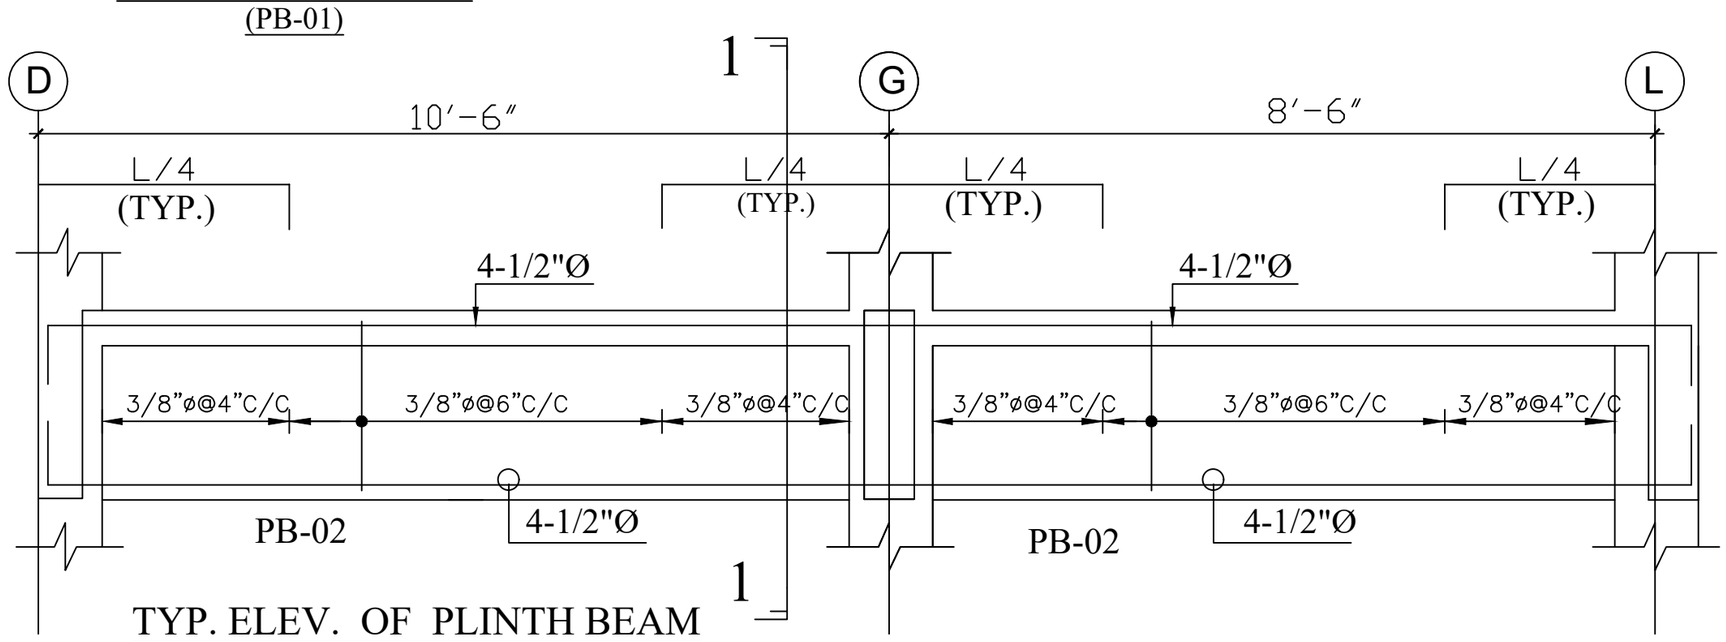

TYP. ELEV. OF PLINTH BEAM
(ON GRID ' 24 ' SIZE = 7" X 30")

00 INTERNAL & EXTERNAL PLINTH BEAM DETAIL

GENERAL NOTES:

1. THE COPYRIGHT OF THIS DRAWING IS VESTED IN YourSpreadsheets AND IT MAY NOT BE REPRODUCED IN WHOLE OR PART OR USED FOR THE MANUFACTURE OF ANY ARTICLE WITHOUT THE EXPRESS PERMISSION OF THE COPYRIGHT HOLDERS.
2. WORK TO FIGURED DIMENSIONS ONLY.
3. THIS DRAWING IS TO BE READ IN CONJUNCTION WITH ALL RELEVANT ARCHITECT'S, SERVICE ENGINEER'S AND YourSpreadsheets DRAWINGS .

ALL DRWAING ARE THE PROPOERTY OF THE DESIGNER & THEY ARE NOT TO BE REPRODUCED IN WHOLE OR IN PART WITHOUT WRITTEN CONSENT FROM THE DESIGN WING
CONTRACTOR TO CHECK &VERIFY ALL DIMENSIONS BEFORE COMMENCING WORK & TO REPORT ANY DISCREPANCIES TO THE DESIGN WING.
DO NOT SCALE DRAWINGS.
ALL CONSTRUCTION TO BE ACCORDING TO BEST COMMON PRACTICE.

REV:	DESCRIPTION:	BY:	DATE:
A	ARCHITECTURE DRAWING	----	25-12-25
B	STRUCTURE DRAWING	----	27-12-25

PROJECT NAME:
300 SQ.YARD HOUSE
ARCHITECTURE DRAWING

SIGNATURE BY:

DRAWING TITLE:
ARCHITECTURAL DRAWING

DRAWN BY: MUDASSIR
CHECKED BY: M.SHEHERYAR
APPROVED BY: M.SHEHERYAR
DATE: 27-DEC-2025

CLIENT
MR. ROHAN
KARACHI...

DESIGNED BY:-
E.D.C.O
ENGINEERING DESIGNING CONSTRUCTION OFFICIAL
ARCHITECT| PLANNERS| ENGINEERS| INTERIOR| B.O.Q| EXTERIOR| CONSULT| STRUCTURE DESIGN| PLANNING| LAND SURVEY| CONSTRUCTION| 3D ANIMATION VIDEO| RENOVATION|
MUHAMMAD SHEHERYAR
CONTACT- 0312-2118445|D.H.A PHASE VII

PROJECT NO: AR-7590
SCALE: 1/8"=1'-0"
SHEET SIZE: A3
DRAWING NO: ARC
SHEET NO ----------
REVISION: YES
UNIT: INCHES&FEET

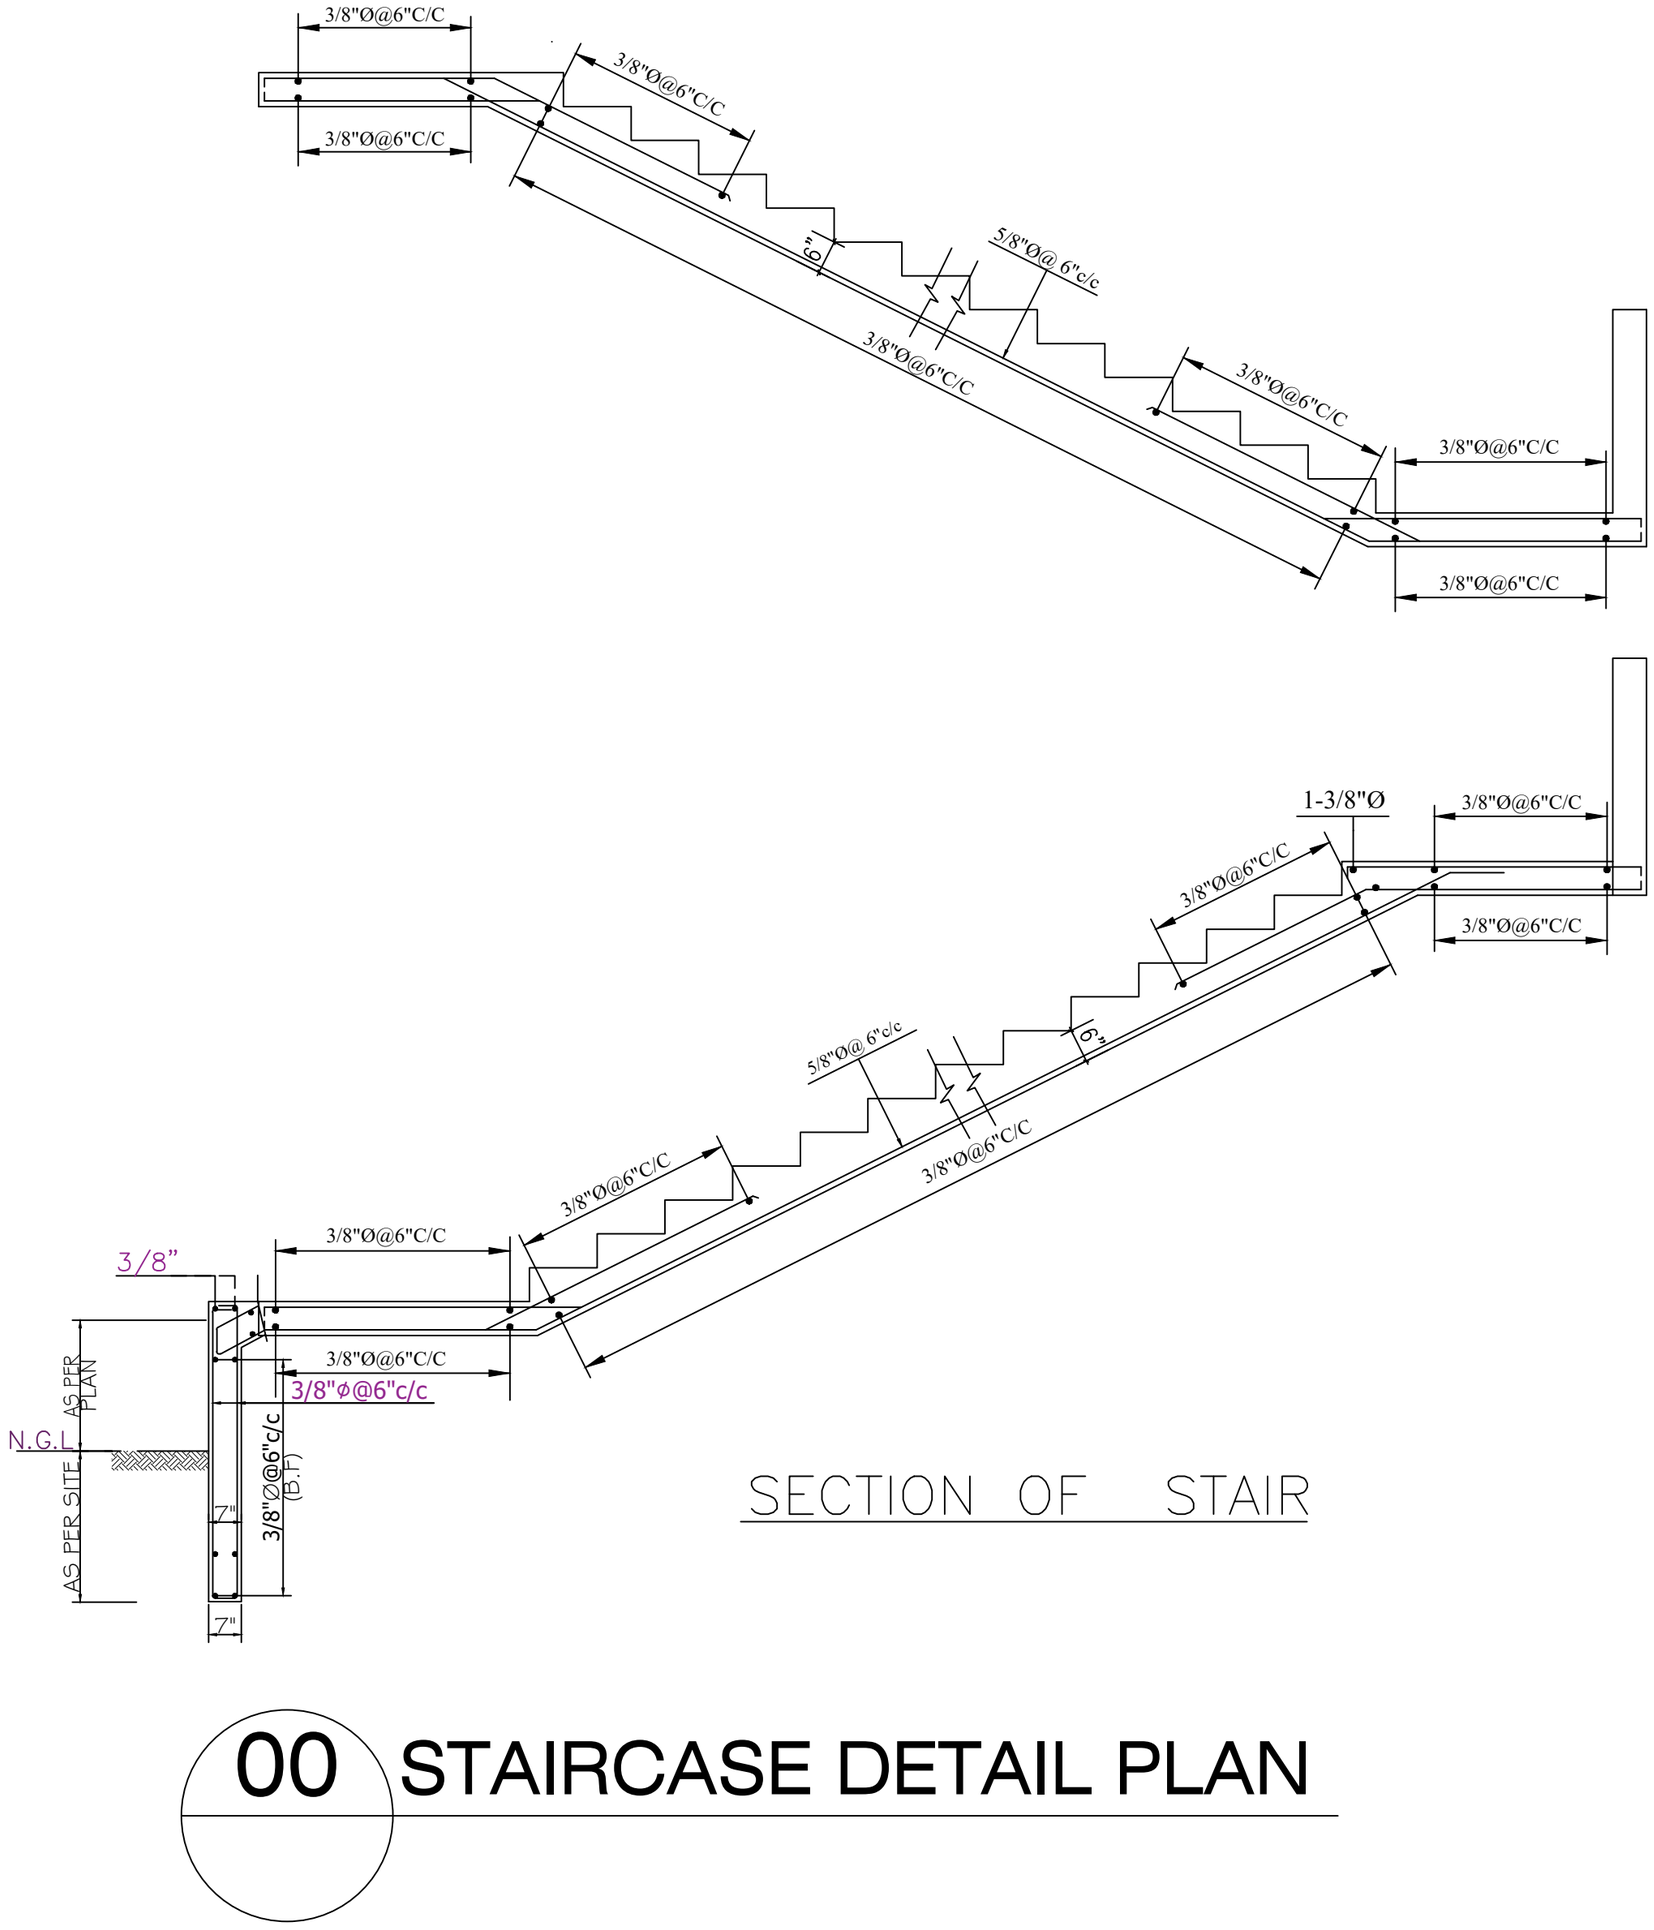

SECTION OF STAIR

00 STAIRCASE DETAIL PLAN

GENERAL NOTES:

1. THE COPYRIGHT OF THIS DRAWING IS VESTED IN YourSpreadsheets AND IT MAY NOT BE REPRODUCED IN WHOLE OR PART OR USED FOR THE MANUFACTURE OF ANY ARTICLE WITHOUT THE EXPRESS PERMISSION OF THE COPYRIGHT HOLDERS.
2. WORK TO FIGURED DIMENSIONS ONLY.
3. THIS DRAWING IS TO BE READ IN CONJUNCTION WITH ALL RELEVANT ARCHITECT'S, SERVICE ENGINEER'S AND YourSpreadsheets DRAWINGS .

ALL DRWAING ARE THE PROPOERTY OF THE DESIGNER & THEY ARE NOT TO BE REPRODUCED IN WHOLE OR IN PART WITHOUT WRITTEN CONSENT FROM THE DESIGN WING
CONTRACTOR TO CHECK &VERIFY ALL DIMENSIONS BEFORE COMMENCING WORK & TO REPORT ANY DISCREPANCIES TO THE DESIGN WING.
DO NOT SCALE DRAWINGS.
ALL CONSTRUCTION TO BE ACCORDING TO BEST COMMON PRACTICE.

REV:	DESCRIPTION:	BY:	DATE:
A	ARCHITECTURE DRAWING	----	25-12-25
B	STRUCTURE DRAWING	----	27-12-25

PROJECT NAME:
300 SQ.YARD HOUSE ARCHITECTURE DRAWING

SIGNATURE BY:

DRAWING TITLE:
ARCHITECTURAL DRAWING

DRAWN BY: MUDASSIR
CHECKED BY: M.SHEHERYAR
APPROVED BY: M.SHEHERYAR
DATE: 27-DEC-2025

CLIENT
MR. ROHAN
KARACHI...

DESIGNED BY:-

E.D.C.O
ENGINEERING DESIGNING CONSTRUCTION OFFICIAL

ARCHITECT| PLANNERS| ENGINEERS| INTERIOR| B.O.Q| EXTERIOR| CONSULT| STRUCTURE DESIGN| PLANNING| LAND SURVEY| CONSTRUCTION| 3D ANIMATION VIDEO| RENOVATION|
MUHAMMAD SHEHERYAR
CONTACT- 0312-2118445|D.H.A PHASE VII

PROJECT NO: AR-7590
SCALE: 1/8"=1'-0"
SHEET SIZE: A3
DRAWING NO: ARC
SHEET NO ----------
REVISION: YES
UNIT: INCHES&FEET

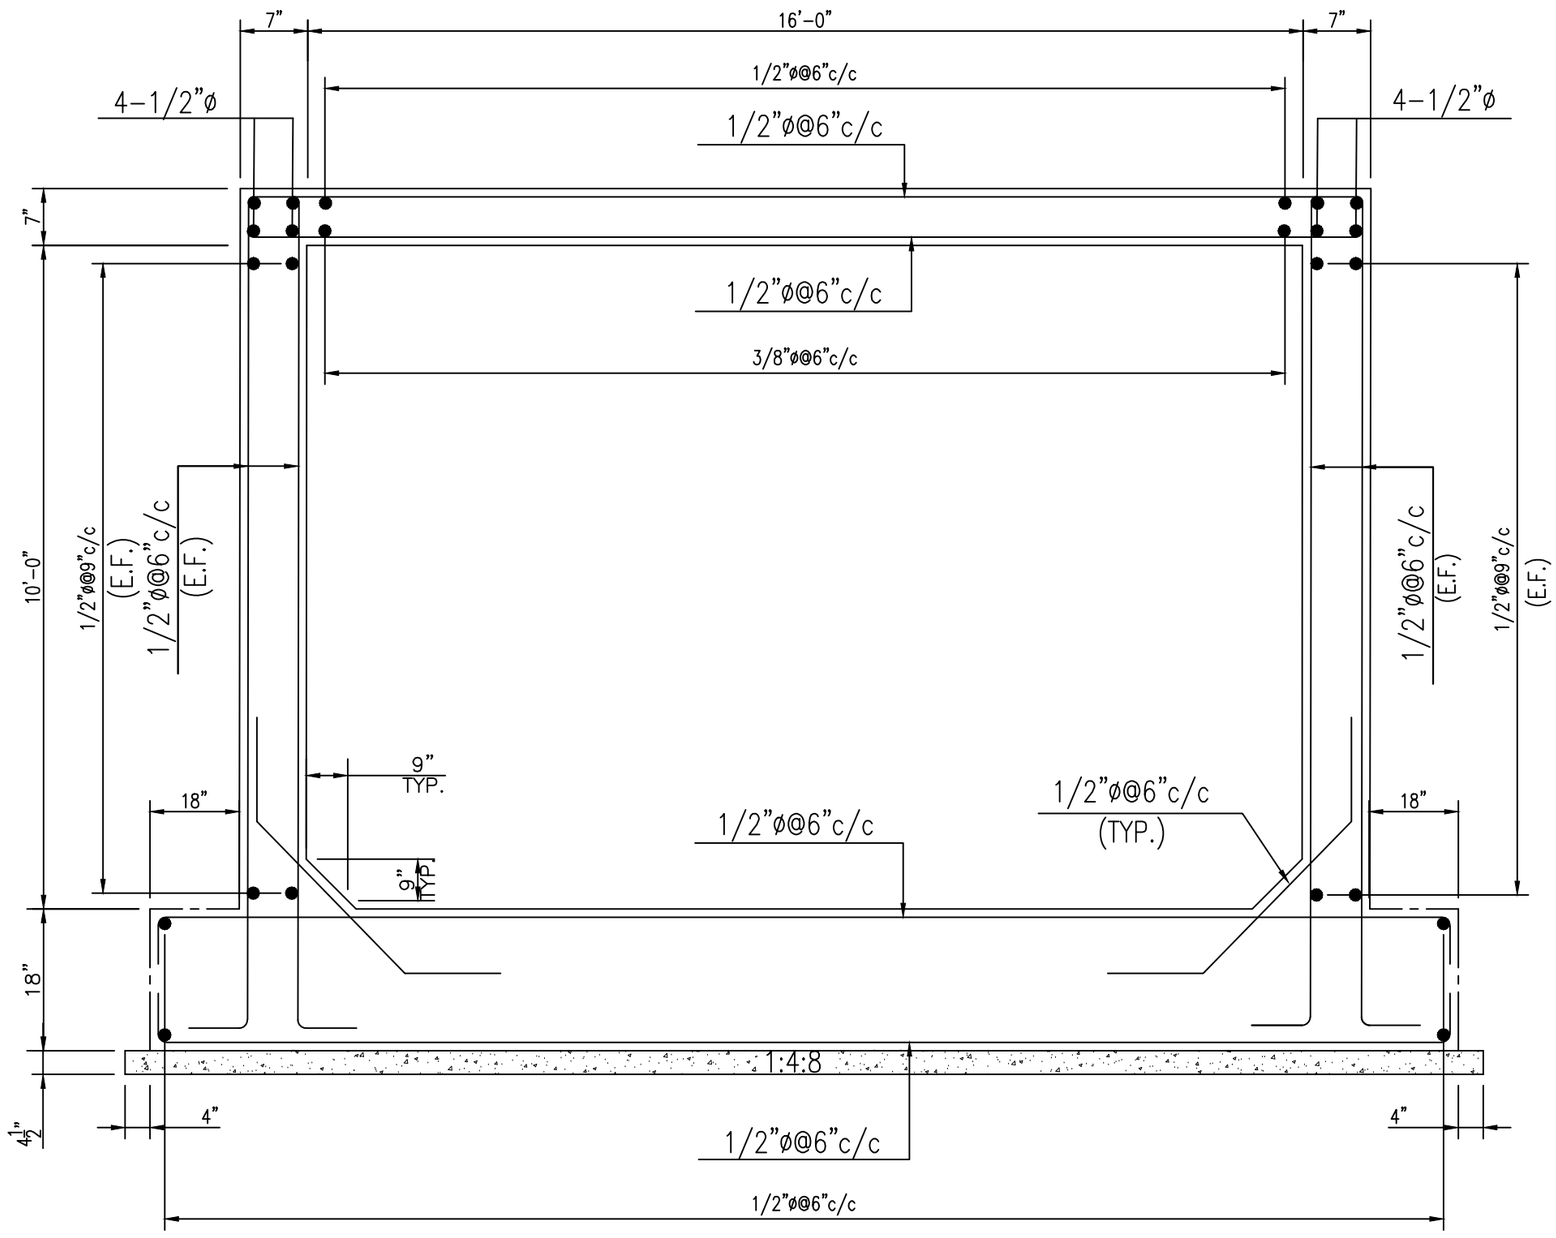

SECTION OF U.G.W.TANK

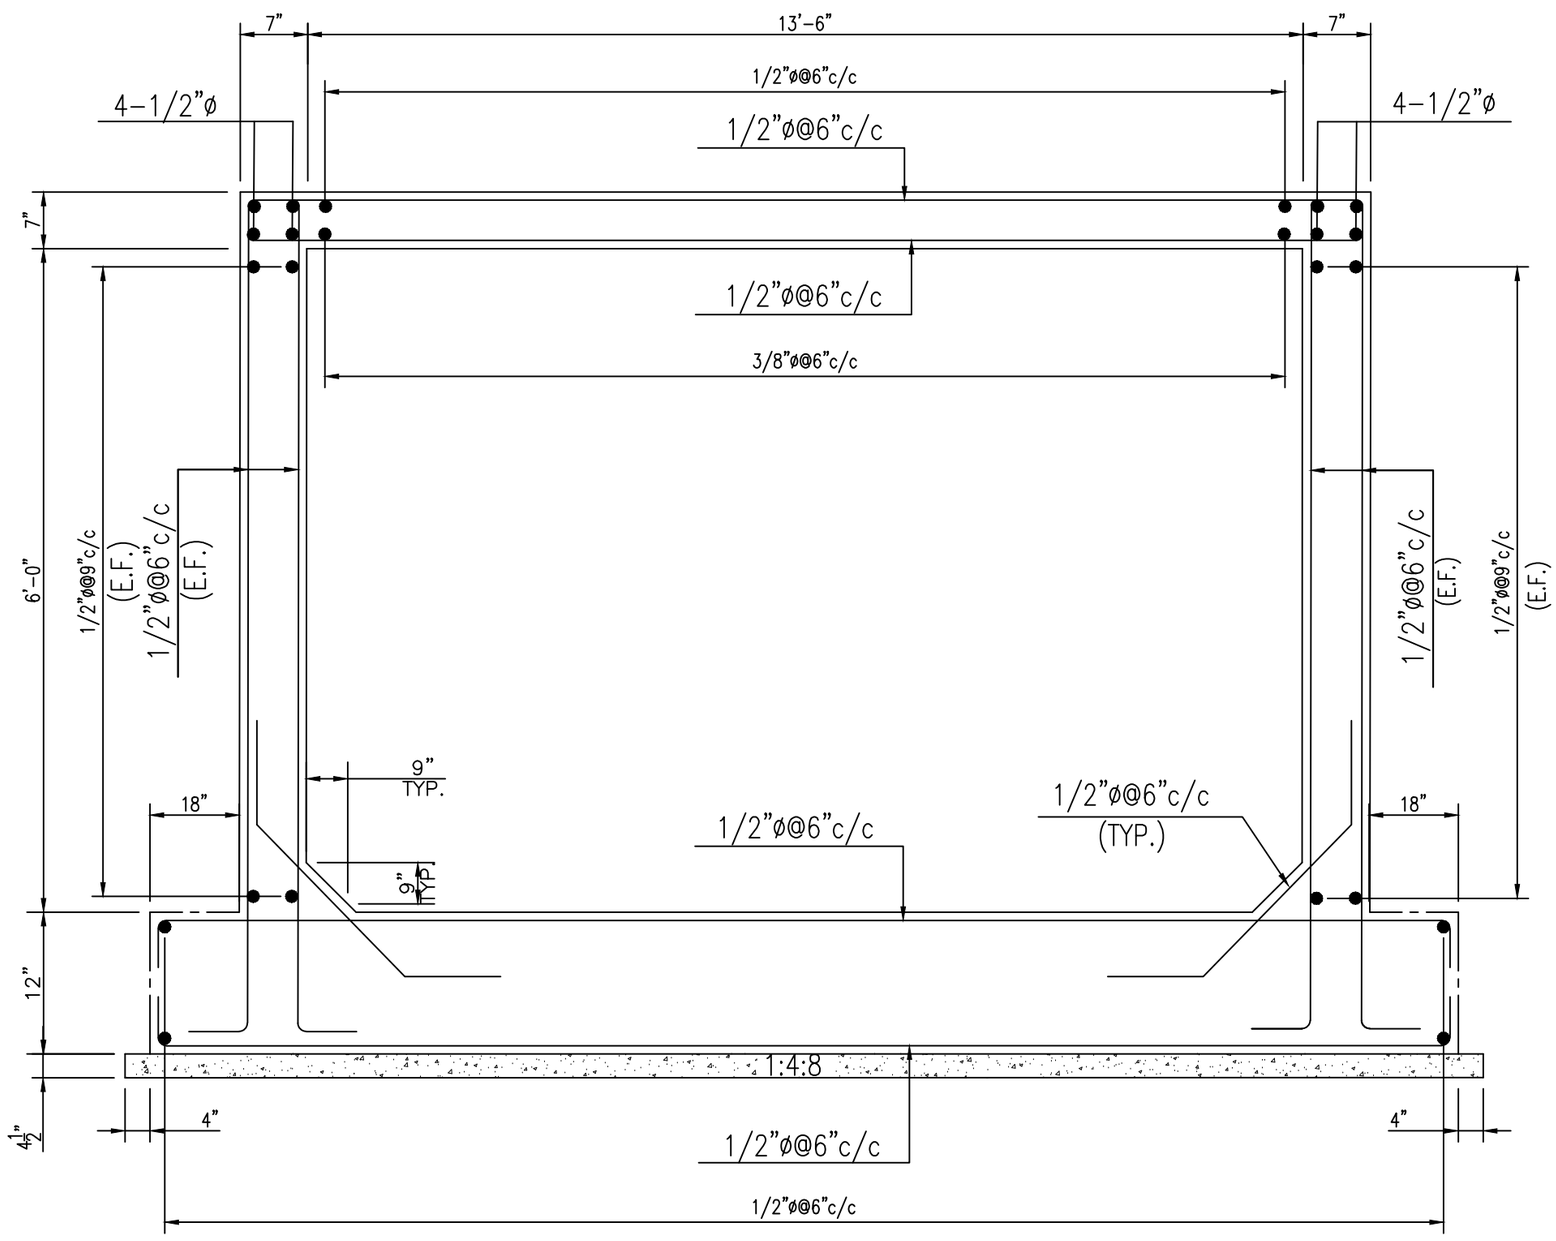

SECTION OF O.H.W.TANK

2'-0" RISE FROM SLAB

00 UNDERGROUND TANK & OVERHEAD TANK DETAIL

GENERAL NOTES:

1. THE COPYRIGHT OF THIS DRAWING IS VESTED IN YourSpreadsheets AND IT MAY NOT BE REPRODUCED IN WHOLE OR PART OR USED FOR THE MANUFACTURE OF ANY ARTICLE WITHOUT THE EXPRESS PERMISSION OF THE COPYRIGHT HOLDERS.
2. WORK TO FIGURED DIMENSIONS ONLY.
3. THIS DRAWING IS TO BE READ IN CONJUNCTION WITH ALL RELEVANT ARCHITECT'S, SERVICE ENGINEER'S AND YourSpreadsheets DRAWINGS .
ALL DRWAING ARE THE PROPOERTY OF THE DESIGNER & THEY ARE NOT TO BE REPRODUCED IN WHOLE OR IN PART WITHOUT WRITTEN CONSENT FROM THE DESIGN WING
CONTRACTOR TO CHECK &VERIFY ALL DIMENSIONS BEFORE COMMENCING WORK & TO REPORT ANY DISCREPANCIES TO THE DESIGN WING.
DO NOT SCALE DRAWINGS.
ALL CONSTRUCTION TO BE ACCORDING TO BEST COMMON PRACTICE.

REV:	DESCRIPTION:	BY:	DATE:
A	ARCHITECTURE DRAWING	----	25-12-25
B	STRUCTURE DRAWING	----	27-12-25

PROJECT NAME:
300 SQ.YARD HOUSE
ARCHITECTURE DRAWING

SIGNATURE BY:

DRAWING TITLE:
ARCHITECTURAL DRAWING

DRAWN BY: MUDASSIR
CHECKED BY: M.SHEHERYAR
APPROVED BY: M.SHEHERYAR
DATE: 27-DEC-2025

CLIENT
MR. ROHAN
KARACHI...

DESIGNED BY:-

E.D.C.O
ENGINEERING DESIGNING CONSTRUCTION OFFICIAL
ARCHITECT| PLANNERS| ENGINEERS| INTERIOR| B.O.Q| EXTERIOR| CONSULT| STRUCTURE DESIGN| PLANNING| LAND SURVEY| CONSTRUCTION| 3D ANIMATION VIDEO| RENOVATION|
MUHAMMAD SHEHERYAR
CONTACT- 0312-2118445|D.H.A PHASE VII

PROJECT NO: AR-7590
SCALE: 1/8"=1'-0"
SHEET SIZE: A3
DRAWING NO: ARC
SHEET NO ----------
REVISION: YES
UNIT: INCHES&FEET

GEN.NOTES

1. Coordinate all structural drawings with architectural drawing.
2. Foundations have designed for an assumed bearing capacity of 1.5tsf
3. Use c.c.1/1/2-3 mix for columns & water. Structures .(fc'=4000 ps)
4. Use 1 : 1.5 : 3 conc mix for all other R.C.C. works (fc' = 4000 psi)
5. Over laps shall be 54x Ø.
6. Use O.P Cement in all r.c.c works upto Plinth Level.
7. All foundations shall bear on undisturbed natural soil using S.R Cement Up to plinth level.
8. All steel is S 60" Steel with a minimum yield strength of (60,000 P.S.I) and confirming to ASTM A 615 For Deformed bars.
9. Contractor shall prepare AT Least 4 Cubes for each pour and shall submit the test report to Architect / ST. Engineer for 28 days crushing strength. In case not cast contractor will responsible for negligence.
10. PROVIDED CLEAR COVER, IF NOT OTHERWISE SPECIFIED.

a) FOUNDATIONS = 3" BOTTOM, 2 "TOP TO MAIN REINF.
b) COLUMNS = 1" TO MAIN REINFORCEMENT.
c) BEAMS = 1" TO MAIN REINFORCEMENT FROM TOP & BOTTOM.

11. CONCRETE SHALL DEVELOPED 28 DAYS WORK CUBE STRENGTH OF:
COLUM fc'= 4000 psi (CUBE STRENGTH 4000 psi).
ALL CONCRETE fc' = 4000 psi. (CUBE STRENGTH 4000 psi.
12. DO NOT SCALE ANY BAR LENGTH & DIMENSIONS.
13. ALL DETAIL MUST BE STRICTLY FOLLOWED.
14. All reinforcements shall be cold worked twisted bars with min yield strength 60, 000 psi
15. DO NOT STORE SAND OR DEBRIS IN ONE ROOM, EXCEEDING DESIGN LIVE LOAD.
16- 4000 PSI FOR RAFT /FOUNDATION.
17- 4000 PSI FOR COLUMN/ BEAM/ SLAB.
18- ALL LEVELS TO BE CO-ORDINATED WITH ARCH. DRAWING.
19- READY MIX CONCRETE TO BE USED.
20- RAFT /FOUNDATION THICKNESS ALSO SHOULD BE DEPEND ON SOIL CONDITION DURING EXCAVATION.
21- S.R CEMENT SHOULD BE USE IN FOUNDATION (FALCON)
22- ALL SLAB ARE 6" THICKNESS UNLESS NOTED OTHERWISE.

GENERAL NOTES:
1. THE COPYRIGHT OF THIS DRAWING IS VESTED IN YourSpreadsheets AND IT MAY NOT BE REPRODUCED IN WHOLE OR PART OR USED FOR THE MANUFACTURE OF ANY ARTICLE WITHOUT THE EXPRESS PERMISSION OF THE COPYRIGHT HOLDERS.
2. WORK TO FIGURED DIMENSIONS ONLY.
3. THIS DRAWING IS TO BE READ IN CONJUNCTION WITH ALL RELEVANT ARCHITECT'S, SERVICE ENGINEER'S AND YourSpreadsheets DRAWINGS .
ALL DRWAING ARE THE PROPOERTY OF THE DESIGNER & THEY ARE NOT TO BE REPRODUCED IN WHOLE OR IN PART WITHOUT WRITTEN CONSENT FROM THE DESIGN WING
CONTRACTOR TO CHECK &VERIFY ALL DIMENSIONS BEFORE COMMENCING WORK & TO REPORT ANY DISCREPANCIES TO THE DESIGN WING.
DO NOT SCALE DRAWINGS.
ALL CONSTRUCTION TO BE ACCORDING TO BEST COMMON PRACTICE.

REV:	DESCRIPTION:	BY:	DATE:
A	ARCHITECTURE DRAWING	----	25-12-25
B	STRUCTURE DRAWING	----	27-12-25

PROJECT NAME:
300 SQ.YARD HOUSE ARCHITECTURE DRAWING

SIGNATURE BY:

DRAWING TITLE:
ARCHITECTURAL DRAWING

DRAWN BY: MUDASSIR
CHECKED BY: M.SHEHERYAR
APPROVED BY: M.SHEHERYAR
DATE: 27-DEC-2025

CLIENT
MR. ROHAN
KARACHI...

DESIGNED BY:-
E.D.C.O
ENGINEERING DESIGNING CONSTRUCTION OFFICIAL
ARCHITECT| PLANNERS| ENGINEERS| INTERIOR| B.O.Q| EXTERIOR| CONSULT| STRUCTURE DESIGN| PLANNING| LAND SURVEY| CONSTRUCTION| 3D ANIMATION VIDEO| RENOVATION|
MUHAMMAD SHEHERYAR
CONTACT- 0312-2118445|D.H.A PHASE VII

PROJECT NO: AR-7590
SCALE: 1/8"=1'-0"
SHEET SIZE: A3
DRAWING NO: ARC
SHEET NO ----------
REVISION: YES
UNIT: INCHES&FEET

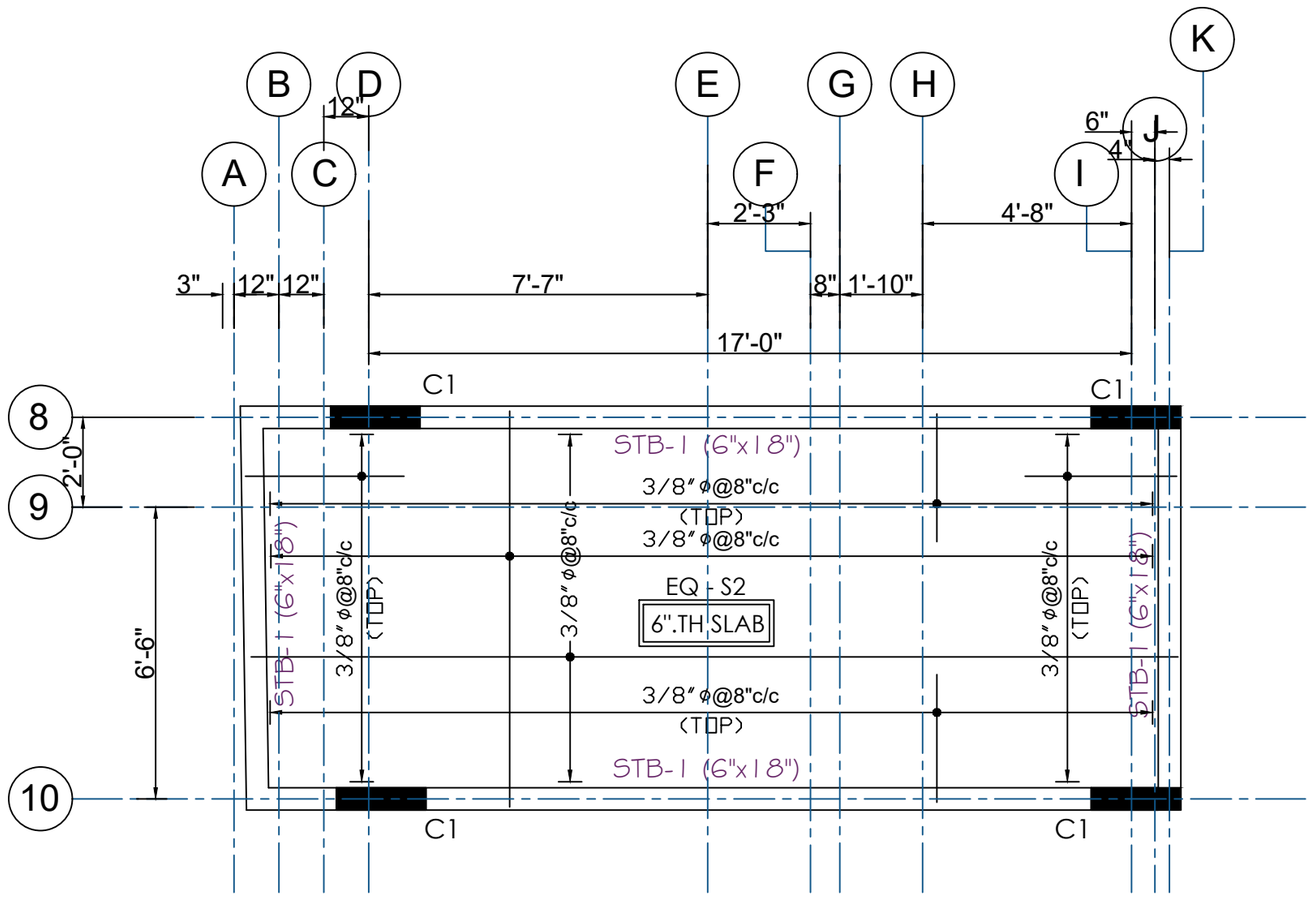

STAIR TOWER FRAMING PLAN

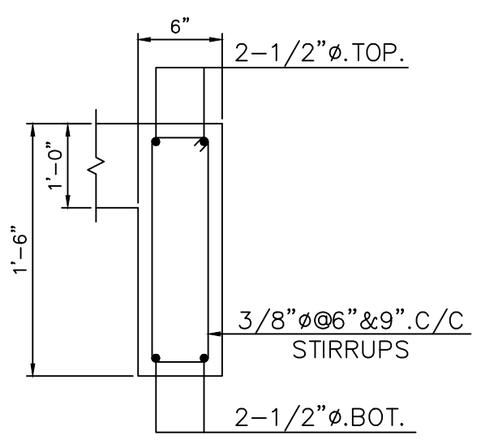

BEAM STB1

SCALE 1"=1'-0"

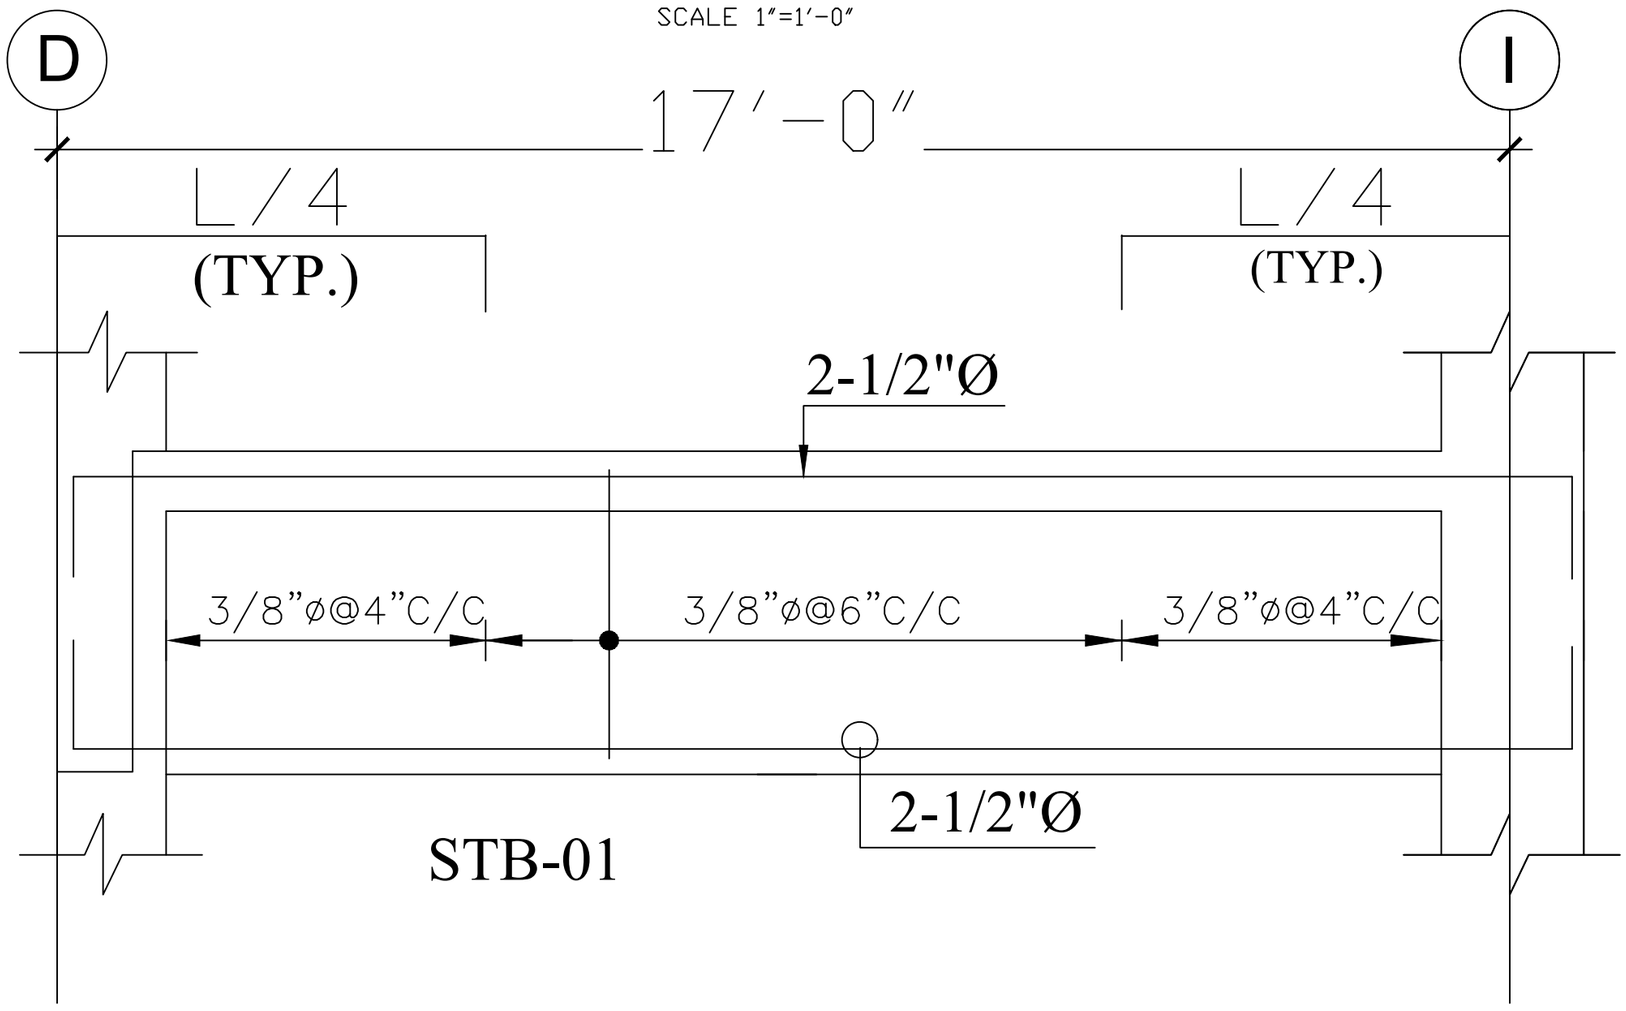

TYP. ELEV. OF STAIR TOWER BEAM

(ON GRID ' 8 ' SIZE = 6" X 18")

00 STAIR TOWER FRAMING PLAN

GENERAL NOTES:

1. THE COPYRIGHT OF THIS DRAWING IS VESTED IN YourSpreadsheets AND IT MAY NOT BE REPRODUCED IN WHOLE OR PART OR USED FOR THE MANUFACTURE OF ANY ARTICLE WITHOUT THE EXPRESS PERMISSION OF THE COPYRIGHT HOLDERS.
2. WORK TO FIGURED DIMENSIONS ONLY.
3. THIS DRAWING IS TO BE READ IN CONJUNCTION WITH ALL RELEVANT ARCHITECT'S, SERVICE ENGINEER'S AND YourSpreadsheets DRAWINGS .

ALL DRWAING ARE THE PROPOERTY OF THE DESIGNER & THEY ARE NOT TO BE REPRODUCED IN WHOLE OR IN PART WITHOUT WRITTEN CONSENT FROM THE DESIGN WING

CONTRACTOR TO CHECK &VERIFY ALL DIMENSIONS BEFORE COMMENCING WORK & TO REPORT ANY DISCREPANCIES TO THE DESIGN WING.

DO NOT SCALE DRAWINGS.

ALL CONSTRUCTION TO BE ACCORDING TO BEST COMMON PRACTICE.

REV:	DESCRIPTION:	BY:	DATE:
A	ARCHITECTURE DRAWING	----	25-12-25
B	STRUCTURE DRAWING	----	27-12-25

PROJECT NAME:
300 SQ.YARD HOUSE ARCHITECTURE DRAWING

SIGNATURE BY:

DRAWING TITLE:
ARCHITECTURAL DRAWING

DRAWN BY: MUDASSIR
CHECKED BY: M.SHEHERYAR
APPROVED BY: M.SHEHERYAR
DATE: 27-DEC-2025

CLIENT
MR. ROHAN
KARACHI...

DESIGNED BY:-

E.D.C.O
ENGINEERING DESIGNING CONSTRUCTION OFFICIAL
ARCHITECT| PLANNERS| ENGINEERS| INTERIOR| B.O.Q| EXTERIOR| CONSULT| STRUCTURE DESIGN| PLANNING| LAND SURVEY| CONSTRUCTION| 3D ANIMATION VIDEO| RENOVATION|
MUHAMMAD SHEHERYAR
CONTACT- 0312-2118445|D.H.A PHASE VII

PROJECT NO: AR-7590
SCALE: 1/8"=1'-0"
SHEET SIZE: A3
DRAWING NO: ARC
SHEET NO ----------
REVISION: YES
UNIT: INCHES&FEET

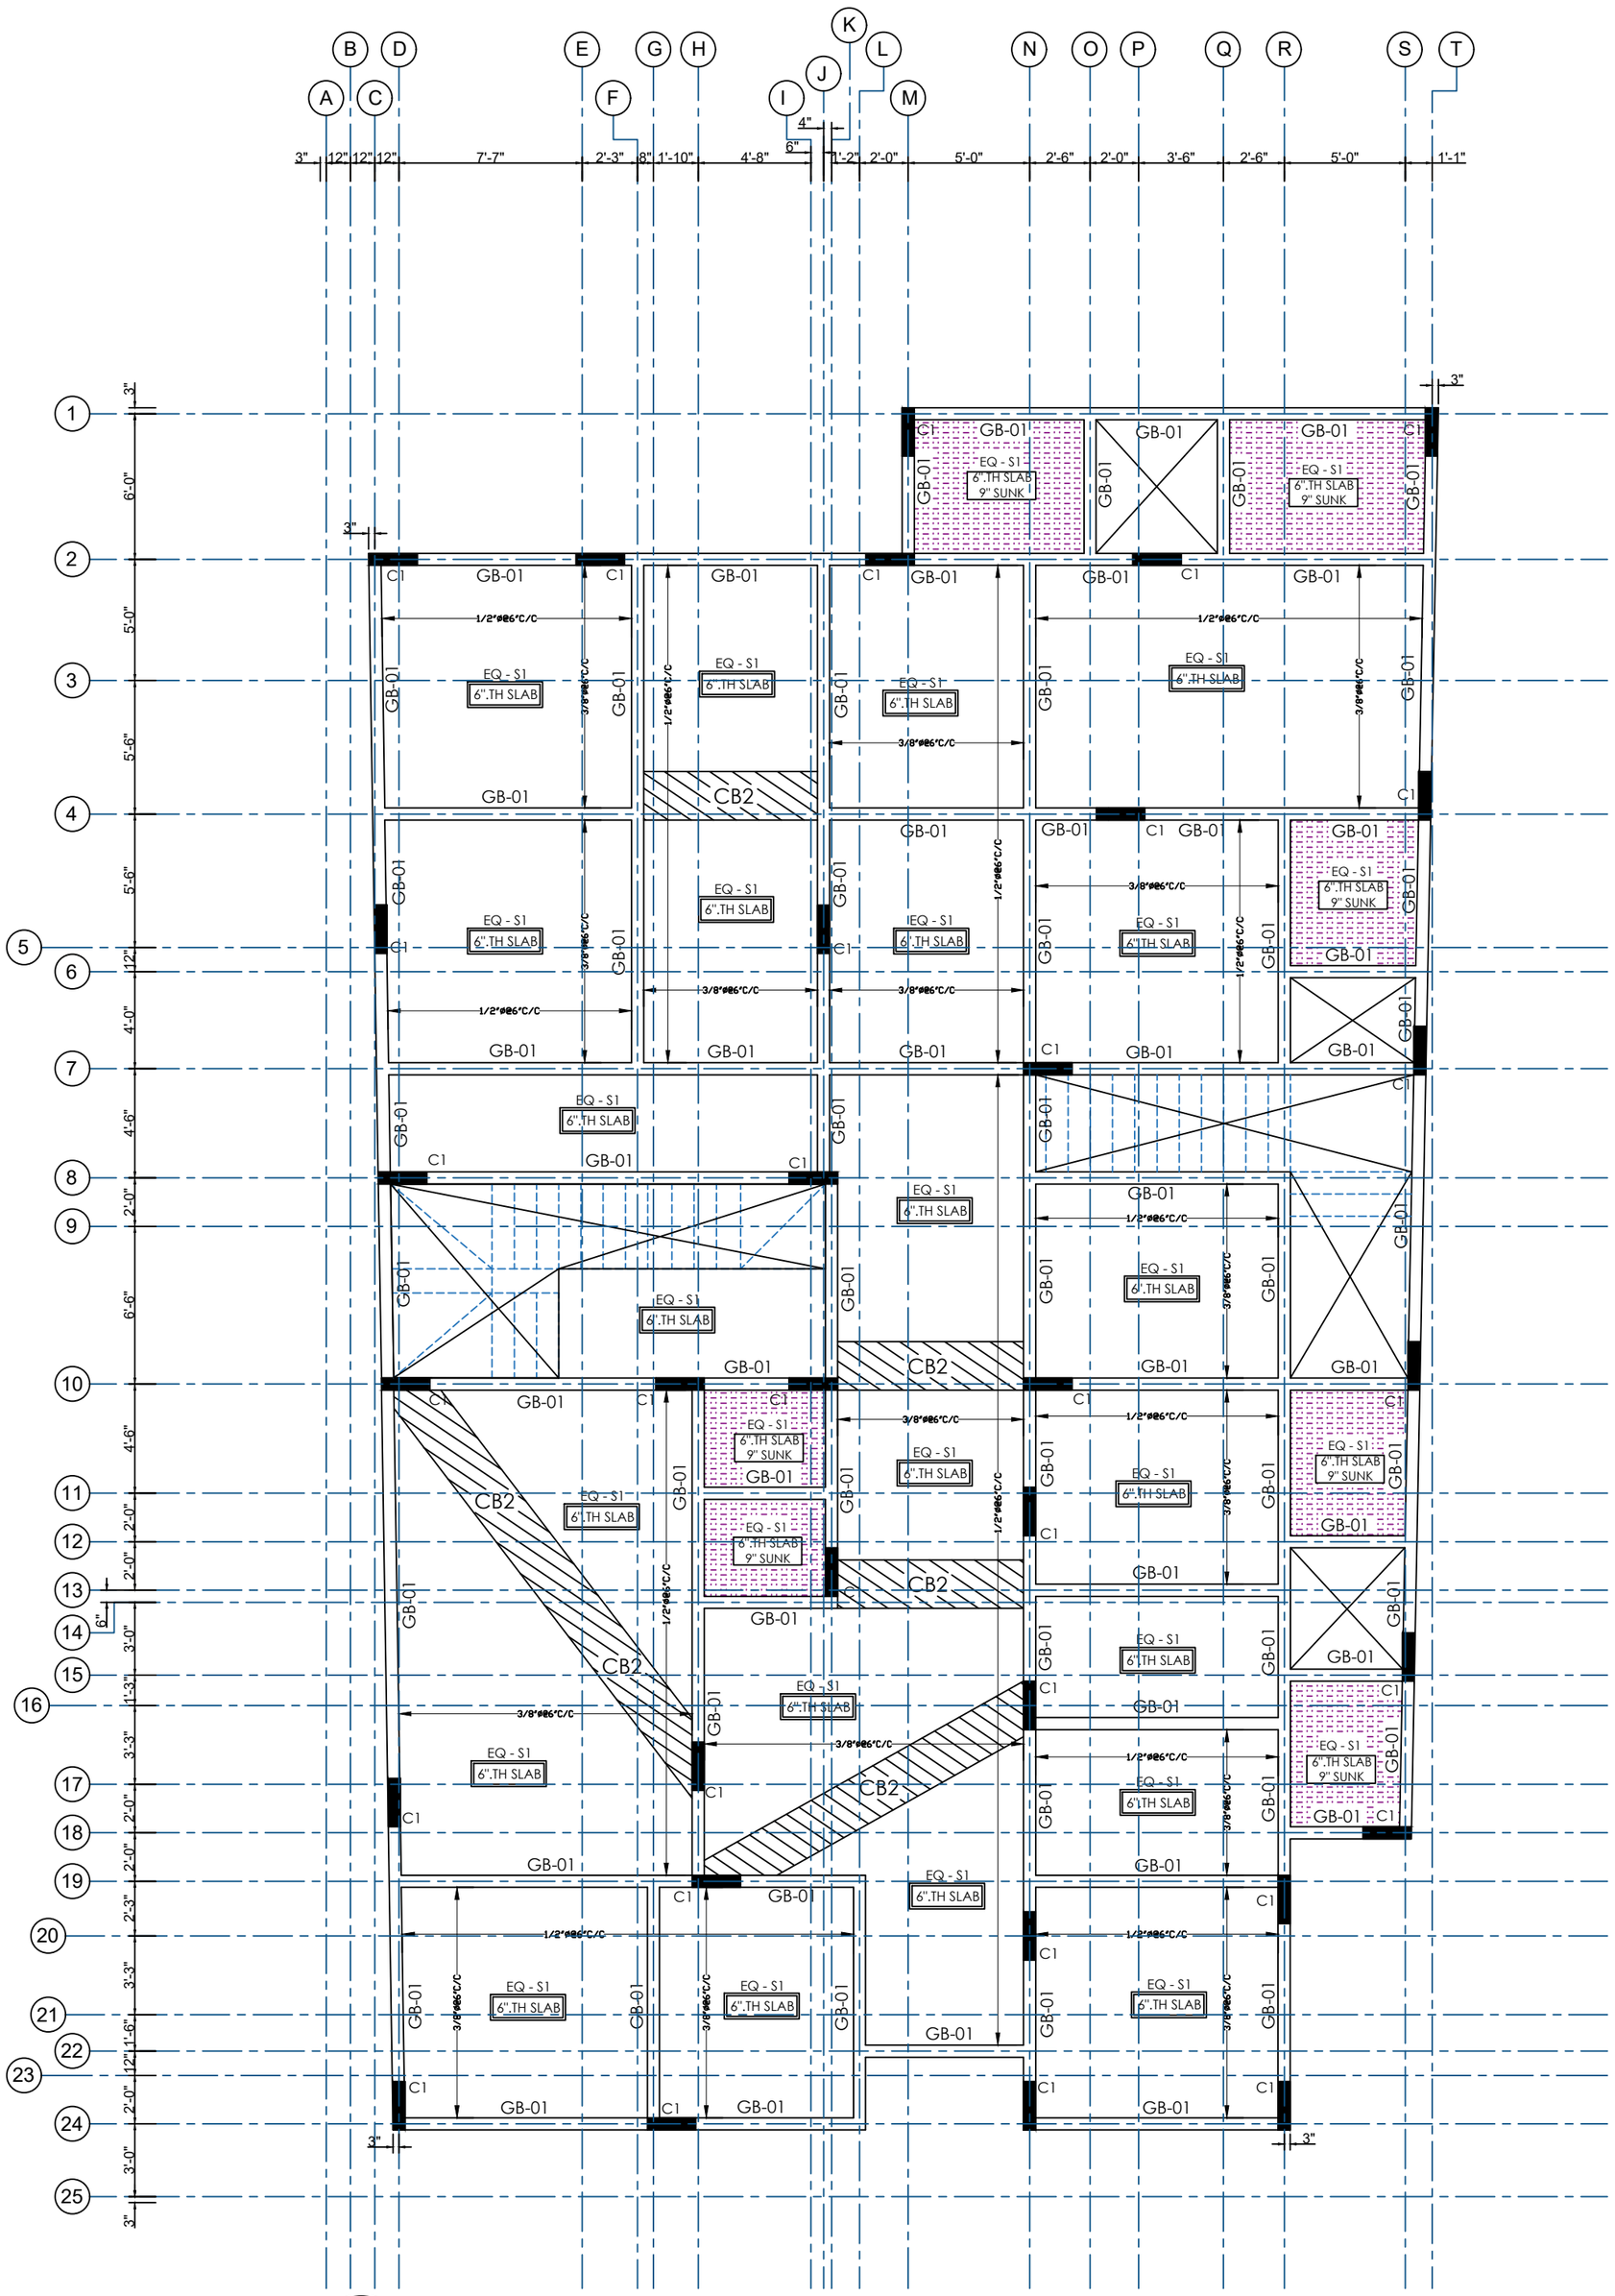

14 GROUND FLOOR FRAMING PLAN

NOTES:-

1- 4000 PSI FOR RAFT / FOUNDATION.
2- 4000 PSI FOR COLUMN/ BEAM/ SLAB.
3- ALL LEVELS TO BE CO-ORDINATED WITH ARCH. DRAWING.
4- READY MIX CONCRETE TO BE USED.
5- RAFT /FOUNDATION THICKNESS ALSO SHOULD BE DEPEND ON SOIL CONDITION DURING EXCAVATION.

GENERAL NOTES:

1. THE COPYRIGHT OF THIS DRAWING IS VESTED IN YourSpreadsheets AND IT MAY NOT BE REPRODUCED IN WHOLE OR PART OR USED FOR THE MANUFACTURE OF ANY ARTICLE WITHOUT THE EXPRESS PERMISSION OF THE COPYRIGHT HOLDERS.
2. WORK TO FIGURED DIMENSIONS ONLY.
3. THIS DRAWING IS TO BE READ IN CONJUNCTION WITH ALL RELEVANT ARCHITECT'S, SERVICE ENGINEER'S AND YourSpreadsheets DRAWINGS .

ALL DRWAING ARE THE PROPOERTY OF THE DESIGNER & THEY ARE NOT TO BE REPRODUCED IN WHOLE OR IN PART WITHOUT WRITTEN CONSENT FROM THE DESIGN WING

CONTRACTOR TO CHECK &VERIFY ALL DIMENSIONS BEFORE COMMENCING WORK & TO REPORT ANY DISCREPANCIES TO THE DESIGN WING.

DO NOT SCALE DRAWINGS.

ALL CONSTRUCTION TO BE ACCORDING TO BEST COMMON PRACTICE.

REV:	DESCRIPTION:	BY:	DATE:
A	ARCHITECTURE DRAWING	----	25-12-25
B	STRUCTURE DRAWING	----	27-12-25

PROJECT NAME:
300 SQ.YARD HOUSE ARCHITECTURE DRAWING

SIGNATURE BY:

DRAWING TITLE:
ARCHITECTURAL DRAWING

DRAWN BY: MUDASSIR

CHECKED BY: M.SHEHERYAR

APPROVED BY: M.SHEHERYAR

DATE: 27-DEC-2025

CLIENT
MR. ROHAN
KARACHI...

DESIGNED BY:-

E.D.C.O
ENGINEERING DESIGNING CONSTRUCTION OFFICIAL
ARCHITECT| PLANNERS| ENGINEERS| INTERIOR| B.O.Q| EXTERIOR| CONSULT| STRUCTURE DESIGN| PLANNING| LAND SURVEY| CONSTRUCTION| 3D ANIMATION VIDEO| RENOVATION|
MUHAMMAD SHEHERYAR
CONTACT- 0312-2118445|D.H.A PHASE VII

PROJECT NO: AR-7590

SCALE: 1/8"=1'-0"

SHEET SIZE: A3

DRAWING NO: ARC

SHEET NO: ----------

REVISION: YES

UNIT: INCHES&FEET

S E W N

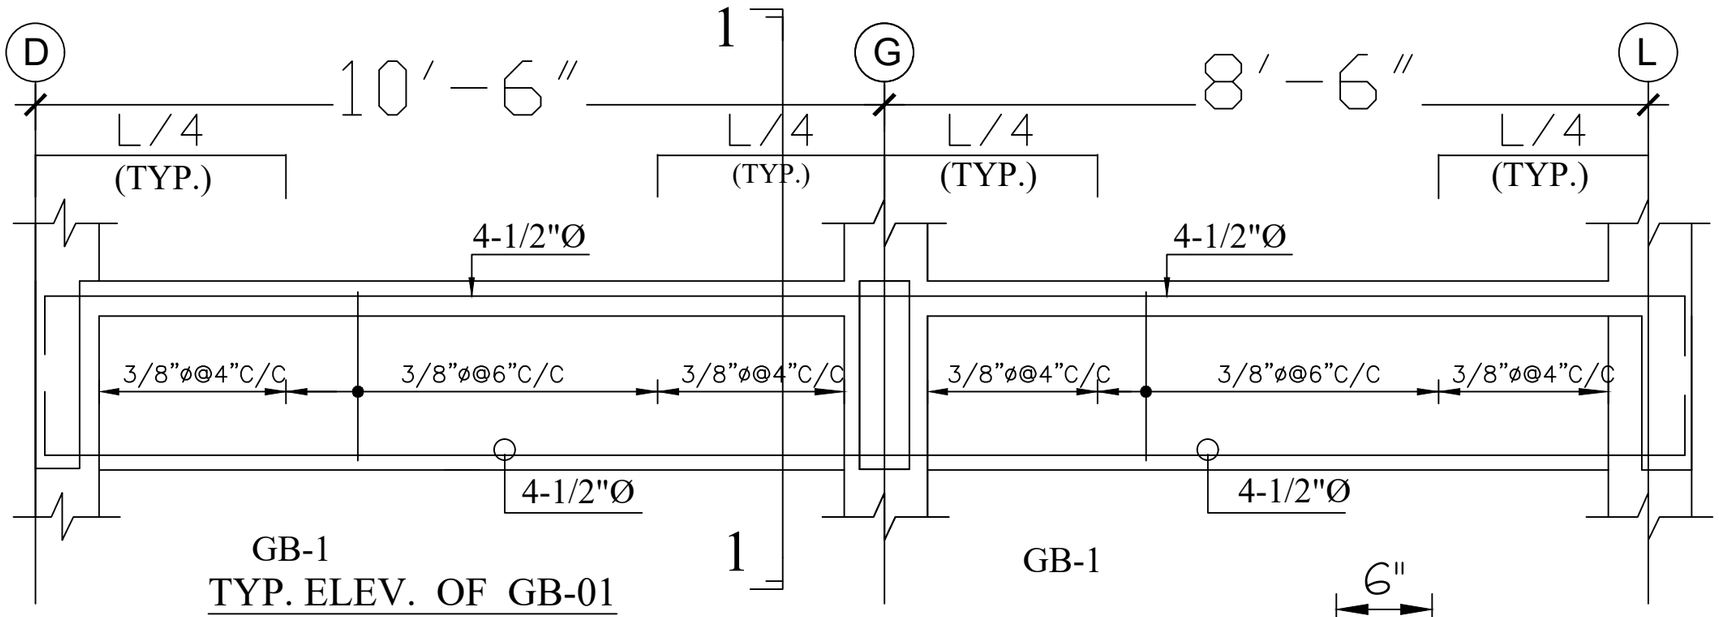

GB-1

GB-1

TYP. ELEV. OF GB-01

(ON GRID ' 24 ' SIZE = 6" X 30")

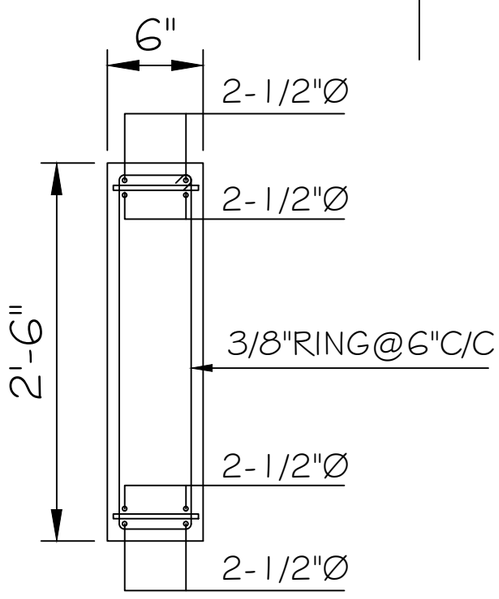

GB-1 (6″×30″)

SCALE 3/4″ = 1′-0″

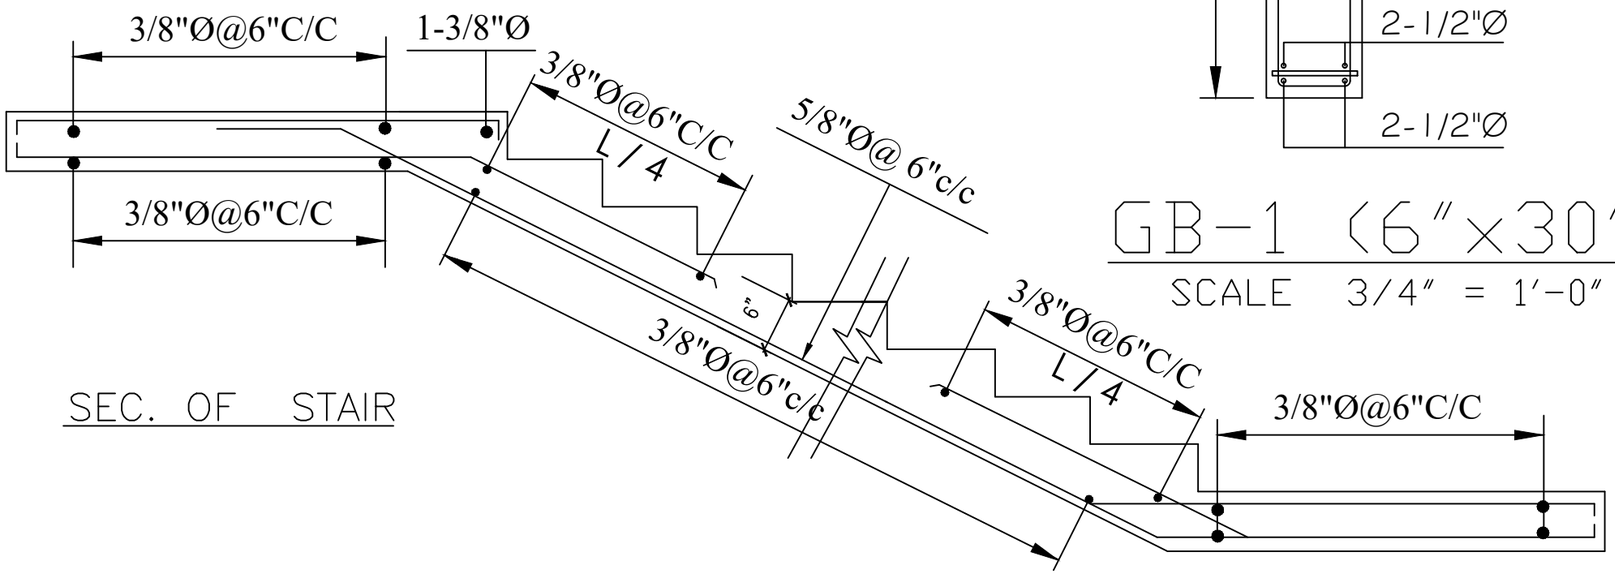

SEC. OF STAIR

SCHEDULE OF BEAM

MARKS	WIDTH	DEPTH	BOTTOM	TOP	EXTRA TOP	EXTRA BOT	RING
GB1	6"	30"	4-1/2"Ø	4-1/2"Ø	-	-	3/8"Ø@6" C/C

PLAN COLUMN L/4 4"@C/C REST @6"C/C

NOTES:-

01- ALL SLAB ARE 6" THICK UNLESS NOTED OTHER WISE.

02- FOR ALL LEVELS, GRIDS, DIMENSIONS ETC , REFER ARCH. DRGS.

03- PROVIDE 3/8" DIA @ 6" C/C DISTRIBUTION BARS NOTE SHOWN IN PLAN.

14 GROUND FLOOR FRAMING DETAIL

NOTES:-

1- 4000 PSI FOR RAFT / FOUNDATION.
2- 4000 PSI FOR COLUMN/ BEAM/ SLAB.
3- ALL LEVELS TO BE CO-ORDINATED WITH ARCH. DRAWING.
4- READY MIX CONCRETE TO BE USED.
5- RAFT /FOUNDATION THICKNESS ALSO SHOULD BE DEPEND ON SOIL CONDITION DURING EXCAVATION.

GENERAL NOTES:

1. THE COPYRIGHT OF THIS DRAWING IS VESTED IN YourSpreadsheets AND IT MAY NOT BE REPRODUCED IN WHOLE OR PART OR USED FOR THE MANUFACTURE OF ANY ARTICLE WITHOUT THE EXPRESS PERMISSION OF THE COPYRIGHT HOLDERS.
2. WORK TO FIGURED DIMENSIONS ONLY.
3. THIS DRAWING IS TO BE READ IN CONJUNCTION WITH ALL RELEVANT ARCHITECT'S, SERVICE ENGINEER'S AND YourSpreadsheets DRAWINGS .
ALL DRWAING ARE THE PROPOERTY OF THE DESIGNER & THEY ARE NOT TO BE REPRODUCED IN WHOLE OR IN PART WITHOUT WRITTEN CONSENT FROM THE DESIGN WING
CONTRACTOR TO CHECK &VERIFY ALL DIMENSIONS BEFORE COMMENCING WORK & TO REPORT ANY DISCREPANCIES TO THE DESIGN WING.
DO NOT SCALE DRAWINGS.
ALL CONSTRUCTION TO BE ACCORDING TO BEST COMMON PRACTICE.

REV:	DESCRIPTION:	BY:	DATE:
A	ARCHITECTURE DRAWING	----	25-12-25
B	STRUCTURE DRAWING	----	27-12-25

PROJECT NAME:
300 SQ.YARD HOUSE
ARCHITECTURE DRAWING

SIGNATURE BY:

DRAWING TITLE:
ARCHITECTURAL DRAWING

DRAWN BY: MUDASSIR
CHECKED BY: M.SHEHERYAR
APPROVED BY: M.SHEHERYAR
DATE: 27-DEC-2025

CLIENT
MR. ROHAN
KARACHI...

DESIGNED BY:-
E.D.C.O
ENGINEERING DESIGNING CONSTRUCTION OFFICIAL
ARCHITECT| PLANNERS| ENGINEERS| INTERIOR| B.O.Q| EXTERIOR| CONSULT| STRUCTURE DESIGN| PLANNING| LAND SURVEY| CONSTRUCTION| 3D ANIMATION VIDEO| RENOVATION|
MUHAMMAD SHEHERYAR
CONTACT- 0312-2118445|D.H.A PHASE VII

PROJECT NO: AR-7590
SCALE: 1/8"=1'-0"
SHEET SIZE: A3
DRAWING NO: ARC
SHEET NO ----------
REVISION: YES
UNIT: INCHES&FEET

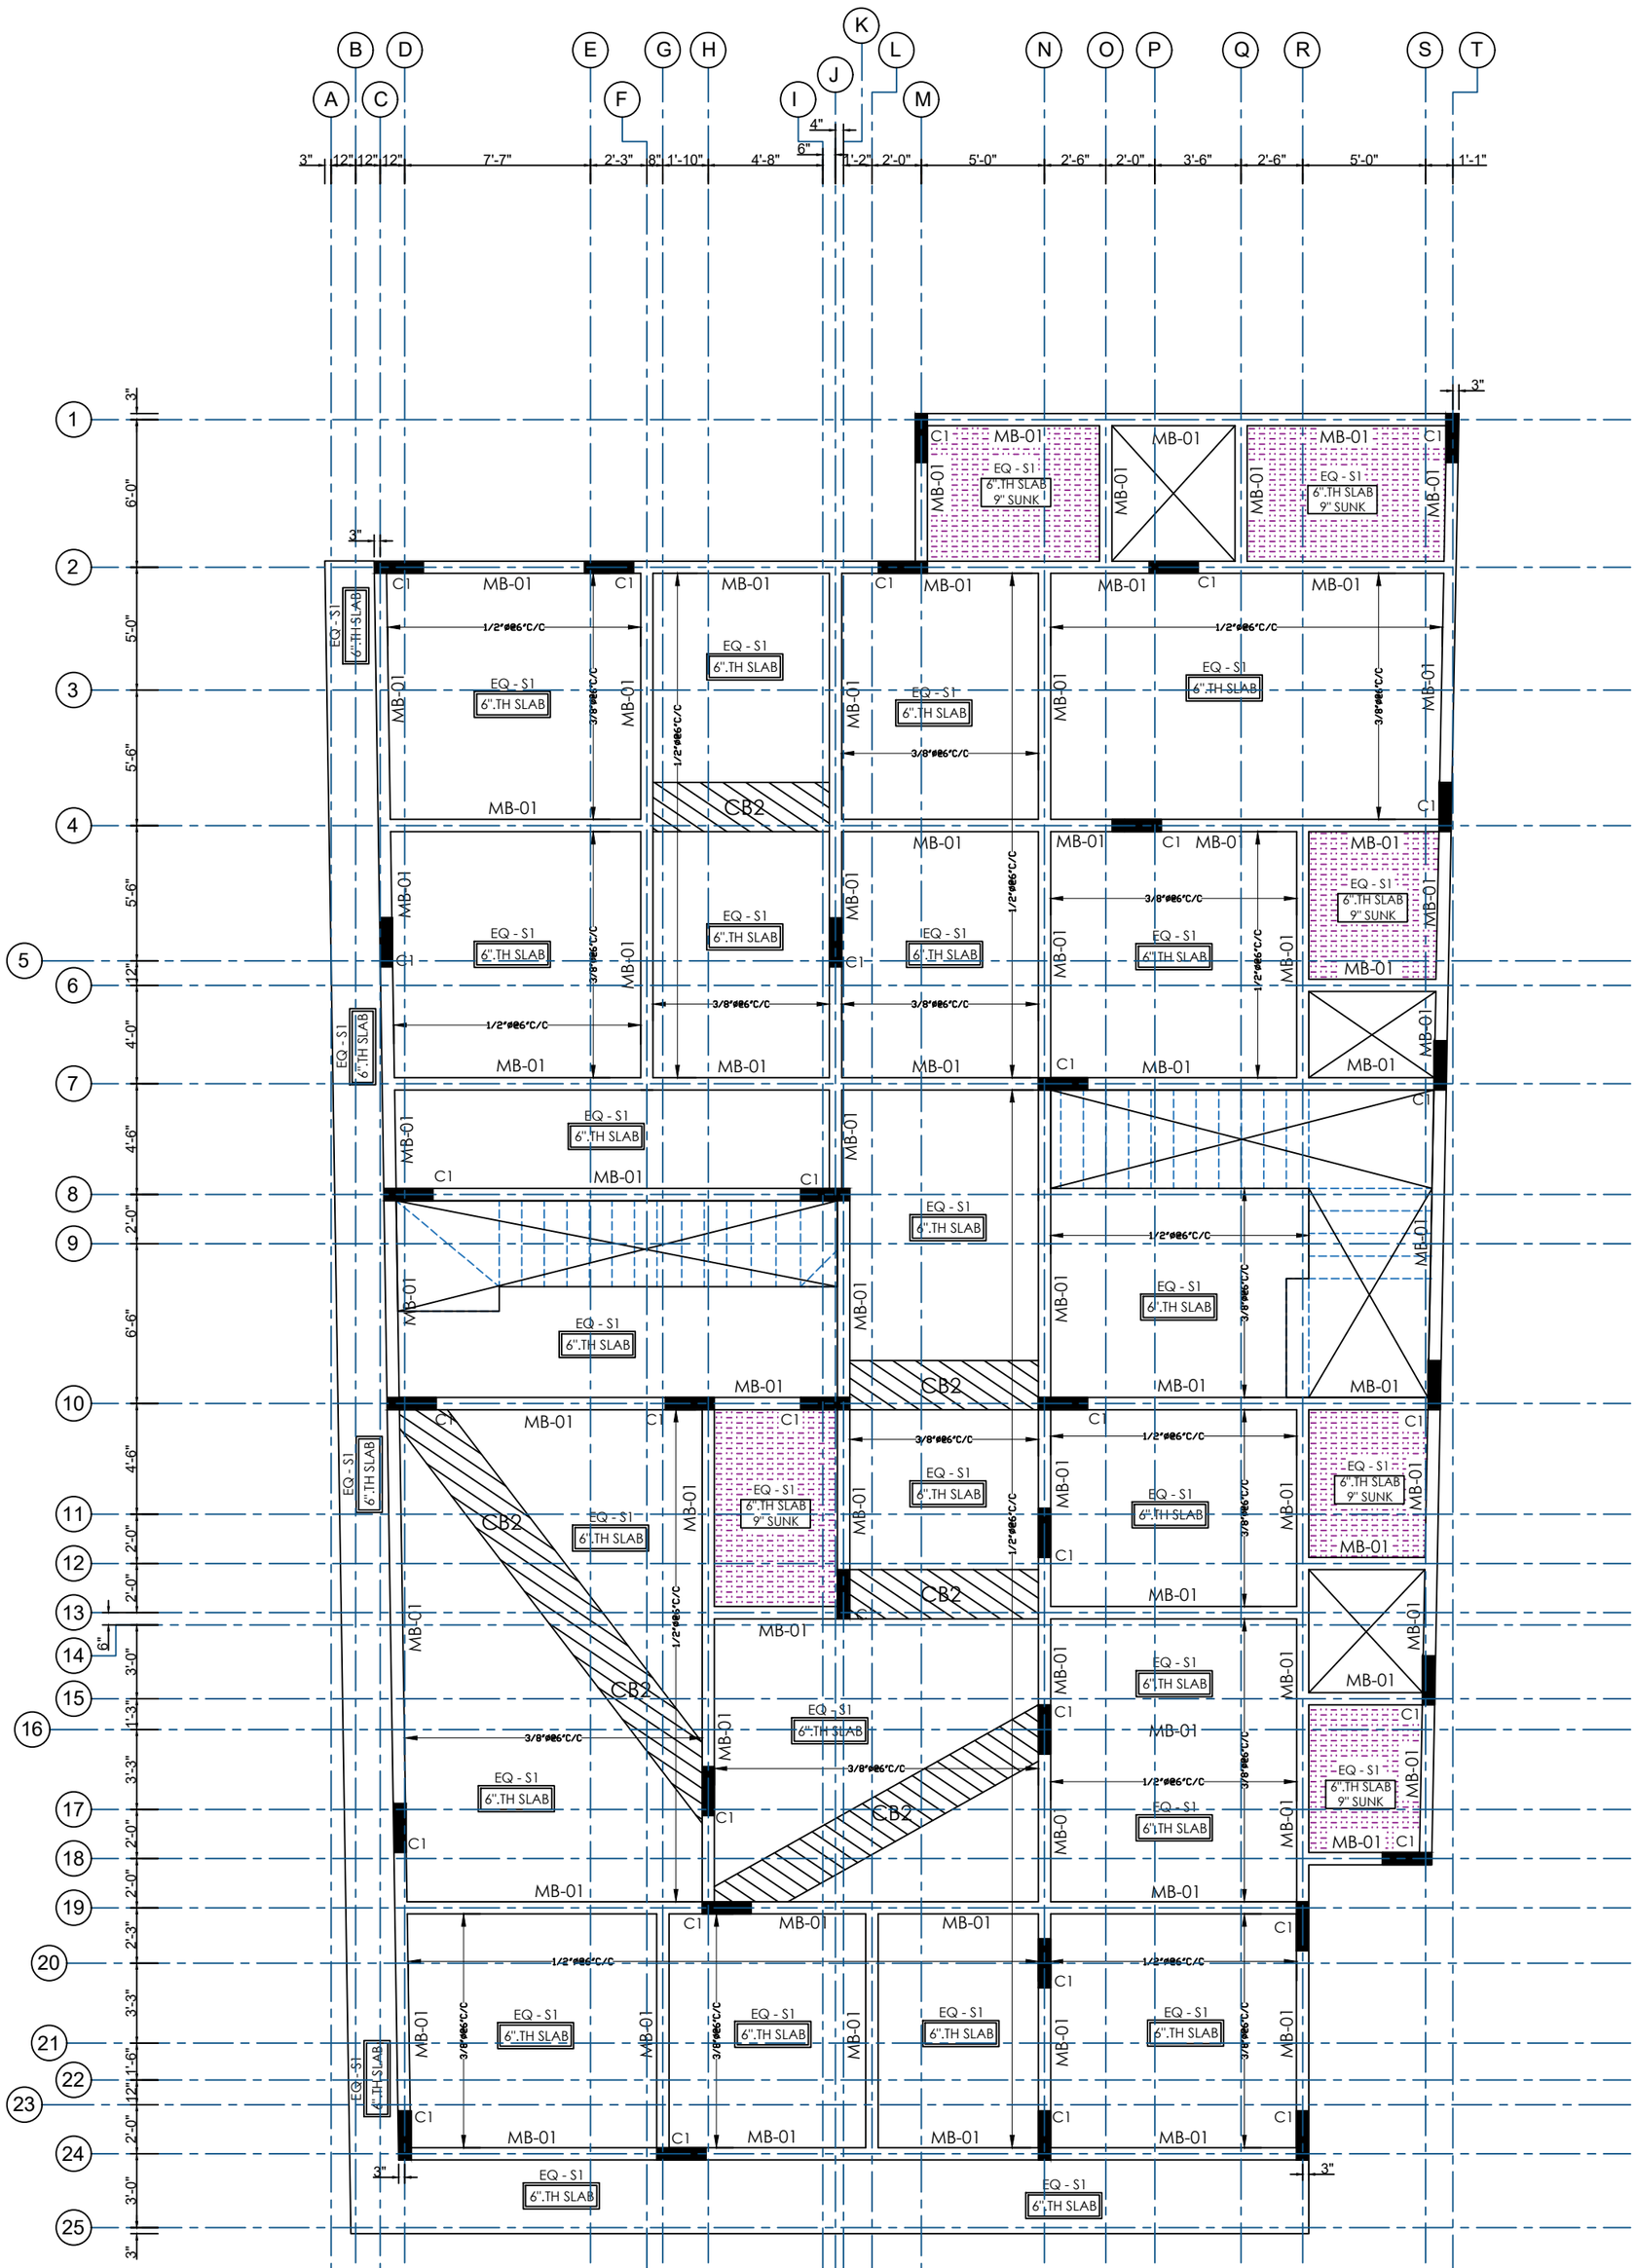

14 MEZZANINE FLOOR FRAMING PLAN

NOTES:-

1- 4000 PSI FOR RAFT / FOUNDATION.
2- 4000 PSI FOR COLUMN/ BEAM/ SLAB.
3- ALL LEVELS TO BE CO-ORDINATED WITH ARCH. DRAWING.
4- READY MIX CONCRETE TO BE USED.
5- RAFT /FOUNDATION THICKNESS ALSO SHOULD BE DEPEND ON SOIL CONDITION DURING EXCAVATION.

GENERAL NOTES:

1. THE COPYRIGHT OF THIS DRAWING IS VESTED IN YourSpreadsheets AND IT MAY NOT BE REPRODUCED IN WHOLE OR PART OR USED FOR THE MANUFACTURE OF ANY ARTICLE WITHOUT THE EXPRESS PERMISSION OF THE COPYRIGHT HOLDERS.
2. WORK TO FIGURED DIMENSIONS ONLY.
3. THIS DRAWING IS TO BE READ IN CONJUNCTION WITH ALL RELEVANT ARCHITECT'S, SERVICE ENGINEER'S AND YourSpreadsheets DRAWINGS .

ALL DRWAING ARE THE PROPOERTY OF THE DESIGNER & THEY ARE NOT TO BE REPRODUCED IN WHOLE OR IN PART WITHOUT WRITTEN CONSENT FROM THE DESIGN WING

CONTRACTOR TO CHECK &VERIFY ALL DIMENSIONS BEFORE COMMENCING WORK & TO REPORT ANY DISCREPANCIES TO THE DESIGN WING.
DO NOT SCALE DRAWINGS.
ALL CONSTRUCTION TO BE ACCORDING TO BEST COMMON PRACTICE.

REV:	DESCRIPTION:	BY:	DATE:
A	ARCHITECTURE DRAWING	----	25-12-25
B	STRUCTURE DRAWING	----	27-12-25

PROJECT NAME:
300 SQ.YARD HOUSE ARCHITECTURE DRAWING

SIGNATURE BY:

DRAWING TITLE:
ARCHITECTURAL DRAWING

DRAWN BY: MUDASSIR
CHECKED BY: M.SHEHERYAR
APPROVED BY: M.SHEHERYAR
DATE: 27-DEC-2025

CLIENT
MR. ROHAN
KARACHI...

DESIGNED BY:-

E.D.C.O
ENGINEERING DESIGNING CONSTRUCTION OFFICIAL
ARCHITECT| PLANNERS| ENGINEERS| INTERIOR| B.O.Q| EXTERIOR| CONSULT| STRUCTURE DESIGN| PLANNING| LAND SURVEY| CONSTRUCTION| 3D ANIMATION VIDEO| RENOVATION|
MUHAMMAD SHEHERYAR
CONTACT- 0312-2118445|D.H.A PHASE VII

PROJECT NO: AR-7590
SCALE: 1/8"=1'-0"
SHEET SIZE: A3
DRAWING NO: ARC
SHEET NO ----------
REVISION: YES
UNIT: INCHES&FEET

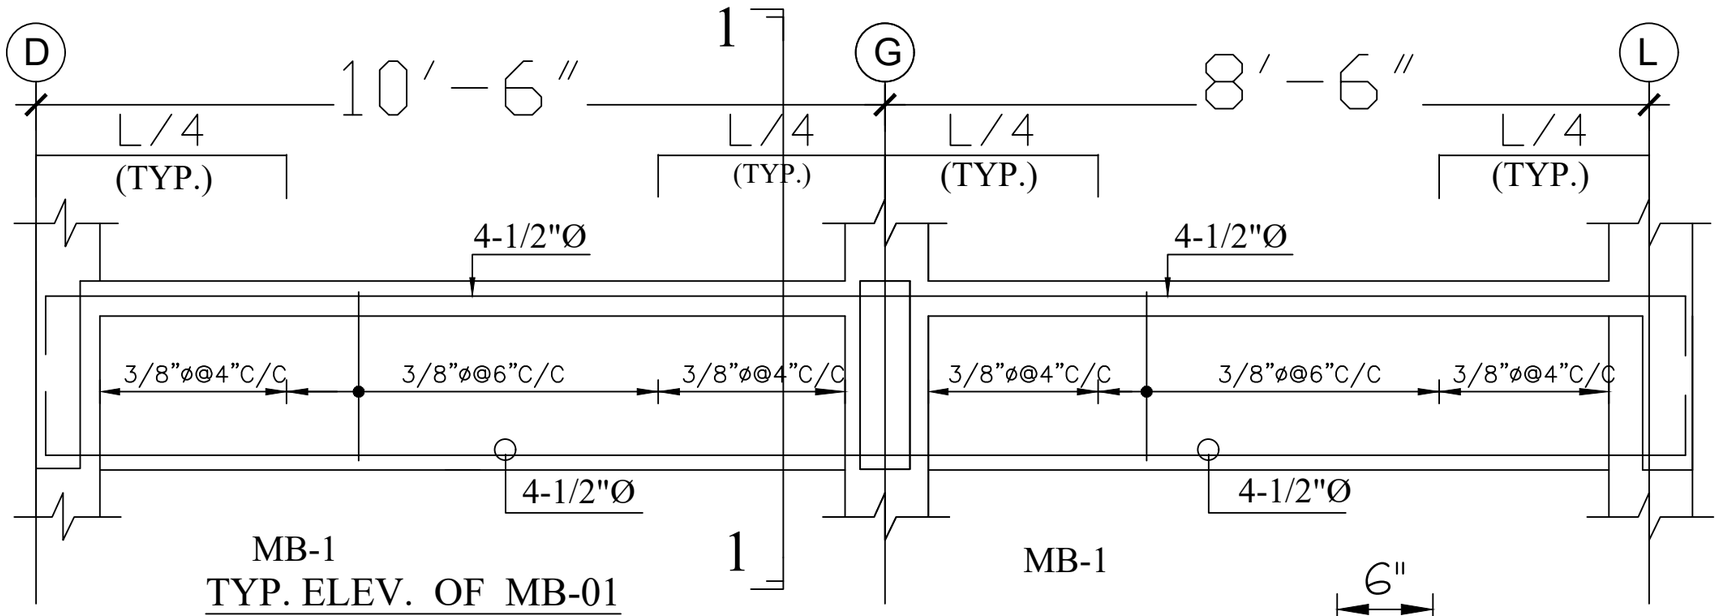

MB-1

TYP. ELEV. OF MB-01

(ON GRID ' 24 ' SIZE = 6" X 30")

MB-1

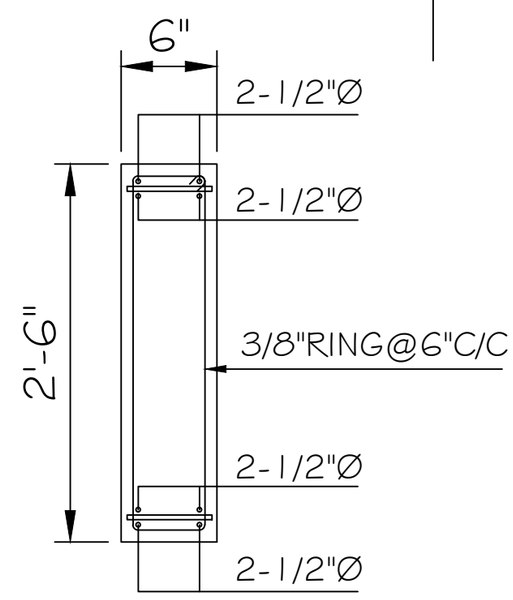

MB-1 (6″×30″)

SCALE 3/4″ = 1′-0″

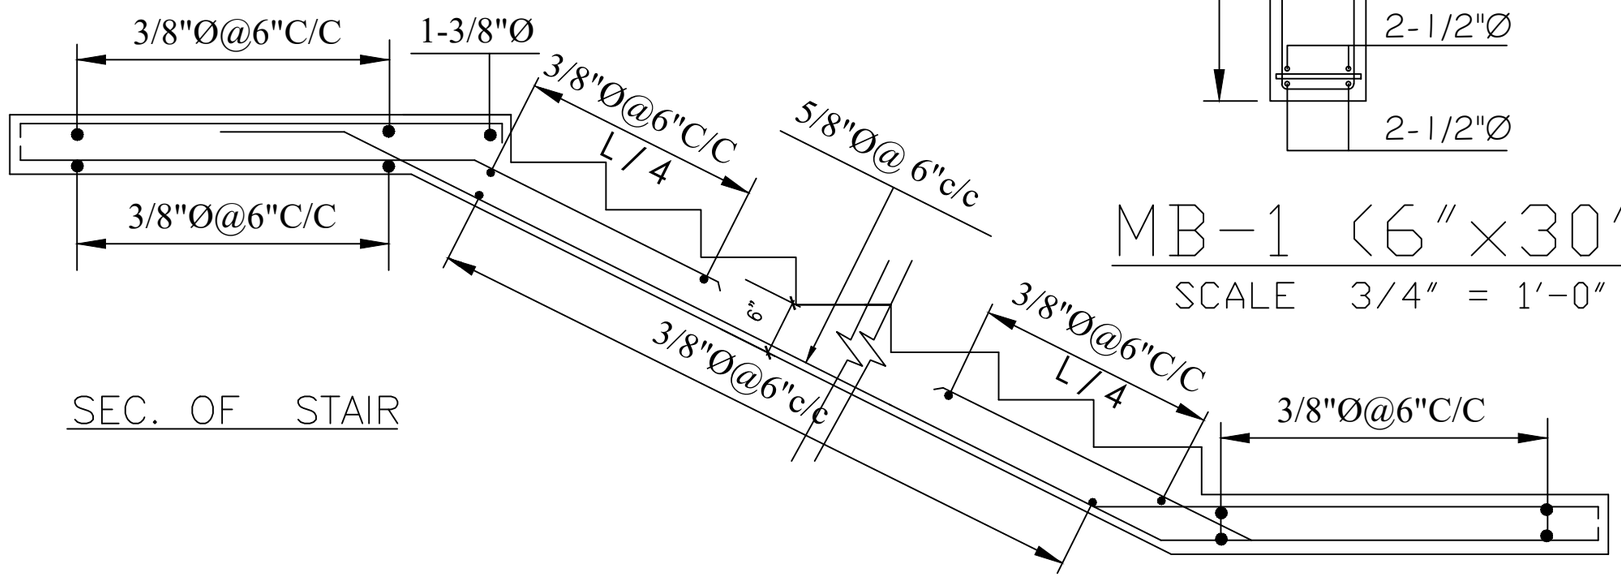

SEC. OF STAIR

SCHEDULE OF BEAM

MARKS	WIDTH	DEPTH	BOTTOM	TOP	EXTRA TOP	EXTRA BOT	RING
MB1	6"	30"	4-1/2"Ø	4-1/2"Ø	-	-	3/8"Ø@6" C/C

PLAN COLUMN L/4 4"@C/C REST @6"C/C

NOTES:-
01- ALL SLAB ARE 6" THICK UNLESS NOTED OTHER WISE.
02- FOR ALL LEVELS, GRIDS, DIMENSIONS ETC , REFER ARCH. DRGS.
03- PROVIDE 3/8" DIA @ 6" C/C DISTRIBUTION BARS NOTE SHOWN IN PLAN.

14 MEZZANINE FLOOR FRAMING DETAIL

NOTES:-

1- 4000 PSI FOR RAFT / FOUNDATION.
2- 4000 PSI FOR COLUMN/ BEAM/ SLAB.
3- ALL LEVELS TO BE CO-ORDINATED WITH ARCH. DRAWING.
4- READY MIX CONCRETE TO BE USED.
5- RAFT /FOUNDATION THICKNESS ALSO SHOULD BE DEPEND ON SOIL CONDITION DURING EXCAVATION.

GENERAL NOTES:

1. THE COPYRIGHT OF THIS DRAWING IS VESTED IN YourSpreadsheets AND IT MAY NOT BE REPRODUCED IN WHOLE OR PART OR USED FOR THE MANUFACTURE OF ANY ARTICLE WITHOUT THE EXPRESS PERMISSION OF THE COPYRIGHT HOLDERS.
2. WORK TO FIGURED DIMENSIONS ONLY.
3. THIS DRAWING IS TO BE READ IN CONJUNCTION WITH ALL RELEVANT ARCHITECT'S, SERVICE ENGINEER'S AND YourSpreadsheets DRAWINGS .
ALL DRWAING ARE THE PROPOERTY OF THE DESIGNER & THEY ARE NOT TO BE REPRODUCED IN WHOLE OR IN PART WITHOUT WRITTEN CONSENT FROM THE DESIGN WING
CONTRACTOR TO CHECK &VERIFY ALL DIMENSIONS BEFORE COMMENCING WORK & TO REPORT ANY DISCREPANCIES TO THE DESIGN WING.
DO NOT SCALE DRAWINGS.
ALL CONSTRUCTION TO BE ACCORDING TO BEST COMMON PRACTICE.

REV:	DESCRIPTION:	BY:	DATE:
A	ARCHITECTURE DRAWING	----	25-12-25
B	STRUCTURE DRAWING	----	27-12-25

PROJECT NAME:
300 SQ.YARD HOUSE
ARCHITECTURE DRAWING

SIGNATURE BY:

DRAWING TITLE:
ARCHITECTURAL DRAWING

DRAWN BY: MUDASSIR
CHECKED BY: M.SHEHERYAR
APPROVED BY: M.SHEHERYAR
DATE: 27-DEC-2025

CLIENT
MR. ROHAN
KARACHI...

DESIGNED BY:-
E.D.C.O
ENGINEERING DESIGNING CONSTRUCTION OFFICIAL
ARCHITECT| PLANNERS| ENGINEERS| INTERIOR| B.O.Q| EXTERIOR| CONSULT| STRUCTURE DESIGN| PLANNING| LAND SURVEY| CONSTRUCTION| 3D ANIMATION VIDEO| RENOVATION|
MUHAMMAD SHEHERYAR
CONTACT- 0312-2118445|D.H.A PHASE VII

PROJECT NO: AR-7590
SCALE: 1/8"=1'-0"
SHEET SIZE: A3
DRAWING NO: ARC
SHEET NO ----------
REVISION: YES
UNIT: INCHES&FEET

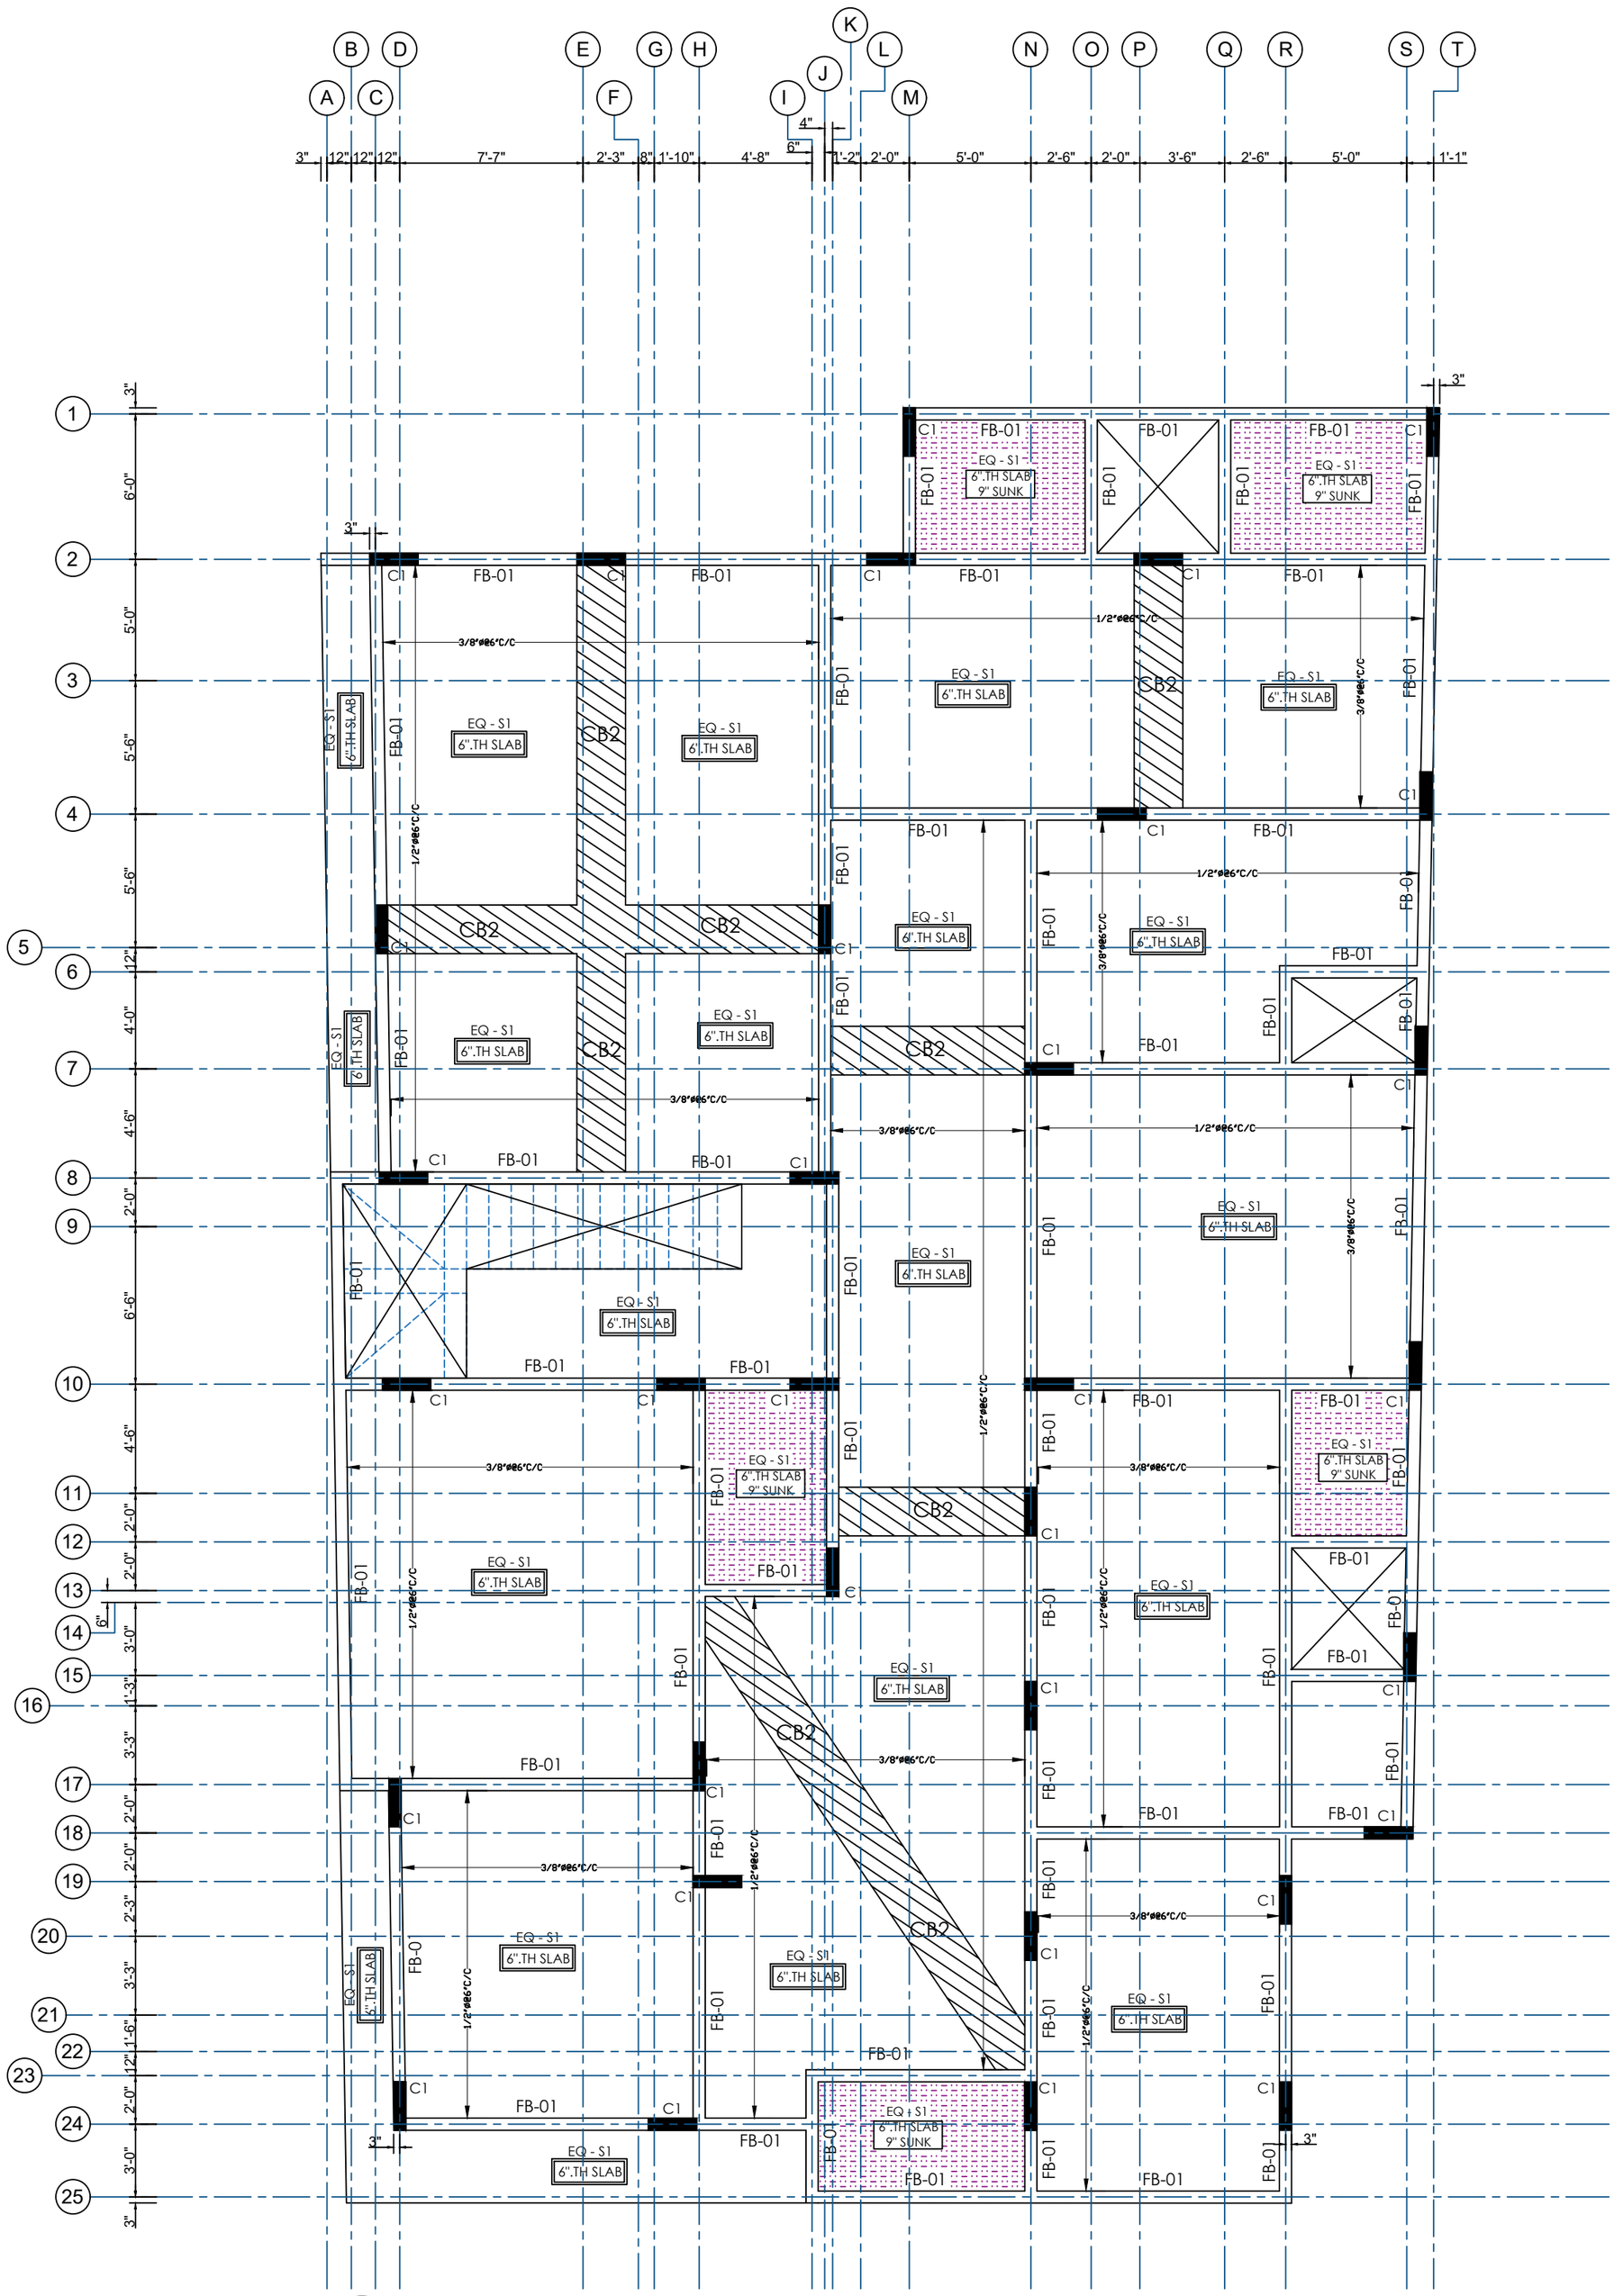

14 FIRST FLOOR FRAMING PLAN

NOTES:-

1- 4000 PSI FOR RAFT / FOUNDATION.
2- 4000 PSI FOR COLUMN/ BEAM/ SLAB.
3- ALL LEVELS TO BE CO-ORDINATED WITH ARCH. DRAWING.
4- READY MIX CONCRETE TO BE USED.
5- RAFT /FOUNDATION THICKNESS ALSO SHOULD BE DEPEND ON SOIL CONDITION DURING EXCAVATION.

GENERAL NOTES:

1. THE COPYRIGHT OF THIS DRAWING IS VESTED IN YourSpreadsheets AND IT MAY NOT BE REPRODUCED IN WHOLE OR PART OR USED FOR THE MANUFACTURE OF ANY ARTICLE WITHOUT THE EXPRESS PERMISSION OF THE COPYRIGHT HOLDERS.
2. WORK TO FIGURED DIMENSIONS ONLY.
3. THIS DRAWING IS TO BE READ IN CONJUNCTION WITH ALL RELEVANT ARCHITECT'S, SERVICE ENGINEER'S AND YourSpreadsheets DRAWINGS .

ALL DRWAING ARE THE PROPOERTY OF THE DESIGNER & THEY ARE NOT TO BE REPRODUCED IN WHOLE OR IN PART WITHOUT WRITTEN CONSENT FROM THE DESIGN WING
CONTRACTOR TO CHECK &VERIFY ALL DIMENSIONS BEFORE COMMENCING WORK & TO REPORT ANY DISCREPANCIES TO THE DESIGN WING.
DO NOT SCALE DRAWINGS.
ALL CONSTRUCTION TO BE ACCORDING TO BEST COMMON PRACTICE.

REV:	DESCRIPTION:	BY:	DATE:
A	ARCHITECTURE DRAWING	----	25-12-25
B	STRUCTURE DRAWING	----	27-12-25

PROJECT NAME:
300 SQ.YARD HOUSE ARCHITECTURE DRAWING

SIGNATURE BY:

DRAWING TITLE:
ARCHITECTURAL DRAWING

DRAWN BY: MUDASSIR
CHECKED BY: M.SHEHERYAR
APPROVED BY: M.SHEHERYAR
DATE: 27-DEC-2025

CLIENT
MR. ROHAN
KARACHI...

DESIGNED BY:-

E.D.C.O
ENGINEERING DESIGNING CONSTRUCTION OFFICIAL
ARCHITECT| PLANNERS| ENGINEERS| INTERIOR| B.O.Q| EXTERIOR| CONSULT| STRUCTURE DESIGN| PLANNING| LAND SURVEY| CONSTRUCTION| 3D ANIMATION VIDEO| RENOVATION|
MUHAMMAD SHEHERYAR
CONTACT- 0312-2118445|D.H.A PHASE VII

PROJECT NO: AR-7590
SCALE: 1/8"=1'-0"
SHEET SIZE: A3
DRAWING NO: ARC
SHEET NO ----------
REVISION: YES
UNIT: INCHES&FEET

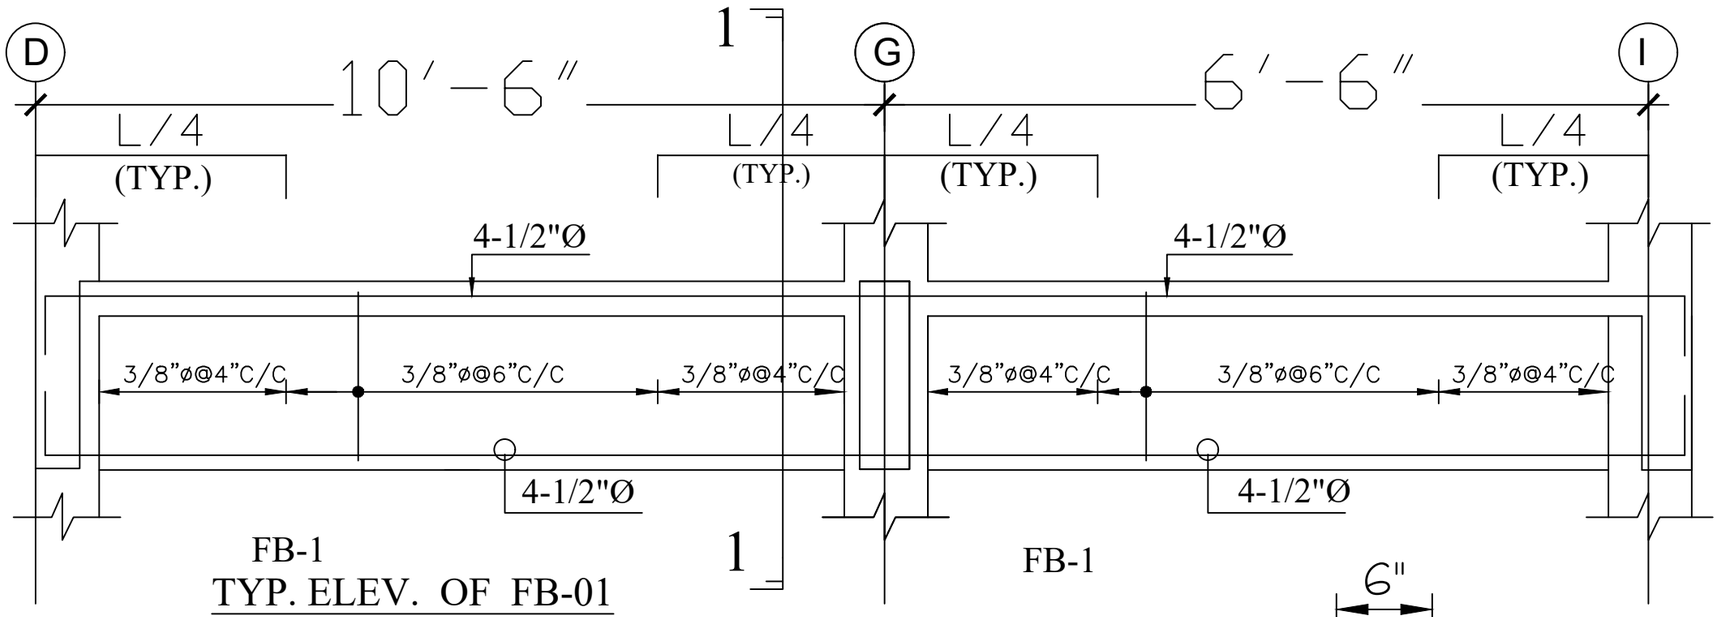

TYP. ELEV. OF FB-01

(ON GRID ' 24 ' SIZE = 6" X 30")

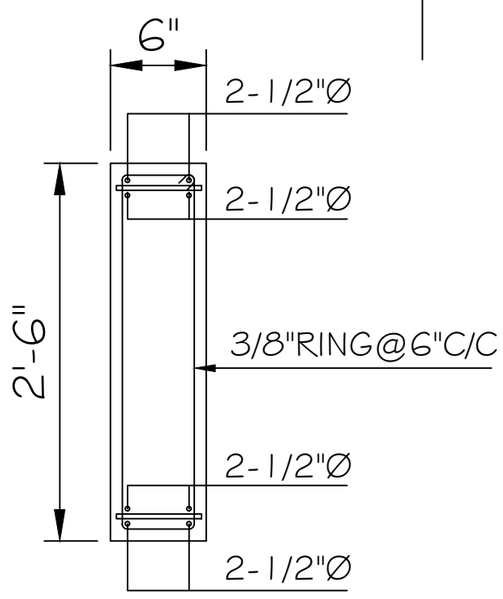

FB-1 (6″×30″)

SCALE 3/4″ = 1′-0″

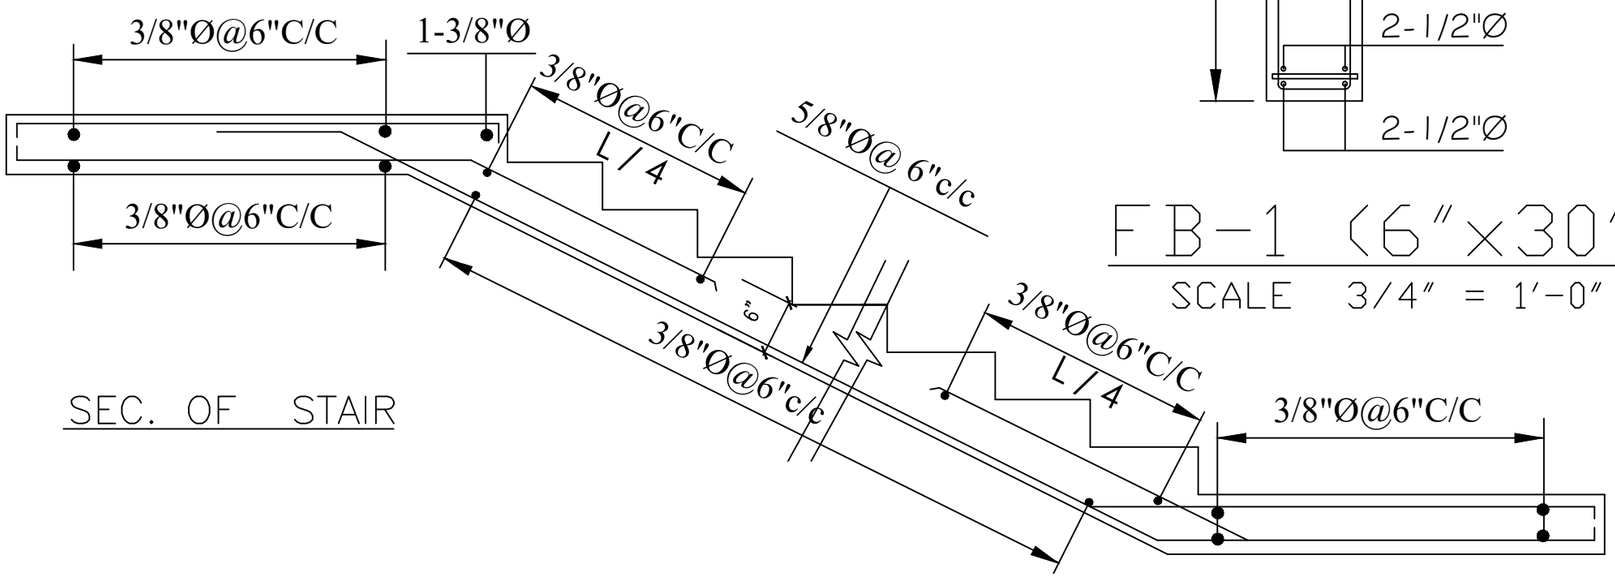

SEC. OF STAIR

SCHEDULE OF BEAM

MARKS	WIDTH	DEPTH	BOTTOM	TOP	EXTRA TOP	EXTRA BOT	RING
FB1	6"	30"	4-1/2"Ø	4-1/2"Ø	-	-	3/8"Ø@6" C/C

PLAN COLUMN L/4 4"@C/C REST @6"C/C

NOTES:-

01- ALL SLAB ARE 6" THICK UNLESS NOTED OTHER WISE.

02- FOR ALL LEVELS, GRIDS, DIMENSIONS ETC , REFER ARCH. DRGS.

03- PROVIDE 3/8" DIA @ 6" C/C DISTRIBUTION BARS NOTE SHOWN IN PLAN.

14 FIRST FLOOR FRAMING DETAIL

NOTES:-

1- 4000 PSI FOR RAFT / FOUNDATION.
2- 4000 PSI FOR COLUMN/ BEAM/ SLAB.
3- ALL LEVELS TO BE CO-ORDINATED WITH ARCH. DRAWING.
4- READY MIX CONCRETE TO BE USED.
5- RAFT /FOUNDATION THICKNESS ALSO SHOULD BE DEPEND ON SOIL CONDITION DURING EXCAVATION.

GENERAL NOTES:

1. THE COPYRIGHT OF THIS DRAWING IS VESTED IN YourSpreadsheets AND IT MAY NOT BE REPRODUCED IN WHOLE OR PART OR USED FOR THE MANUFACTURE OF ANY ARTICLE WITHOUT THE EXPRESS PERMISSION OF THE COPYRIGHT HOLDERS.
2. WORK TO FIGURED DIMENSIONS ONLY.
3. THIS DRAWING IS TO BE READ IN CONJUNCTION WITH ALL RELEVANT ARCHITECT'S, SERVICE ENGINEER'S AND YourSpreadsheets DRAWINGS .
ALL DRWAING ARE THE PROPOERTY OF THE DESIGNER & THEY ARE NOT TO BE REPRODUCED IN WHOLE OR IN PART WITHOUT WRITTEN CONSENT FROM THE DESIGN WING
CONTRACTOR TO CHECK &VERIFY ALL DIMENSIONS BEFORE COMMENCING WORK & TO REPORT ANY DISCREPANCIES TO THE DESIGN WING.
DO NOT SCALE DRAWINGS.
ALL CONSTRUCTION TO BE ACCORDING TO BEST COMMON PRACTICE.

REV:	DESCRIPTION:	BY:	DATE:
A	ARCHITECTURE DRAWING	----	25-12-25
B	STRUCTURE DRAWING	----	27-12-25

PROJECT NAME:
300 SQ.YARD HOUSE ARCHITECTURE DRAWING

SIGNATURE BY:

DRAWING TITLE:
ARCHITECTURAL DRAWING

DRAWN BY: MUDASSIR
CHECKED BY: M.SHEHERYAR
APPROVED BY: M.SHEHERYAR
DATE: 27-DEC-2025

CLIENT
MR. ROHAN
KARACHI...

DESIGNED BY:-
E.D.C.O
ENGINEERING DESIGNING CONSTRUCTION OFFICIAL
ARCHITECT| PLANNERS| ENGINEERS| INTERIOR| B.O.Q| EXTERIOR| CONSULT| STRUCTURE DESIGN| PLANNING| LAND SURVEY| CONSTRUCTION| 3D ANIMATION VIDEO| RENOVATION|
MUHAMMAD SHEHERYAR
CONTACT- 0312-2118445|D.H.A PHASE VII

PROJECT NO: AR-7590
SCALE: 1/8"=1'-0"
SHEET SIZE: A3
DRAWING NO: ARC
SHEET NO ----------
REVISION: YES
UNIT: INCHES&FEET

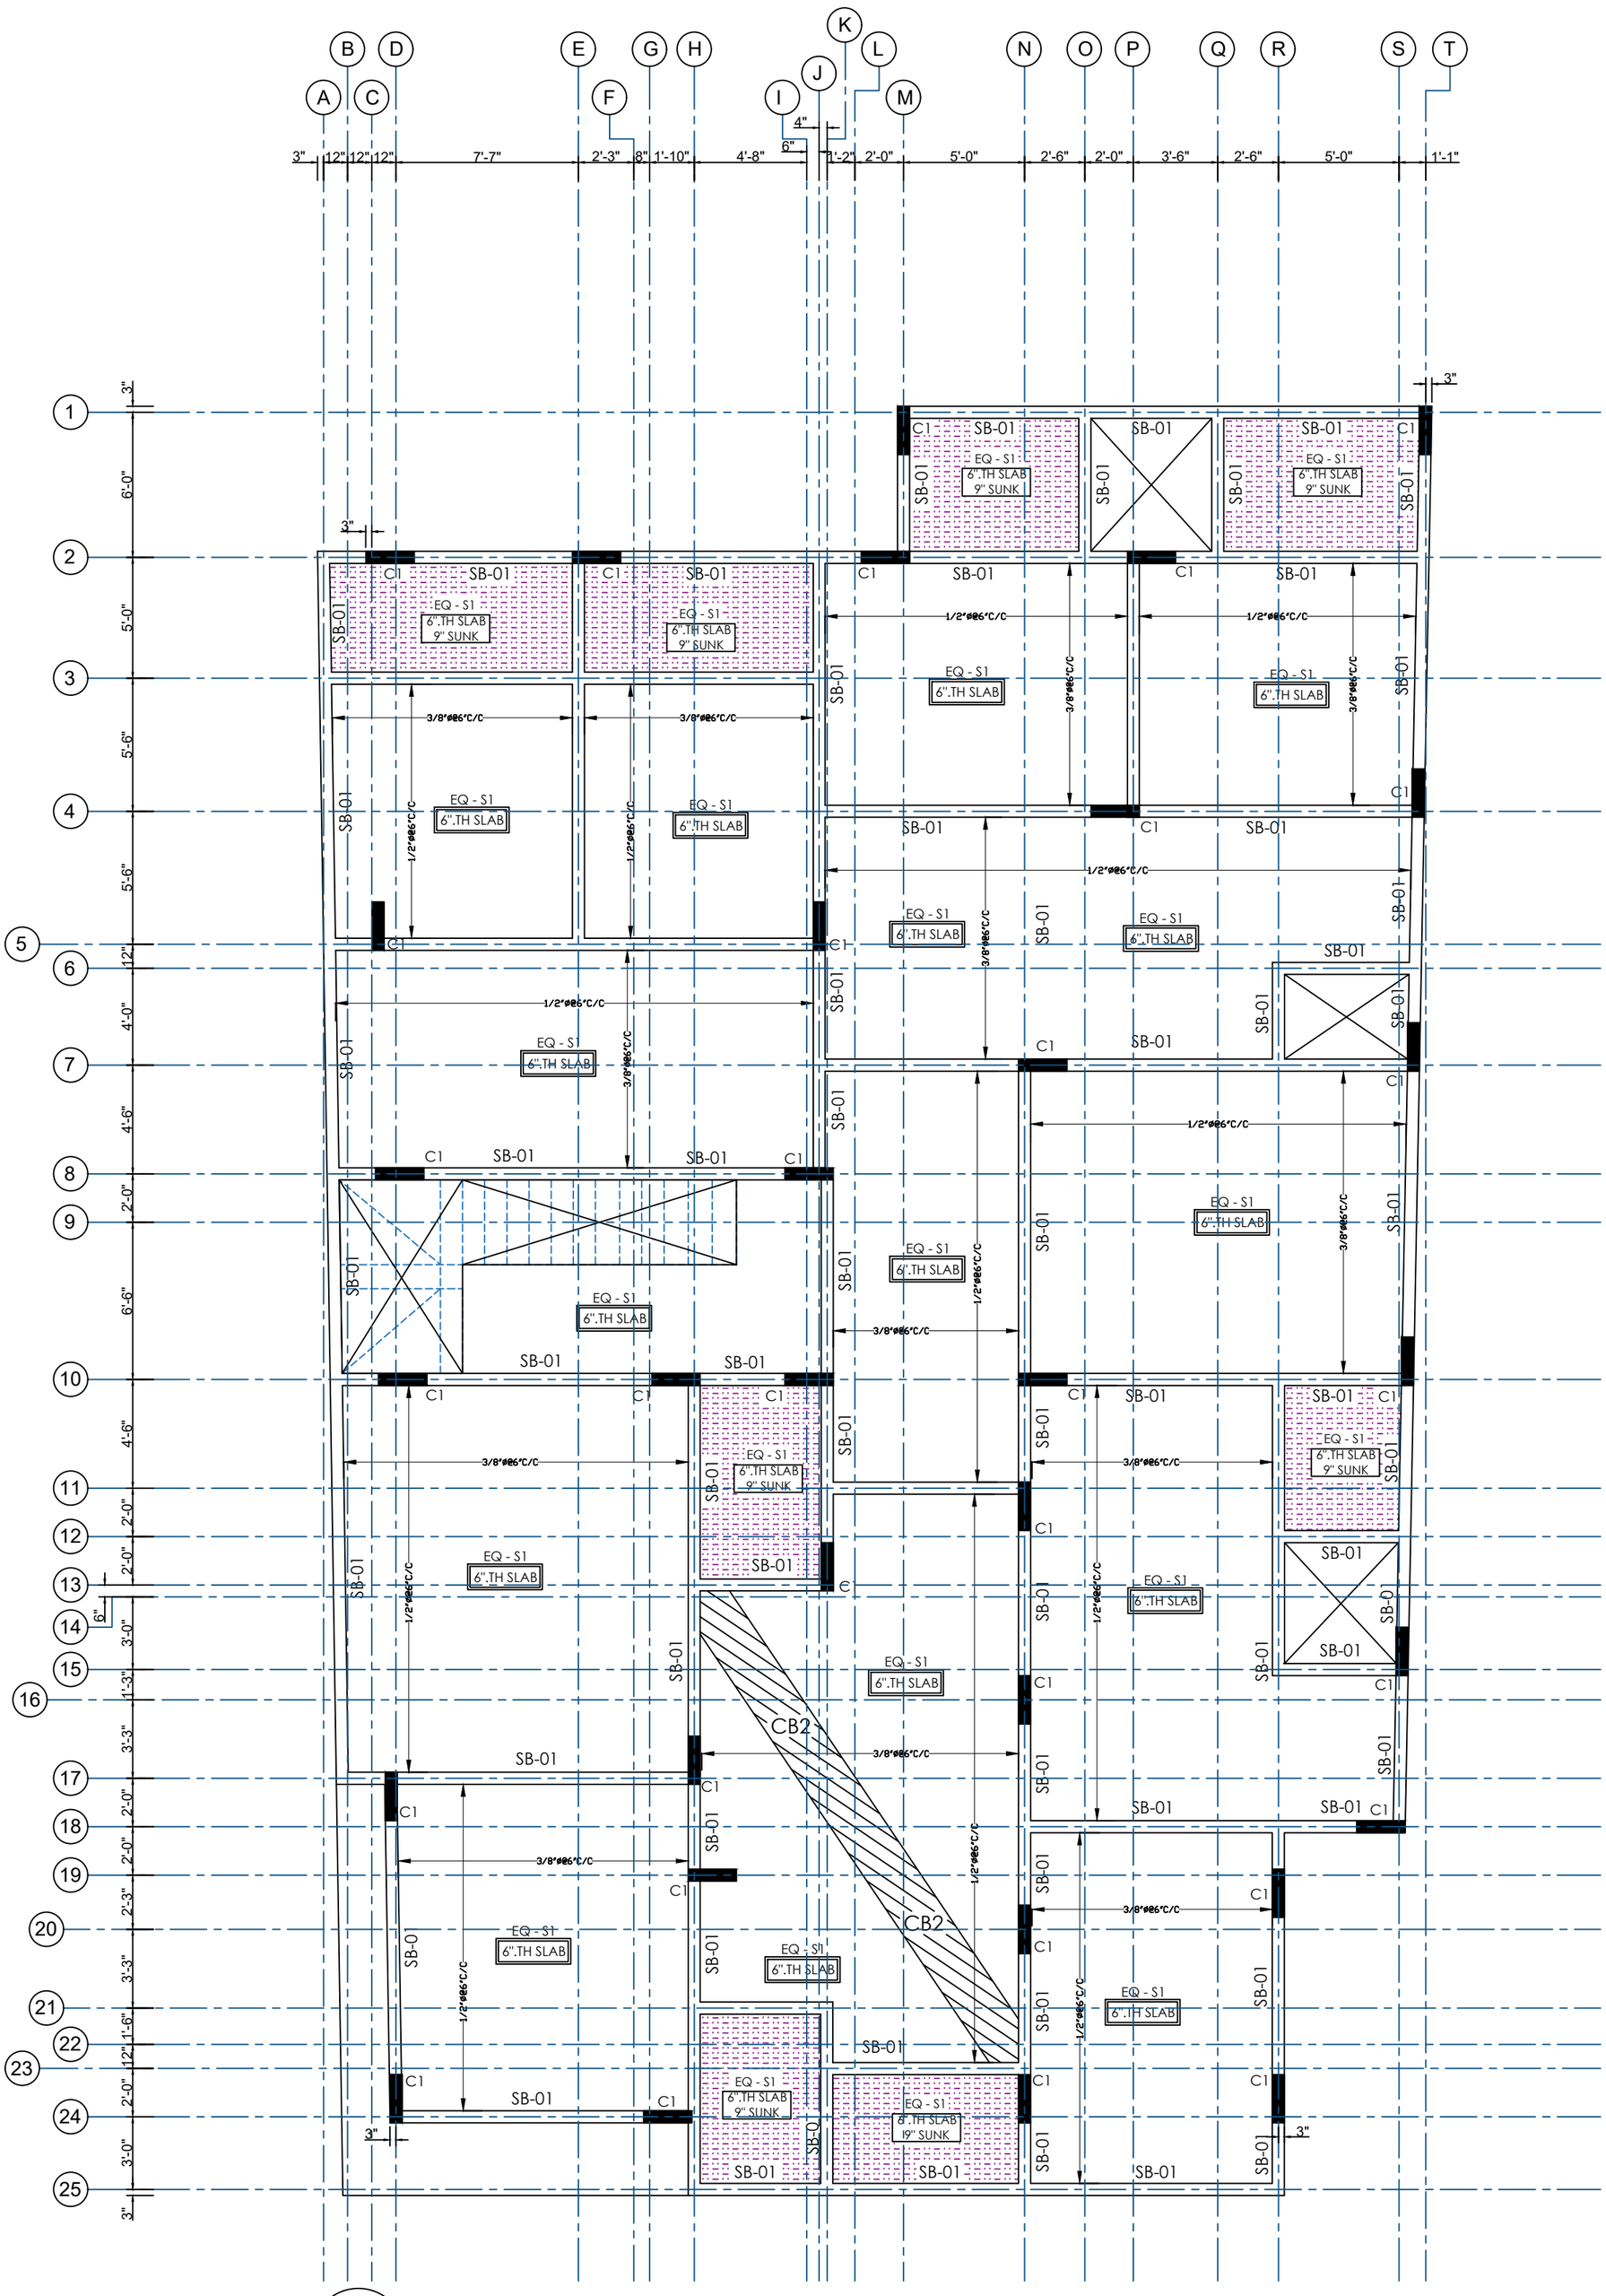

14 SECOND FLOOR FRAMING PLAN

NOTES:-

1- 4000 PSI FOR RAFT / FOUNDATION.
2- 4000 PSI FOR COLUMN/ BEAM/ SLAB.
3- ALL LEVELS TO BE CO-ORDINATED WITH ARCH. DRAWING.
4- READY MIX CONCRETE TO BE USED.
5- RAFT /FOUNDATION THICKNESS ALSO SHOULD BE DEPEND ON SOIL CONDITION DURING EXCAVATION.

GENERAL NOTES:

1. THE COPYRIGHT OF THIS DRAWING IS VESTED IN YourSpreadsheets AND IT MAY NOT BE REPRODUCED IN WHOLE OR PART OR USED FOR THE MANUFACTURE OF ANY ARTICLE WITHOUT THE EXPRESS PERMISSION OF THE COPYRIGHT HOLDERS.
2. WORK TO FIGURED DIMENSIONS ONLY.
3. THIS DRAWING IS TO BE READ IN CONJUNCTION WITH ALL RELEVANT ARCHITECT'S, SERVICE ENGINEER'S AND YourSpreadsheets DRAWINGS .
ALL DRWAING ARE THE PROPOERTY OF THE DESIGNER & THEY ARE NOT TO BE REPRODUCED IN WHOLE OR IN PART WITHOUT WRITTEN CONSENT FROM THE DESIGN WING
CONTRACTOR TO CHECK &VERIFY ALL DIMENSIONS BEFORE COMMENCING WORK & TO REPORT ANY DISCREPANCIES TO THE DESIGN WING.
DO NOT SCALE DRAWINGS.
ALL CONSTRUCTION TO BE ACCORDING TO BEST COMMON PRACTICE.

REV:	DESCRIPTION:	BY:	DATE:
A	ARCHITECTURE DRAWING	----	25-12-25
B	STRUCTURE DRAWING	----	27-12-25

PROJECT NAME:
300 SQ.YARD HOUSE ARCHITECTURE DRAWING

SIGNATURE BY:

DRAWING TITLE:
ARCHITECTURAL DRAWING

DRAWN BY: MUDASSIR
CHECKED BY: M.SHEHERYAR
APPROVED BY: M.SHEHERYAR
DATE: 27-DEC-2025

CLIENT
MR. ROHAN
KARACHI...

DESIGNED BY:-

E.D.C.O
ENGINEERING DESIGNING CONSTRUCTION OFFICIAL
ARCHITECT| PLANNERS| ENGINEERS| INTERIOR| B.O.Q| EXTERIOR| CONSULT| STRUCTURE DESIGN| PLANNING| LAND SURVEY| CONSTRUCTION| 3D ANIMATION VIDEO| RENOVATION|
MUHAMMAD SHEHERYAR
CONTACT- 0312-2118445|D.H.A PHASE VII

PROJECT NO: AR-7590
SCALE: 1/8"=1'-0"
SHEET SIZE: A3
DRAWING NO: ARC
SHEET NO: ----------
REVISION: YES
UNIT: INCHES&FEET

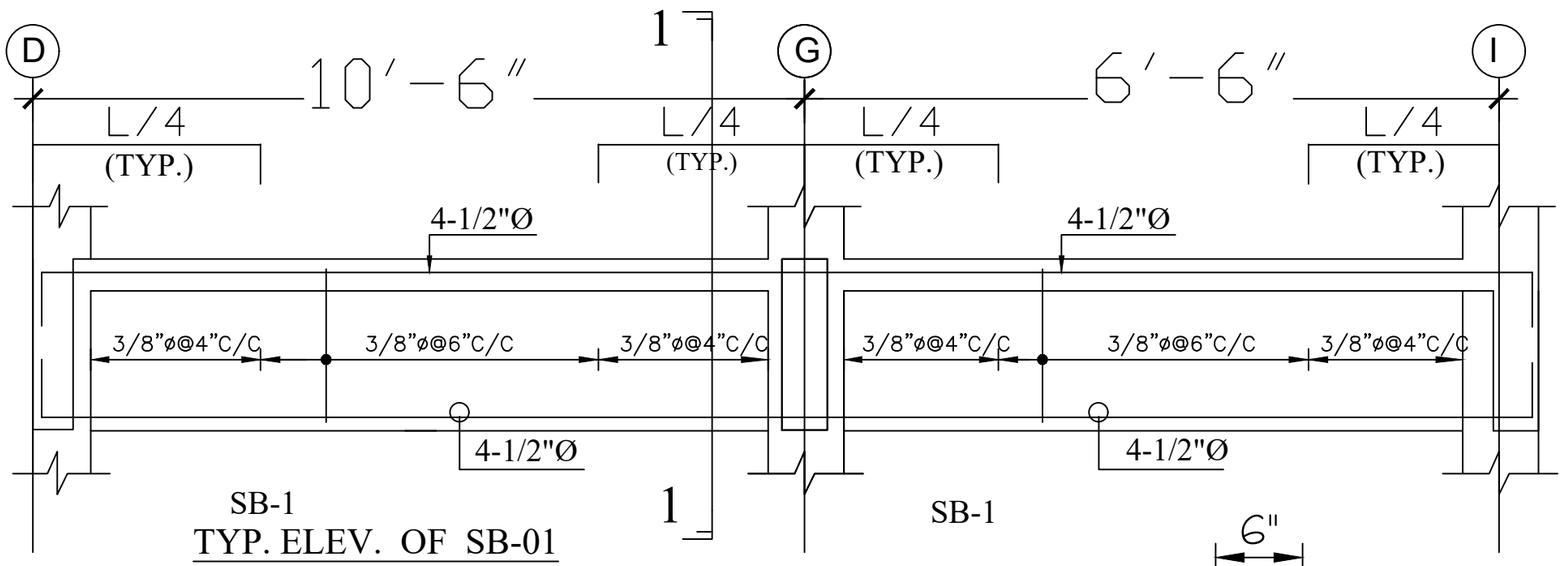

TYP. ELEV. OF SB-01

(ON GRID ' 24 ' SIZE = 6" X 30")

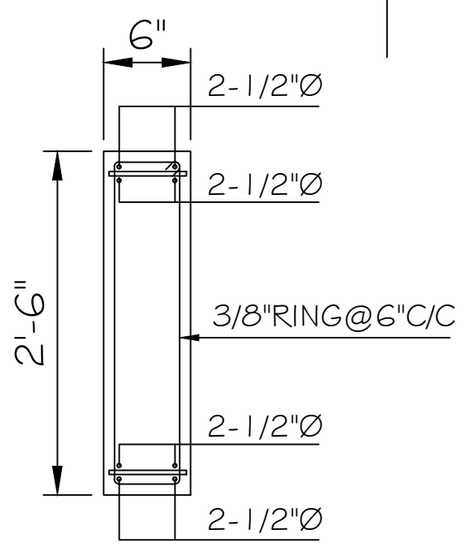

SB-1 (6″×30″)

SCALE 3/4″ = 1′-0″

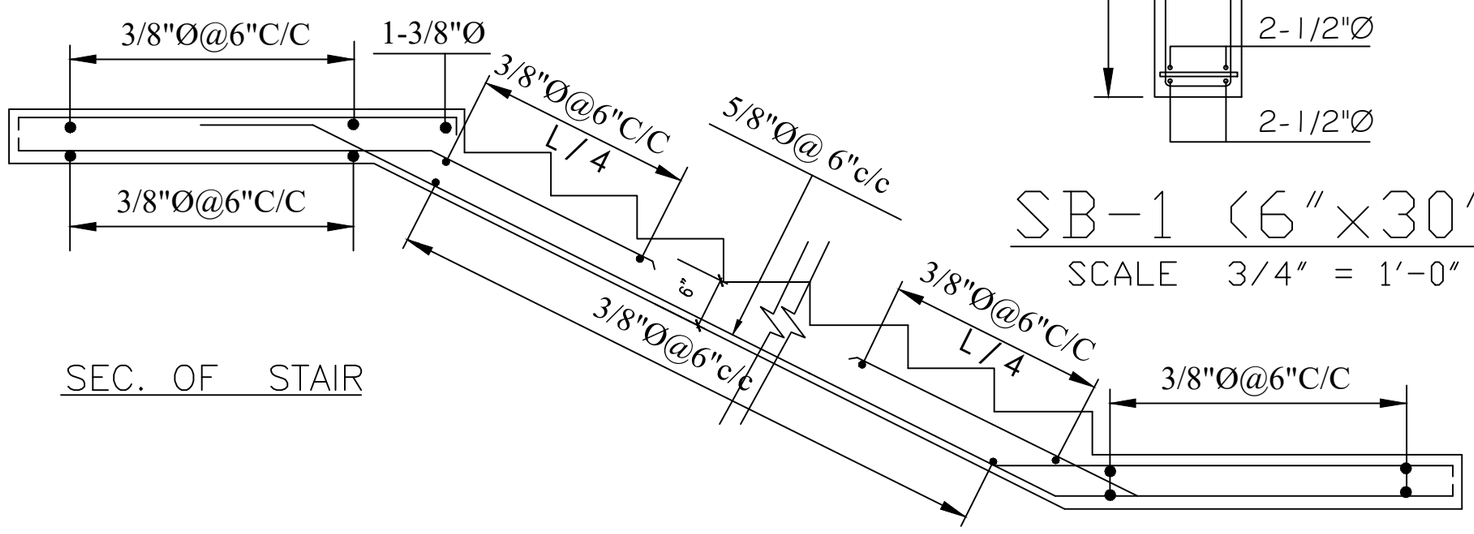

SEC. OF STAIR

SCHEDULE OF BEAM							
MARKS	**WIDTH**	**DEPTH**	**BOTTOM**	**TOP**	**EXTRA TOP**	**EXTRA BOT**	**RING**
SB1	**6"**	**30"**	**4-1/2"Ø**	**4-1/2"Ø**	**-**	**-**	**3/8"Ø@6" C/C**

PLAN COLUMN L/4 4"@C/C REST @6"C/C

NOTES:-
01- ALL SLAB ARE 6" THICK UNLESS NOTED OTHER WISE.
02- FOR ALL LEVELS, GRIDS, DIMENSIONS ETC , REFER ARCH. DRGS.
03- PROVIDE 3/8" DIA @ 6" C/C DISTRIBUTION BARS NOTE SHOWN IN PLAN.

14 SECOND FLOOR FRAMING DETAIL

NOTES:-

1- 4000 PSI FOR RAFT / FOUNDATION.
2- 4000 PSI FOR COLUMN/ BEAM/ SLAB.
3- ALL LEVELS TO BE CO-ORDINATED WITH ARCH. DRAWING.
4- READY MIX CONCRETE TO BE USED.
5- RAFT /FOUNDATION THICKNESS ALSO SHOULD BE DEPEND ON SOIL CONDITION DURING EXCAVATION.

GENERAL NOTES:

1. THE COPYRIGHT OF THIS DRAWING IS VESTED IN YourSpreadsheets AND IT MAY NOT BE REPRODUCED IN WHOLE OR PART OR USED FOR THE MANUFACTURE OF ANY ARTICLE WITHOUT THE EXPRESS PERMISSION OF THE COPYRIGHT HOLDERS.
2. WORK TO FIGURED DIMENSIONS ONLY.
3. THIS DRAWING IS TO BE READ IN CONJUNCTION WITH ALL RELEVANT ARCHITECT'S, SERVICE ENGINEER'S AND YourSpreadsheets DRAWINGS .
ALL DRWAING ARE THE PROPOERTY OF THE DESIGNER & THEY ARE NOT TO BE REPRODUCED IN WHOLE OR IN PART WITHOUT WRITTEN CONSENT FROM THE DESIGN WING
CONTRACTOR TO CHECK &VERIFY ALL DIMENSIONS BEFORE COMMENCING WORK & TO REPORT ANY DISCREPANCIES TO THE DESIGN WING.
DO NOT SCALE DRAWINGS.
ALL CONSTRUCTION TO BE ACCORDING TO BEST COMMON PRACTICE.

REV:	DESCRIPTION:	BY:	DATE:
A	ARCHITECTURE DRAWING	----	25-12-25
B	STRUCTURE DRAWING	----	27-12-25

PROJECT NAME:
300 SQ.YARD HOUSE
ARCHITECTURE DRAWING

SIGNATURE BY:

DRAWING TITLE:
ARCHITECTURAL DRAWING

DRAWN BY: MUDASSIR
CHECKED BY: M.SHEHERYAR
APPROVED BY: M.SHEHERYAR
DATE: 27-DEC-2025

CLIENT
MR. ROHAN
KARACHI...

DESIGNED BY:-
E.D.C.O
ENGINEERING DESIGNING CONSTRUCTION OFFICIAL
ARCHITECT| PLANNERS| ENGINEERS| INTERIOR| B.O.Q| EXTERIOR| CONSULT| STRUCTURE DESIGN| PLANNING| LAND SURVEY| CONSTRUCTION| 3D ANIMATION VIDEO| RENOVATION|
MUHAMMAD SHEHERYAR
CONTACT- 0312-2118445|D.H.A PHASE VII

PROJECT NO: AR-7590
SCALE: 1/8"=1'-0"
SHEET SIZE: A3
DRAWING NO: ARC
SHEET NO ----------
REVISION: YES
UNIT: INCHES&FEET

GENERAL NOTES:

1. THE COPYRIGHT OF THIS DRAWING IS VESTED IN YourSpreadsheets AND IT MAY NOT BE REPRODUCED IN WHOLE OR PART OR USED FOR THE MANUFACTURE OF ANY ARTICLE WITHOUT THE EXPRESS PERMISSION OF THE COPYRIGHT HOLDERS.
2. WORK TO FIGURED DIMENSIONS ONLY.
3. THIS DRAWING IS TO BE READ IN CONJUNCTION WITH ALL RELEVANT ARCHITECT'S, SERVICE ENGINEER'S AND YourSpreadsheets DRAWINGS .

ALL DRWAING ARE THE PROPOERTY OF THE DESIGNER & THEY ARE NOT TO BE REPRODUCED IN WHOLE OR IN PART WITHOUT WRITTEN CONSENT FROM THE DESIGN WING
CONTRACTOR TO CHECK &VERIFY ALL DIMENSIONS BEFORE COMMENCING WORK & TO REPORT ANY DISCREPANCIES TO THE DESIGN WING.
DO NOT SCALE DRAWINGS.
ALL CONSTRUCTION TO BE ACCORDING TO BEST COMMON PRACTICE.

REV:	DESCRIPTION:	BY:	DATE:
A	ARCHITECTURE DRAWING	----	25-12-25
B	STRUCTURE DRAWING	----	27-12-25

ELECTRICAL

LAYOUT

DRAWING

PROJECT NAME:
300 SQ.YARD HOUSE ARCHITECTURE DRAWING

SIGNATURE BY:

DRAWING TITLE:
ARCHITECTURAL DRAWING

DRAWN BY: MUDASSIR

CHECKED BY: M.SHEHERYAR

APPROVED BY: M.SHEHERYAR

DATE: 27-DEC-2025

CLIENT
MR. ROHAN
KARACHI...

DESIGNED BY:-

E.D.C.O
ENGINEERING DESIGNING CONSTRUCTION OFFICIAL
ARCHITECT| PLANNERS| ENGINEERS| INTERIOR| B.O.Q| EXTERIOR| CONSULT| STRUCTURE DESIGN| PLANNING| LAND SURVEY| CONSTRUCTION| 3D ANIMATION VIDEO| RENOVATION|
MUHAMMAD SHEHERYAR
CONTACT- 0312-2118445|D.H.A PHASE VII

PROJECT NO: AR-7590

SCALE: 1/8"=1'-0"

SHEET SIZE: A3

DRAWING NO: ARC

SHEET NO ----------

REVISION: YES

UNIT: INCHES&FEET

S E W N

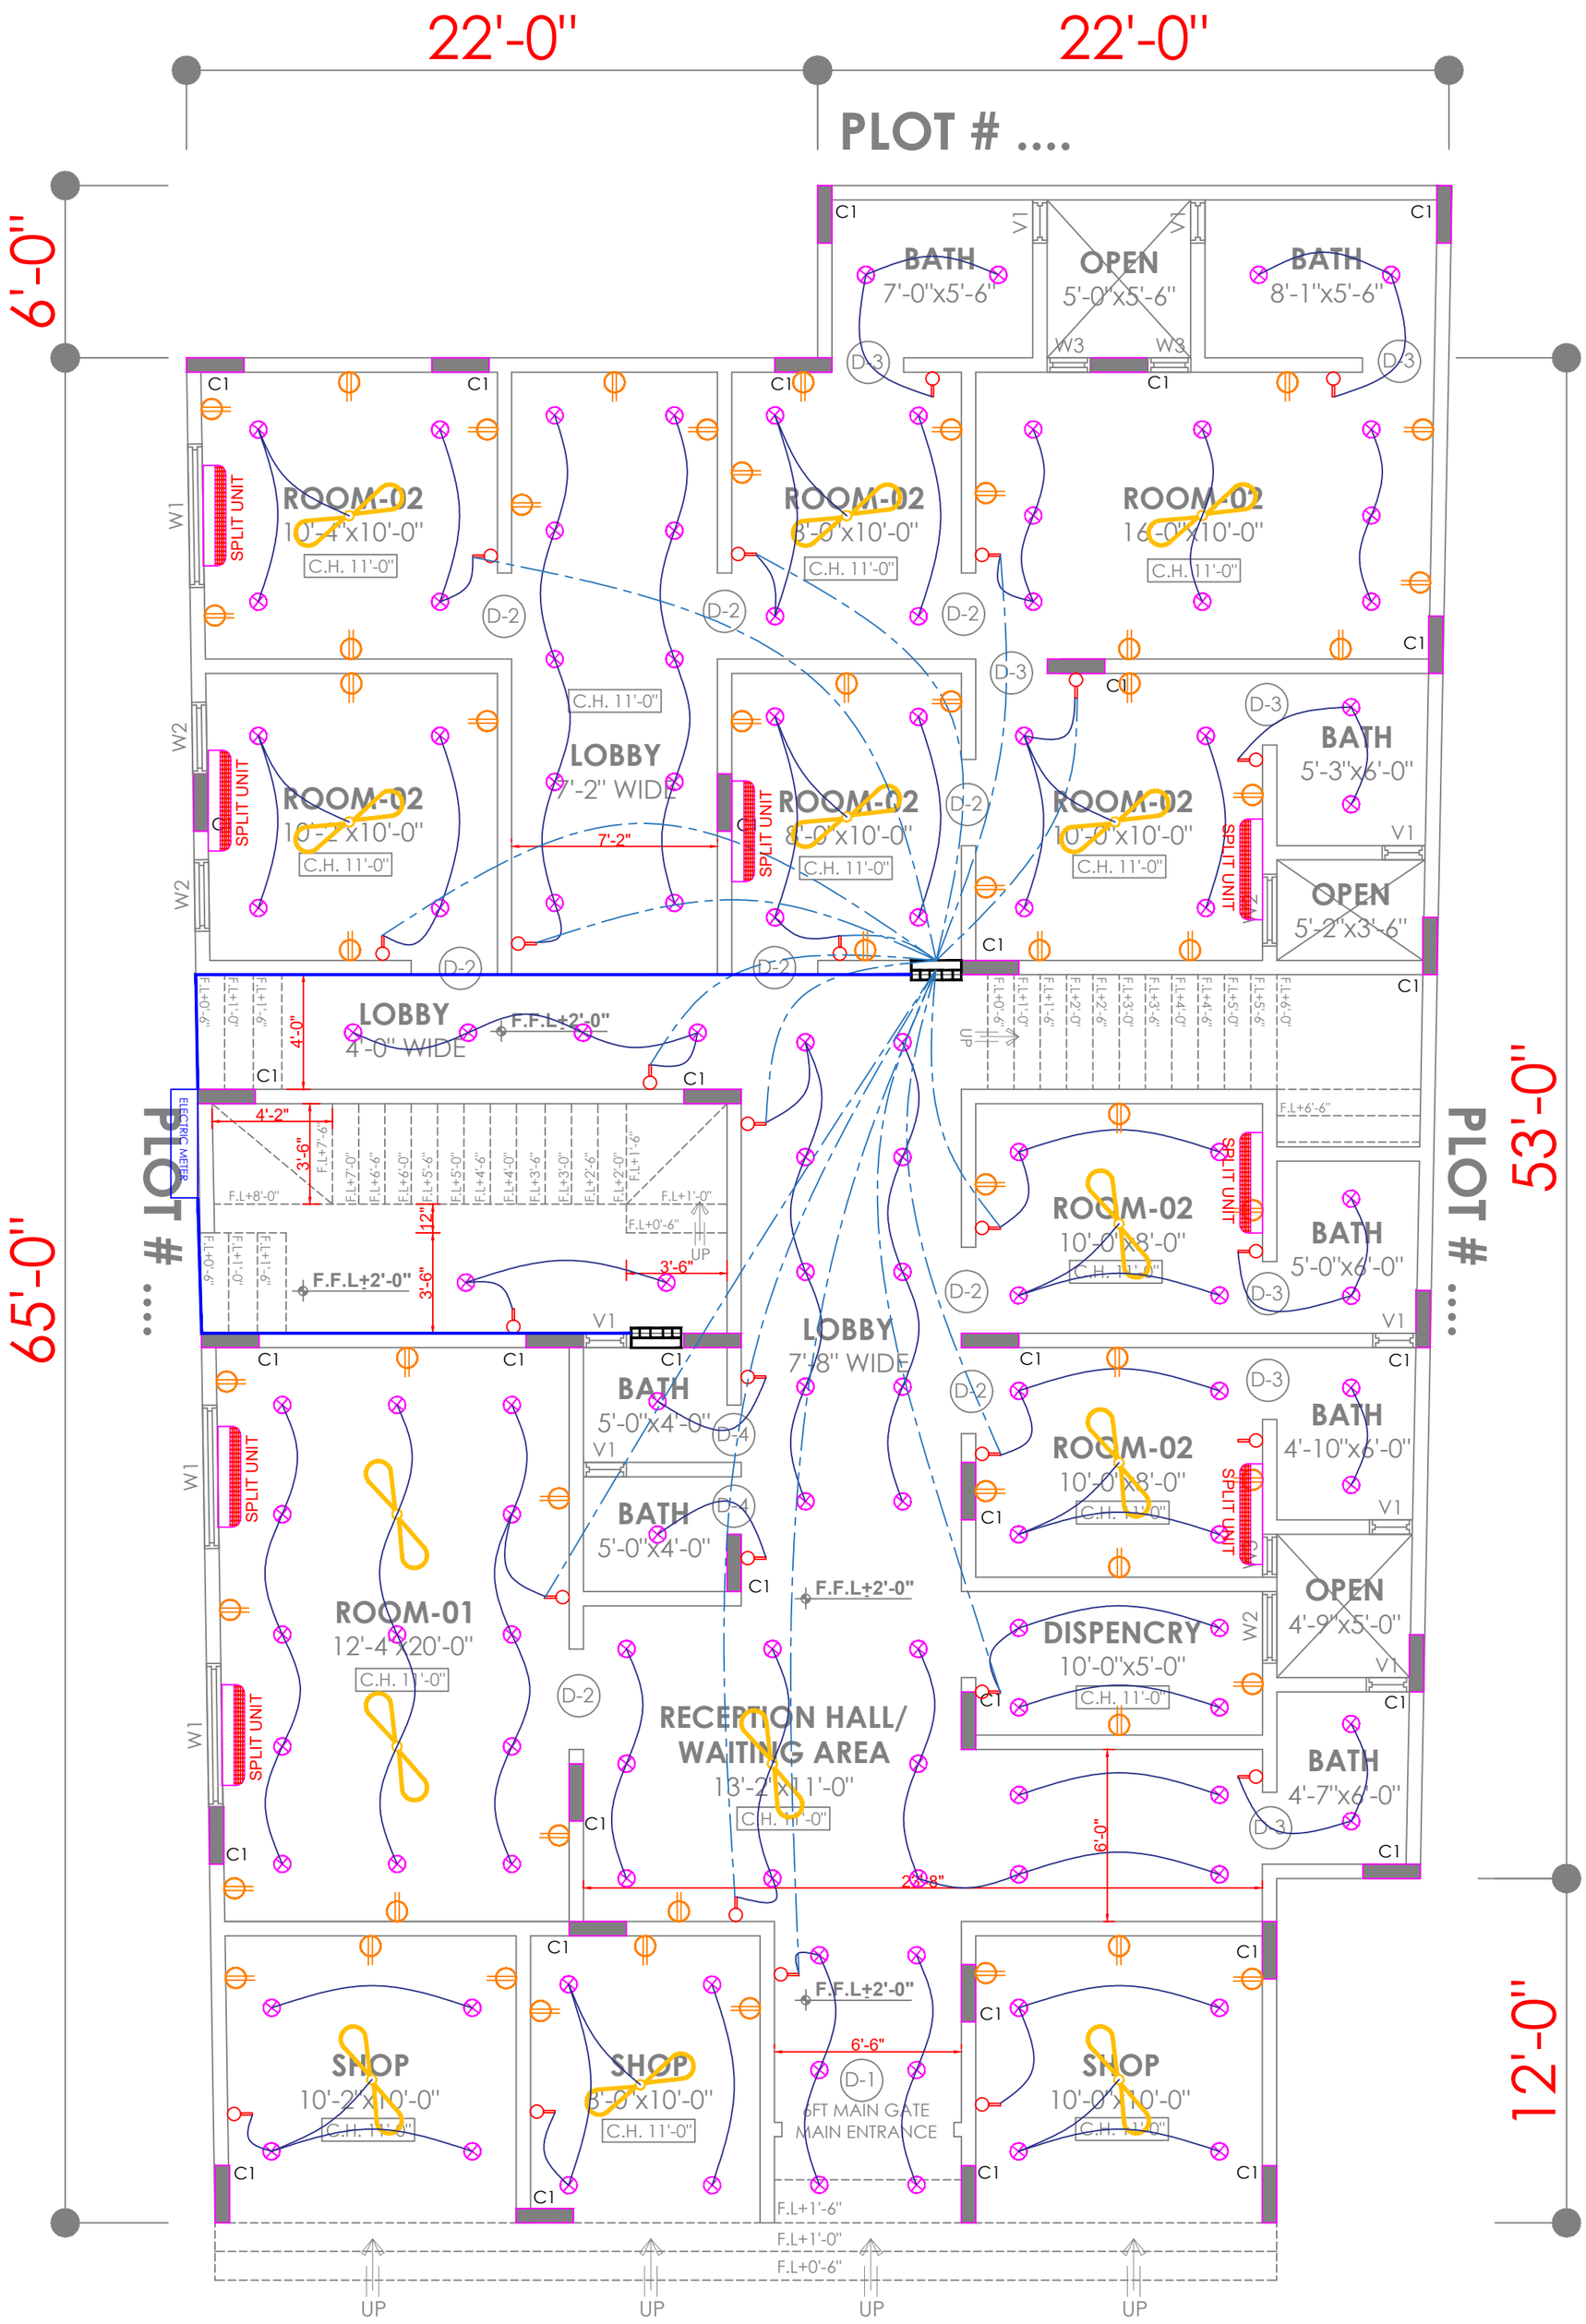

1 GROUND FLOOR PLAN
AR-01

GENERAL NOTES:

1. THE COPYRIGHT OF THIS DRAWING IS VESTED IN YourSpreadsheets AND IT MAY NOT BE REPRODUCED IN WHOLE OR PART OR USED FOR THE MANUFACTURE OF ANY ARTICLE WITHOUT THE EXPRESS PERMISSION OF THE COPYRIGHT HOLDERS.
2. WORK TO FIGURED DIMENSIONS ONLY.
3. THIS DRAWING IS TO BE READ IN CONJUNCTION WITH ALL RELEVANT ARCHITECT'S, SERVICE ENGINEER'S AND YourSpreadsheets DRAWINGS .

ALL DRWAING ARE THE PROPOERTY OF THE DESIGNER & THEY ARE NOT TO BE REPRODUCED IN WHOLE OR IN PART WITHOUT WRITTEN CONSENT FROM THE DESIGN WING
CONTRACTOR TO CHECK &VERIFY ALL DIMENSIONS BEFORE COMMENCING WORK & TO REPORT ANY DISCREPANCIES TO THE DESIGN WING.
DO NOT SCALE DRAWINGS.
ALL CONSTRUCTION TO BE ACCORDING TO BEST COMMON PRACTICE.

REV:	DESCRIPTION:	BY:	DATE:
A	ARCHITECTURE DRAWING	----	25-12-25
B	STRUCTURE DRAWING	----	27-12-25

PROJECT NAME:
300 SQ.YARD HOUSE ARCHITECTURE DRAWING

SIGNATURE BY:

DRAWING TITLE:
ARCHITECTURAL DRAWING

DRAWN BY: MUDASSIR
CHECKED BY: M.SHEHERYAR
APPROVED BY: M.SHEHERYAR
DATE: 27-DEC-2025

CLIENT
MR. ROHAN
KARACHI...

DESIGNED BY:-

E.D.C.O
ENGINEERING DESIGNING CONSTRUCTION OFFICIAL
ARCHITECT| PLANNERS| ENGINEERS| INTERIOR| B.O.Q| EXTERIOR| CONSULT| STRUCTURE DESIGN| PLANNING| LAND SURVEY| CONSTRUCTION| 3D ANIMATION VIDEO| RENOVATION|
MUHAMMAD SHEHERYAR
CONTACT- 0312-2118445|D.H.A PHASE VII

PROJECT NO: AR-7590
SCALE: 1/8"=1'-0"
SHEET SIZE: A3
DRAWING NO: ARC
SHEET NO ----------
REVISION: YES
UNIT: INCHES&FEET

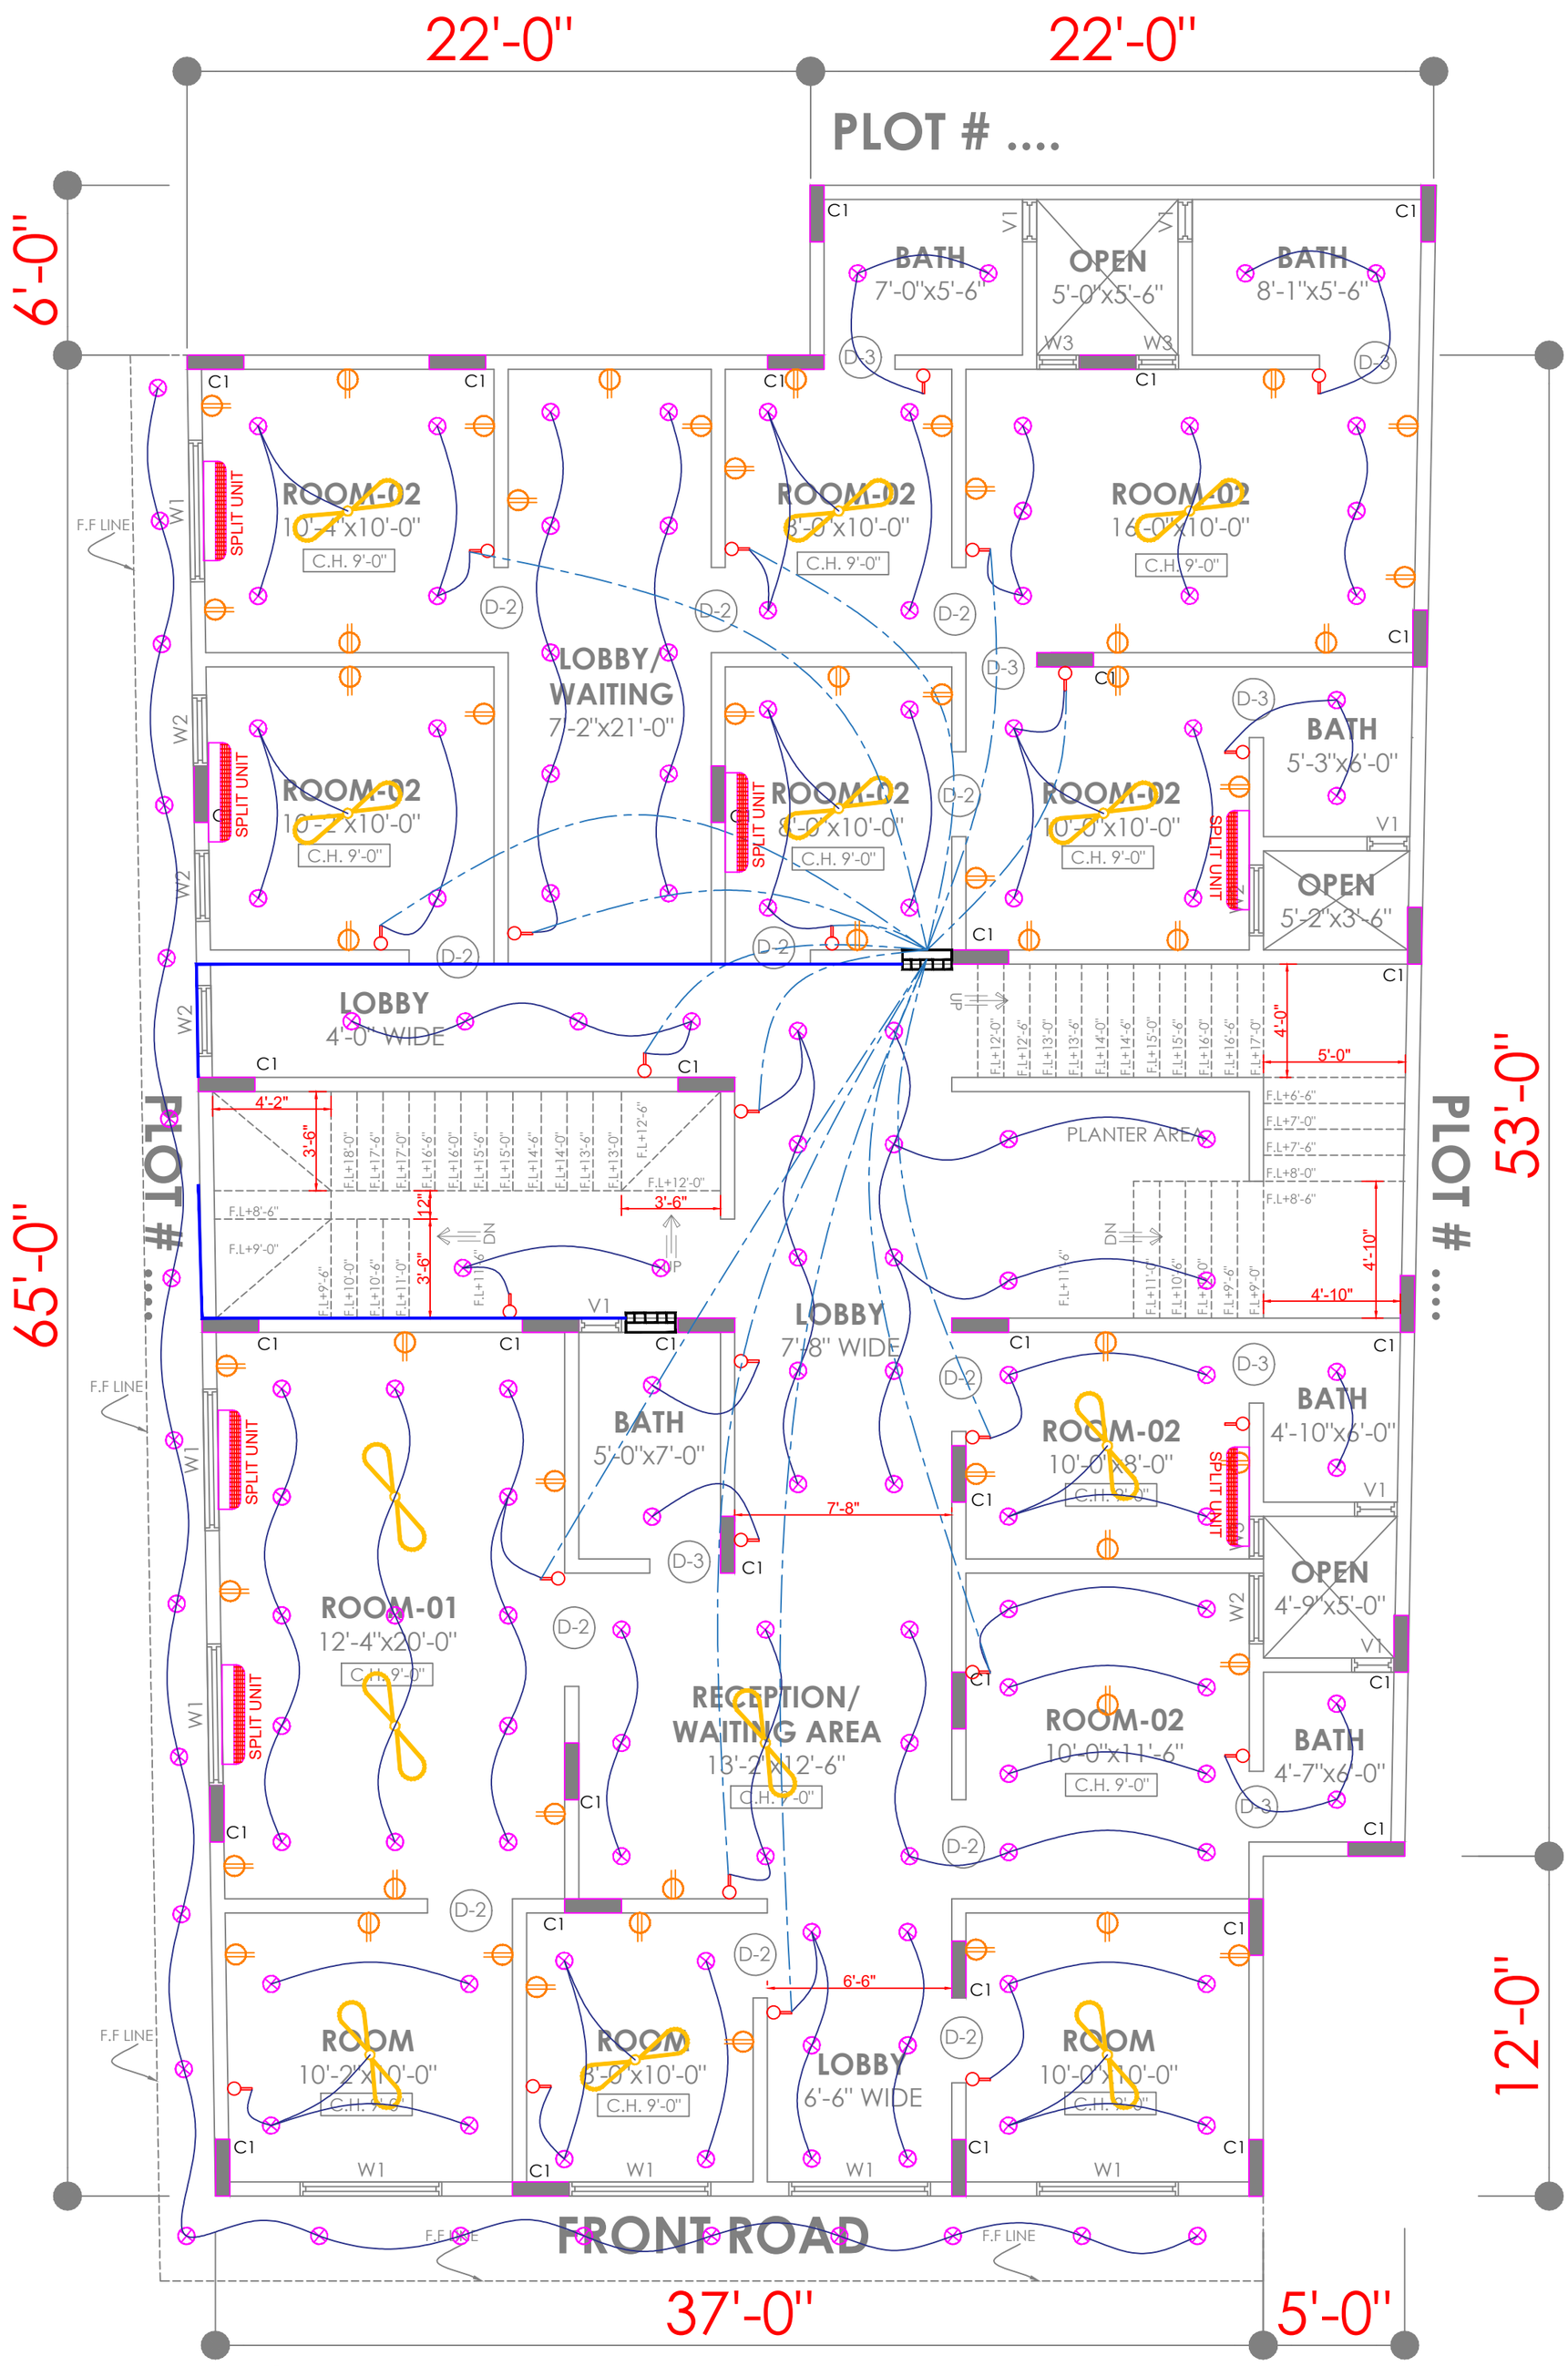

2 MEZZANINE FLOOR PLAN
AR-02

GENERAL NOTES:

1. THE COPYRIGHT OF THIS DRAWING IS VESTED IN YourSpreadsheets AND IT MAY NOT BE REPRODUCED IN WHOLE OR PART OR USED FOR THE MANUFACTURE OF ANY ARTICLE WITHOUT THE EXPRESS PERMISSION OF THE COPYRIGHT HOLDERS.
2. WORK TO FIGURED DIMENSIONS ONLY.
3. THIS DRAWING IS TO BE READ IN CONJUNCTION WITH ALL RELEVANT ARCHITECT'S, SERVICE ENGINEER'S AND YourSpreadsheets DRAWINGS .
ALL DRWAING ARE THE PROPOERTY OF THE DESIGNER & THEY ARE NOT TO BE REPRODUCED IN WHOLE OR IN PART WITHOUT WRITTEN CONSENT FROM THE DESIGN WING
CONTRACTOR TO CHECK &VERIFY ALL DIMENSIONS BEFORE COMMENCING WORK & TO REPORT ANY DISCREPANCIES TO THE DESIGN WING.
DO NOT SCALE DRAWINGS.
ALL CONSTRUCTION TO BE ACCORDING TO BEST COMMON PRACTICE.

REV:	DESCRIPTION:	BY:	DATE:
A	ARCHITECTURE DRAWING	----	25-12-25
B	STRUCTURE DRAWING	----	27-12-25

PROJECT NAME:
300 SQ.YARD HOUSE ARCHITECTURE DRAWING

SIGNATURE BY:

DRAWING TITLE:
ARCHITECTURAL DRAWING

DRAWN BY: MUDASSIR
CHECKED BY: M.SHEHERYAR
APPROVED BY: M.SHEHERYAR
DATE: 27-DEC-2025

CLIENT
MR. ROHAN
KARACHI...

DESIGNED BY:-

E.D.C.O
ENGINEERING DESIGNING CONSTRUCTION OFFICIAL
ARCHITECT| PLANNERS| ENGINEERS| INTERIOR| B.O.Q| EXTERIOR| CONSULT| STRUCTURE DESIGN| PLANNING| LAND SURVEY| CONSTRUCTION| 3D ANIMATION VIDEO| RENOVATION|
MUHAMMAD SHEHERYAR
CONTACT- 0312-2118445|D.H.A PHASE VII

PROJECT NO: AR-7590
SCALE: 1/8"=1'-0"
SHEET SIZE: A3
DRAWING NO: ARC
SHEET NO ----------
REVISION: YES
UNIT: INCHES&FEET

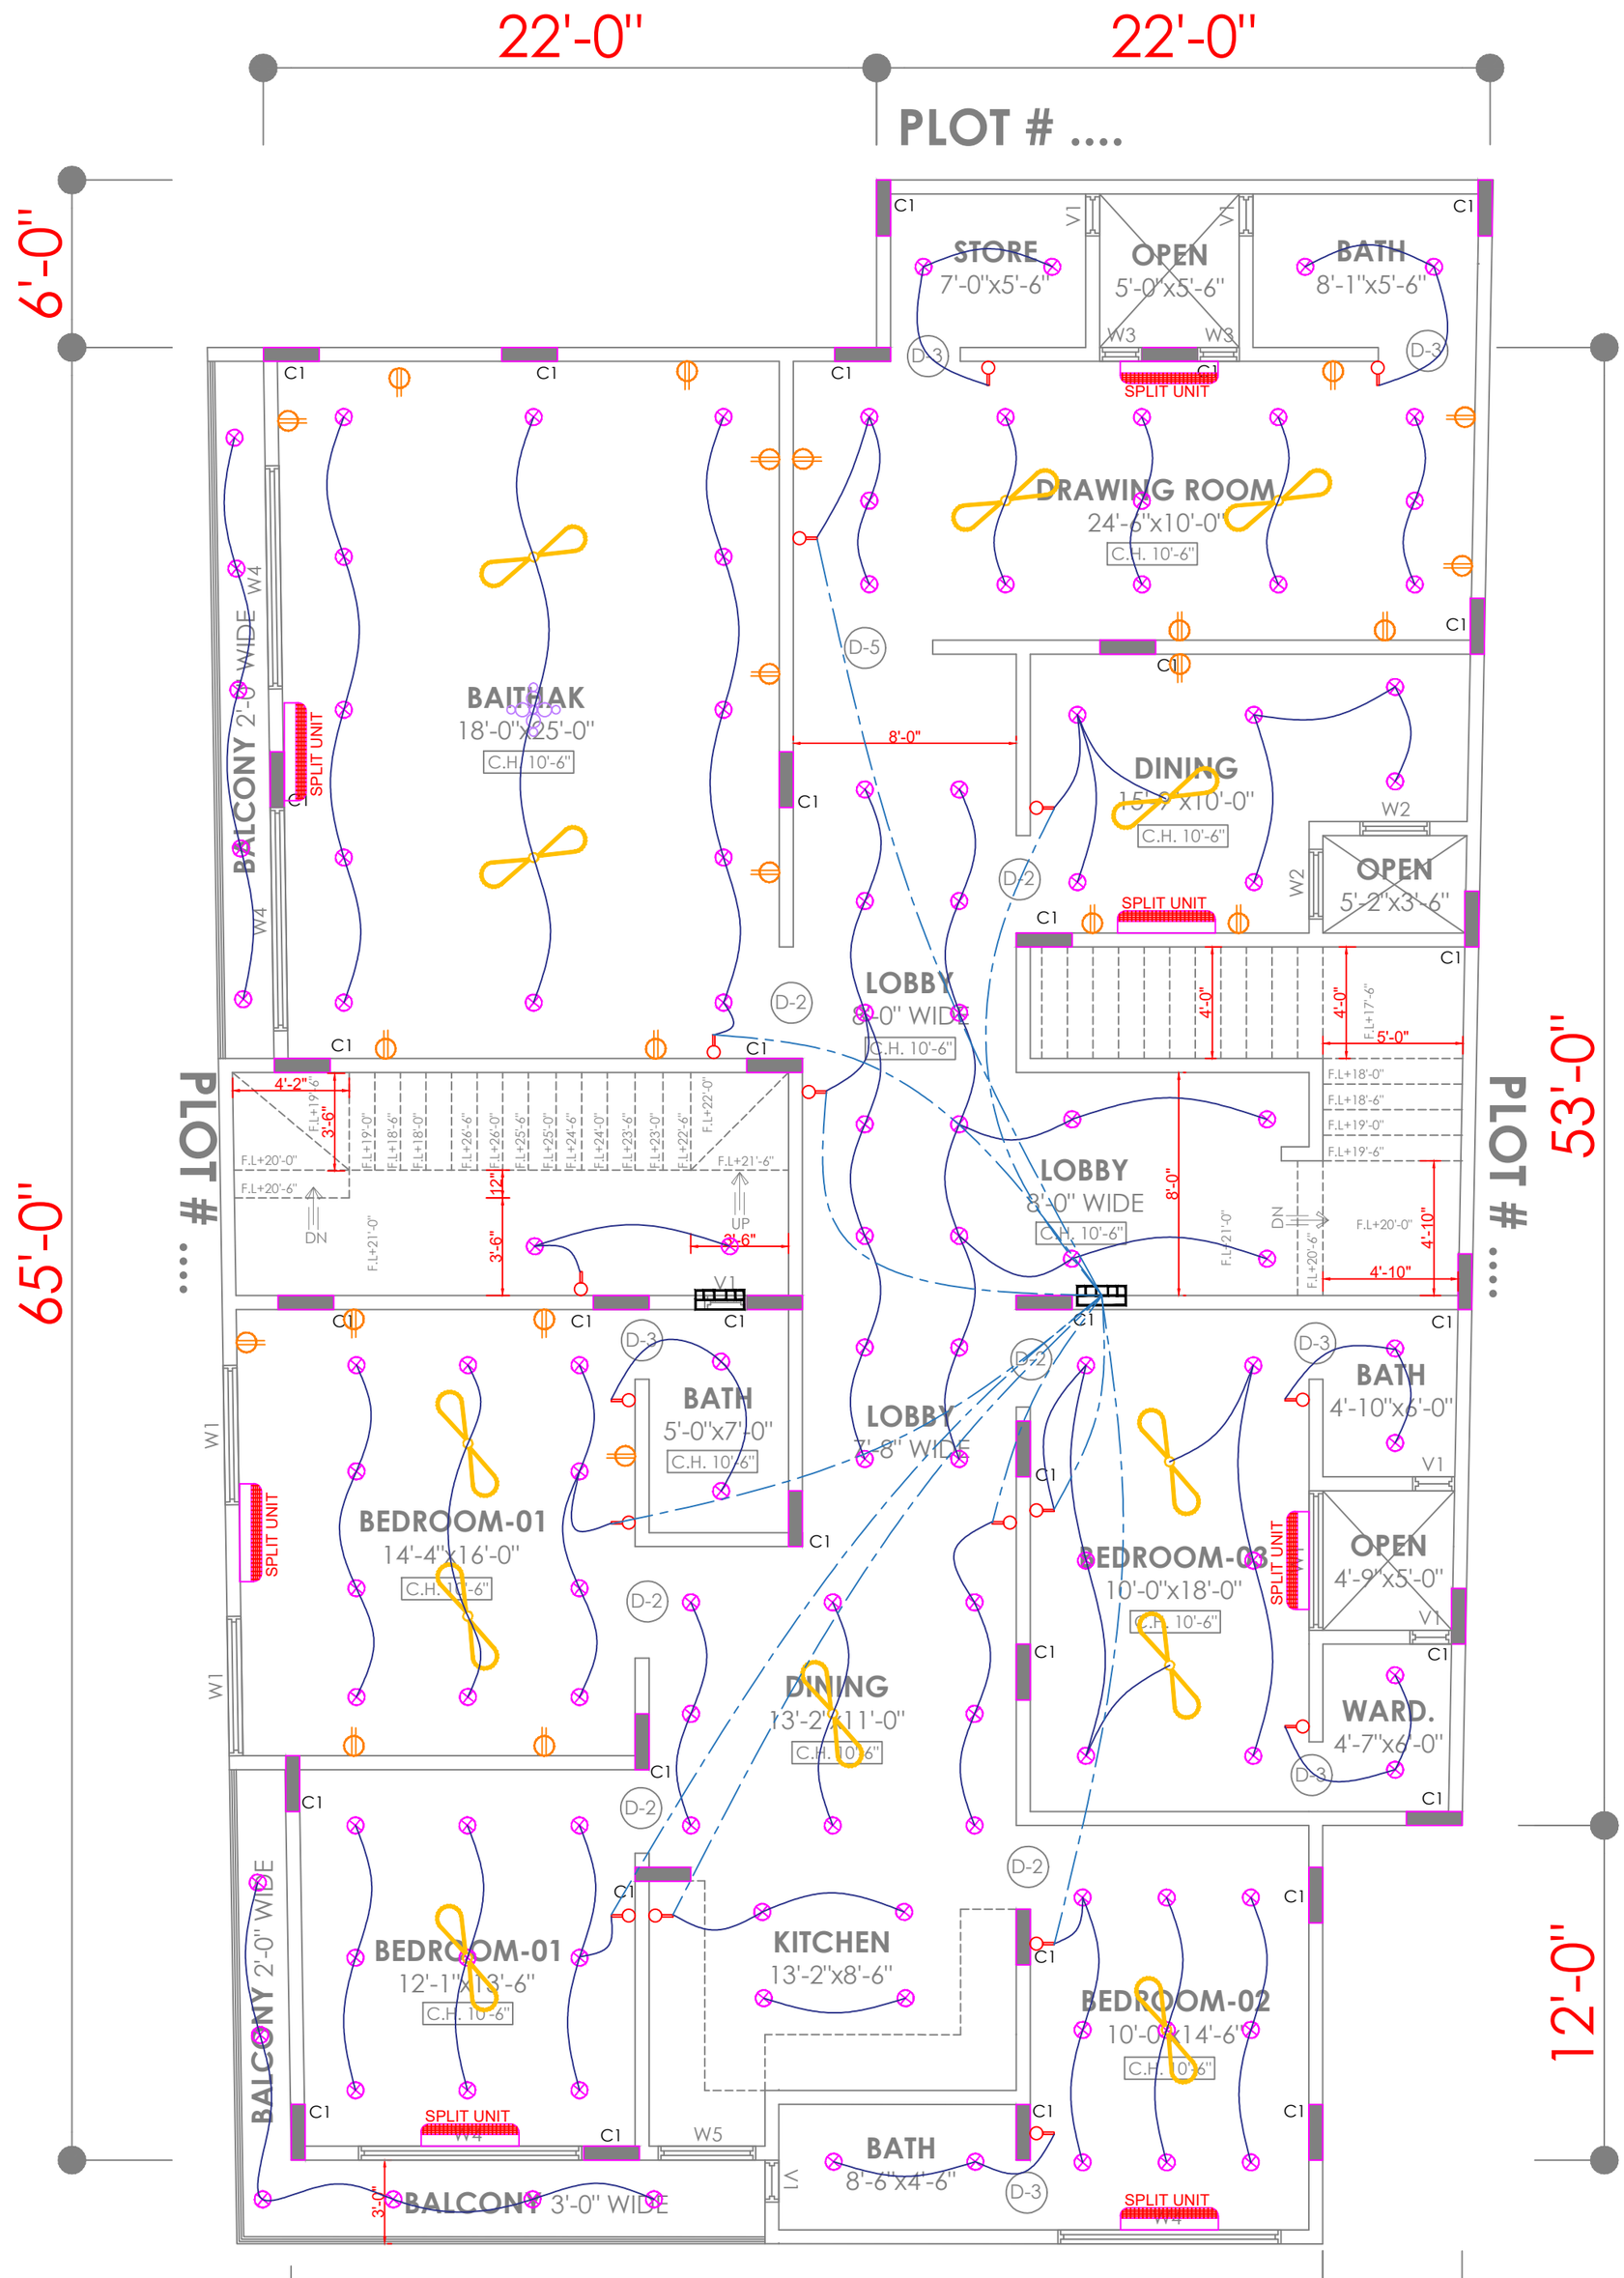

3 FIRST FLOOR PLAN
AR-03

GENERAL NOTES:

1. THE COPYRIGHT OF THIS DRAWING IS VESTED IN YourSpreadsheets AND IT MAY NOT BE REPRODUCED IN WHOLE OR PART OR USED FOR THE MANUFACTURE OF ANY ARTICLE WITHOUT THE EXPRESS PERMISSION OF THE COPYRIGHT HOLDERS.
2. WORK TO FIGURED DIMENSIONS ONLY.
3. THIS DRAWING IS TO BE READ IN CONJUNCTION WITH ALL RELEVANT ARCHITECT'S, SERVICE ENGINEER'S AND YourSpreadsheets DRAWINGS .
ALL DRWAING ARE THE PROPOERTY OF THE DESIGNER & THEY ARE NOT TO BE REPRODUCED IN WHOLE OR IN PART WITHOUT WRITTEN CONSENT FROM THE DESIGN WING
CONTRACTOR TO CHECK &VERIFY ALL DIMENSIONS BEFORE COMMENCING WORK & TO REPORT ANY DISCREPANCIES TO THE DESIGN WING.
DO NOT SCALE DRAWINGS.
ALL CONSTRUCTION TO BE ACCORDING TO BEST COMMON PRACTICE.

REV:	DESCRIPTION:	BY:	DATE:
A	ARCHITECTURE DRAWING	----	25-12-25
B	STRUCTURE DRAWING	----	27-12-25

PROJECT NAME:
300 SQ.YARD HOUSE ARCHITECTURE DRAWING

SIGNATURE BY:

DRAWING TITLE:
ARCHITECTURAL DRAWING

DRAWN BY: MUDASSIR
CHECKED BY: M.SHEHERYAR
APPROVED BY: M.SHEHERYAR
DATE: 27-DEC-2025

CLIENT
MR. ROHAN
KARACHI...

DESIGNED BY:-

E.D.C.O
ENGINEERING DESIGNING CONSTRUCTION OFFICIAL
ARCHITECT| PLANNERS| ENGINEERS| INTERIOR| B.O.Q| EXTERIOR| CONSULT| STRUCTURE DESIGN| PLANNING| LAND SURVEY| CONSTRUCTION| 3D ANIMATION VIDEO| RENOVATION|
MUHAMMAD SHEHERYAR
CONTACT- 0312-2118445|D.H.A PHASE VII

PROJECT NO: AR-7590
SCALE: 1/8"=1'-0"
SHEET SIZE: A3
DRAWING NO: ARC
SHEET NO ----------
REVISION: YES
UNIT: INCHES&FEET

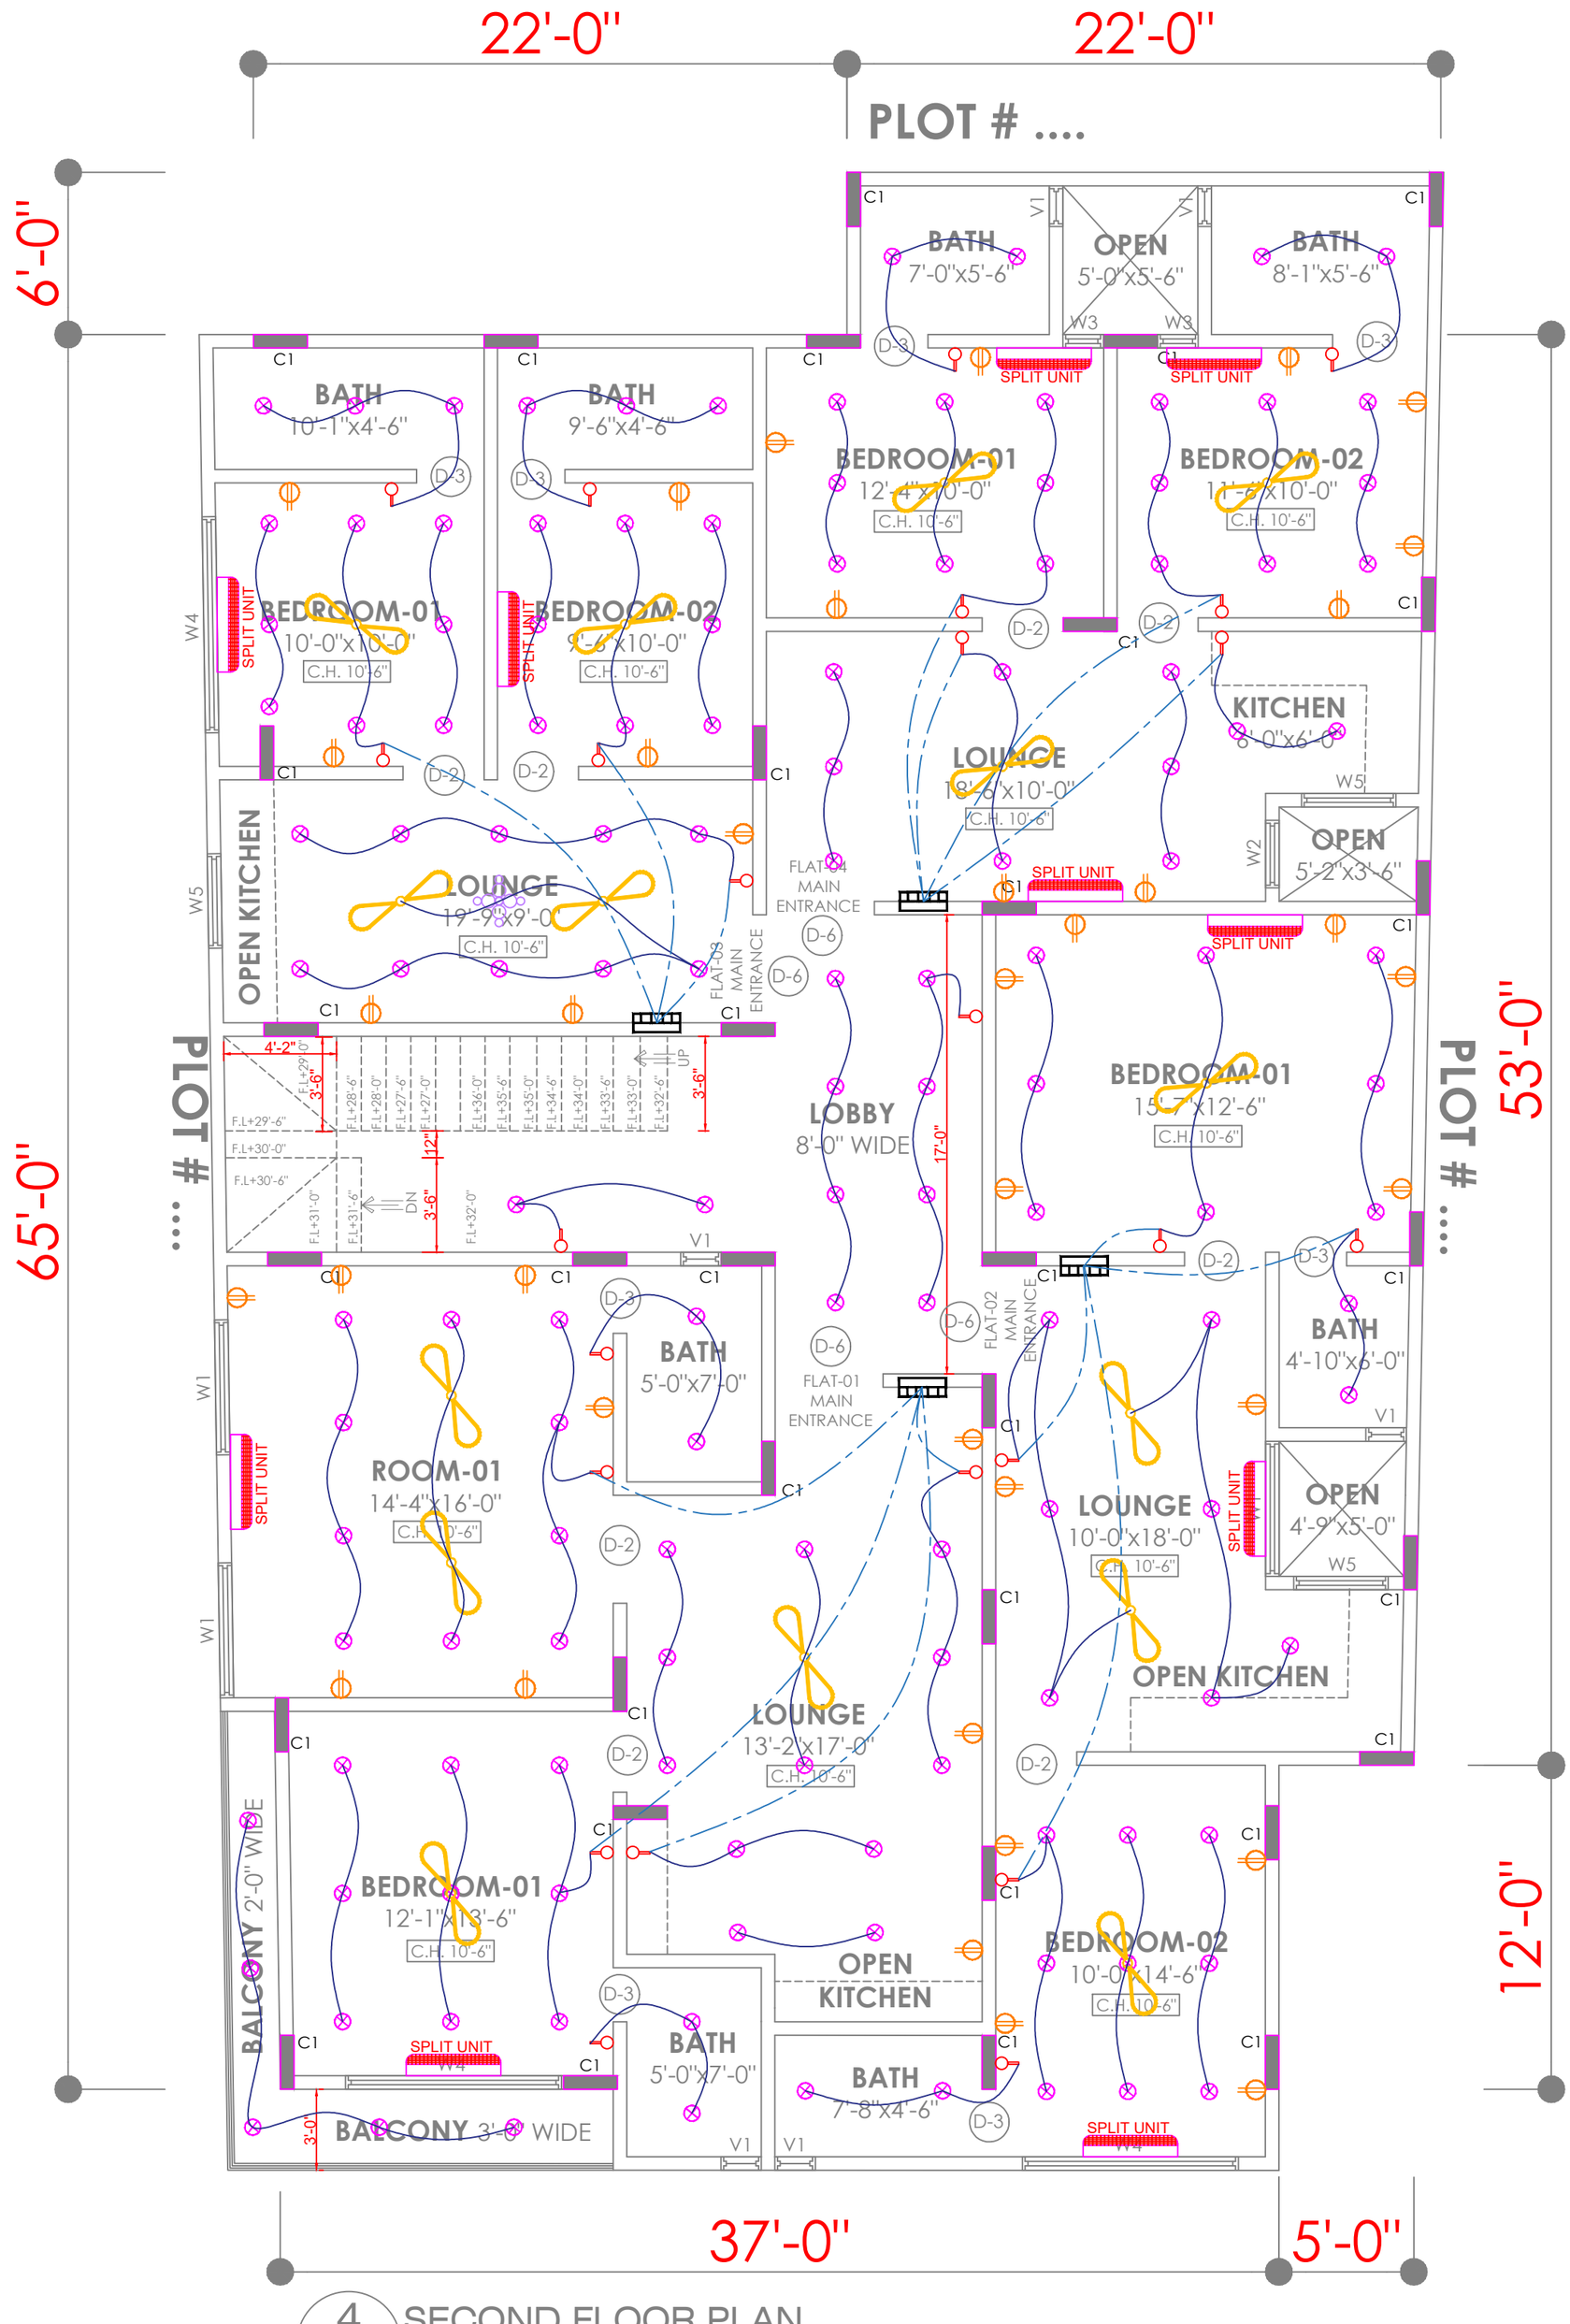

4 SECOND FLOOR PLAN
AR-04

GENERAL NOTES:

1. THE COPYRIGHT OF THIS DRAWING IS VESTED IN YourSpreadsheets AND IT MAY NOT BE REPRODUCED IN WHOLE OR PART OR USED FOR THE MANUFACTURE OF ANY ARTICLE WITHOUT THE EXPRESS PERMISSION OF THE COPYRIGHT HOLDERS.
2. WORK TO FIGURED DIMENSIONS ONLY.
3. THIS DRAWING IS TO BE READ IN CONJUNCTION WITH ALL RELEVANT ARCHITECT'S, SERVICE ENGINEER'S AND YourSpreadsheets DRAWINGS .

ALL DRWAING ARE THE PROPOERTY OF THE DESIGNER & THEY ARE NOT TO BE REPRODUCED IN WHOLE OR IN PART WITHOUT WRITTEN CONSENT FROM THE DESIGN WING
CONTRACTOR TO CHECK &VERIFY ALL DIMENSIONS BEFORE COMMENCING WORK & TO REPORT ANY DISCREPANCIES TO THE DESIGN WING.
DO NOT SCALE DRAWINGS.
ALL CONSTRUCTION TO BE ACCORDING TO BEST COMMON PRACTICE.

REV:	DESCRIPTION:	BY:	DATE:
A	ARCHITECTURE DRAWING	----	25-12-25
B	STRUCTURE DRAWING	----	27-12-25

PROJECT NAME:
300 SQ.YARD HOUSE ARCHITECTURE DRAWING

SIGNATURE BY:

DRAWING TITLE:
ARCHITECTURAL DRAWING

DRAWN BY: MUDASSIR
CHECKED BY: M.SHEHERYAR
APPROVED BY: M.SHEHERYAR
DATE: 27-DEC-2025

CLIENT
MR. ROHAN
KARACHI...

DESIGNED BY:-

E.D.C.O
ENGINEERING DESIGNING CONSTRUCTION OFFICIAL
ARCHITECT| PLANNERS| ENGINEERS| INTERIOR| B.O.Q| EXTERIOR| CONSULT| STRUCTURE DESIGN| PLANNING| LAND SURVEY| CONSTRUCTION| 3D ANIMATION VIDEO| RENOVATION|
MUHAMMAD SHEHERYAR
CONTACT- 0312-2118445|D.H.A PHASE VII

PROJECT NO: AR-7590
SCALE: 1/8"=1'-0"
SHEET SIZE: A3
DRAWING NO: ARC
SHEET NO ----------
REVISION: YES
UNIT: INCHES&FEET

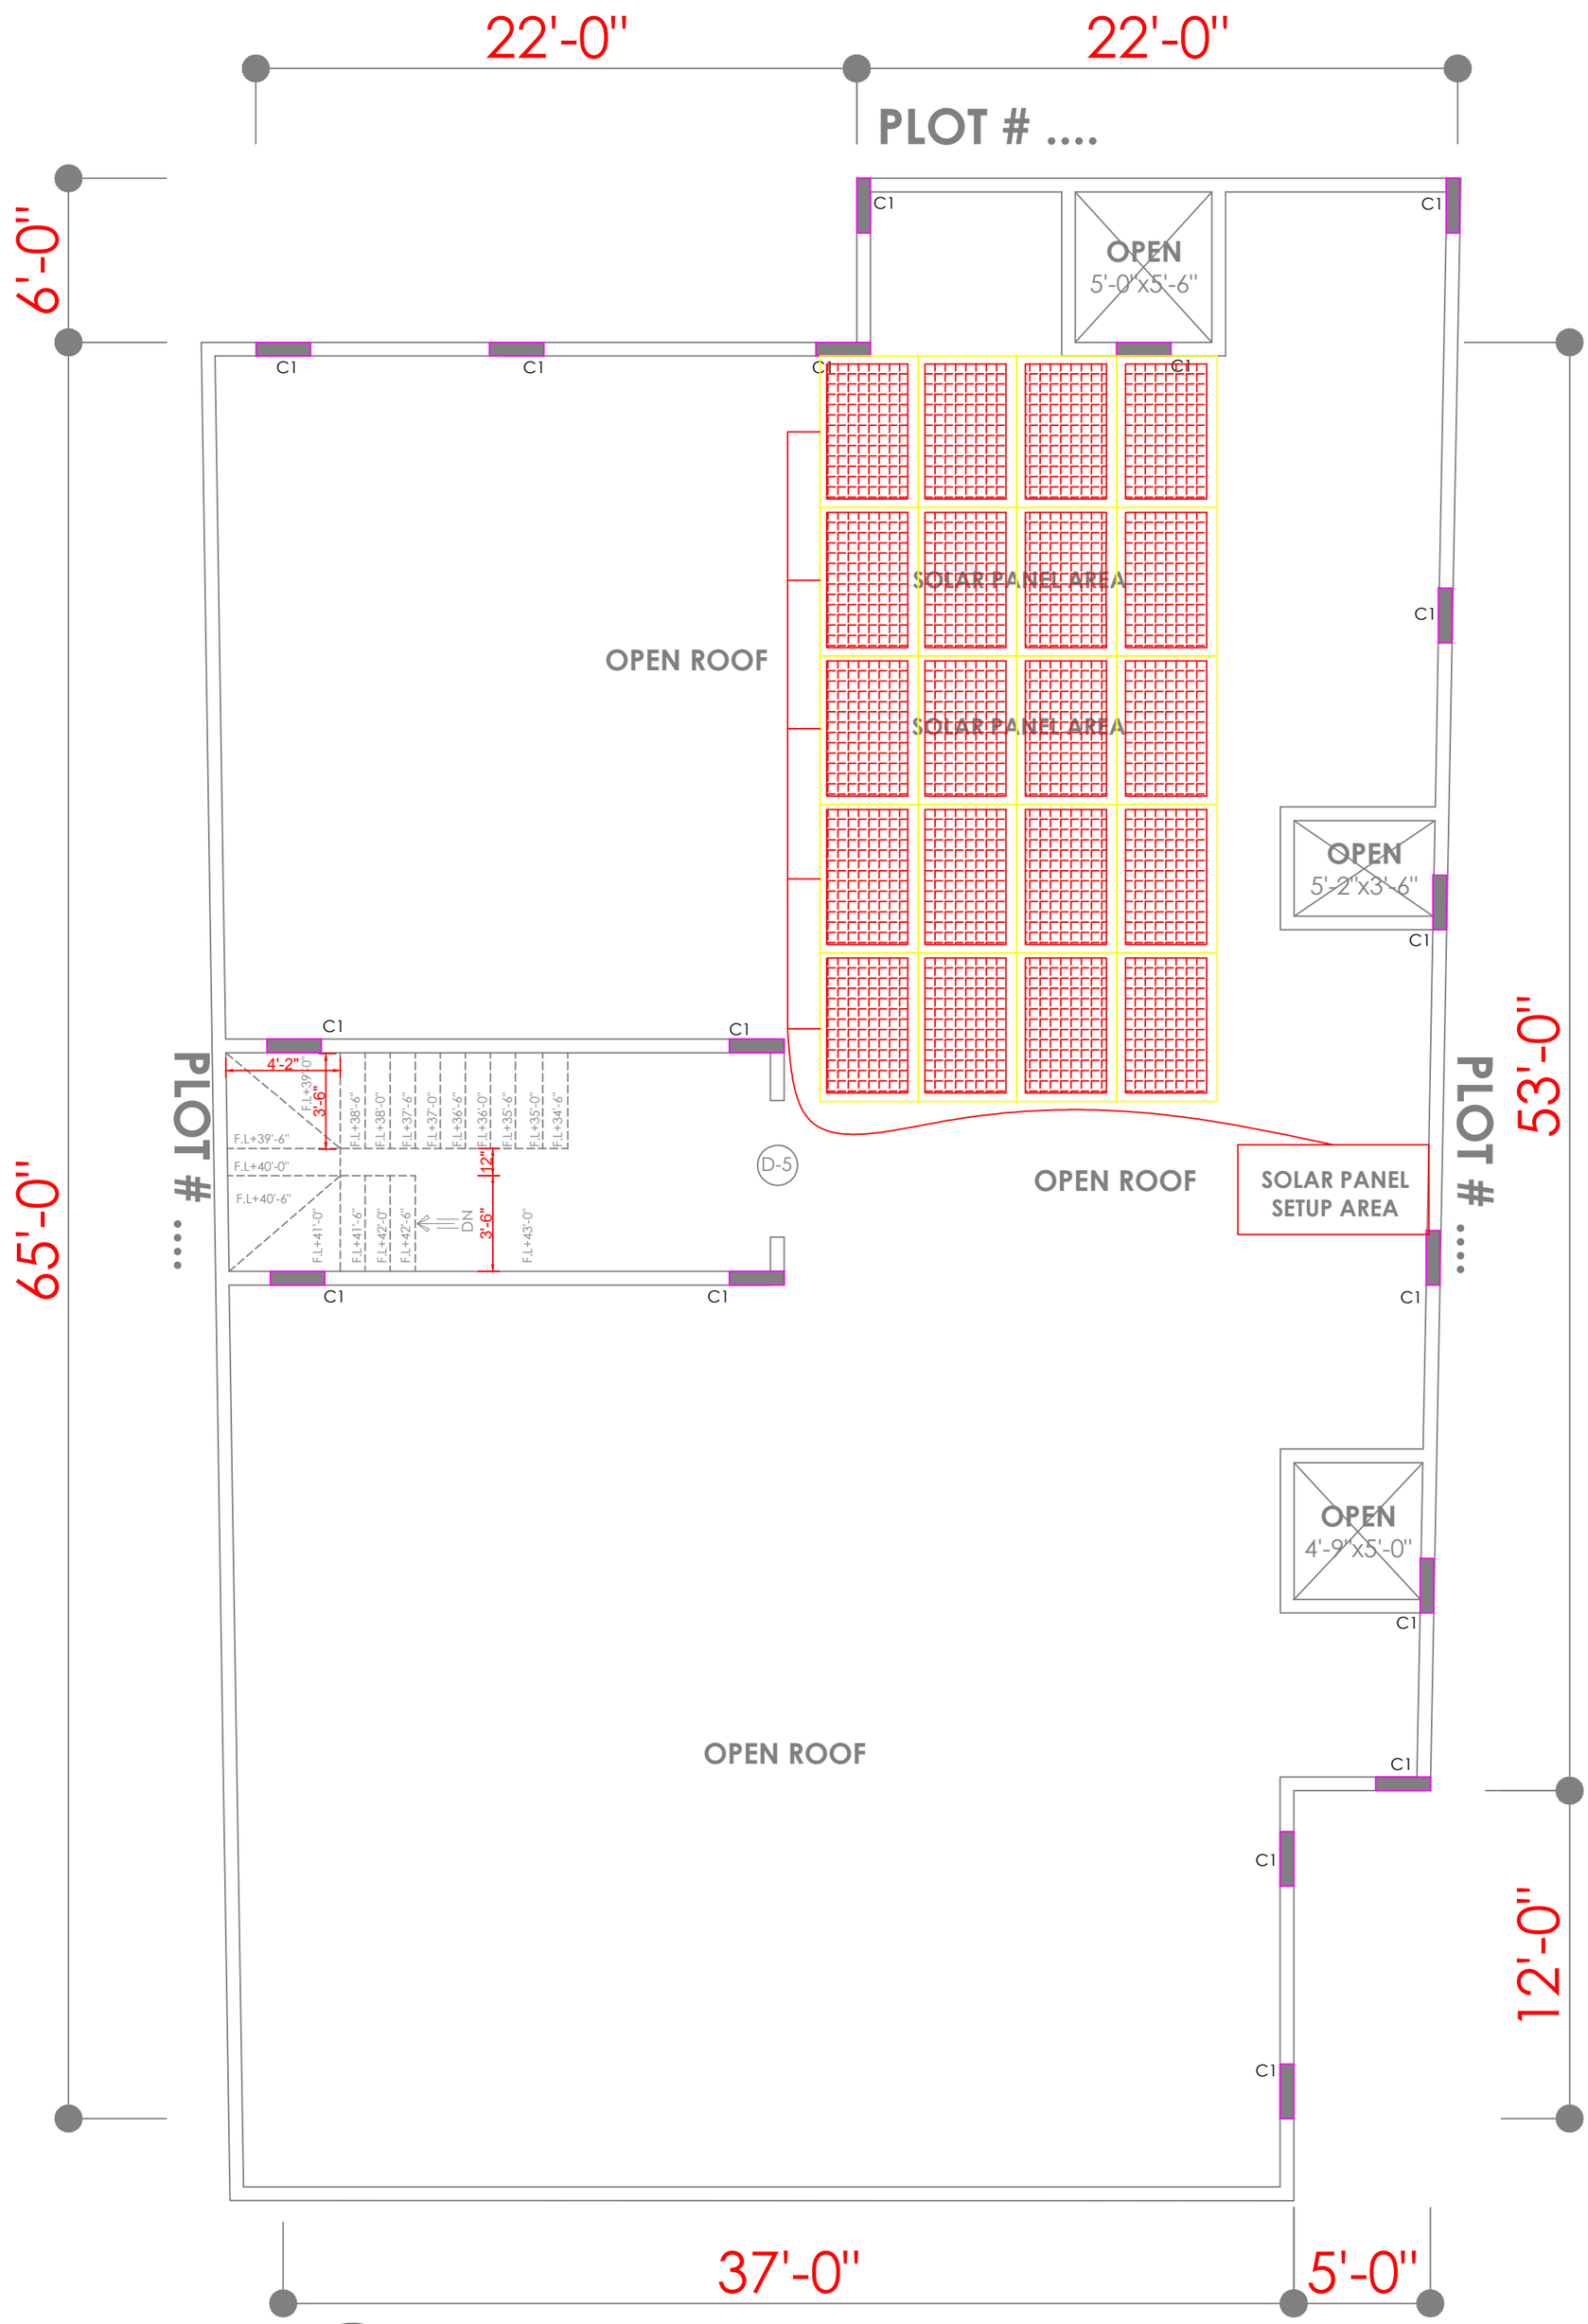

5
AR-05
ROOF TOP PLAN

GENERAL NOTES:

1. THE COPYRIGHT OF THIS DRAWING IS VESTED IN YourSpreadsheets AND IT MAY NOT BE REPRODUCED IN WHOLE OR PART OR USED FOR THE MANUFACTURE OF ANY ARTICLE WITHOUT THE EXPRESS PERMISSION OF THE COPYRIGHT HOLDERS.
2. WORK TO FIGURED DIMENSIONS ONLY.
3. THIS DRAWING IS TO BE READ IN CONJUNCTION WITH ALL RELEVANT ARCHITECT'S, SERVICE ENGINEER'S AND YourSpreadsheets DRAWINGS .

ALL DRWAING ARE THE PROPOERTY OF THE DESIGNER & THEY ARE NOT TO BE REPRODUCED IN WHOLE OR IN PART WITHOUT WRITTEN CONSENT FROM THE DESIGN WING

CONTRACTOR TO CHECK &VERIFY ALL DIMENSIONS BEFORE COMMENCING WORK & TO REPORT ANY DISCREPANCIES TO THE DESIGN WING.

DO NOT SCALE DRAWINGS.

ALL CONSTRUCTION TO BE ACCORDING TO BEST COMMON PRACTICE.

REV:	DESCRIPTION:	BY:	DATE:
A	ARCHITECTURE DRAWING	----	25-12-25
B	STRUCTURE DRAWING	----	27-12-25

PROJECT NAME:
300 SQ.YARD HOUSE ARCHITECTURE DRAWING

SIGNATURE BY:

DRAWING TITLE:
ARCHITECTURAL DRAWING

DRAWN BY: MUDASSIR

CHECKED BY: M.SHEHERYAR

APPROVED BY: M.SHEHERYAR

DATE: 27-DEC-2025

CLIENT
MR. ROHAN
KARACHI...

DESIGNED BY:-

E.D.C.O
ENGINEERING DESIGNING CONSTRUCTION OFFICIAL
ARCHITECT| PLANNERS| ENGINEERS| INTERIOR| B.O.Q| EXTERIOR| CONSULT| STRUCTURE DESIGN| PLANNING| LAND SURVEY| CONSTRUCTION| 3D ANIMATION VIDEO| RENOVATION|
MUHAMMAD SHEHERYAR
CONTACT- 0312-2118445|D.H.A PHASE VII

PROJECT NO: AR-7590

SCALE: 1/8"=1'-0"

SHEET SIZE: A3

DRAWING NO: ARC

SHEET NO ----------

REVISION: YES

UNIT: INCHES&FEET

S E W N

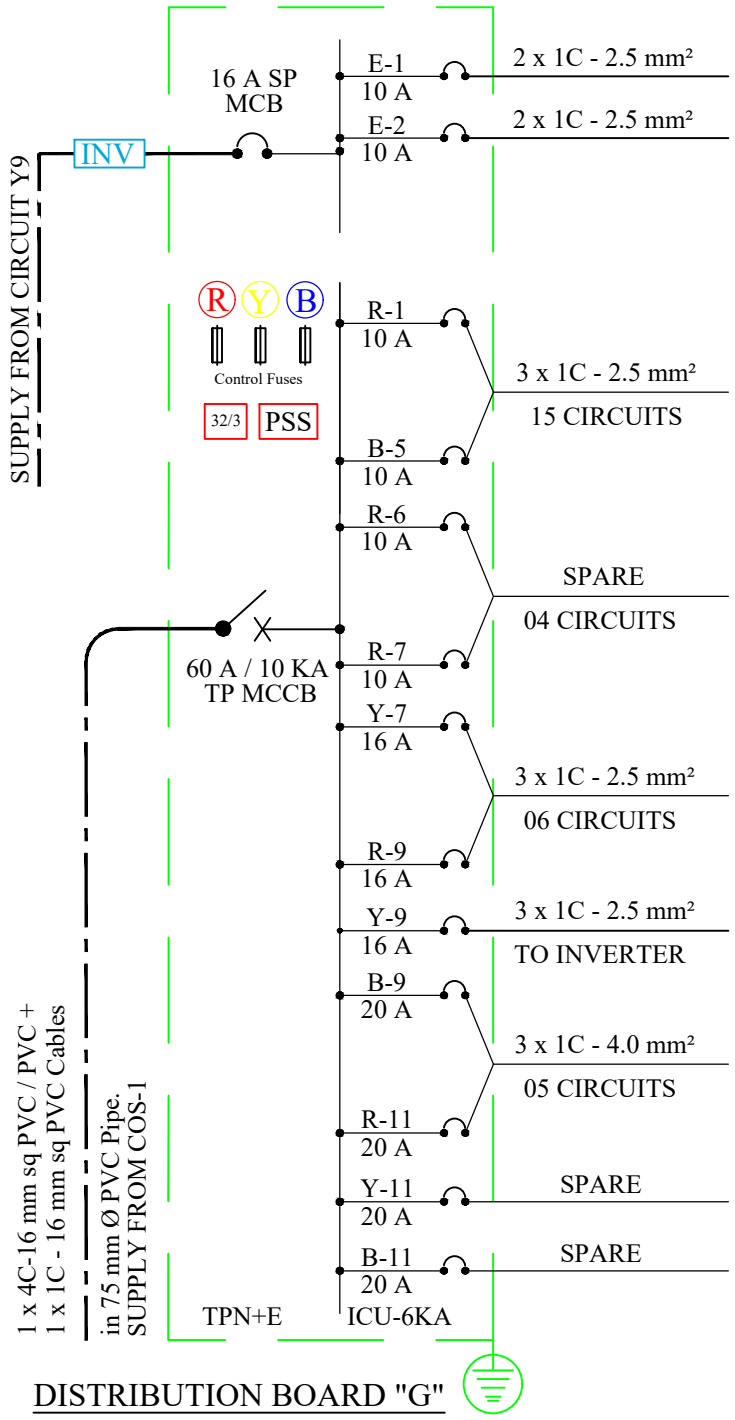
16 A SP
MCB
INV
SUPPLY FROM CIRCUIT Y9
E-1
10 A
2 x 1C - 2.5 mm²
E-2
10 A
2 x 1C - 2.5 mm²
R Y B
Control Fuses
32/3
PSS
R-1
10 A
3 x 1C - 2.5 mm²
15 CIRCUITS
B-5
10 A
R-6
10 A
SPARE
04 CIRCUITS
60 A / 10 KA
TP MCCB
R-7
10 A
Y-7
16 A
3 x 1C - 2.5 mm²
06 CIRCUITS
R-9
16 A
Y-9
16 A
3 x 1C - 2.5 mm²
TO INVERTER
B-9
20 A
3 x 1C - 4.0 mm²
05 CIRCUITS
R-11
20 A
Y-11
20 A
SPARE
B-11
20 A
SPARE
1 x 4C-16 mm sq PVC / PVC +
1 x 1C - 16 mm sq PVC Cables
in 75 mm Ø PVC Pipe.
SUPPLY FROM COS-1
TPN+E
ICU-6KA
DISTRIBUTION BOARD "G"

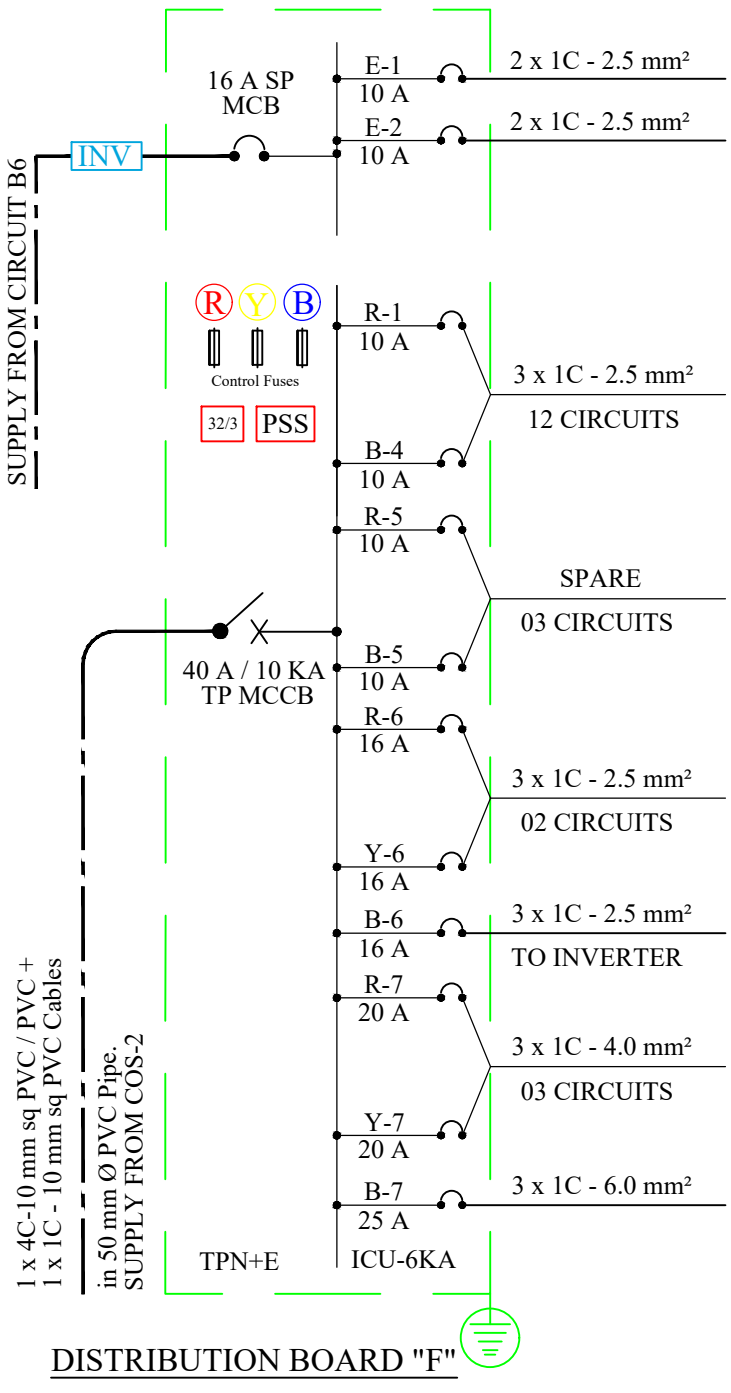
16 A SP
MCB
INV
SUPPLY FROM CIRCUIT B6
E-1
10 A
2 x 1C - 2.5 mm²
E-2
10 A
2 x 1C - 2.5 mm²
R Y B
Control Fuses
32/3
PSS
R-1
10 A
3 x 1C - 2.5 mm²
12 CIRCUITS
B-4
10 A
R-5
10 A
SPARE
03 CIRCUITS
40 A / 10 KA
TP MCCB
B-5
10 A
R-6
16 A
3 x 1C - 2.5 mm²
02 CIRCUITS
Y-6
16 A
B-6
16 A
3 x 1C - 2.5 mm²
TO INVERTER
R-7
20 A
3 x 1C - 4.0 mm²
03 CIRCUITS
Y-7
20 A
B-7
25 A
3 x 1C - 6.0 mm²
1 x 4C-10 mm sq PVC / PVC +
1 x 1C - 10 mm sq PVC Cables
in 50 mm Ø PVC Pipe.
SUPPLY FROM COS-2
TPN+E
ICU-6KA
DISTRIBUTION BOARD "F"

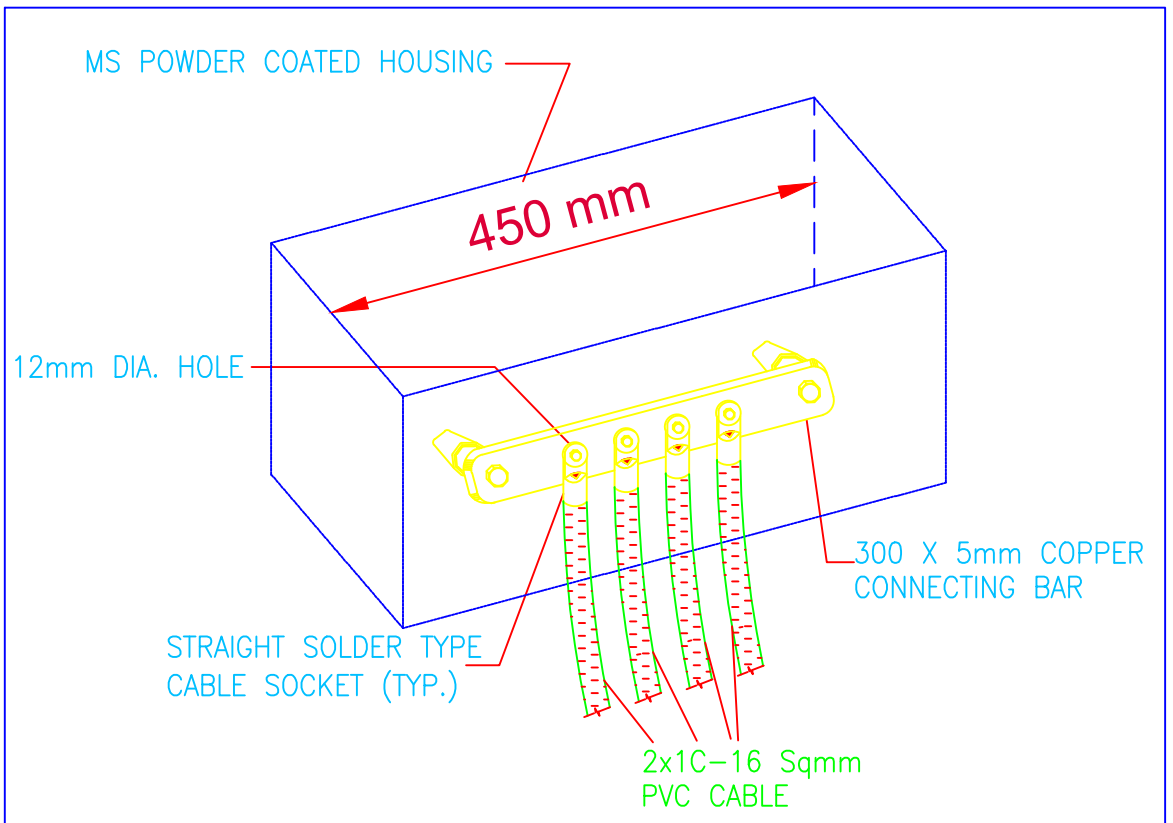

EARTH TEST POINT

ELECTRICAL DISTRIBUTION
SCHEMATIC DIAGRAM

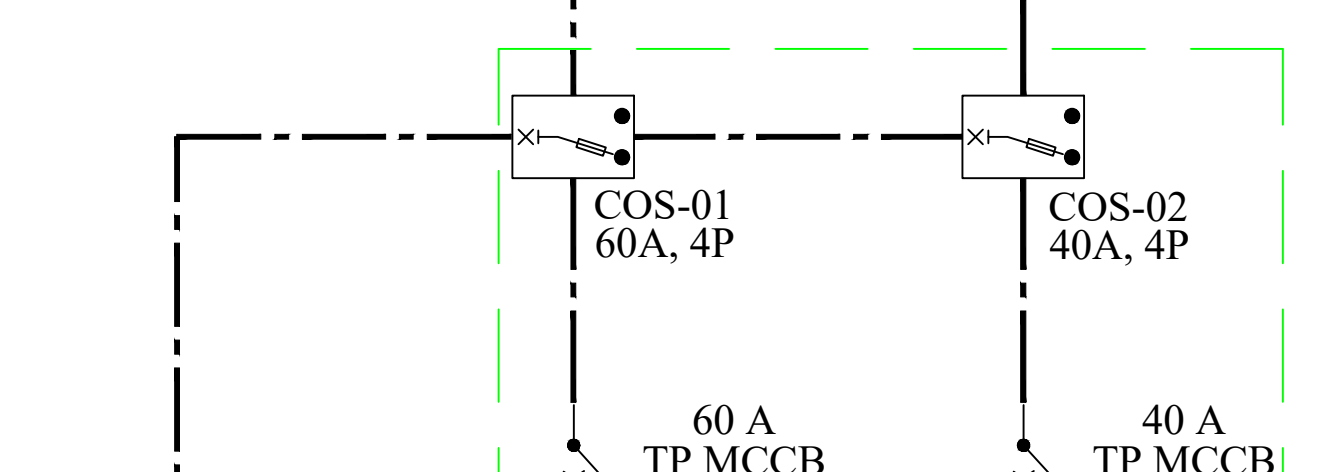

DOOR INTERCOM SCHEMATIC DIAGRAM

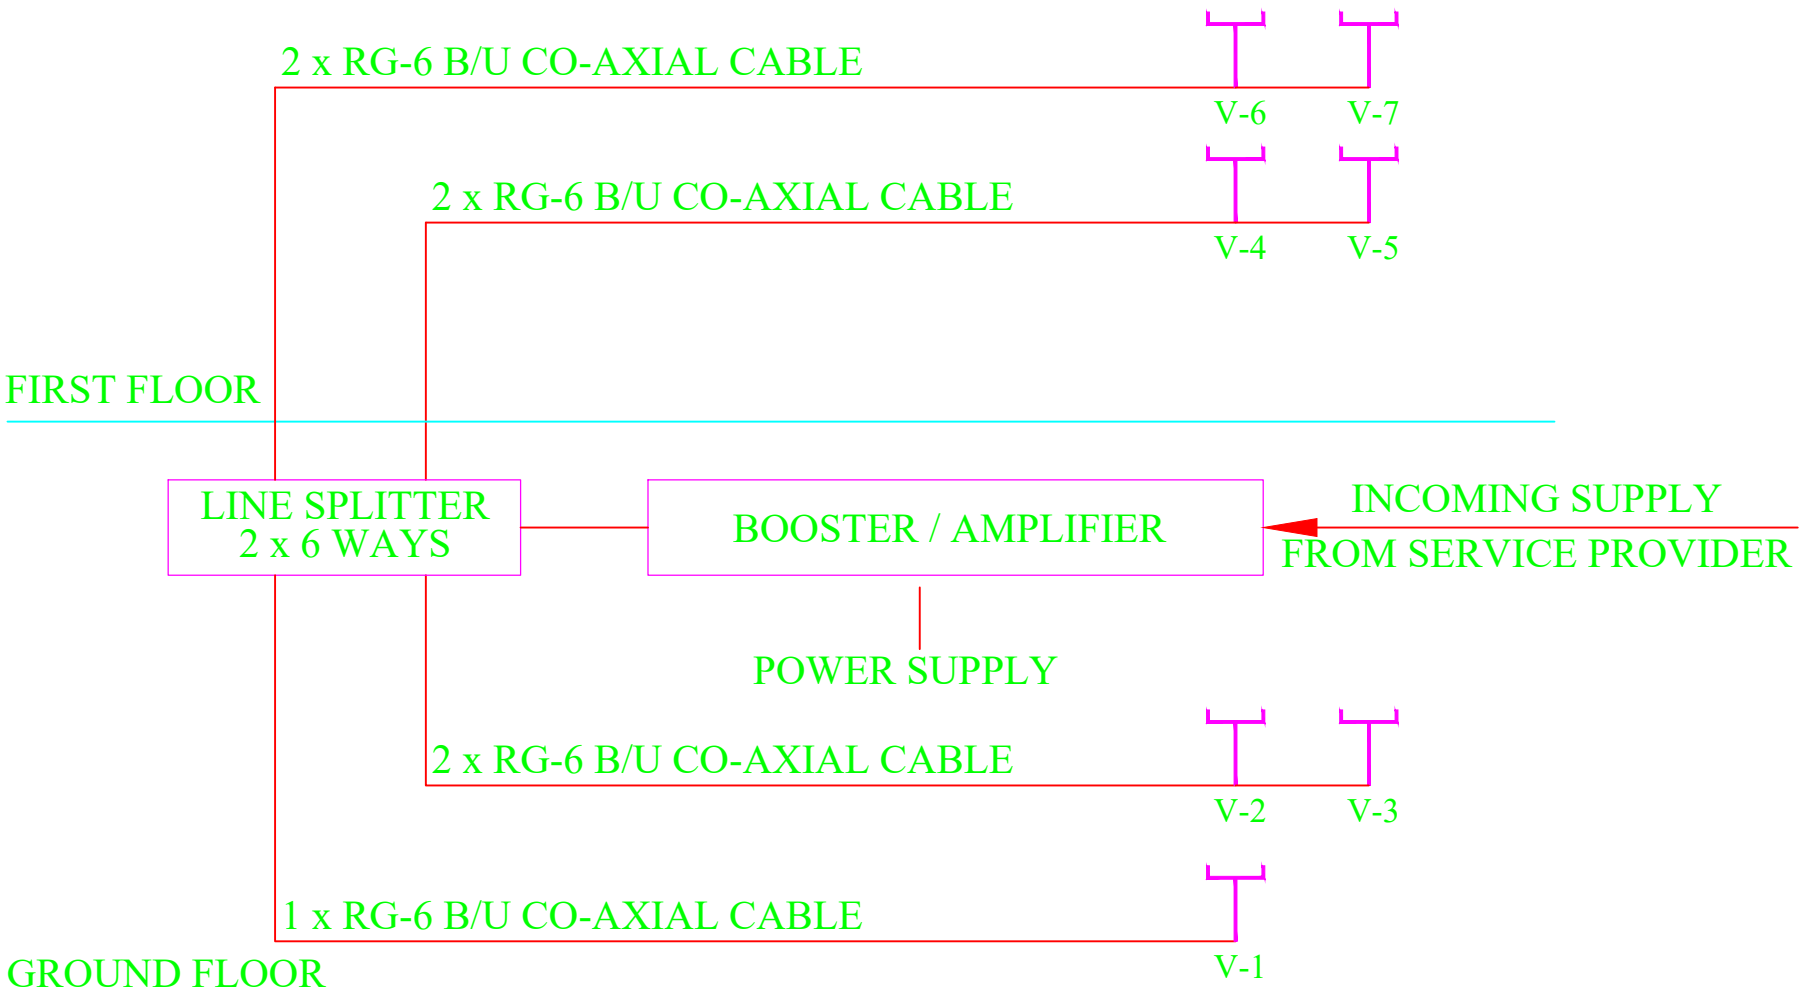

CATV SYSTEM SCHEMATIC DIAGRAM

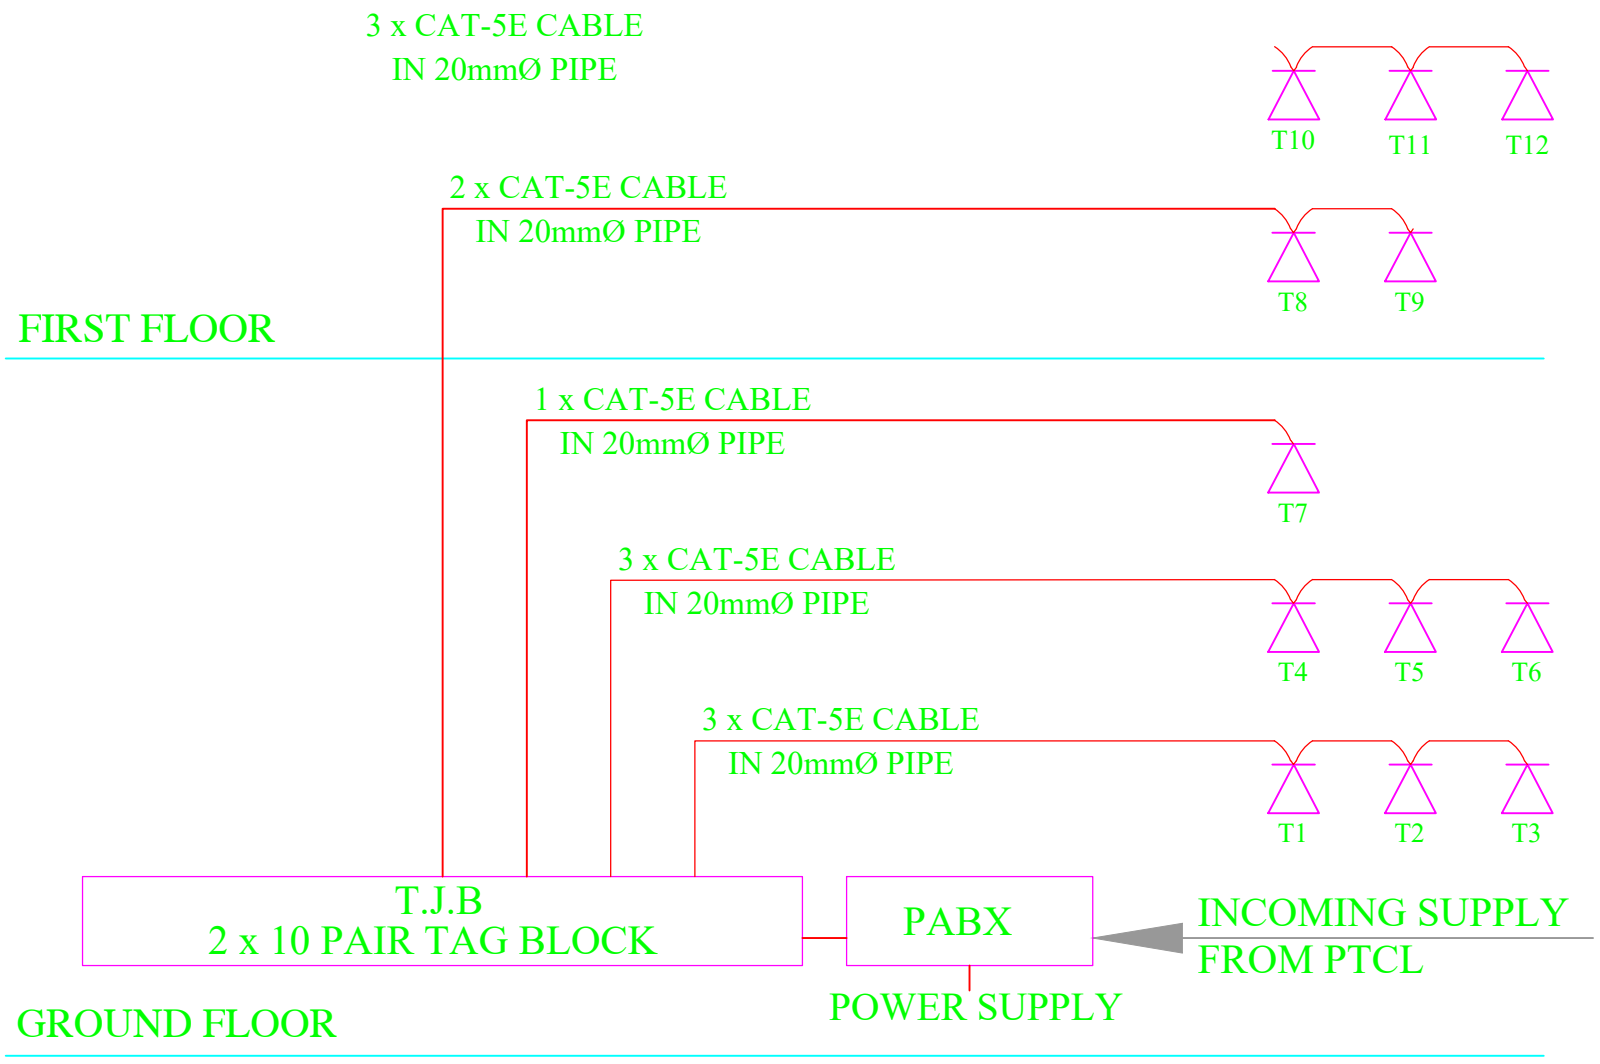

VOICE SYSTEM SCHEMATIC DIAGRAM

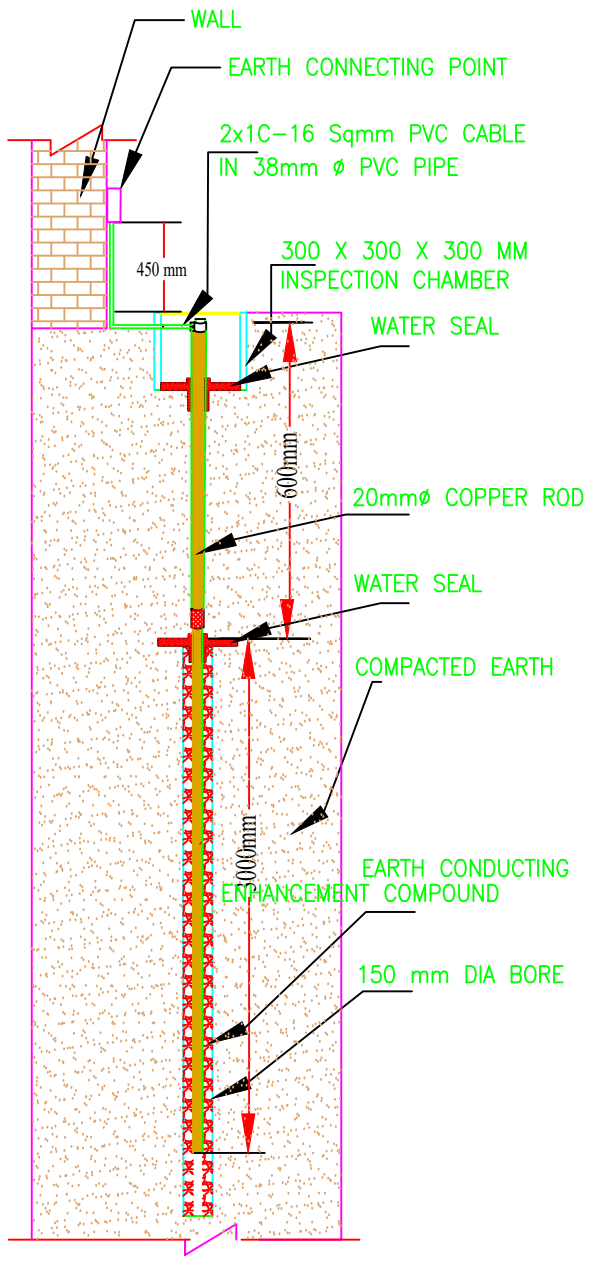

DETAIL OF ENVIRONMENTAL FREE EARHTING

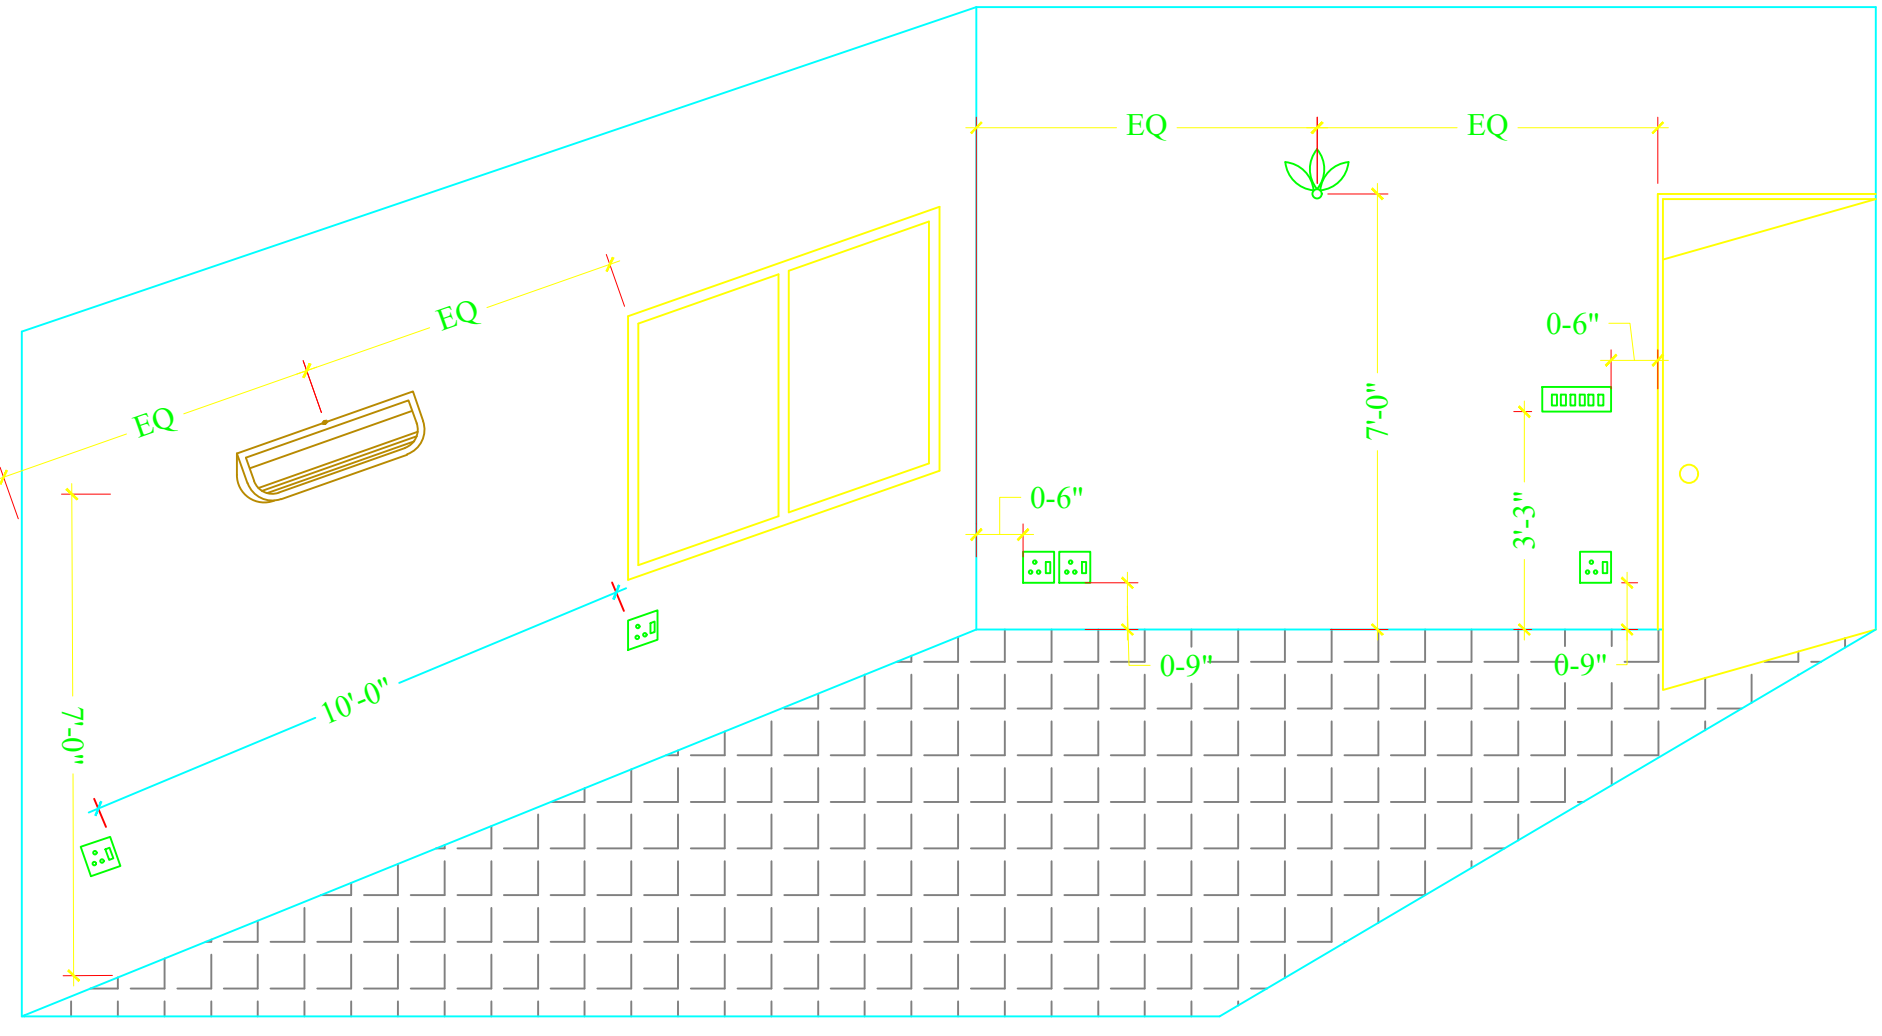

ELECTRICAL LEGEND

SYMBOLS	DESCRIPTION	HEIGHT FROM F.F.L
	10A S.P SWITCH (SWITCH BOX)	FROM F.F.L 42"
	CEILING LIGHT WITH 18W ENERGY SAVER	SURFACE
	DIRECTIONAL LIGHT / SPOT LIGHT	SURFACE
	4" DIA CONCEILED LIGHT WITH 14W PLEC LAMP	AS PER SITE
	FLUORESCENT CEILING LIGHT TCS- 240	SURFACE
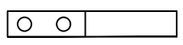	MIRROR LIGHT FIXTURE INCANDESCENT TUBLER	FROM F.F.L 6'-6"
	PENDENT LIGHT FIXTURE	PENDENT
	FANCY LIGHT FIXTURE WITH 14W PLEC LAMP	FROM F.F.L 8'-0"
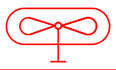	WALL BRACKET FAN 80W	FROM F.F.L 7'-6"
	EXHAUST FAN (12" DIA)	FROM F.F.L 8'-6"
	GATE LIGHT WITH 18W PLEC LAMP	AS PER SITE COND.
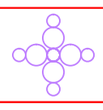	CHANDELIER (500W)	AT CEILING
	BULK HEAD WITH 18W PLEC LAMP	AS PER SITE COND.
	LIGHT FIXTURE TMS-140	SURFACE
	LIGHT FIXTURE WITH 14W PLEC LAMP	AS PER SITE COND.
	LIGHT ON FLOOR	FLOOR
	CEILING FAN 80W (WITH FAN HOOK STEEL BOX)	CEILING
	5A SHAVER SWITCH SOCKET 2PIN	FROM F.F.L 42"
	SPLIT UNIT (INDOOR UNIT)	AS PER SITE COND.
	SPLIT UNIT CONDENSER	AS PER SITE COND.
	LCD CABLE OUTLET	FROM F.F.L 4'-6"
	GATE INTERCOM UNIT	FROM F.F.L 4'-6"
	CONDUIT RUN UNDER CEILING SLAB	———
	CONDUIT RUN UNDER FLOOR	———
	CONDUIT RUN UNDER WALL	———
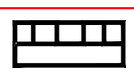	L. DB (DISTRIBUTION BOARD)	FROM F.F.L TO TOP OF L.DB 7'-0"
	BELL / BELL PUSH	BEEL F.F.L TO 7' BELL PUSH F.F.L 42"
	15A POWER SOCKET	FROM F.F.L TO MID POINT OF BOX 1'-0"
	5A 10A LIGHT PLUG	FROM F.F.L TO MID POINT OF BOX 1'-0"
	TELEPHONE OUTLET (RJ-11)	FROM F.F.L TO MID POINT OF BOX 1'-0"
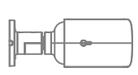	C.C. TV CAMERA (RJ-11)	AS PER SITE

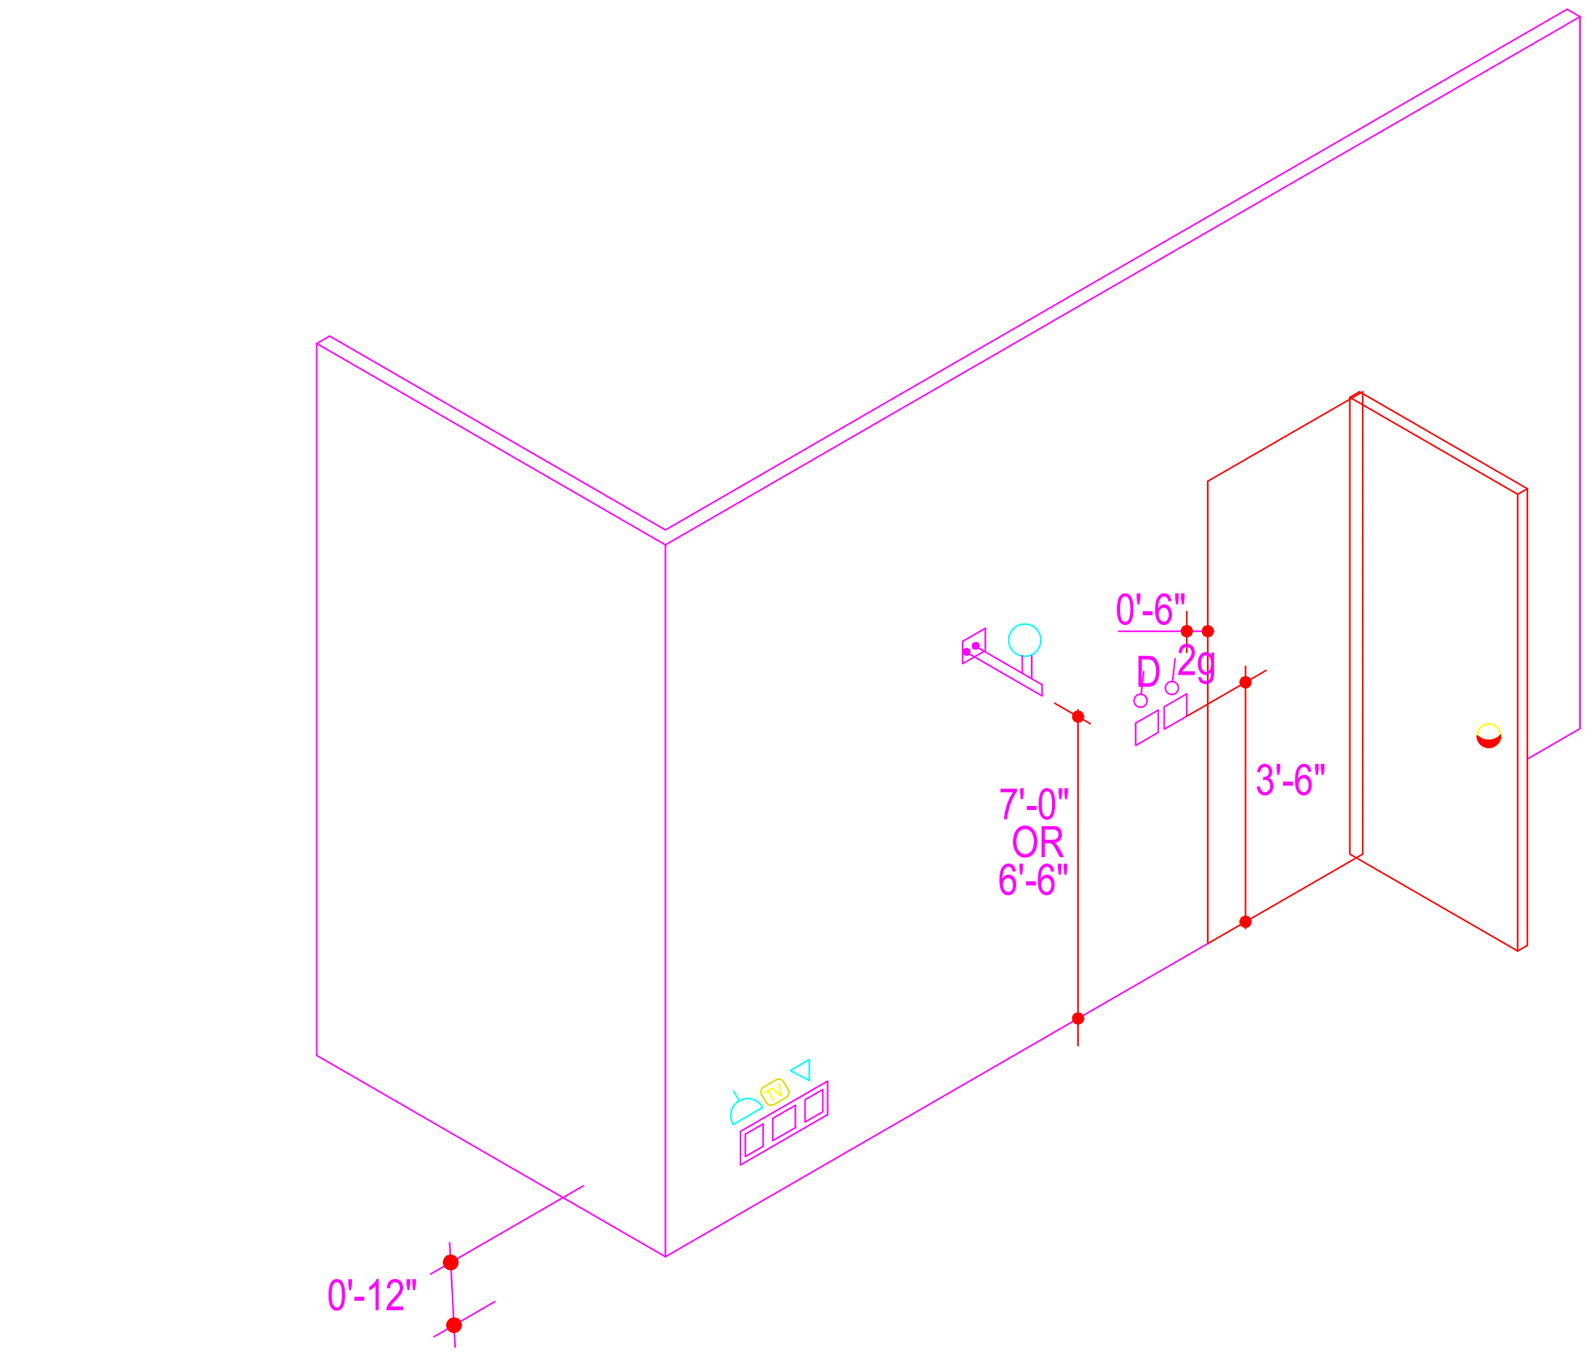

MOUNTING HEIGHT DETAIL FOR SWITCH SOCKET ETC.
(OR AS DIRECTED BY ARCHITECT)

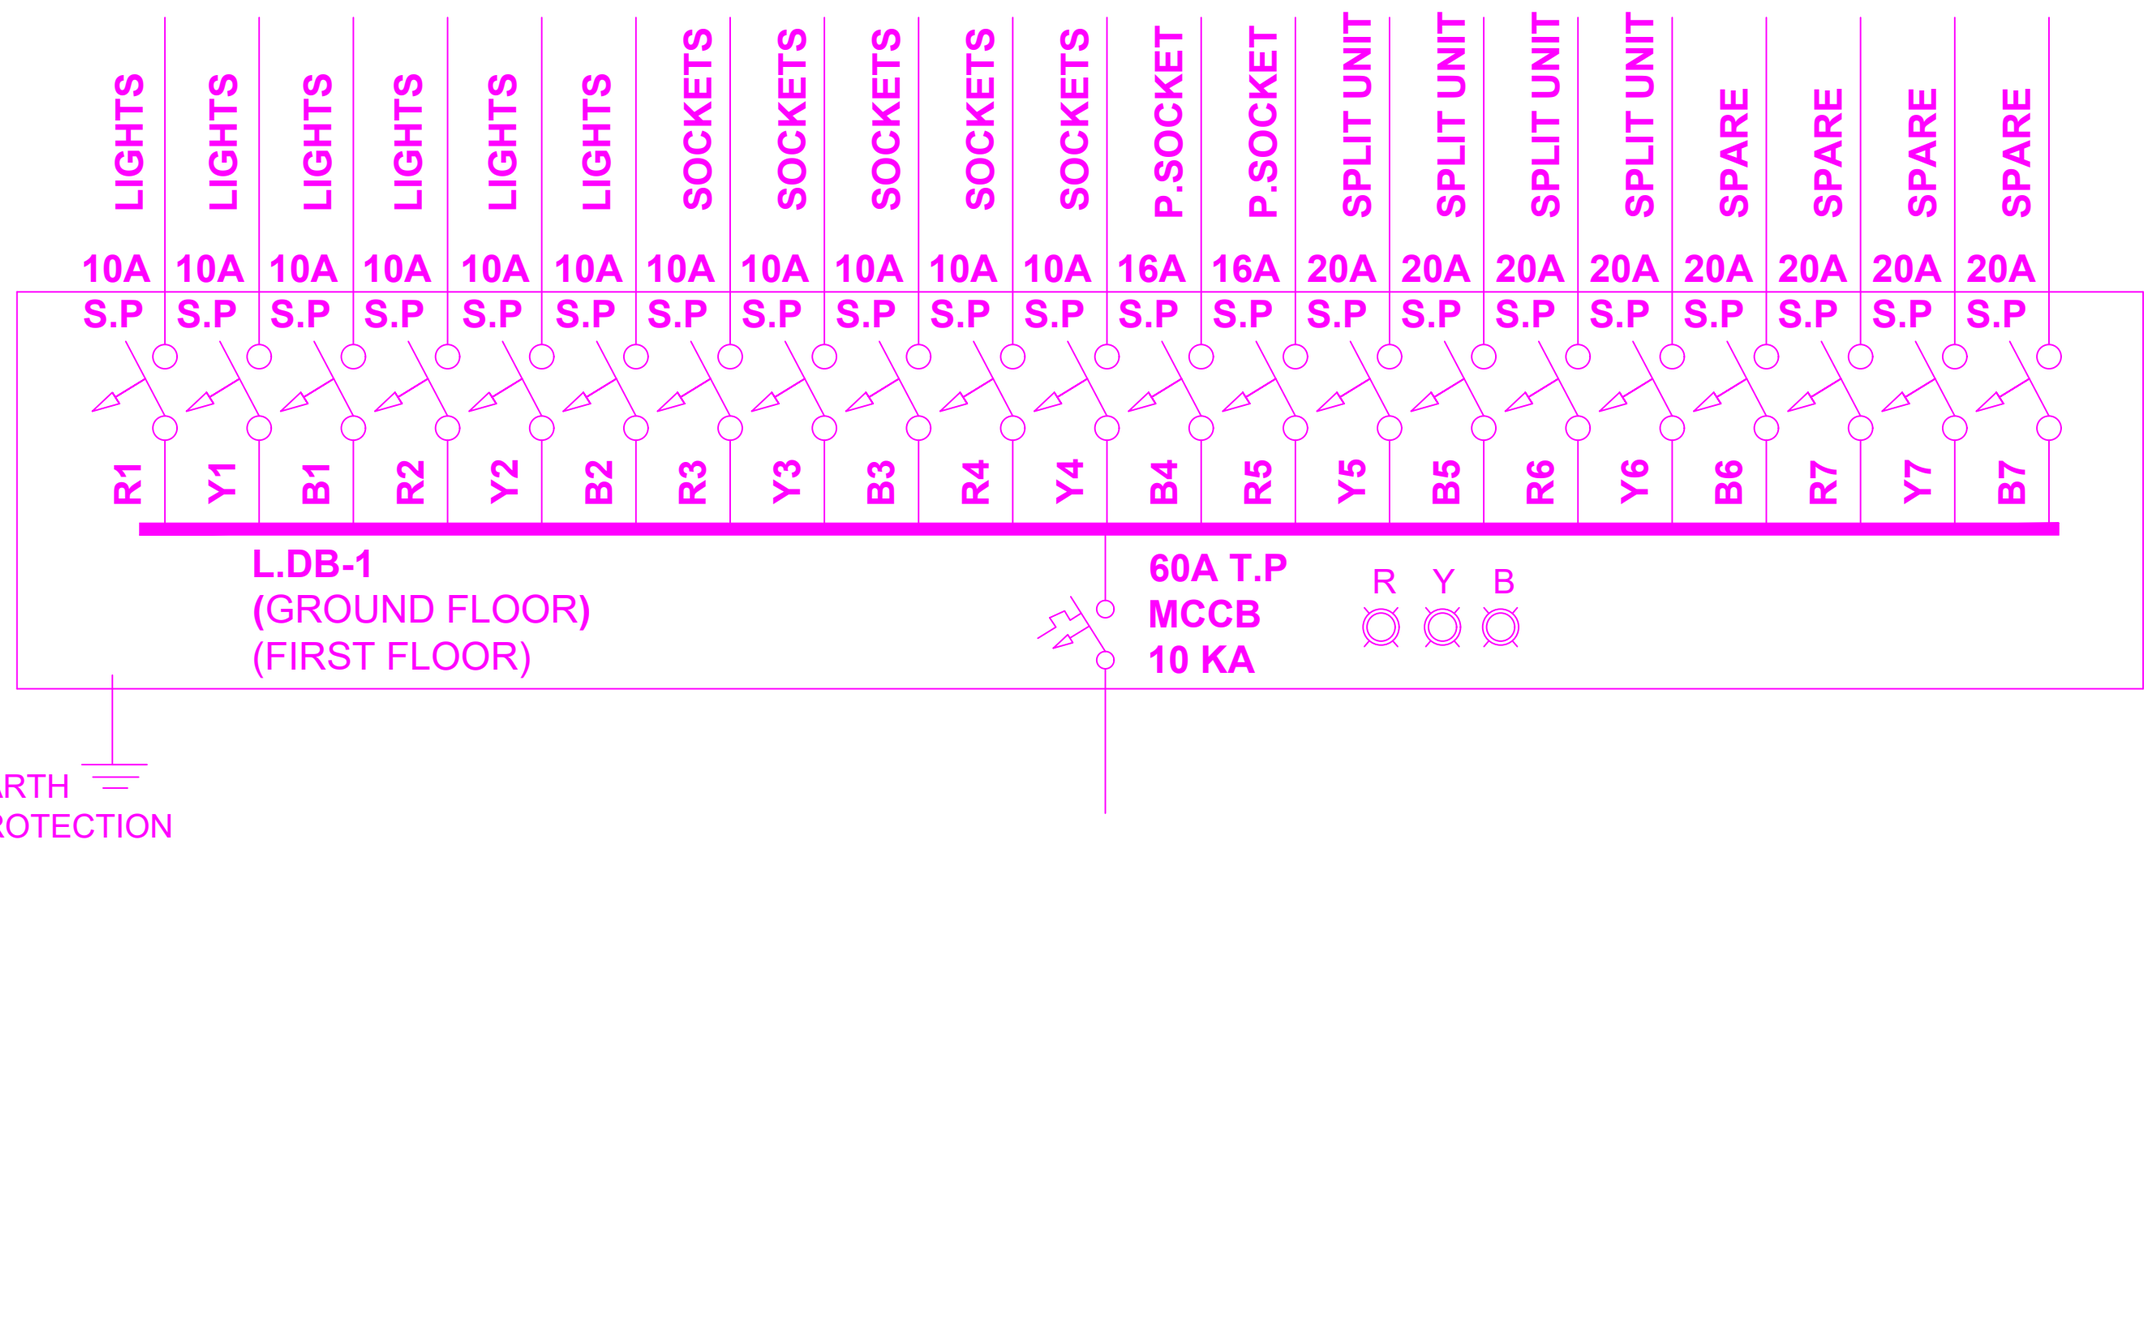

WIRING SCHEDULE

	DESCRIPTION	CABLE SIZE CU/PVC	CONDUIT SIZE	LOCATION
01	TELEPHONE SYSTEM (RJ-11)	4PAIR CAT-5e	25mmØ	FLOOR
02	LIGHT POINT / FAN POINT	**3x1.5mm² 1CORE**	25mmØ	CEILING
03	5A LIGHT PLUG	3x2.5mm² 1CORE	25mmØ	FLOOR
04	SPLIT UNIT 2 TON	2x6mm²+1x4mm²	25mmØ	CEILING
05	SPLIT UNIT 1.5 TON	**2x4mm²+1x2.5mm²**	25mmØ	CEILING
06	SPLIT UNIT 1 TON	**2x4mm²+1x2.5mm²**	25mmØ	CEILING
07	15A POWER SWITCH SOCKET	2x4mm²+1x2.5mm²	25mmØ	FLOOR
08	LIGHT CKT D.B TO SWITCH BOX	3x2.5mm² 1CORE	25mmØ	CEILING

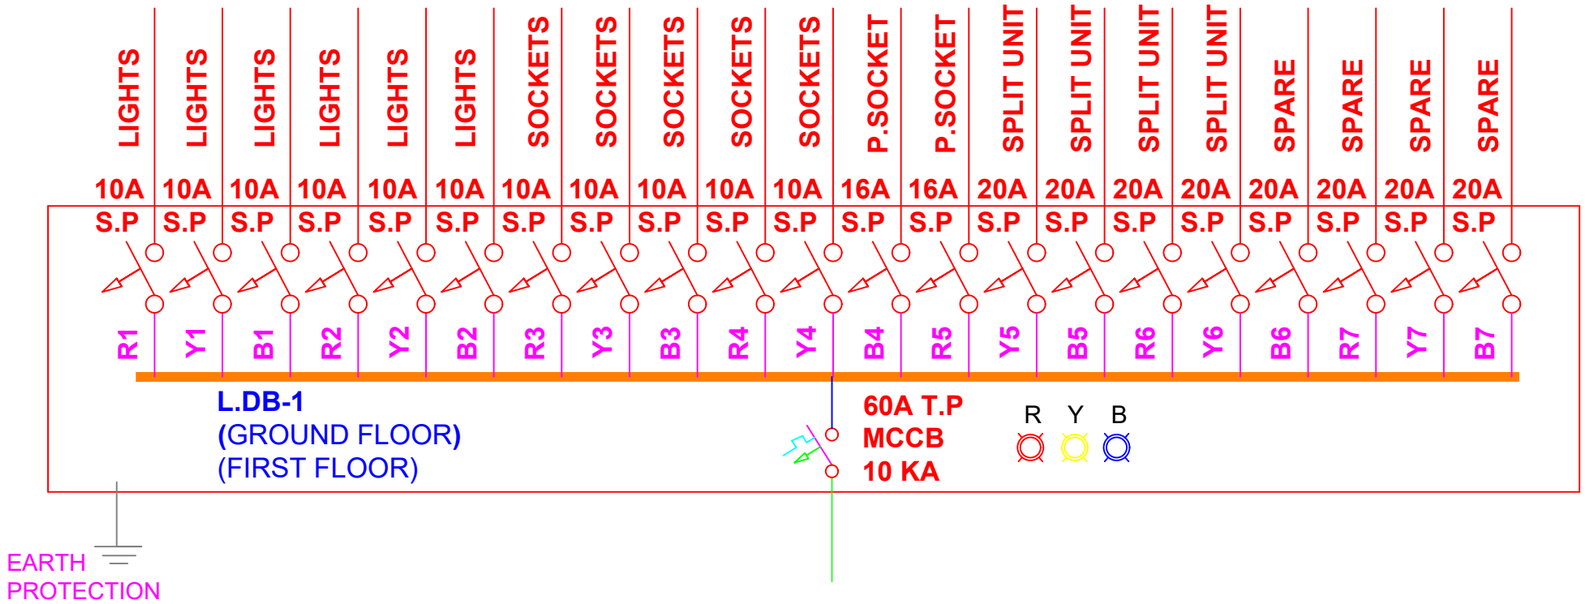

PLUMBING

LAYOUT

DRAWING

GENERAL NOTES:

1. THE COPYRIGHT OF THIS DRAWING IS VESTED IN YourSpreadsheets AND IT MAY NOT BE REPRODUCED IN WHOLE OR PART OR USED FOR THE MANUFACTURE OF ANY ARTICLE WITHOUT THE EXPRESS PERMISSION OF THE COPYRIGHT HOLDERS.
2. WORK TO FIGURED DIMENSIONS ONLY.
3. THIS DRAWING IS TO BE READ IN CONJUNCTION WITH ALL RELEVANT ARCHITECT'S, SERVICE ENGINEER'S AND YourSpreadsheets DRAWINGS .

ALL DRWAING ARE THE PROPOERTY OF THE DESIGNER & THEY ARE NOT TO BE REPRODUCED IN WHOLE OR IN PART WITHOUT WRITTEN CONSENT FROM THE DESIGN WING
CONTRACTOR TO CHECK &VERIFY ALL DIMENSIONS BEFORE COMMENCING WORK & TO REPORT ANY DISCREPANCIES TO THE DESIGN WING.
DO NOT SCALE DRAWINGS.
ALL CONSTRUCTION TO BE ACCORDING TO BEST COMMON PRACTICE.

REV:	DESCRIPTION:	BY:	DATE:
A	ARCHITECTURE DRAWING	----	25-12-25
B	STRUCTURE DRAWING	----	27-12-25

PROJECT NAME:
300 SQ.YARD HOUSE ARCHITECTURE DRAWING

SIGNATURE BY:

DRAWING TITLE:
ARCHITECTURAL DRAWING

DRAWN BY: MUDASSIR

CHECKED BY: M.SHEHERYAR

APPROVED BY: M.SHEHERYAR

DATE: 27-DEC-2025

CLIENT
MR. ROHAN
KARACHI...

DESIGNED BY:-

E.D.C.O
ENGINEERING DESIGNING CONSTRUCTION OFFICIAL
ARCHITECT| PLANNERS| ENGINEERS| INTERIOR| B.O.Q| EXTERIOR| CONSULT| STRUCTURE DESIGN| PLANNING| LAND SURVEY| CONSTRUCTION| 3D ANIMATION VIDEO| RENOVATION|
MUHAMMAD SHEHERYAR
CONTACT- 0312-2118445|D.H.A PHASE VII

PROJECT NO: AR-7590

SCALE: 1/8"=1'-0"

SHEET SIZE: A3

DRAWING NO: ARC

SHEET NO ----------

REVISION: YES

UNIT: INCHES&FEET

S E W N

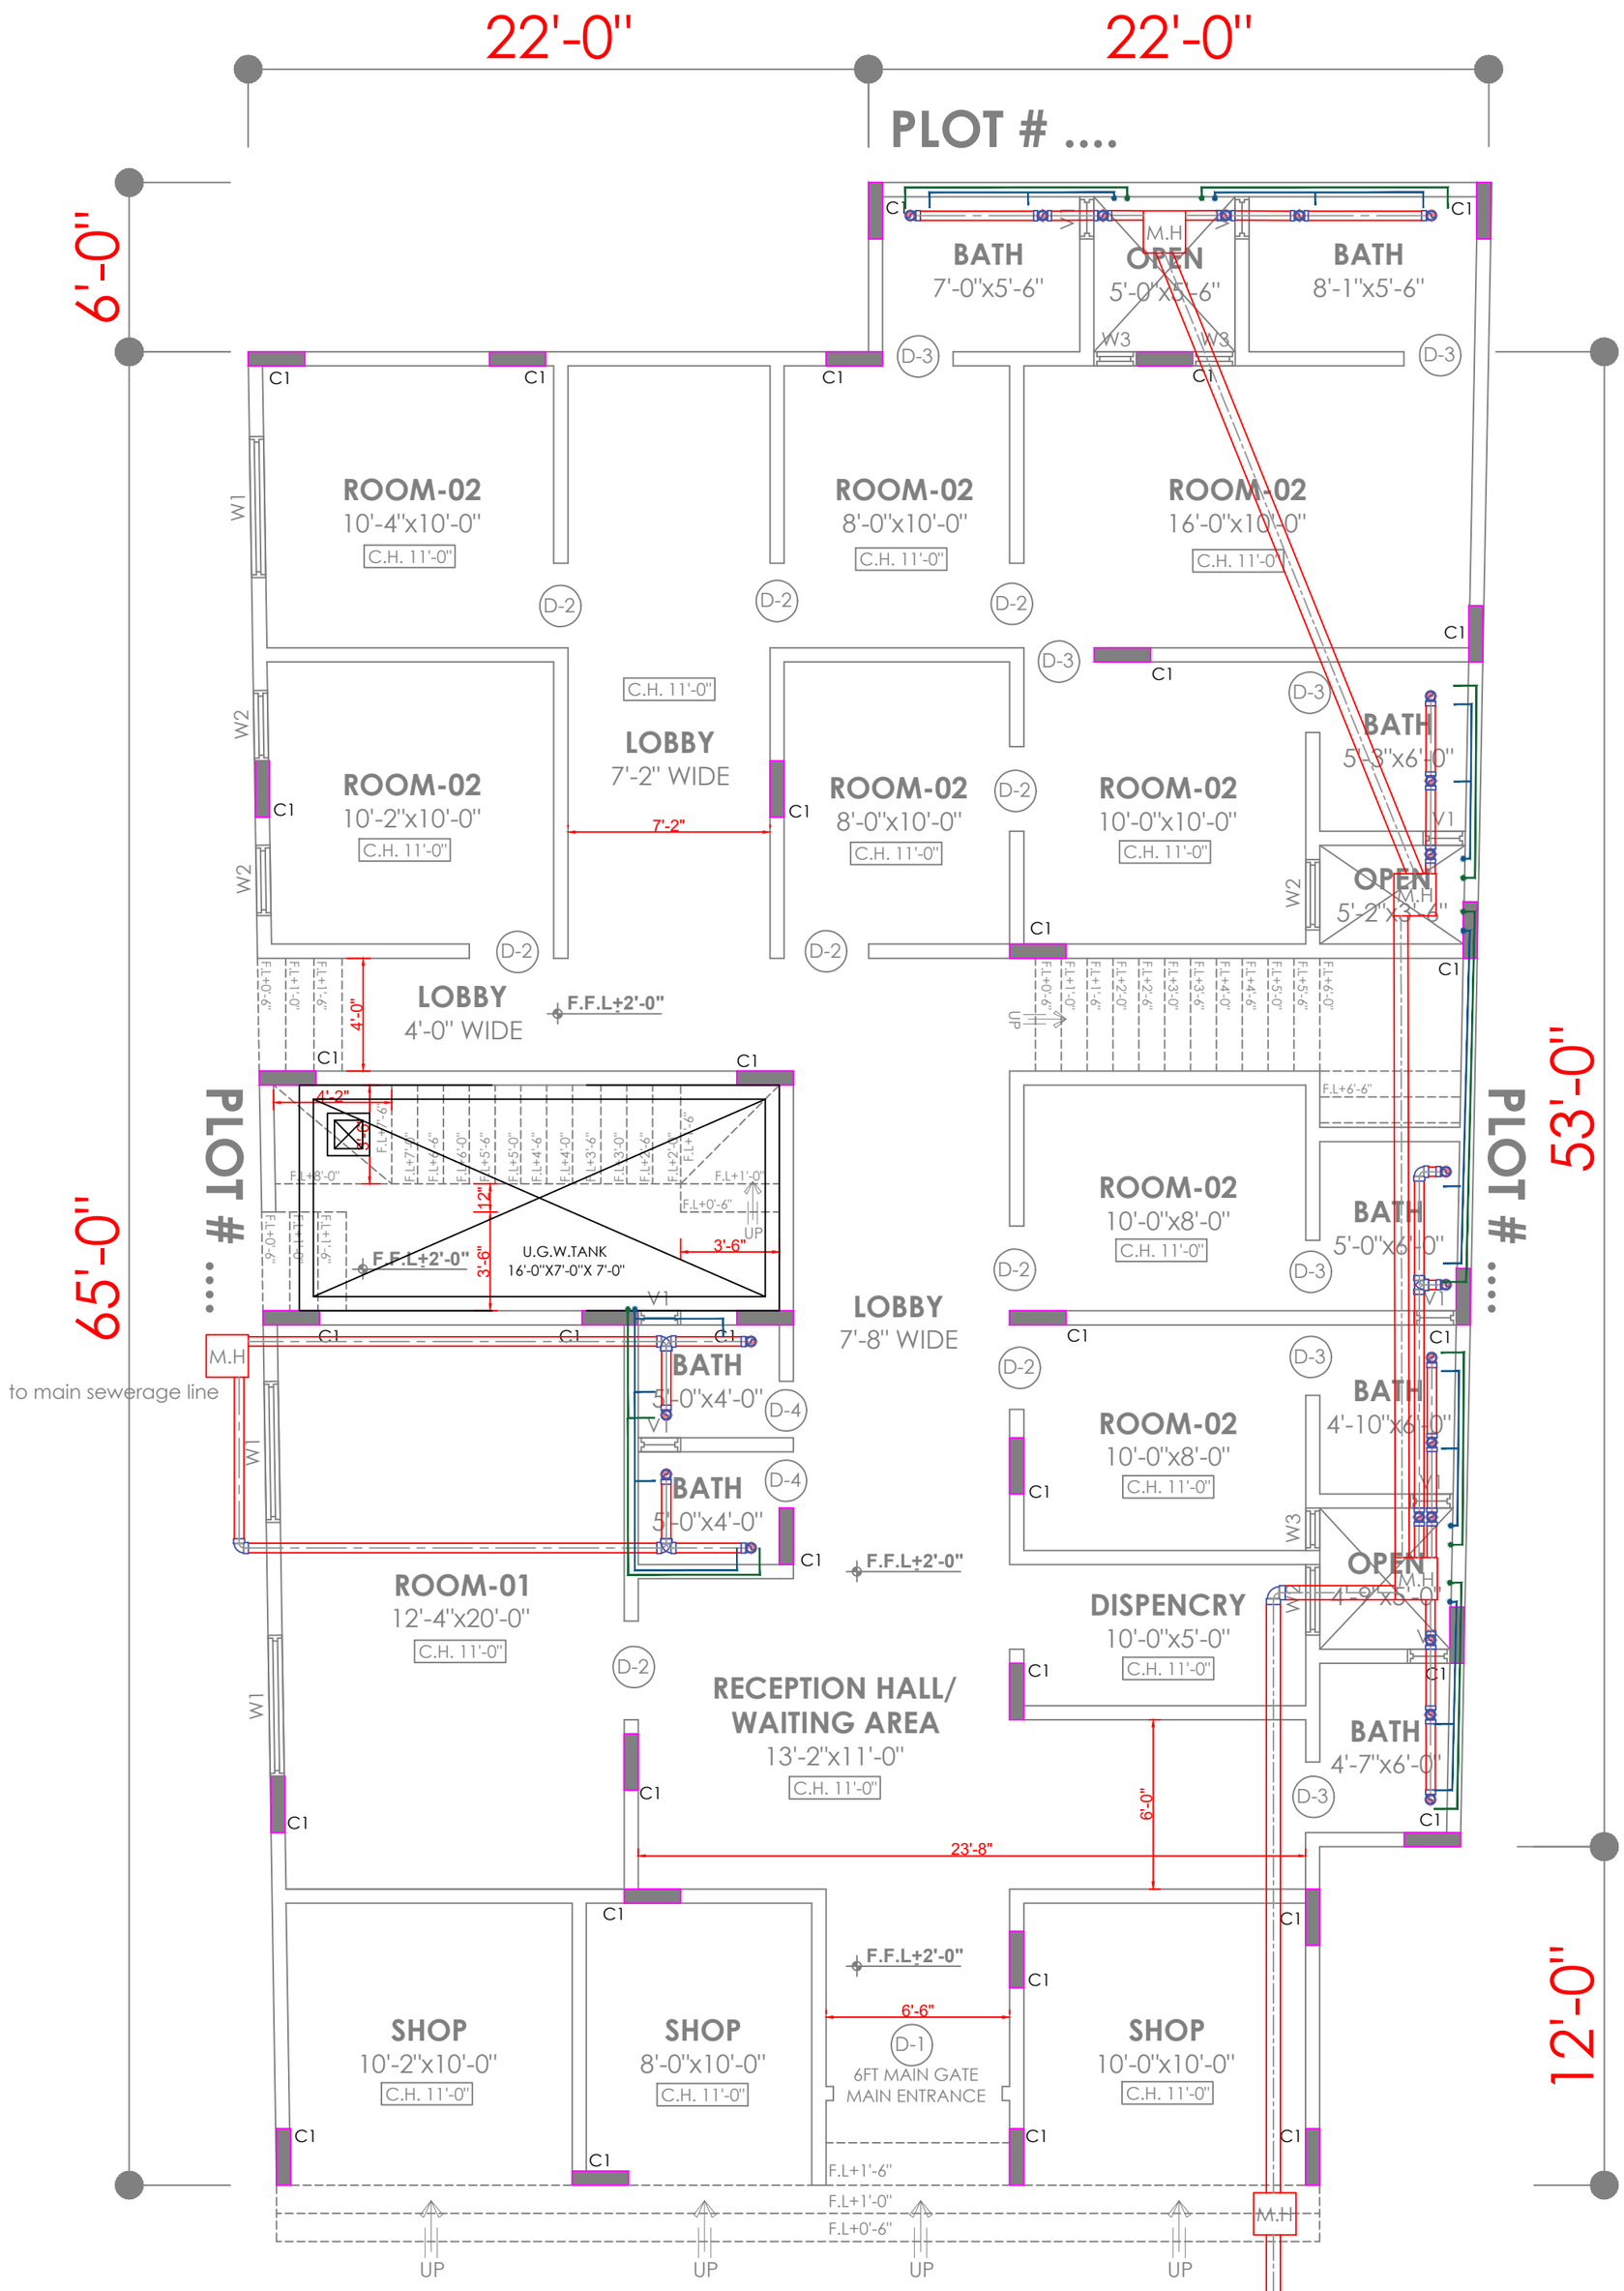

1 GROUND FLOOR PLAN
AR-01

GENERAL NOTES:

1. THE COPYRIGHT OF THIS DRAWING IS VESTED IN YourSpreadsheets AND IT MAY NOT BE REPRODUCED IN WHOLE OR PART OR USED FOR THE MANUFACTURE OF ANY ARTICLE WITHOUT THE EXPRESS PERMISSION OF THE COPYRIGHT HOLDERS.
2. WORK TO FIGURED DIMENSIONS ONLY.
3. THIS DRAWING IS TO BE READ IN CONJUNCTION WITH ALL RELEVANT ARCHITECT'S, SERVICE ENGINEER'S AND YourSpreadsheets DRAWINGS .

ALL DRWAING ARE THE PROPOERTY OF THE DESIGNER & THEY ARE NOT TO BE REPRODUCED IN WHOLE OR IN PART WITHOUT WRITTEN CONSENT FROM THE DESIGN WING
CONTRACTOR TO CHECK &VERIFY ALL DIMENSIONS BEFORE COMMENCING WORK & TO REPORT ANY DISCREPANCIES TO THE DESIGN WING.
DO NOT SCALE DRAWINGS.
ALL CONSTRUCTION TO BE ACCORDING TO BEST COMMON PRACTICE.

REV:	DESCRIPTION:	BY:	DATE:
A	ARCHITECTURE DRAWING	----	25-12-25
B	STRUCTURE DRAWING	----	27-12-25

PROJECT NAME:
300 SQ.YARD HOUSE ARCHITECTURE DRAWING

SIGNATURE BY:

DRAWING TITLE:
ARCHITECTURAL DRAWING

DRAWN BY: MUDASSIR
CHECKED BY: M.SHEHERYAR
APPROVED BY: M.SHEHERYAR
DATE: 27-DEC-2025

CLIENT
MR. ROHAN
KARACHI...

DESIGNED BY:-

E.D.C.O
ENGINEERING DESIGNING CONSTRUCTION OFFICIAL
ARCHITECT| PLANNERS| ENGINEERS| INTERIOR| B.O.Q| EXTERIOR| CONSULT| STRUCTURE DESIGN| PLANNING| LAND SURVEY| CONSTRUCTION| 3D ANIMATION VIDEO| RENOVATION|
MUHAMMAD SHEHERYAR
CONTACT- 0312-2118445|D.H.A PHASE VII

PROJECT NO: AR-7590
SCALE: 1/8"=1'-0"
SHEET SIZE: A3
DRAWING NO: ARC
SHEET NO ----------
REVISION: YES
UNIT: INCHES&FEET

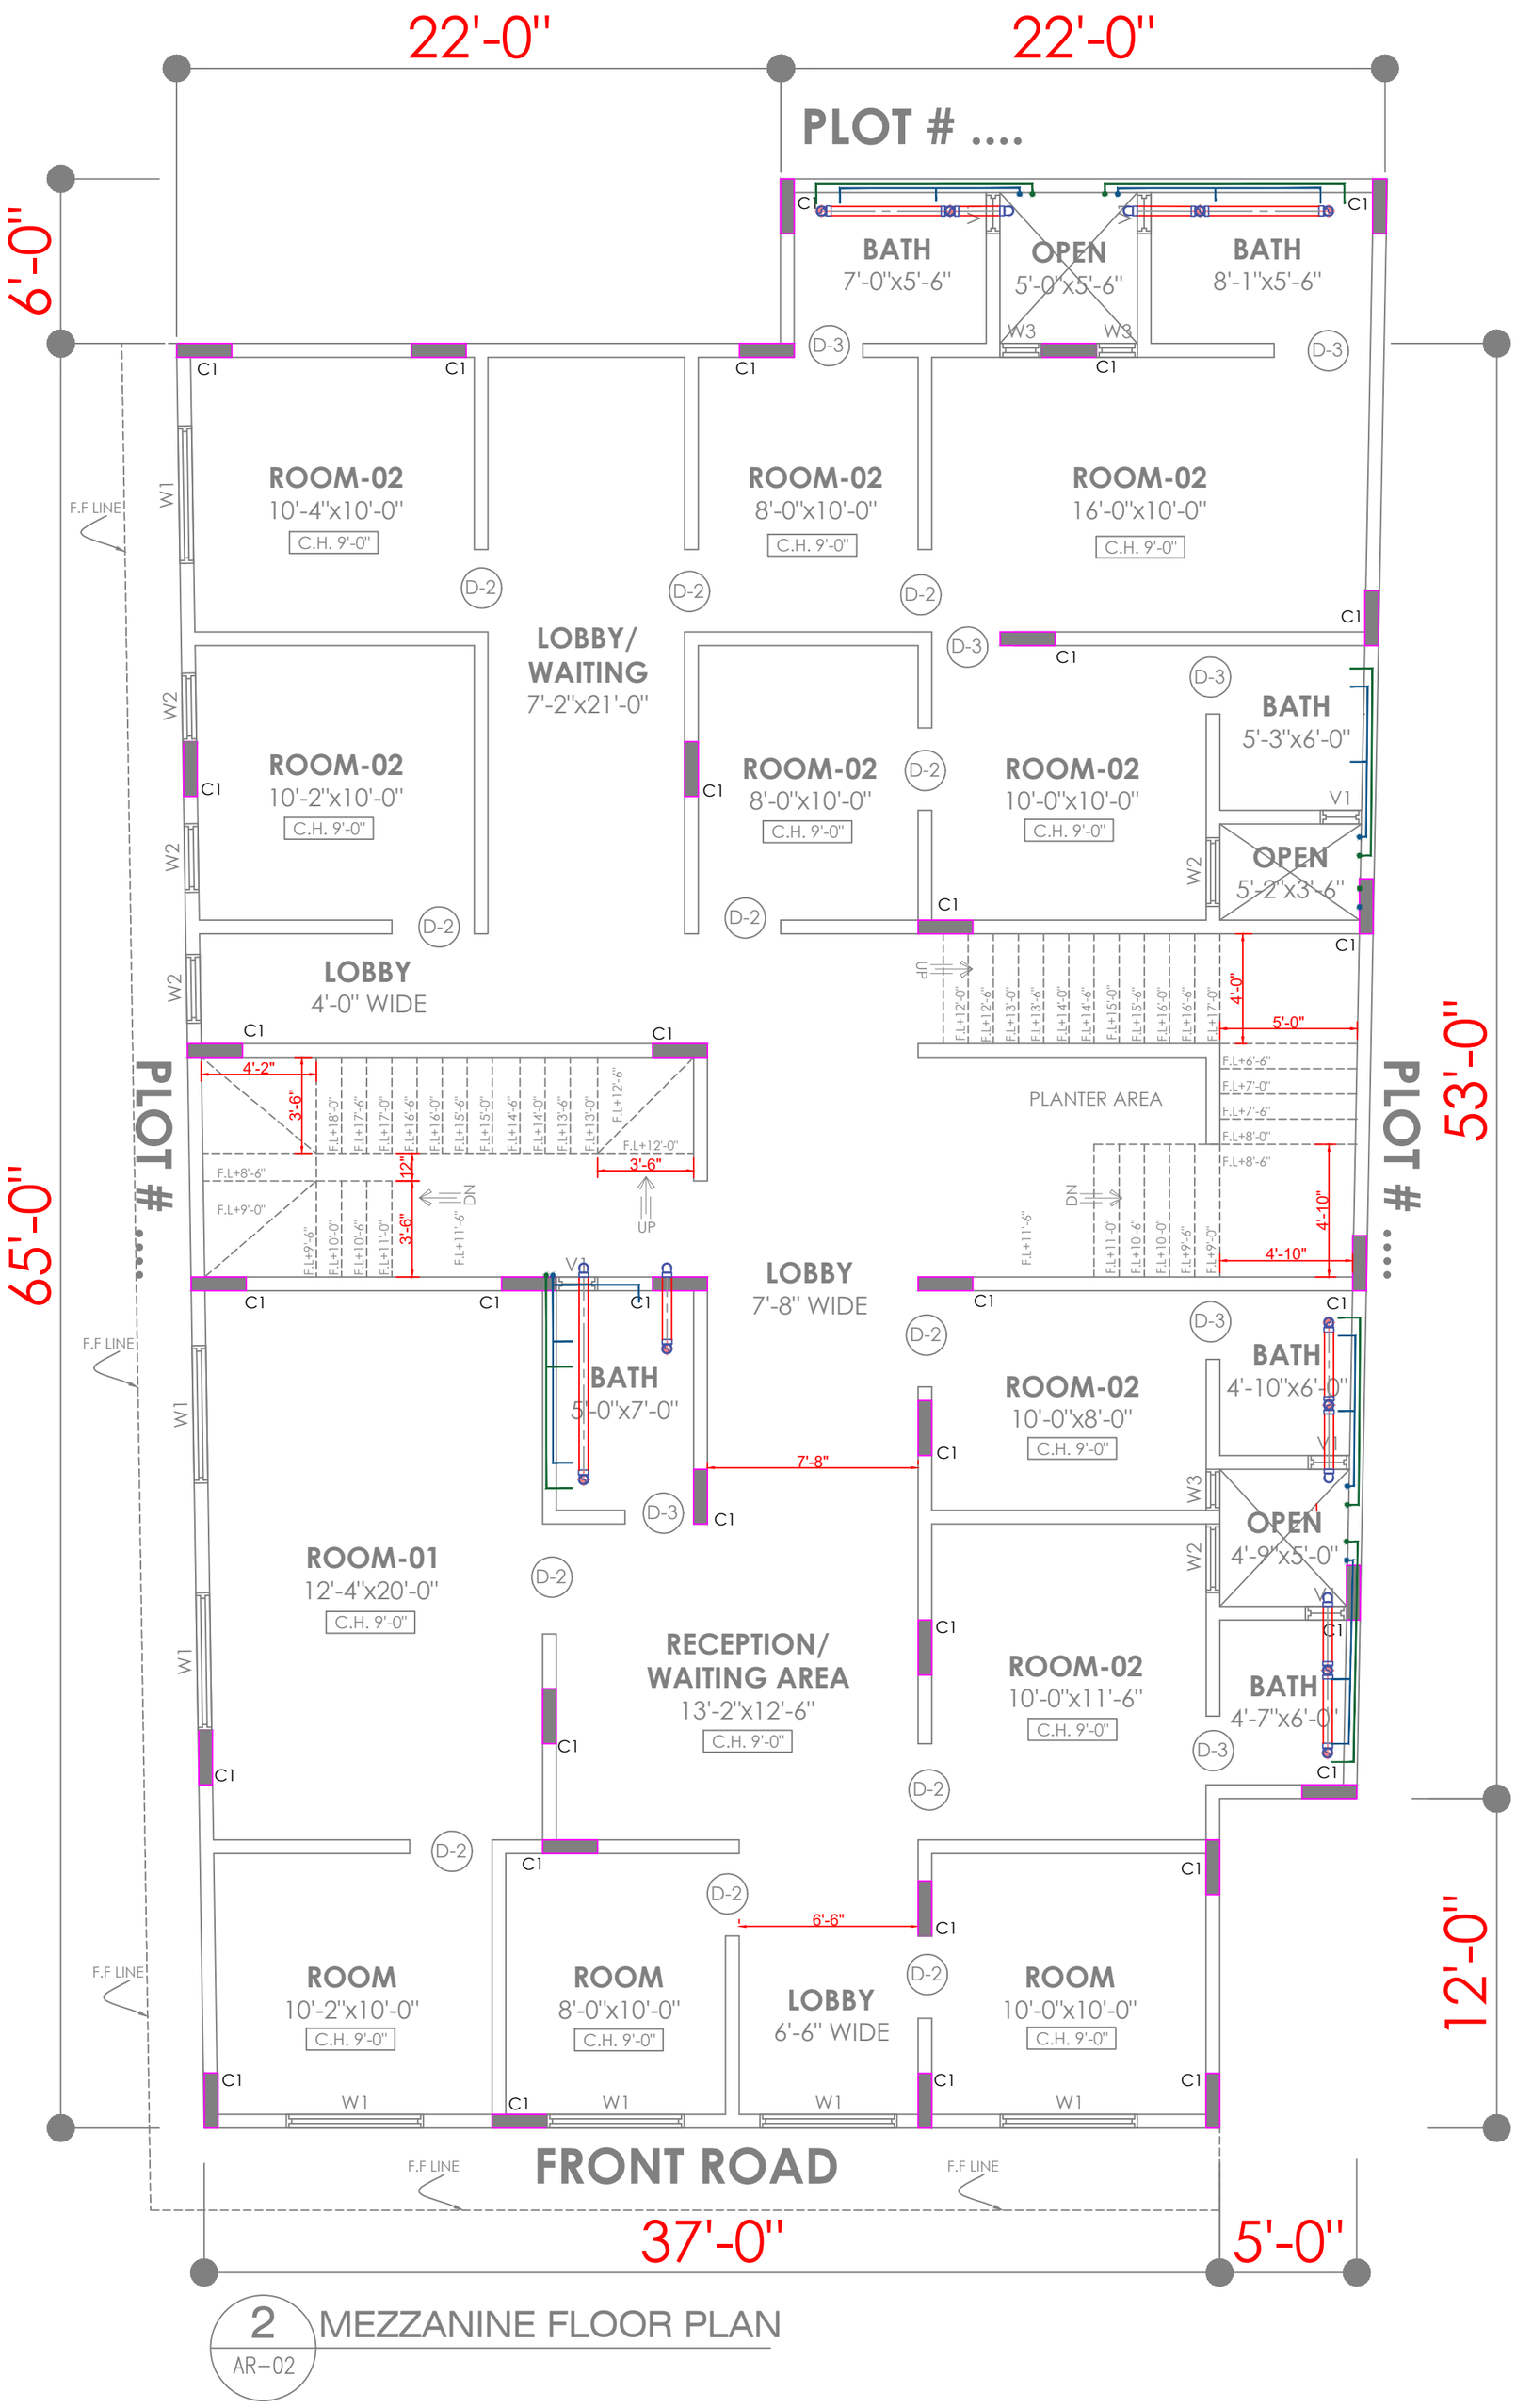

2 MEZZANINE FLOOR PLAN
AR–02

GENERAL NOTES:

1. THE COPYRIGHT OF THIS DRAWING IS VESTED IN YourSpreadsheets AND IT MAY NOT BE REPRODUCED IN WHOLE OR PART OR USED FOR THE MANUFACTURE OF ANY ARTICLE WITHOUT THE EXPRESS PERMISSION OF THE COPYRIGHT HOLDERS.
2. WORK TO FIGURED DIMENSIONS ONLY.
3. THIS DRAWING IS TO BE READ IN CONJUNCTION WITH ALL RELEVANT ARCHITECT'S, SERVICE ENGINEER'S AND YourSpreadsheets DRAWINGS .

ALL DRWAING ARE THE PROPOERTY OF THE DESIGNER & THEY ARE NOT TO BE REPRODUCED IN WHOLE OR IN PART WITHOUT WRITTEN CONSENT FROM THE DESIGN WING
CONTRACTOR TO CHECK &VERIFY ALL DIMENSIONS BEFORE COMMENCING WORK & TO REPORT ANY DISCREPANCIES TO THE DESIGN WING.
DO NOT SCALE DRAWINGS.
ALL CONSTRUCTION TO BE ACCORDING TO BEST COMMON PRACTICE.

REV:	DESCRIPTION:	BY:	DATE:
A	ARCHITECTURE DRAWING	----	25-12-25
B	STRUCTURE DRAWING	----	27-12-25

PROJECT NAME:
300 SQ.YARD HOUSE ARCHITECTURE DRAWING

SIGNATURE BY:

DRAWING TITLE:
ARCHITECTURAL DRAWING

DRAWN BY: MUDASSIR
CHECKED BY: M.SHEHERYAR
APPROVED BY: M.SHEHERYAR
DATE: 27-DEC-2025

CLIENT
MR. ROHAN
KARACHI...

DESIGNED BY:-
E.D.C.O
ENGINEERING DESIGNING CONSTRUCTION OFFICIAL
ARCHITECT| PLANNERS| ENGINEERS| INTERIOR| B.O.Q| EXTERIOR| CONSULT| STRUCTURE DESIGN| PLANNING| LAND SURVEY| CONSTRUCTION| 3D ANIMATION VIDEO| RENOVATION|
MUHAMMAD SHEHERYAR
CONTACT- 0312-2118445|D.H.A PHASE VII

PROJECT NO: AR-7590
SCALE: 1/8"=1'-0"
SHEET SIZE: A3
DRAWING NO: ARC
SHEET NO ----------
REVISION: YES
UNIT: INCHES&FEET

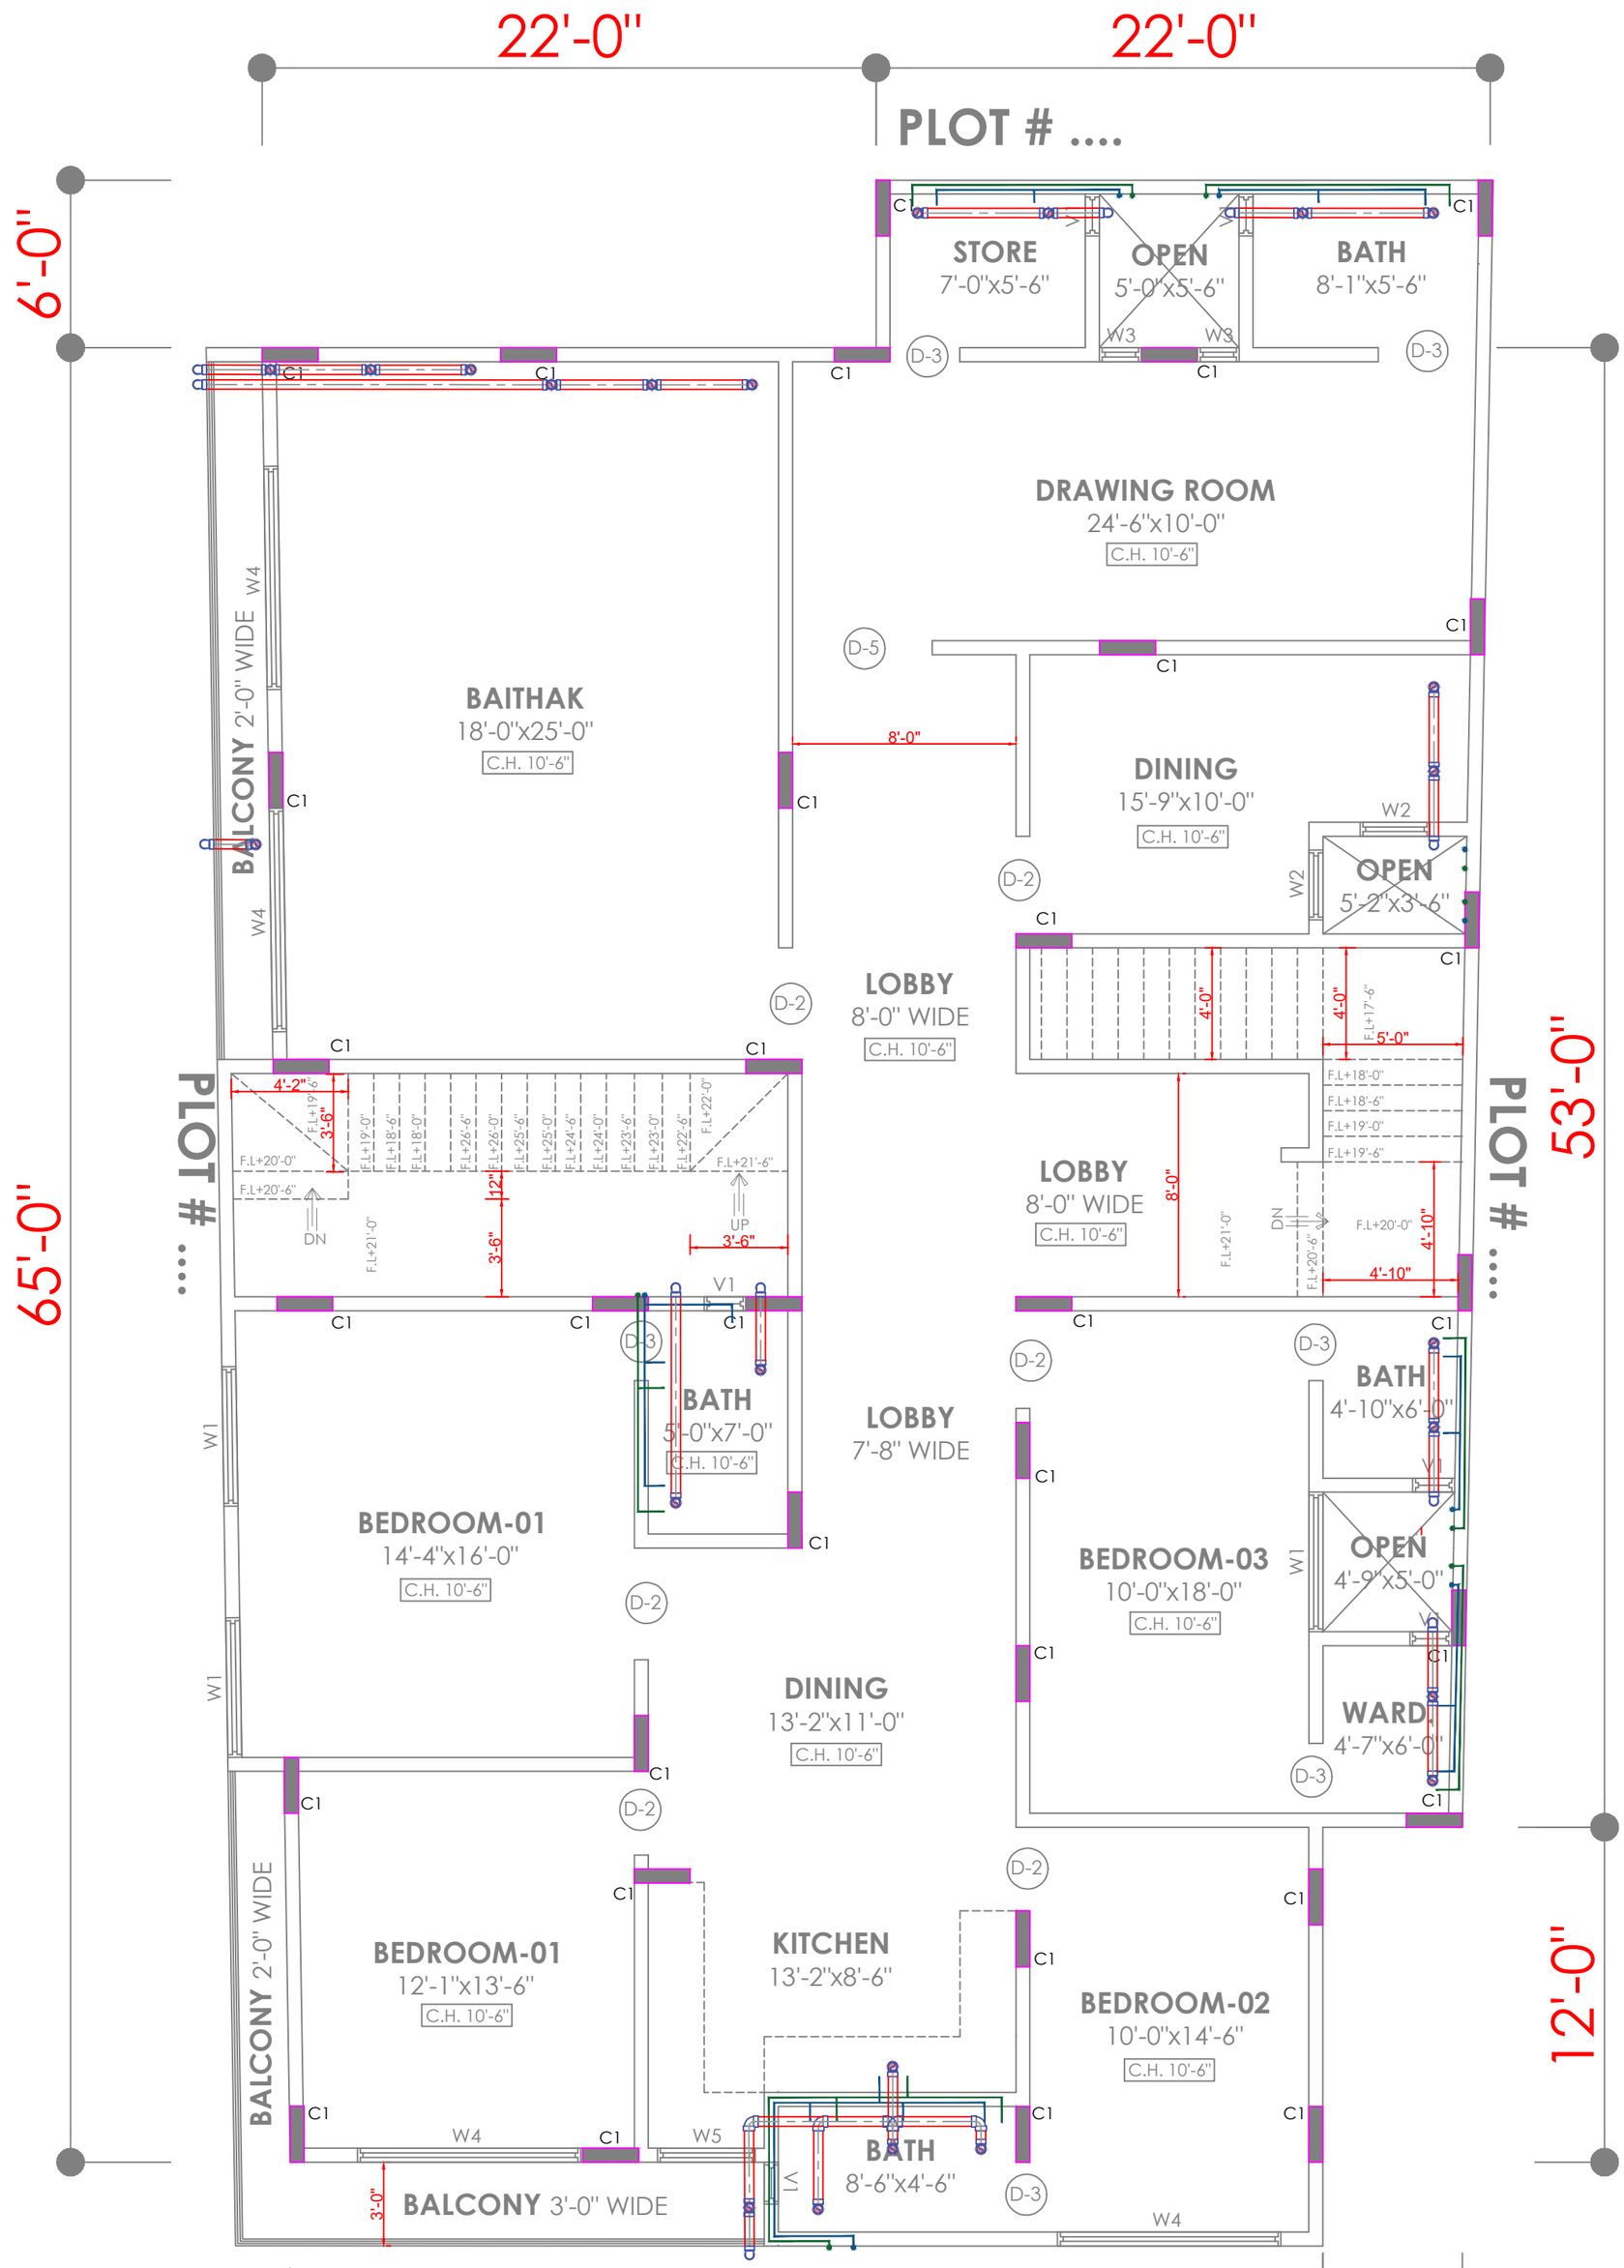

3 FIRST FLOOR PLAN
AR–03

GENERAL NOTES:

1. THE COPYRIGHT OF THIS DRAWING IS VESTED IN YourSpreadsheets AND IT MAY NOT BE REPRODUCED IN WHOLE OR PART OR USED FOR THE MANUFACTURE OF ANY ARTICLE WITHOUT THE EXPRESS PERMISSION OF THE COPYRIGHT HOLDERS.
2. WORK TO FIGURED DIMENSIONS ONLY.
3. THIS DRAWING IS TO BE READ IN CONJUNCTION WITH ALL RELEVANT ARCHITECT'S, SERVICE ENGINEER'S AND YourSpreadsheets DRAWINGS .

ALL DRWAING ARE THE PROPOERTY OF THE DESIGNER & THEY ARE NOT TO BE REPRODUCED IN WHOLE OR IN PART WITHOUT WRITTEN CONSENT FROM THE DESIGN WING
CONTRACTOR TO CHECK &VERIFY ALL DIMENSIONS BEFORE COMMENCING WORK & TO REPORT ANY DISCREPANCIES TO THE DESIGN WING.
DO NOT SCALE DRAWINGS.
ALL CONSTRUCTION TO BE ACCORDING TO BEST COMMON PRACTICE.

REV:	DESCRIPTION:	BY:	DATE:
A	ARCHITECTURE DRAWING	----	25-12-25
B	STRUCTURE DRAWING	----	27-12-25

PROJECT NAME:
300 SQ.YARD HOUSE ARCHITECTURE DRAWING

SIGNATURE BY:

DRAWING TITLE:
ARCHITECTURAL DRAWING

DRAWN BY:	CHECKED BY:
MUDASSIR	M.SHEHERYAR

APPROVED BY:	DATE:
M.SHEHERYAR	27-DEC-2025

CLIENT
MR. ROHAN
KARACHI...

DESIGNED BY:-

E.D.C.O
ENGINEERING DESIGNING CONSTRUCTION OFFICIAL
ARCHITECT| PLANNERS| ENGINEERS| INTERIOR| B.O.Q| EXTERIOR| CONSULT| STRUCTURE DESIGN| PLANNING| LAND SURVEY| CONSTRUCTION| 3D ANIMATION VIDEO| RENOVATION|
MUHAMMAD SHEHERYAR
CONTACT- 0312-2118445|D.H.A PHASE VII

PROJECT NO:	SCALE:	SHEET SIZE:
AR-7590	1/8"=1'-0"	A3

DRAWING NO:	SHEET NO
ARC	----------

REVISION: YES

UNIT: INCHES&FEET

S E W N

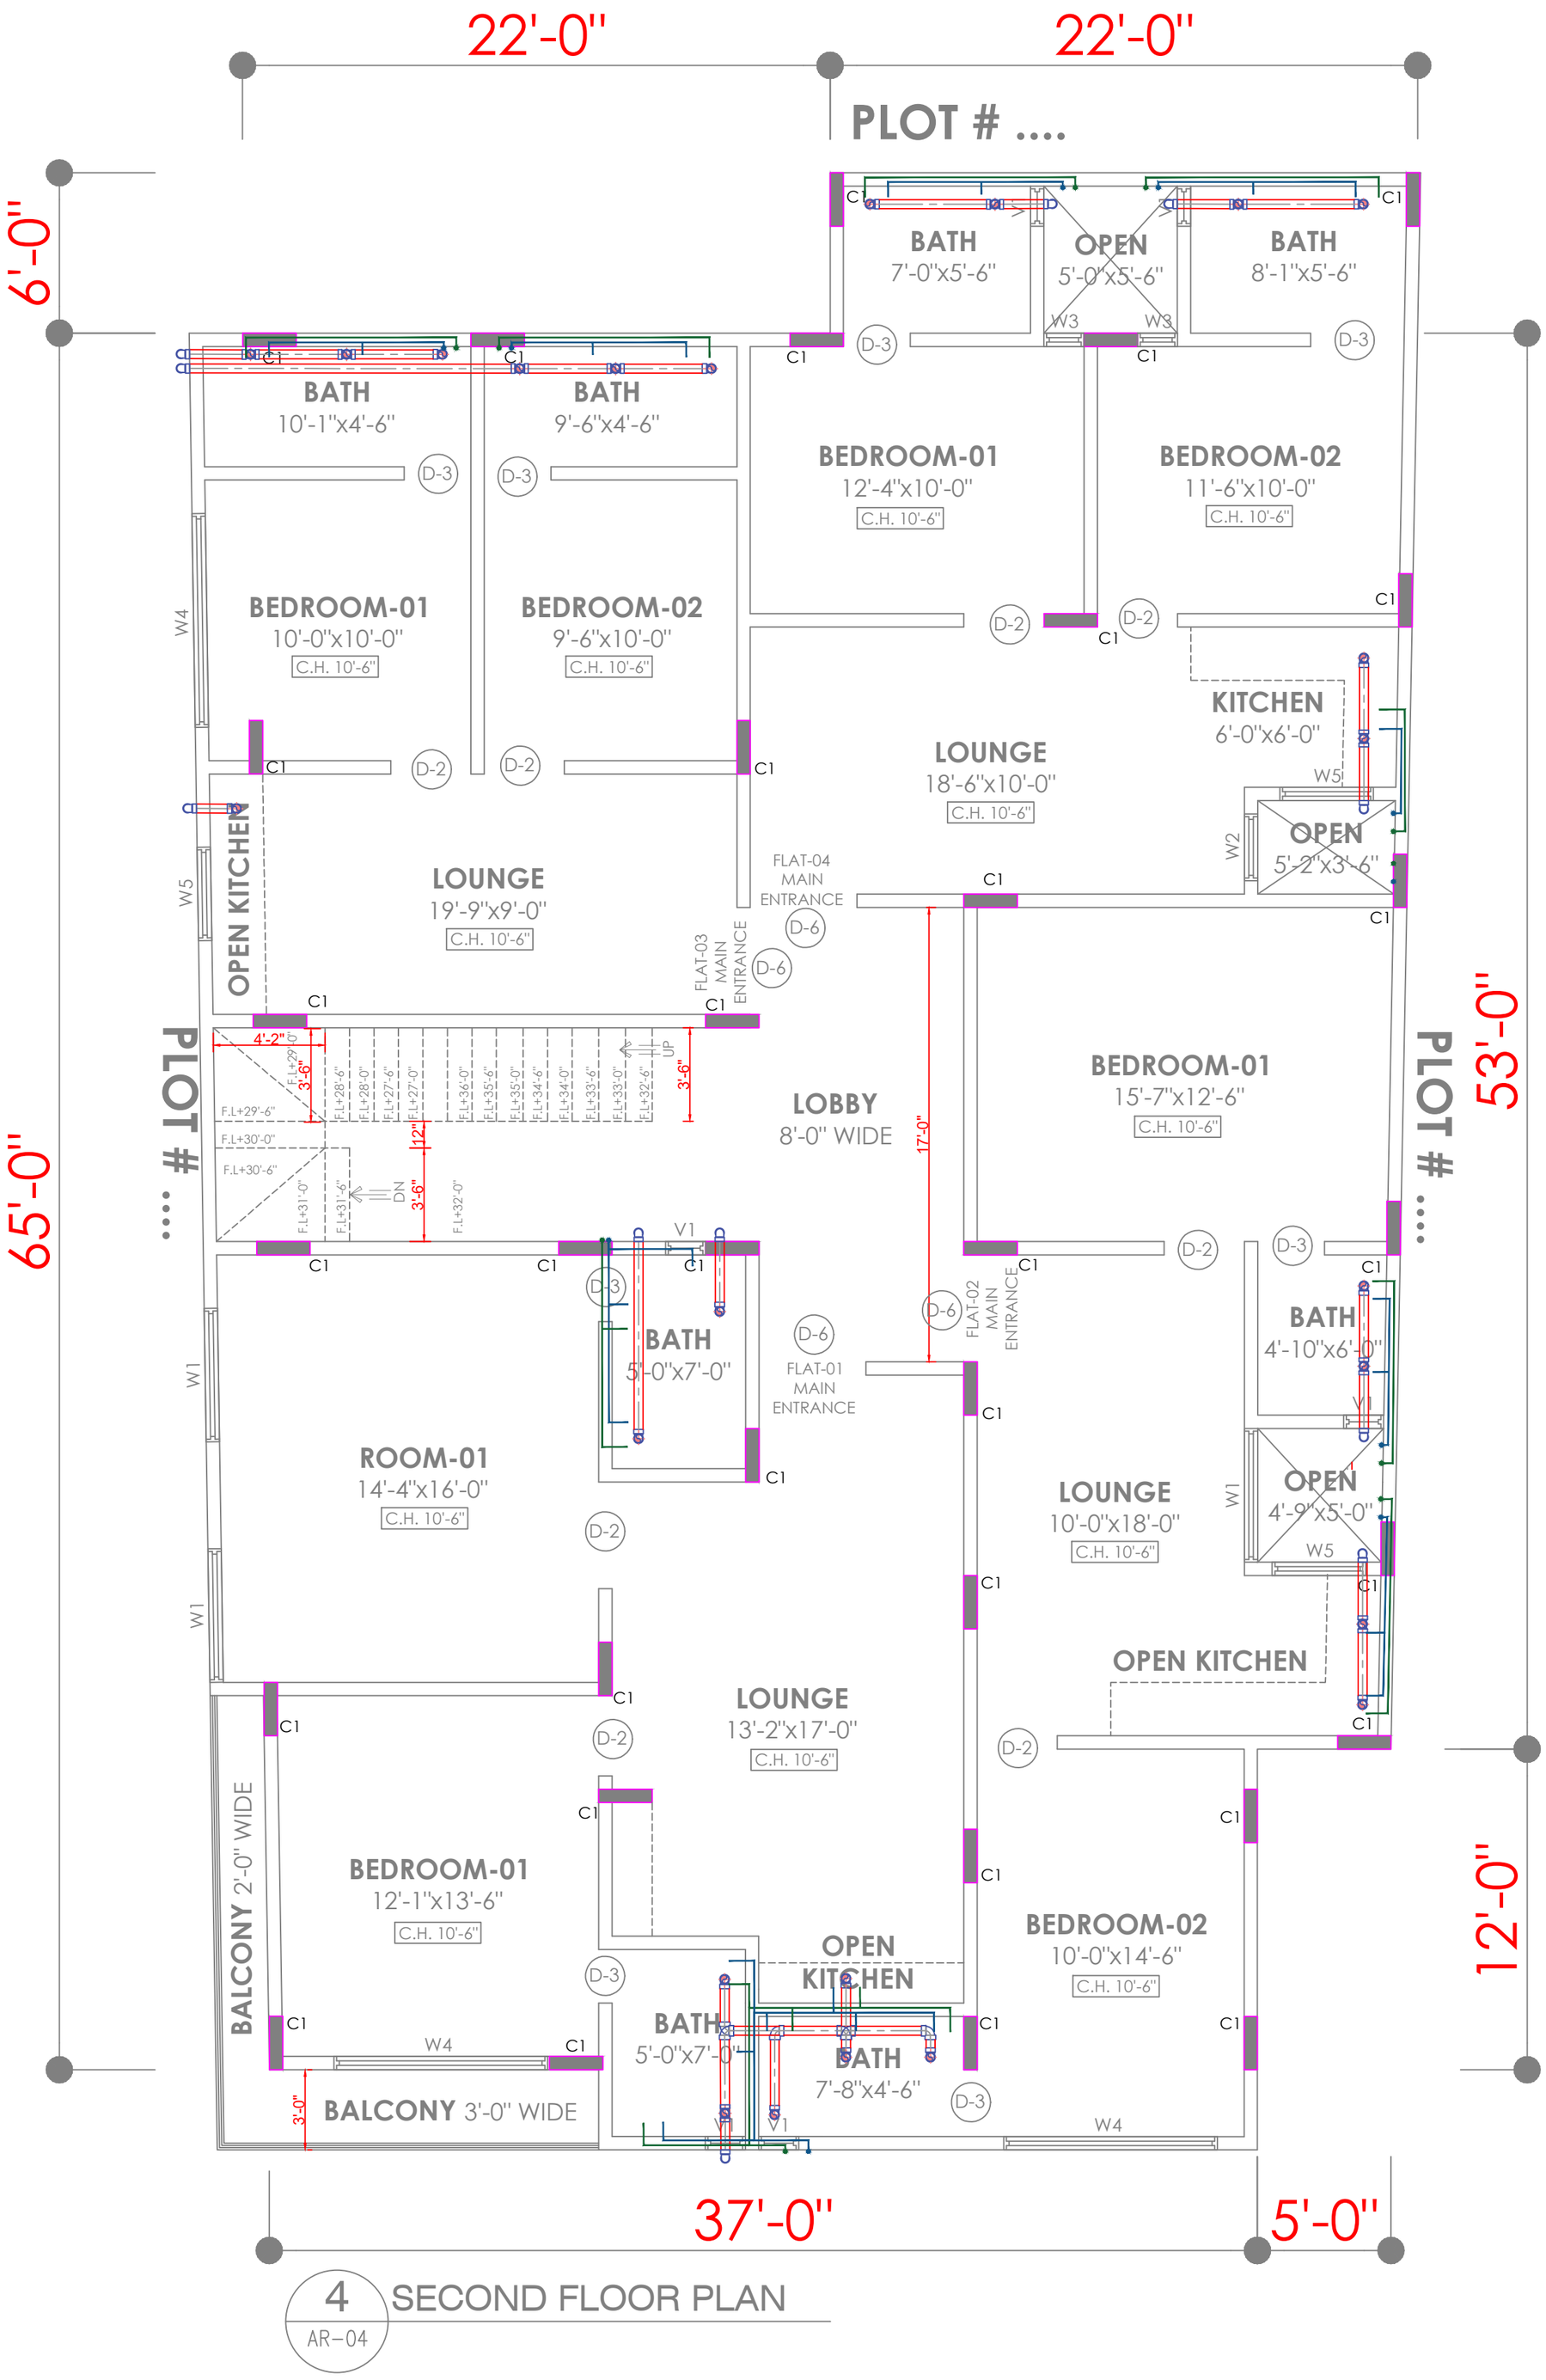

4 SECOND FLOOR PLAN
AR–04

GENERAL NOTES:

1. THE COPYRIGHT OF THIS DRAWING IS VESTED IN YourSpreadsheets AND IT MAY NOT BE REPRODUCED IN WHOLE OR PART OR USED FOR THE MANUFACTURE OF ANY ARTICLE WITHOUT THE EXPRESS PERMISSION OF THE COPYRIGHT HOLDERS.
2. WORK TO FIGURED DIMENSIONS ONLY.
3. THIS DRAWING IS TO BE READ IN CONJUNCTION WITH ALL RELEVANT ARCHITECT'S, SERVICE ENGINEER'S AND YourSpreadsheets DRAWINGS .

ALL DRWAING ARE THE PROPOERTY OF THE DESIGNER & THEY ARE NOT TO BE REPRODUCED IN WHOLE OR IN PART WITHOUT WRITTEN CONSENT FROM THE DESIGN WING
CONTRACTOR TO CHECK &VERIFY ALL DIMENSIONS BEFORE COMMENCING WORK & TO REPORT ANY DISCREPANCIES TO THE DESIGN WING.
DO NOT SCALE DRAWINGS.
ALL CONSTRUCTION TO BE ACCORDING TO BEST COMMON PRACTICE.

REV:	DESCRIPTION:	BY:	DATE:
A	ARCHITECTURE DRAWING	----	25-12-25
B	STRUCTURE DRAWING	----	27-12-25

PROJECT NAME:
300 SQ.YARD HOUSE ARCHITECTURE DRAWING

SIGNATURE BY:

DRAWING TITLE:
ARCHITECTURAL DRAWING

DRAWN BY: MUDASSIR
CHECKED BY: M.SHEHERYAR
APPROVED BY: M.SHEHERYAR
DATE: 27-DEC-2025

CLIENT
MR. ROHAN
KARACHI...

DESIGNED BY:-

E.D.C.O
ENGINEERING DESIGNING CONSTRUCTION OFFICIAL
ARCHITECT| PLANNERS| ENGINEERS| INTERIOR| B.O.Q| EXTERIOR| CONSULT| STRUCTURE DESIGN| PLANNING| LAND SURVEY| CONSTRUCTION| 3D ANIMATION VIDEO| RENOVATION|
MUHAMMAD SHEHERYAR
CONTACT- 0312-2118445|D.H.A PHASE VII

PROJECT NO: AR-7590
SCALE: 1/8"=1'-0"
SHEET SIZE: A3
DRAWING NO: ARC
SHEET NO ----------
REVISION: YES
UNIT: INCHES&FEET

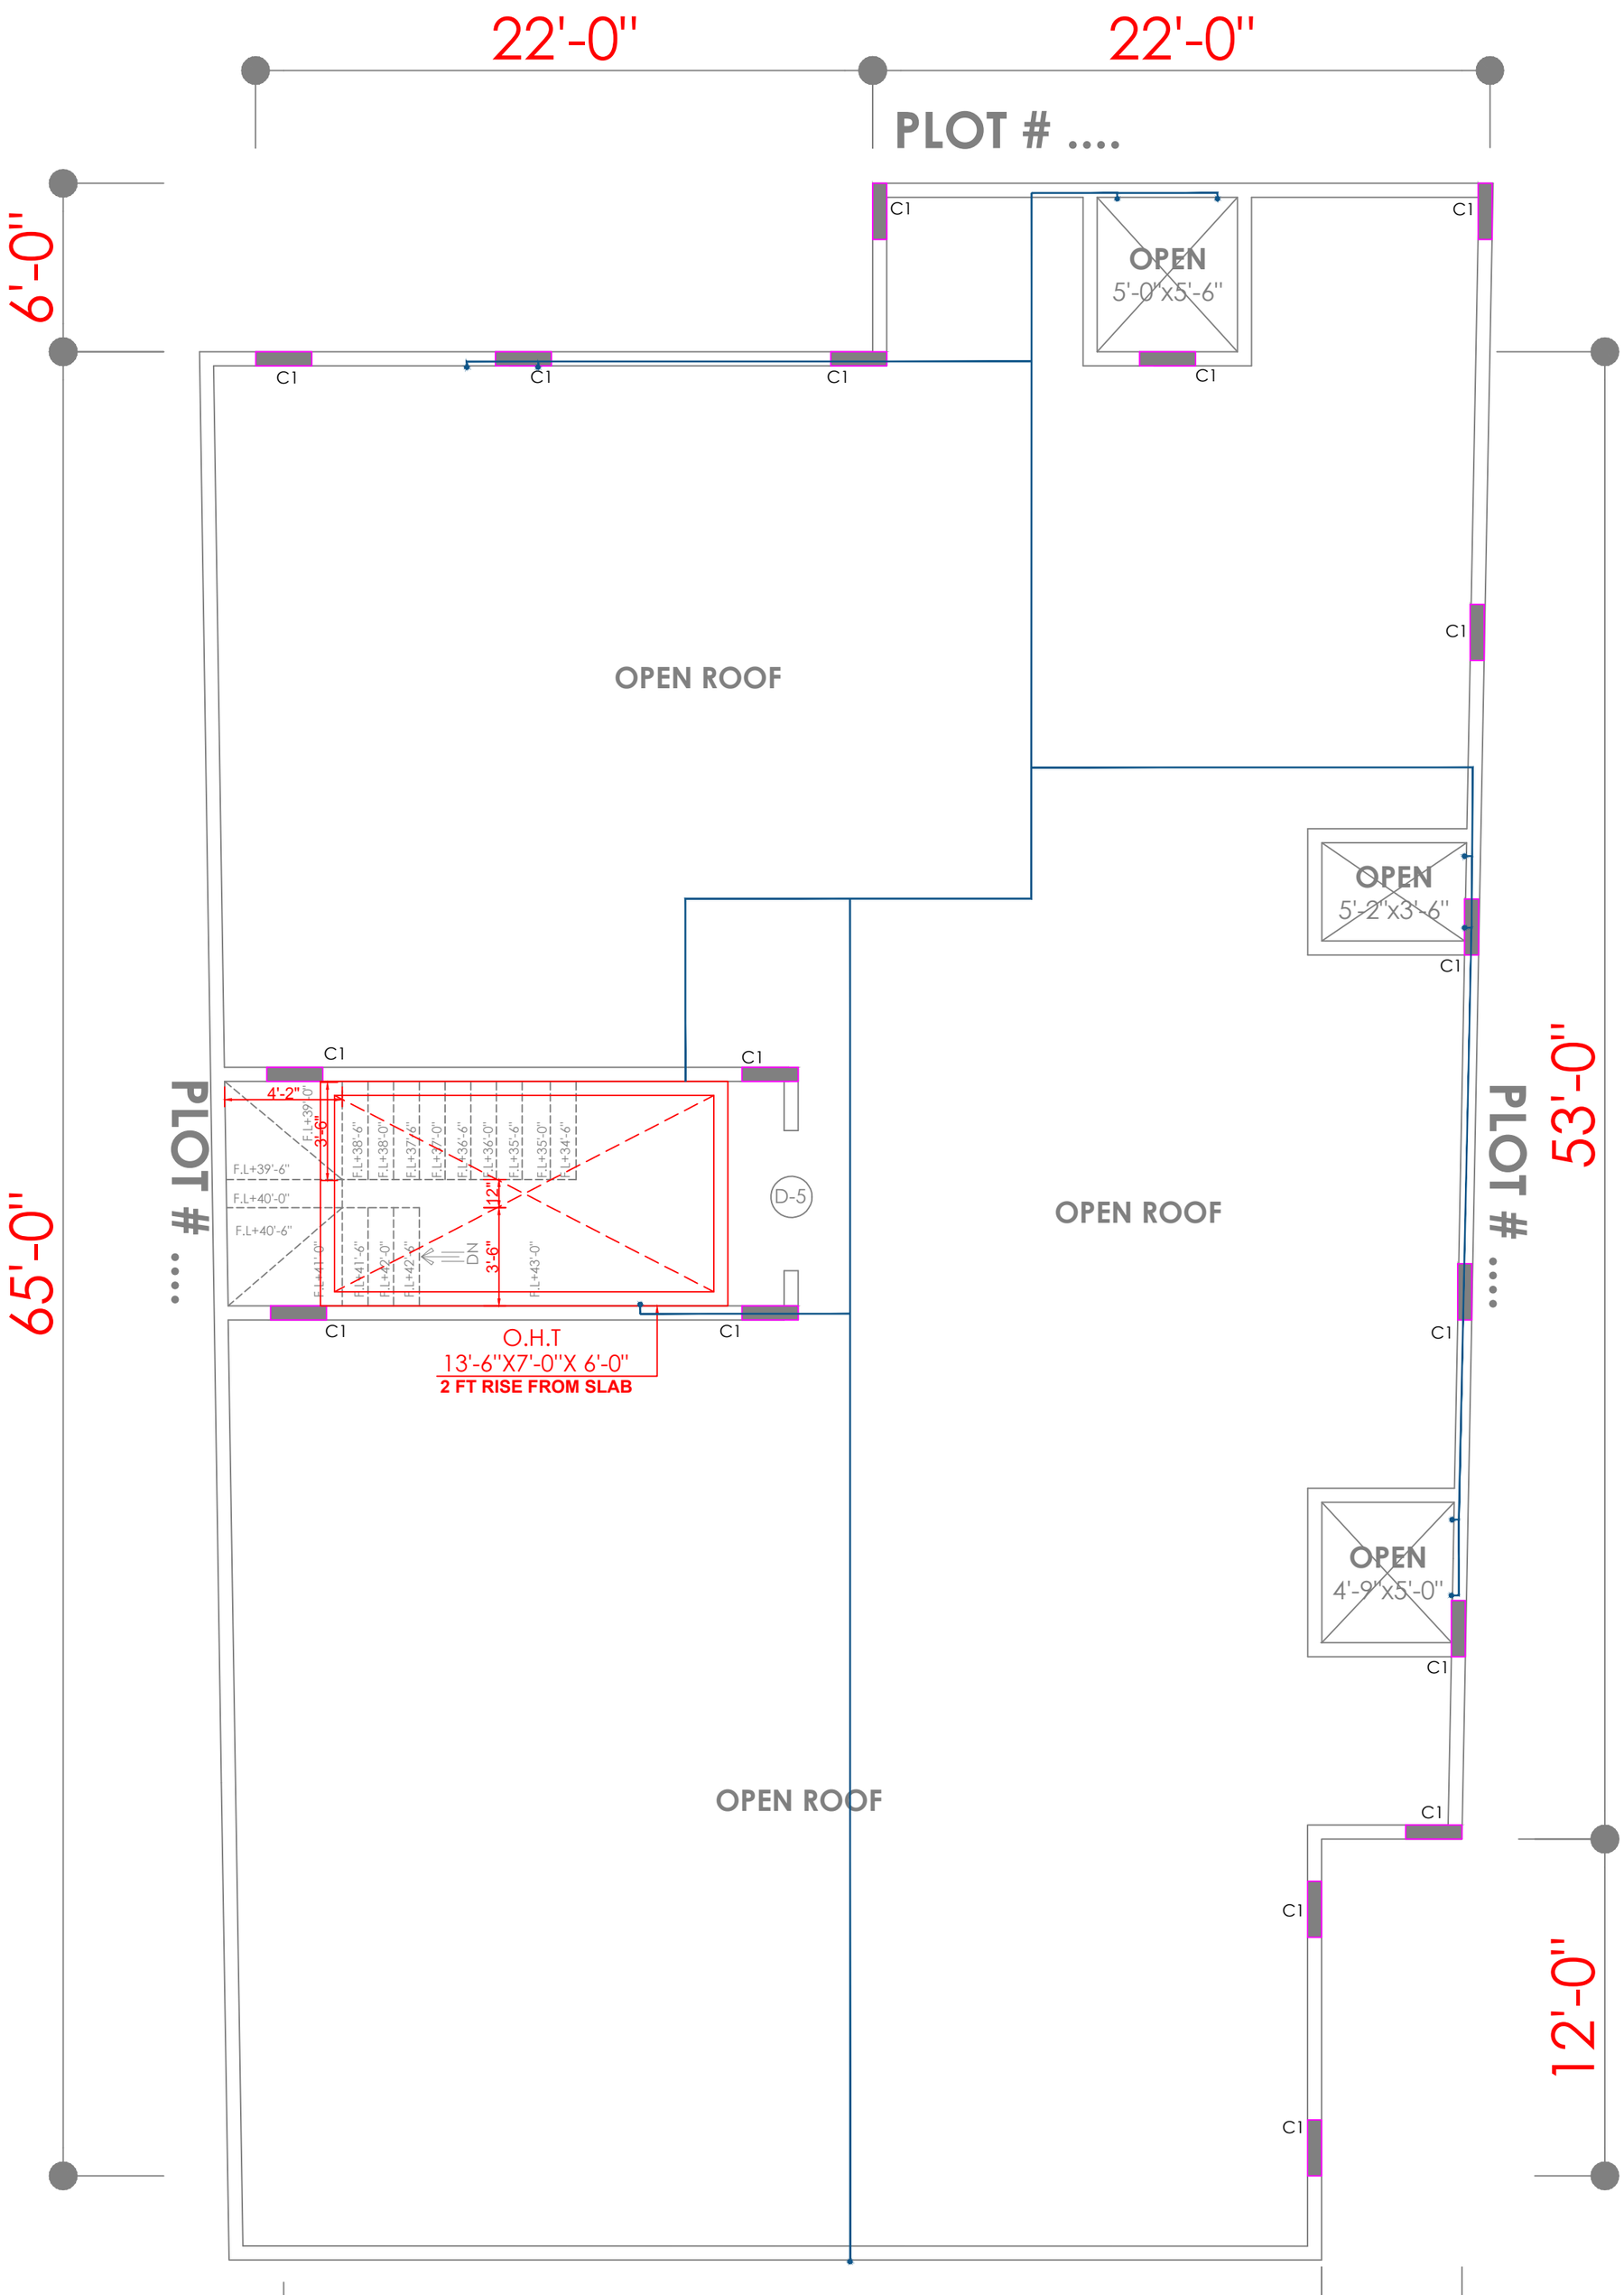

5 ROOF TOP PLAN
AR–05

GENERAL NOTES:

1. THE COPYRIGHT OF THIS DRAWING IS VESTED IN YourSpreadsheets AND IT MAY NOT BE REPRODUCED IN WHOLE OR PART OR USED FOR THE MANUFACTURE OF ANY ARTICLE WITHOUT THE EXPRESS PERMISSION OF THE COPYRIGHT HOLDERS.
2. WORK TO FIGURED DIMENSIONS ONLY.
3. THIS DRAWING IS TO BE READ IN CONJUNCTION WITH ALL RELEVANT ARCHITECT'S, SERVICE ENGINEER'S AND YourSpreadsheets DRAWINGS .

ALL DRWAING ARE THE PROPOERTY OF THE DESIGNER & THEY ARE NOT TO BE REPRODUCED IN WHOLE OR IN PART WITHOUT WRITTEN CONSENT FROM THE DESIGN WING

CONTRACTOR TO CHECK &VERIFY ALL DIMENSIONS BEFORE COMMENCING WORK & TO REPORT ANY DISCREPANCIES TO THE DESIGN WING.

DO NOT SCALE DRAWINGS.

ALL CONSTRUCTION TO BE ACCORDING TO BEST COMMON PRACTICE.

REV:	DESCRIPTION:	BY:	DATE:
A	ARCHITECTURE DRAWING	----	25-12-25
B	STRUCTURE DRAWING	----	27-12-25

PROJECT NAME:
300 SQ.YARD HOUSE ARCHITECTURE DRAWING

SIGNATURE BY:

DRAWING TITLE:
ARCHITECTURAL DRAWING

DRAWN BY: MUDASSIR
CHECKED BY: M.SHEHERYAR
APPROVED BY: M.SHEHERYAR
DATE: 27-DEC-2025

CLIENT
MR. ROHAN
KARACHI...

DESIGNED BY:-
E.D.C.O
ENGINEERING DESIGNING CONSTRUCTION OFFICIAL
ARCHITECT| PLANNERS| ENGINEERS| INTERIOR| B.O.Q| EXTERIOR| CONSULT| STRUCTURE DESIGN| PLANNING| LAND SURVEY| CONSTRUCTION| 3D ANIMATION VIDEO| RENOVATION|
MUHAMMAD SHEHERYAR
CONTACT- 0312-2118445|D.H.A PHASE VII

PROJECT NO: AR-7590
SCALE: 1/8"=1'-0"
SHEET SIZE: A3
DRAWING NO: ARC
SHEET NO ----------
REVISION: YES
UNIT: INCHES&FEET

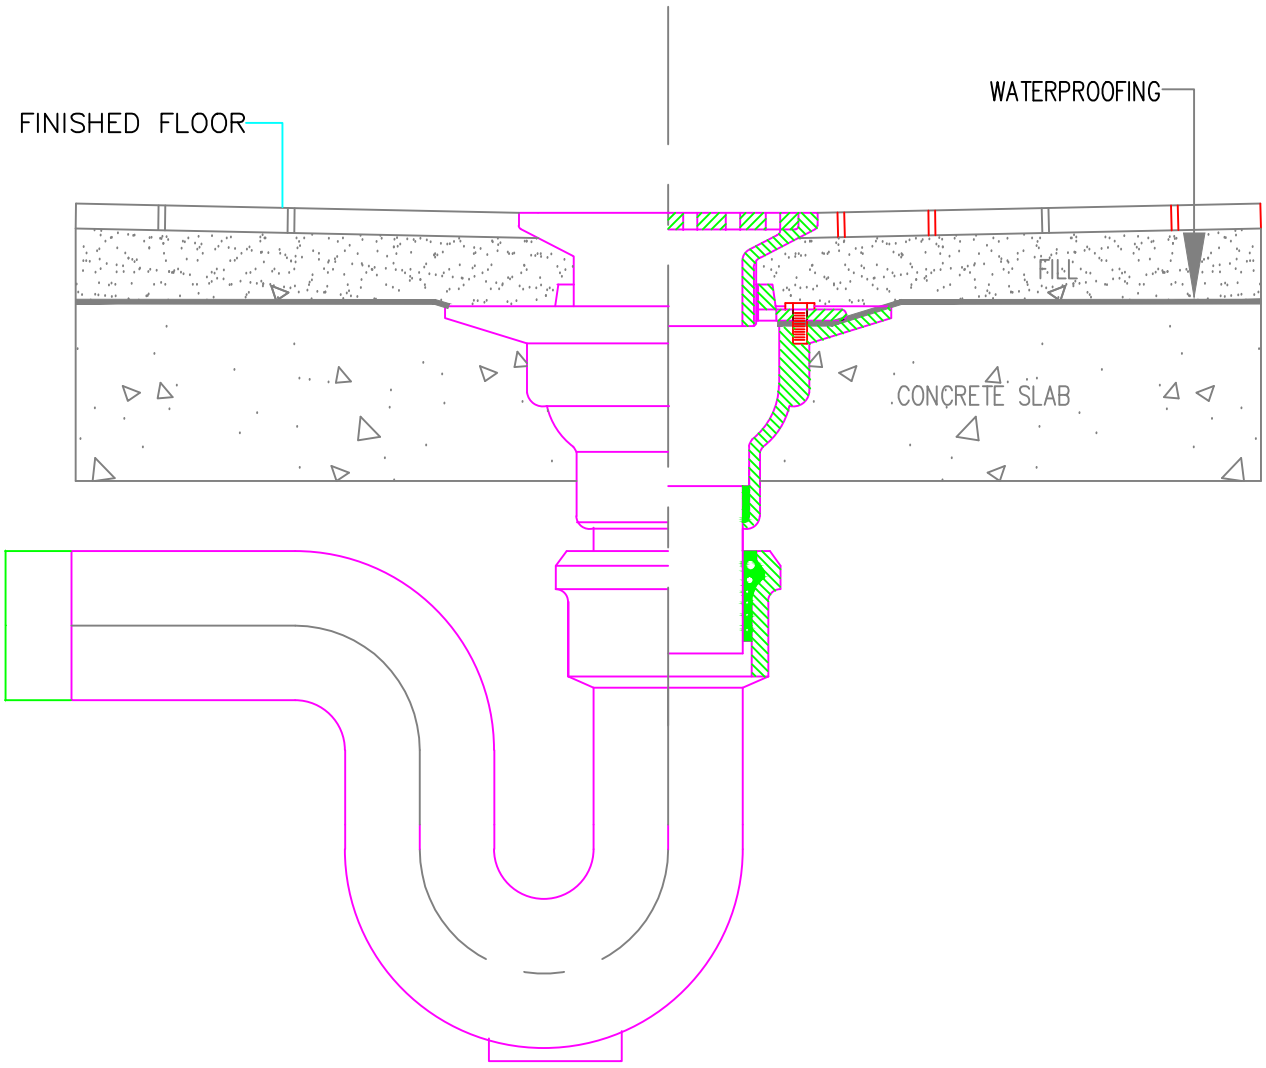

FLOOR DRAIN (MAID TOILET)

NOT TO SCALE

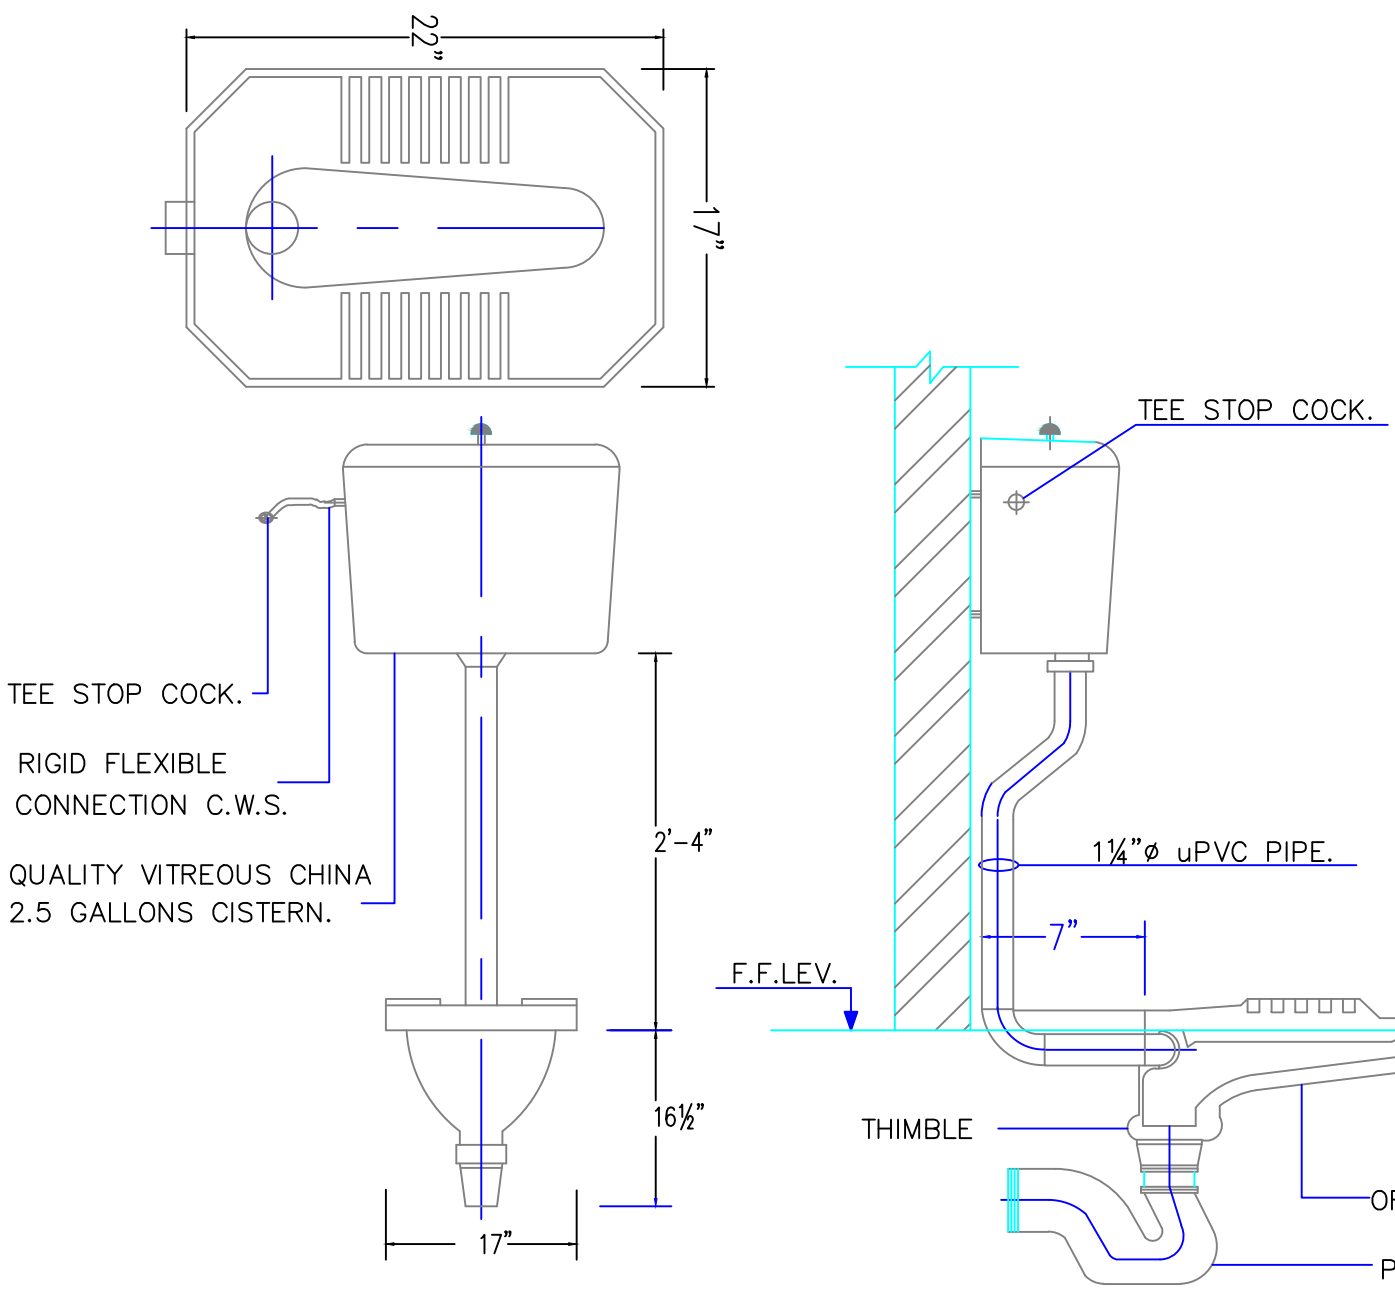

INDIAN WC INSTALLATION DETAIL

NOT TO SCALE

TRANSFER PUMP SET INSTALLATION DETAIL

NOT TO SCALE

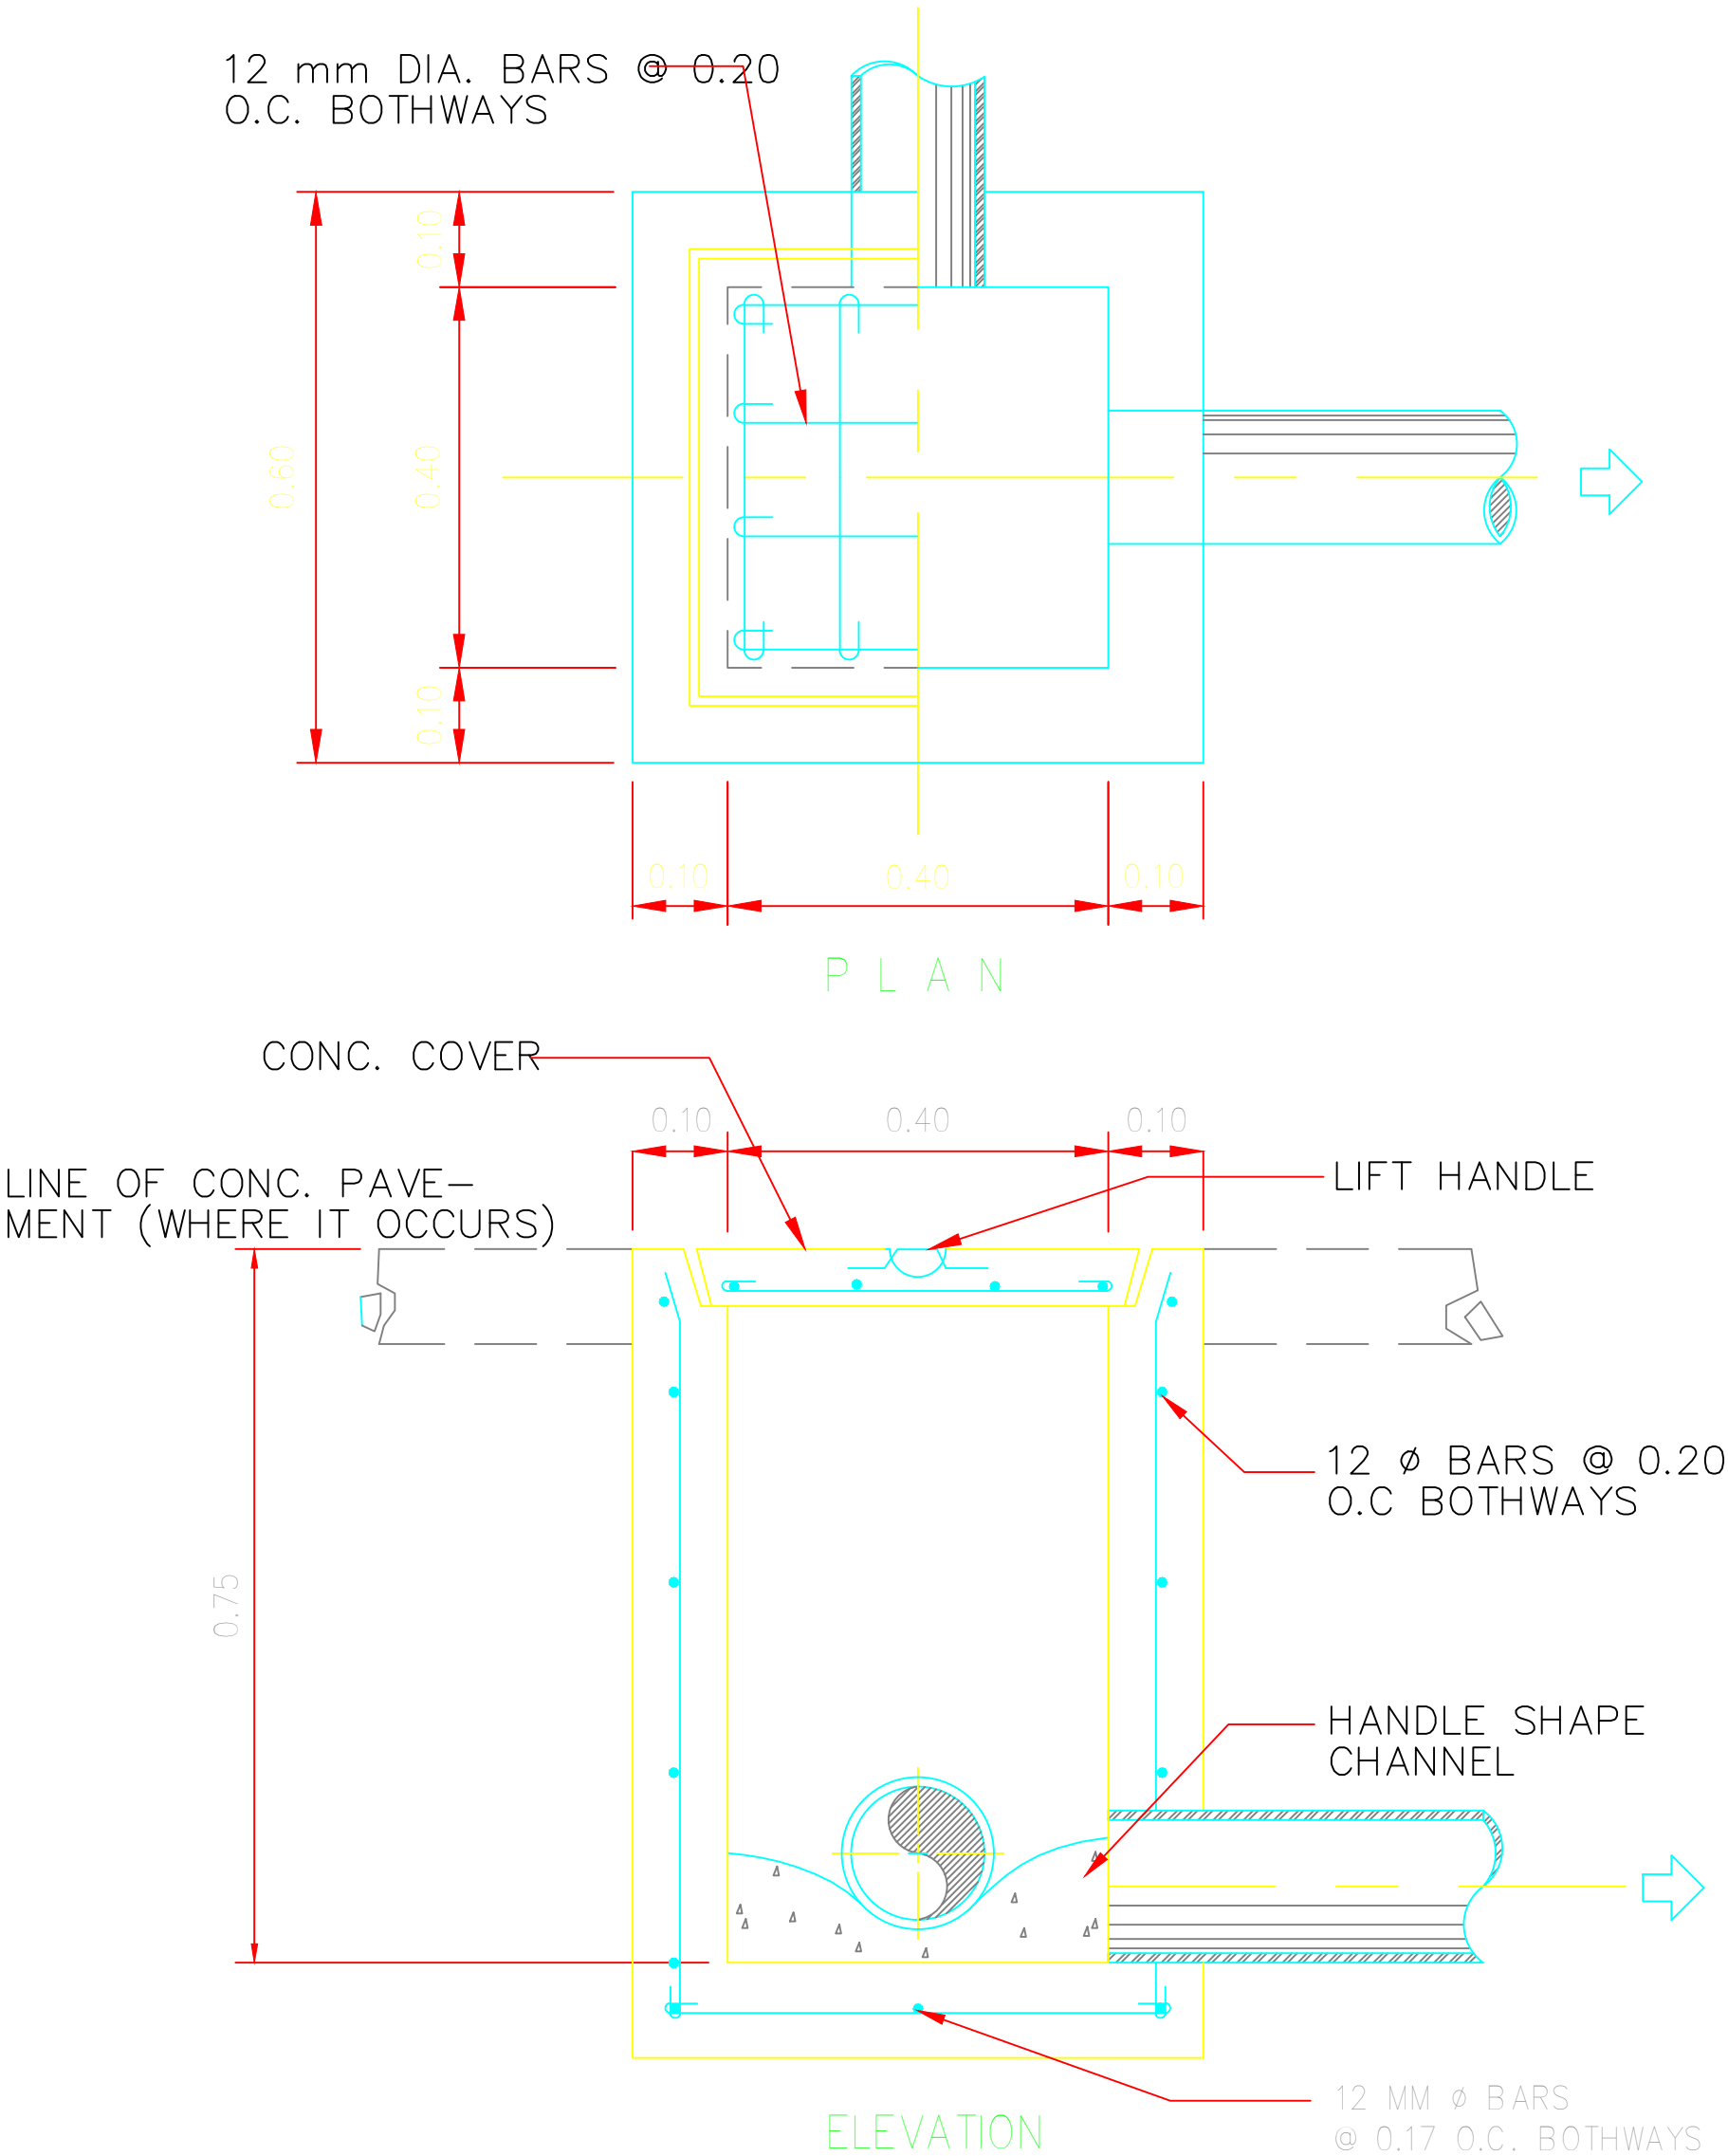

MANHOLE INSTALLATION DETAIL

NOT TO SCALE

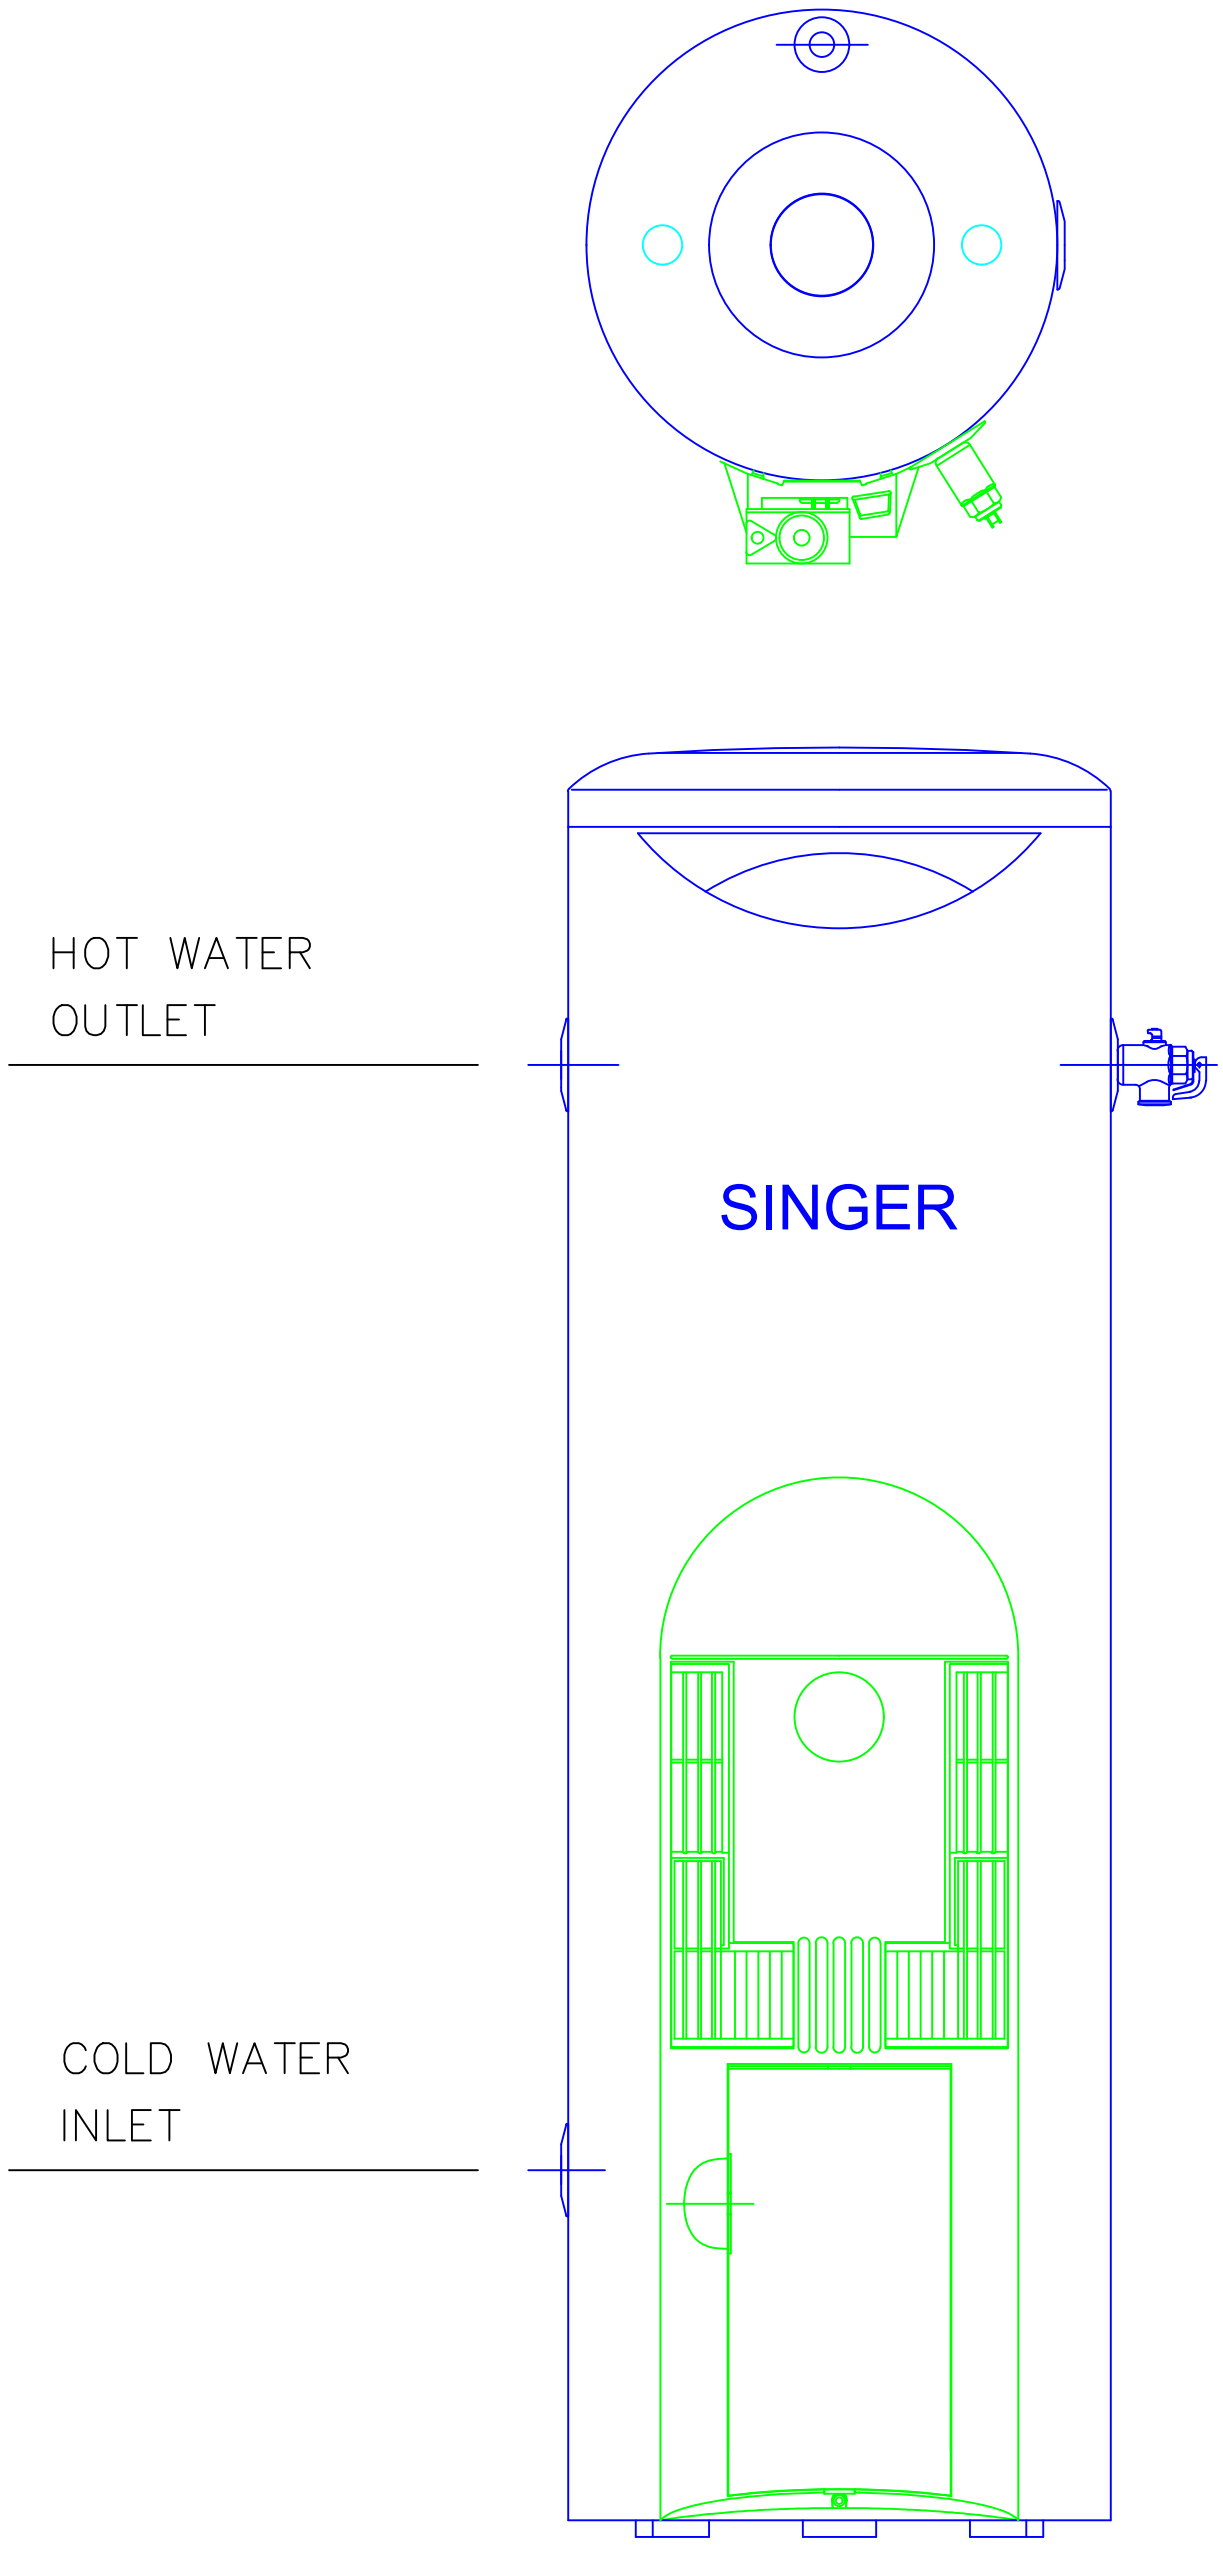

WATER GEYSER INSTALLATION DETAIL

NOT TO SCALE

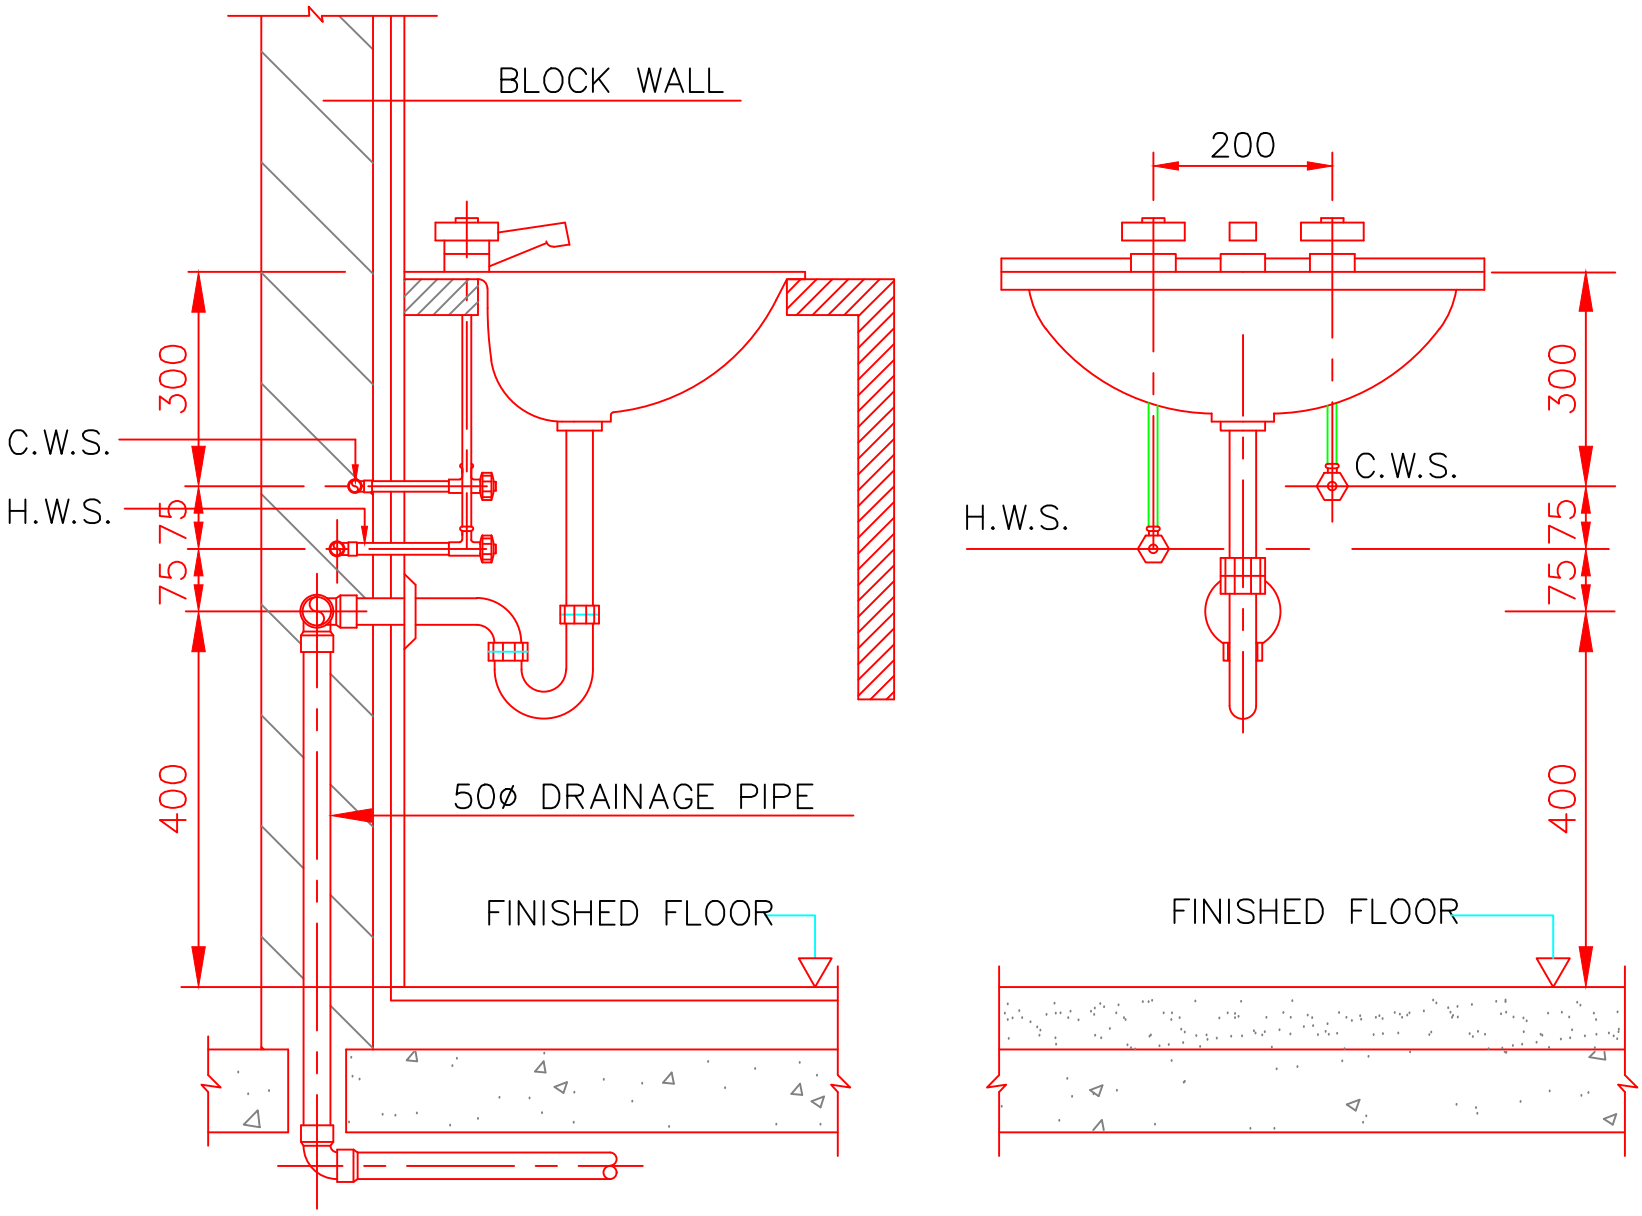

WASH BASIN INSTALLATION DETAIL

NOT TO SCALE

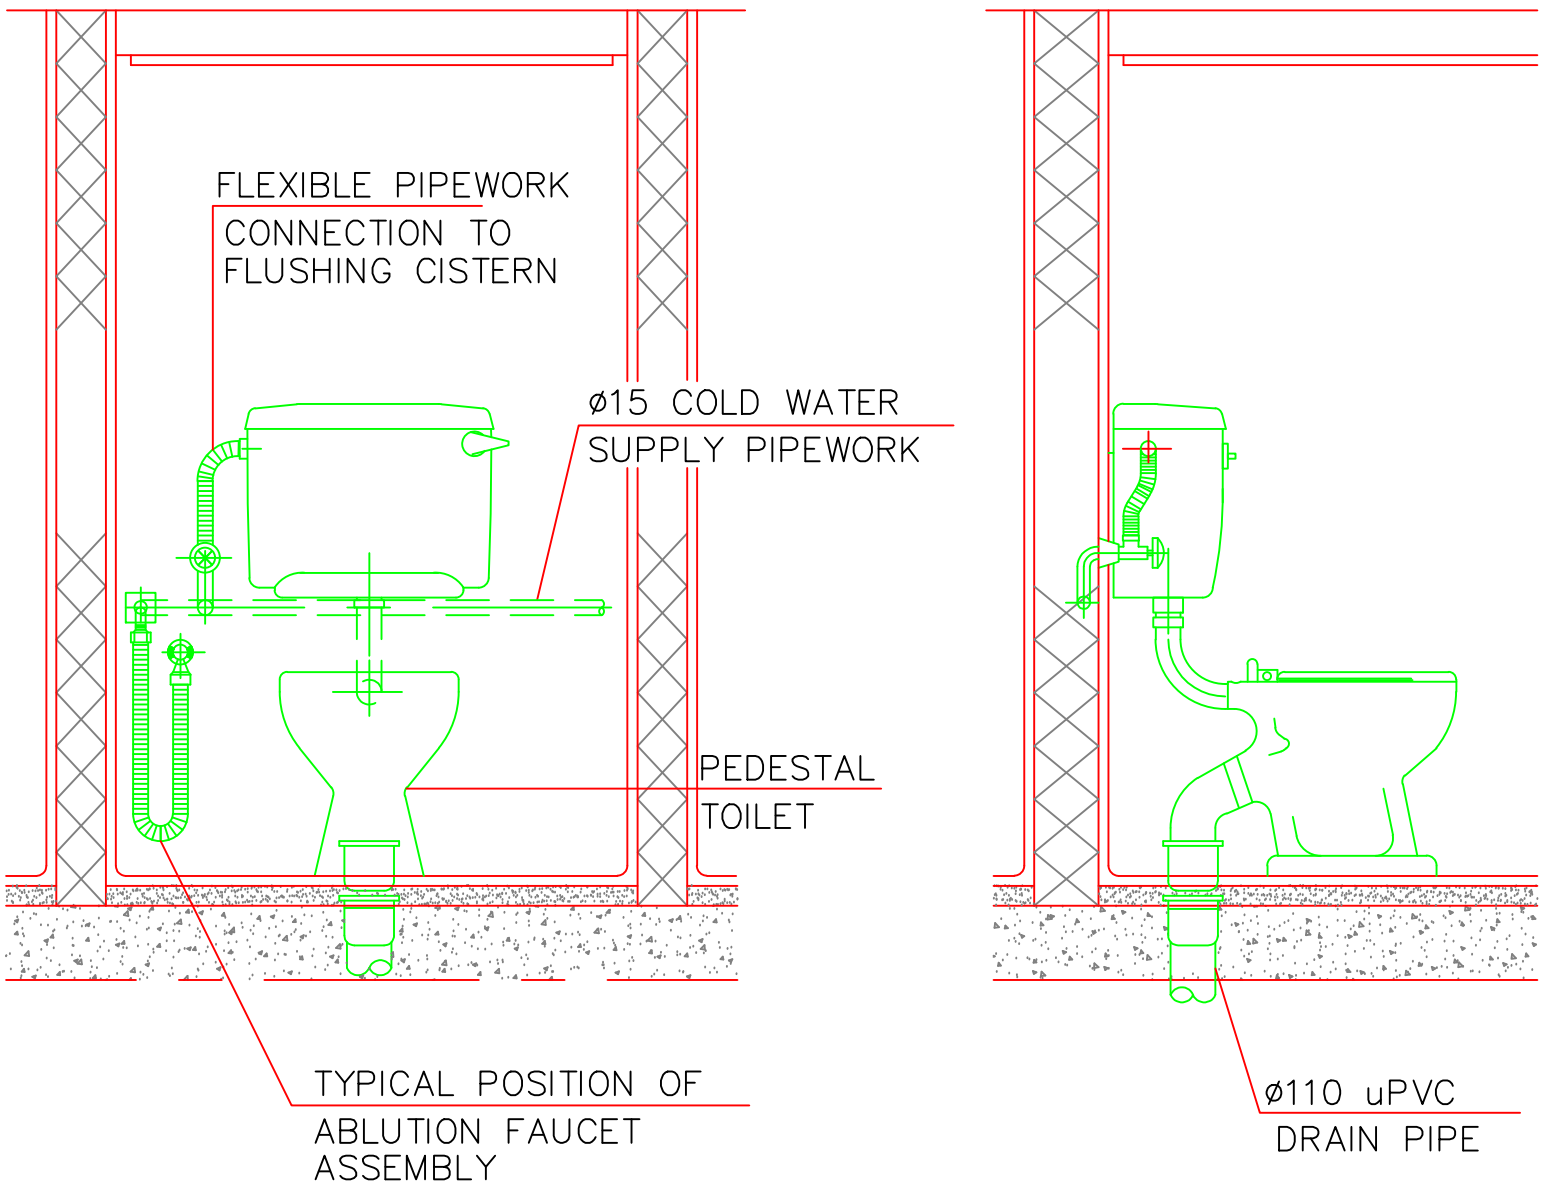

WESTREN WC INSTALLATION DETAIL

NOT TO SCALE

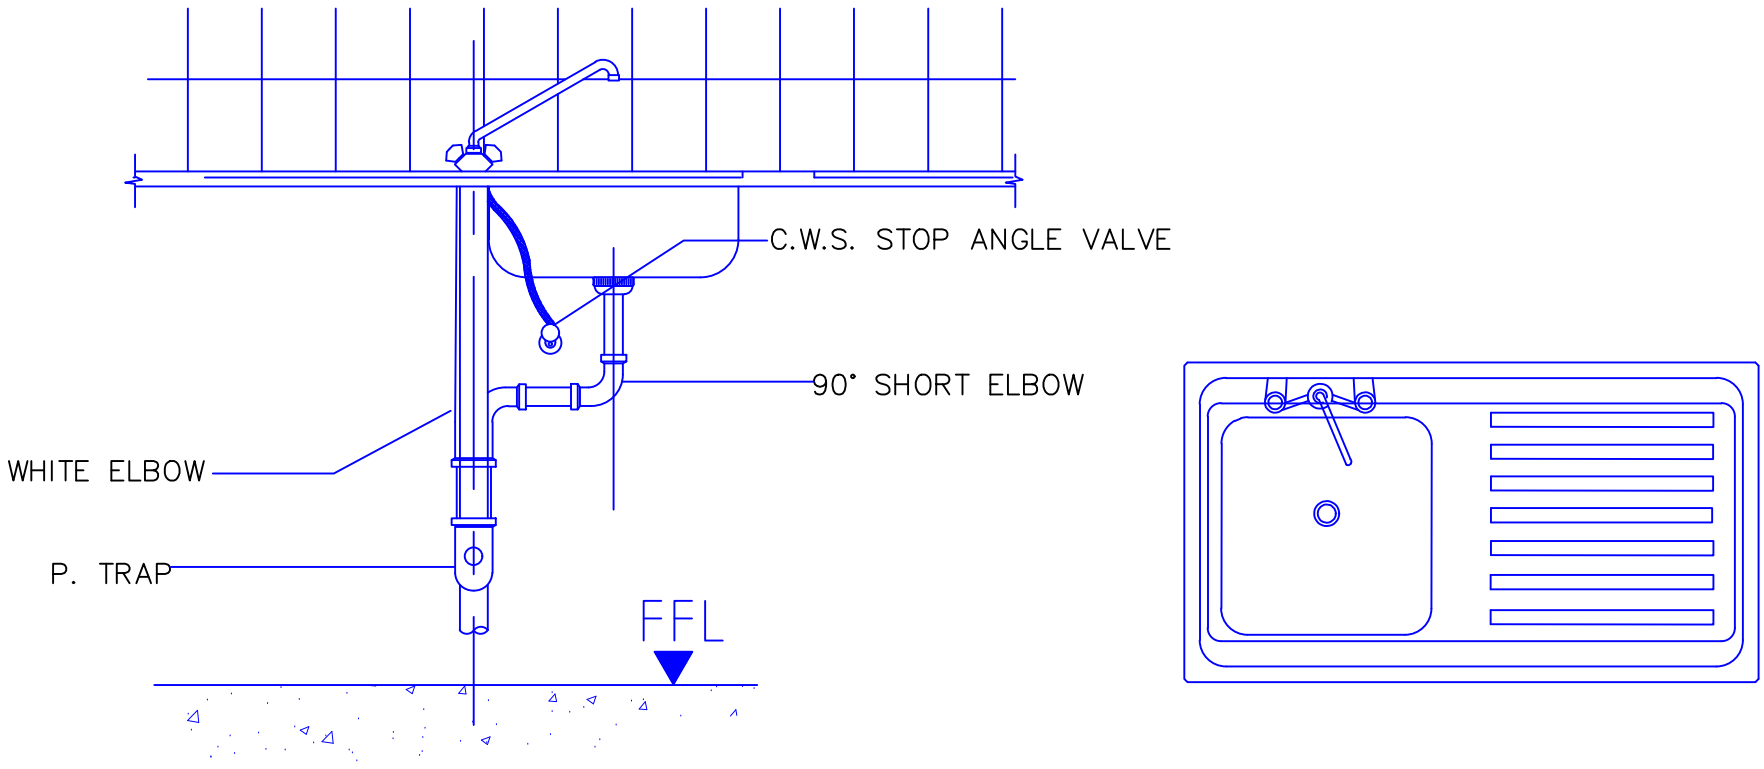

KITCHEN SINK INSTALLATION DETAIL

NOT TO SCALE

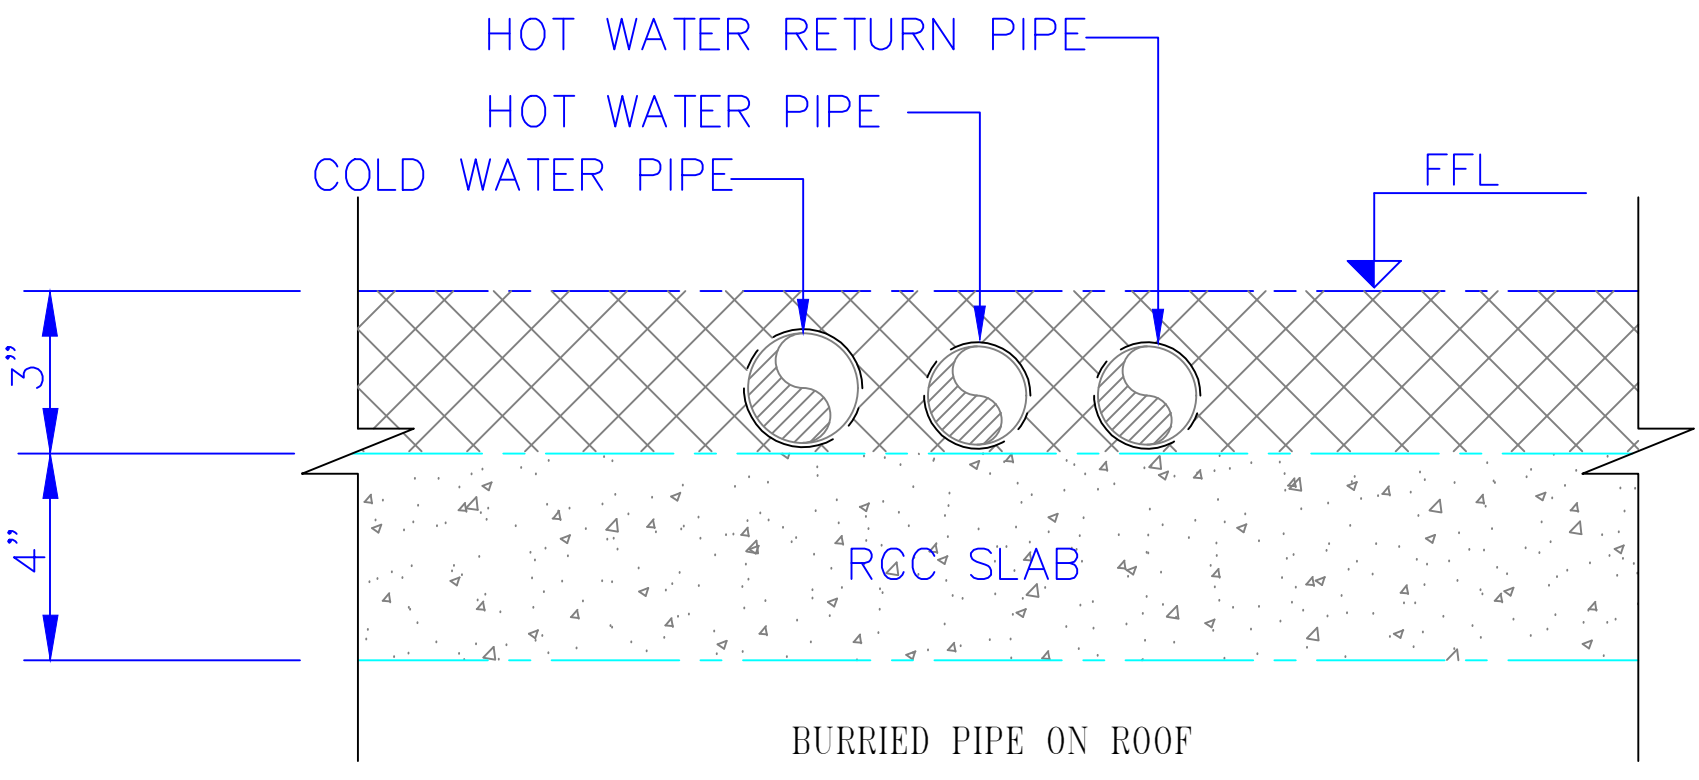

BURRIED PIPE ON ROOF

NOT TO SCALE

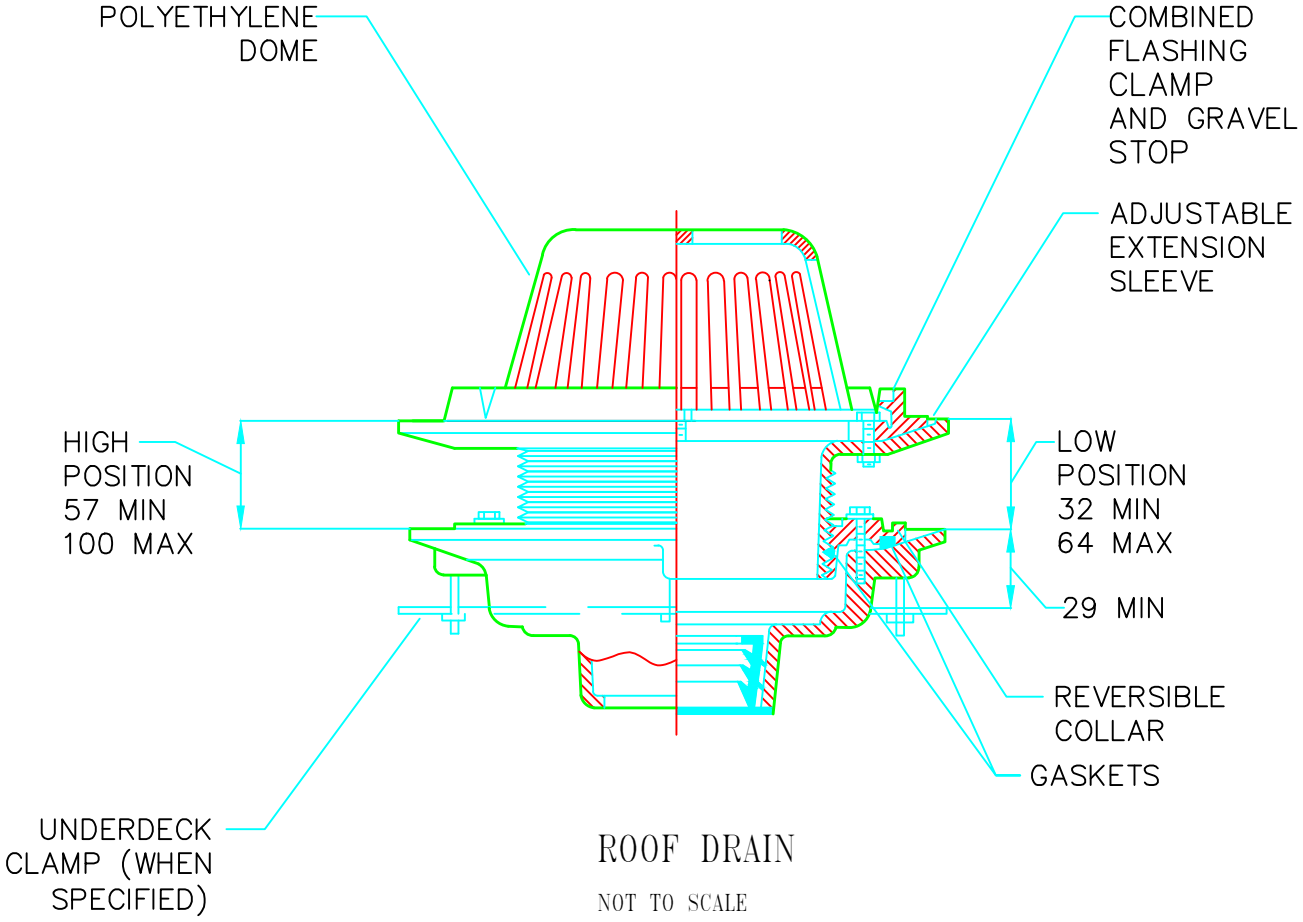

ROOF DRAIN

NOT TO SCALE

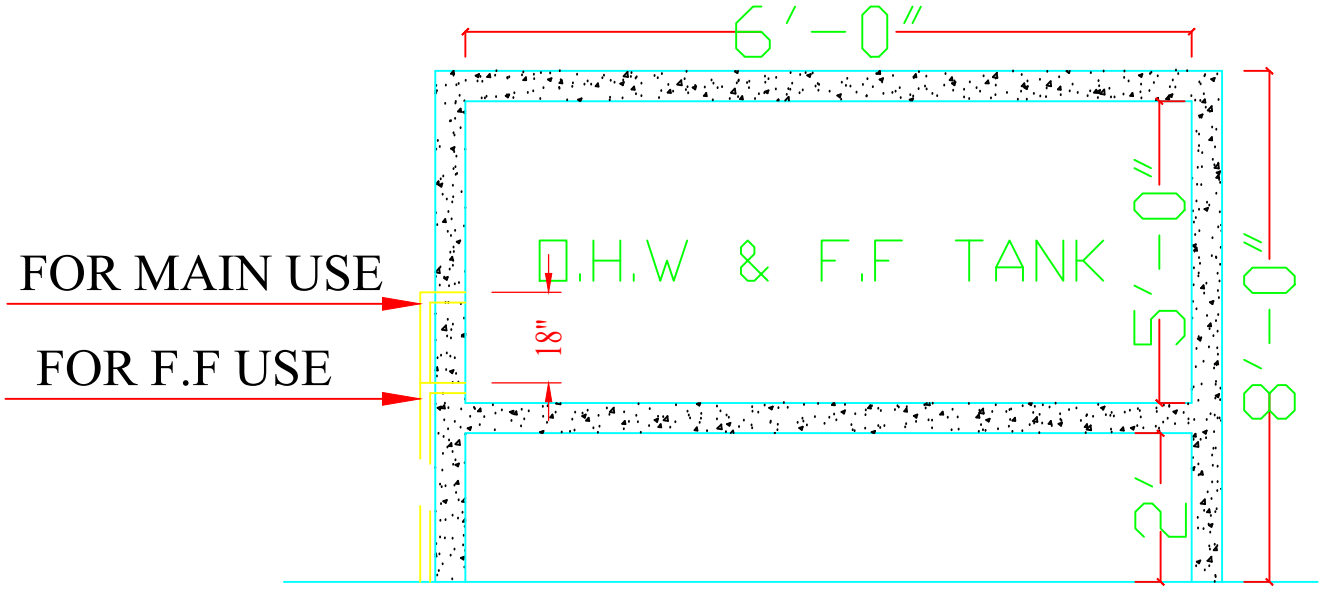

SECTION C-C

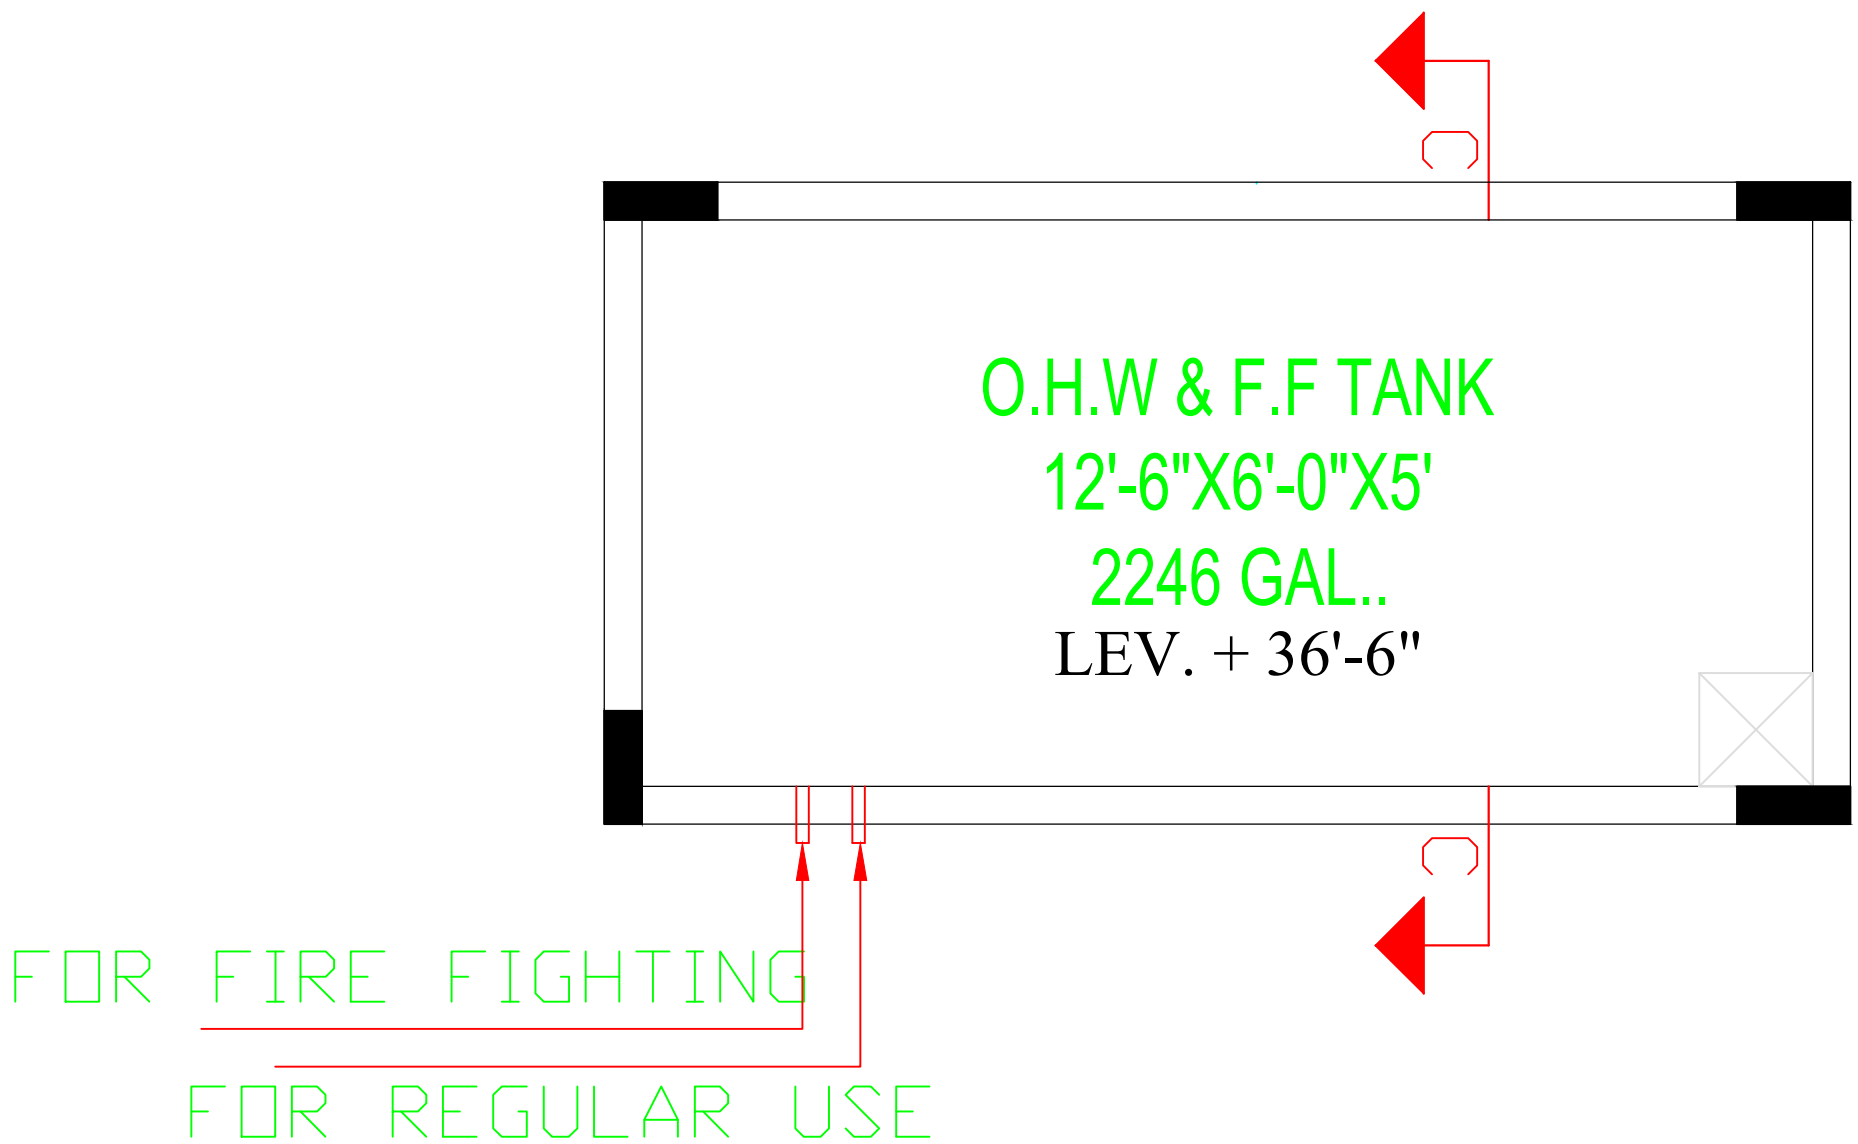

PLAN OF O/H&F.F.W. TANK

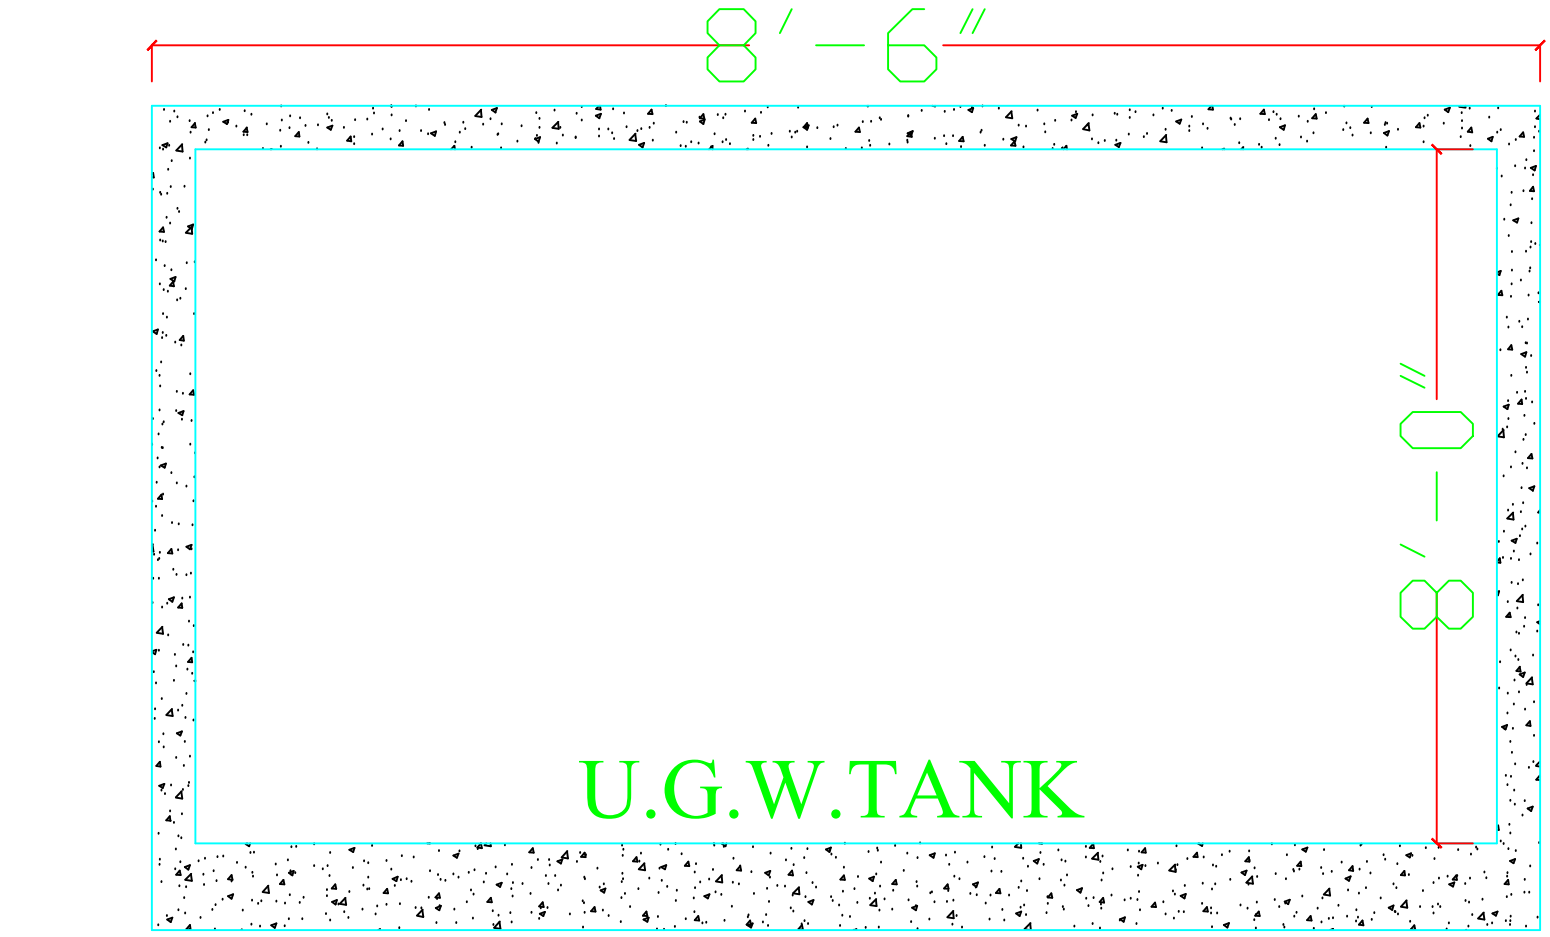

SECTION B-B

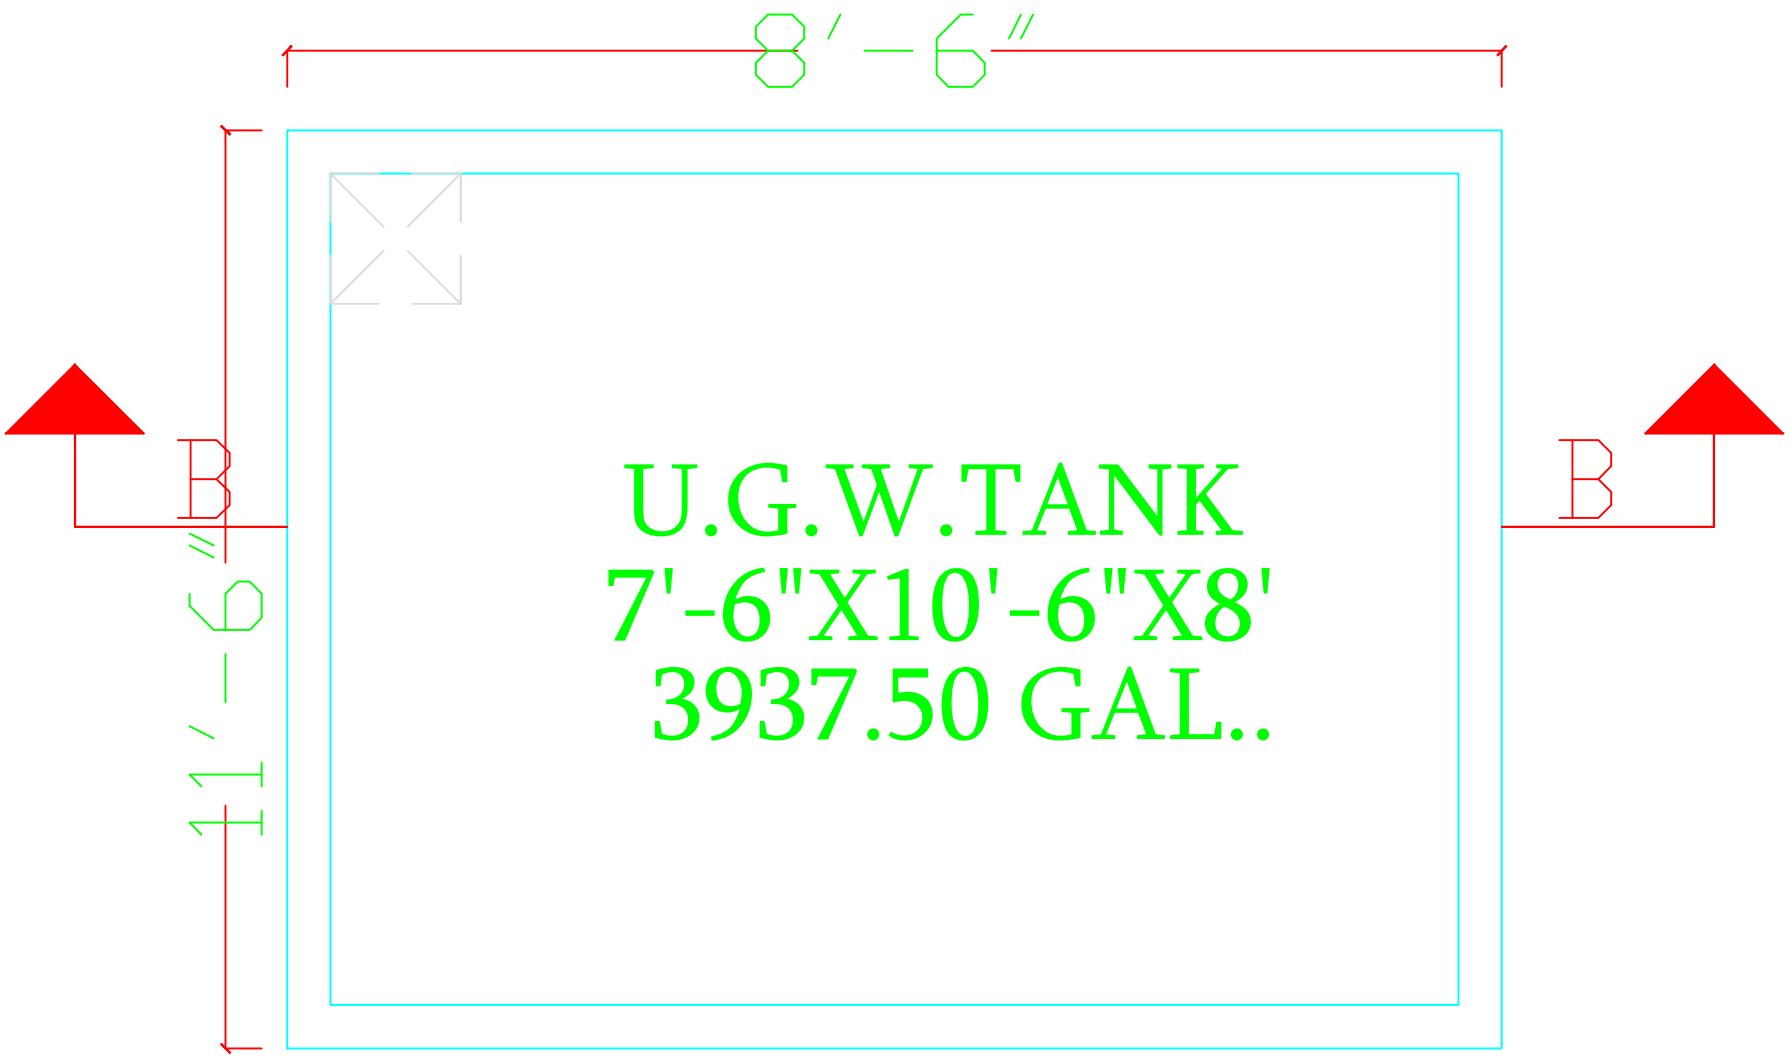

PLAN OF U.G.W. TANK

SYMBOL	DESCRIPTION
	COLD WATER PIPE
	HOT WATER PIPE
	GASS PIPE
	SOIL PIPE (ABOVE FLOOR/BELOW FLOOR)
	WASTE PIPE (ABOVE FLOOR/BELOW FLOOR)
	VENT PIPE
FIRE	FIRE LINE
	RAIN WATER PIPE (ABOVE FLOOR/BELOW FLOOR)
FHB.	FIRE HOSE BOX
E.W.C	ELECTRIC WATER COOLER
	ELECTRIC WATER HEATER
	GEYSER
	GATE VALVE IN CHAMBER
GV	GATE VALVE ON HORIZONTAL PIPE
	GATE VALVE ON VERTICAL PIPE
	CHECK VALVE OR NON-RETURN VALVE
	FLOAT VALVE
	STRAINER
FCO	FLOOR CLEAN OUT
	BIB TAP
FD	FLOOR DRAIN
FT	FLOOR TRAP
	PIPE RISER WITH BEND (FROM ABOVE TO BELOW)
	DIRECTION OF FLOW
MS	MUSLIM SHOWER
G.T	GULLY TRAP
	CARBON DIOXIDE PORTABLE FIRE EXTINGUISHER
	DRY CHEMICAL POWDER
	FOAM
	SIAMESE CONNECTION DETAILS
FHC.	FIRE HOSE CABINET

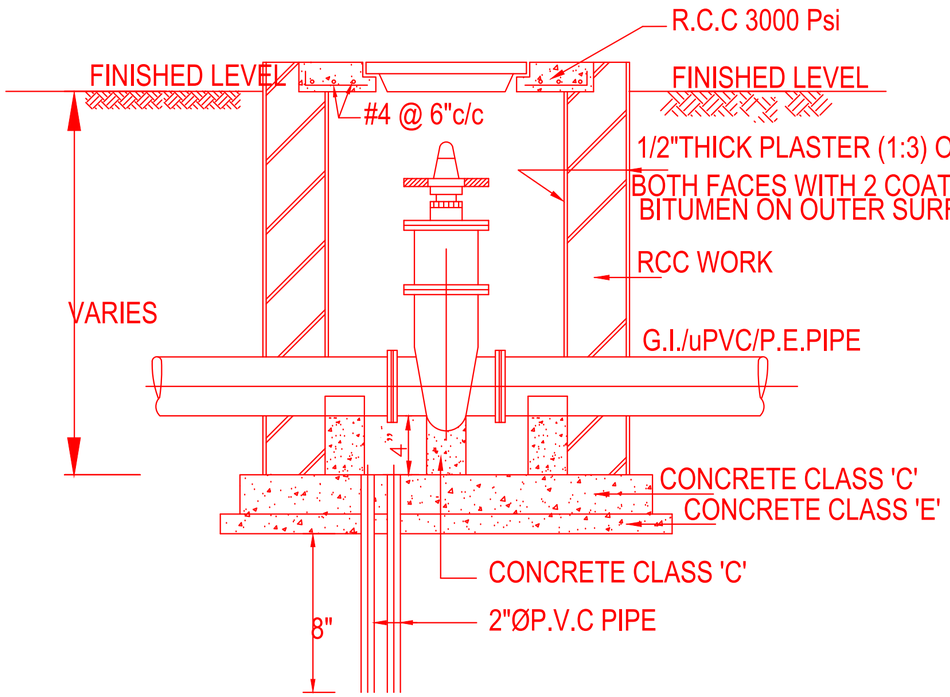

SECTION C-C

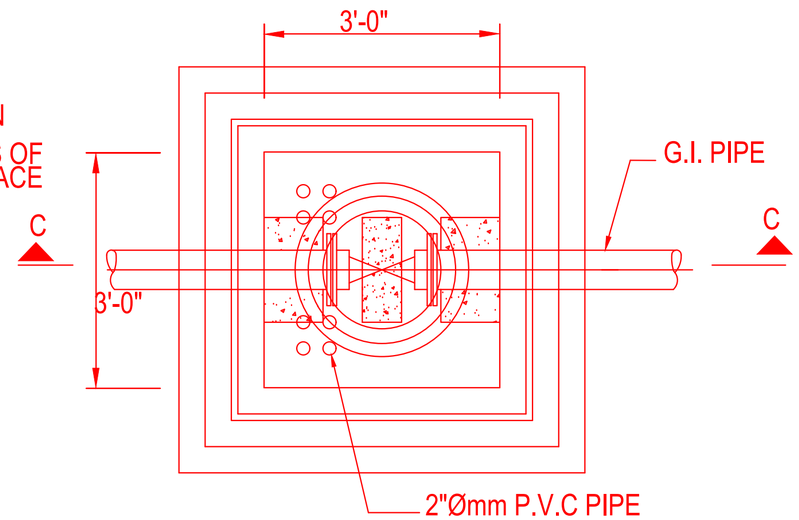

SECTIONAL PLAN
GATE VALVE CHAMBER
SCALE: N.T.S

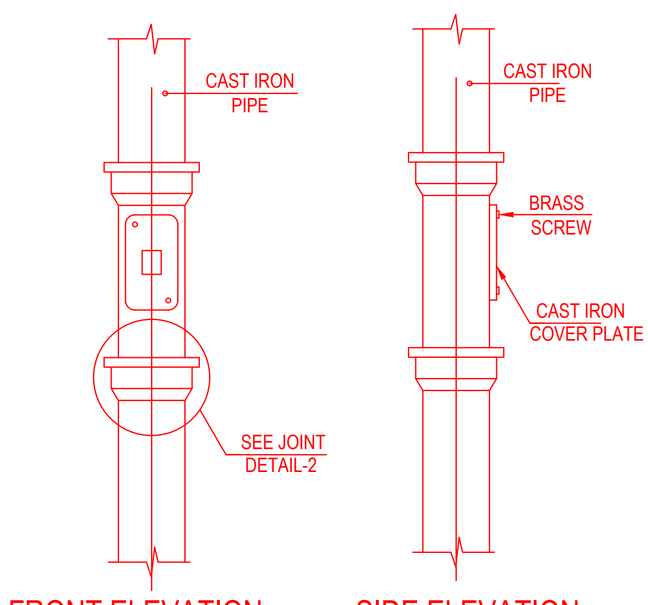

FRONT ELEVATION SIDE ELEVATION

ACCESS DOOR

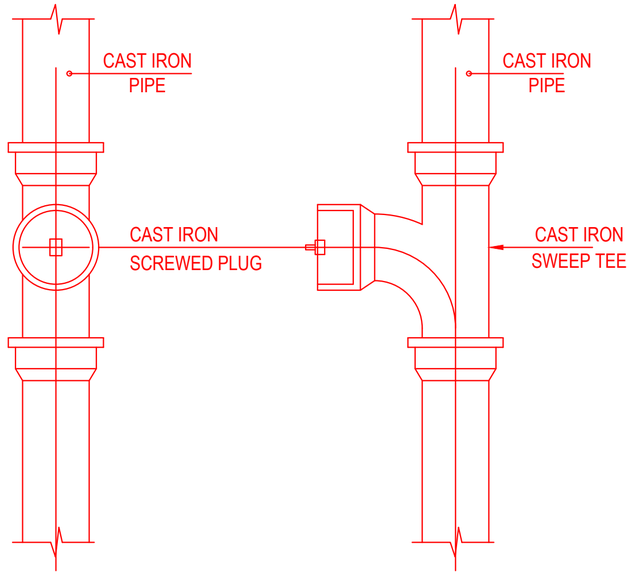

FRONT ELEVATION SIDE ELEVATION

STACK CLEANOUT

THANK YOU!

FOR CONNECTING US

E.D.C.O

ARCHITECTURAL STUDIO

GENERAL NOTES:

1. THE COPYRIGHT OF THIS DRAWING IS VESTED IN YourSpreadsheets AND IT MAY NOT BE REPRODUCED IN WHOLE OR PART OR USED FOR THE MANUFACTURE OF ANY ARTICLE WITHOUT THE EXPRESS PERMISSION OF THE COPYRIGHT HOLDERS.
2. WORK TO FIGURED DIMENSIONS ONLY.
3. THIS DRAWING IS TO BE READ IN CONJUNCTION WITH ALL RELEVANT ARCHITECT'S, SERVICE ENGINEER'S AND YourSpreadsheets DRAWINGS .

ALL DRWAING ARE THE PROPOERTY OF THE DESIGNER & THEY ARE NOT TO BE REPRODUCED IN WHOLE OR IN PART WITHOUT WRITTEN CONSENT FROM THE DESIGN WING
CONTRACTOR TO CHECK &VERIFY ALL DIMENSIONS BEFORE COMMENCING WORK & TO REPORT ANY DISCREPANCIES TO THE DESIGN WING.
DO NOT SCALE DRAWINGS.
ALL CONSTRUCTION TO BE ACCORDING TO BEST COMMON PRACTICE.

REV:	DESCRIPTION:	BY:	DATE:
A	ARCHITECTURE DRAWING	----	25-12-25
B	STRUCTURE DRAWING	----	27-12-25

PROJECT NAME:
300 SQ.YARD HOUSE
ARCHITECTURE DRAWING

SIGNATURE BY:

DRAWING TITLE:
ARCHITECTURAL DRAWING

DRAWN BY: MUDASSIR
CHECKED BY: M.SHEHERYAR
APPROVED BY: M.SHEHERYAR
DATE: 27-DEC-2025

CLIENT
MR. ROHAN
KARACHI...

DESIGNED BY:-

E.D.C.O
ENGINEERING DESIGNING CONSTRUCTION OFFICIAL

ARCHITECT| PLANNERS| ENGINEERS| INTERIOR| B.O.Q| EXTERIOR| CONSULT| STRUCTURE DESIGN| PLANNING| LAND SURVEY| CONSTRUCTION| 3D ANIMATION VIDEO| RENOVATION|
MUHAMMAD SHEHERYAR
CONTACT- 0312-2118445|D.H.A PHASE VII

PROJECT NO: AR-7590
SCALE: 1/8"=1'-0"
SHEET SIZE: A3
DRAWING NO: ARC
SHEET NO ----------
REVISION: YES
UNIT: INCHES&FEET