PROJECT:-

PROPOSED DRAWING FOR HOSPITAL

ADDRESS:-

PLOT NO. _____WEST CITY HOSPITAL,
MOMINABAD,ORANGI TOWN,
K A R A C H I.

CLIENT:-

DR. IMRAN

DATE:-

09-05-2025


THE CAD DESIGNER

ARCHITECT, ENGINEERS, PLANNERS
GULSHAN-E-HADEED, PHASE I & II EXT. BIN QASIM,
KARACHI.
CELL: 0306-2776176

ARCHITECTURAL DRAWINGS

THE CAD DESIGNER

ARCHITECT, ENGINEERS, PLANNERS
GULSHAN-E-HADEED, PHASE I & II EXT. BIN QASIM,
KARACHI.
CELL: 0306-2776176

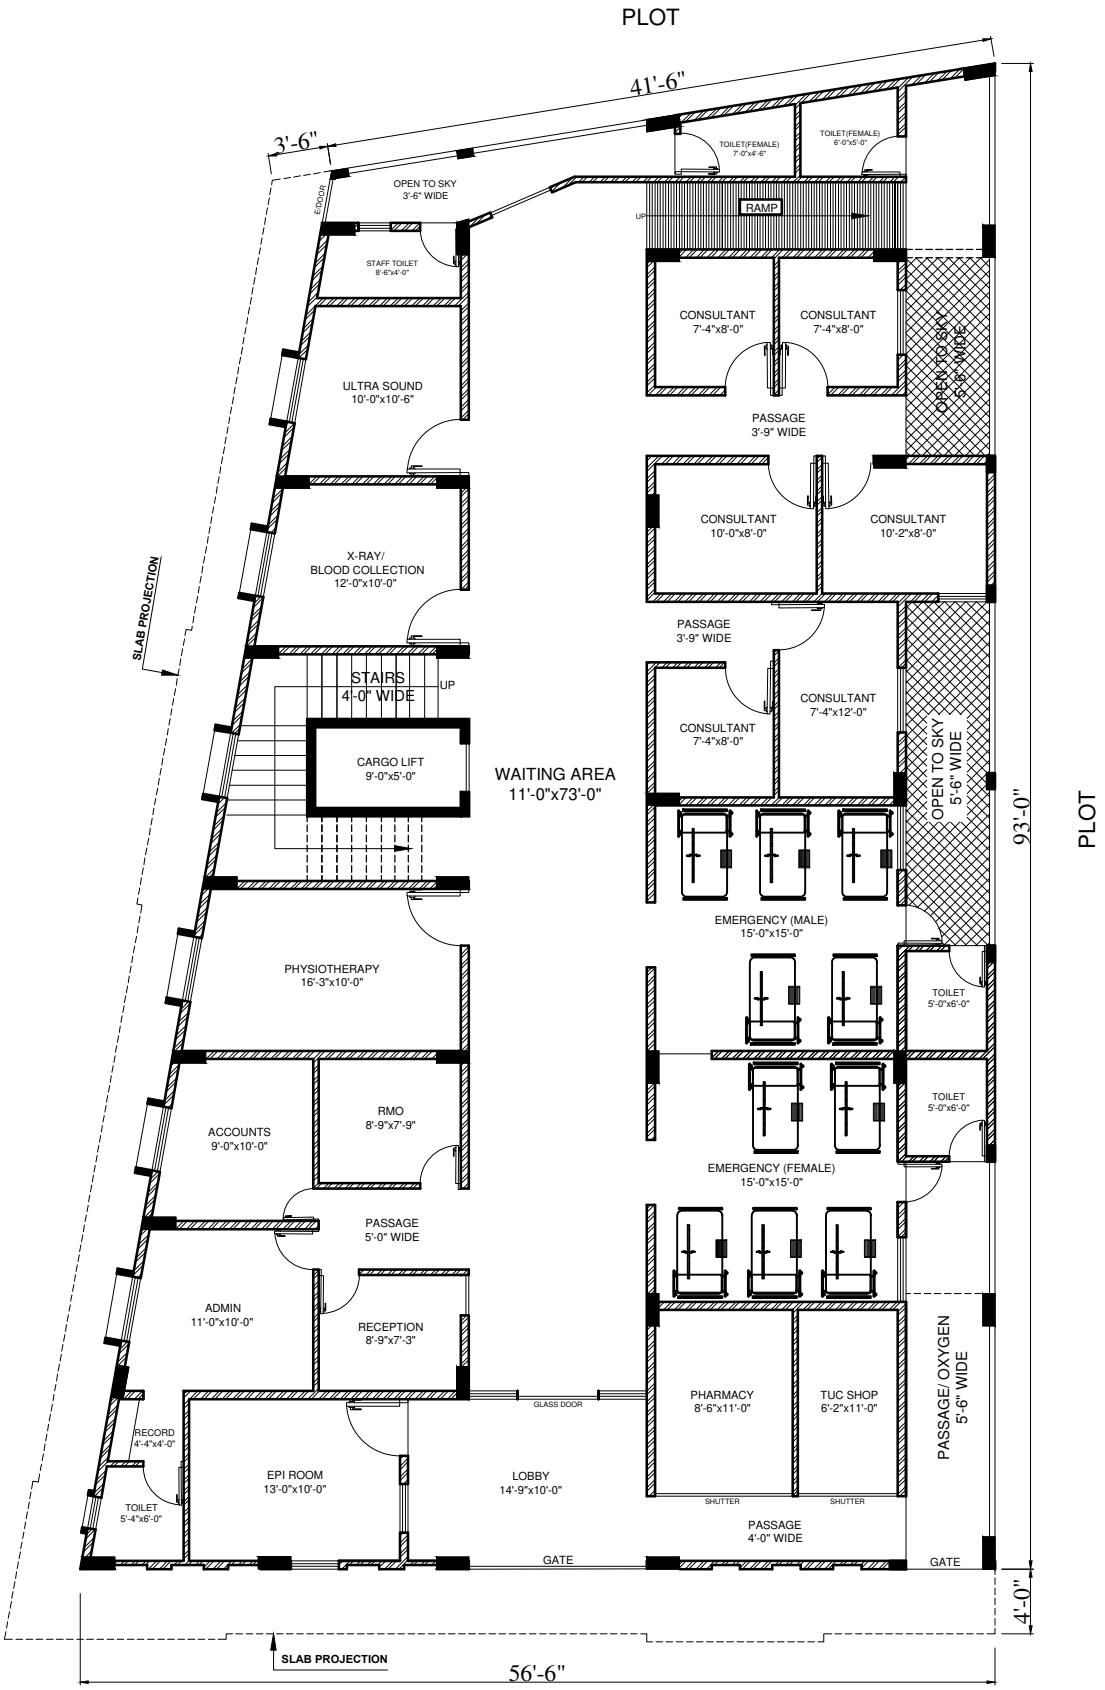


MAIN ROAD

GROUND FLOOR PLAN

PROJECT:-	PROPOSED DRAWING FOR HOSPITAL	DATE:-	09 - 05 - 2025
TITLE:-	**GROUND FLOOR PLAN**	SCALE:-	1/8" = 1'-0"
ADDRESS:-	PLOT NO. _____WEST CITY HOSPITAL, MOMINABAD, ORANGI TOWN, K A R A C H I.	CHECKED BY:-	AGAH
		CAD BY:-	SUFYAN
		PRINT DATE:-	09 - 05 - 2025
CLIENT:-	DR.IMRAN	DRG NO. :-	A - 2025/01-01-02


THE CAD DESIGNER
ARCHITECT, ENGINEERS, PLANNERS
GULSHAN-E-HADEED, PHASE I & II EXT. BIN QASIM, KARACHI
CELL:0306-2776176

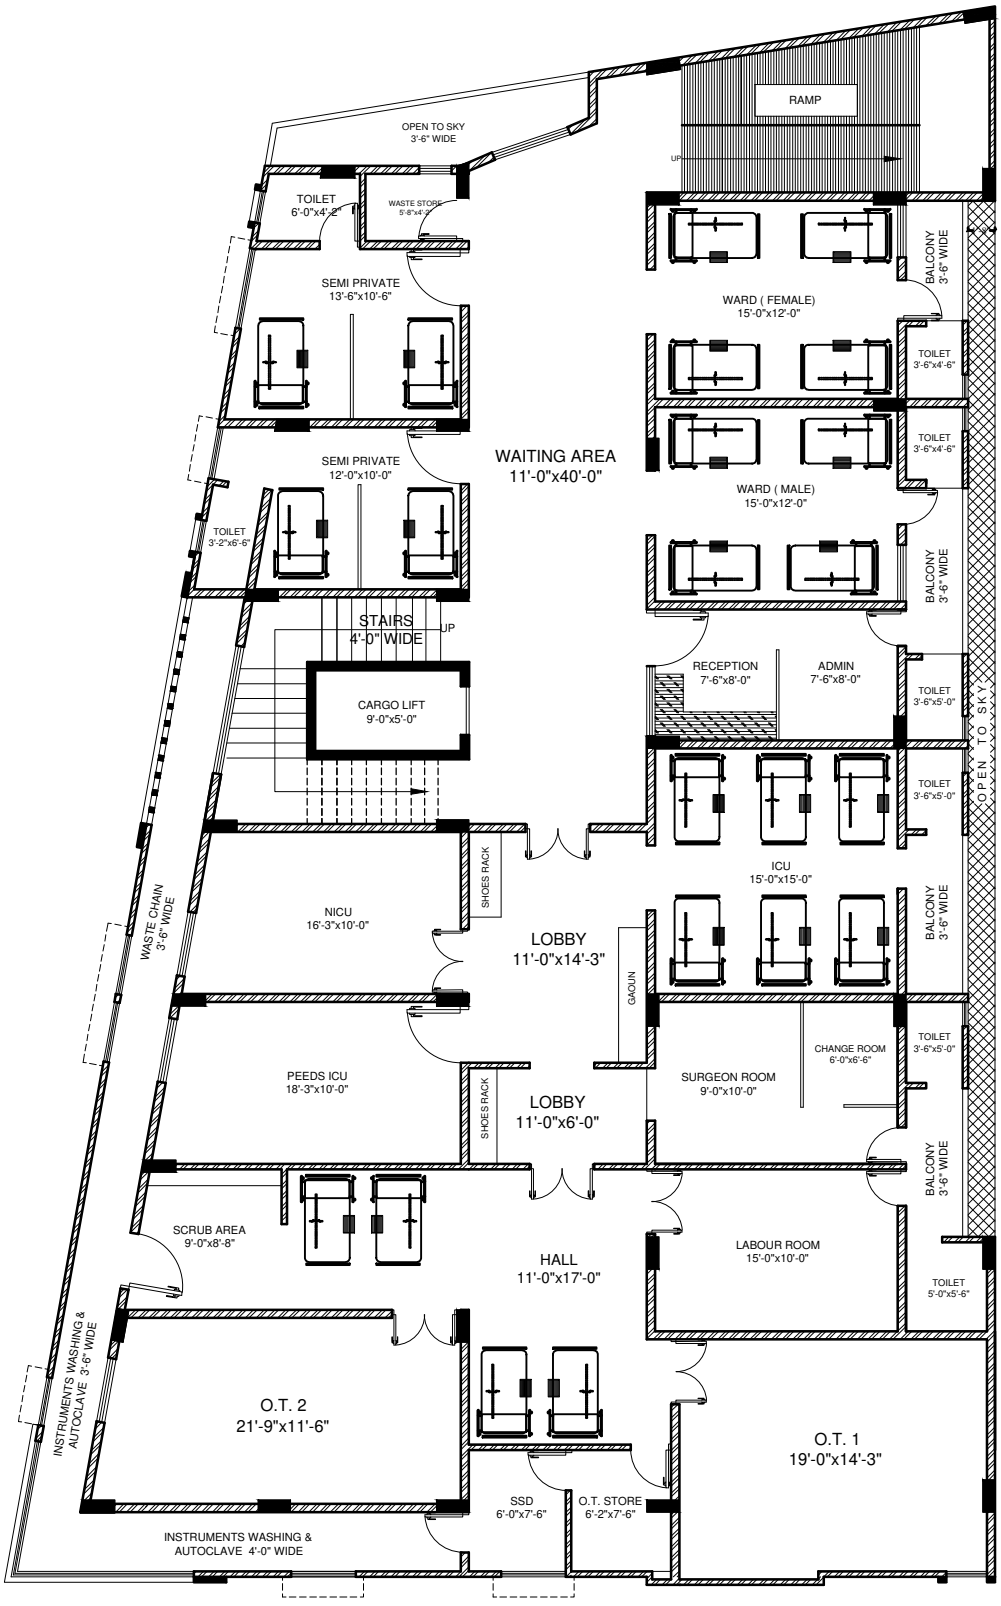

FIRST FLOOR PLAN

PROJECT:-	PROPOSED DRAWING FOR HOSPITAL	DATE:-	09 - 05 - 2025
TITLE:-	**FIRST FLOOR PLAN**	SCALE:-	1/8" = 1'-0"
ADDRESS:-	PLOT NO. _____WEST CITY HOSPITAL, MOMINABAD, ORANGI TOWN, K A R A C H I.	CHECKED BY:-	AGAH
		CAD BY:-	SUFYAN
		PRINT DATE:-	09 - 05 - 2025
CLIENT:-	DR.IMRAN	DRG NO. :-	A - 2025/01-01-02


THE CAD DESIGNER
ARCHITECT, ENGINEERS, PLANNERS
GULSHAN-E-HADEED, PHASE I & II EXT. BIN QASIM, KARACHI
CELL:0306-2776176

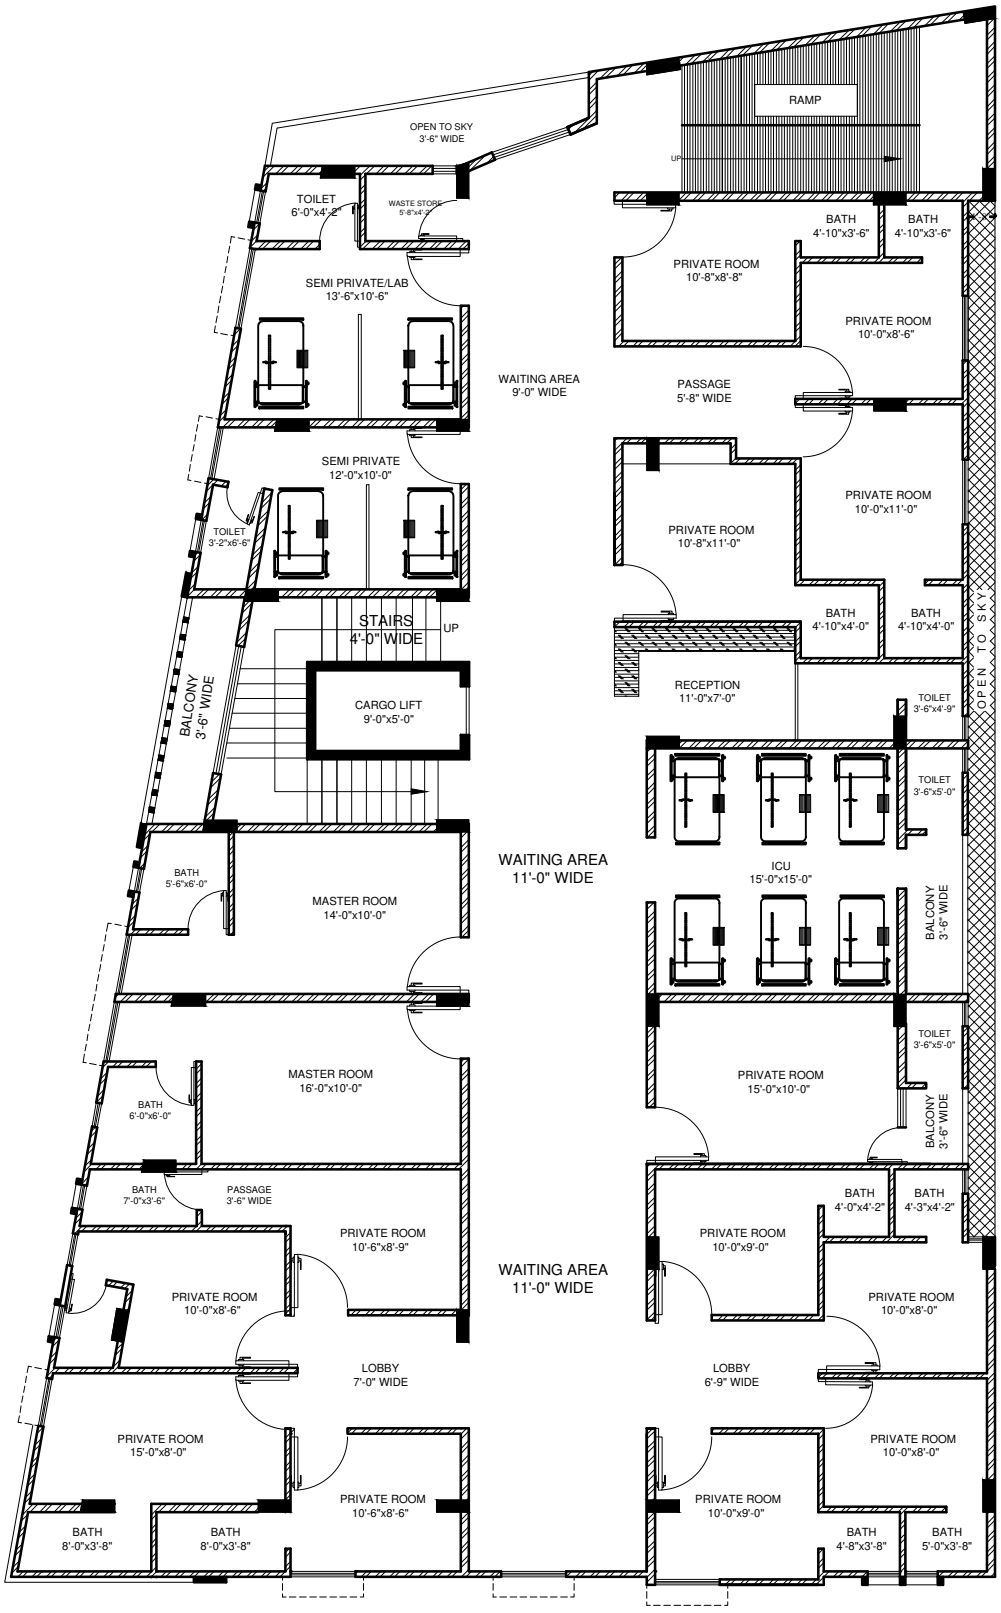

SECOND FLOOR PLAN

PROJECT:-	PROPOSED DRAWING FOR HOSPITAL	DATE:-	09 - 05 - 2025
TITLE:-	**SECOND FLOOR PLAN**	SCALE:-	1/8" = 1'-0"
ADDRESS:-	PLOT NO. _____WEST CITY HOSPITAL, MOMINABAD, ORANGI TOWN, K A R A C H I.	CHECKED BY:-	AGAH
		CAD BY:-	SUFYAN
		PRINT DATE:-	09 - 05 - 2025
CLIENT:-	DR.IMRAN	DRG NO. :-	A - 2025/01-01-02


THE CAD DESIGNER
ARCHITECT, ENGINEERS, PLANNERS
GULSHAN-E-HADEED, PHASE I & II EXT. BIN QASIM, KARACHI
CELL:0306-2776176

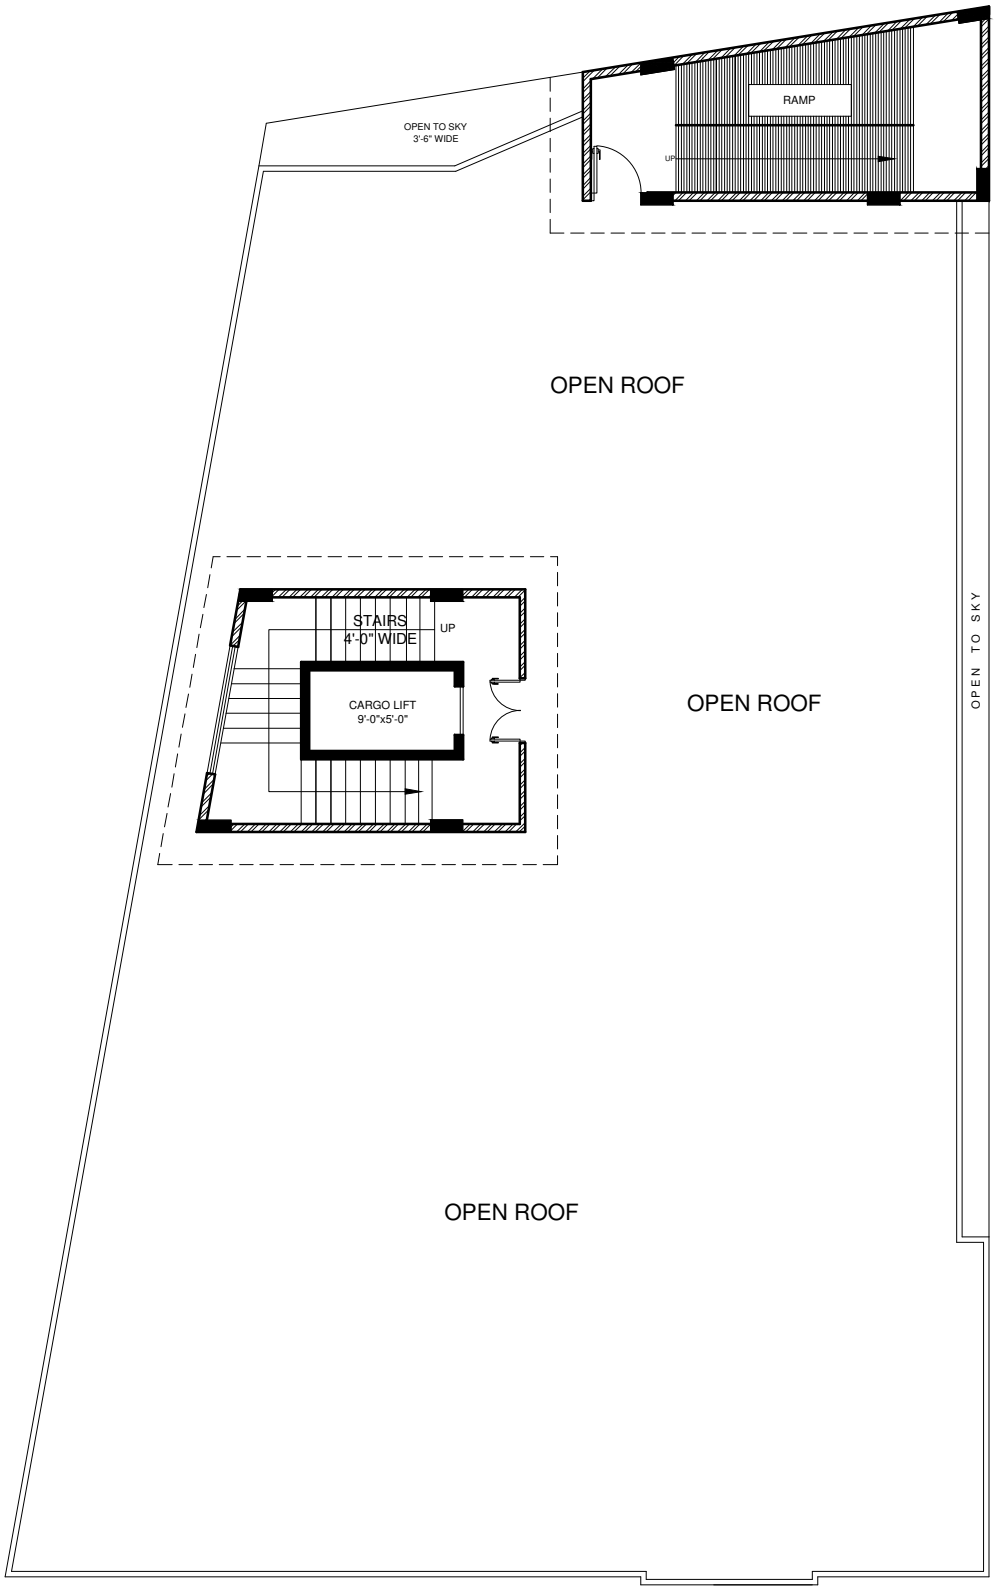

TOP FLOOR PLAN

PROJECT:-	PROPOSED DRAWING FOR HOSPITAL	DATE:-	09 - 05 - 2025
TITLE:-	**TOP FLOOR PLAN**	SCALE:-	1/8" = 1'-0"
ADDRESS:-	PLOT NO. _____WEST CITY HOSPITAL, MOMINABAD, ORANGI TOWN, K A R A C H I.	CHECKED BY:-	AGAH
		CAD BY:-	SUFYAN
		PRINT DATE:-	09 - 05 - 2025
CLIENT:-	DR.IMRAN	DRG NO. :-	A - 2025/01-01-02

THE CAD DESIGNER
ARCHITECT, ENGINEERS, PLANNERS
GULSHAN-E-HADEED, PHASE I & II EXT. BIN QASIM, KARACHI
CELL:0306-2776176

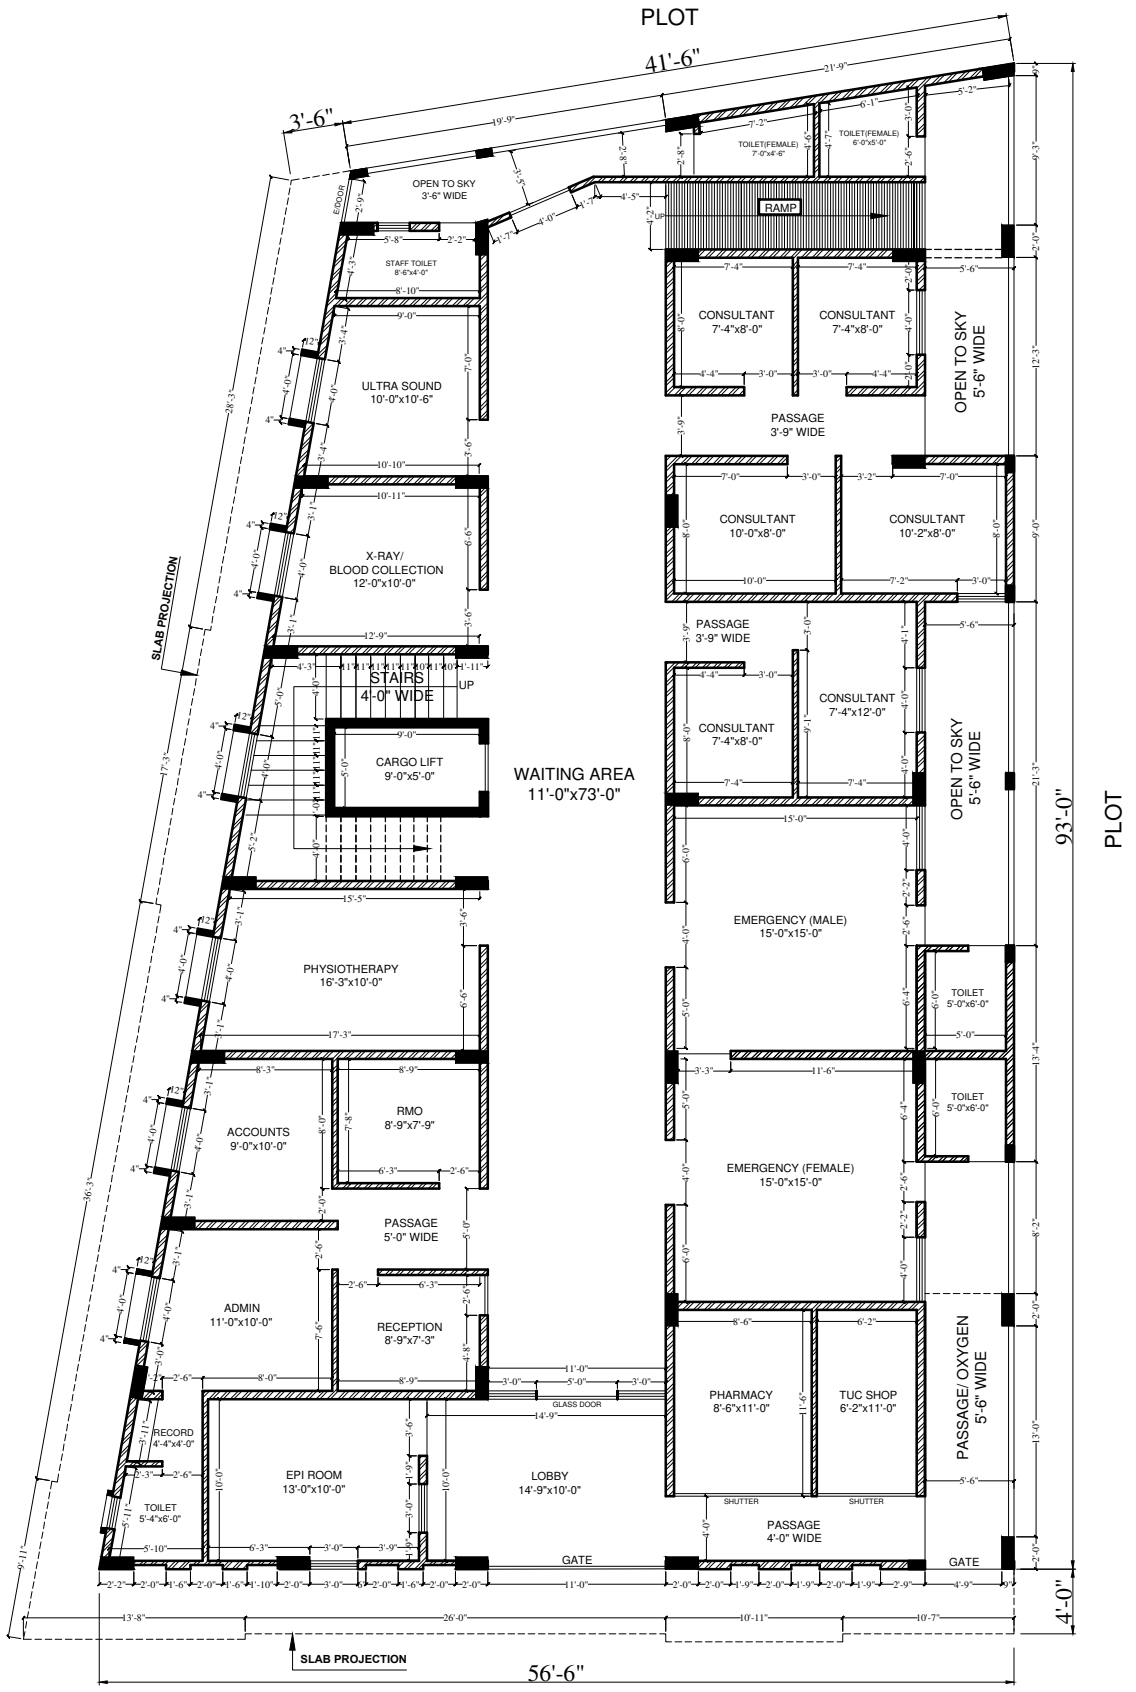


MAIN ROAD

GROUND FLOOR WORKING PLAN

PROJECT:-	PROPOSED DRAWING FOR HOSPITAL	DATE:-	09 - 05 - 2025
TITLE:-	**GROUND FLOOR WORKING PLAN**	SCALE:-	1/8" = 1'-0"
ADDRESS:-	PLOT NO. _____WEST CITY HOSPITAL, MOMINABAD, ORANGI TOWN, K A R A C H I.	CHECKED BY:-	AGAH
		CAD BY:-	SUFYAN
		PRINT DATE:-	09 - 05 - 2025
CLIENT:-	DR.IMRAN	DRG NO. :-	A - 2025/01-01-02


THE CAD DESIGNER
ARCHITECT, ENGINEERS, PLANNERS
GULSHAN-E-HADEED, PHASE I & II EXT. BIN QASIM, KARACHI
CELL:0306-2776176

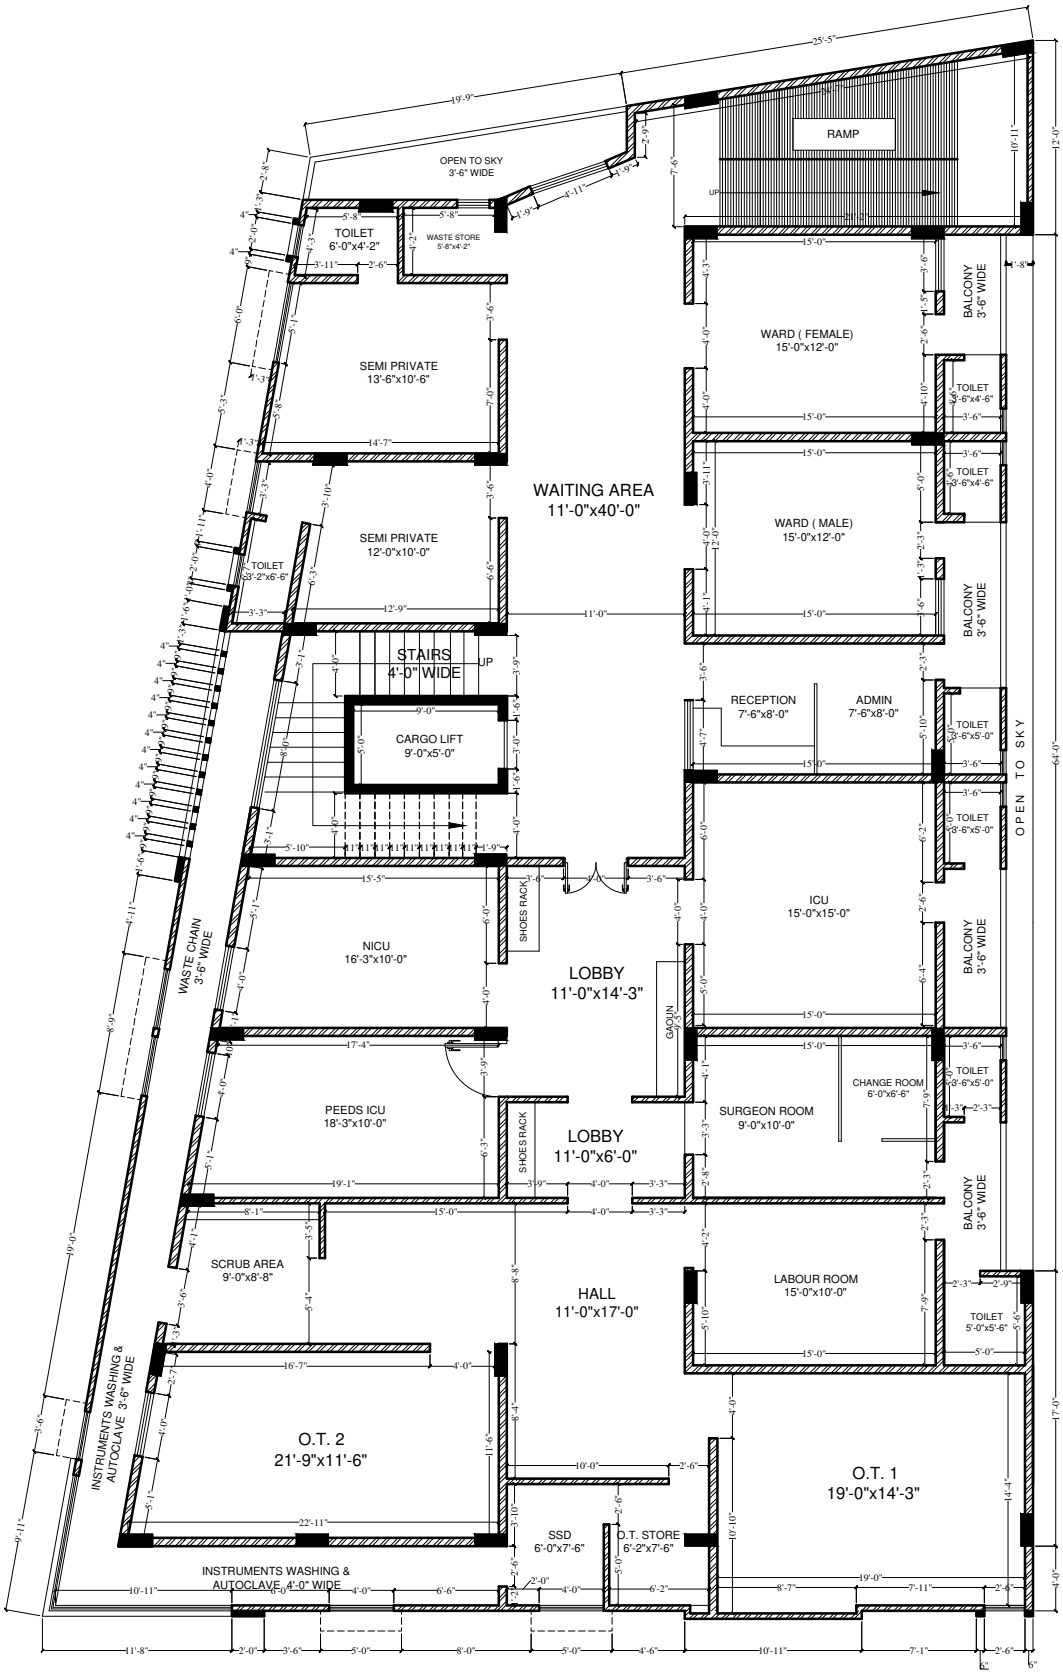

FIRST FLOOR WORKING LAN

PROJECT:-	PROPOSED DRAWING FOR HOSPITAL	DATE:-	09 - 05 - 2025
TITLE:-	**FIRST FLOOR WORKING PLAN**	SCALE:-	1/8" = 1'-0"
ADDRESS:-	PLOT NO. _____WEST CITY HOSPITAL, MOMINABAD, ORANGI TOWN, K A R A C H I.	CHECKED BY:-	AGAH
		CAD BY:-	SUFYAN
		PRINT DATE:-	09 - 05 - 2025
CLIENT:-	DR.IMRAN	DRG NO. :-	A - 2025/01-01-02


THE CAD DESIGNER
ARCHITECT, ENGINEERS, PLANNERS
GULSHAN-E-HADEED, PHASE I & II EXT. BIN QASIM, KARACHI
CELL:0306-2776176

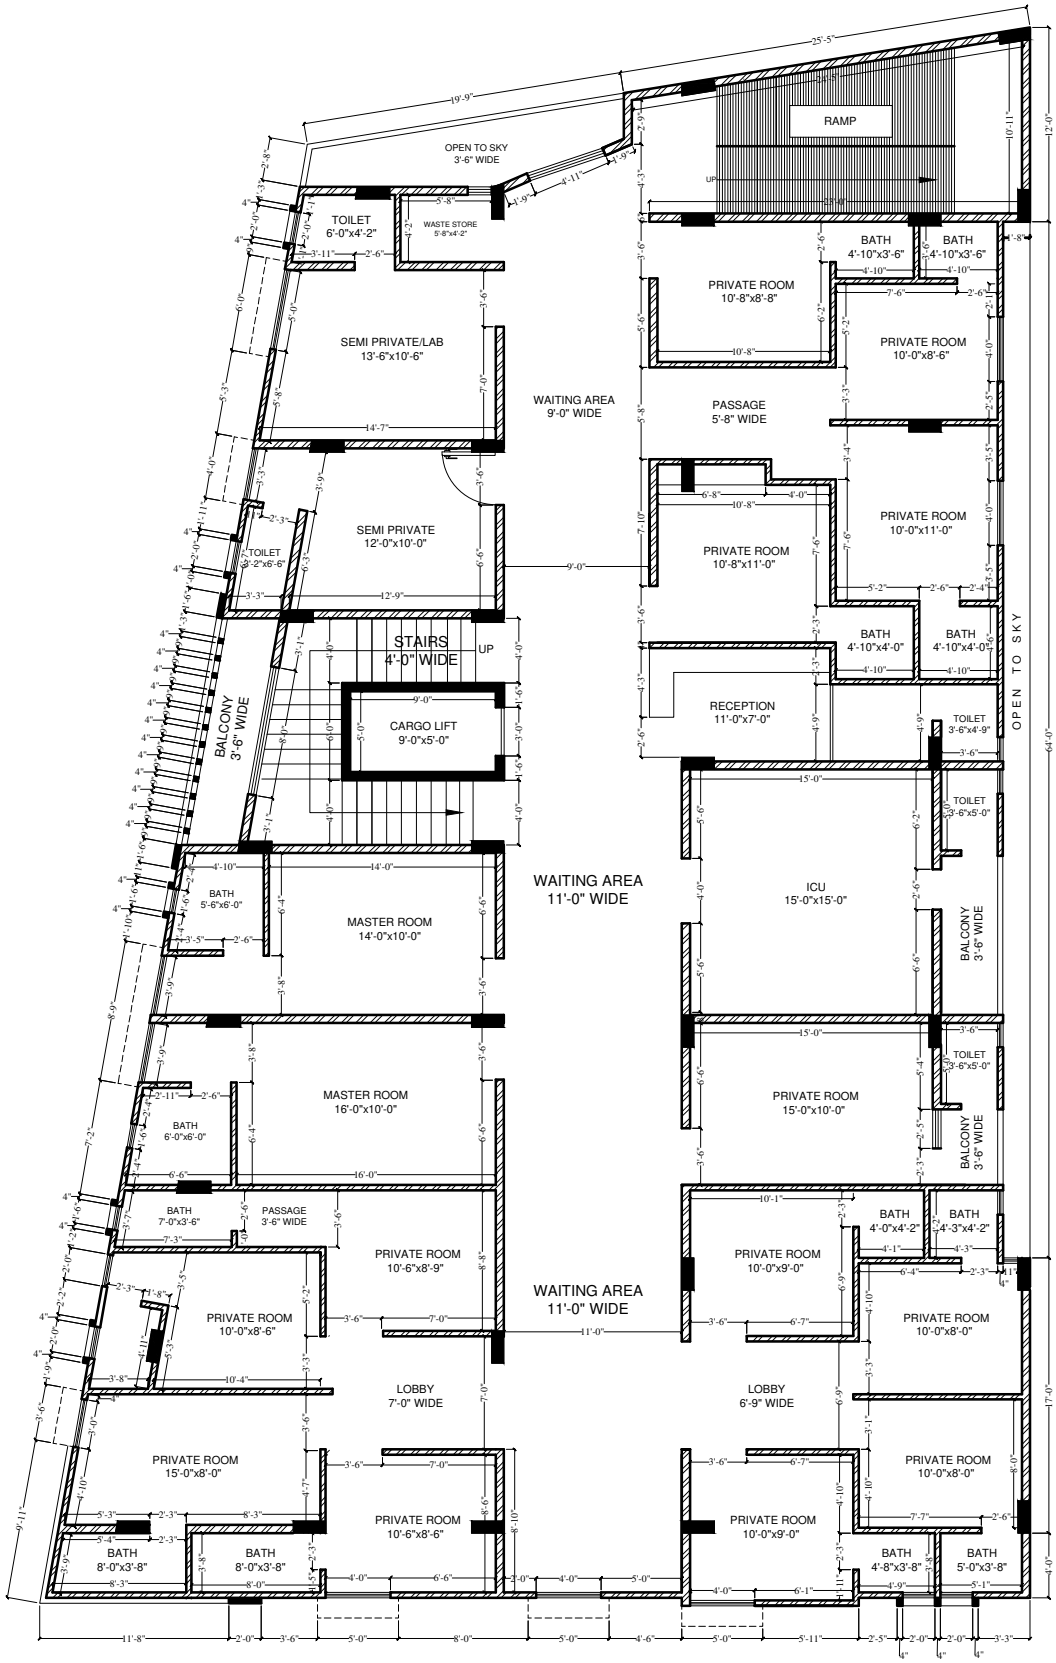

SECOND FLOOR WORKING PLAN

PROJECT:-	PROPOSED DRAWING FOR HOSPITAL	DATE:-	09 - 05 - 2025
TITLE:-	**SECOND FLOOR WORKING PLAN**	SCALE:-	1/8" = 1'-0"
ADDRESS:-	PLOT NO. _____WEST CITY HOSPITAL, MOMINABAD, ORANGI TOWN, K A R A C H I.	CHECKED BY:-	AGAH
		CAD BY:-	SUFYAN
		PRINT DATE:-	09 - 05 - 2025
CLIENT:-	DR.IMRAN	DRG NO. :-	A - 2025/01-01-02

THE CAD DESIGNER
ARCHITECT, ENGINEERS, PLANNERS
GULSHAN-E-HADEED, PHASE I & II EXT. BIN QASIM, KARACHI
CELL:0306-2776176

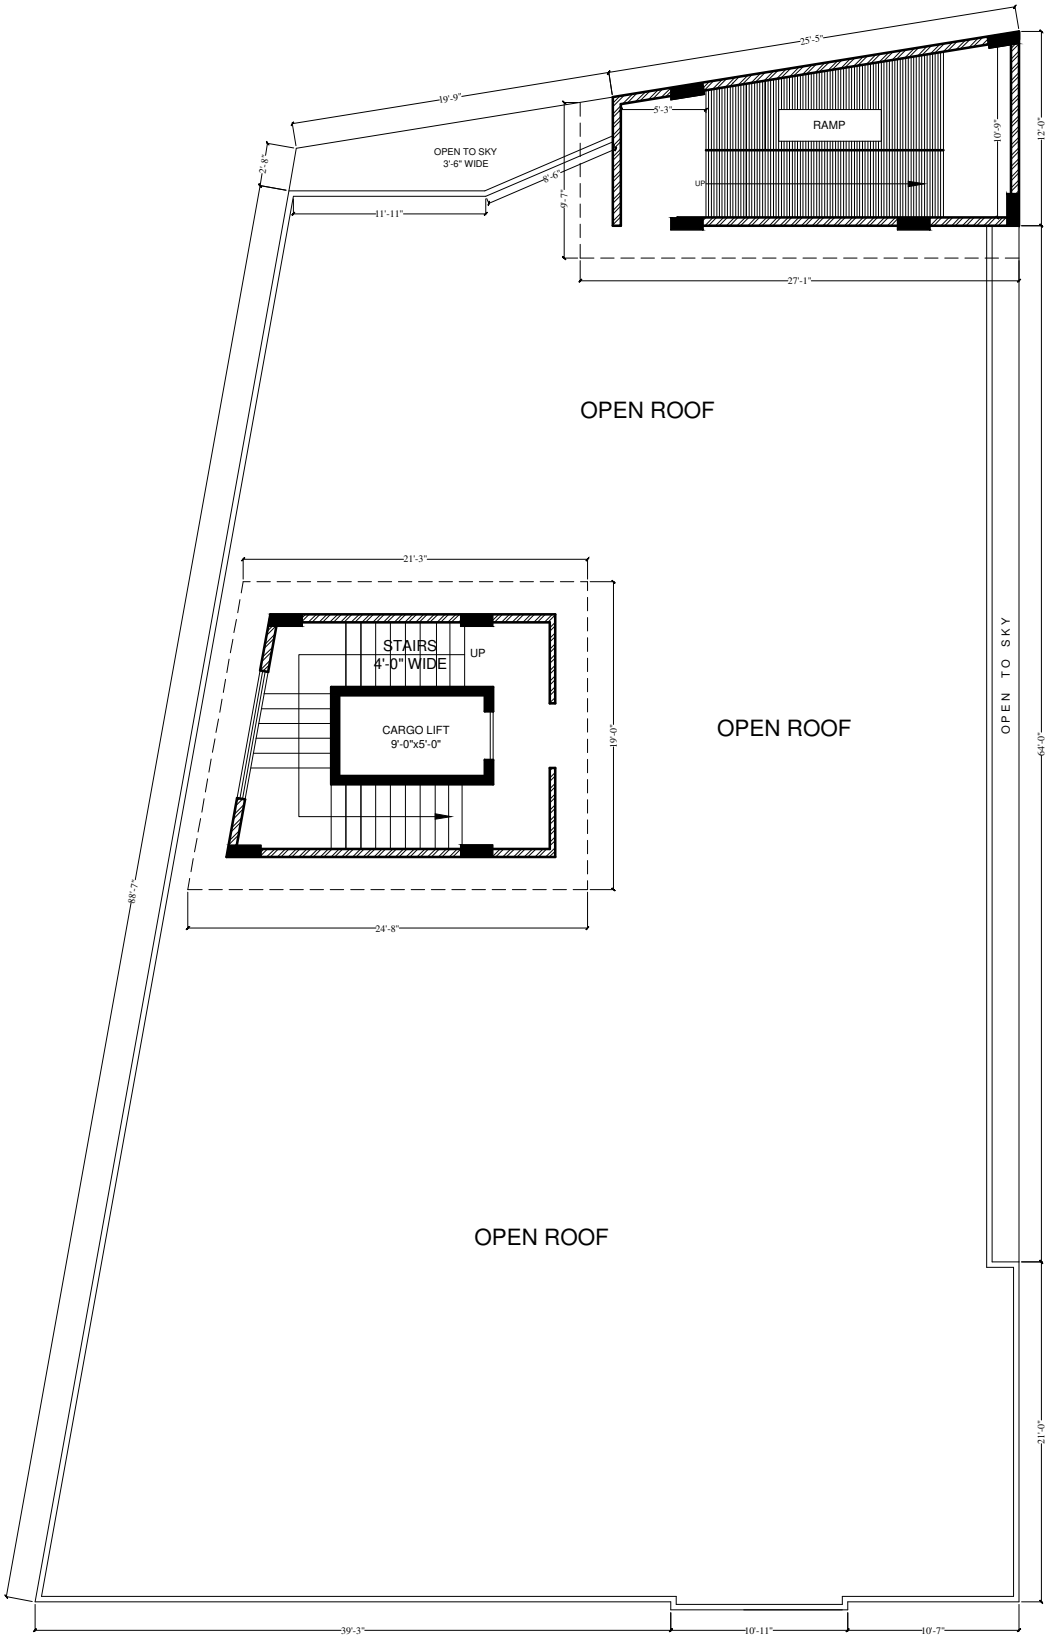

TOP FLOOR WORKING PLAN

PROJECT:-	PROPOSED DRAWING FOR HOSPITAL	DATE:-	09 - 05 - 2025
TITLE:-	**TOP FLOOR WORKING PLAN**	SCALE:-	1/8" = 1'-0"
ADDRESS:-	PLOT NO. _____WEST CITY HOSPITAL, MOMINABAD, ORANGI TOWN, K A R A C H I.	CHECKED BY:-	AGAH
		CAD BY:-	SUFYAN
		PRINT DATE:-	09 - 05 - 2025
CLIENT:-	DR.IMRAN	DRG NO. :-	A - 2025/01-01-02

THE CAD DESIGNER
ARCHITECT, ENGINEERS, PLANNERS
GULSHAN-E-HADEED, PHASE I & II EXT. BIN QASIM, KARACHI
CELL:0306-2776176


STRUCTURAL DRAWINGS

THE CAD DESIGNER
ARCHITECT, ENGINEERS, PLANNERS
GULSHAN-E-HADEED, PHASE I & II EXT. BIN
QASIM, KARACHI
CELL :0323-2446599
0306-2776176

GENERAL NOTES

1. THESE NOTES ARE APPLICABLE FOR ALL DRAWINGS UNLESS MENTIONED OTHERWISE.
2. CO-ORDINATE STRUCTURAL DRAWINGS WITH ARCHITECTURAL DRAWINGS INCASE OF DISCREPANCY REFER TO ARCHITECT.
3. ALL WORKS SHALL BE IN ACCORDANCE WITH RELEVENT ACI/BRITISH STANDARDS.
4. UNLESS NOTED OTHERWISE, ALL R.C.C WORK SHALL HAVE 1:2:4 MINIMUM OF FC' 3ksi (FOR BEAMS & SLABS) FC' 4ksi (FOR COLUMN & O.H.W.TANK WALL) Fy 60ksi WORK CYLINDER STRENGTH AT 28 DAYS.
5. ALL R.C.C WORK SHALL BE INTERNALLY VIBRATED THRU ELECTRO-MECHANICAL VIBRATOR..
6. CLEAR CONCRETE COVER TO MAIN REINFORCEMENT SHALL BE AS FOLLOWS:
   FOUNDATION. . . . . = 2"
   COLUMNS/BEAMS . . . . . = 1.5"
   SLAB. . . . . = 3/4"
7. ALL FOOTINGS TO BE PLACED 5'-0" BELOW N.G.L
8. IT IS THE RESPONSIBILITY OF THE CONTRACTOR TO CHECK SCHEDULE WITH STRUCTURAL DRGS, IN CASE OF DISCREPANCY REFER ARCHITECT.
9. LAYOUT DIMENSIONS MUST BE CHECKED BY THE ARCHITECT BEFORE STRUCTURAL DRAWINGS ARE ISSUED FOR CONSTRUCTION.
10. ALL R.C.C WORK SHALL BE CONTINUOUSLY MOIST CURED FOR 14-DAYS.
11. UNLESS NOTED OTHERWISE FORM WORK FROM R.C.C WORK SHALL BE REMOVED ACCORDING TO THE TIME INDICATED BELOW
    COLUMNS/BEAM SIDES . . . . . AFTER 48 HRS OF POURING
    BEAM BOTTOM . . . . . 28 DAYS
    SLAB . . . . . 21 DAYS


    ALL ELECTRICAL CONDUITS SHALL BE PLACED ON TOP OF BOTTOM REINFORCEMENT.
12. LAP LENGTH IN MAIN REINFORCMENT SHALL BE AS FOLLOWS UNLESS MENTIONED OTHERWISE
    COLUMN MAIN BARS ..... 48 DIA
    BEAM MAIN BARS ..... 48 DIA

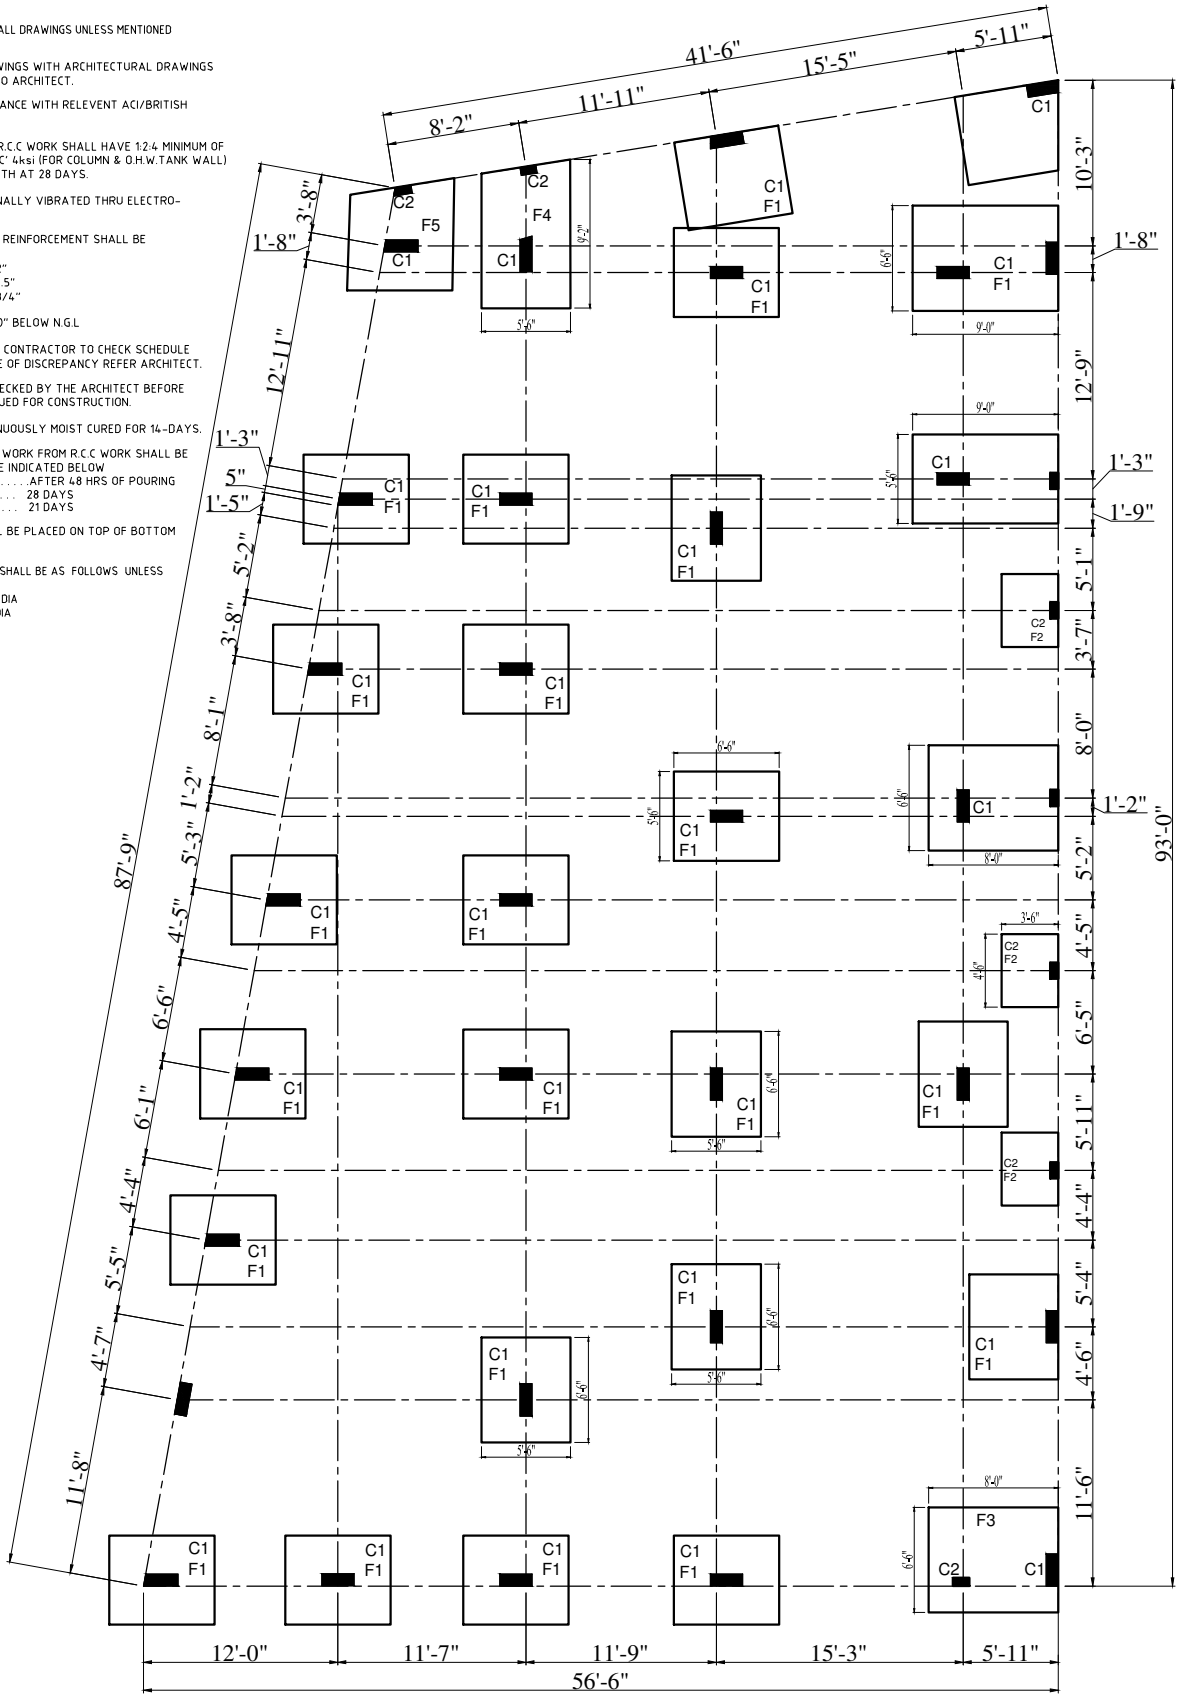


COLUMN LAYOUT PLAN

PROJECT:-	PROPOSED DRAWING FOR HOSPITAL	DATE:-	09 - 05 - 2025
TITLE:-	**PLINTH BEAM PLAN**	SCALE:-	1/8" = 1'-0"
ADDRESS:-	PLOT NO. _____WEST CITY HOSPITAL, MOMINABAD, ORANGI TOWN, K A R A C H I.	CHECKED BY:-	AGAH
		CAD BY:-	SUFYAN
		PRINT DATE:-	09 - 05 - 2025
CLIENT:-	DR.IMRAN	DRG NO. :-	A - 2025/01-01-02


THE CAD DESIGNER
ARCHITECT, ENGINEERS, PLANNERS
GULSHAN-E-HADEED, PHASE I & II EXT. BIN QASIM, KARACHI
CELL:0306-2776176

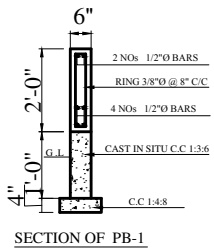

SECTION OF PB-1

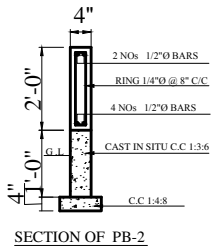

SECTION OF PB-2

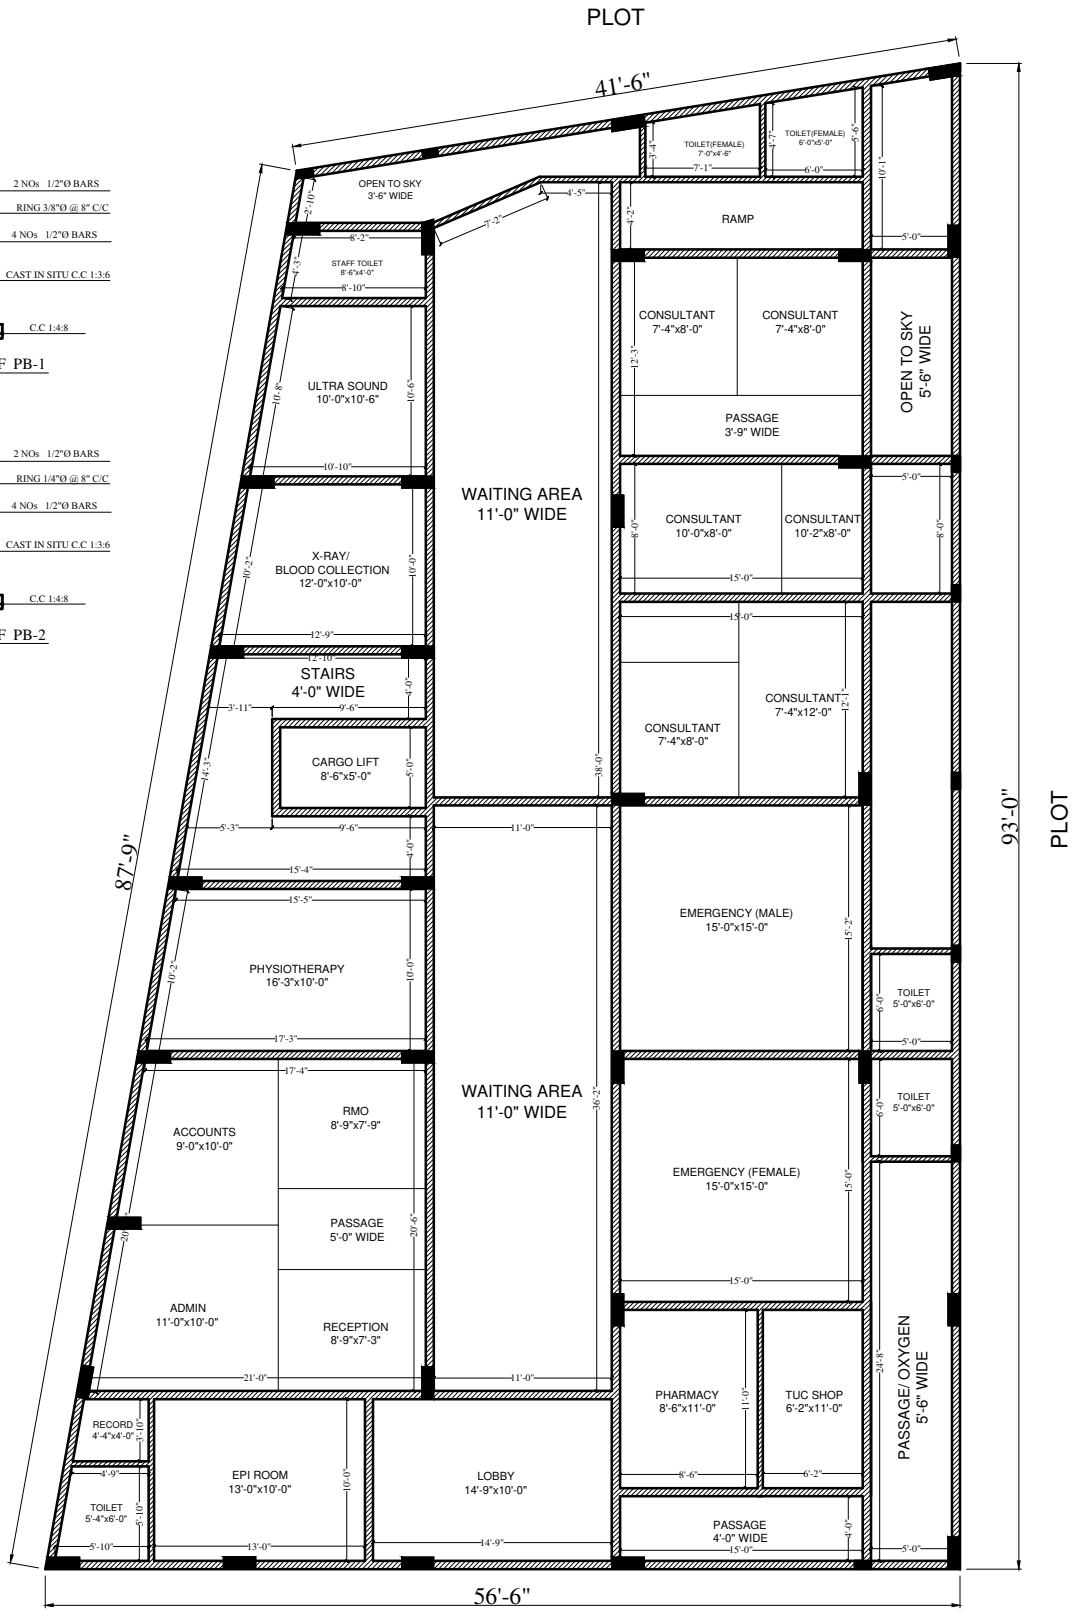


MAIN ROAD


PLINTH BEAM PLAN

PROJECT:-	PROPOSED DRAWING FOR HOSPITAL	DATE:-	09 - 05 - 2025
TITLE:-	**PLINTH BEAM PLAN**	SCALE:-	1/8" = 1'-0"
ADDRESS:-	PLOT NO. _____WEST CITY HOSPITAL, MOMINABAD, ORANGI TOWN, K A R A C H I.	CHECKED BY:-	AGAH
		CAD BY:-	SUFYAN
		PRINT DATE:-	09 - 05 - 2025
CLIENT:-	DR.IMRAN	DRG NO. :-	A - 2025/01-01-02


THE CAD DESIGNER
ARCHITECT, ENGINEERS, PLANNERS
GULSHAN-E-HADEED, PHASE I & II EXT. BIN QASIM, KARACHI
CELL:0306-2776176

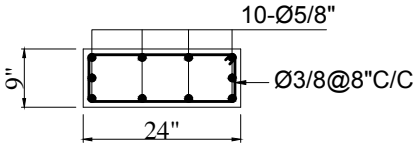


SEC.OF C-1

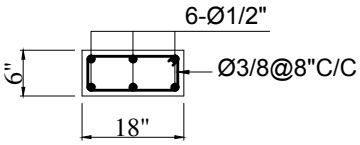

SEC.OF C-2

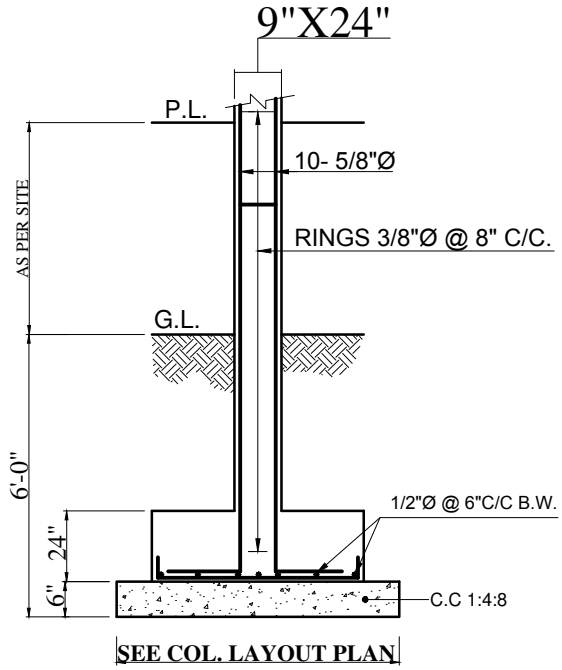

SEC. OF COLUMN (C-1)

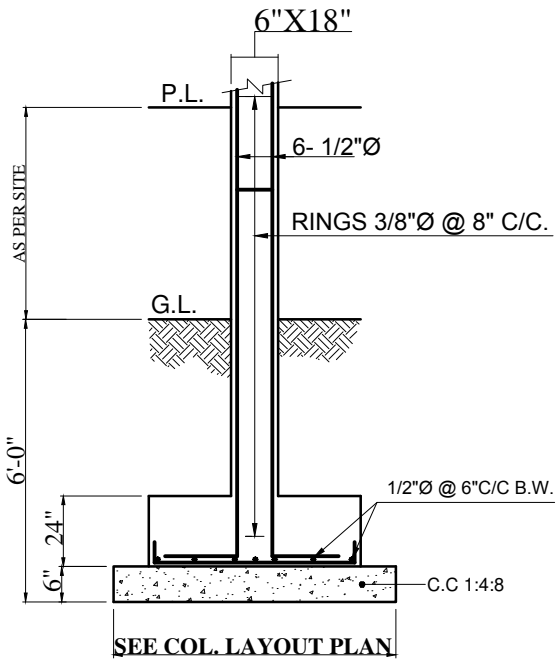


SEC. OF COLUMN (C-2)
BOUNDARY WALL


COLUMN DETAIL & SECTION

PROJECT:-	PROPOSED DRAWING FOR HOSPITAL	DATE:-	09 - 05 - 2025
TITLE:-	**COLUMN DETAIL & SECTON**	SCALE:-	1/8" = 1'-0"
ADDRESS:-	PLOT NO. _____WEST CITY HOSPITAL, MOMINABAD, ORANGI TOWN, K A R A C H I.	CHECKED BY:-	AGAH
		CAD BY:-	SUFYAN
		PRINT DATE:-	09 - 05 - 2025
CLIENT:-	DR.IMRAN	DRG NO. :-	A - 2025/01-01-02


THE CAD DESIGNER
ARCHITECT, ENGINEERS, PLANNERS
GULSHAN-E-HADEED, PHASE I & II EXT. BIN QASIM, KARACHI
CELL:0306-2776176

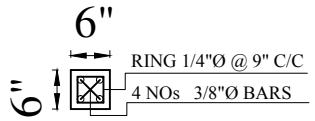


SECTION OF R.C.C LINTOL

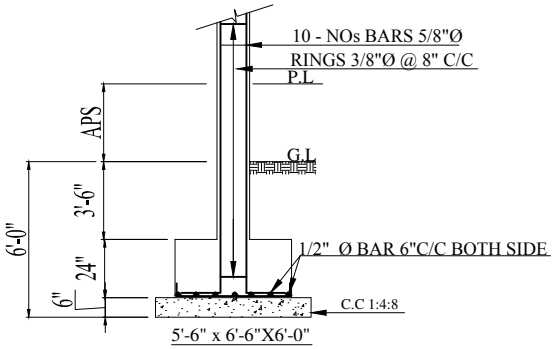

SECTON OF R.C.C COLUMN C-1

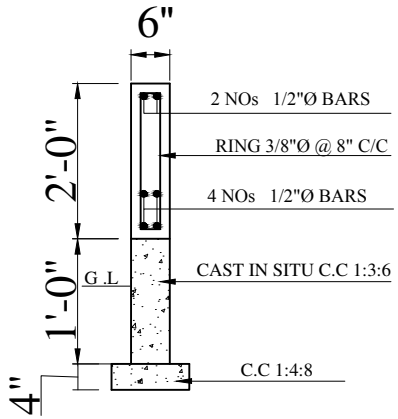

SECTION OF PLINTH BEAM

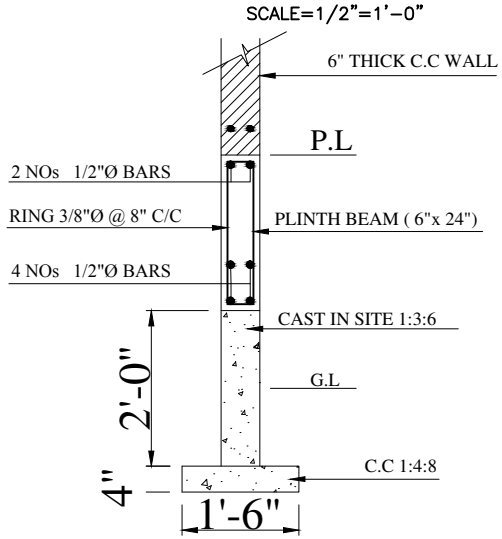

SECTON OF WALL

SCHEDULE OF R.C.C(Ratio 1:2:4)

R.C.C COLUMN (9"x24") C-1

10 NOs VERTICAL 5/8"Ø BARS
RINGS 3/8"Ø @ 8" C/C

R.C.C COLUMN (6"x18") C-2 BOUNDARY WALL

6 NOs VERTICAL 1/2"Ø BARS
RINGS 1/4"Ø @ 8" C/C

R.C.C BEAM (6"x 24")

TOP 4 NOs 1/2"Ø BARS
BOTTOM 4 NOs 1/2"Ø BARS
RINGs 3/8"Ø @ 8" C/C

R.C.C SLAB (6"THICK)

SHORT SPIAN 1/2"Ø @ 5" C/C
LONG SPIAN 3/8"Ø @ 7" C/C

R.C.C CONCEILD BEAM


10 NOs 5/8"Ø BARs
RINGs 3/8"Ø @ 8" C/C

R.C.C PLINTH BEAM


6 NOs 5/8"Ø BARs
RINGs 3/8"Ø @ 8" C/C

PROJECT:-	PROPOSED DRAWING FOR HOSPITAL	DATE:-	09 - 05 - 2025
TITLE:-	RCC DETAILS	SCALE:-	1/8" = 1'-0"
ADDRESS:-	PLOT NO. _____WEST CITY HOSPITAL, MOMINABAD, ORANGI TOWN, K A R A C H I.	CHECKED BY:-	AGAH
		DESIGN BY:-	SUFYAN
		PRINT DATE:-	09 - 05 - 2025
CLIENT:-	DR.IMRAN	DRG NO. :-	A - 2025/01-01-02


THE CAD DESIGNER
ARCHITECT, ENGINEERS, PLANNERS
GULSHAN-E-HADEED, PHASE I & II EXT. BIN QASIM, KARACHI
CELL:0306-2776176

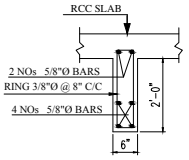


SECTION OF BEAM (B-1)

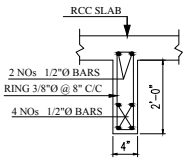


SECTION OF BEAM (B-2)

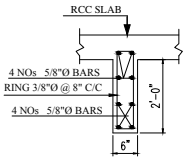


SECTION OF BEAM (B-3)

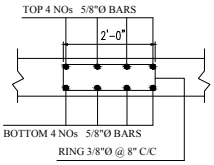

SECTION OF CONCEALED BEAM-1

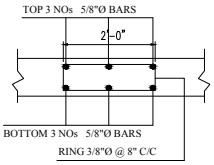


SECTION OF CONCEALED BEAM

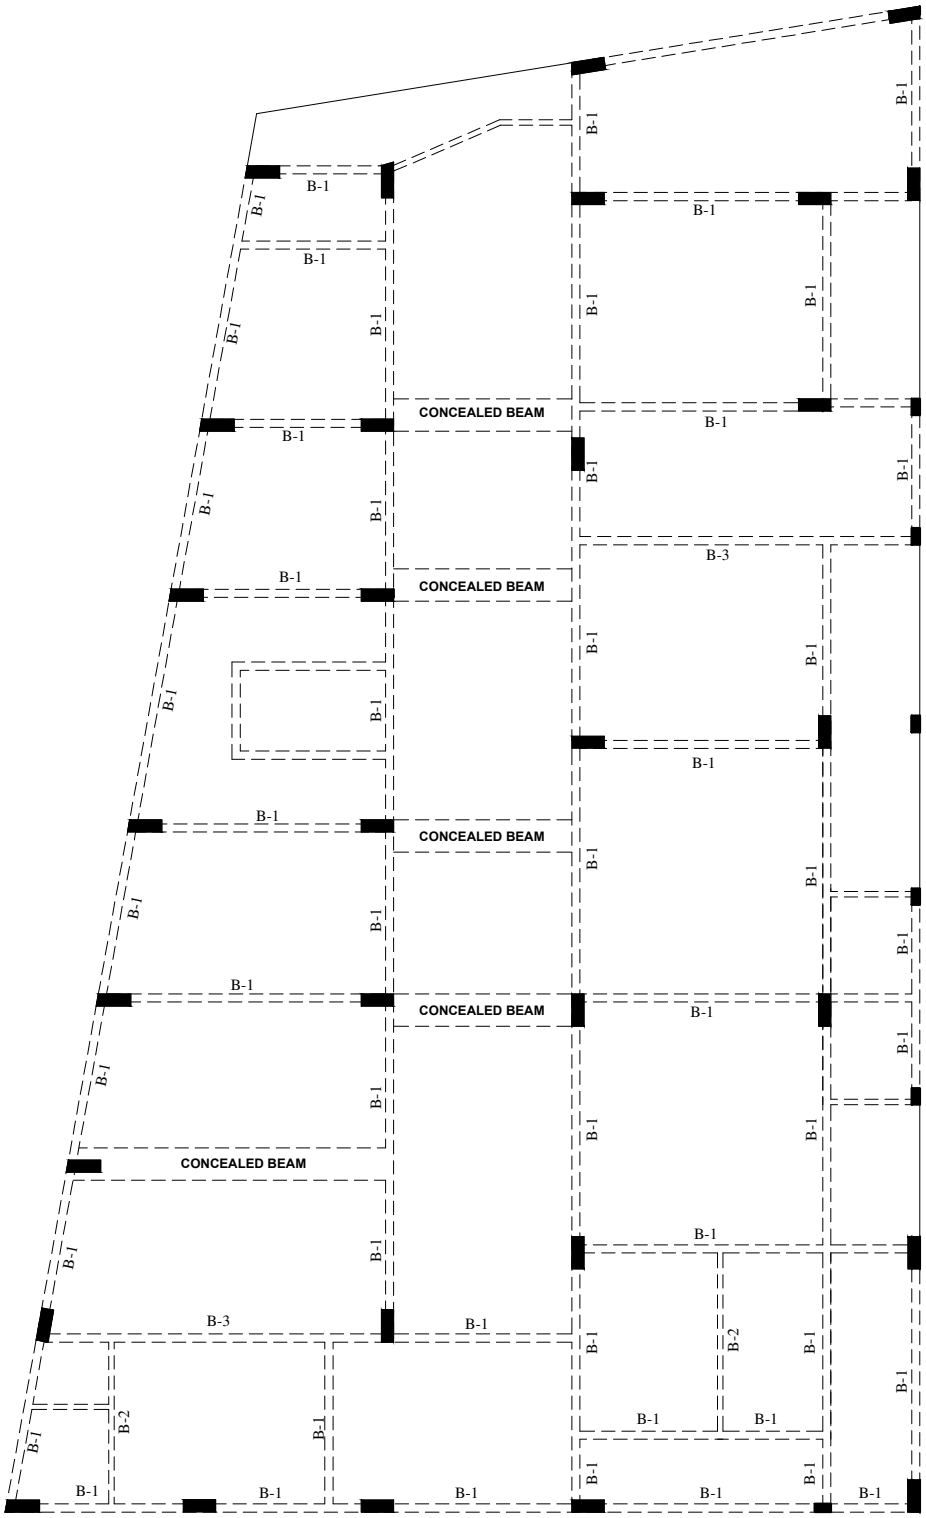


GROUND FLOOR ROOF BEAM PLAN

PROJECT:-	PROPOSED DRAWING FOR HOSPITAL	DATE:-	09 - 05 - 2025
TITLE:-	**GROUND FLOOR ROOF BEAM PLAN**	SCALE:-	1/8" = 1'-0"
ADDRESS:-	PLOT NO. _____WEST CITY HOSPITAL, MOMINABAD, ORANGI TOWN, K A R A C H I.	CHECKED BY:-	AGAH
		CAD BY:-	SUFYAN
		PRINT DATE:-	09 - 05 - 2025
CLIENT:-	DR.IMRAN	DRG NO. :-	A - 2025/01-01-02


THE CAD DESIGNER
ARCHITECT, ENGINEERS, PLANNERS
GULSHAN-E-HADEED, PHASE I & II EXT. BIN QASIM, KARACHI
CELL:0306-2776176

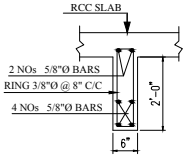


SECTION OF BEAM (B-1)

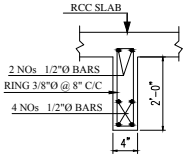


SECTION OF BEAM (B-2)

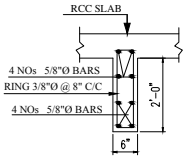


SECTION OF BEAM (B-3)

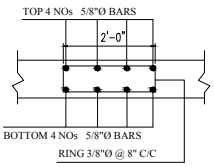

SECTION OF CONCEALED BEAM-1

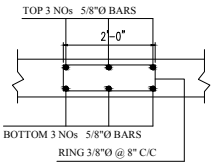


SECTION OF CONCEALED BEAM

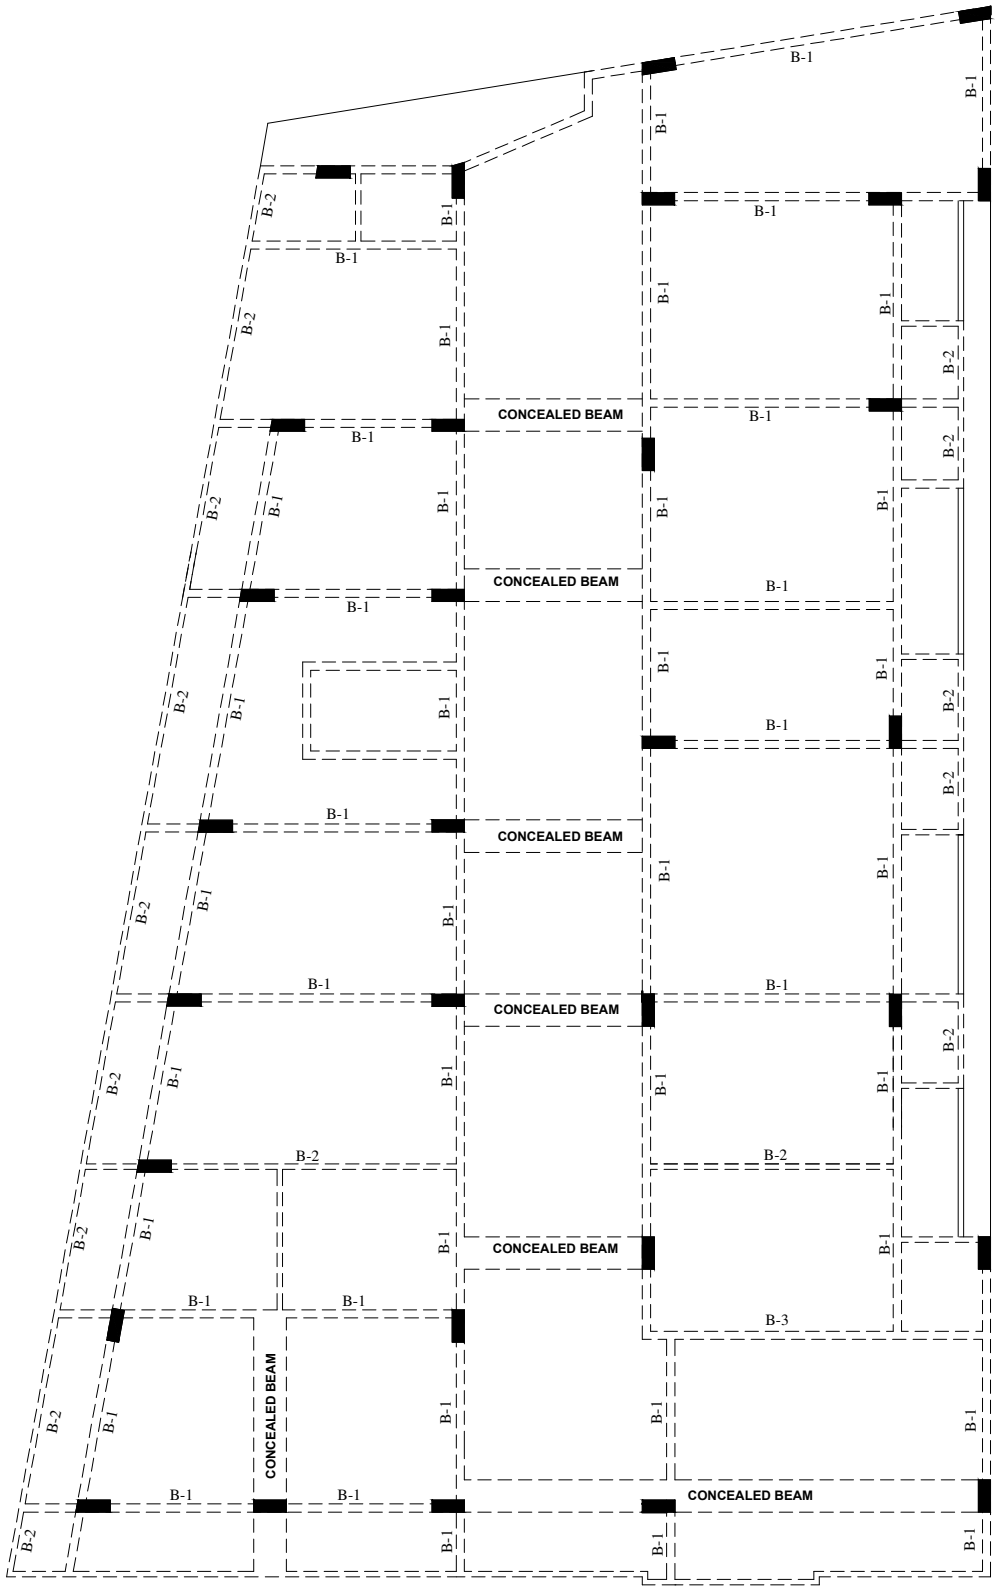


FIRST FLOOR ROOF BEAM PLAN

PROJECT:-	PROPOSED DRAWING FOR HOSPITAL	DATE:-	09 - 05 - 2025
TITLE:-	**FIRST FLOOR ROOF BEAM PLAN**	SCALE:-	1/8" = 1'-0"
ADDRESS:-	PLOT NO. _____WEST CITY HOSPITAL, MOMINABAD, ORANGI TOWN, K A R A C H I.	CHECKED BY:-	AGAH
		CAD BY:-	SUFYAN
		PRINT DATE:-	09 - 05 - 2025
CLIENT:-	DR.IMRAN	DRG NO. :-	A - 2025/01-01-02


THE CAD DESIGNER
ARCHITECT, ENGINEERS, PLANNERS
GULSHAN-E-HADEED, PHASE I & II EXT. BIN QASIM, KARACHI
CELL:0306-2776176

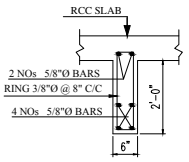


SECTION OF BEAM (B-1)

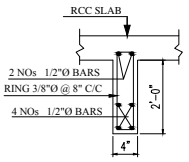


SECTION OF BEAM (B-2)

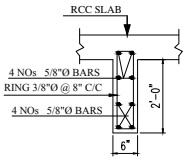


SECTION OF BEAM (B-3)

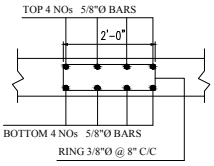

SECTION OF CONCEALED BEAM-1

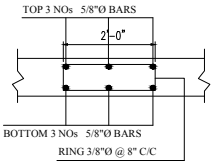


SECTION OF CONCEALED BEAM

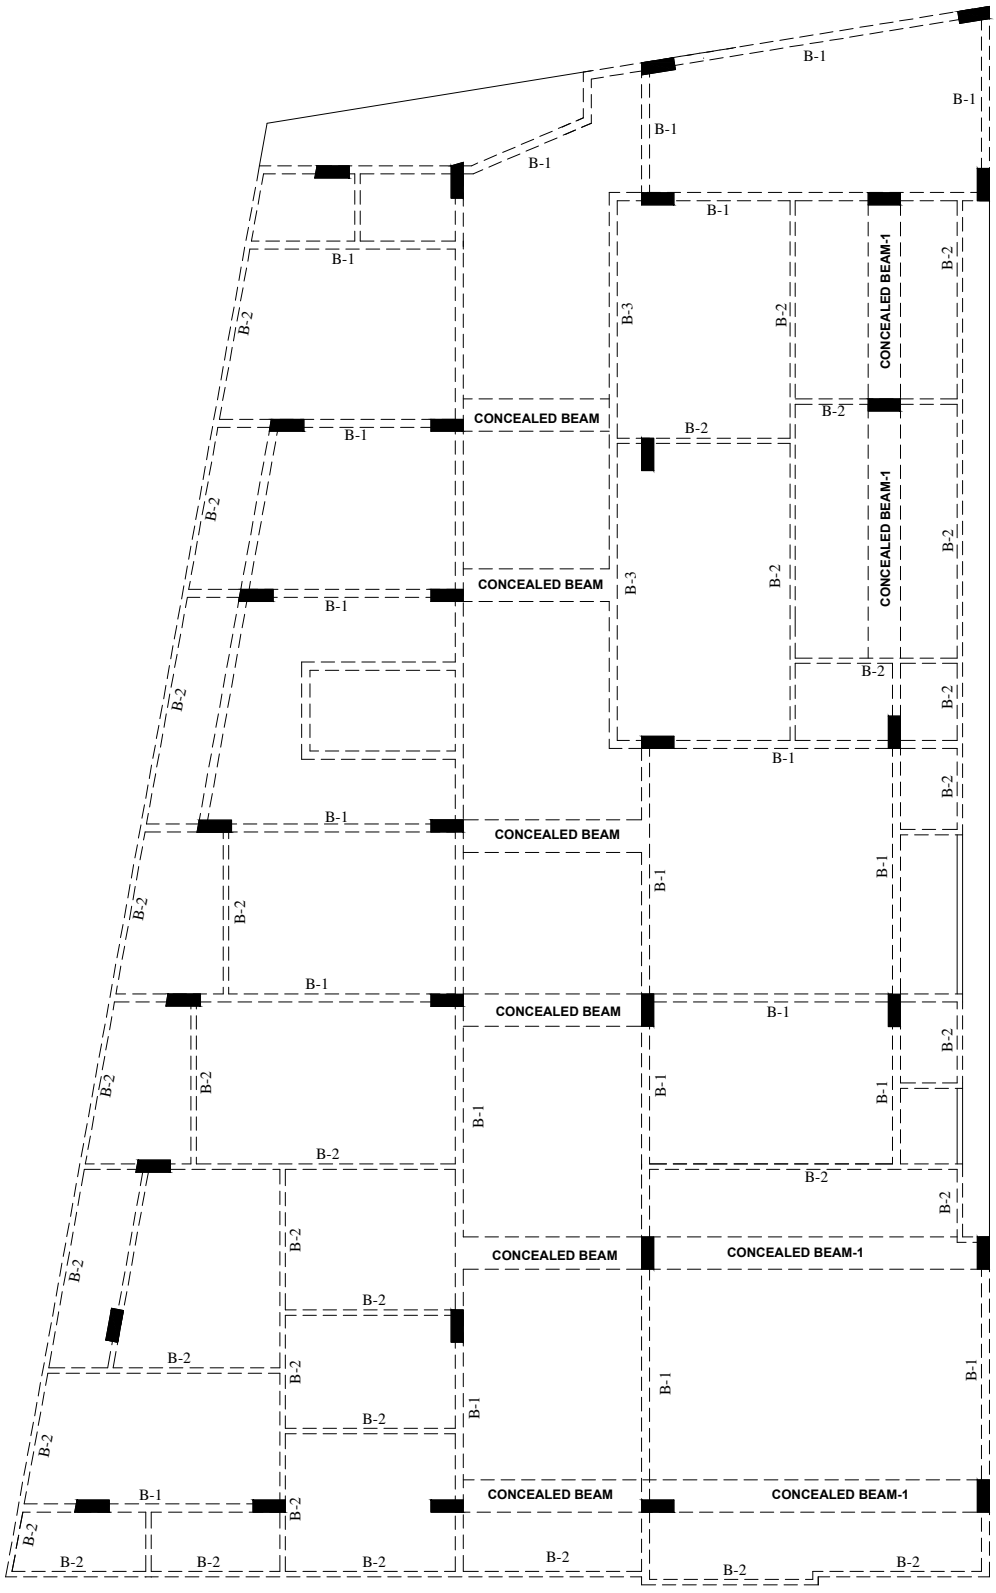


SECOND FLOOR ROOF BEAM PLAN

PROJECT:-	PROPOSED DRAWING FOR HOSPITAL	DATE:-	09 - 05 - 2025
TITLE:-	**SECOND FLOOR ROOF BEAM PLAN**	SCALE:-	1/8" = 1'-0"
ADDRESS:-	PLOT NO. _____WEST CITY HOSPITAL, MOMINABAD, ORANGI TOWN, K A R A C H I.	CHECKED BY:-	AGAH
		CAD BY:-	SUFYAN
		PRINT DATE:-	09 - 05 - 2025
CLIENT:-	DR.IMRAN	DRG NO. :-	A - 2025/01-01-02


THE CAD DESIGNER
ARCHITECT, ENGINEERS, PLANNERS
GULSHAN-E-HADEED, PHASE I & II EXT. BIN QASIM, KARACHI
CELL:0306-2776176

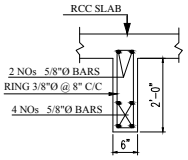


SECTION OF BEAM (B-1)

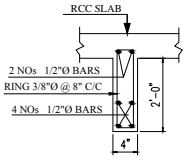


SECTION OF BEAM (B-2)

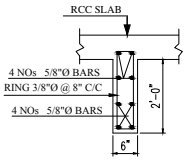


SECTION OF BEAM (B-3)

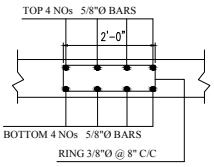

SECTION OF CONCEALED BEAM-1

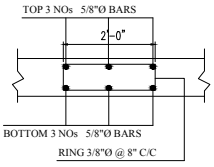

SECTION OF CONCEALED BEAM

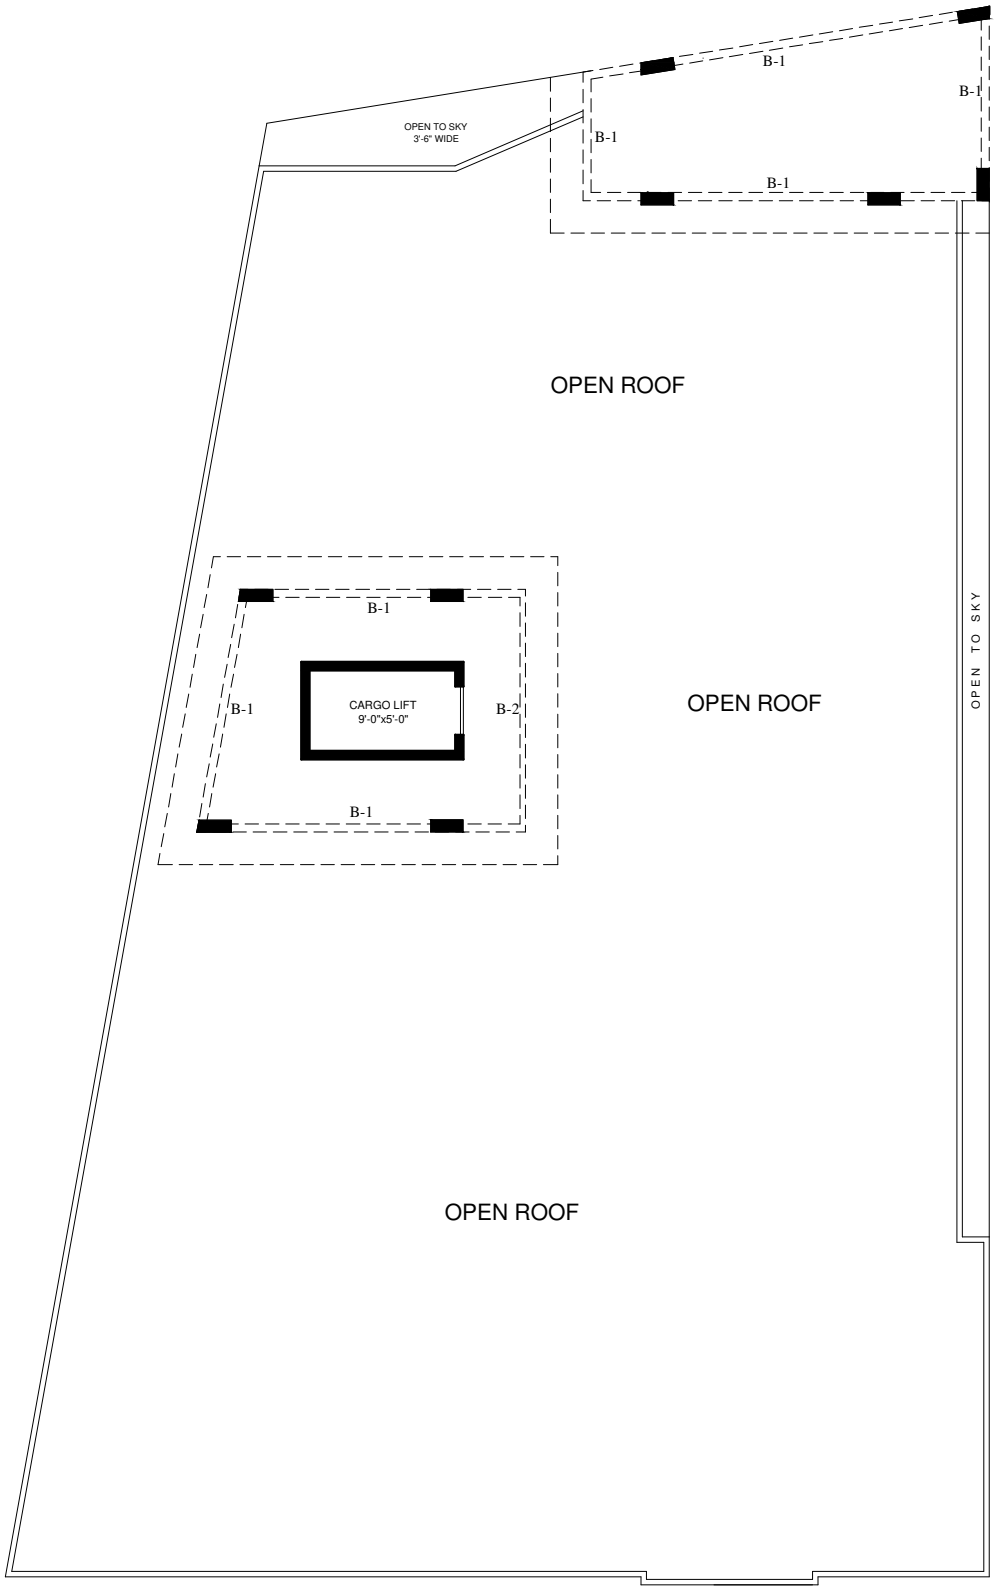

TOP FLOOR ROOF BEAM PLAN

PROJECT:-	PROPOSED DRAWING FOR HOSPITAL	DATE:-	09 - 05 - 2025
TITLE:-	**TOP FLOOR ROOF BEAM PLAN**	SCALE:-	1/8" = 1'-0"
ADDRESS:-	PLOT NO. _____WEST CITY HOSPITAL, MOMINABAD, ORANGI TOWN, K A R A C H I.	CHECKED BY:-	AGAH
		CAD BY:-	SUFYAN
		PRINT DATE:-	09 - 05 - 2025
CLIENT:-	DR.IMRAN	DRG NO. :-	A - 2025/01-01-02


THE CAD DESIGNER
ARCHITECT, ENGINEERS, PLANNERS
GULSHAN-E-HADEED, PHASE I & II EXT. BIN QASIM, KARACHI
CELL:0306-2776176

ELECTRICAL DRAWINGS

THE CAD DESIGNER
ARCHITECT, ENGINEERS, PLANNERS
GULSHAN-E-HADEED, PHASE I & II EXT. BIN
QASIM, KARACHI
CELL :0323-2446599
0306-2776176

LEGEND

S.No.	SYMBOLS	DESCRIPTION
01		FLUORESCENT LAMP PHILIPS GCD-240 WITH 2X40 WATT LAMPS.
02		FAN
03		INCANDESCENT LAMP PHILIPS NCD-533 WITH 2X100W LAMPS.
04		EXHAUST FAN 12"SWEEP.
05		POWER PLUG 15 AMPS,220 VOLTS GRADE.
06		LIGHT PLUG 10 AMPS,220 VOLTS GRADE(UNIVERSAL TYPE)
07		PIANO SWITCH 10 AMPS,220 VOLTS GRADE.
08		TELEPHONE ROSSET.
09		ELECTRICAL DISTRIBUTION BOARD.
10		ONE WAY 10A SWITCH
11		DIMMER
12		SURFACE DOWN LIGHT 17W
13		CEILING MOUNTED COMPACT POWER LIGHT 23W
14		LED CEILING DOWN LIGHT 7W
15		LED CEILING DOWN LIGHT 11W
16		LED CEILING DOWN LIGHT 23W
17		WEATHER PROOF CEILING LIGHT
18		WEATHER PROOF WALL LIGHT
19		WALL LIGHT 14W
20		MIRROR LIGHT
21		LED FLOOD LIGHT
22		LED STRIP LIGHT
23		CHANDELIER
24		UNDER GROUND LIGHT 15W
25		EXHAUST FAN
26		GATE LIGHT
27		BELL PUSH BUTTON, INTERCOM & CAMERA

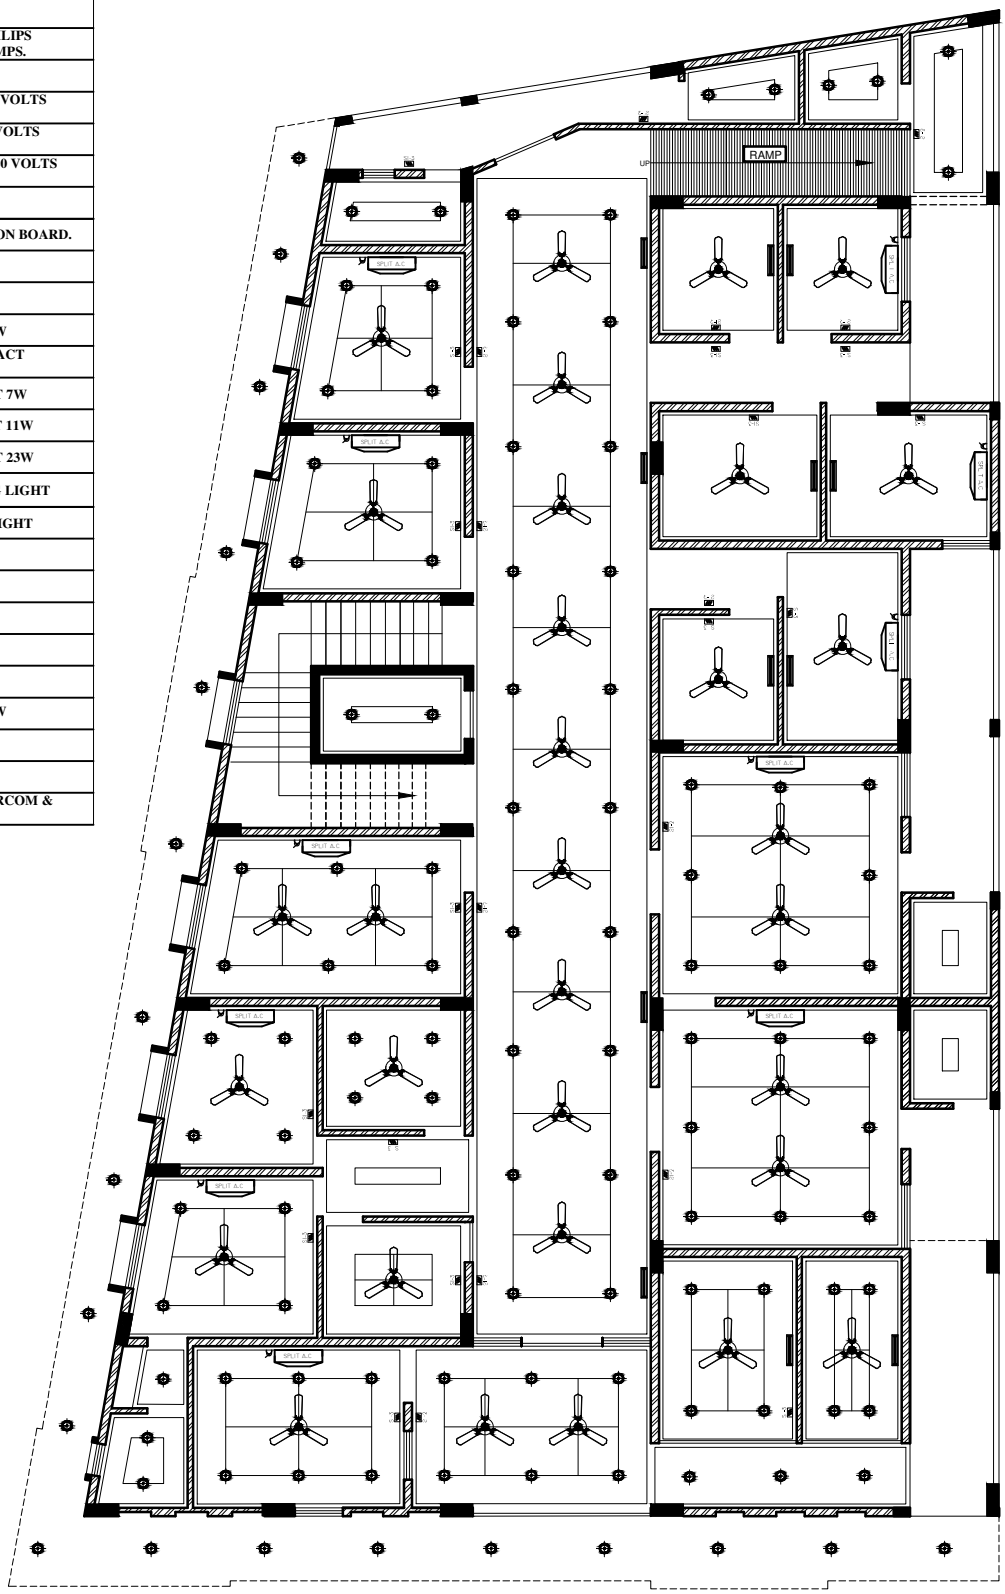


GROUND FLOOR ELECTRICAL PLAN

PROJECT:-	PROPOSED DRAWING FOR HOSPITAL	DATE:-	09 - 05 - 2025
TITLE:-	**GROUND FLOOR ELECTRICAL PLAN**	SCALE:-	1/8" = 1'-0"
ADDRESS:-	PLOT NO. _____WEST CITY HOSPITAL, MOMINABAD, ORANGI TOWN, K A R A C H I.	CHECKED BY:-	AGAH
		CAD BY:-	SUFYAN
		PRINT DATE:-	09 - 05 - 2025
CLIENT:-	DR.IMRAN	DRG NO. :-	A - 2025/01-01-02

THE CAD DESIGNER
ARCHITECT, ENGINEERS, PLANNERS
GULSHAN-E-HADEED, PHASE I & II EXT. BIN QASIM, KARACHI
CELL:0306-2776176

LEGEND

S.No.	SYMBOLS	DESCRIPTION
01		FLUORESCENT LAMP PHILIPS GCD-240 WITH 2X40 WATT LAMPS.
02		FAN
03		INCANDESCENT LAMP PHILIPS NCD-533 WITH 2X100W LAMPS.
04		EXHAUST FAN 12"SWEEP.
05		POWER PLUG 15 AMPS,220 VOLTS GRADE.
06		LIGHT PLUG 10 AMPS,220 VOLTS GRADE(UNIVERSAL TYPE)
07		PIANO SWITCH 10 AMPS,220 VOLTS GRADE.
08		TELEPHONE ROSSET.
09		ELECTRICAL DISTRIBUTION BOARD.
10		ONE WAY 10A SWITCH
11		DIMMER
12		SURFACE DOWN LIGHT 17W
13		CEILING MOUNTED COMPACT POWER LIGHT 23W
14		LED CEILING DOWN LIGHT 7W
15		LED CEILING DOWN LIGHT 11W
16		LED CEILING DOWN LIGHT 23W
17		WEATHER PROOF CEILING LIGHT
18		WEATHER PROOF WALL LIGHT
19		WALL LIGHT 14W
20		MIRROR LIGHT
21		LED FLOOD LIGHT
22		LED STRIP LIGHT
23		CHANDELIER
24		UNDER GROUND LIGHT 15W
25		EXHAUST FAN
26		GATE LIGHT
27		BELL PUSH BUTTON, INTERCOM & CAMERA

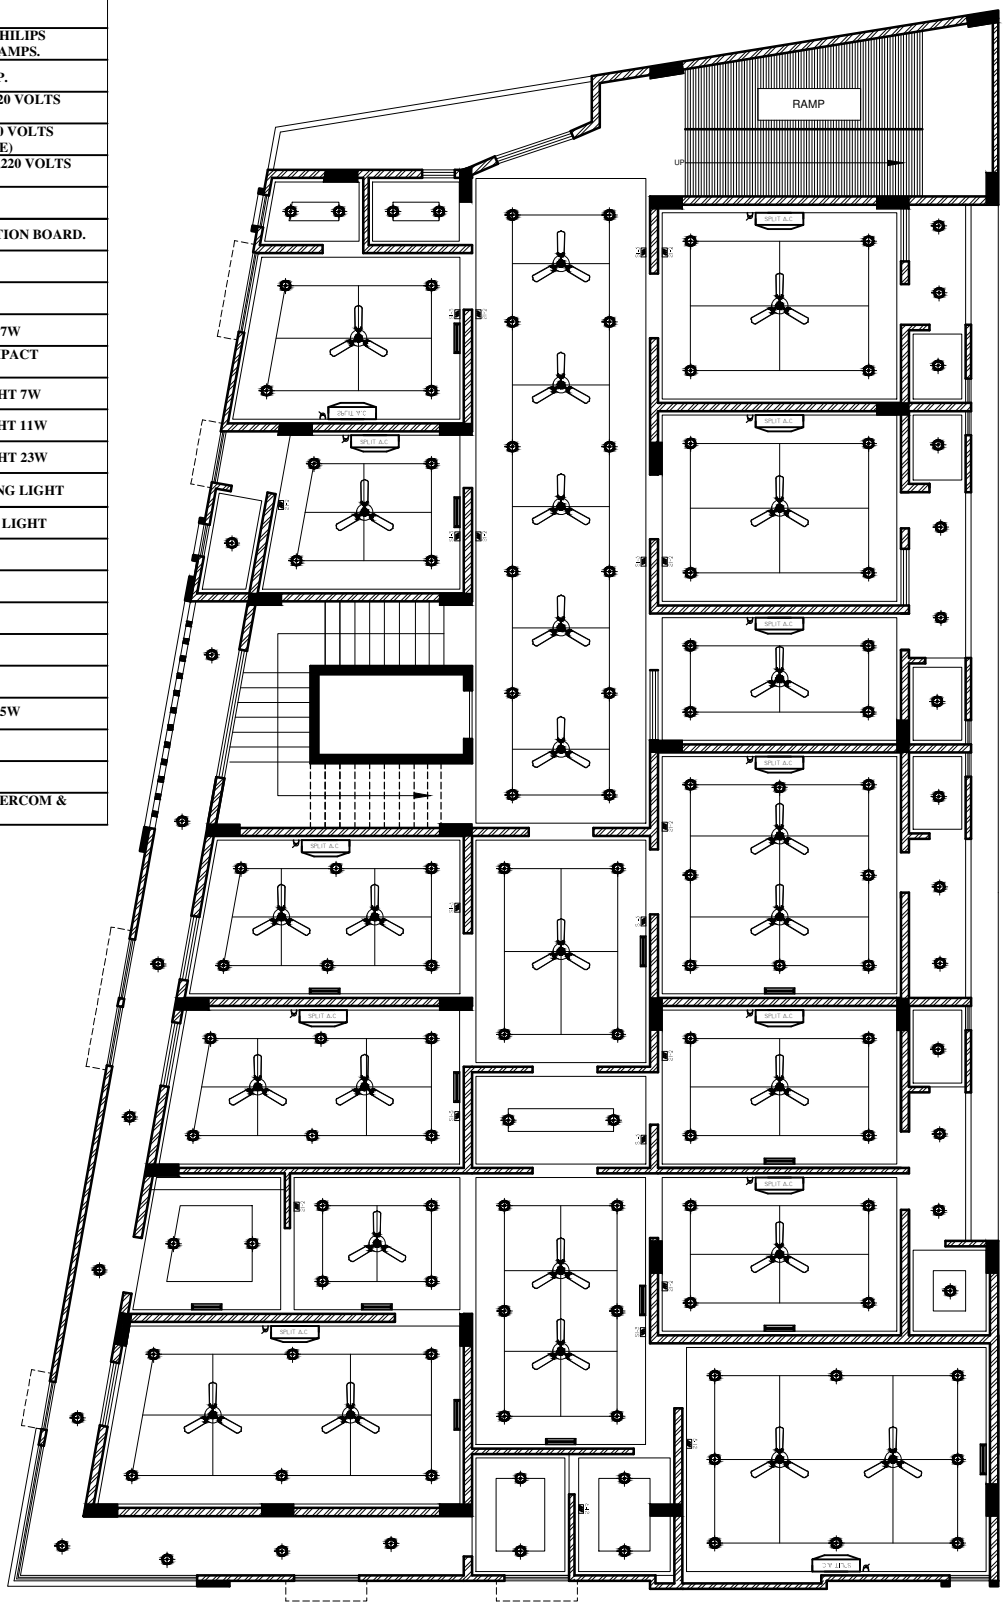


FIRST FLOOR ELECTRICAL PLAN

PROJECT:-	PROPOSED DRAWING FOR HOSPITAL	DATE:-	09 - 05 - 2025
TITLE:-	**FIRST FLOOR ELECTRICAL PLAN**	SCALE:-	1/8" = 1'-0"
ADDRESS:-	PLOT NO. _____WEST CITY HOSPITAL, MOMINABAD, ORANGI TOWN, K A R A C H I.	CHECKED BY:-	AGAH
		CAD BY:-	SUFYAN
		PRINT DATE:-	09 - 05 - 2025
CLIENT:-	DR.IMRAN	DRG NO. :-	A - 2025/01-01-02

THE CAD DESIGNER
ARCHITECT, ENGINEERS, PLANNERS
GULSHAN-E-HADEED, PHASE I & II EXT. BIN QASIM, KARACHI
CELL:0306-2776176

LEGEND

S.No.	SYMBOLS	DESCRIPTION
01		FLUORESCENT LAMP PHILIPS GCD-240 WITH 2X40 WATT LAMPS.
02		FAN
03		INCANDESCENT LAMP PHILIPS NCD-533 WITH 2X100W LAMPS.
04		EXHAUST FAN 12"SWEEP.
05		POWER PLUG 15 AMPS,220 VOLTS GRADE.
06		LIGHT PLUG 10 AMPS,220 VOLTS GRADE(UNIVERSAL TYPE)
07		PIANO SWITCH 10 AMPS,220 VOLTS GRADE.
08		TELEPHONE ROSSET.
09		ELECTRICAL DISTRIBUTION BOARD.
10		ONE WAY 10A SWITCH
11		DIMMER
12		SURFACE DOWN LIGHT 17W
13		CEILING MOUNTED COMPACT POWER LIGHT 23W
14		LED CEILING DOWN LIGHT 7W
15		LED CEILING DOWN LIGHT 11W
16		LED CEILING DOWN LIGHT 23W
17		WEATHER PROOF CEILING LIGHT
18		WEATHER PROOF WALL LIGHT
19		WALL LIGHT 14W
20		MIRROR LIGHT
21		LED FLOOD LIGHT
22		LED STRIP LIGHT
23		CHANDELIER
24		UNDER GROUND LIGHT 15W
25		EXHAUST FAN
26		GATE LIGHT
27		BELL PUSH BUTTON, INTERCOM & CAMERA

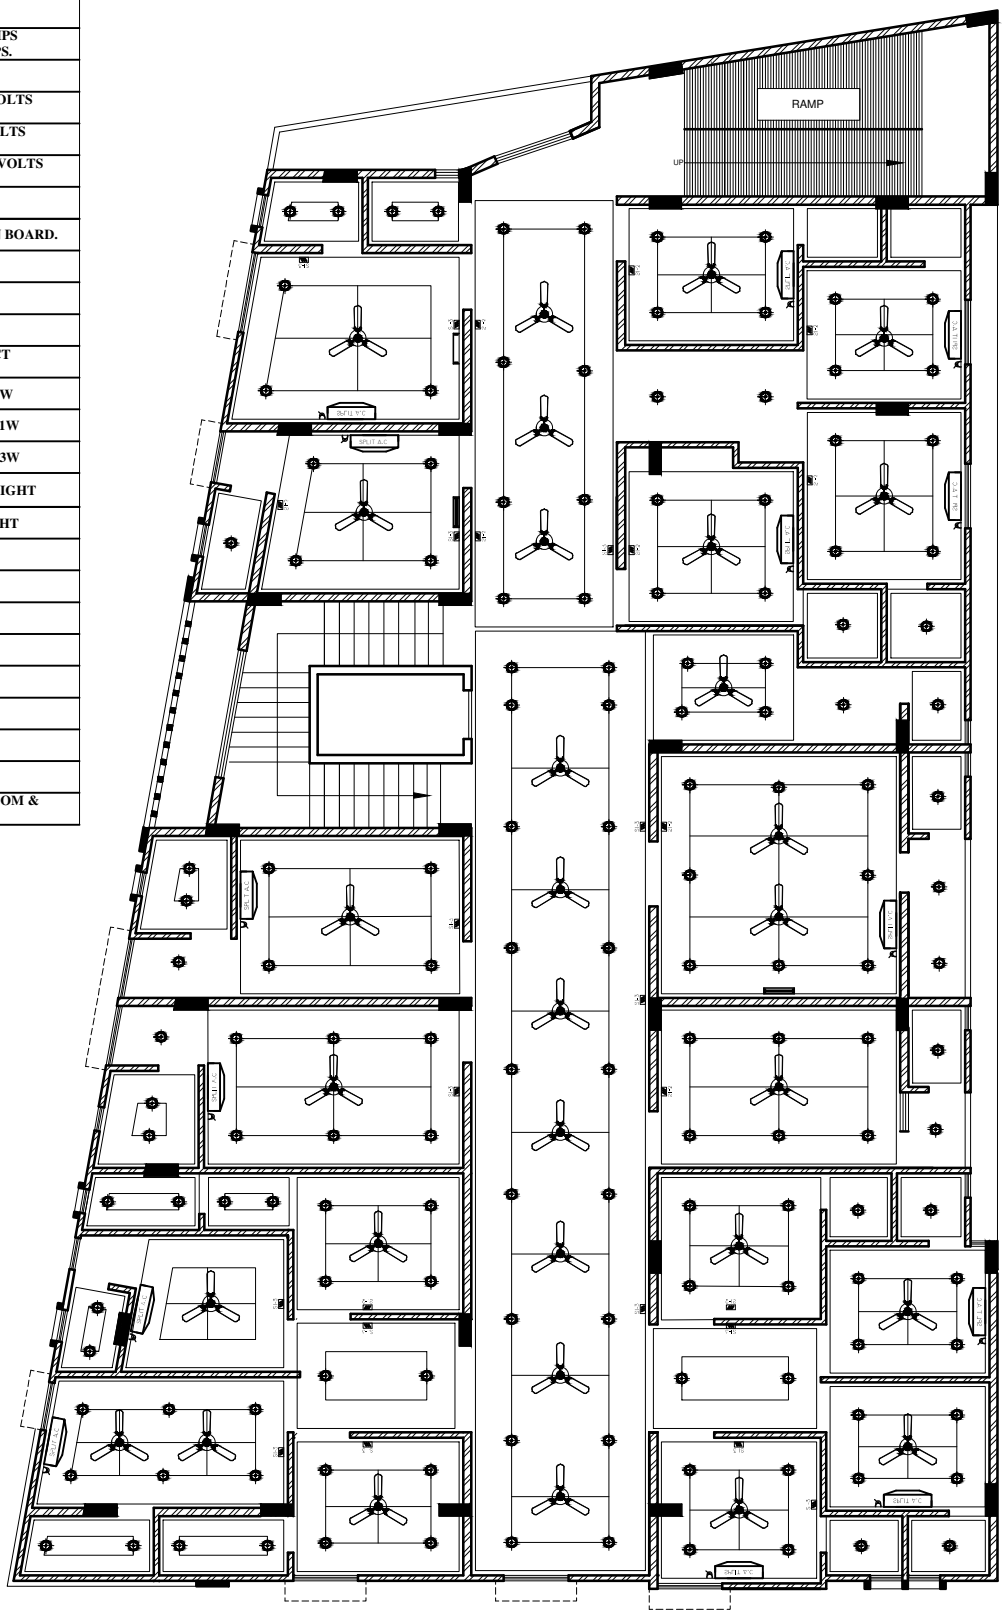

SECOND FLOOR ELECTRICAL PLAN

PROJECT:-	PROPOSED DRAWING FOR HOSPITAL
TITLE:-	**SECOND FLOOR ELECTRICAL PLAN**
ADDRESS:-	PLOT NO. _____WEST CITY HOSPITAL, MOMINABAD, ORANGI TOWN, K A R A C H I.
CLIENT:-	DR.IMRAN


DATE:-	09 - 05 - 2025
SCALE:-	1/8" = 1'-0"
CHECKED BY:-	AGAH
CAD BY:-	SUFYAN
PRINT DATE:-	09 - 05 - 2025
DRG NO. :-	A - 2025/01-01-02

THE CAD DESIGNER

ARCHITECT, ENGINEERS, PLANNERS
GULSHAN-E-HADEED, PHASE I & II EXT. BIN QASIM, KARACHI
CELL:0306-2776176

LEGEND


S.No.	SYMBOLS	DESCRIPTION
01		FLUORESCENT LAMP PHILIPS GCD-240 WITH 2X40 WATT LAMPS.
02		FAN
03		INCANDESCENT LAMP PHILIPS NCD-533 WITH 2X100W LAMPS.
04		EXHAUST FAN 12"SWEEP.
05		POWER PLUG 15 AMPS,220 VOLTS GRADE.
06		LIGHT PLUG 10 AMPS,220 VOLTS GRADE(UNIVERSAL TYPE)
07		PIANO SWITCH 10 AMPS,220 VOLTS GRADE.
08		TELEPHONE ROSSET.
09		ELECTRICAL DISTRIBUTION BOARD.
10		ONE WAY 10A SWITCH
11		DIMMER
12		SURFACE DOWN LIGHT 17W
13		CEILING MOUNTED COMPACT POWER LIGHT 23W
14		LED CEILING DOWN LIGHT 7W
15		LED CEILING DOWN LIGHT 11W
16		LED CEILING DOWN LIGHT 23W
17		WEATHER PROOF CEILING LIGHT
18		WEATHER PROOF WALL LIGHT
19		WALL LIGHT 14W
20		MIRROR LIGHT
21		LED FLOOD LIGHT
22		LED STRIP LIGHT
23		CHANDELIER
24		UNDER GROUND LIGHT 15W
25		EXHAUST FAN
26		GATE LIGHT
27		BELL PUSH BUTTON, INTERCOM & CAMERA

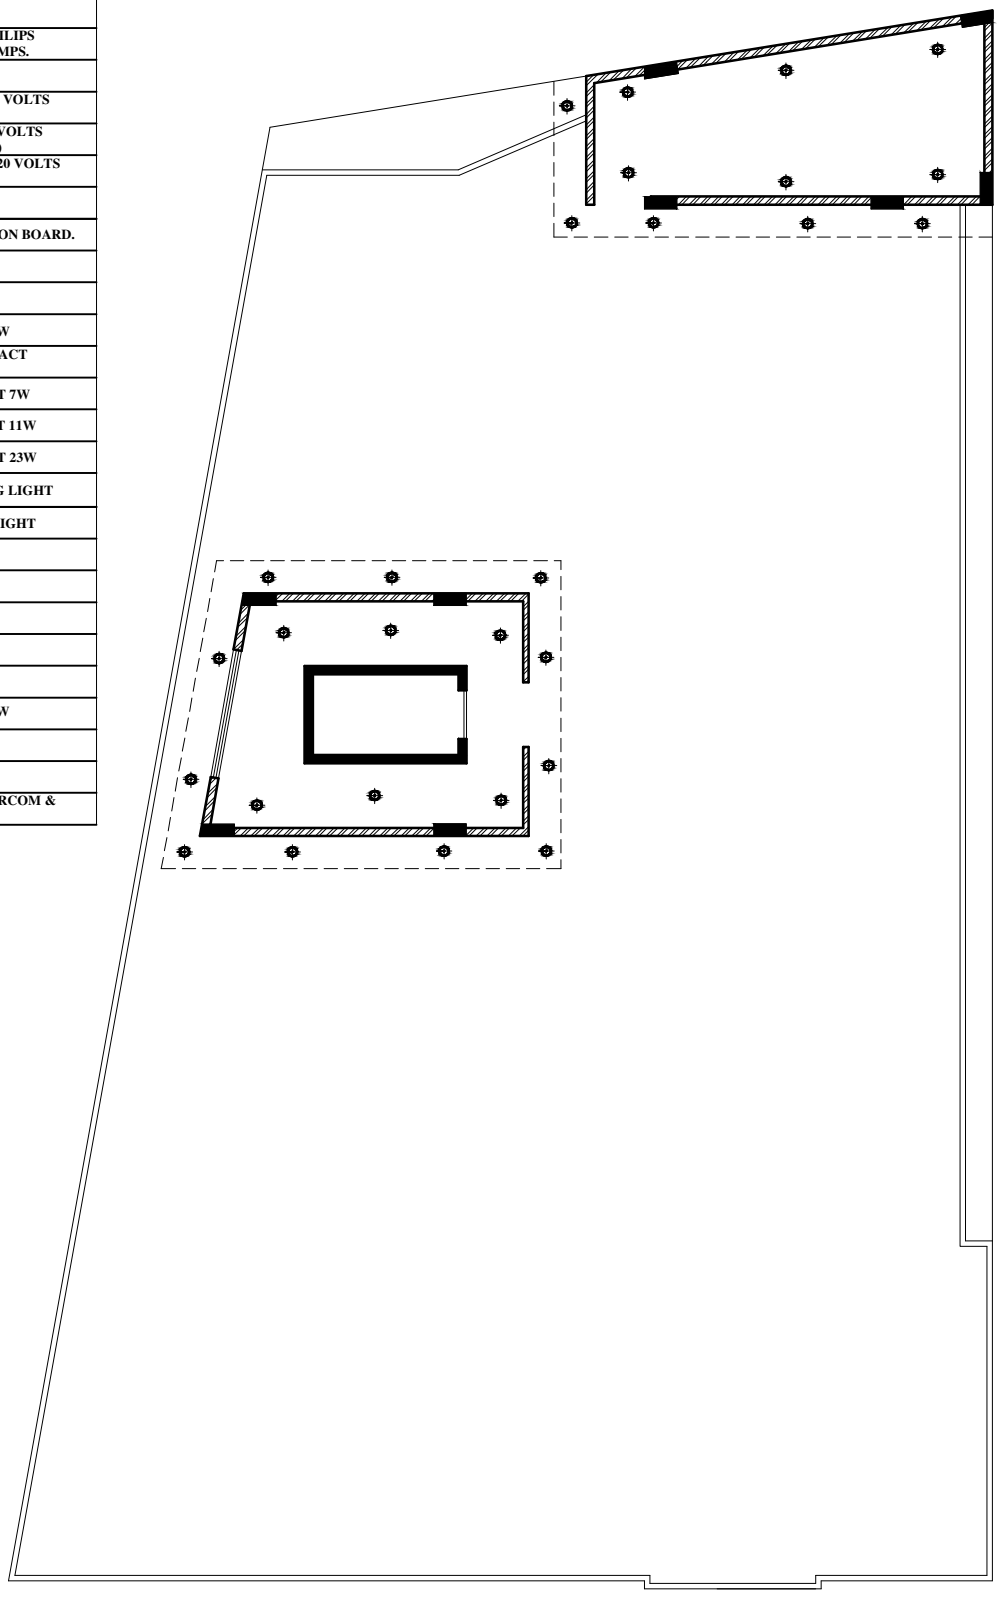


TOP FLOOR ELECTRICAL PLAN

PROJECT:-	PROPOSED DRAWING FOR HOSPITAL	DATE:-	09 - 05 - 2025
TITLE:-	**TOP FLOOR ELECTRICAL PLAN**	SCALE:-	1/8" = 1'-0"
ADDRESS:-	PLOT NO. _____WEST CITY HOSPITAL, MOMINABAD, ORANGI TOWN, K A R A C H I.	CHECKED BY:-	AGAH
		CAD BY:-	SUFYAN
		PRINT DATE:-	09 - 05 - 2025
CLIENT:-	DR.IMRAN	DRG NO. :-	A - 2025/01-01-02

THE CAD DESIGNER
ARCHITECT, ENGINEERS, PLANNERS
GULSHAN-E-HADEED, PHASE I & II EXT. BIN QASIM, KARACHI
CELL:0306-2776176

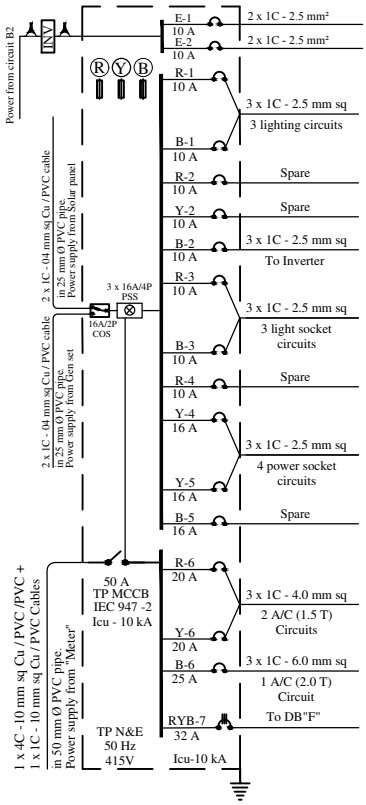


DISTRIBUTION BOARD "G"

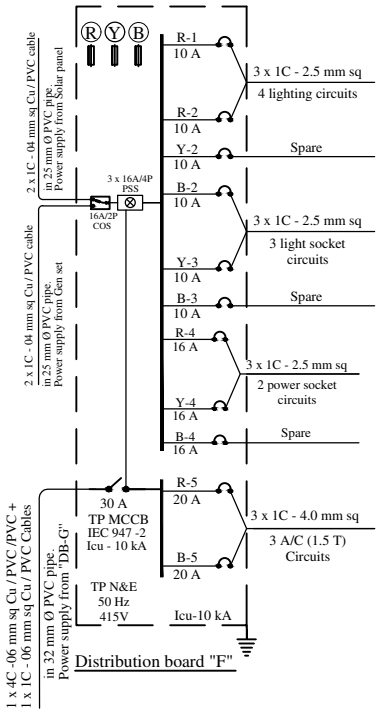


Distribution board "F"

S.#	Schedule of Panel board	
01	Protection class	1P-40
02	Manufacturing standard	IEC-439-1
03	Type of enclosure	Flush / surface / floor (as per site requirement)
04	Color	Epoxy powder coated RAL-7032 / 120 microns
05	Wiring	Pre-wired, 1/3 phase, 2/4 wires
06	Voltage	400 / 240 V ± 10 %
07	Frequency	50 HZ ± 2 %
08	Enclosure (DB's)	1.5 mm MS sheet steel
09	Name plate	10 mm riveted at top of door
10	Grounding	All metallic parts
11	Safety cover	Hinged door
12	Drawing pocket	Sheet steel (inside door)
13	Panel lock	Key operated
14	Bus bars / wires	99.9 % pure annealed copper
15	Cable entry	Top & bottom
16	Space	25 % for future expansion
17	Danger sign	On safety cover
18	Testing	The testing to be done at manufacturer's workshop for insulation and functional operation of all components and devices.
19	MS sheet work	Clean down to bare shine by de-rusting, de-greasing & base coat of phosphate
20	Space	Sufficient space to be provided on neutral and earth bars for pre-drilled holes for cable connections.
21	Operating Doors of Panel	The doors shall be front operated, however, it should be possible to remove/re-fix the back plates.
22	Barrier	Each MCCB shall have inter-polar insulation barrier both on incoming and outgoing side.
23	Protected cover	All terminals, bus-bars and other live parts shall be fully protected under a cover sheet.
24	Dimensions & Mounting	dimensions/mounting arrangements shown in the drawings may be tailored according to physical constraints at site


Note: Shop drawing (Two sets of Hard copies) shall be submitted for approval before fabrication.

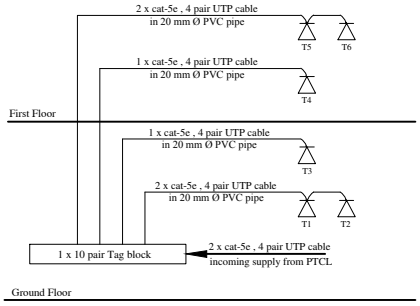


VOICE SYSTEM SCHEMATIC DIAGRAM

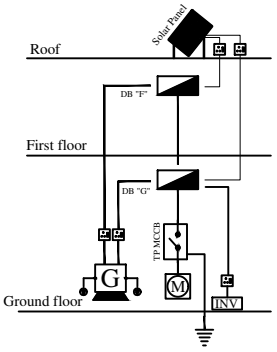

ELECTRICAL DISTRIBUTION SCHEMATIC DIAGRAM

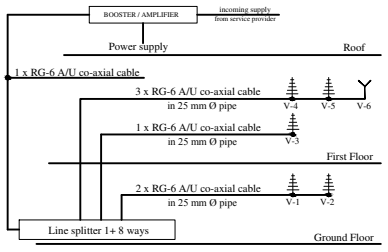

CATV SYSTEM SCHEMATIC DIAGRAM

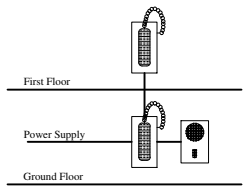


DOOR INTERCOM SCHEMATIC DIAGRAM


DETAIL-1

PROJECT:-	PROPOSED DRAWING FOR HOSPITAL	DATE:-	09 - 05 - 2025
TITLE:-	**DETAIL-1**	SCALE:-	1/8" = 1'-0"
ADDRESS:-	PLOT NO. _____WEST CITY HOSPITAL, MOMINABAD, ORANGI TOWN, K A R A C H I.	CHECKED BY:-	AGAH
		CAD BY:-	SUFYAN
		PRINT DATE:-	09 - 05 - 2025
CLIENT:-	DR.IMRAN	DRG NO. :-	A - 2025/01-01-02


THE CAD DESIGNER
ARCHITECT, ENGINEERS, PLANNERS
GULSHAN-E-HADEED, PHASE I & II EXT. BIN QASIM, KARACHI
CELL:0306-2776176

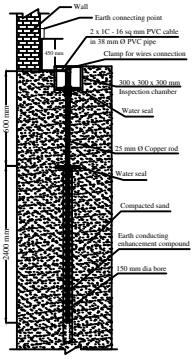


DETAIL OF ENVIRONMENTAL FREE EARTHLING

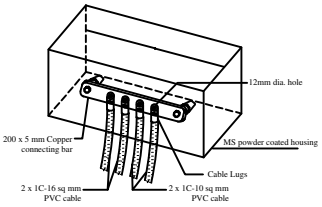


EARTH TEST POINT

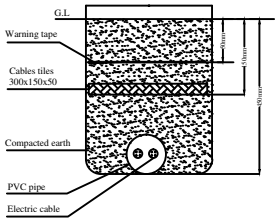


DETAIL OF UNDER GROUND CABLE INSTALLATION

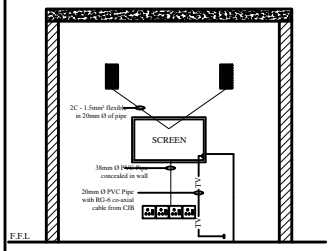


DETAIL OF SOCKETS INSTALLATION FOR TV

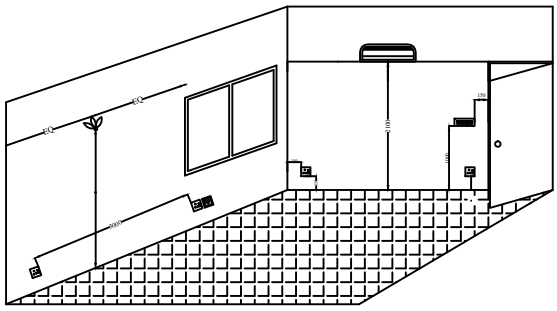


DETAIL OF FIXTURES AND FITTING

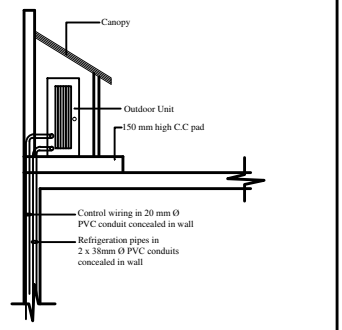

Condensing unit detail

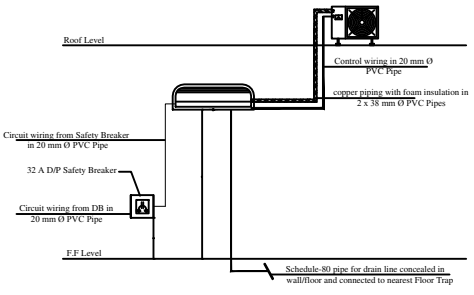

Split A/C Installation detail

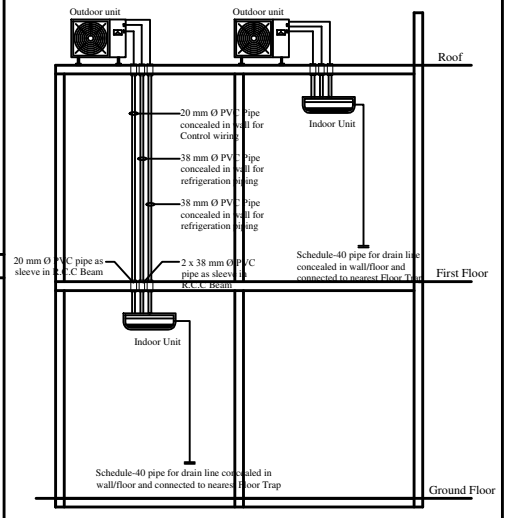

Split unit typical riser installation detail

DETAIL-2


PROJECT:-	PROPOSED DRAWING FOR HOSPITAL	DATE:-	09 - 05 - 2025
TITLE:-	**DETAIL-2**	SCALE:-	1/8" = 1'-0"
ADDRESS:-	PLOT NO. _____WEST CITY HOSPITAL, MOMINABAD, ORANGI TOWN, K A R A C H I.	CHECKED BY:-	AGAH
		CAD BY:-	SUFYAN
		PRINT DATE:-	09 - 05 - 2025
CLIENT:-	DR.IMRAN	DRG NO. :-	A - 2025/01-01-02


THE CAD DESIGNER
ARCHITECT, ENGINEERS, PLANNERS
GULSHAN-E-HADEED, PHASE I & II EXT. BIN QASIM, KARACHI
CELL:0306-2776176

PLUMBING DRAWINGS

THE CAD DESIGNER
ARCHITECT, ENGINEERS, PLANNERS
GULSHAN-E-HADEED, PHASE I & II EXT. BIN
QASIM, KARACHI
CELL :0323-2446599
0306-2776176

LEGEND

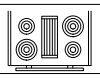S.No.	SYMBOLS	DESCRIPTION
01	■	FLOW TRAP
02		VANITY
03		SHOWER
04		W.C.INDIAN
05		SINK
06		HOB
07	MH	MANHOLE WITH COVER
08		PUMP AND MOTOR
09		DOUBLE BIB COCK
10		T-STOP COCK

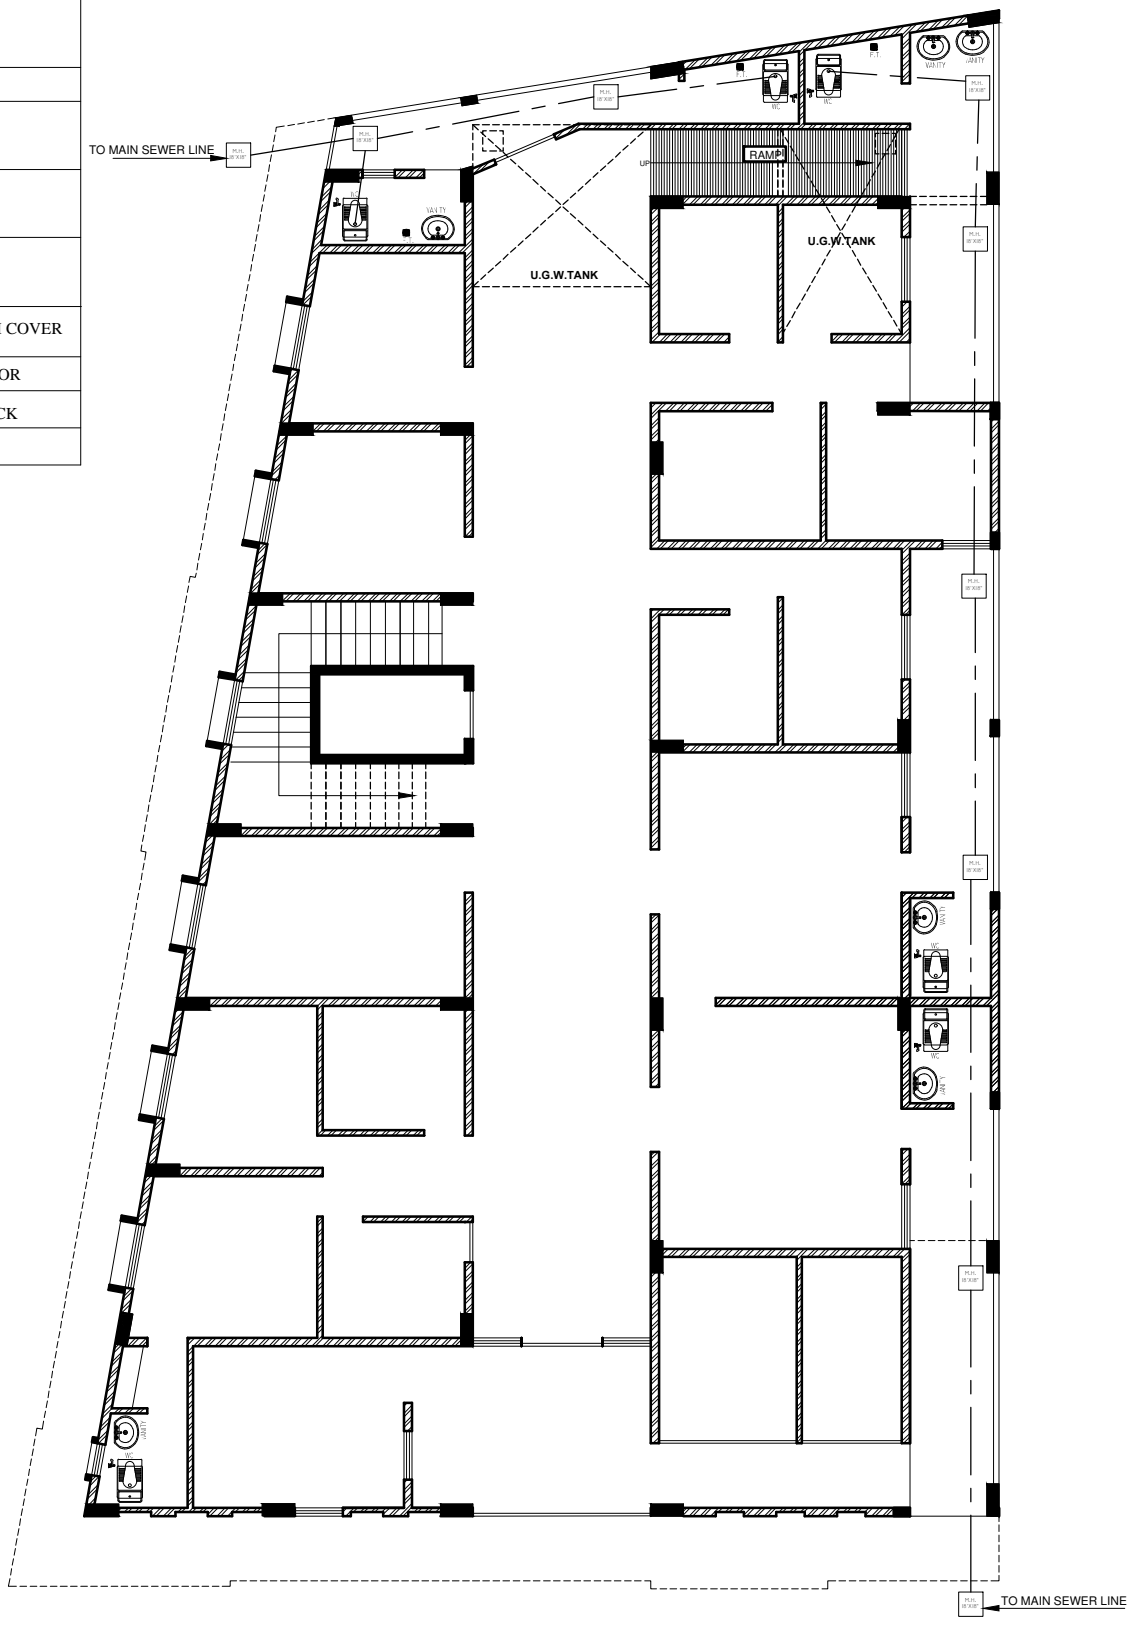


GROUND FLOOR PLUMBING PLAN

PROJECT:-	PROPOSED DRAWING FOR HOSPITAL	DATE:-	09 - 05 - 2025
TITLE:-	**GROUND FLOOR PLUMBING PLAN**	SCALE:-	1/8" = 1'-0"
ADDRESS:-	PLOT NO. _____WEST CITY HOSPITAL, MOMINABAD, ORANGI TOWN, K A R A C H I.	CHECKED BY:-	AGAH
		CAD BY:-	SUFYAN
		PRINT DATE:-	09 - 05 - 2025
CLIENT:-	DR.IMRAN	DRG NO. :-	A - 2025/01-01-02

THE CAD DESIGNER
ARCHITECT, ENGINEERS, PLANNERS
GULSHAN-E-HADEED, PHASE I & II EXT. BIN QASIM, KARACHI
CELL:0306-2776176

LEGEND

S.No.	SYMBOLS	DESCRIPTION
01		FLOW TRAP
02		VANITY
03		SHOWER
04		W.C.INDIAN
05		SINK
06		HOB
07	MH	MANHOLE WITH COVER
08		PUMP AND MOTOR
09		DOUBLE BIB COCK
10		T-STOP COCK

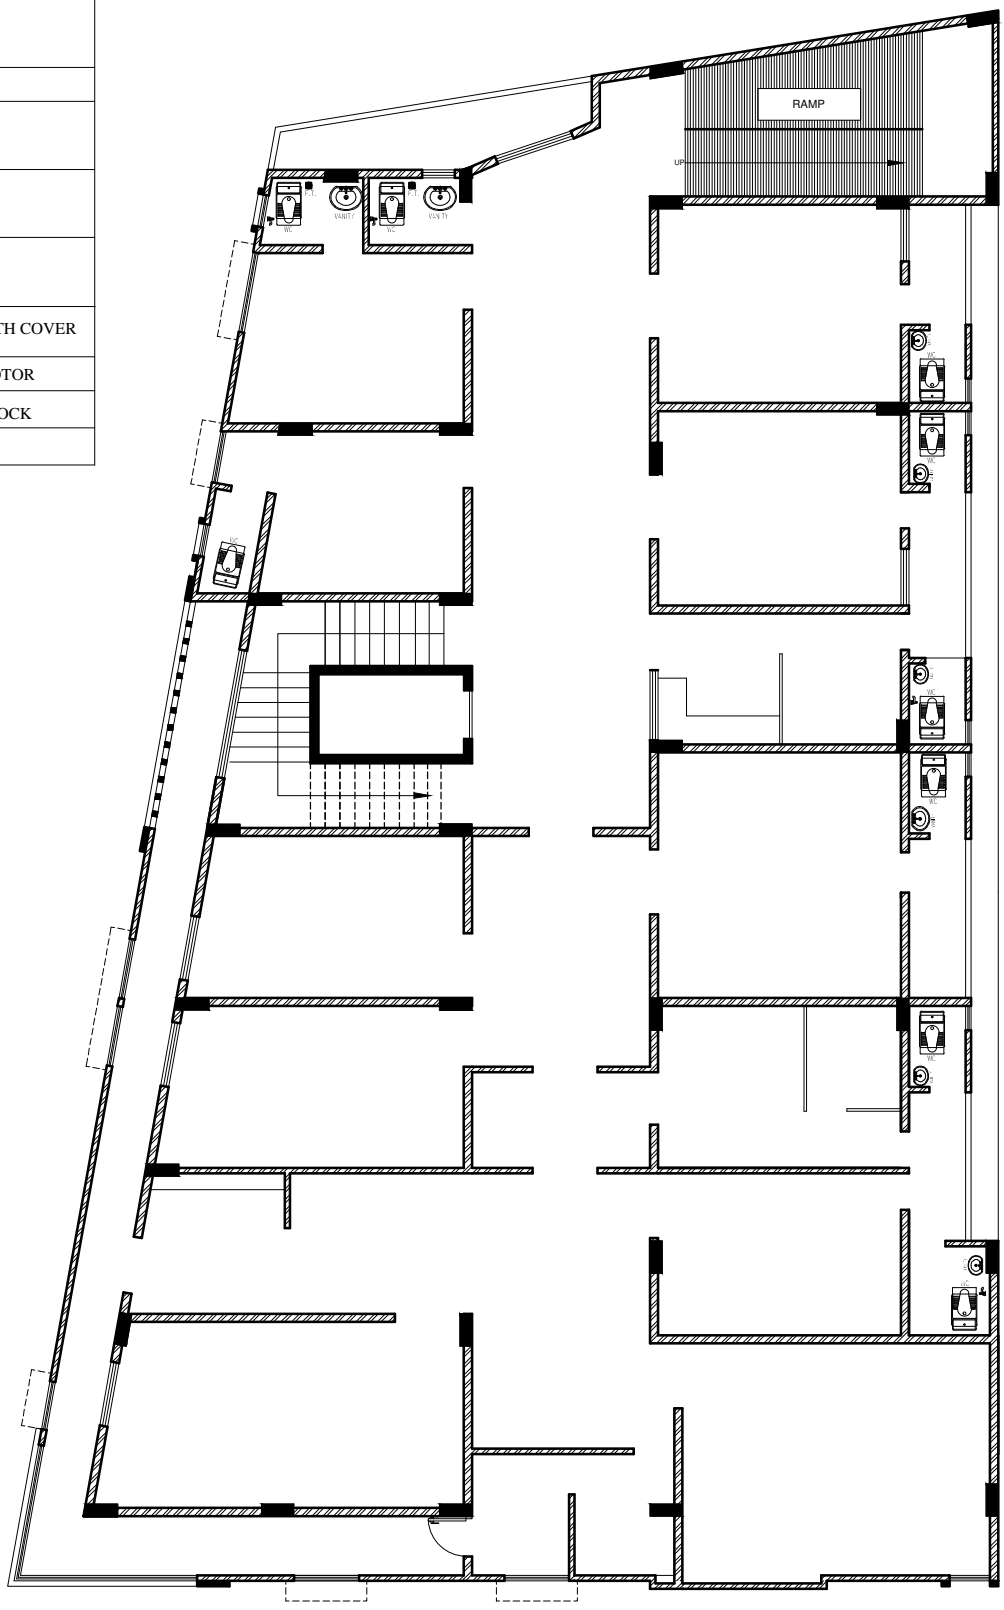


FIRST FLOOR PLUMBING PLAN

PROJECT:-	PROPOSED DRAWING FOR HOSPITAL	DATE:-	09 - 05 - 2025
TITLE:-	**FIRST FLOOR PLUMBING PLAN**	SCALE:-	1/8" = 1'-0"
ADDRESS:-	PLOT NO. _____WEST CITY HOSPITAL, MOMINABAD, ORANGI TOWN, K A R A C H I.	CHECKED BY:-	AGAH
		CAD BY:-	SUFYAN
		PRINT DATE:-	09 - 05 - 2025
CLIENT:-	DR.IMRAN	DRG NO. :-	A - 2025/01-01-02

THE CAD DESIGNER
ARCHITECT, ENGINEERS, PLANNERS
GULSHAN-E-HADEED, PHASE I & II EXT. BIN QASIM, KARACHI
CELL:0306-2776176

LEGEND

S.No.	SYMBOLS	DESCRIPTION
01	■	FLOW TRAP
02		VANITY
03		SHOWER
04		W.C.INDIAN
05		SINK
06		HOB
07	MH	MANHOLE WITH COVER
08		PUMP AND MOTOR
09		DOUBLE BIB COCK
10		T-STOP COCK

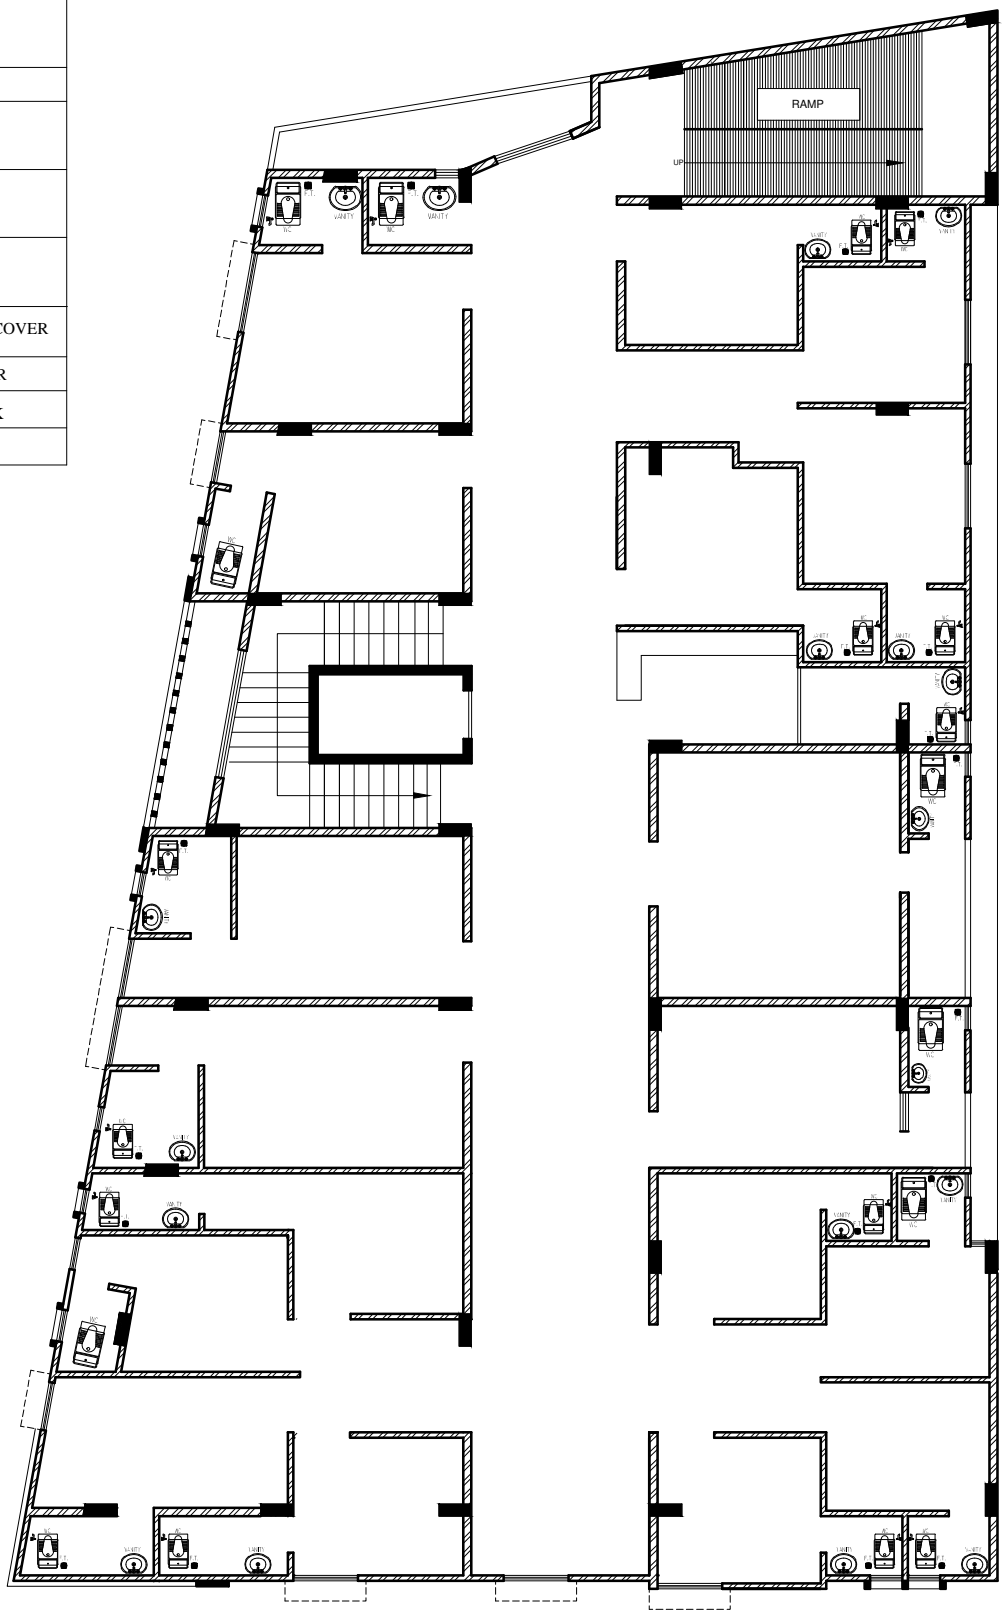

SECOND FLOOR PLUMBING PLAN


PROJECT:-	PROPOSED DRAWING FOR HOSPITAL
TITLE:-	**SECOND FLOOR PLUMBING PLAN**
ADDRESS:-	PLOT NO. _____WEST CITY HOSPITAL, MOMINABAD, ORANGI TOWN, K A R A C H I.
CLIENT:-	DR.IMRAN

DATE:-	09 - 05 - 2025
SCALE:-	1/8" = 1'-0"
CHECKED BY:-	AGAH
CAD BY:-	SUFYAN
PRINT DATE:-	09 - 05 - 2025
DRG NO. :-	A - 2025/01-01-02

THE CAD DESIGNER
ARCHITECT, ENGINEERS, PLANNERS
GULSHAN-E-HADEED, PHASE I & II EXT. BIN QASIM, KARACHI
CELL:0306-2776176

LEGEND

S.No.	SYMBOLS	DESCRIPTION
01		FLOW TRAP
02		VANITY
03		SHOWER
04		W.C.INDIAN
05		SINK
06		HOB
07	MH	MANHOLE WITH COVER
08		PUMP AND MOTOR
09		DOUBLE BIB COCK
10		T-STOP COCK

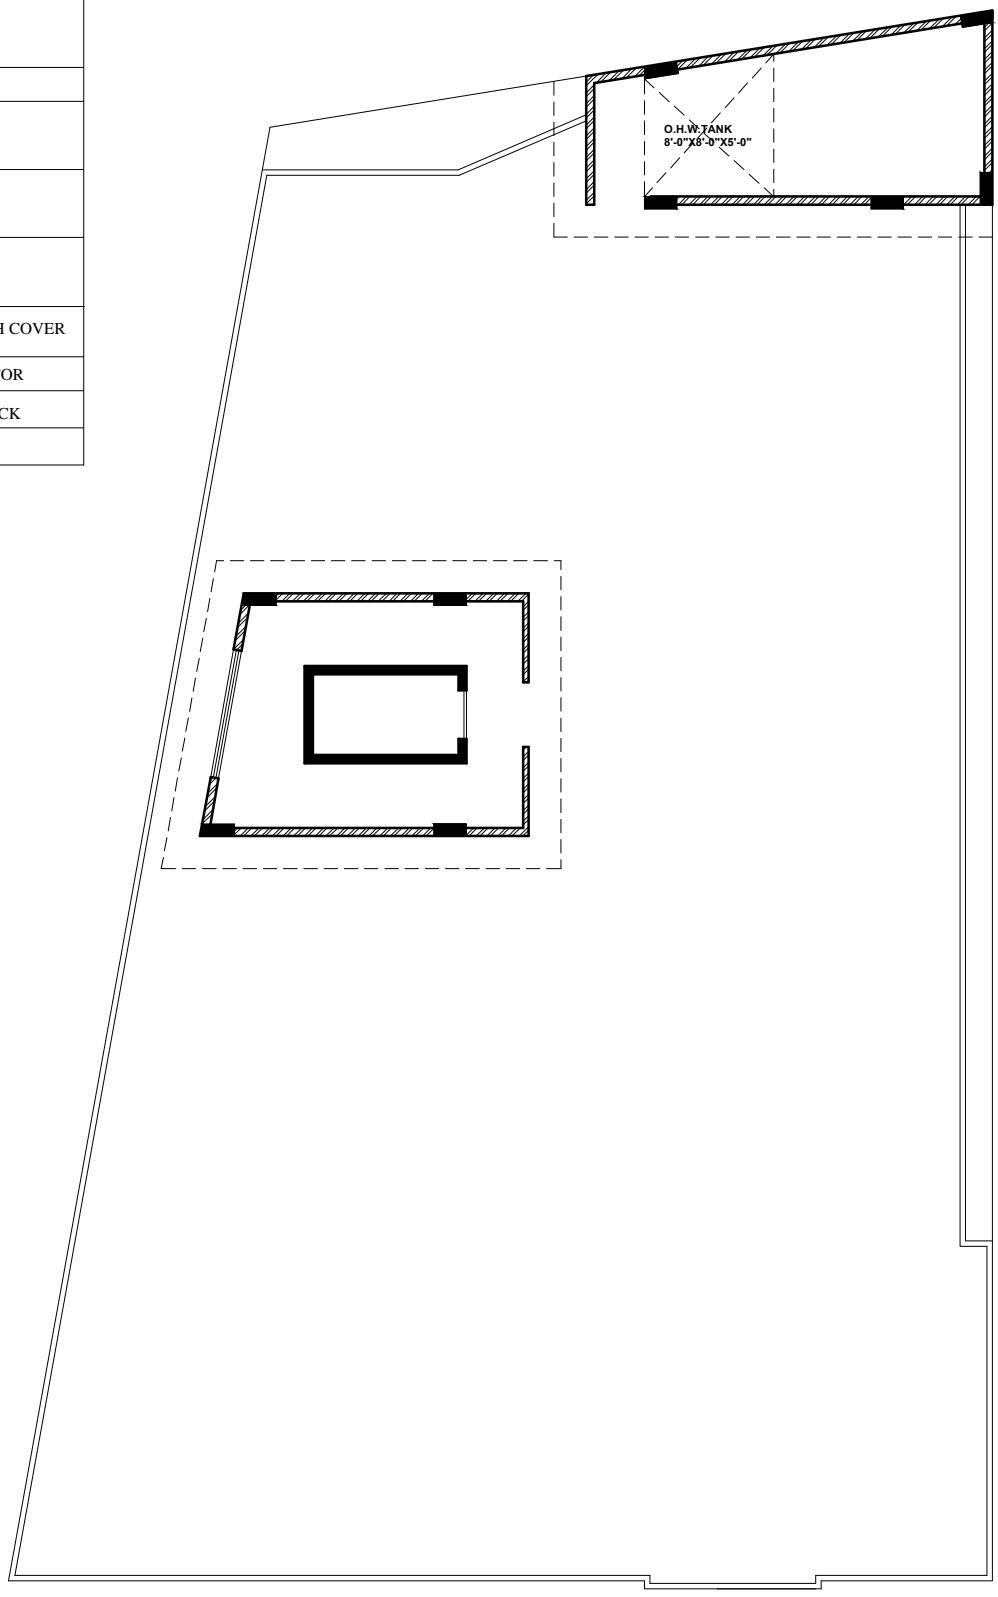


TOP FLOOR PLUMBING PLAN


PROJECT:-	PROPOSED DRAWING FOR HOSPITAL
TITLE:-	**TOP FLOOR PLUMBING PLAN**
ADDRESS:-	PLOT NO. _____WEST CITY HOSPITAL, MOMINABAD, ORANGI TOWN, K A R A C H I.
CLIENT:-	DR.IMRAN

DATE:-	09 - 05 - 2025
SCALE:-	1/8" = 1'-0"
CHECKED BY:-	AGAH
CAD BY:-	SUFYAN
PRINT DATE:-	09 - 05 - 2025
DRG NO. :-	A - 2025/01-01-02


THE CAD DESIGNER
ARCHITECT, ENGINEERS, PLANNERS
GULSHAN-E-HADEED, PHASE I & II EXT. BIN QASIM, KARACHI
CELL:0306-2776176

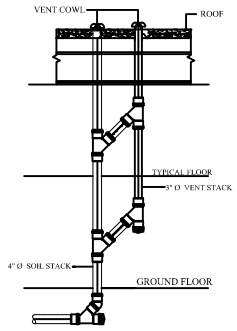


TYPICAL DETAIL OF VENT PIPE

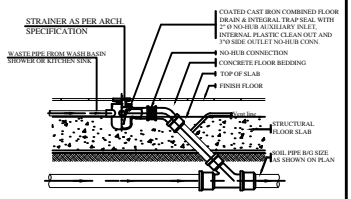


FLOOR GULLY CONNECTION TO MAIN PIPE

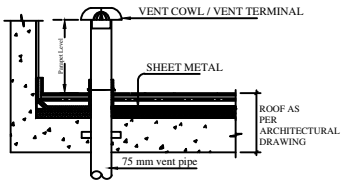


VENT THROUGH ROOF

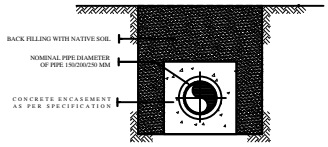

BURIED SEWER PIPE

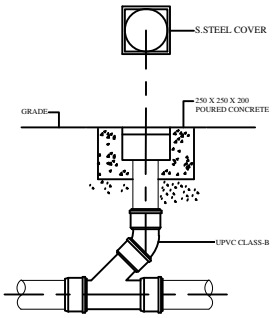

FLOOR CLEAN OUT INSTALLATION DETAIL

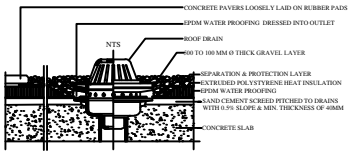


ROOF DRAIN


NOTES

1- SUCTION & DISCHARGE PIPING SHALL BE SUPPORTED INDEPENDENTLY OF PUMP TO PREVENT ANY STRESS ON PUMP SUCTION & DISCHARGE NOZZLES.


2- THE PUMP FOUNDATION INDICATED IS FOR A CONCRETE BASE TYPE , FOR FLOATING FOUNDATION BASE TYPE REFER TO EQUIPMENT ISOLATION BASE DETAIL.

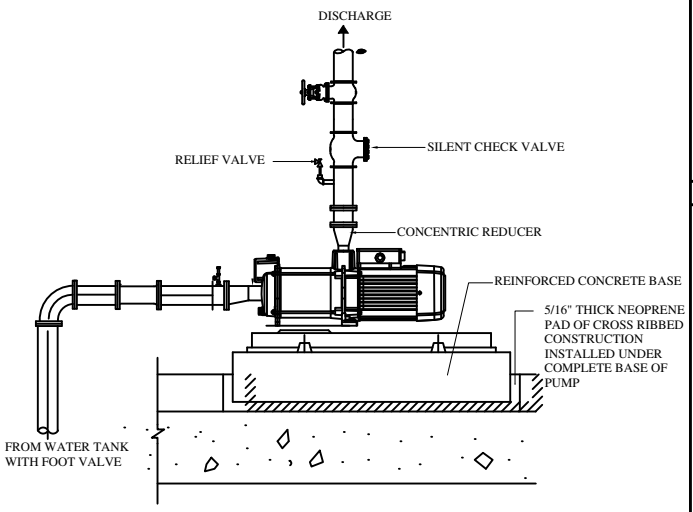

TRANSFER PUMP INSTALLATION SECTION

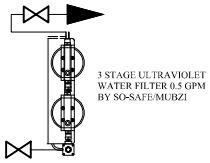

WATER FILTER DETAIL

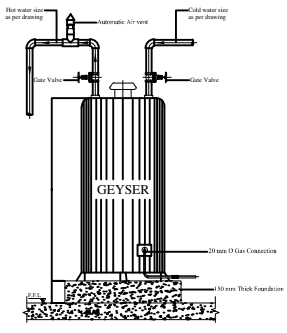


DETAIL OF GEYSER


PLUMBING DETAIL-1

PROJECT:-	PROPOSED DRAWING FOR HOSPITAL	DATE:-	09 - 05 - 2025
TITLE:-	**PLUMBING DETAIL-1**	SCALE:-	1/8" = 1'-0"
ADDRESS:-	PLOT NO. _____WEST CITY HOSPITAL, MOMINABAD, ORANGI TOWN, K A R A C H I.	CHECKED BY:-	AGAH
		CAD BY:-	SUFYAN
		PRINT DATE:-	09 - 05 - 2025
CLIENT:-	DR.IMRAN	DRG NO. :-	A - 2025/01-01-02

THE CAD DESIGNER
ARCHITECT, ENGINEERS, PLANNERS
GULSHAN-E-HADEED, PHASE I & II EXT. BIN QASIM, KARACHI
CELL:0306-2776176

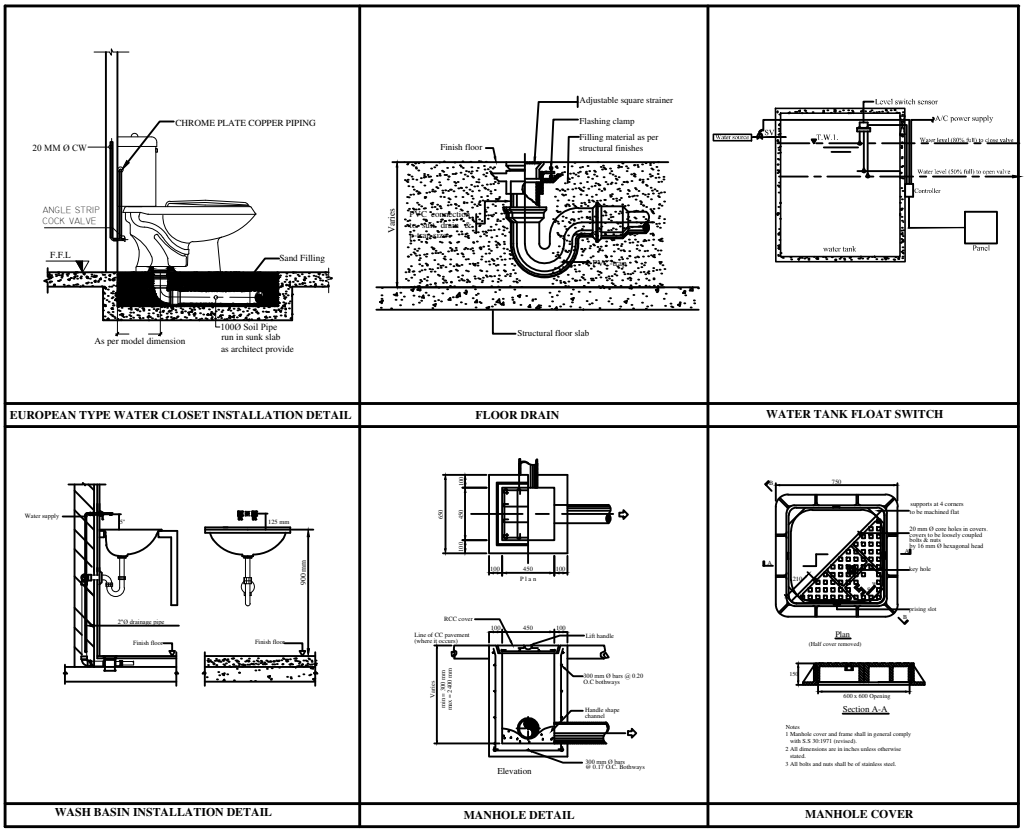

WATER TRANSFER PUMP									
Service	Location	Flow rate each		Head	Motor data				
		GPM	Liters/Sec	Ft	Hp	Kw	Hz	Volts	Phase
Water transfer pump	Ground floor	20	1.26	60	1.0	0.75	50	220	1

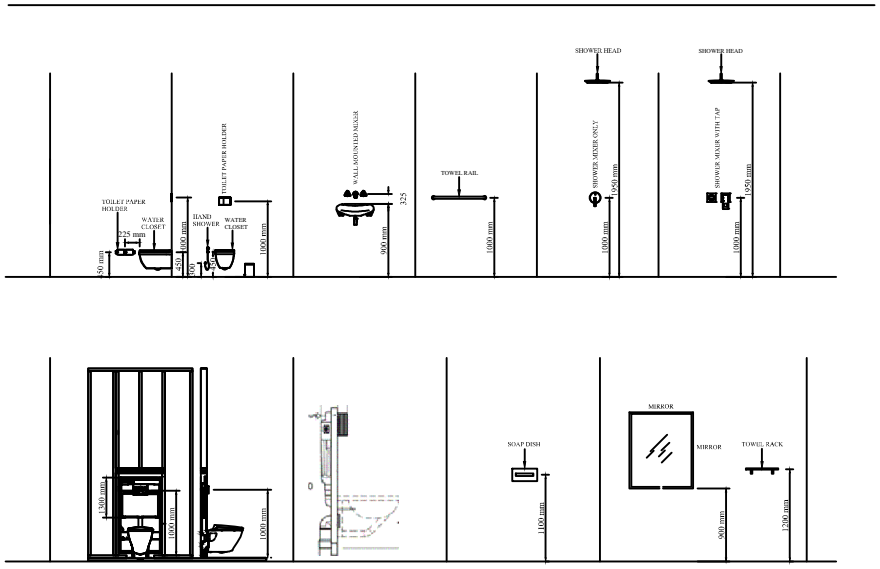

PLUMBING DETAIL-2

PROJECT:-	PROPOSED DRAWING FOR HOSPITAL	DATE:-	09 - 05 - 2025
TITLE:-	**PLUMBING DETAIL-2**	SCALE:-	1/8" = 1'-0"
ADDRESS:-	PLOT NO. _____WEST CITY HOSPITAL, MOMINABAD, ORANGI TOWN, K A R A C H I.	CHECKED BY:-	AGAH
		CAD BY:-	SUFYAN
		PRINT DATE:-	09 - 05 - 2025
CLIENT:-	DR.IMRAN	DRG NO. :-	A - 2025/01-01-02

THE CAD DESIGNER
ARCHITECT, ENGINEERS, PLANNERS
GULSHAN-E-HADEED, PHASE I & II EXT. BIN QASIM, KARACHI
CELL:0306-2776176