
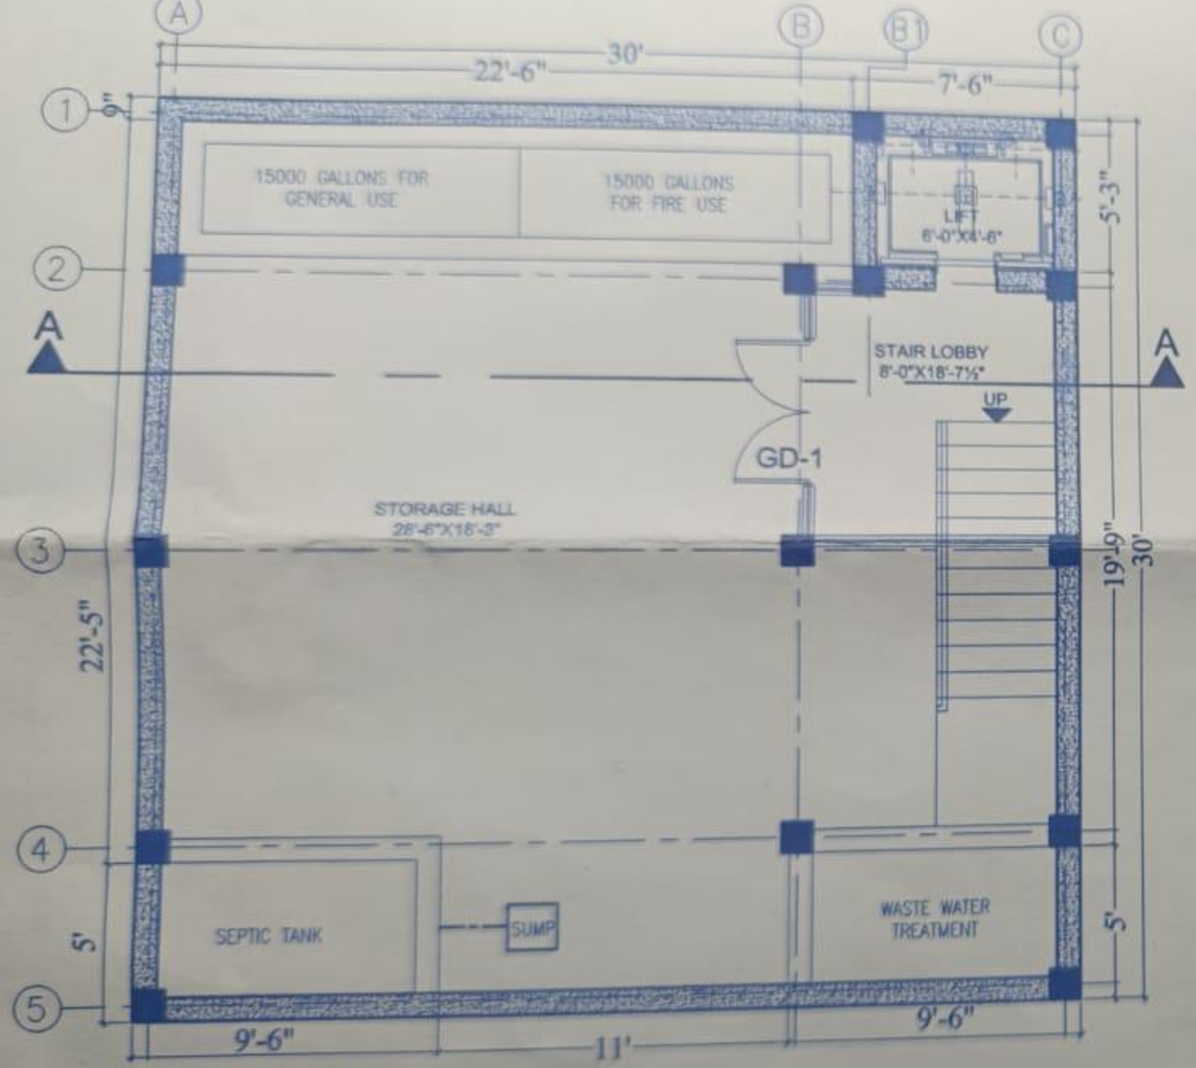


BASEMENT PLAN

SCALE 1"=8'-0"

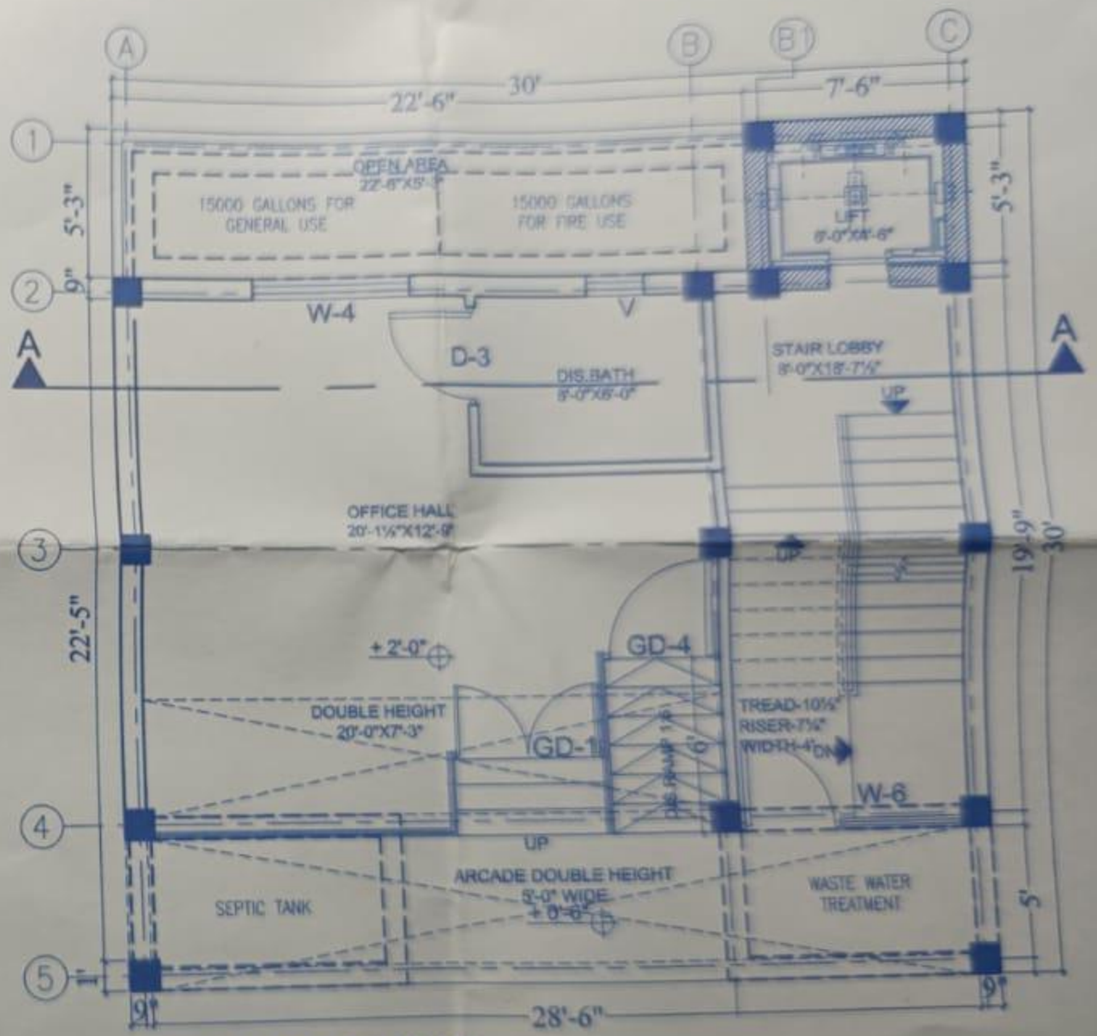


GROUND FLOOR PLAN

SCALE 1"=8'-0"




SE

SCAL

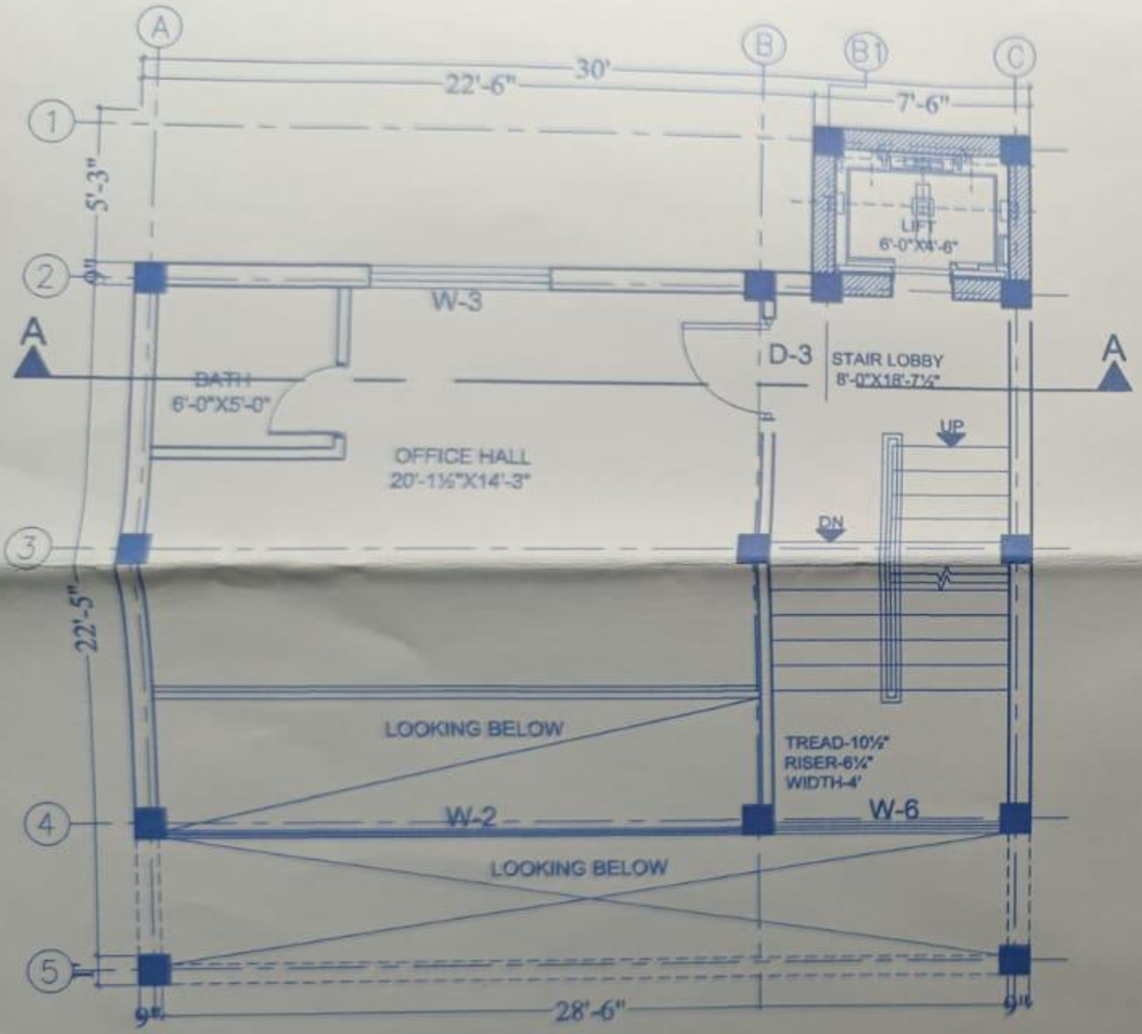

FIRST FLOOR PLAN
SCALE 1"=8'-0"

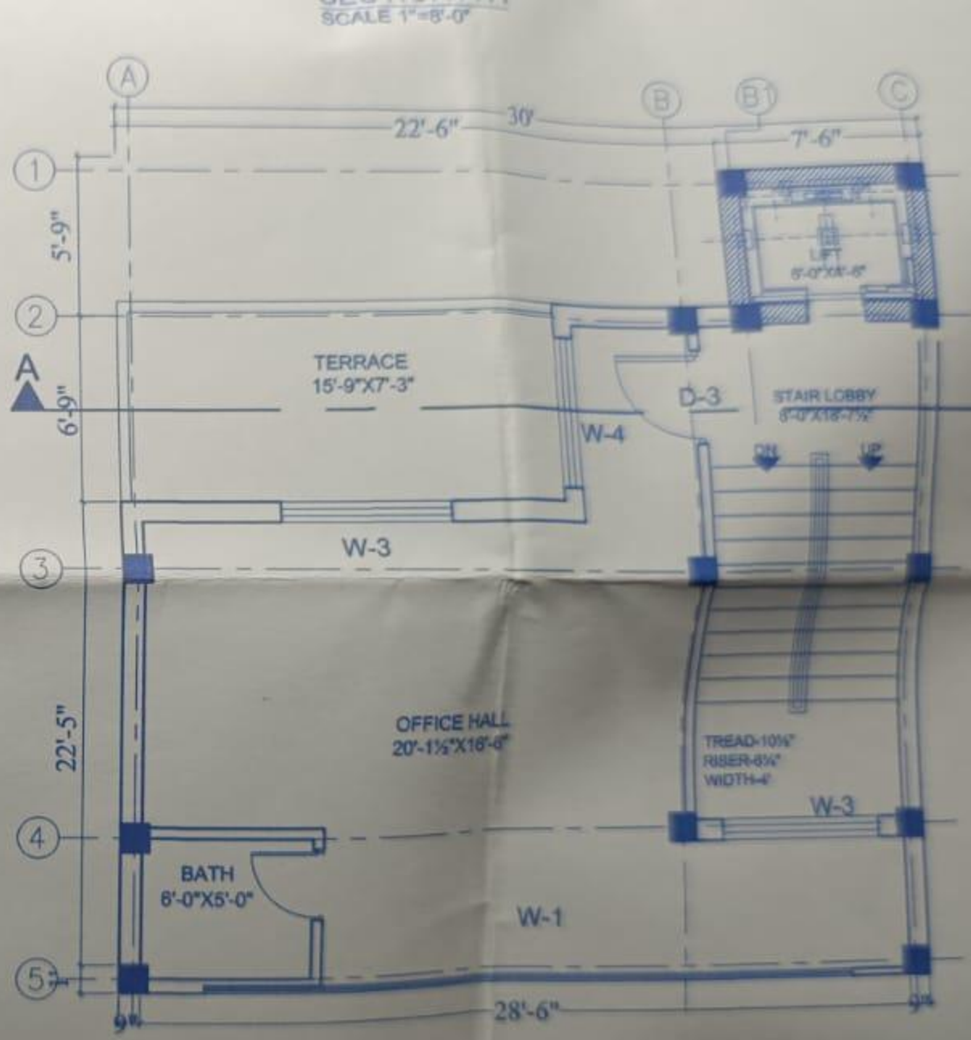


2ND TO 5th FLOOR PLAN
SCALE 1"=8'-0"




TOP FLOOR PL
SCALE 1"=8'-0"

SLAB OVER BASEMENT

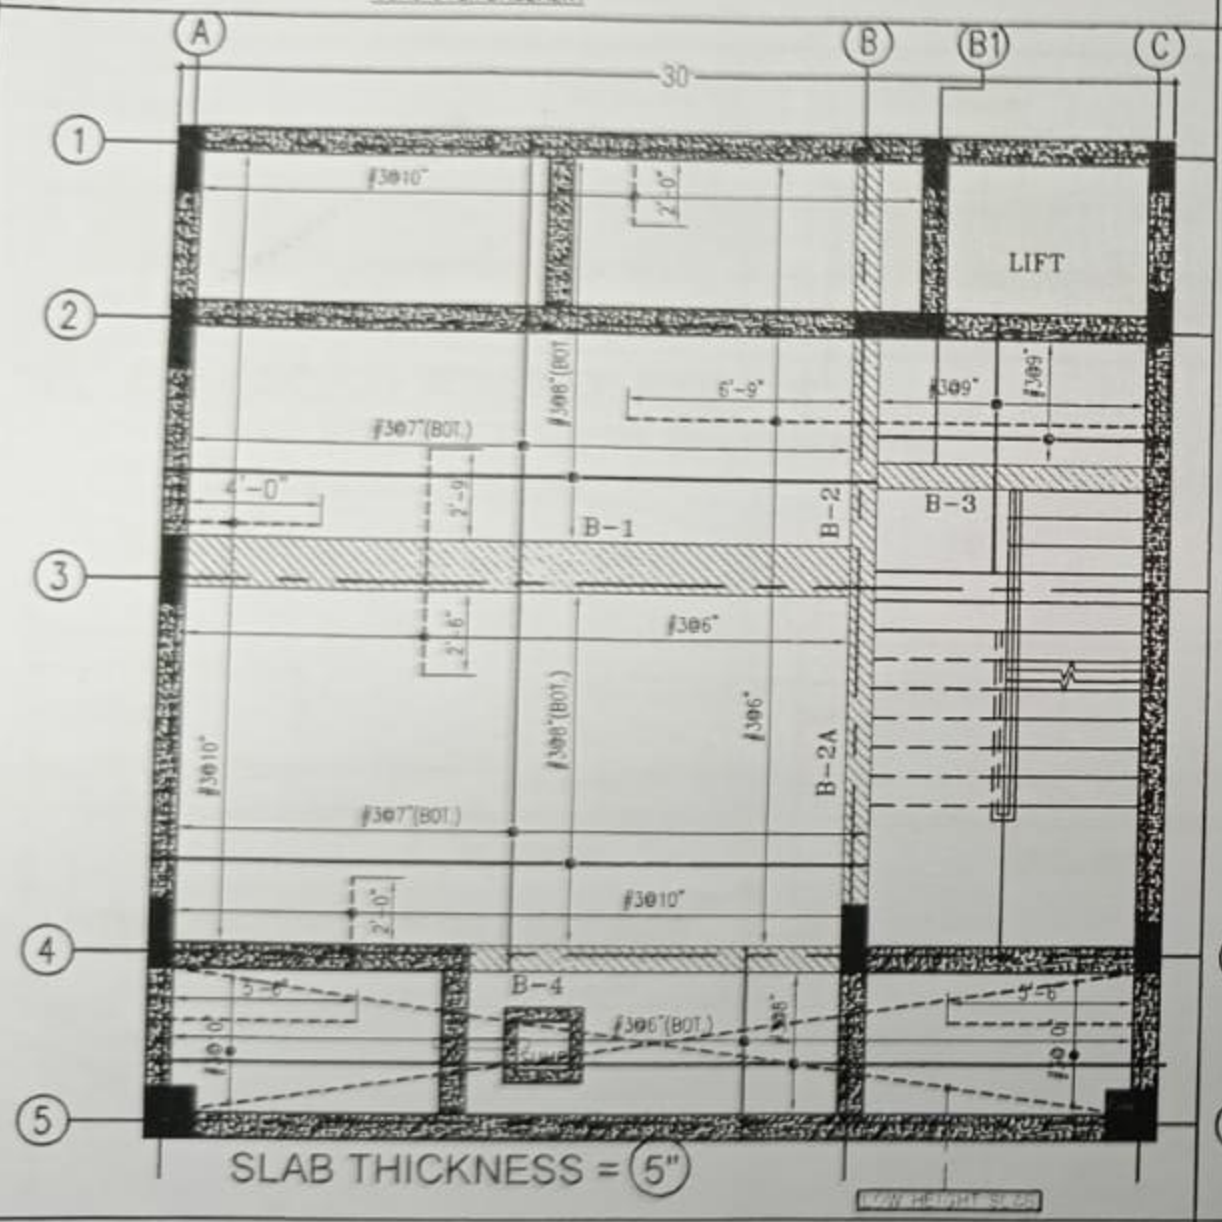


SLAB THICKNESS = (5")

SLAB OVER GROUND FLOOR

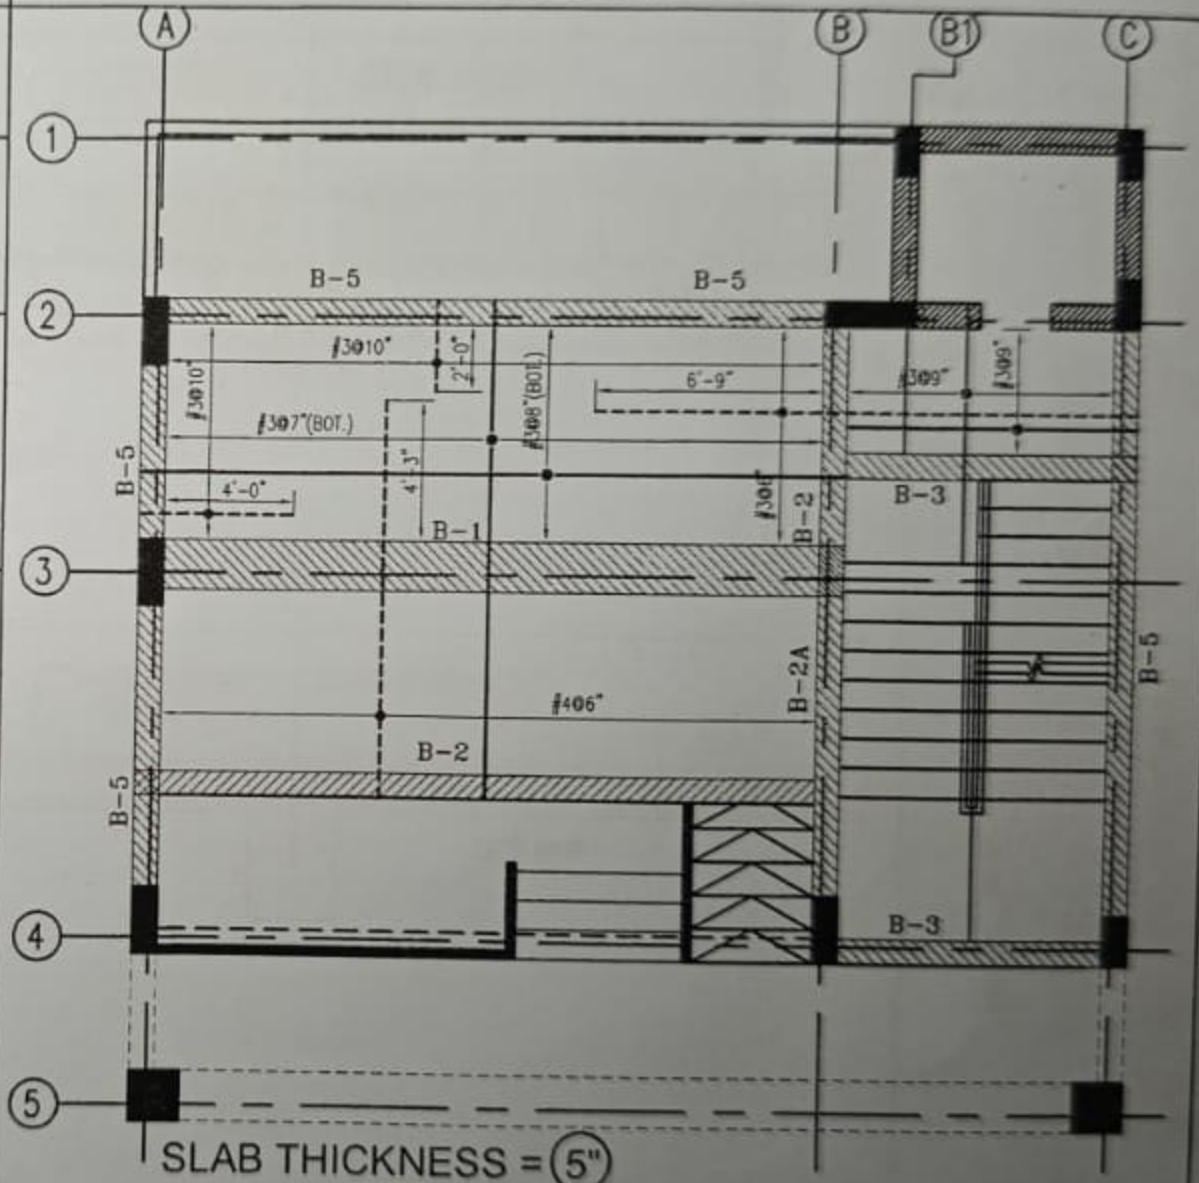

SLAB THICKNESS = (5")

SLAB OVER FIRST FLOOR

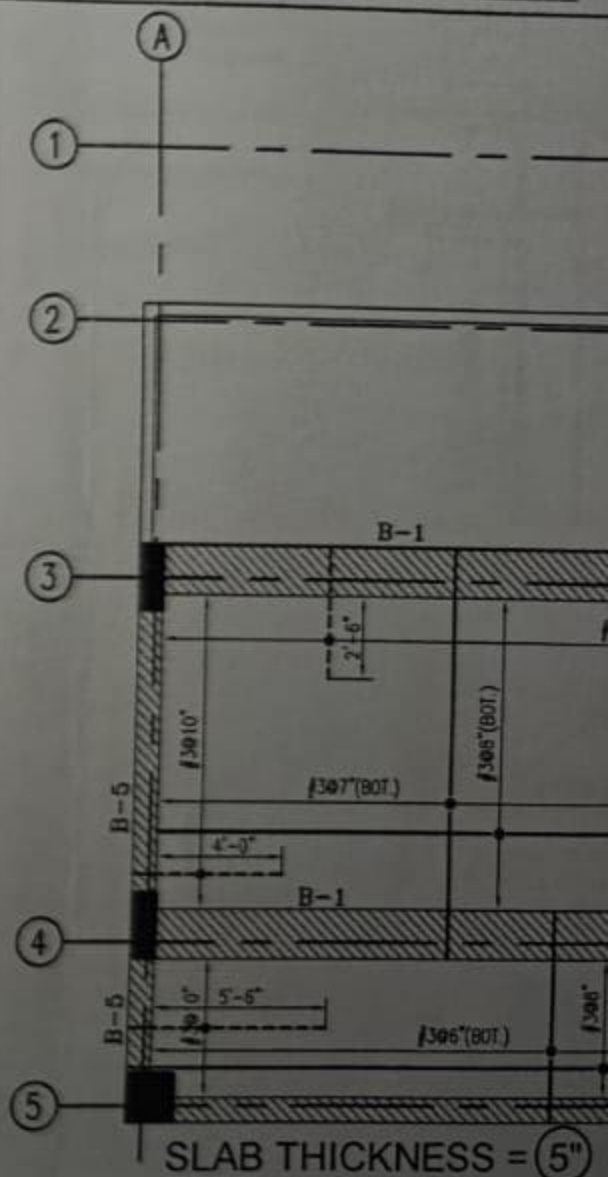

SLAB THICKNESS = (5")

SLAB OVER 3RD FLOOR

SLAB OVER 4TH FLOOR


SLAB OVER 5th

SLAB THICKNESS = (5")


SLAB THICKNESS = (5")


SLAB THICKNESS = (5")


RAFT REINFORCEMENT PLAN

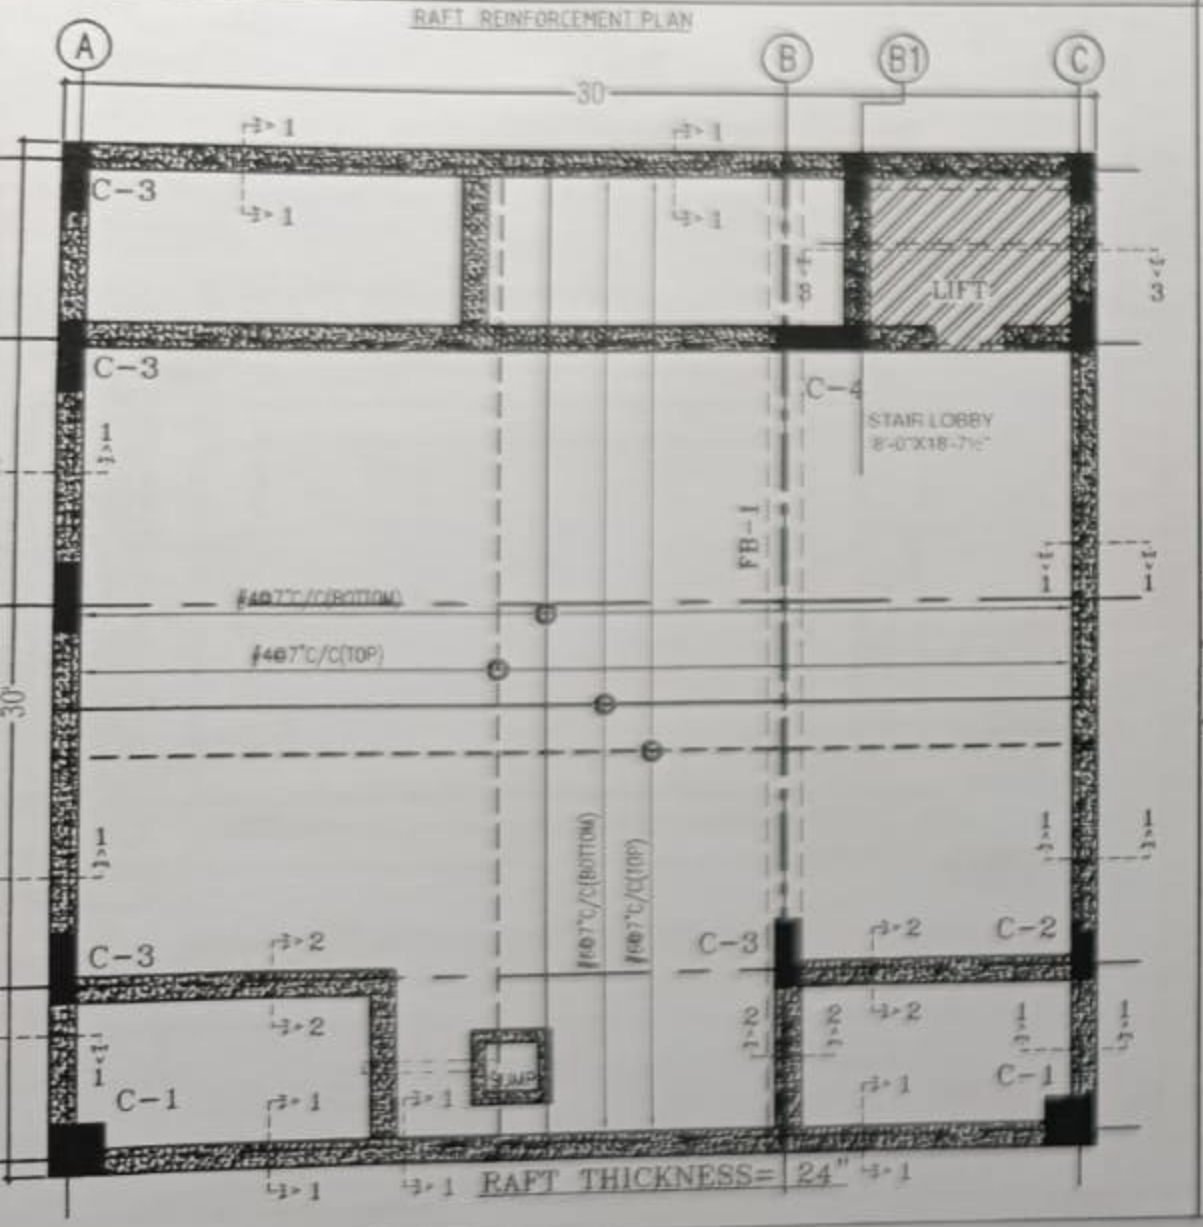



FOUNDATION SECTION DETAIL

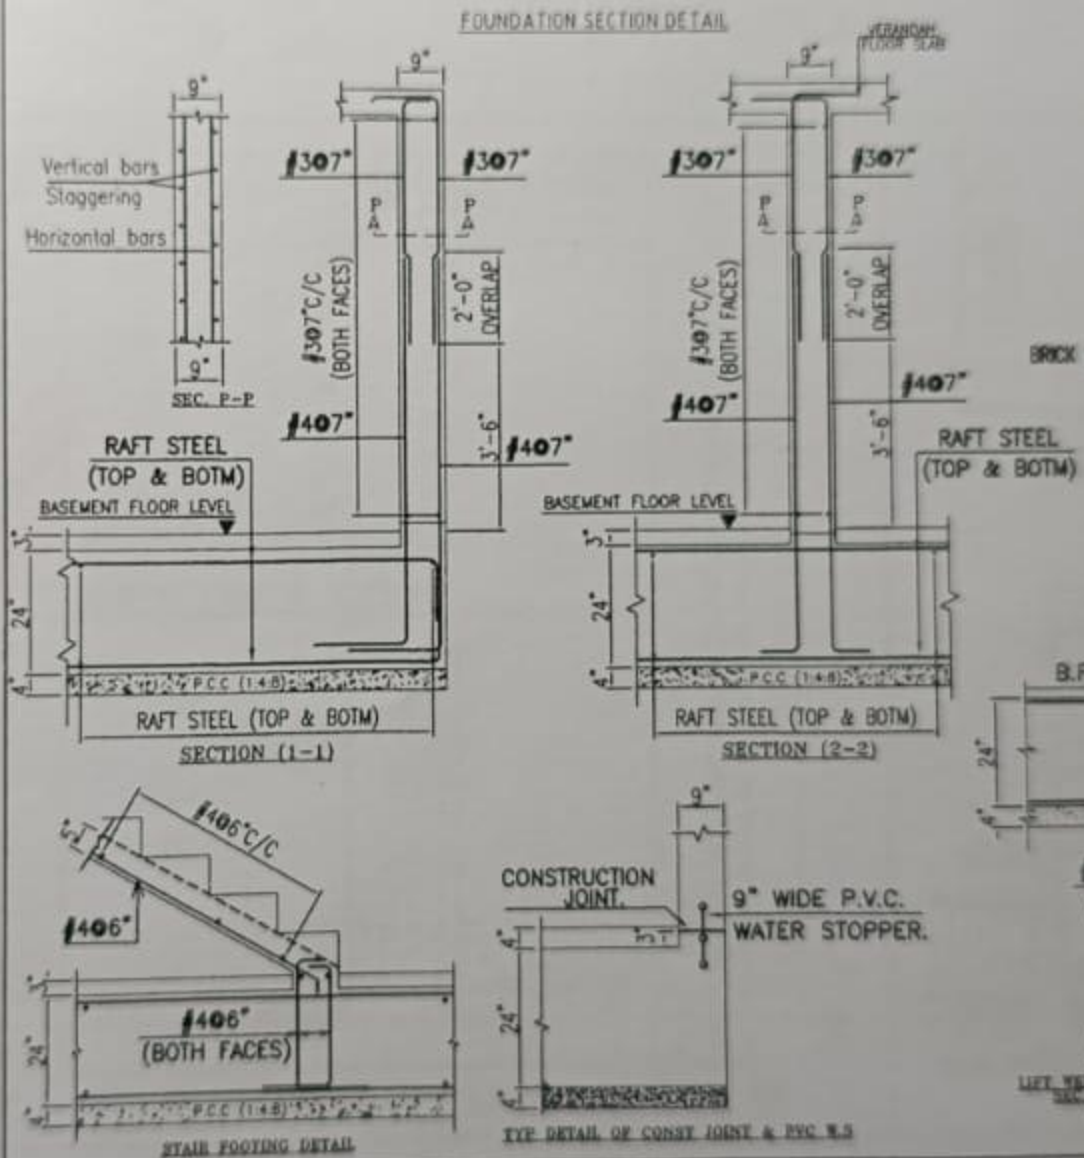


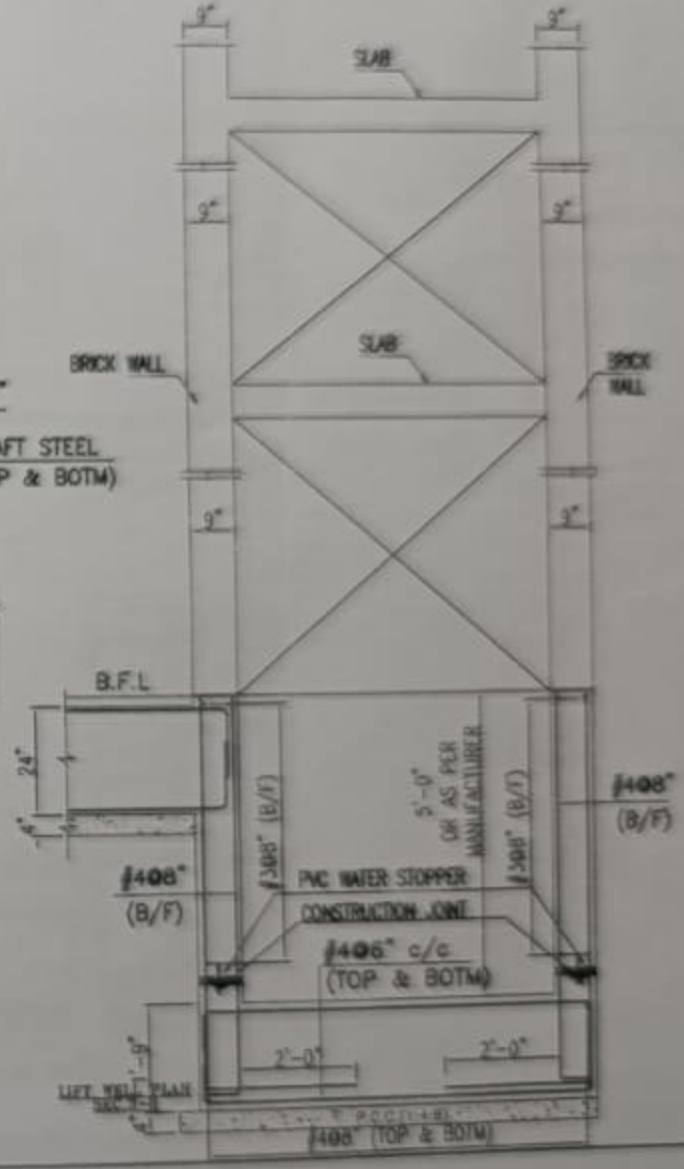


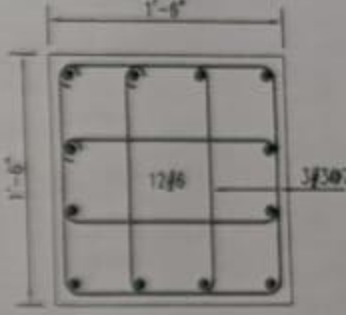

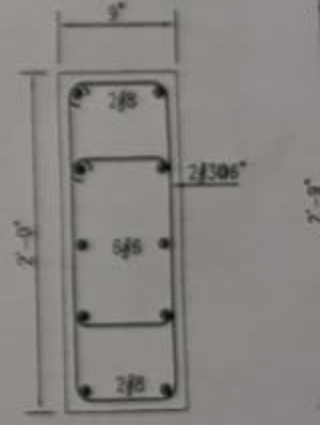

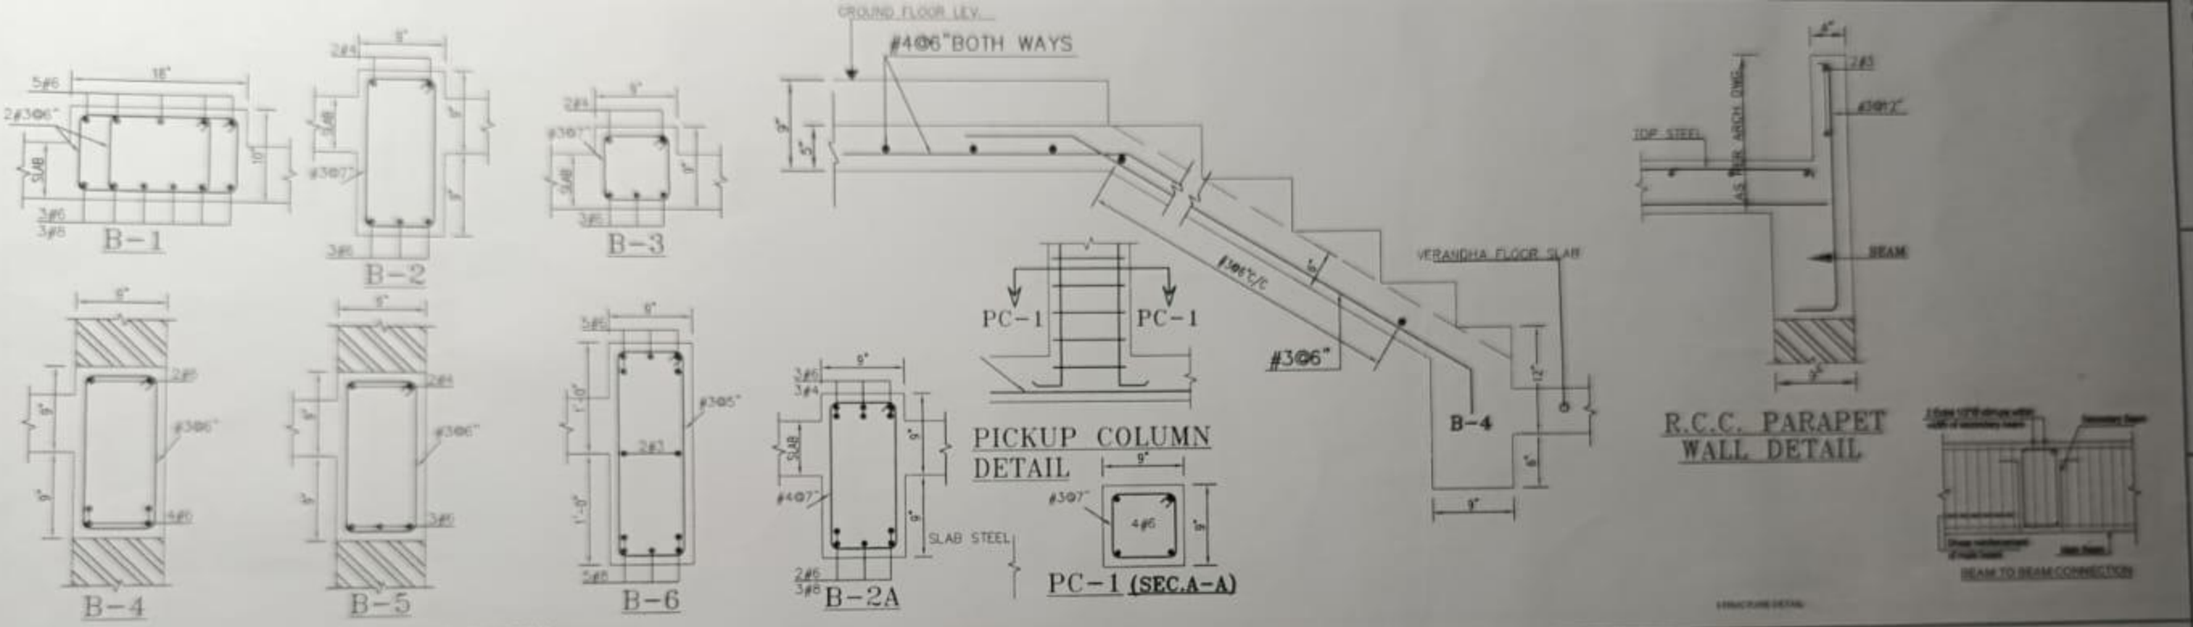

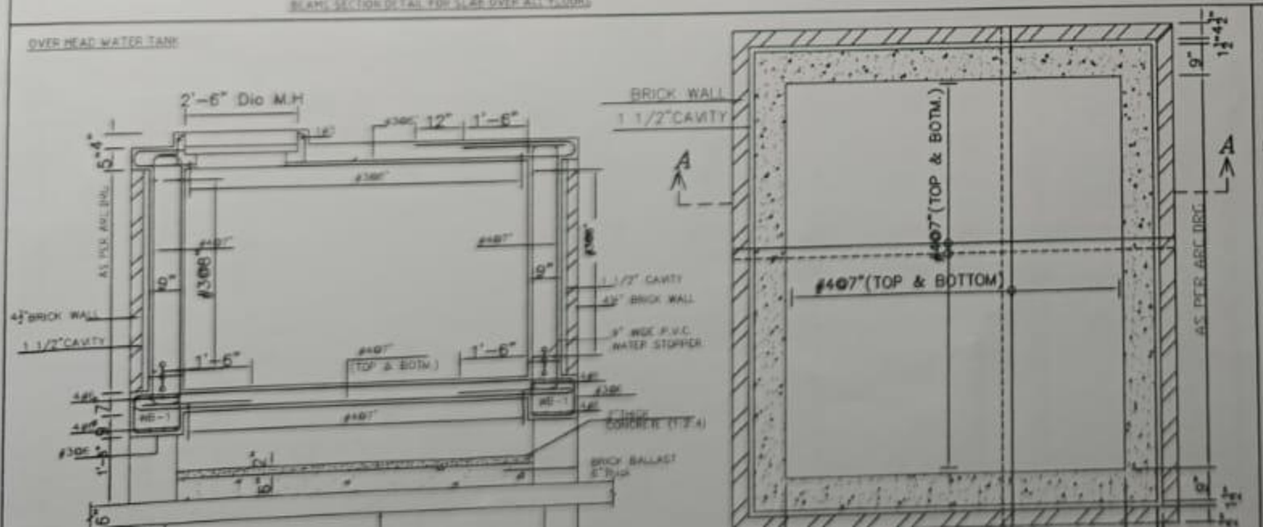

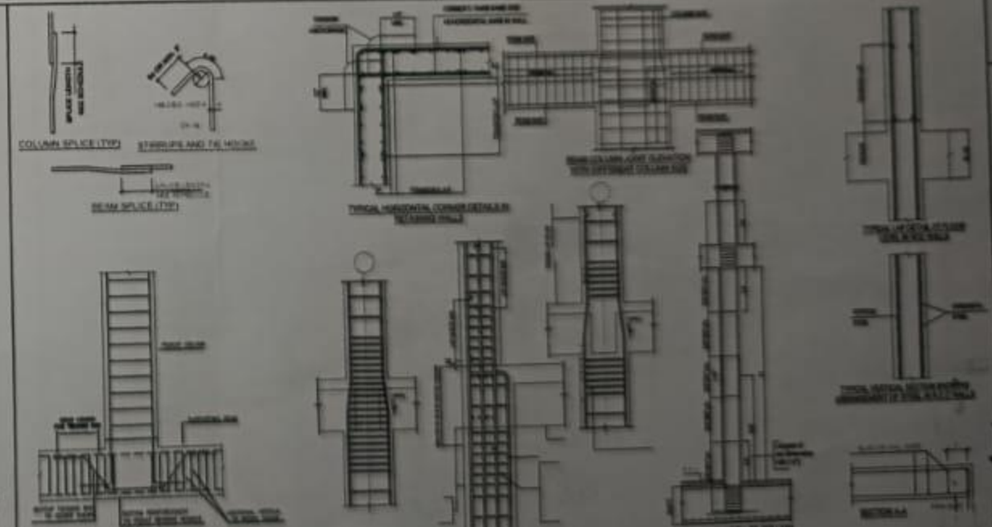

PROJECT

OWNER SIGNATURE

STRUCTURE ENGLISH STA

JAVAID KH
Professional E
Registration No.